

A PORTION OF TENTATIVE TRACT
MAP NO. 16248
TOTAL LOTS: 1-65 AND LOTS A-R
TOTAL ACREAGE: 7.537 AC.
DATE OF SURVEY: JANUARY, 2002

TRACT MAP NO. 16249

IN THE UNINCORPORATED TERRITORY OF THE COUNTY OF ORANGE,
STATE OF CALIFORNIA

BEING A SUBDIVISION OF LOT 11, AS SHOWN ON TRACT MAP NO. 16203
FILED IN BOOK 826, PAGES 8 THROUGH 20 INCLUSIVE, OF MISCELLANEOUS MAPS
IN THE OFFICE OF THE COUNTY RECORDER OF SAID COUNTY, STATE OF CALIFORNIA

ADAMS - STREETER CIVIL ENGINEERING, INC. JAN A. ADAMS, R.C.E. 21687
DATE OF SURVEY: JANUARY, 2002

ACCEPTED AND FILED AT THE
REQUEST OF

FIRST AMERICAN TITLE COMPANY

DATE August 22, 2002
TIME 10:55 AM FEE \$ 21.00
INSTRUMENT # 2002-105124 M/M
BOOK 835 PAGE 26-23

DARLENE J. BLOOM
INTERIM COUNTY CLERK-RECORDER
BY [Signature]
DEPUTY

OWNER'S CERTIFICATE:

WE, THE UNDERSIGNED, BEING ALL PARTIES HAVING ANY RECORD TITLE INTEREST IN THE LAND COVERED BY THIS MAP, DO HEREBY CONSENT TO THE PREPARATION AND RECORDATION OF SAID MAP, AS SHOWN WITHIN THE DISTINCTIVE BORDER LINE.

WE HEREBY DEDICATE TO THE COUNTY OF ORANGE:

1. AN EASEMENT FOR EMERGENCY AND PUBLIC SERVICE VEHICULAR INGRESS-EGRESS AS SHOWN HEREON.

WE ALSO DEDICATE TO THE SANTA MARGARITA WATER DISTRICT, THE EASEMENTS FOR SEWER, WATER AND ACCESS PURPOSES AS SHOWN ON SAID MAP, WHICH EASEMENTS SHALL BE SUBJECT TO THE SAME TERMS AND CONDITIONS AS ARE SHOWN IN THAT CERTAIN EASEMENT RECORDED OCTOBER 6, 1980, IN BOOK 13776, PAGE 341, OF OFFICIAL RECORDS, COUNTY OF ORANGE.

BARRATT-BAYWOOD II, LLC, A CALIFORNIA LIMITED LIABILITY COMPANY

[Signature]
PRINT NAME S. R. REID
PRINT TITLE MANAGING MEMBER

[Signature]
PRINT NAME R. W. LAING
PRINT TITLE MANAGING MEMBER

DMB LADERA, LLC A DELAWARE LIMITED LIABILITY COMPANY AS BENEFICIARY UNDER A DEED OF TRUST RECORDED FEBRUARY 19, 2002 AS INSTRUMENT NO. 20020140148 OF OFFICIAL RECORDS.

BY: RANCHO MISSION VIEJO, LLC, A DELAWARE LIMITED LIABILITY COMPANY, AS AGENT AND/OR MANAGER.

[Signature]
PRINT NAME Donald T. Stahlin
PRINT TITLE Director of Community Development

[Signature]
PRINT NAME Stephen C. Schuch
PRINT TITLE Exec Vice President

BANK OF AMERICA, NATIONAL ASSOCIATION, A NATIONAL BANKING ASSOCIATION AS BENEFICIARY UNDER A DEED OF TRUST RECORDED FEBRUARY 19, 2002 AS INSTRUMENT NO. 20020140149 OF OFFICIAL RECORDS.

[Signature]
PRINT NAME Anthony Oliver
PRINT TITLE Vice President

[Signature]
PRINT NAME Charla A. Wells
PRINT TITLE Vice President

STATE OF CALIFORNIA)
COUNTY OF San Diego)ss

ON THIS 21st DAY OF MAY, 2002, BEFORE ME, Stephanie C. Hagan, A NOTARY PUBLIC IN AND FOR SAID STATE, PERSONALLY APPEARED Donald T. Stahlin AND Stephen C. Schuch PERSONALLY KNOWN TO ME (OR PROVED TO ME ON THE BASIS OF SATISFACTORY EVIDENCE) TO BE THE PERSONS WHOSE NAMES ARE SUBSCRIBED TO THE WITHIN INSTRUMENT AND ACKNOWLEDGED TO ME THAT THEY EXECUTED THE SAME IN THEIR AUTHORIZED CAPACITIES, AND THAT BY THEIR SIGNATURES ON THE INSTRUMENT THE PERSONS OR THE ENTITY UPON BEHALF OF WHICH THE PERSONS ACTED, EXECUTED THE INSTRUMENT.

WITNESS MY HAND:

[Signature]
NOTARY PUBLIC IN AND FOR SAID STATE

[Signature]
PRINT NAME

MY PRINCIPAL PLACE OF BUSINESS
IS IN San Diego COUNTY

MY COMMISSION EXPIRES March 24, 2004
my commission # 1254668

STATE OF CALIFORNIA)
COUNTY OF ORANGE)ss

ON THIS 3rd DAY OF June, 2002, BEFORE ME, Tina T. Baker, A NOTARY PUBLIC IN AND FOR SAID STATE, PERSONALLY APPEARED Donald T. Stahlin AND Stephen C. Schuch PERSONALLY KNOWN TO ME (OR PROVED TO ME ON THE BASIS OF SATISFACTORY EVIDENCE) TO BE THE PERSONS WHOSE NAMES ARE SUBSCRIBED TO THE WITHIN INSTRUMENT AND ACKNOWLEDGED TO ME THAT THEY EXECUTED THE SAME IN THEIR AUTHORIZED CAPACITIES, AND THAT BY THEIR SIGNATURES ON THE INSTRUMENT THE PERSONS OR THE ENTITY UPON BEHALF OF WHICH THE PERSONS ACTED, EXECUTED THE INSTRUMENT.

WITNESS MY HAND:

[Signature]
NOTARY PUBLIC IN AND FOR SAID STATE

[Signature]
PRINT NAME

MY PRINCIPAL PLACE OF BUSINESS
IS IN Orange COUNTY

MY COMMISSION EXPIRES 8-29-04

STATE OF CALIFORNIA)
COUNTY OF San Diego)ss

ON THIS 24th DAY OF May, 2002, BEFORE ME, Peggy J. French, A NOTARY PUBLIC IN AND FOR SAID STATE, PERSONALLY APPEARED Donald T. Stahlin AND Stephen C. Schuch PERSONALLY KNOWN TO ME (OR PROVED TO ME ON THE BASIS OF SATISFACTORY EVIDENCE) TO BE THE PERSONS WHOSE NAMES ARE SUBSCRIBED TO THE WITHIN INSTRUMENT AND ACKNOWLEDGED TO ME THAT THEY EXECUTED THE SAME IN THEIR AUTHORIZED CAPACITIES, AND THAT BY THEIR SIGNATURES ON THE INSTRUMENT THE PERSONS OR THE ENTITY UPON BEHALF OF WHICH THE PERSONS ACTED, EXECUTED THE INSTRUMENT.

WITNESS MY HAND:

[Signature]
NOTARY PUBLIC IN AND FOR SAID STATE

[Signature]
PRINT NAME

MY PRINCIPAL PLACE OF BUSINESS
IS IN San Diego COUNTY

MY COMMISSION EXPIRES January 2, 2003
Commission # 1207169

SIGNATURE OMISSIONS


PURSUANT TO THE PROVISIONS OF SECTION 66436 (a)(C) OF THE SUBDIVISION MAP ACT, THE FOLLOWING SIGNATURES HAVE BEEN OMITTED:

LADERA DEVELOPMENT COMPANY, LLC, HOLDER OF OIL, GAS AND MINERAL RIGHTS RECORDED AS INSTRUMENT NO. 19960624029 OF OFFICIAL RECORDS.

ENGINEER'S STATEMENT

THIS MAP WAS PREPARED BY ME OR UNDER MY DIRECTION AND IS BASED UPON A FIELD SURVEY IN CONFORMANCE WITH THE REQUIREMENTS OF THE SUBDIVISION MAP ACT AND LOCAL ORDINANCE AT THE REQUEST OF BARRATT-BAYWOOD II, LLC IN JANUARY, 2002. I HEREBY STATE THAT ALL MONUMENTS ARE OF THE CHARACTER AND OCCUPY THE POSITIONS INDICATED, OR THAT THEY WILL BE SET IN SUCH POSITIONS; AND THAT SAID MONUMENTS ARE SUFFICIENT TO ENABLE THE SURVEY TO BE RETRACED. I HEREBY STATE THAT THIS FINAL MAP SUBSTANTIALLY CONFORMS TO THE CONDITIONALLY APPROVED TENTATIVE MAP.

JAN A. ADAMS, R.C.E. 21687
EXPIRES: 9/30/05

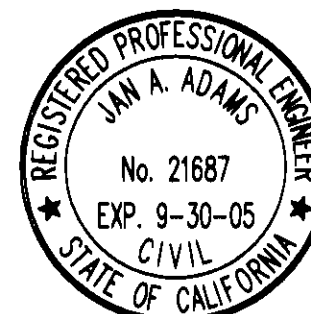


COUNTY SURVEYOR'S STATEMENT

I HEREBY STATE THAT I HAVE EXAMINED THIS MAP AND HAVE FOUND IT TO BE SUBSTANTIALLY IN CONFORMANCE WITH THE TENTATIVE MAP AS FILED WITH, AMENDED AND APPROVED BY THE ORANGE COUNTY SUBDIVISION COMMITTEE; THAT ALL PROVISIONS OF THE SUBDIVISION MAP ACT AND COUNTY SUBDIVISION REGULATIONS HAVE BEEN COMPLIED WITH AND I AM SATISFIED SAID MAP IS TECHNICALLY CORRECT.

DATED THE 7TH DAY OF AUGUST, 2002.

[Signature]
JOHN CANAS, COUNTY SURVEYOR
LS 4408 EXPIRATION DATE: 9-30-05

BY: MICHAEL K. SULLIVAN, DEPUTY
LS 6254 EXPIRES 8/30/08

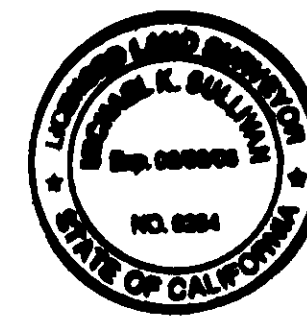

COUNTY TREASURER - TAX COLLECTOR'S CERTIFICATE

STATE OF CALIFORNIA)
COUNTY OF ORANGE)ss

I HEREBY CERTIFY THAT ACCORDING TO THE RECORDS OF MY OFFICE, THERE ARE NO LIENS AGAINST THE LAND COVERED BY THIS MAP OR ANY PART THEREOF FOR UNPAID STATE, COUNTY, MUNICIPAL OR LOCAL TAXES OR SPECIAL ASSESSMENTS COLLECTED AS TAXES, EXCEPT TAXES OR SPECIAL ASSESSMENTS COLLECTED AS TAXES NOT YET PAYABLE.

AND DO CERTIFY TO THE RECORDER OF ORANGE COUNTY THAT THE PROVISIONS OF THE SUBDIVISION MAP ACT HAVE BEEN COMPLIED WITH REGARDING DEPOSITS TO SECURE PAYMENT OF TAXES OR SPECIAL ASSESSMENTS COLLECTED AS TAXES ON THE LAND COVERED BY THIS MAP.

DATED THIS 26 DAY OF JUNE, 2002

JOHN M. W. MOORLACH

COUNTY TREASURER - TAX COLLECTOR

BY

[Signature]
DEPUTY TREASURER - TAX COLLECTOR

CLERK OF THE BOARD OF SUPERVISOR'S CERTIFICATE

STATE OF CALIFORNIA)
COUNTY OF ORANGE)ss

I HEREBY CERTIFY THAT THIS MAP PRESENTED FOR APPROVAL TO THE BOARD OF SUPERVISORS OF ORANGE COUNTY AT A REGULAR MEETING THEREOF HELD ON THE 26th DAY OF August, 2002, AND THAT THEREUPON SAID BOARD DID, BY AN ORDER DULY PASSED AND ENTERED, APPROVE SAID MAP.


AND DID ALSO ACCEPT ON BEHALF OF THE COUNTY OF ORANGE:

1. THE EASEMENT FOR EMERGENCY AND PUBLIC SERVICE VEHICULAR INGRESS-EGRESS, AS DEDICATED.

AND DID ALSO APPROVE SUBJECT MAP PURSUANT TO THE PROVISIONS OF SECTION 66436 (a)(C) OF THE SUBDIVISION MAP ACT.

DATED THIS 26th DAY OF August, 2002.

[Signature]
DARLENE J. BLOOM, CLERK OF THE BOARD OF SUPERVISORS

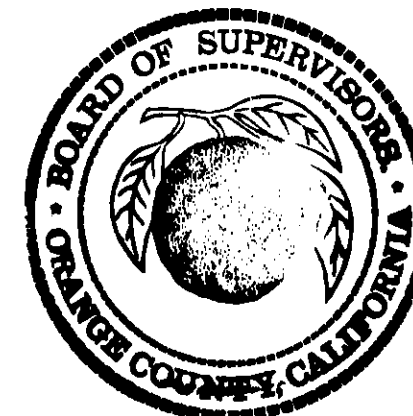

CERTIFICATE OF ACCEPTANCE

THE UNDERSIGNED, BEING THE DULY APPOINTED AGENT OF THE SANTA MARGARITA WATER DISTRICT, A PUBLIC CORPORATION OF ORANGE COUNTY, CALIFORNIA, PURSUANT TO ITS RESOLUTION NO. 88-10-2, DOES HEREBY ACCEPT ON BEHALF OF SAID DISTRICT THE EASEMENTS FOR SEWER, WATER AND ACCESS PURPOSES, AS DEDICATED AND AS SHOWN ON THIS TRACT MAP, BY AND BETWEEN THE SANTA MARGARITA WATER DISTRICT AND BARRATT-BAYWOOD II, LLC AND DOES HEREBY CERTIFY THAT THE GRANTEE CONSENTS TO THE RECORDATION OF SAID TRACT.

BY: [Signature]
DANIEL R. FERONS, CHIEF ENGINEER
SANTA MARGARITA WATER DISTRICT

STATE OF CALIFORNIA)
COUNTY OF ORANGE)ss

ON THIS 4th DAY OF June, 2002, BEFORE ME, ANDREA EVANS, A NOTARY PUBLIC IN AND FOR SAID STATE, PERSONALLY APPEARED Daniel R. Ferons PERSONALLY KNOWN TO ME (OR PROVED TO ME ON THE BASIS OF SATISFACTORY EVIDENCE) TO BE THE PERSONS WHOSE NAMES ARE SUBSCRIBED TO THE WITHIN INSTRUMENT AND ACKNOWLEDGED TO ME THAT THEY EXECUTED THE SAME IN THEIR AUTHORIZED CAPACITIES, AND THAT BY THEIR SIGNATURES ON THE INSTRUMENT THE PERSONS OR THE ENTITY UPON BEHALF OF WHICH THE PERSONS ACTED, EXECUTED THE INSTRUMENT.

WITNESS MY HAND:

[Signature]
NOTARY PUBLIC IN AND FOR SAID STATE

[Signature]
PRINT NAME

MY PRINCIPAL PLACE OF BUSINESS
IS IN Orange COUNTY

MY COMMISSION EXPIRES April 8, 2004

SHEET 2 OF 8 SHEETS

A PORTION OF TENTATIVE TRACT
MAP NO. 16248
TOTAL LOTS: 1-65 AND LOTS A-R
TOTAL ACREAGE: 7.537 AC.
DATE OF SURVEY: JANUARY, 2002

TRACT MAP NO. 16249

IN THE UNINCORPORATED TERRITORY OF THE COUNTY OF ORANGE,
STATE OF CALIFORNIA

ADAMS - STREETER CIVIL ENGINEERING, INC. JAN A. ADAMS, R.C.E. 21687
DATE OF SURVEY: JANUARY, 2002

NOTES:

LETTERED LOTS ARE NOT SEPARATE BUILDING SITES.

LOTS DESIGNATED AS OPEN SPACES ARE FOR LANDSCAPE PURPOSES
AND WILL BE MAINTAINED BY THE HOMEOWNER'S ASSOCIATION.


(X) - INDICATES SHEET NUMBER.

LETTERED LOT INFORMATION

LOT	AREA	USE	LOT	AREA	USE
A	0.148 AC.	OPEN SPACE	N	0.180 AC.	PRIVATE STREET
B	0.251 AC.	OPEN SPACE	O	0.362 AC.	PRIVATE STREET
C	0.378 AC.	OPEN SPACE	P	0.223 AC.	PRIVATE STREET
D	0.301 AC.	OPEN SPACE	Q	0.096 AC.	PRIVATE STREET
E	0.489 AC.	OPEN SPACE	R	0.023 AC.	OPEN SPACE
F	0.103 AC.	OPEN SPACE			
G	0.420 AC.	OPEN SPACE			
H	0.302 AC.	OPEN SPACE			
I	0.015 AC.	OPEN SPACE			
J	0.155 AC.	OPEN SPACE			
K	0.078 AC.	PRIVATE STREET			
L	0.118 AC.	PRIVATE STREET			
M	0.102 AC.	PRIVATE STREET			

GPS NO. 1448
FOUND 2 1/2" IRON PIPE W/2" BRASS CAP
STAMPED "GPS 1448 9-95" PER TRACT
NO. 16025, MM 812/22-29.

N 2146790.819
E 6142602.585

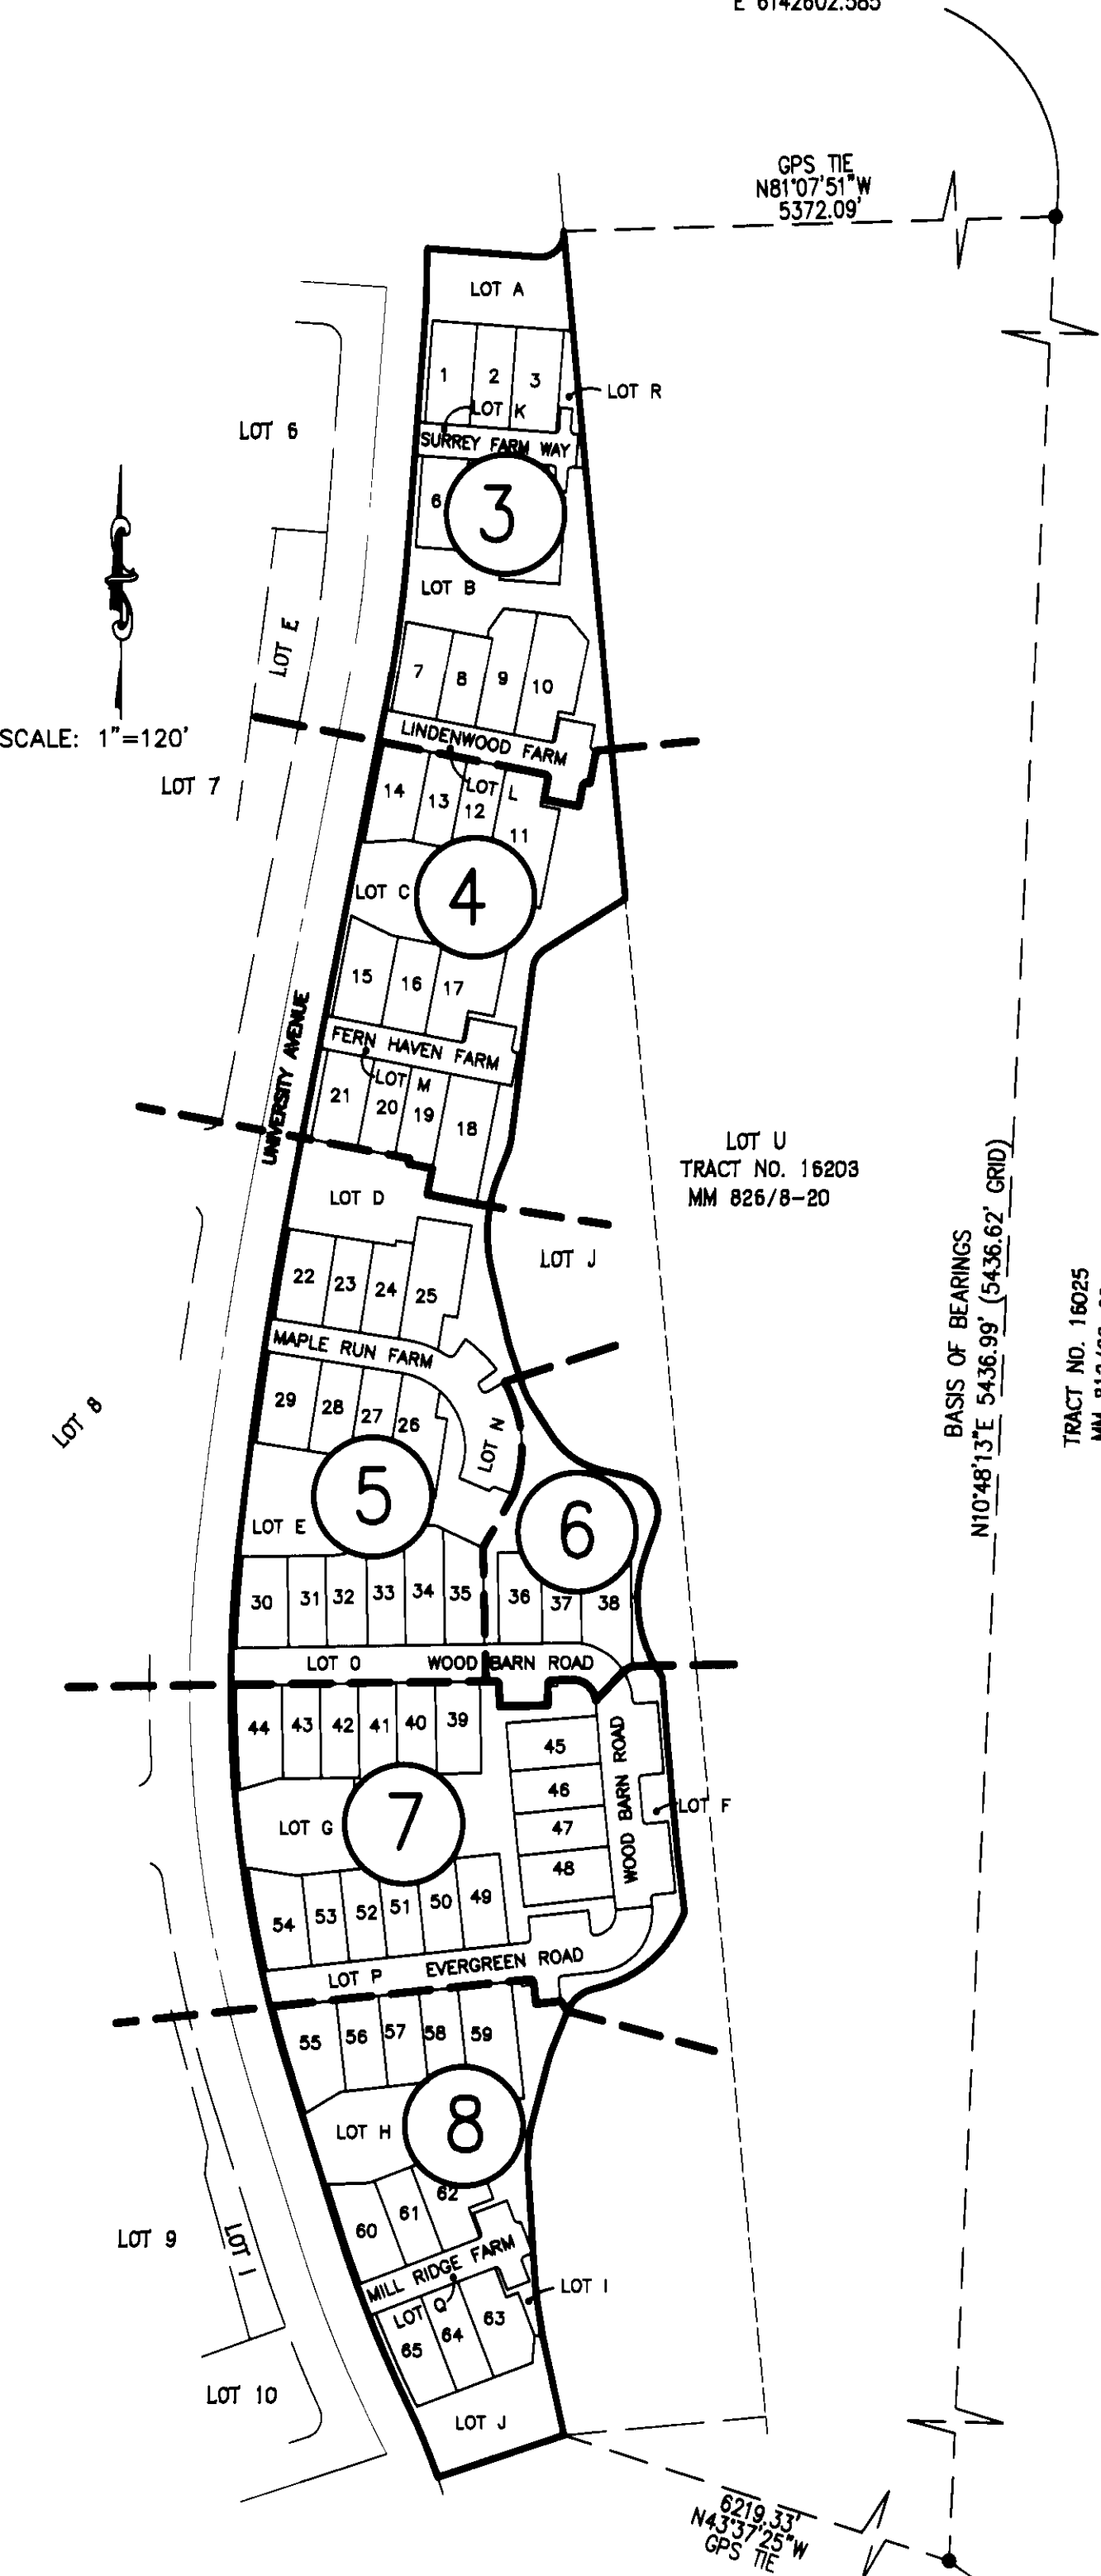

SHEET INDEX AND BOUNDARY CONTROL

EASEMENT NOTES:

- (A) AN EASEMENT FOR EMERGENCY AND PUBLIC SERVICE VEHICULAR INGRESS-EGRESS IN FAVOR OF THE COUNTY OF ORANGE.
- (B) AN EASEMENT FOR SEWER AND WATER PIPELINE AND ACCESS PURPOSES IN FAVOR OF THE SANTA MARGARITA WATER DISTRICT.

BASIS OF BEARINGS

THE BEARINGS SHOWN HEREON ARE BASED ON THE BEARING BETWEEN ORANGE COUNTY SURVEYOR'S HORIZONTAL CONTROL STATION "GPS NO. 1417" AND "GPS NO. 1448", BEING N. 10°48'13" E., PER RECORDS ON FILE IN THE OFFICE OF THE ORANGE COUNTY SURVEYOR.

DATUM STATEMENT

COORDINATES SHOWN HEREON ARE BASED IN THE CALIFORNIA COORDINATE SYSTEM (CCS83) ZONE VI, 1983 NAD (1991.35 EPOCH), O.C.S. GPS ADJUSTMENT. ALL DISTANCE SHOWN HEREON ARE GROUND, UNLESS OTHERWISE NOTED. TO OBTAIN GRID DISTANCE MULTIPLY GROUND DISTANCE BY 0.99993286.

AUTOMATIC FIRE SPRINKLER NOTE:

ALL RESIDENTIAL STRUCTURES EXCEEDING 5,500 SQUARE FEET AND ALL STRUCTURES EXCEEDING FIRE DEPARTMENT ACCESS REQUIREMENTS SHALL BE PROTECTED BY AN AUTOMATIC FIRE SPRINKLER SYSTEM, IN A MANNER MEETING THE APPROVAL OF THE FIRE CHIEF.

SPECIAL FIRE PROTECTION NOTE:

PROPERTY IS CONDITIONALLY EXCLUDED FROM A SPECIAL FIRE PROTECTION AREA.


ALL REQUIREMENTS FOR DEVELOPMENT AND CONSTRUCTION WITHIN A "SPECIAL FIRE PROTECTION AREA" INCLUDING INCREASED STREET WIDTHS AND CLASS A ROOF ASSEMBLIES WILL BE MET.

MONUMENT NOTES:

- 1. ● INDICATES FOUND MONUMENT AS NOTED.
- 2. ▲ INDICATES 2" IRON PIPE, TAGGED "R.C.E. 21687", OR LEAD, TACK AND TAG "R.C.E. 21687" IN CONCRETE, OR 8" SPIKE AND WASHER STAMPED "RCE 21687" IN ASPHALT PAVING TO BE SET, UNLESS OTHERWISE NOTED.
- 3. ▲ INDICATES 2" IRON PIPE, TAGGED "R.C.E. 21687" TO BE SET PRIOR TO RECORDATION.
- 4. ○ INDICATES LEAD, TACK AND TAG "R.C.E. 21687" TO BE SET ON AN OFFSET SHOWN HEREON OUTSIDE THE TRUE LOT CORNER IN THE TOP OF ADJACENT CONCRETE CURB, UNLESS OTHERWISE NOTED.
- 5. ■ INDICATES LOCATION OF 1" IRON PIPE, TAGGED "LS 5557", OR SPIKE AND WASHER, STAMPED "LS 5557", OR LEAD, TACK AND TAG "LS 5557" TO BE SET PER TRACT NO. 16203, MM 826/8-20, UNLESS OTHERWISE NOTED.
- 6. ■ INDICATES LOCATION OF 2" IRON PIPE, TAGGED "LS 5557", OR SPIKE AND WASHER, STAMPED "LS 5557", OR LEAD, TACK AND TAG "LS 5557" TO BE SET PER TRACT NO. 16203, MM 826/8-20, UNLESS OTHERWISE NOTED.
- 7. 1" IRON PIPE, TAGGED "R.C.E. 21687", OR SPIKE AND WASHER, STAMPED "R.C.E. 21687", OR LEAD, TACK AND TAG "R.C.E. 21687" TO BE SET AT ALL LOT CORNERS, EXCEPT AT LOT CORNERS THAT ABUT A STREET, WHICH WILL BE SET ON A 0.50' OFFSET OUTSIDE THE TRUE LOT CORNER ON A PROLONGATION OF THE SIDE LOT LINE BY A LEAD, TACK AND TAG "R.C.E. 21687" IN THE TOP OF ADJACENT CONCRETE CURB, UNLESS OTHERWISE NOTED.
- 8. 8" SPIKE AND WASHER STAMPED "RCE 21687" IN ASPHALT PAVING, OR LEAD, TACK AND TAG "R.C.E. 21687" IN CONCRETE, OR 1" IRON PIPE, TAGGED "RCE 21687" TO BE SET AT ALL CENTERLINE INTERSECTIONS OF PRIVATE STREETS WITH PUBLIC STREETS, B.C.'S, E.C.'S AND ALL OTHER CENTERLINE POINTS OF CONTROL, UNLESS OTHERWISE NOTED.
- 9. ALL MONUMENTS SHOWN AS "TO BE SET" WILL BE SET WITHIN 90 DAYS AFTER THE ACCEPTANCE OF THE FINAL IMPROVEMENTS.
- 10. NO MONUMENTS ARE TO BE SET AT BC'S AND EC'S OF STREET RIGHT OF WAY LINES.

REFERENCES:

- () INDICATES MEASURED AND RECORD PER TRACT MAP NO. 16203, M.M. 826/8-20.

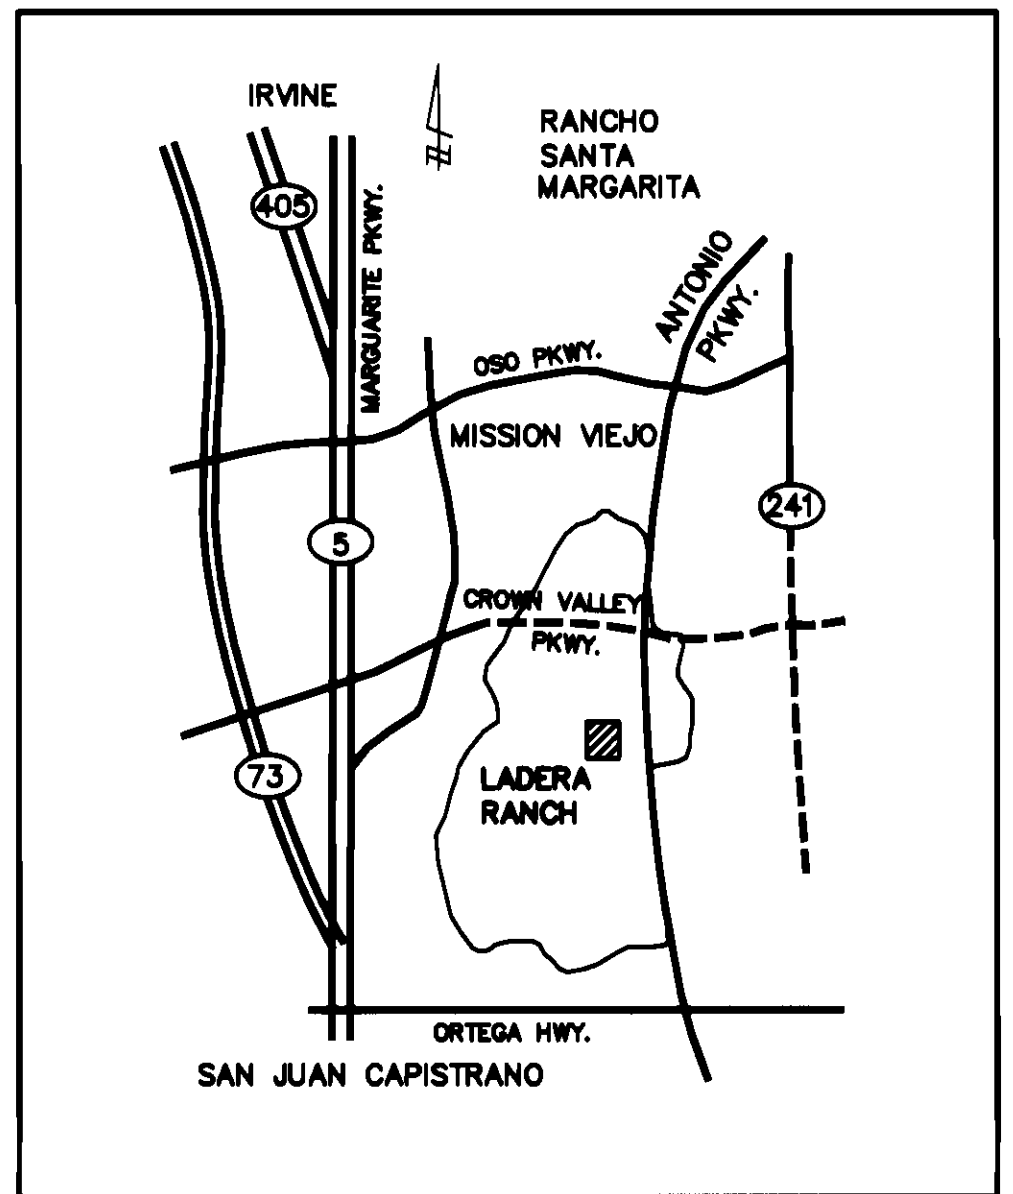

VICINITY MAP

SHEET 3 OF 8 SHEETS

A PORTION OF TENTATIVE TRACT
MAP NO. 16248
TOTAL LOTS: 1-65 AND LOTS A-R
TOTAL ACREAGE: 7.537 AC.
DATE OF SURVEY: JANUARY, 2002

TRACT MAP NO. 16249

IN THE UNINCORPORATED TERRITORY OF THE COUNTY OF ORANGE,
STATE OF CALIFORNIA

ADAMS - STREETER CML ENGINEERING, INC. JAN A. ADAMS, R.C.E. 21687
DATE OF SURVEY: JANUARY, 2002

- ① $\Delta=90^{\circ}00'00''$
 $R=3.00'$
 $L=4.71'$
- ② $N04^{\circ}22'20''E$ 16.00'
- ③ $\Delta=19^{\circ}28'17''$
 $R=3.00'$
 $L=1.02'$
- ④ $\Delta=70^{\circ}31'43''$
 $R=3.00'$
 $L=3.69'$
- ⑤ $N15^{\circ}05'57''W$ (RAD)
- ⑥ $\Delta=22^{\circ}26'39''$
 $R=3.00'$
 $L=1.18'$
- ⑦ $\Delta=67^{\circ}33'21''$
 $R=3.00'$
 $L=3.54'$
- ⑧ $N11^{\circ}20'22''W$ (RAD)

CL CREIGHTON PLACE

LOT 5

LOT 5

LOT A
0.148 AC

LOT R
0.023 AC

SURREY FARM
WAY

LOT K
0.078 AC

DETAIL "A"
NTS

LOT 6
TRACT NO. 16203
MM 826/8-20

CL UNIVERSITY AVENUE

LOT B
0.251 AC

LOT U
TRACT NO. 16203
MM 826/8-20

LOT E

LOT L
0.118 AC
LINDENWOOD FARM
(PVT. ST.)

NOTES:

SEE SHEET 2 FOR BOUNDARY CONTROL SHEET INDEX,
MONUMENT NOTES, EASEMENT NOTES, DATUM STATEMENT
AND BASIS OF BEARINGS.

LETTERED LOTS ARE NOT SEPARATE BUILDING SITES.

LOTS DESIGNATED AS OPEN SPACES ARE FOR LANDSCAPE PURPOSES
AND WILL BE MAINTAINED BY THE HOMEOWNER'S ASSOCIATION.

SEE SHEET 4

SCALE: 1"=20'

FOR EASEMENT DATA
SEE SHEET 4

SHEET 5 OF 8 SHEETS


A PORTION OF TENTATIVE TRACT
MAP NO. 16248
TOTAL LOTS: 1-65 AND LOTS A-R
TOTAL ACREAGE: 7.537 AC.
DATE OF SURVEY: JANUARY, 2002

TRACT MAP NO. 16249

IN THE UNINCORPORATED TERRITORY OF THE COUNTY OF ORANGE,
STATE OF CALIFORNIA

ADAMS - STREETER CIVIL ENGINEERING, INC. JAN A. ADAMS, R.C.E. 21687
DATE OF SURVEY: JANUARY, 2002

- ① $\Delta=87^{\circ}59'22''$
 $R=3.00'$
 $L=4.61'$
- ② $\Delta=02^{\circ}13'56''$
 $R=82.50'$
 $L=3.21'$
- ③ $N56^{\circ}01'01''E$ (RAD)(PRC)
- ④ $N58^{\circ}14'57''E$ (RAD)(PRC)

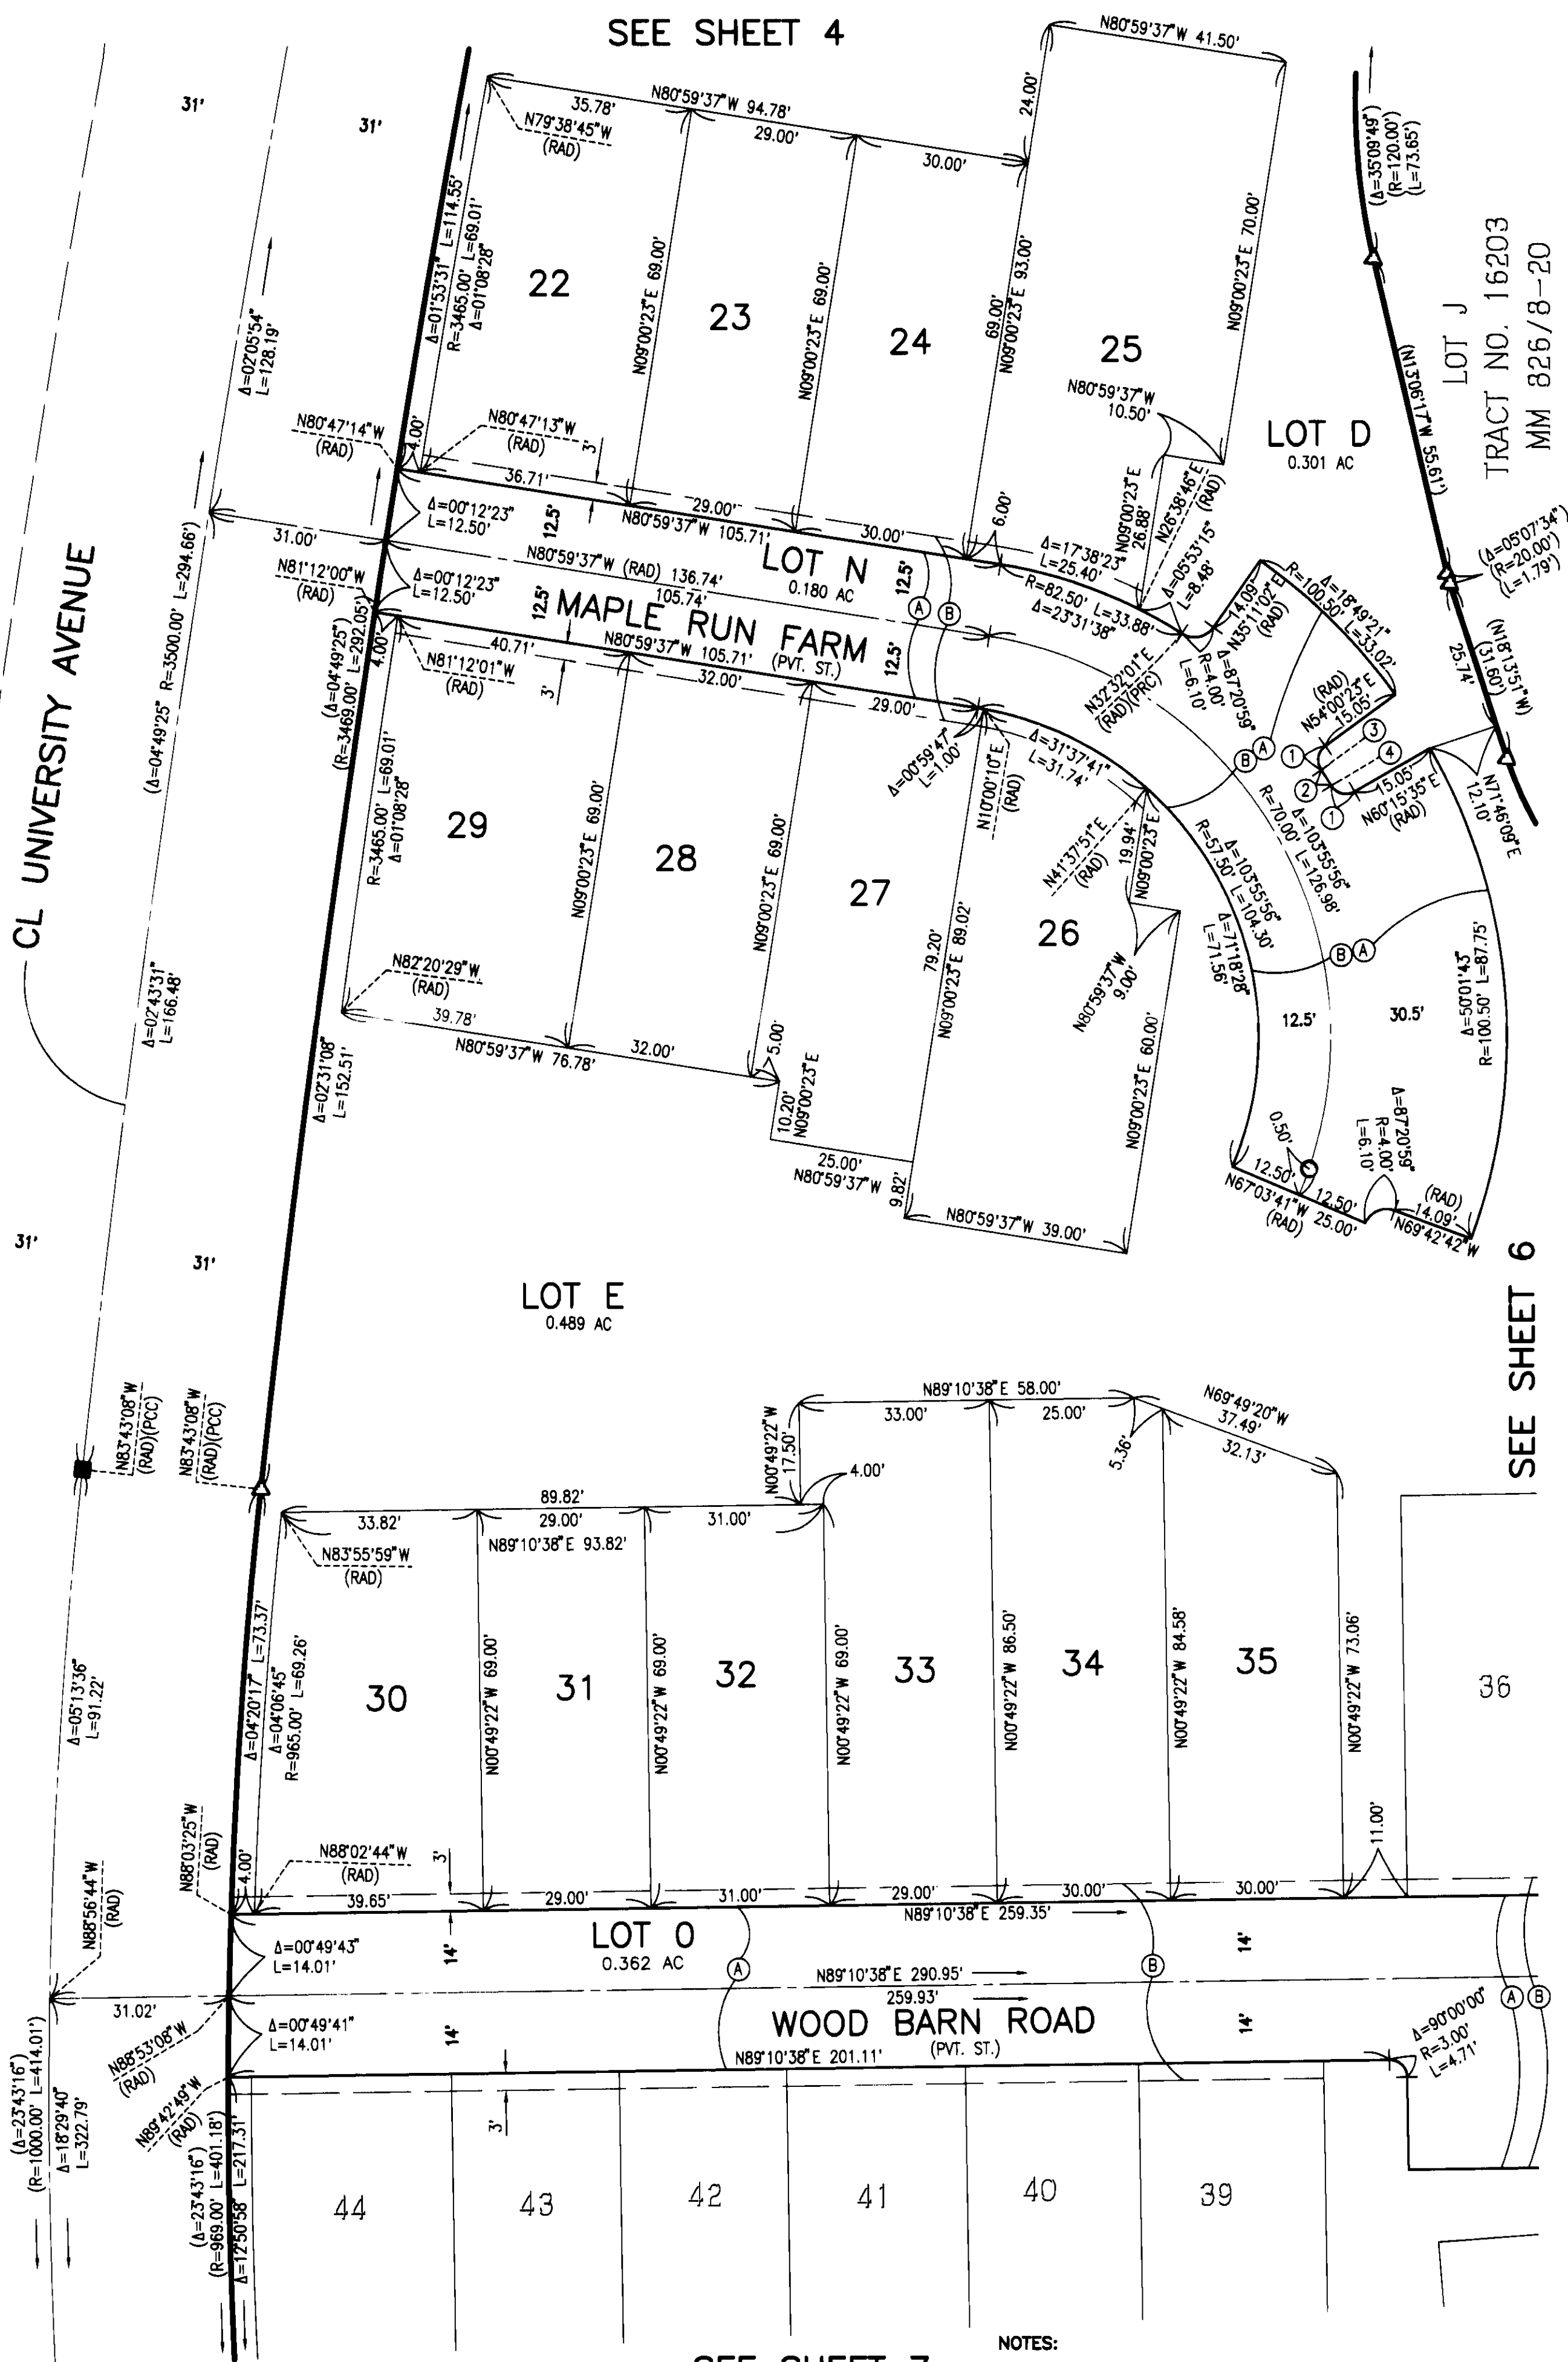

SCALE: 1"=20'

NOTES:

SEE SHEET 2 FOR BOUNDARY CONTROL SHEET INDEX,
MONUMENT NOTES, EASEMENT NOTES, DATUM STATEMENT
AND BASIS OF BEARINGS.

LETTERED LOTS ARE NOT SEPARATE BUILDING SITES.

LOTS DESIGNATED AS OPEN SPACES ARE FOR LANDSCAPE PURPOSES
AND WILL BE MAINTAINED BY THE HOMEOWNER'S ASSOCIATION.

SHEET 6 OF 8 SHEETS
A PORTION OF TENTATIVE TRACT
MAP NO. 16248
TOTAL LOTS: 1-65 AND LOTS A-R
TOTAL ACREAGE: 7.537 AC.
DATE OF SURVEY: JANUARY, 2002

TRACT MAP NO. 16249

IN THE UNINCORPORATED TERRITORY OF THE COUNTY OF ORANGE,
STATE OF CALIFORNIA

ADAMS - STREETER CIVIL ENGINEERING, INC. JAN A. ADAMS, R.C.E. 21687
DATE OF SURVEY: JANUARY, 2002

NOTES:


SEE SHEET 2 FOR BOUNDARY CONTROL SHEET INDEX,
MONUMENT NOTES, EASEMENT NOTES, DATUM STATEMENT
AND BASIS OF BEARINGS.

LETTERED LOTS ARE NOT SEPARATE BUILDING SITES.

LOTS DESIGNATED AS OPEN SPACES ARE FOR LANDSCAPE PURPOSES
AND WILL BE MAINTAINED BY THE HOMEOWNER'S ASSOCIATION.

SEE SHEET 4

SEE SHEET 5

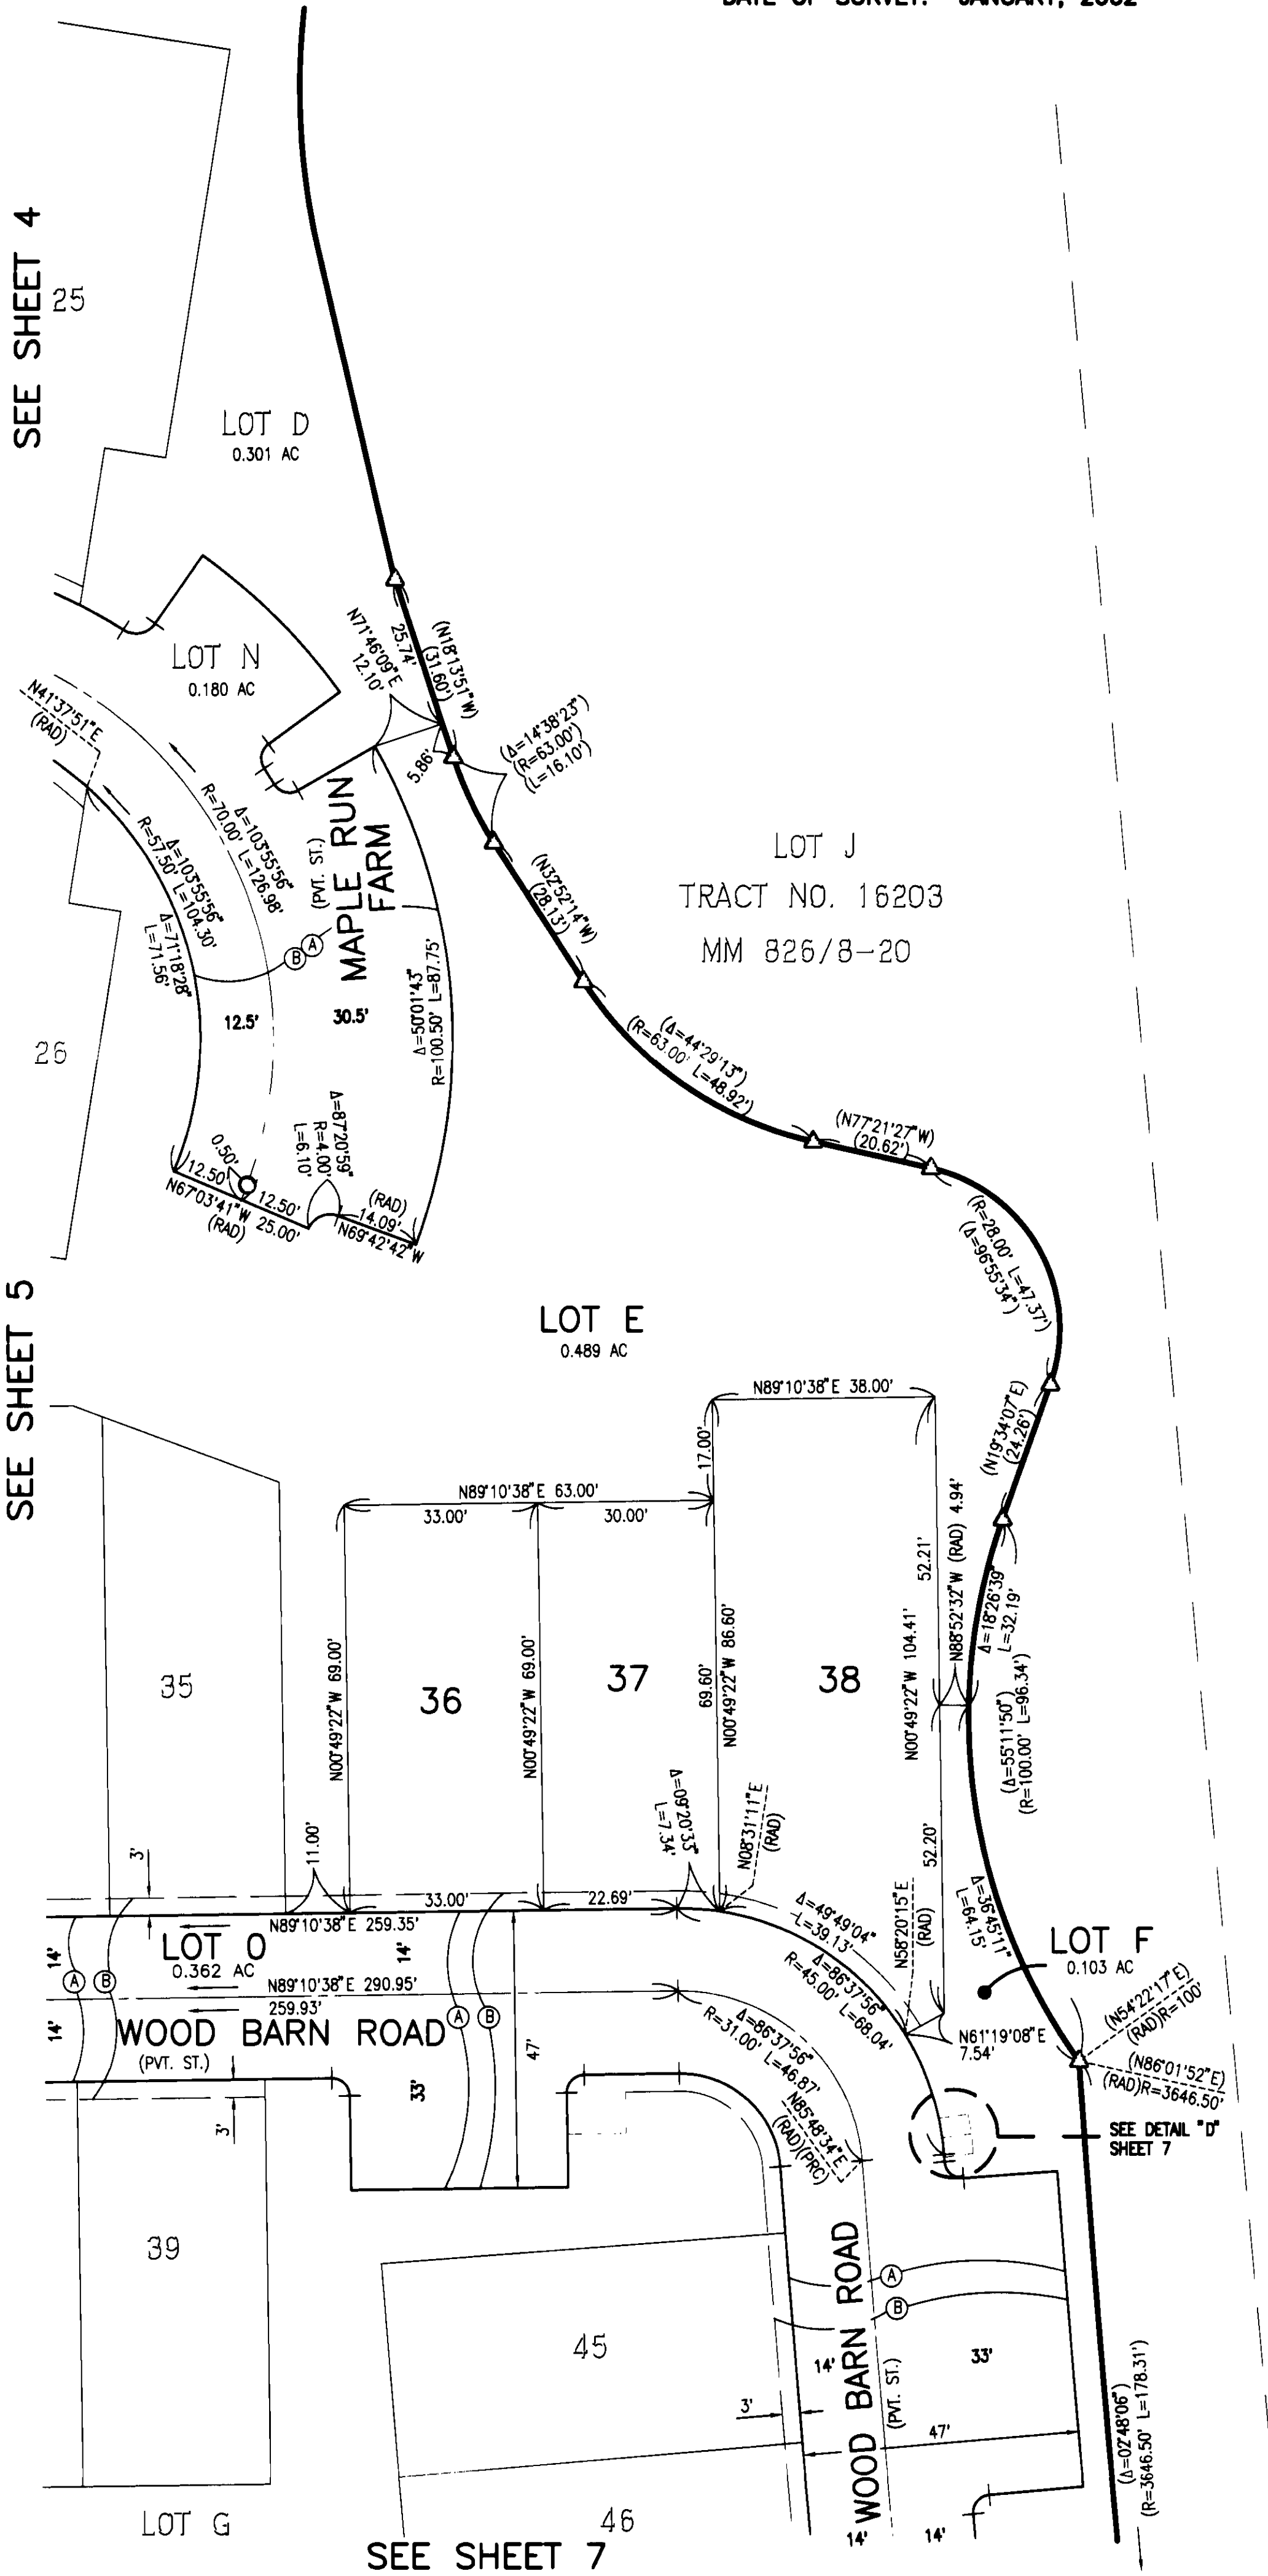

LOT U

SCALE: 1"=20'

SHEET 7 OF 8 SHEETS

A PORTION OF TENTATIVE TRACT
MAP NO. 16249
TOTAL LOTS: 1-65 AND LOTS A-R
TOTAL ACREAGE: 7.537 AC.
DATE OF SURVEY: JANUARY, 2002

TRACT MAP NO. 16249

IN THE UNINCORPORATED TERRITORY OF THE COUNTY OF ORANGE,
STATE OF CALIFORNIA


ADAMS - STREETER CIVIL ENGINEERING, INC. JAN A. ADAMS, R.C.E. 21687
DATE OF SURVEY: JANUARY, 2002

- ① N83°21'15"E (RAD)(PRC)
- ② N83°25'56"E (RAD)(PCC)
- ③ N85°47'25"E (RAD)(PCC)
- ④ $\Delta=90^{\circ}00'00''$
 $R=3.00'$
 $L=4.71'$
- ⑤ $\Delta=90^{\circ}02'49''$
 $R=3.00'$
 $L=4.71'$

SEE SHEET 8

SEE SHEET 5

SEE SHEET 6

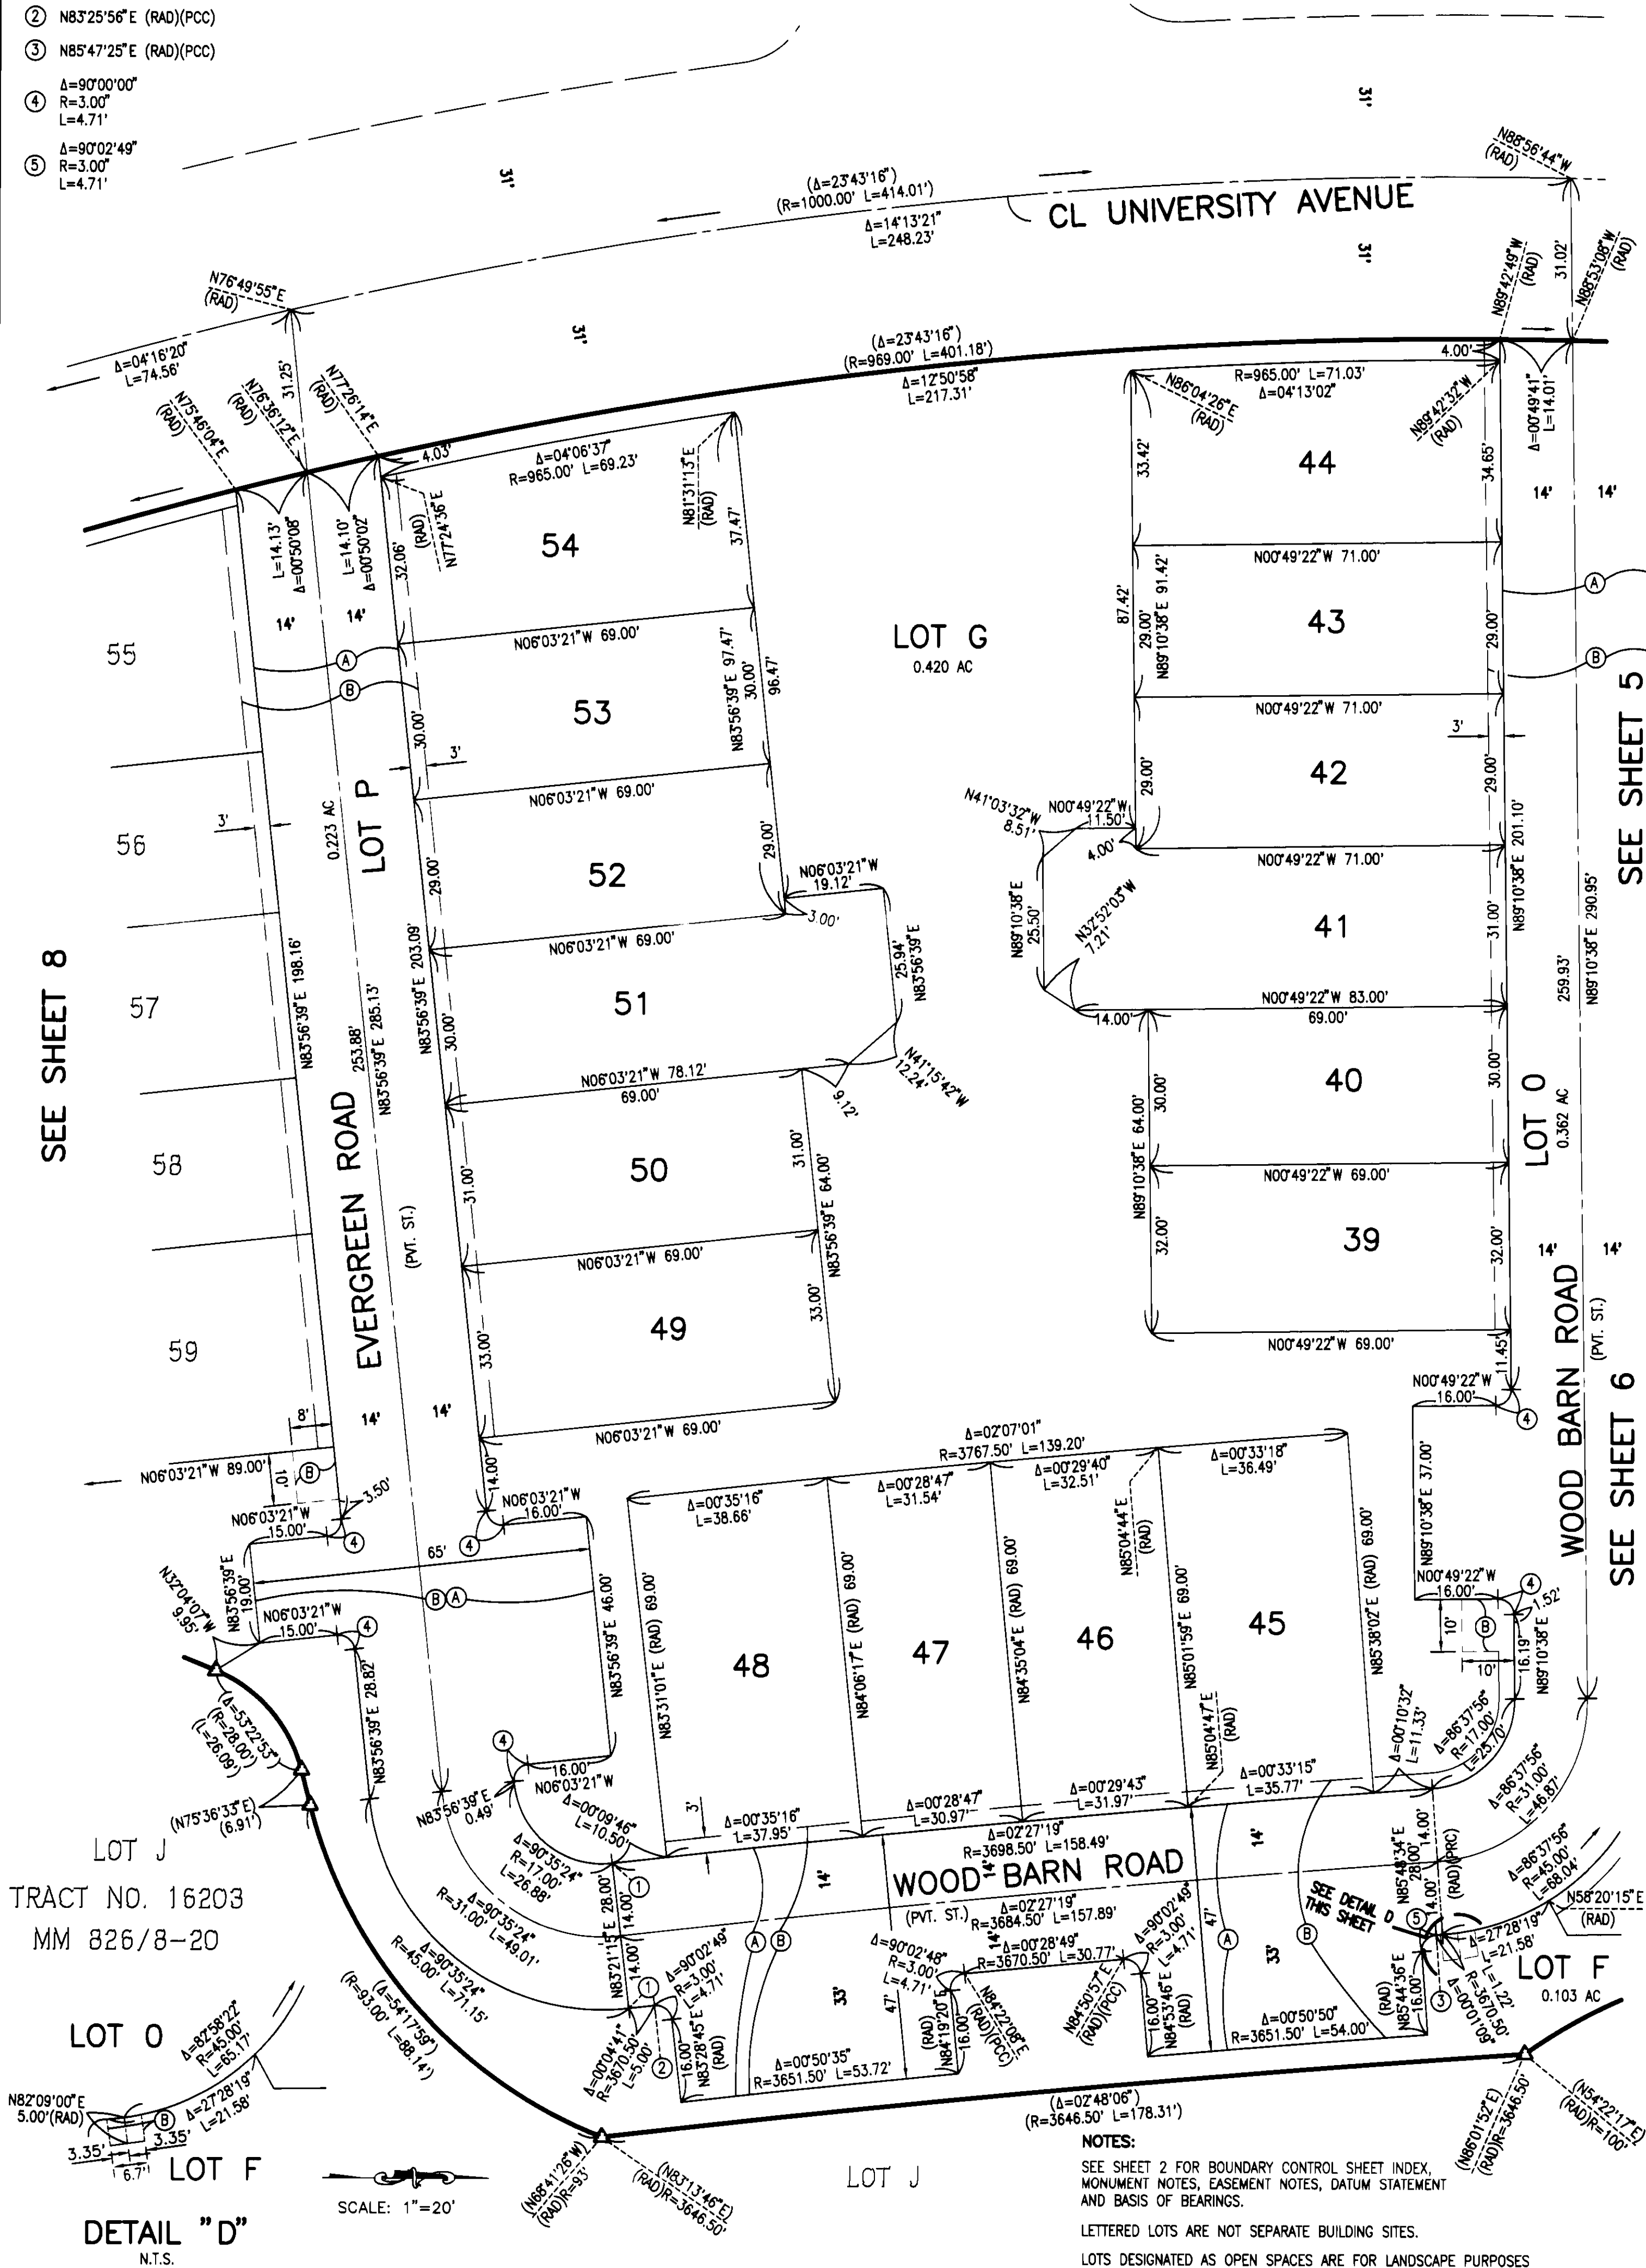

DETAIL "D"
N.T.S.

SCALE: 1"=20'

NOTES:

SEE SHEET 2 FOR BOUNDARY CONTROL SHEET INDEX,
MONUMENT NOTES, EASEMENT NOTES, DATUM STATEMENT
AND BASIS OF BEARINGS.

LETTERED LOTS ARE NOT SEPARATE BUILDING SITES.

LOTS DESIGNATED AS OPEN SPACES ARE FOR LANDSCAPE PURPOSES
AND WILL BE MAINTAINED BY THE HOMEOWNER'S ASSOCIATION.

JN 01-1371

SHEET 8 OF 8 SHEETS
A PORTION OF TENTATIVE TRACT
MAP NO. 16248
TOTAL LOTS: 1-65 AND LOTS A-R
TOTAL ACREAGE: 7.537 AC.
DATE OF SURVEY: DECEMBER, 2001

TRACT MAP NO. 16249

IN THE UNINCORPORATED TERRITORY OF THE COUNTY OF ORANGE,
STATE OF CALIFORNIA

ADAMS - STREETER CIVIL ENGINEERING, INC. JAN A. ADAMS, R.C.E. 21687
DATE OF SURVEY: NOVEMBER, 2001

SEE SHEET 7

