

SHEET 1 OF 4 SHEETS
3.388 ACRES
22 NUMBERED LOTS AND
LETTERED LOTS "A" THROUGH "C"
DATE OF SURVEY: NOVEMBER 2001
(ALL OF VESTING TENTATIVE
TRACT No. 16270)

TRACT NO. 16270

IN THE UNINCORPORATED TERRITORY OF THE COUNTY OF ORANGE, STATE OF CALIFORNIA.
BEING A SUBDIVISION OF LOT 6 AND LOT "1" OF TRACT No. 16157, AS SHOWN ON THE MAP
THEREOF FILED IN BOOK 813 AT PAGES 1 THROUGH 9, INCLUSIVE, OF MISCELLANEOUS
MAPS, IN THE OFFICE OF THE COUNTY RECORDER OF ORANGE COUNTY, CALIFORNIA.
FUSCOE ENGINEERING, INC.
JERRY L. USELTON, L.S. 5347 NOVEMBER 2001

ACCEPTED AND FILED AT THE
REQUEST OF
FIRST AMERICAN TITLE INS. CO.
DATE SEPTEMBER 27, 2002
TIME 04:30 PM FEE \$ 13.00
INSTRUMENT # 20020835742
BOOK 836 PAGE 40-43 m/a
DARLENE J. BLOOM
INTERIM COUNTY CLERK-RECORDER
BY: [Signature] DEPUTY

OWNERSHIP CERTIFICATE:

WE THE UNDERSIGNED, BEING ALL PARTIES HAVING ANY RECORD TITLE INTEREST
IN THE LAND COVERED BY THIS MAP, DO HEREBY CONSENT TO THE PREPARATION
AND RECORDATION OF SAID MAP, AS SHOWN WITHIN THE DISTINCTIVE BORDER LINE.

WE HEREBY DEDICATE TO THE COUNTY OF ORANGE:
1. THE EASEMENTS FOR SIDEWALK PURPOSES AS SHOWN ON SAID MAP

WE ALSO HEREBY DEDICATE TO THE SANTA MARGARITA WATER DISTRICT PIPELINE EASEMENTS
FOR SEWER, WATER AND ACCESS PURPOSES AS SHOWN ON SAID MAP, WHICH EASEMENTS SHALL
BE SUBJECT TO THE SAME TERMS AND CONDITIONS AS ARE SHOWN IN THAT CERTAIN EASEMENT
RECORDED OCTOBER 6, 1980 IN BOOK 13776, PAGE 341 OF OFFICIAL RECORDS, COUNTY OF
ORANGE.

STANDARD PACIFIC CORP., A DELAWARE CORPORATION, OWNER

BY: [Signature] NAME CLINTON H. FULLEN II TITLE V.P., OPERATIONS
BY: [Signature] NAME KAREN SPARGO TITLE V.P. Sales & Marketing

DMB LADERA, LLC, A DELAWARE LIMITED LIABILITY COMPANY,
BENEFICIARY UNDER A DEED OF TRUST RECORDED JANUARY 8, 2002 AS
INSTRUMENT No. 20020015423 OF OFFICIAL RECORDS OF ORANGE COUNTY, CALIFORNIA
BY: RANCHO MISSION VIEJO, L.L.C., A DELAWARE LIMITED LIABILITY COMPANY,
AS AGENT AND/OR MANAGER.

BY: [Signature] NAME DONALD T. STRAHIN TITLE DIRECTOR
BY: [Signature] NAME Stephen C. Schrank TITLE Executive Vice President

STATE OF CALIFORNIA }
COUNTY OF ORANGE } SS
ON THIS 11th DAY OF JULY, 2002, BEFORE ME, KATHIEEN M VILLARI
PERSONALLY APPEARED CLINTON H. FULLEN II + KAREN SPARGO
PERSONALLY KNOWN TO ME (OR PROVED TO ME ON THE BASIS OF SATISFACTORY EVIDENCE) TO BE THE
PERSON(S) WHOSE NAME(S) IS/ARE SUBSCRIBED TO THE WITHIN INSTRUMENT AND ACKNOWLEDGED TO ME THAT
HE/SHE/ THEY EXECUTED THE SAME IN HIS/HER/ THEIR AUTHORIZED CAPACITY(IES), AND THAT BY
HIS/HER/ THEIR SIGNATURE(S) ON THE INSTRUMENT THE PERSON(S), OR THE ENTITY UPON BEHALF OF WHICH
THE PERSON(S) ACTED, EXECUTED THE INSTRUMENT.
MY PRINCIPAL PLACE OF BUSINESS
IS IN ORANGE COUNTY.
MY COMMISSION EXPIRES: 8-10-2003
WITNESS MY HAND:
[Signature]
(SIGNATURE)
NOTARY PUBLIC IN AND FOR SAID STATE
KATHIEEN M VILLARI
(PRINT NAME)

STATE OF CALIFORNIA }
COUNTY OF ORANGE } SS
ON THIS 24th DAY OF July, 2002, BEFORE ME, Tina T. Balen
PERSONALLY APPEARED Donald T. Strahin and Stephen C. Schrank
PERSONALLY KNOWN TO ME (OR PROVED TO ME ON THE BASIS OF SATISFACTORY EVIDENCE) TO BE THE
PERSON(S) WHOSE NAME(S) IS/ARE SUBSCRIBED TO THE WITHIN INSTRUMENT AND ACKNOWLEDGED TO ME THAT
HE/SHE/ THEY EXECUTED THE SAME IN HIS/HER/ THEIR AUTHORIZED CAPACITY(IES), AND THAT BY
HIS/HER/ THEIR SIGNATURE(S) ON THE INSTRUMENT THE PERSON(S), OR THE ENTITY UPON BEHALF OF WHICH
THE PERSON(S) ACTED, EXECUTED THE INSTRUMENT.
MY PRINCIPAL PLACE OF BUSINESS
IS IN Orange COUNTY.
MY COMMISSION EXPIRES: 8-29-04
WITNESS MY HAND:
[Signature]
(SIGNATURE)
NOTARY PUBLIC IN AND FOR SAID STATE
Tina T. Balen
(PRINT NAME)

SANTA MARGARITA WATER DISTRICT CERTIFICATE OF ACCEPTANCE:

THE UNDERSIGNED BEING THE DULY APPOINTED AGENT OF THE SANTA MARGARITA WATER
DISTRICT, A PUBLIC CORPORATION IN ORANGE COUNTY, CALIFORNIA, PURSUANT TO ITS
RESOLUTION NO. 88-10-2, DOES HEREBY ACCEPT ON BEHALF OF SAID DISTRICT THE
PIPELINE EASEMENTS FOR SEWER, WATER AND ACCESS PURPOSES, AS DEDICATED AND AS
SHOWN ON THIS TRACT MAP, BY AND BETWEEN THE SANTA MARGARITA WATER DISTRICT AND
STANDARD PACIFIC CORP., AND DOES HEREBY CERTIFY THAT THE GRANTEE CONSENTS TO THE
RECORDATION OF SAID TRACT MAP.

[Signature]
DANIEL R. FERONS, CHIEF ENGINEER
SANTA MARGARITA WATER DISTRICT

STATE OF CALIFORNIA }
COUNTY OF ORANGE } SS
ON THIS 31st DAY OF JULY, 2002, BEFORE ME, ANDREA M EVANS
PERSONALLY APPEARED DANIEL R. FERONS
PERSONALLY KNOWN TO ME (OR PROVED TO ME ON THE BASIS OF SATISFACTORY EVIDENCE) TO BE THE
PERSON(S) WHOSE NAME(S) IS/ARE SUBSCRIBED TO THE WITHIN INSTRUMENT AND ACKNOWLEDGED TO ME THAT
HE/SHE/ THEY EXECUTED THE SAME IN HIS/HER/ THEIR AUTHORIZED CAPACITY(IES), AND THAT BY
HIS/HER/ THEIR SIGNATURE(S) ON THE INSTRUMENT THE PERSON(S), OR THE ENTITY UPON BEHALF OF WHICH
THE PERSON(S) ACTED, EXECUTED THE INSTRUMENT.
MY PRINCIPAL PLACE OF BUSINESS
IS IN ORANGE COUNTY.
MY COMMISSION EXPIRES: 4-8-04
WITNESS MY HAND:
[Signature]
(SIGNATURE)
NOTARY PUBLIC IN AND FOR SAID STATE
ANDREA M EVANS
(PRINT NAME)

SURVEYOR'S STATEMENT:

I HEREBY STATE THAT THIS MAP CONSISTING OF FOUR (4) SHEETS, CORRECTLY
REPRESENTS A TRUE AND COMPLETE SURVEY AS SHOWN MADE IN NOVEMBER 2001;
WAS MADE BY ME OR UNDER MY DIRECTION; THAT THE MONUMENTS ARE OF THE
CHARACTER AND OCCUPY (OR WILL OCCUPY) THE POSITIONS INDICATED BY SAID
MAP; AND THAT SAID MONUMENTS ARE (OR WILL BE) SUFFICIENT TO ENABLE THE
SURVEY TO BE RETRACED.

[Signature]
JERRY L. USELTON, L.S. 5347
LICENSE EXPIRES 12/31/03




COUNTY SURVEYOR'S STATEMENT:

I HEREBY STATE THAT I HAVE EXAMINED THIS MAP AND FOUND IT TO BE
SUBSTANTIALLY IN CONFORMANCE WITH THE TENTATIVE MAP, AS FILED WITH,
AMENDED AND APPROVED BY THE ORANGE COUNTY SUBDIVISION COMMITTEE;
THAT ALL PROVISIONS OF THE SUBDIVISION MAP ACT AND COUNTY SUBDIVISION
REGULATIONS HAVE BEEN COMPLIED WITH AND I AM SATISFIED SAID MAP IS
TECHNICALLY CORRECT.

DATED THIS 9th DAY OF SEPTEMBER, 2002.

[Signature]
JOHN CANAS, COUNTY SURVEYOR
L.S. 4408, EXPIRATION DATE: 9/30/05

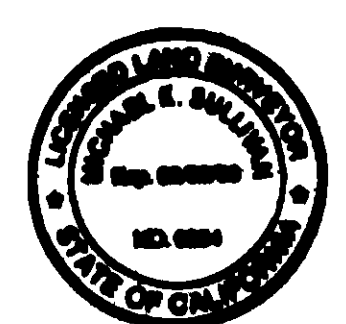

BY: MICHAEL K. SULLIVAN, DEPUTY
LS 6254 EXPIRES 6/30/06

COUNTY TREASURER-TAX COLLECTOR'S CERTIFICATE:

STATE OF CALIFORNIA }
COUNTY OF ORANGE } SS

I HEREBY CERTIFY THAT ACCORDING TO THE RECORDS OF MY OFFICE THERE ARE
NO LIENS AGAINST THE LAND COVERED BY THIS MAP OR ANY PART THEREOF FOR
UNPAID STATE, COUNTY, MUNICIPAL OR LOCAL TAXES OR SPECIAL ASSESSMENTS
COLLECTED AS TAXES, EXCEPT TAXES OR SPECIAL ASSESSMENTS COLLECTED AS
TAXES NOT YET PAYABLE.
AND DO ALSO CERTIFY TO THE RECORDER OF ORANGE COUNTY THAT THE
PROVISIONS OF THE SUBDIVISION MAP ACT HAVE BEEN COMPLIED WITH
REGARDING DEPOSITS TO SECURE THE PAYMENT OF TAXES OR SPECIAL
ASSESSMENTS COLLECTED AS TAXES ON THE LAND COVERED BY THIS MAP.

DATED THIS 8th DAY OF August, 2002

JOHN M. W. MOORLACH COUNTY TREASURER-TAX COLLECTOR BY: [Signature] DEPUTY TREASURER-TAX COLLECTOR

CLERK OF THE BOARD OF SUPERVISOR'S CERTIFICATE:


STATE OF CALIFORNIA }
COUNTY OF ORANGE } SS

I HEREBY CERTIFY THAT THIS MAP WAS PRESENTED FOR APPROVAL TO THE
BOARD OF SUPERVISORS OF ORANGE COUNTY AT A REGULAR MEETING
THEREOF HELD ON THE 24th DAY OF September, 2002,
AND THAT THEREUPON SAID BOARD DID, BY AN ORDER DULY PASSED AND ENTERED,
APPROVE SAID MAP AND DID ACCEPT THE EASEMENTS FOR SIDEWALK PURPOSES AS
DEDICATED.

WE ALSO HEREBY ABANDON, PURSUANT TO SECTION 66499.20 1/2 OF THE
SUBDIVISION MAP ACT, ALL PUBLIC STREETS AND PUBLIC EASEMENTS WITHIN THE
BOUNDARY OF THIS MAP WHICH WERE ACQUIRED BY THE COUNTY OF ORANGE PER
THE MAP OF TRACT No. 16157, FILED IN BOOK 813 AT PAGES 1 THROUGH 9,
INCLUSIVE, OF MISCELLANEOUS MAPS, IN THE OFFICE OF THE RECORDER OF
ORANGE COUNTY, CALIFORNIA, SAID EASEMENTS NOT SHOWN ON THIS MAP.

DATED THIS 24th DAY OF September, 2002.

[Signature]
DARLENE J. BLOOM
CLERK OF THE BOARD OF SUPERVISORS
OF ORANGE COUNTY, CALIFORNIA

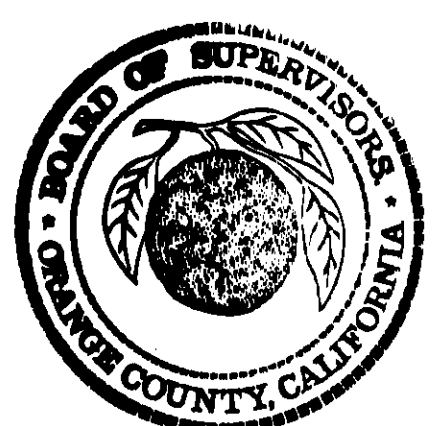

SIGNATURE OMISSION NOTES:

IN ACCORDANCE WITH THE PROVISIONS OF SECTION 66436(a)(3) OF THE
SUBDIVISION MAP ACT, THE FOLLOWING SIGNATURES HAVE BEEN OMITTED:

- 1.) LADERA DEVELOPMENT COMPANY, L.L.C. HOLDER OF OIL, GAS, MINERAL, AND
WATER RIGHTS RECORDED AS INSTRUMENT NO. 19960624029 OF OFFICIAL
RECORDS.
- 2.) LADERA RANCH MAINTENANCE CORPORATION, HOLDER OF AN EASEMENT
RECORDED AS INSTRUMENT NO. 20020349116 OF OFFICIAL RECORDS.

SHEET 2 OF 4 SHEETS

3.388 ACRES
22 NUMBERED LOTS AND
LETTERED LOTS "A" THROUGH "C"
DATE OF SURVEY: NOVEMBER 2001
(ALL OF VESTING TENTATIVE
TRACT No. 16270)

TRACT NO. 16270

IN THE UNINCORPORATED TERRITORY OF THE COUNTY OF ORANGE, STATE OF CALIFORNIA.

FUSCOE ENGINEERING, INC.
JERRY L. USELTON, L.S. 5347 NOVEMBER 2001

BASIS OF BEARINGS:

THE BEARINGS SHOWN HEREON ARE BASED ON THE BEARING BETWEEN O.C.S. HORIZONTAL CONTROL STATION GPS No. 1417 AND STATION GPS No. 1448 BEING NORTH 10°48'13" EAST PER RECORDS ON FILE IN THE OFFICE OF THE ORANGE COUNTY SURVEYOR.

DATUM STATEMENT:

COORDINATES SHOWN ARE BASED ON THE CALIFORNIA COORDINATE SYSTEM (CCS83), ZONE VI, 1983 NAD, (1991.35 EPOCH OSC GPS ADJUSTMENT). ALL DISTANCES SHOWN ARE GROUND, UNLESS OTHERWISE NOTED, TO OBTAIN GRID DISTANCES MULTIPLY GROUND DISTANCE BY 0.999948295

MONUMENT NOTES:

● INDICATES FOUND OCS GPS MONUMENT AS NOTED:

N=2146790.819
E=6142602.585
FOUND 2 1/2" IRON PIPE WITH 2" OCS BRASS CAP STAMPED "GPS
1448 9-95" PER RECORD OF SURVEY 97-1086, R.S.B. 167/26-28 AND
RECORDS ON FILE IN THE ORANGE COUNTY SURVEYORS OFFICE.

N=2141450.558
E=6141583.535
FOUND 2 1/2" IRON PIPE WITH 2" OCS BRASS CAP STAMPED "GPS
1417 9-95" PER TRACT No. 15884, M.M. 784/33-44 AND RECORDS
ON FILE IN THE ORANGE COUNTY SURVEYORS OFFICE.

■ INDICATES 1" I.P. TAGGED "L.S. 5347" OR SPIKE AND WASHER STAMPED "L.S. 5347" OR LEAD AND TAG "L.S. 5347" TO BE SET PRIOR TO RECORDATION OF THIS TRACT

○ INDICATES 1" I.P. TAGGED "L.S. 5557" OR SPIKE AND WASHER STAMPED "L.S. 5557" OR LEAD AND TAG "L.S. 5557" TO BE SET PER TRACT 16157, M.M. 813/1-9.

LEAD AND TAG "L.S. 5347" TO BE SET ON A 0.25 FOOT OFFSET IN TOP OF CURB OR IN SIDEWALK ALONG PROJECTED SIDE LOT LINE (UNLESS OTHERWISE NOTED) WITHIN 90 DAYS AFTER ACCEPTANCE OF IMPROVEMENTS.

NO MONUMENTATION WILL BE SET AT BC's, EC's, PCC's, OR PRC's OF DEDICATED PUBLIC STREET SIDE LINES UNLESS OTHERWISE NOTED.

SURVEYOR'S NOTES:

DATA SHOWN ALONG THIS TRACT BOUNDARY ARE MEASURED AND RECORD PER TRACT No. 16157, M.M. 813/1-9, UNLESS NOTED OTHERWISE.

ALL LETTERED LOTS SHOWN HEREON ARE NOT SEPARATE BUILDING SITES. LOTS "A" AND "C" ARE FOR PRIVATE DRIVEWAY AND PARKING PURPOSES AND ARE TO BE CONVEYED TO THE APPROPRIATE HOMEOWNERS ASSOCIATION. LOT "B" IS FOR PEDESTRIAN ACCESS AND LANDSCAPE PURPOSES AND IS TO BE CONVEYED TO THE APPROPRIATE HOMEOWNERS ASSOCIATION.

NOTE:

ALL COMMERCIAL STRUCTURES OVER 6,000 SQUARE FEET; ALL MULTIFAMILY RESIDENTIAL STRUCTURES; ALL DETACHED, SINGLE-FAMILY STRUCTURES EXCEEDING 5,500 SQUARE FEET, AND, ALL STRUCTURES EXCEEDING FIRE AUTHORITY ACCESS REQUIREMENTS SHALL BE PROTECTED BY AN AUTOMATIC SPRINKLER SYSTEM, IN A MANNER MEETING THE APPROVAL OF THE FIRE CHIEF.

NOTE:

THE PRIVATE STREETS CONSTRUCTED WITHIN THIS MAP SHALL BE OWNED, OPERATED AND MAINTAINED BY THE DEVELOPER, SUCCESSORS OR ASSIGNS. THE COUNTY OF ORANGE SHALL HAVE NO RESPONSIBILITY THEREFORE UNLESS PURSUANT TO APPROPRIATE SECTIONS OF THE STREETS AND HIGHWAYS CODE OF THE STATE OF CALIFORNIA, THE SAID PRIVATE STREETS HAVE BEEN ACCEPTED INTO THE COUNTY ROAD SYSTEM BY APPROPRIATE RESOLUTION OF THE ORANGE COUNTY BOARD OF SUPERVISORS.

NOTE:

THE PROPERTY IS "TOTALLY EXCLUDED" FROM A "SPECIAL FIRE PROTECTION AREA"



HIGH FIRE HAZARD AREA NOTE:

THE LOTS SHOWN ON THIS MAP ARE IN A HIGH FIRE HAZARD AREA DUE TO WLDLAND EXPOSURE.


EASEMENT NOTES:

(A) DENOTES THE EASEMENT FOR WATER, SEWER, AND ACCESS PURPOSES DEDICATED TO THE SANTA MARGARITA WATER DISTRICT HEREON.

(B) DENOTES THE EASEMENT FOR SIDEWALK PURPOSES DEDICATED TO THE COUNTY OF ORANGE HEREON.

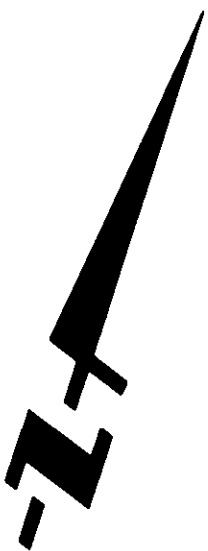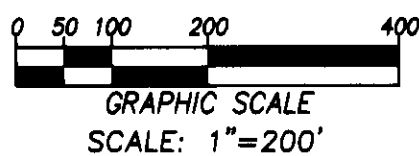

VICINITY MAP AND OCS GPS CONTROL SCHEME

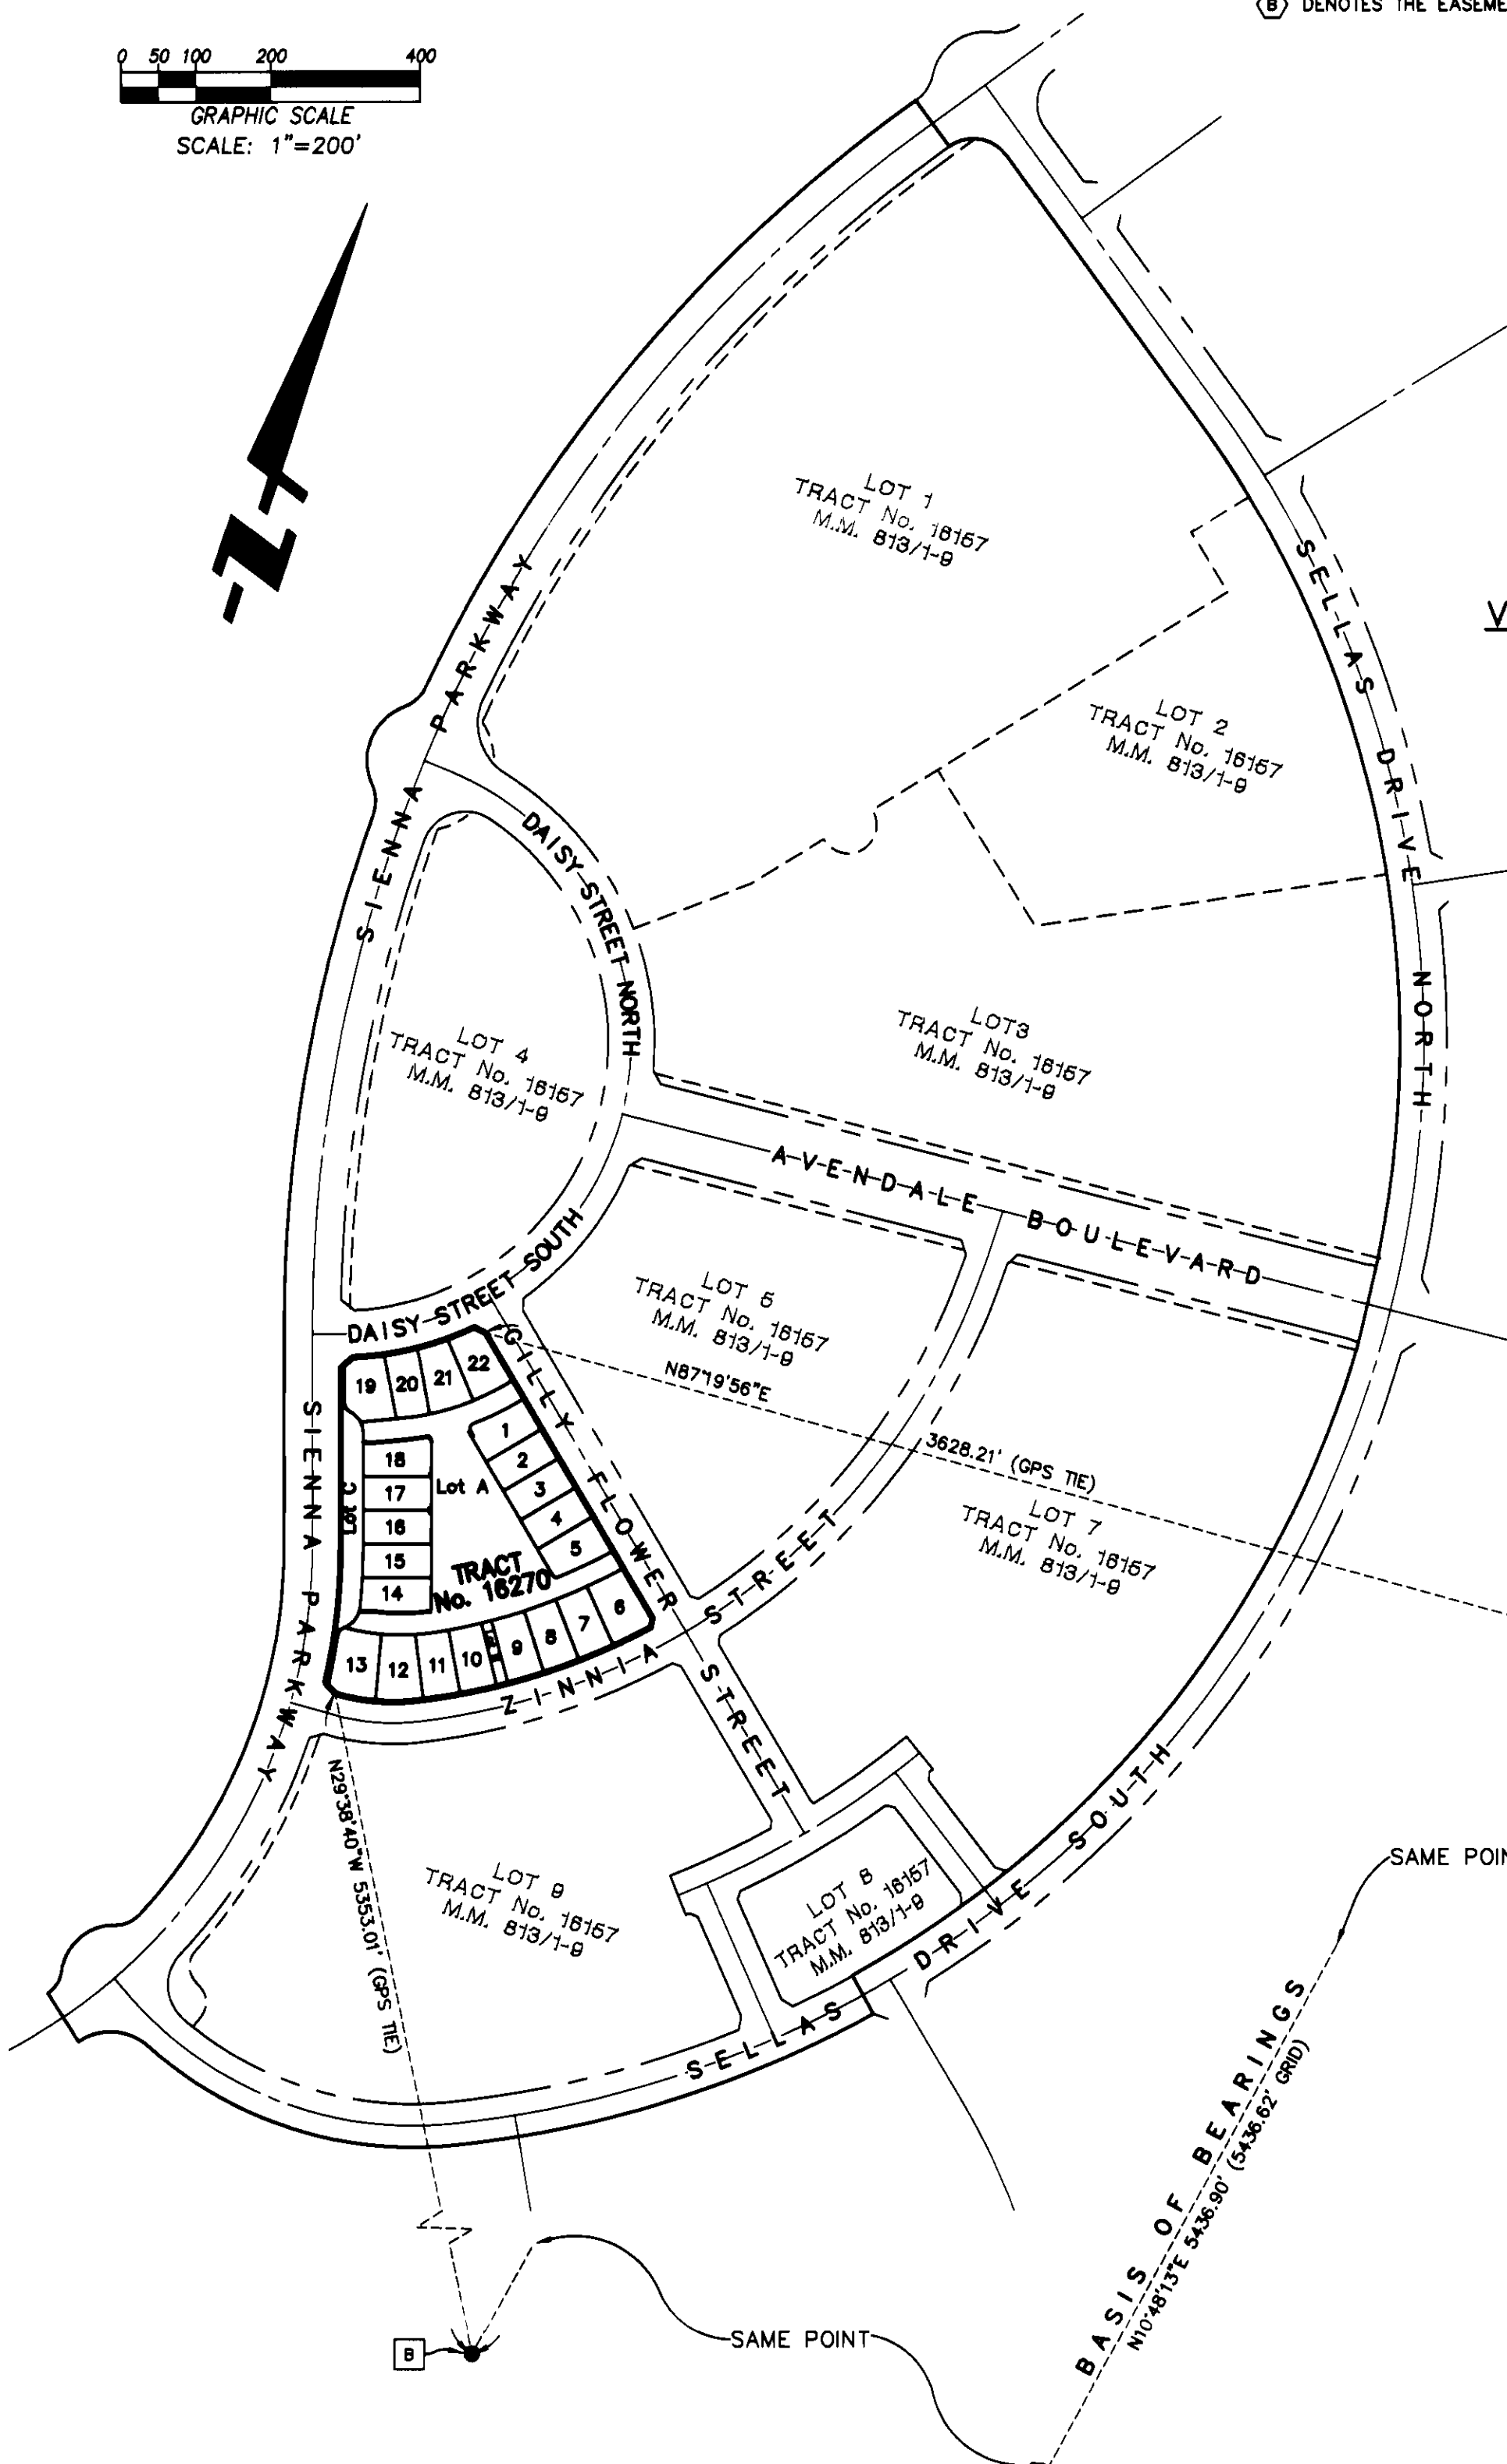


SHEET 3 OF 4 SHEETS
3.388 ACRES
22 NUMBERED LOTS AND
LETTERED LOTS "A" THROUGH "C"
DATE OF SURVEY: NOVEMBER 2001
(ALL OF VESTING TENTATIVE
TRACT No. 16270)

TRACT NO. 16270


IN THE UNINCORPORATED TERRITORY OF THE COUNTY OF ORANGE, STATE OF CALIFORNIA.
FUSCOE ENGINEERING, INC.
JERRY L. USELTON, L.S. 5347 NOVEMBER 2001

TRACT AND LOT BOUNDARY SHEET
SEE SHEET 4 FOR EASEMENT DATA NOT SHOWN HEREON

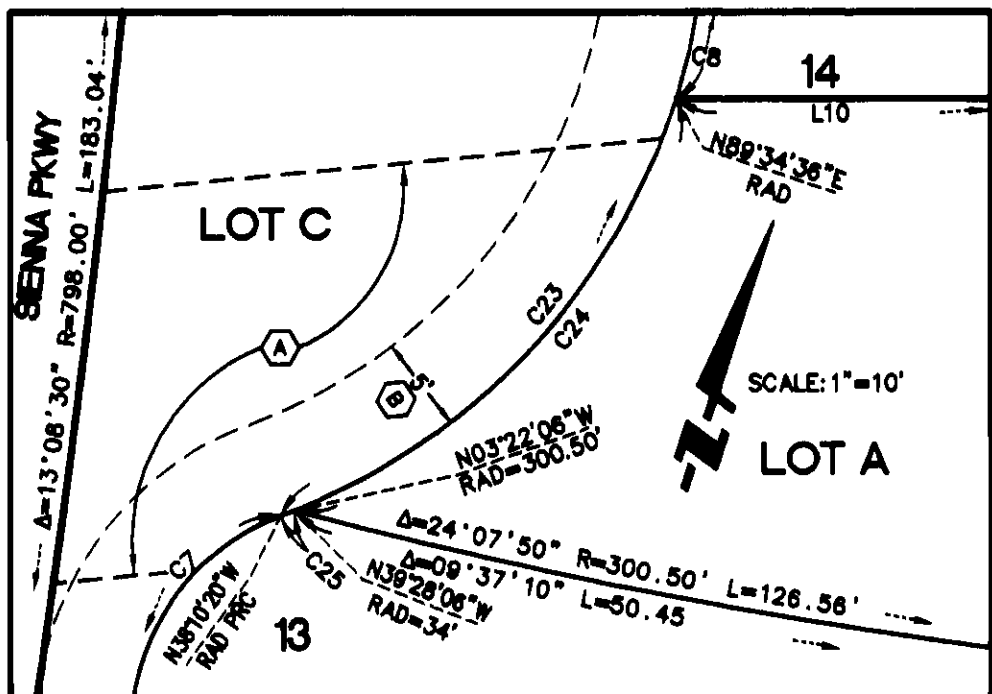

NOTE:

SEE SHEET 2 FOR OCS GPS BOUNDARY CONTROL MAP, BASIS OF BEARINGS, DATUM STATEMENT, MONUMENT NOTES, SURVEYOR'S NOTES, HIGH FIRE HAZARD AREA NOTE, EASEMENT NOTES, AND NOTES.

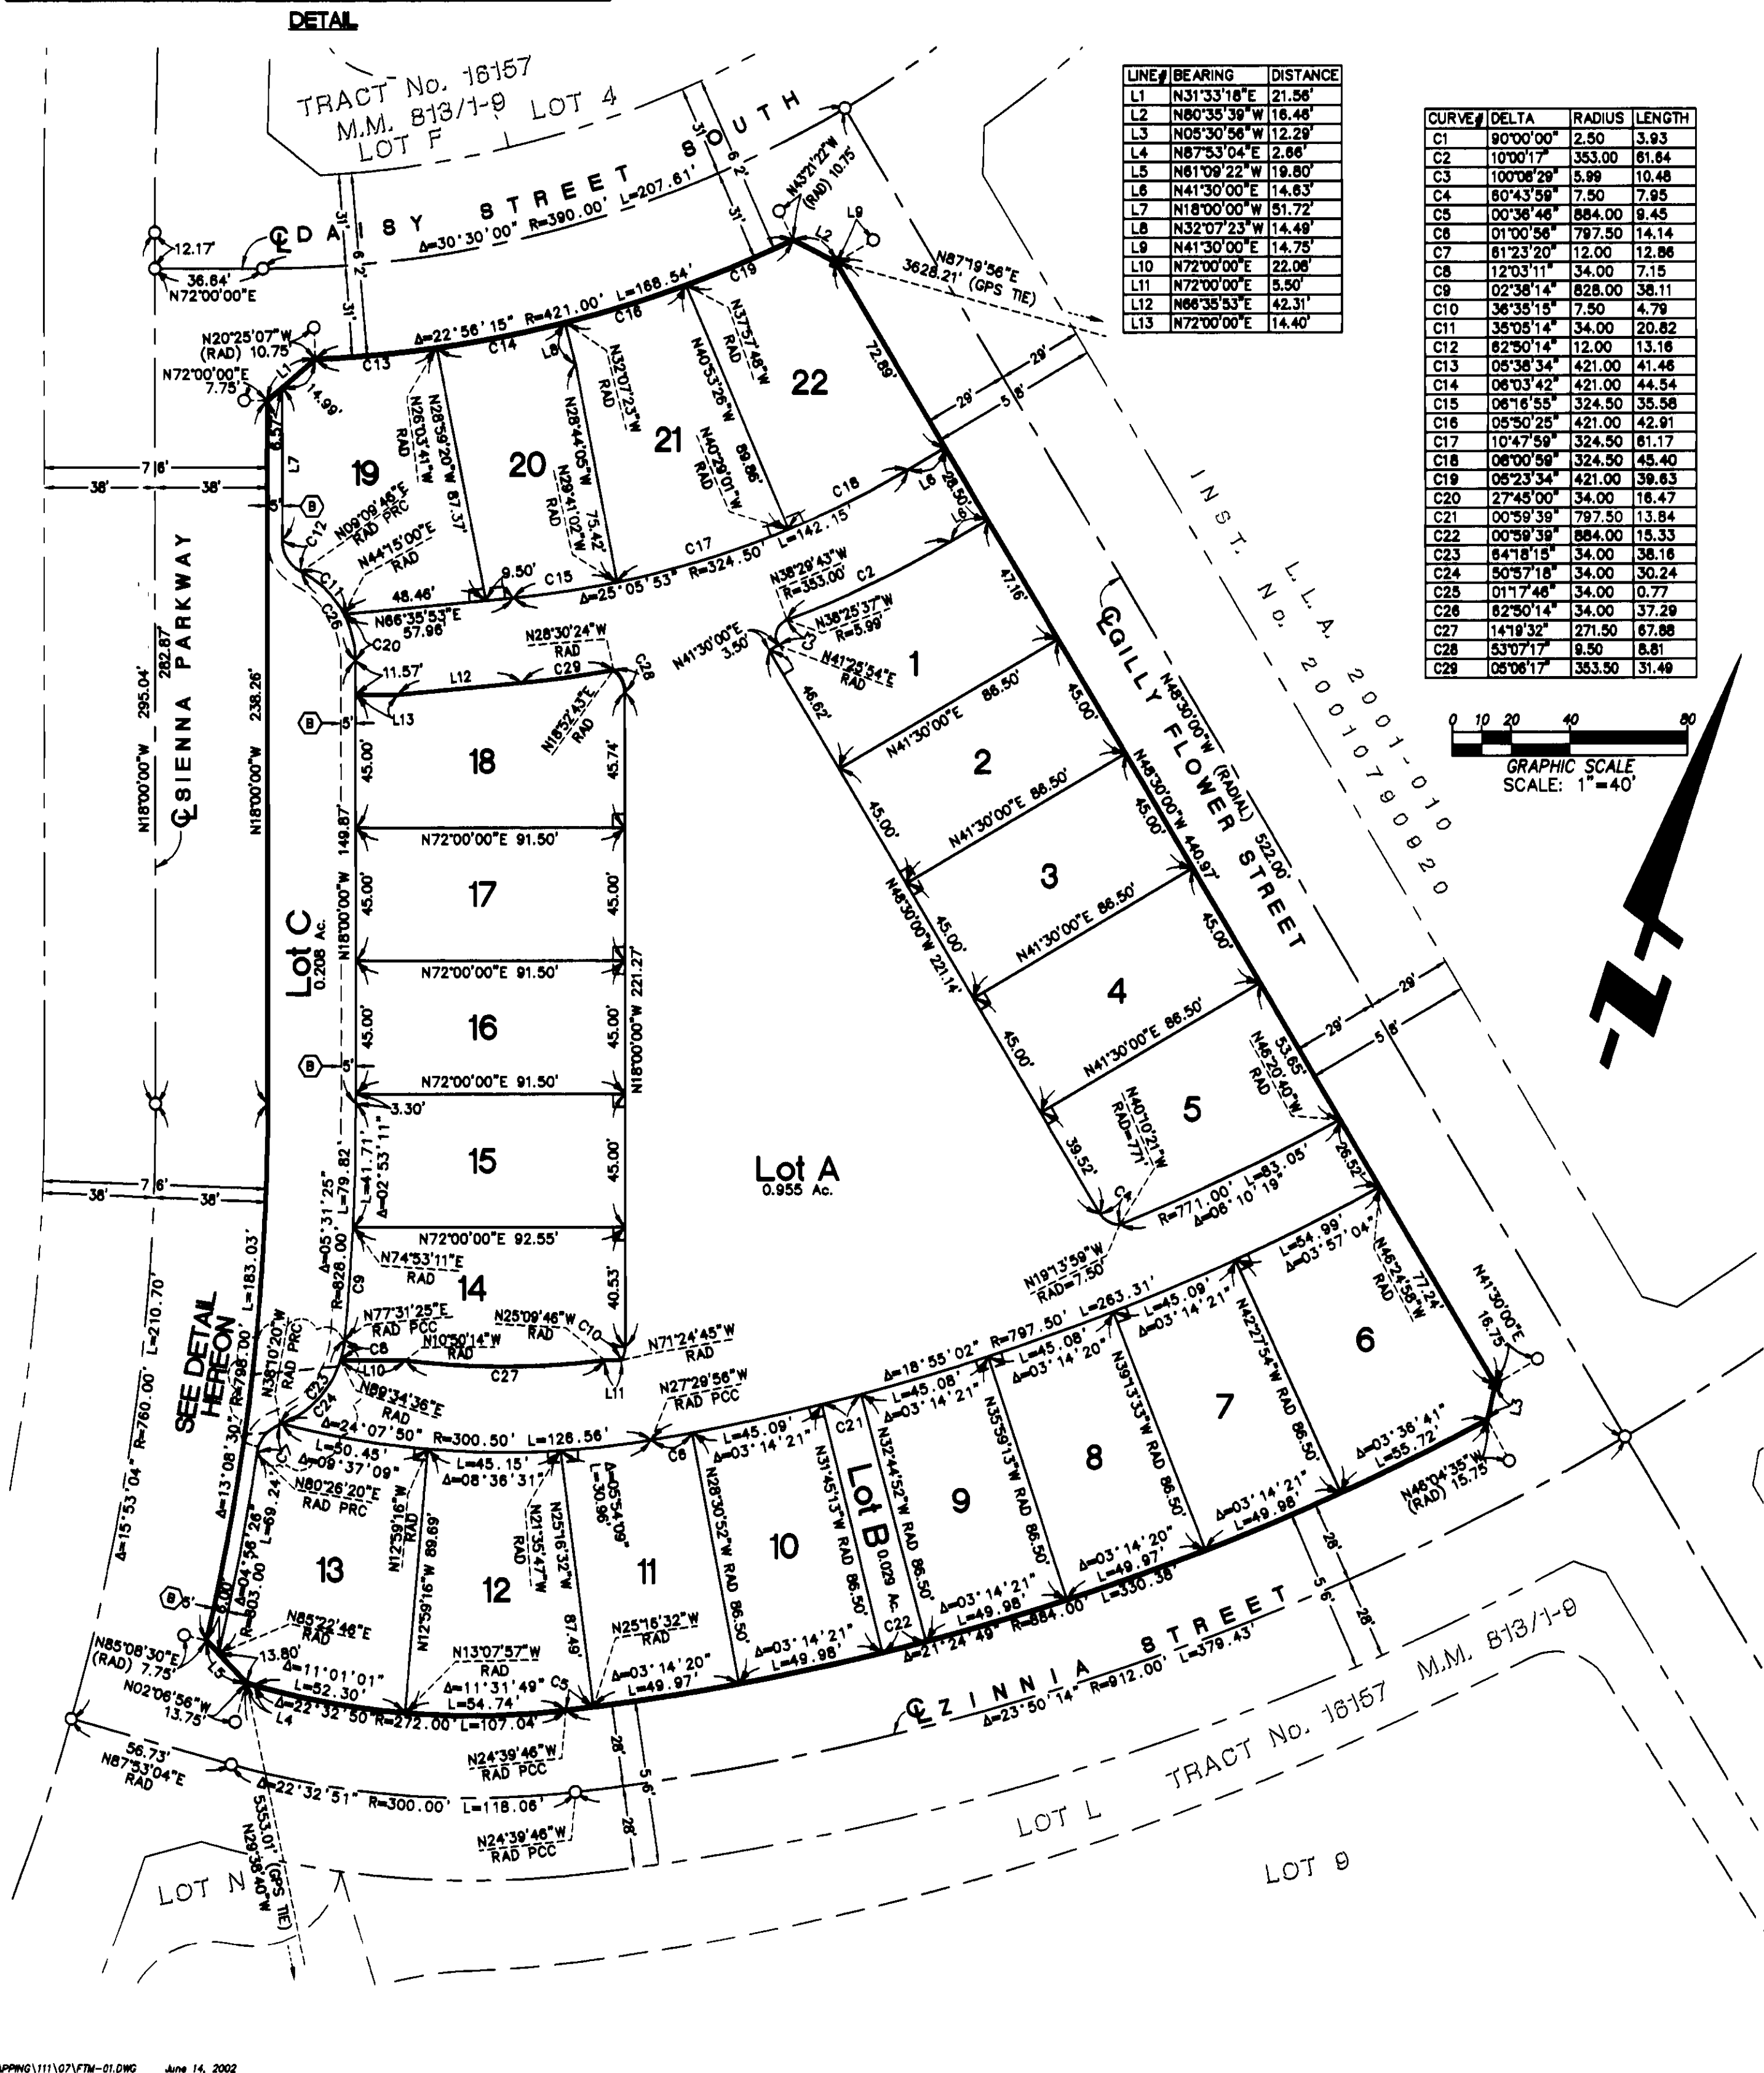

LINE#	BEARING	DISTANCE
L1	N31°33'18"E	21.56'
L2	N80°35'39"W	16.48'
L3	N05°30'56"W	12.29'
L4	N87°53'04"E	2.66'
L5	N81°09'22"W	19.80'
L6	N41°30'00"E	14.83'
L7	N18°00'00"W	51.72'
L8	N32°07'23"W	14.48'
L9	N41°30'00"E	14.75'
L10	N72°00'00"E	22.08'
L11	N72°00'00"E	5.50'
L12	N66°35'53"E	42.31'
L13	N72°00'00"E	14.40'

CURVE#	DELTA	RADIUS	LENGTH
C1	90°00'00"	2.50	3.93
C2	10°00'17"	353.00	81.84
C3	100°06'29"	5.99	10.48
C4	80°43'59"	7.50	7.95
C5	00°36'46"	884.00	9.45
C6	01°00'56"	797.50	14.14
C7	81°23'20"	12.00	12.86
C8	12°03'11"	34.00	7.15
C9	02°38'14"	828.00	38.11
C10	36°35'15"	7.50	4.79
C11	35°05'14"	34.00	20.82
C12	82°50'14"	12.00	13.16
C13	08°38'34"	421.00	41.46
C14	06°03'42"	421.00	44.54
C15	06°16'55"	324.50	35.58
C16	05°50'25"	421.00	42.91
C17	10°47'59"	324.50	61.17
C18	06°00'59"	324.50	45.40
C19	05°23'34"	421.00	39.63
C20	27°45'00"	34.00	18.47
C21	00°59'39"	797.50	13.84
C22	00°59'39"	884.00	15.33
C23	84°18'15"	34.00	38.16
C24	50°57'18"	34.00	30.24
C25	01°17'46"	34.00	0.77
C26	82°50'14"	34.00	37.29
C27	14°19'32"	271.50	67.88
C28	53°07'17"	9.50	8.81
C29	05°06'17"	353.50	31.49



SHEET 4 OF 4 SHEETS

3.388 ACRES
22 NUMBERED LOTS AND
LETTERED LOTS "A" THROUGH "C"
DATE OF SURVEY: NOVEMBER 2001
(ALL OF VESTING TENTATIVE
TRACT No. 16270)

TRACT NO. 16270

IN THE UNINCORPORATED TERRITORY OF THE COUNTY OF ORANGE, STATE OF CALIFORNIA.

FUSCOE ENGINEERING, INC.

JERRY L. USELTON, L.S. 5347 NOVEMBER 2001

NOTE:










SEE SHEET 2 FOR OCS GPS BOUNDARY CONTROL MAP, BASIS OF BEARINGS,
DATUM STATEMENT, MONUMENT NOTES, SURVEYOR'S NOTES,
HIGH FIRE HAZARD AREA NOTE, EASEMENT NOTES, AND NOTES.

EASEMENT DATA SHEET

SEE SHEET 3 FOR TRACT AND LOT BOUNDARY DATA NOT SHOWN HEREON

LINE#	BEARING	DISTANCE
L1	N41°30'00"E	4.00'
L2	N48°30'00"W	11.83'
L3	N41°30'00"E	3.50'
L4	N23°24'07"W	4.00'
L5	N66°35'53"E	12.04'
L6	N66°39'25"E	7.57'

CURVE#	DELTA	RADIUS	LENGTH
C1	100°08'29"	5.99	10.48
C2	23°38'13"	5.99	2.47
C3	76°30'16"	5.99	8.00
C4	04°48'24"	300.50	25.30
C5	01°04'46"	300.50	5.66
C6	00°51'10"	300.50	4.47
C7	07°45'21"	300.50	40.68
C8	25°01'43"	12.00	5.24
C9	00°51'27"	300.50	4.50
C10	06°45'43"	300.50	45.85
C11	09°39'07"	324.50	54.87
C12	01°06'52"	324.50	8.50
C13	00°58'18"	324.50	5.50
C14	07°02'43"	324.50	39.90
C15	01°17'48"	34.00	0.77
C16	47°12'48"	34.00	28.02
C17	03°44'28"	34.00	2.22
C18	36°21'38"	12.00	7.82
C19	05°05'03"	798.00	70.81
C20	01°28'19"	798.00	20.50
C21	06°35'09"	798.00	91.73
C22	61°23'20"	12.00	12.86

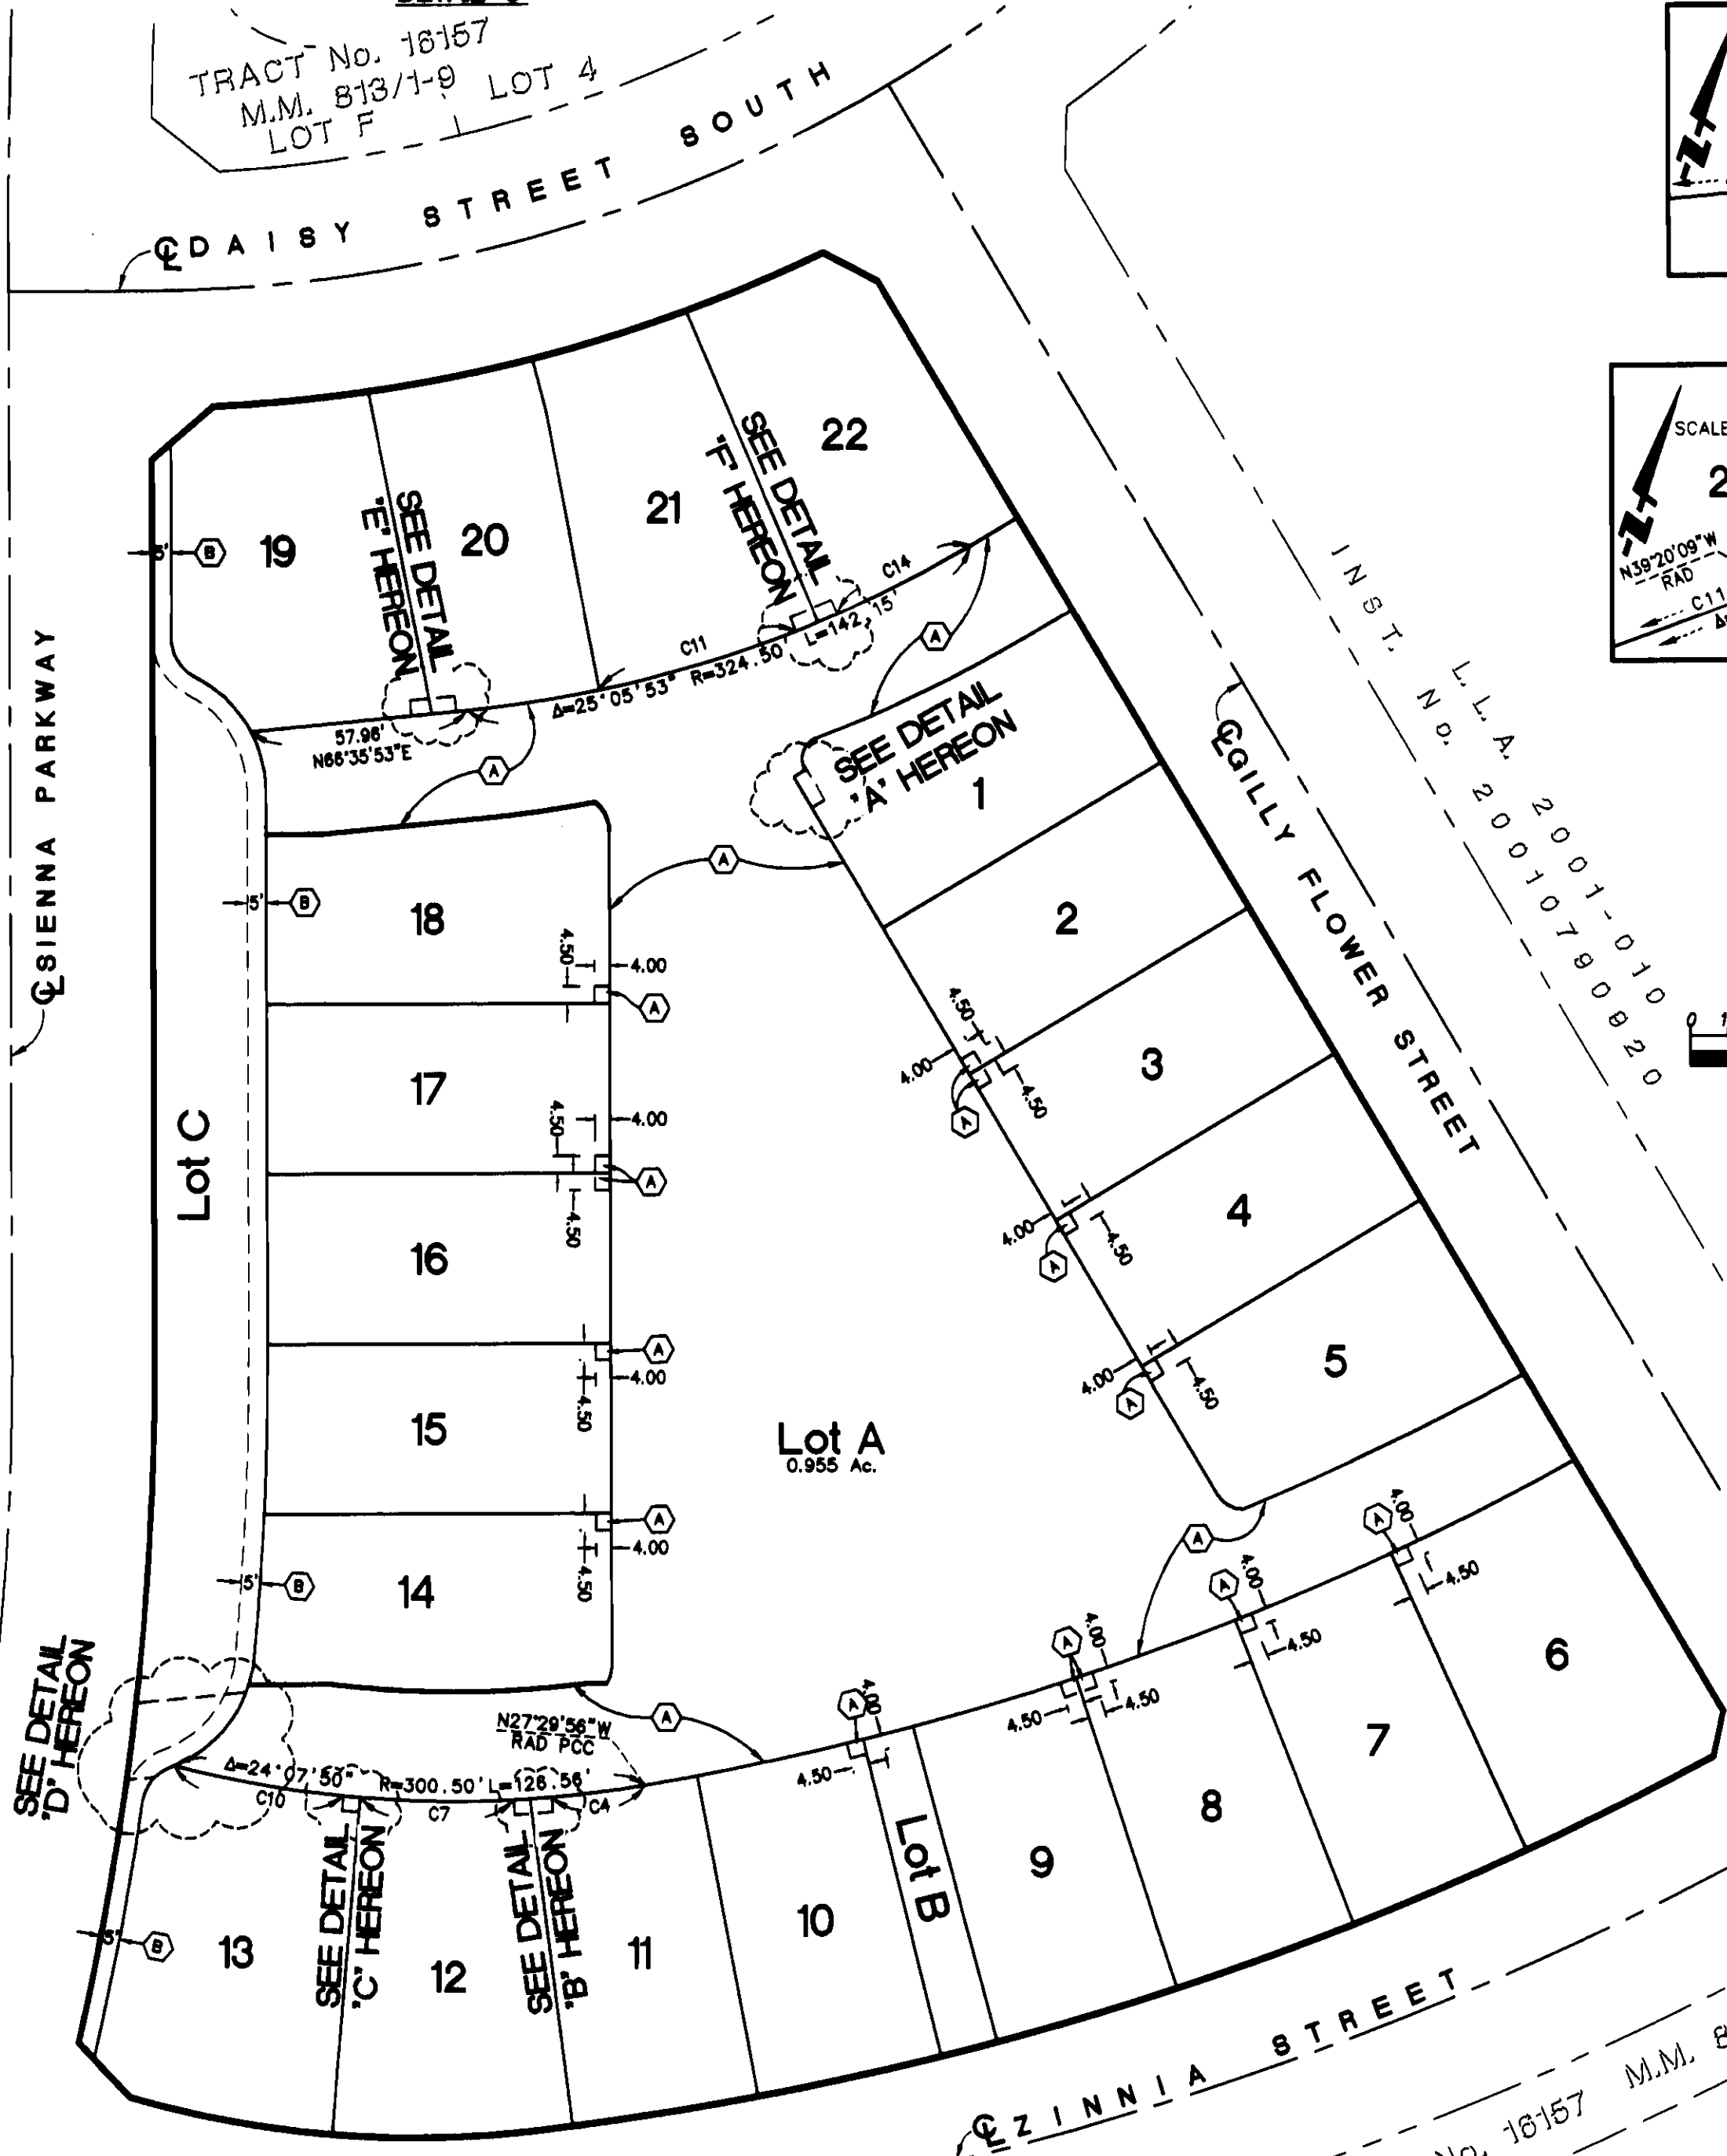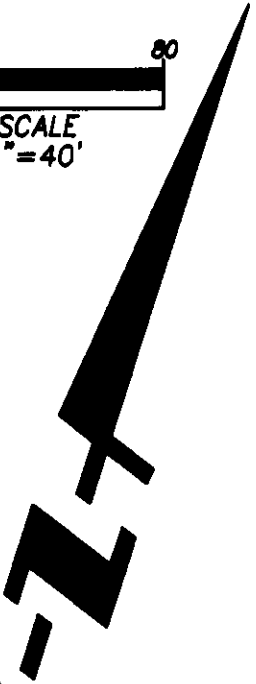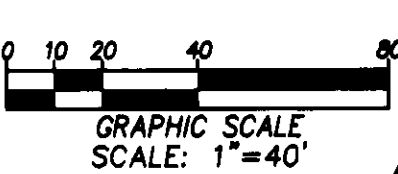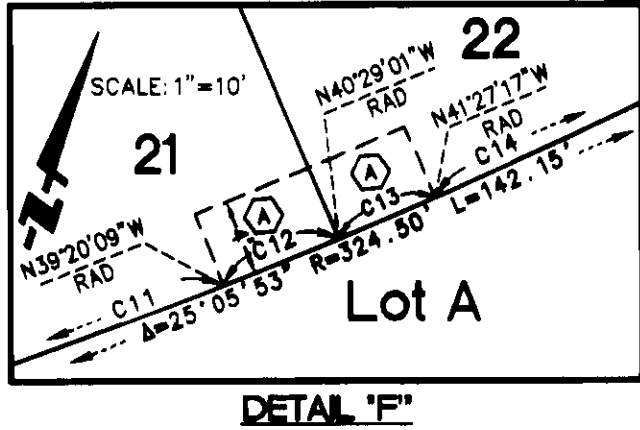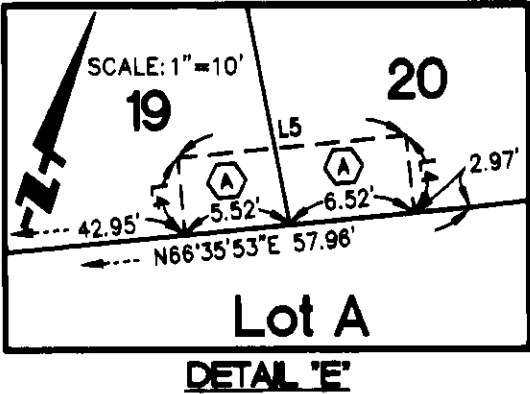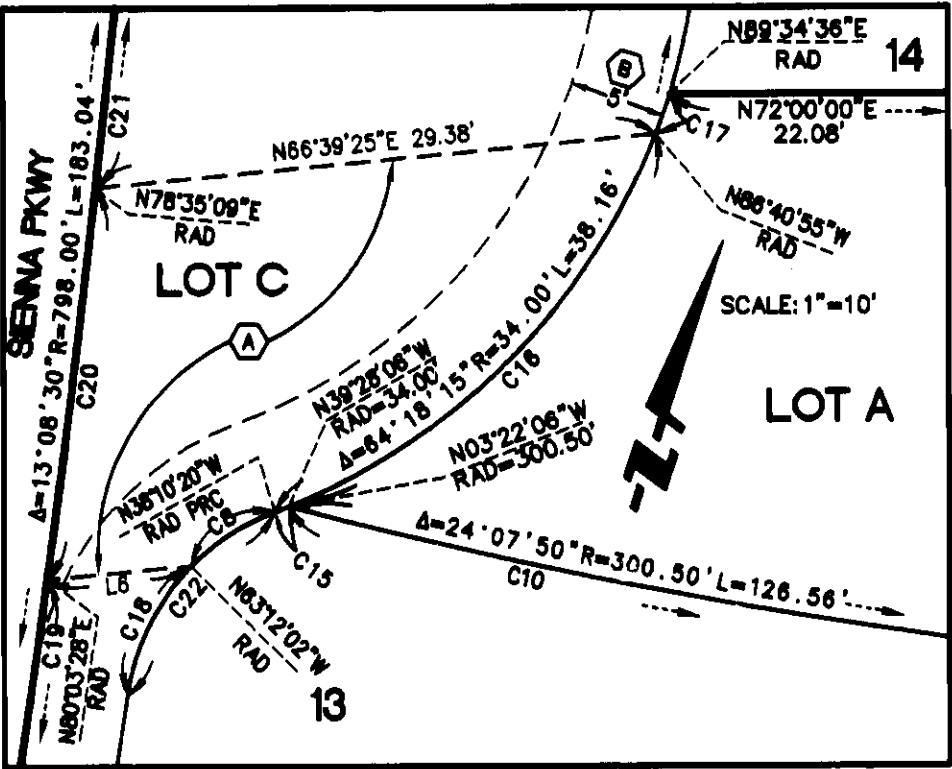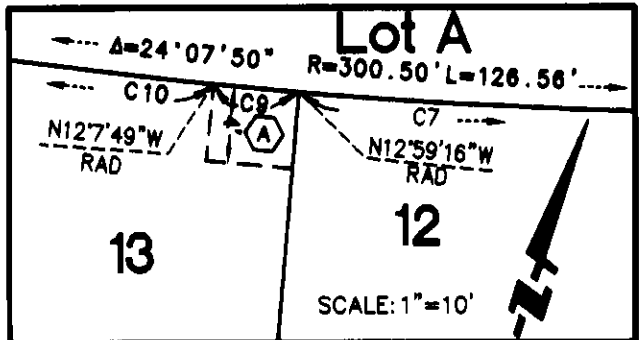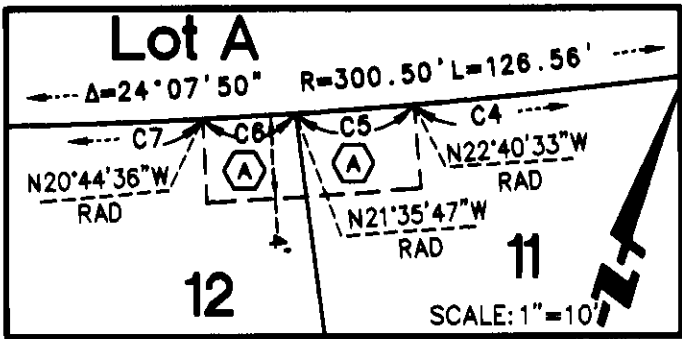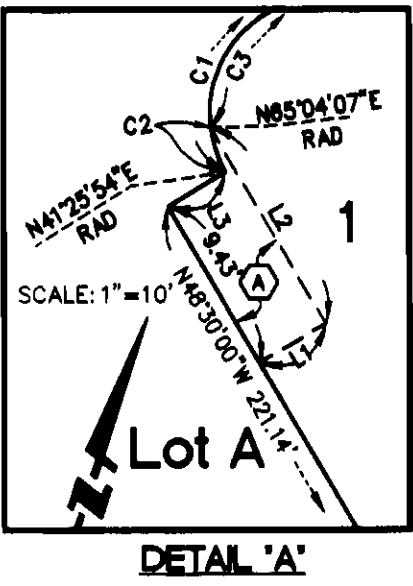

SMWD EASEMENT NOTE:

THE SIDELINES OF THE SMWD EASEMENTS OVER LOTS 2 THROUGH 10, 14 THROUGH 18, AND LOT "B" ARE PARALLEL WITH THE LOT LINES AT THE INDICATED OFFSET. THE SIDELINES OF THE SMWD EASEMENTS OVER LOTS 1, 11 THROUGH 13, 19 THROUGH 22, AND LOT "E" ARE AS SHOWN IN THE DETAILS.