

FINAL UNIT OF VESTING
TENTATIVE TRACT NO. 16271DATE OF SURVEY:
JANUARY 1999IN THE UNINCORPORATED TERRITORY OF ORANGE COUNTY, CALIFORNIA
BEING A SUBDIVISION OF A PORTION OF PARCEL 1 OF LOT LINE ADJUSTMENT NO. LL 98-026
AS SHOWN ON EXHIBIT "B" ATTACHED TO THAT CERTAIN DOCUMENT RECORDED NOVEMBER 21,
1996 AS INSTRUMENT NO. 19960587414 OF OFFICIAL RECORDS, RECORDS OF ORANGE COUNTY,
CALIFORNIA.

JULY 2002

JAMES F. GILLEN, L.S. 5557

HUITT-ZOLIARS

10 NUMBERED LOTS AND 34 LETTERED LOTS

119.147 ACRES

ACCEPTED AND FILED AT THE
REQUEST OF
FIRST AMERICAN TITLE INSURANCE CO.DATE FEBRUARY 27, 2003
TIME 10:16AM FEE \$ 29.00
INSTRUMENT NO. 2003000216298
BOOK 839 PAGE 34-45 m/nBY TOM DALY
COUNTY CLERK-RECORDER
DEPUTY

OWNERSHIP CERTIFICATE:

WE, THE UNDERSIGNED, BEING ALL PARTIES HAVING ANY RECORD TITLE INTEREST IN THE
LAND COVERED BY THIS MAP, DO HEREBY CONSENT TO THE PREPARATION AND RECORDATION
OF SAID MAP, AS SHOWN WITHIN THE DISTINCTIVE BORDER LINE. WE ALSO HEREBY DEDICATE
TO THE PUBLIC FOR STREET PURPOSES: NARROW CANYON ROAD AND ETHEREAL STREET.

WE ALSO HEREBY DEDICATE TO THE COUNTY OF ORANGE:

- (1) THE EASEMENT FOR SIDEWALK PURPOSES AS SHOWN ON SAID MAP.
- (2) THE EASEMENTS FOR STORM DRAIN PURPOSES AS SHOWN ON SAID MAP.
- (3) THE SCENIC PRESERVATION EASEMENTS OVER ALL OF LOTS B, F AND H AS SHOWN ON SAID MAP FOR
THE PURPOSES AND SUBJECT TO THE SAME CONDITIONS AND LIMITATIONS AS SHOWN IN THAT
CERTAIN EASEMENT RECORDED SEPTEMBER 19, 1991 AS DOCUMENT 91-511820 OF OFFICIAL RECORDS.

PURSUANT TO SECTION 7050 OF THE GOVERNMENT CODE, WE HEREBY IRREVOCABLY OFFER
TO DEDICATE TO THE COUNTY OF ORANGE LOT 4 IN FEE SIMPLE FOR LOCAL PARK
PURPOSES, TOGETHER WITH THE RIGHT TO GRANT EASEMENTS FOR PUBLIC UTILITIES
OR OTHER ESSENTIAL PURPOSES.

DMB LADERA, L.L.C., A DELAWARE LIMITED LIABILITY COMPANY.

BY: RANCHO MISSION VIEJO, L.L.C., A DELAWARE LIMITED LIABILITY COMPANY,
AS AGENT AND/OR MANAGER.BY: Thomas V. Staley
PRINT NAME: Thomas V. Staley
PRINT TITLE: V.P. DevelopmentBY: Stephen C. Schrank
PRINT NAME: Stephen C. Schrank
PRINT TITLE: Executive Vice President

SURVEYOR'S STATEMENT:

THIS MAP WAS PREPARED BY ME OR UNDER MY DIRECTION AND IS BASED UPON A FIELD
SURVEY IN CONFORMANCE WITH THE REQUIREMENTS OF THE SUBDIVISION MAP ACT AND
LOCAL ORDINANCES AT THE REQUEST OF RANCHO MISSION VIEJO, LLC ON MARCH 2002.
I HEREBY STATE THAT ALL MONUMENTS ARE OF THE CHARACTER AND OCCUPY THE
POSITIONS INDICATED, OR THAT THEY WILL BE SET IN SUCH POSITIONS; AND THAT SAID
MONUMENTS ARE SUFFICIENT TO ENABLE THE SURVEY TO BE RETRACED. I HEREBY STATE
THAT THIS FINAL MAP SUBSTANTIALLY CONFORMS TO THE CONDITIONALLY APPROVED TENTATIVE MAP.JAMES F. GILLEN
L.S. 5557
EXPIRATION DATE: 9/30/05

COUNTY SURVEYOR'S STATEMENT:

I HEREBY STATE THAT I HAVE EXAMINED THIS MAP AND HAVE FOUND IT TO BE
SUBSTANTIALLY IN CONFORMANCE WITH THE TENTATIVE MAP AS FILED WITH, AMENDED AND
APPROVED BY THE ORANGE COUNTY SUBDIVISION COMMITTEE; THAT ALL PROVISIONS OF THE
SUBDIVISION MAP ACT AND COUNTY SUBDIVISION REGULATIONS HAVE BEEN COMPLIED WITH
AND I AM SATISFIED SAID MAP IS TECHNICALLY CORRECT.DATED THIS 7TH DAY OF FEBRUARY, 2003.BY: Michael K. Sullivan
JOHN CANAS, COUNTY SURVEYOR
LS 4408 EXPIRATION DATE: 09-30-05 BY: MICHAEL K. SULLIVAN, DEPUTY
LS 6254 EXPIRES 03/06

COUNTY TREASURER-TAX COLLECTOR'S CERTIFICATE:

STATE OF CALIFORNIA)
COUNTY OF ORANGE)SSI HEREBY CERTIFY THAT ACCORDING TO THE RECORDS OF MY OFFICE THERE ARE NO LIENS
AGAINST THE LAND COVERED BY THIS MAP OR ANY PART THEREOF FOR UNPAID STATE,
COUNTY, MUNICIPAL OR LOCAL TAXES OR SPECIAL ASSESSMENTS COLLECTED AS TAXES,
EXCEPT TAXES OR SPECIAL ASSESSMENTS COLLECTED AS TAXES NOT YET PAYABLE.AND DO ALSO HEREBY CERTIFY TO THE RECORDER OF ORANGE COUNTY THAT THE PROVISIONS
OF THE SUBDIVISION MAP ACT HAVE BEEN COMPLIED WITH REGARDING DEPOSITS TO SECURE
THE PAYMENT OF TAXES OR SPECIAL ASSESSMENTS COLLECTED AS TAXES ON THE LAND
COVERED BY THIS MAP.DATED THIS 6th DAY OF January, 2003.BY: John M.W. Moorlach
JOHN M.W. MOORLACH
COUNTY TREASURER-TAX COLLECTOR
DEPUTY TREASURER-TAX COLLECTOR

CLERK OF THE BOARD OF SUPERVISORS' CERTIFICATE:

STATE OF CALIFORNIA)
COUNTY OF ORANGE)SSI HEREBY CERTIFY THAT THIS MAP WAS PRESENTED FOR APPROVAL TO THE BOARD OF
SUPERVISORS OF ORANGE COUNTY AT A REGULAR MEETING THEREOF HELD ON THE 25th DAY
OF FEBRUARY 2003, AND THAT THEREUPON SAID BOARD DID, BY AN ORDER DULY PASSED
AND ENTERED, APPROVE SAID MAP AND DID ACCEPT ON BEHALF OF THE PUBLIC, SUBJECT TO
IMPROVEMENTS: THE DEDICATION FOR STREET PURPOSES OF : NARROW CANYON ROAD AND
ETHEREAL STREET.

AND DID ALSO ACCEPT ON BEHALF OF THE COUNTY OF ORANGE:

1. THE EASEMENT FOR SIDEWALK PURPOSES AS DEDICATED.
2. THE EASEMENTS FOR STORM DRAIN PURPOSES AS DEDICATED.
3. THE EASEMENTS FOR SCENIC PRESERVATION PURPOSES AS DEDICATED.

AND DID NOT ACCEPT THE IRREVOCABLE OFFER OF LOT 4 FOR LOCAL PARK
PURPOSES AS DEDICATED.DATED THIS 25th DAY OF FEBRUARY, 2003.BY: Darlene J. Bloom
DARLENE J. BLOOM
CLERK OF THE BOARD OF SUPERVISORS

AUTOMATIC FIRE SPRINKLER NOTE:

ALL COMMERCIAL STRUCTURES GREATER THAN 6,000 SQUARE FEET; ALL MULTIFAMILY RESIDENTIAL
STRUCTURES; ALL SINGLE-FAMILY STRUCTURES EXCEEDING 5,500 SQUARE FEET, AND ALL STRUCTURES
EXCEEDING FIRE DEPARTMENT ACCESS REQUIREMENTS SHALL BE PROTECTED BY AN AUTOMATIC
SPRINKLER SYSTEM.

SPECIAL FIRE PROTECTION NOTE:

PROPERTY IS IN A SPECIAL FIRE PROTECTION AREA AND MUST MEET ALL REQUIREMENTS
FOR DEVELOPMENT WITHIN THE AREA.

HIGH FIRE HAZARD AREA NOTE:

THE LOTS SHOWN ON THIS MAP ARE IN A HIGH FIRE HAZARD AREA DUE TO
WILD LAND EXPOSURE.

NOTE:

SEE SHEET 2 FOR NOTARY ACKNOWLEDGMENTS AND SIGNATURE OMISSIONS.

SHEET 2 OF 12 SHEETS

TRACT NO. 16271

IN THE UNINCORPORATED TERRITORY OF ORANGE COUNTY, CALIFORNIA

JULY 2002

JAMES F. GILLEN, L.S. 5557

HUITT-ZOLLARS

10 NUMBERED LOTS AND 34 LETTERED LOTS

119.147 ACRES

FINAL UNIT OF VESTING
TENTATIVE TRACT NO. 16271

DATE OF SURVEY:
JANUARY 1999



SIGNATURE OMISSIONS:

IN ACCORDANCE WITH THE PROVISIONS OF SECTION 66436(a) (3) OF THE SUBDIVISION
MAP ACT, THE FOLLOWING SIGNATURE HAS BEEN OMITTED:

1. LADERA DEVELOPMENT COMPANY, L.L.C., HOLDER OF OIL, GAS, MINERAL, AND WATER RIGHTS
RECORDED DECEMBER 10, 1996 AS INSTRUMENT NO. 19960624029 OF OFFICIAL RECORDS.

EASEMENT NOTES:

- (A) INDICATES EASEMENT FOR SCENIC PRESERVATION PURPOSES DEDICATED TO THE COUNTY OF ORANGE.
(B) INDICATES SIDEWALK EASEMENT DEDICATED TO THE COUNTY OF ORANGE.
(C) INDICATES STORM DRAIN EASEMENT DEDICATED TO THE COUNTY OF ORANGE.

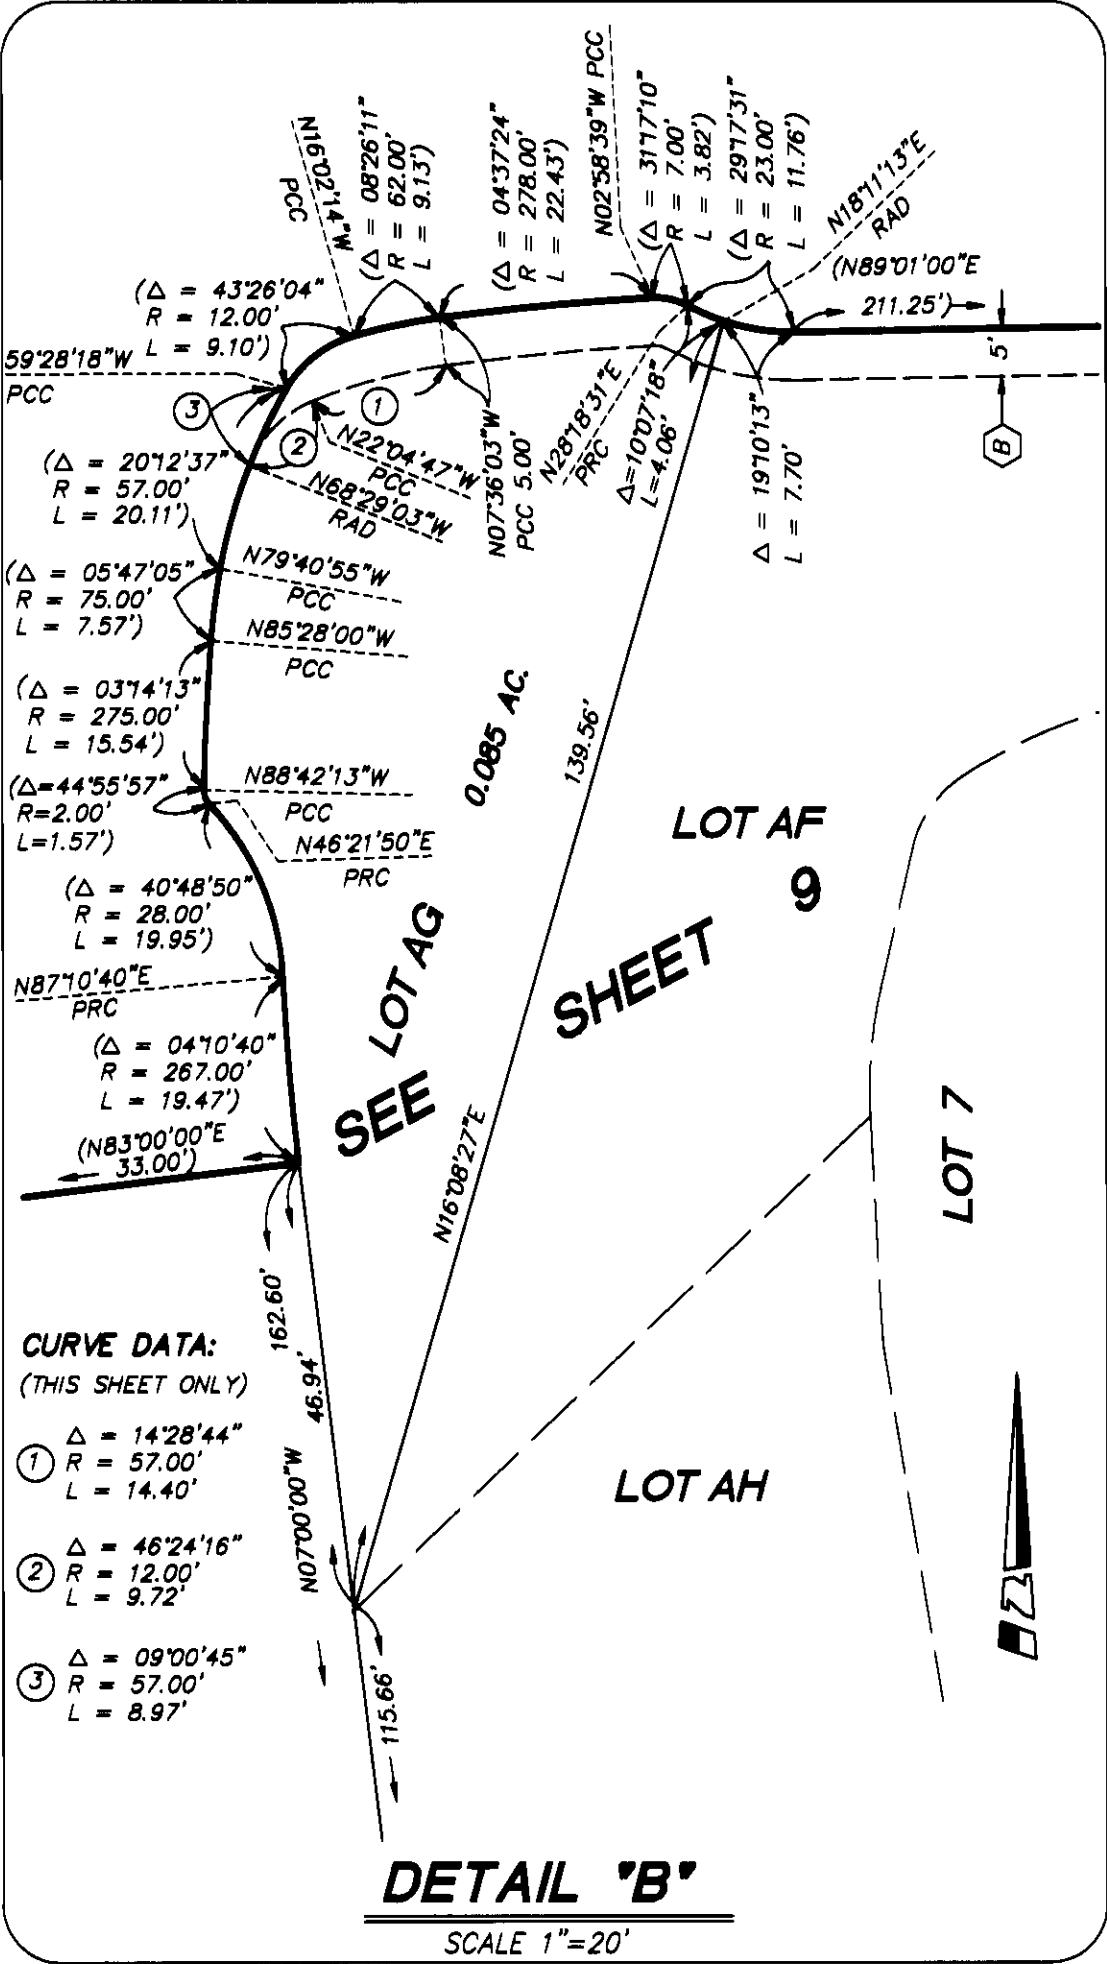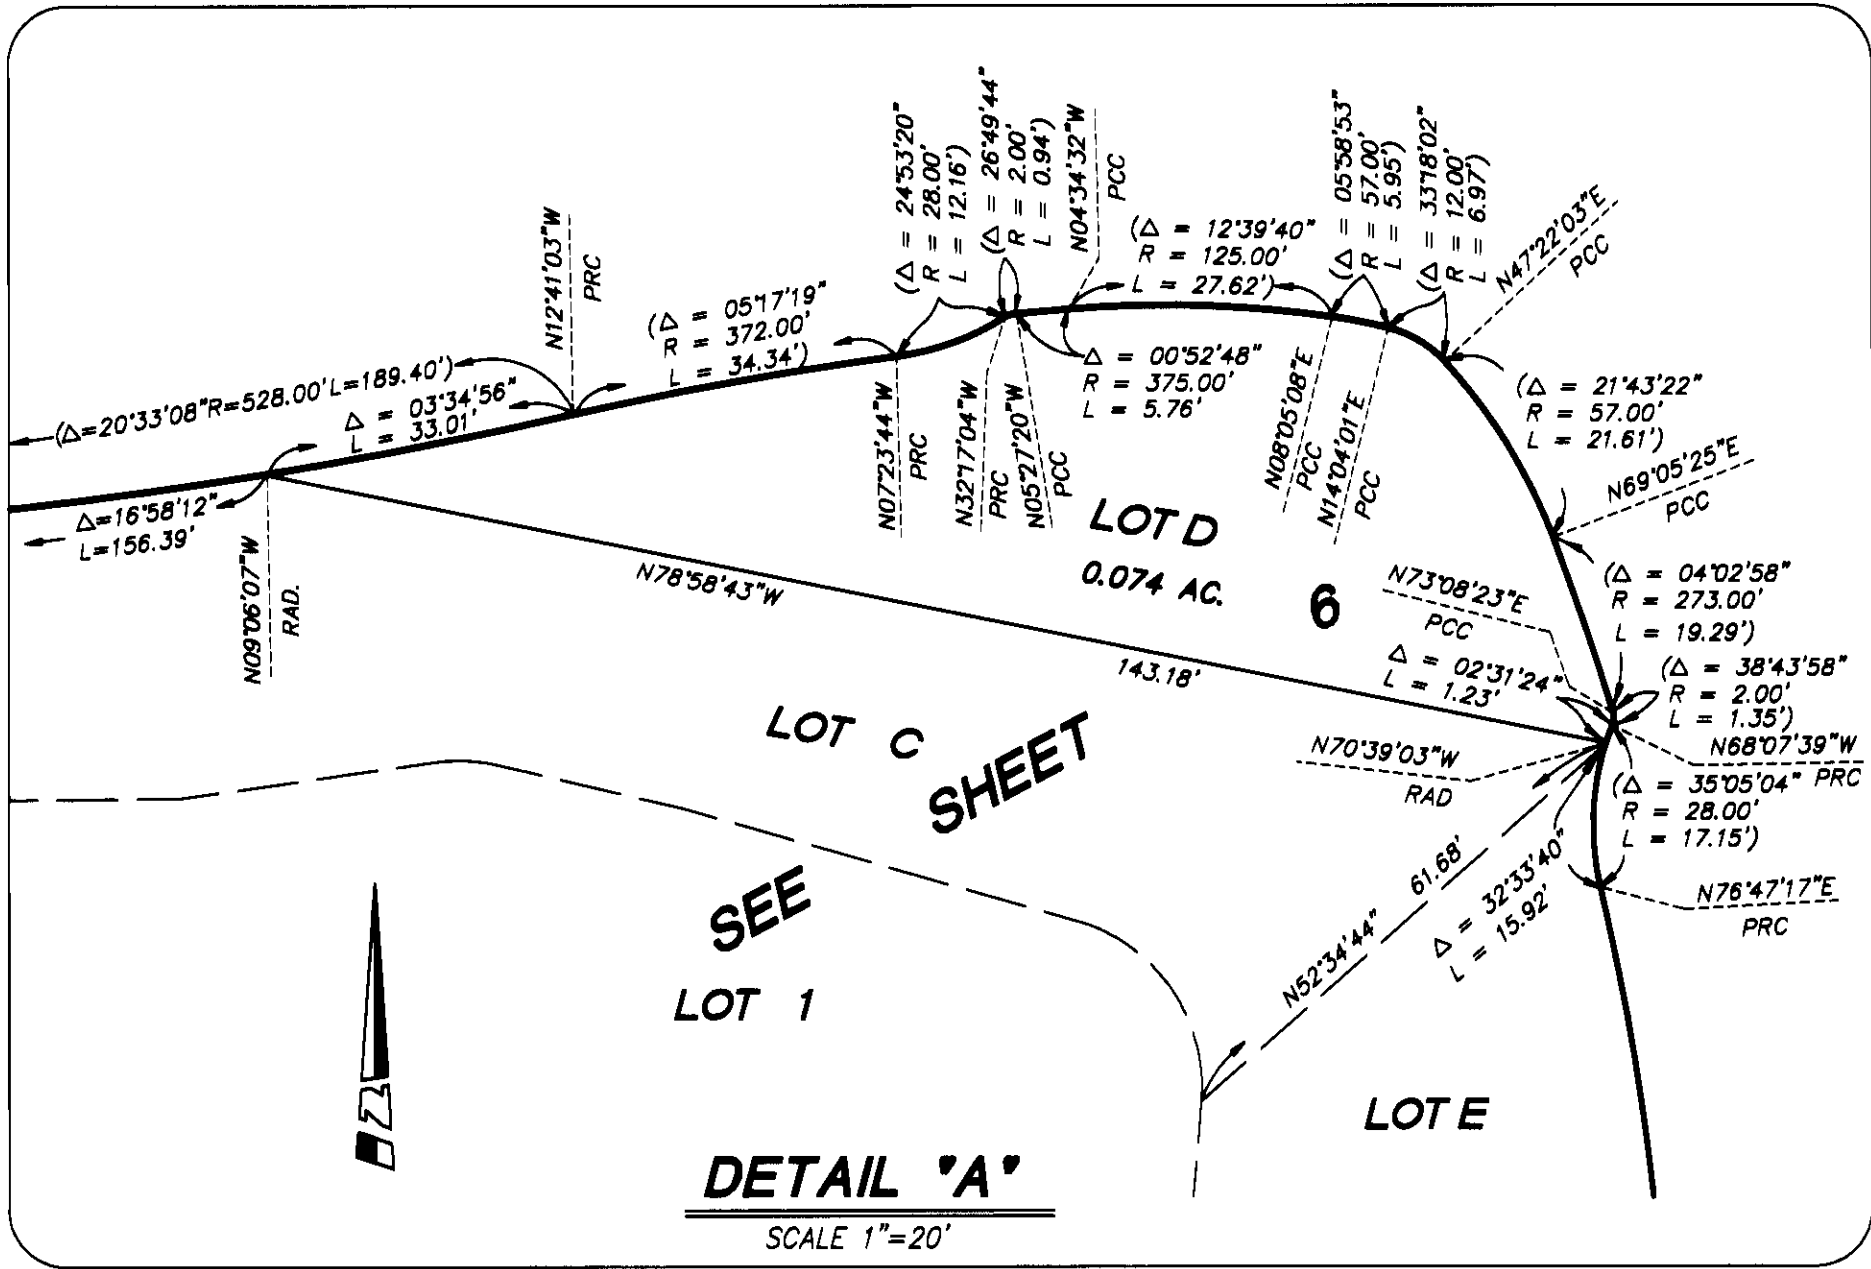

NOTE:

() INDICATES MEASURED AND RECORD PER TRACT NO. 16341
M.M. / , UNLESS OTHERWISE NOTED.

SHEET 3 OF 12 SHEETS

TRACT NO. 16271

IN THE UNINCORPORATED TERRITORY OF ORANGE COUNTY, CALIFORNIA

JULY 2002

JAMES F. GILLEN, L.S. 5557

FINAL UNIT OF VESTING
TENTATIVE TRACT NO. 16271

DATE OF SURVEY:
JANUARY 1999

HUITT-ZOLLARS

10 NUMBERED LOTS AND 34 LETTERED LOTS

119.147 ACRES

BASIS OF BEARINGS:

THE BEARINGS SHOWN HEREON, ARE BASED ON THE BEARING BETWEEN
OCS HORIZONTAL CONTROL STATION GPS NO. 1417 AND STATION GPS
NO. 1448, BEING N10°48'13"E PER RECORDS ON FILE IN THE OFFICE
OF THE ORANGE COUNTY SURVEYOR.


DATUM STATEMENT:

COORDINATES SHOWN ARE BASED ON THE CALIFORNIA COORDINATE SYSTEM,
(CCS83) ZONE VI, 1983 NAD, (1991.35 EPOCH OCS GPS ADJUSTMENT.)

ALL DISTANCES SHOWN ARE GROUND, UNLESS OTHERWISE NOTED. TO OBTAIN
A GRID DISTANCE, MULTIPLY THE GROUND DISTANCE BY 0.999948295.

NOTE:

SEE SHEET 4 FOR SHEET INDEX MAP.

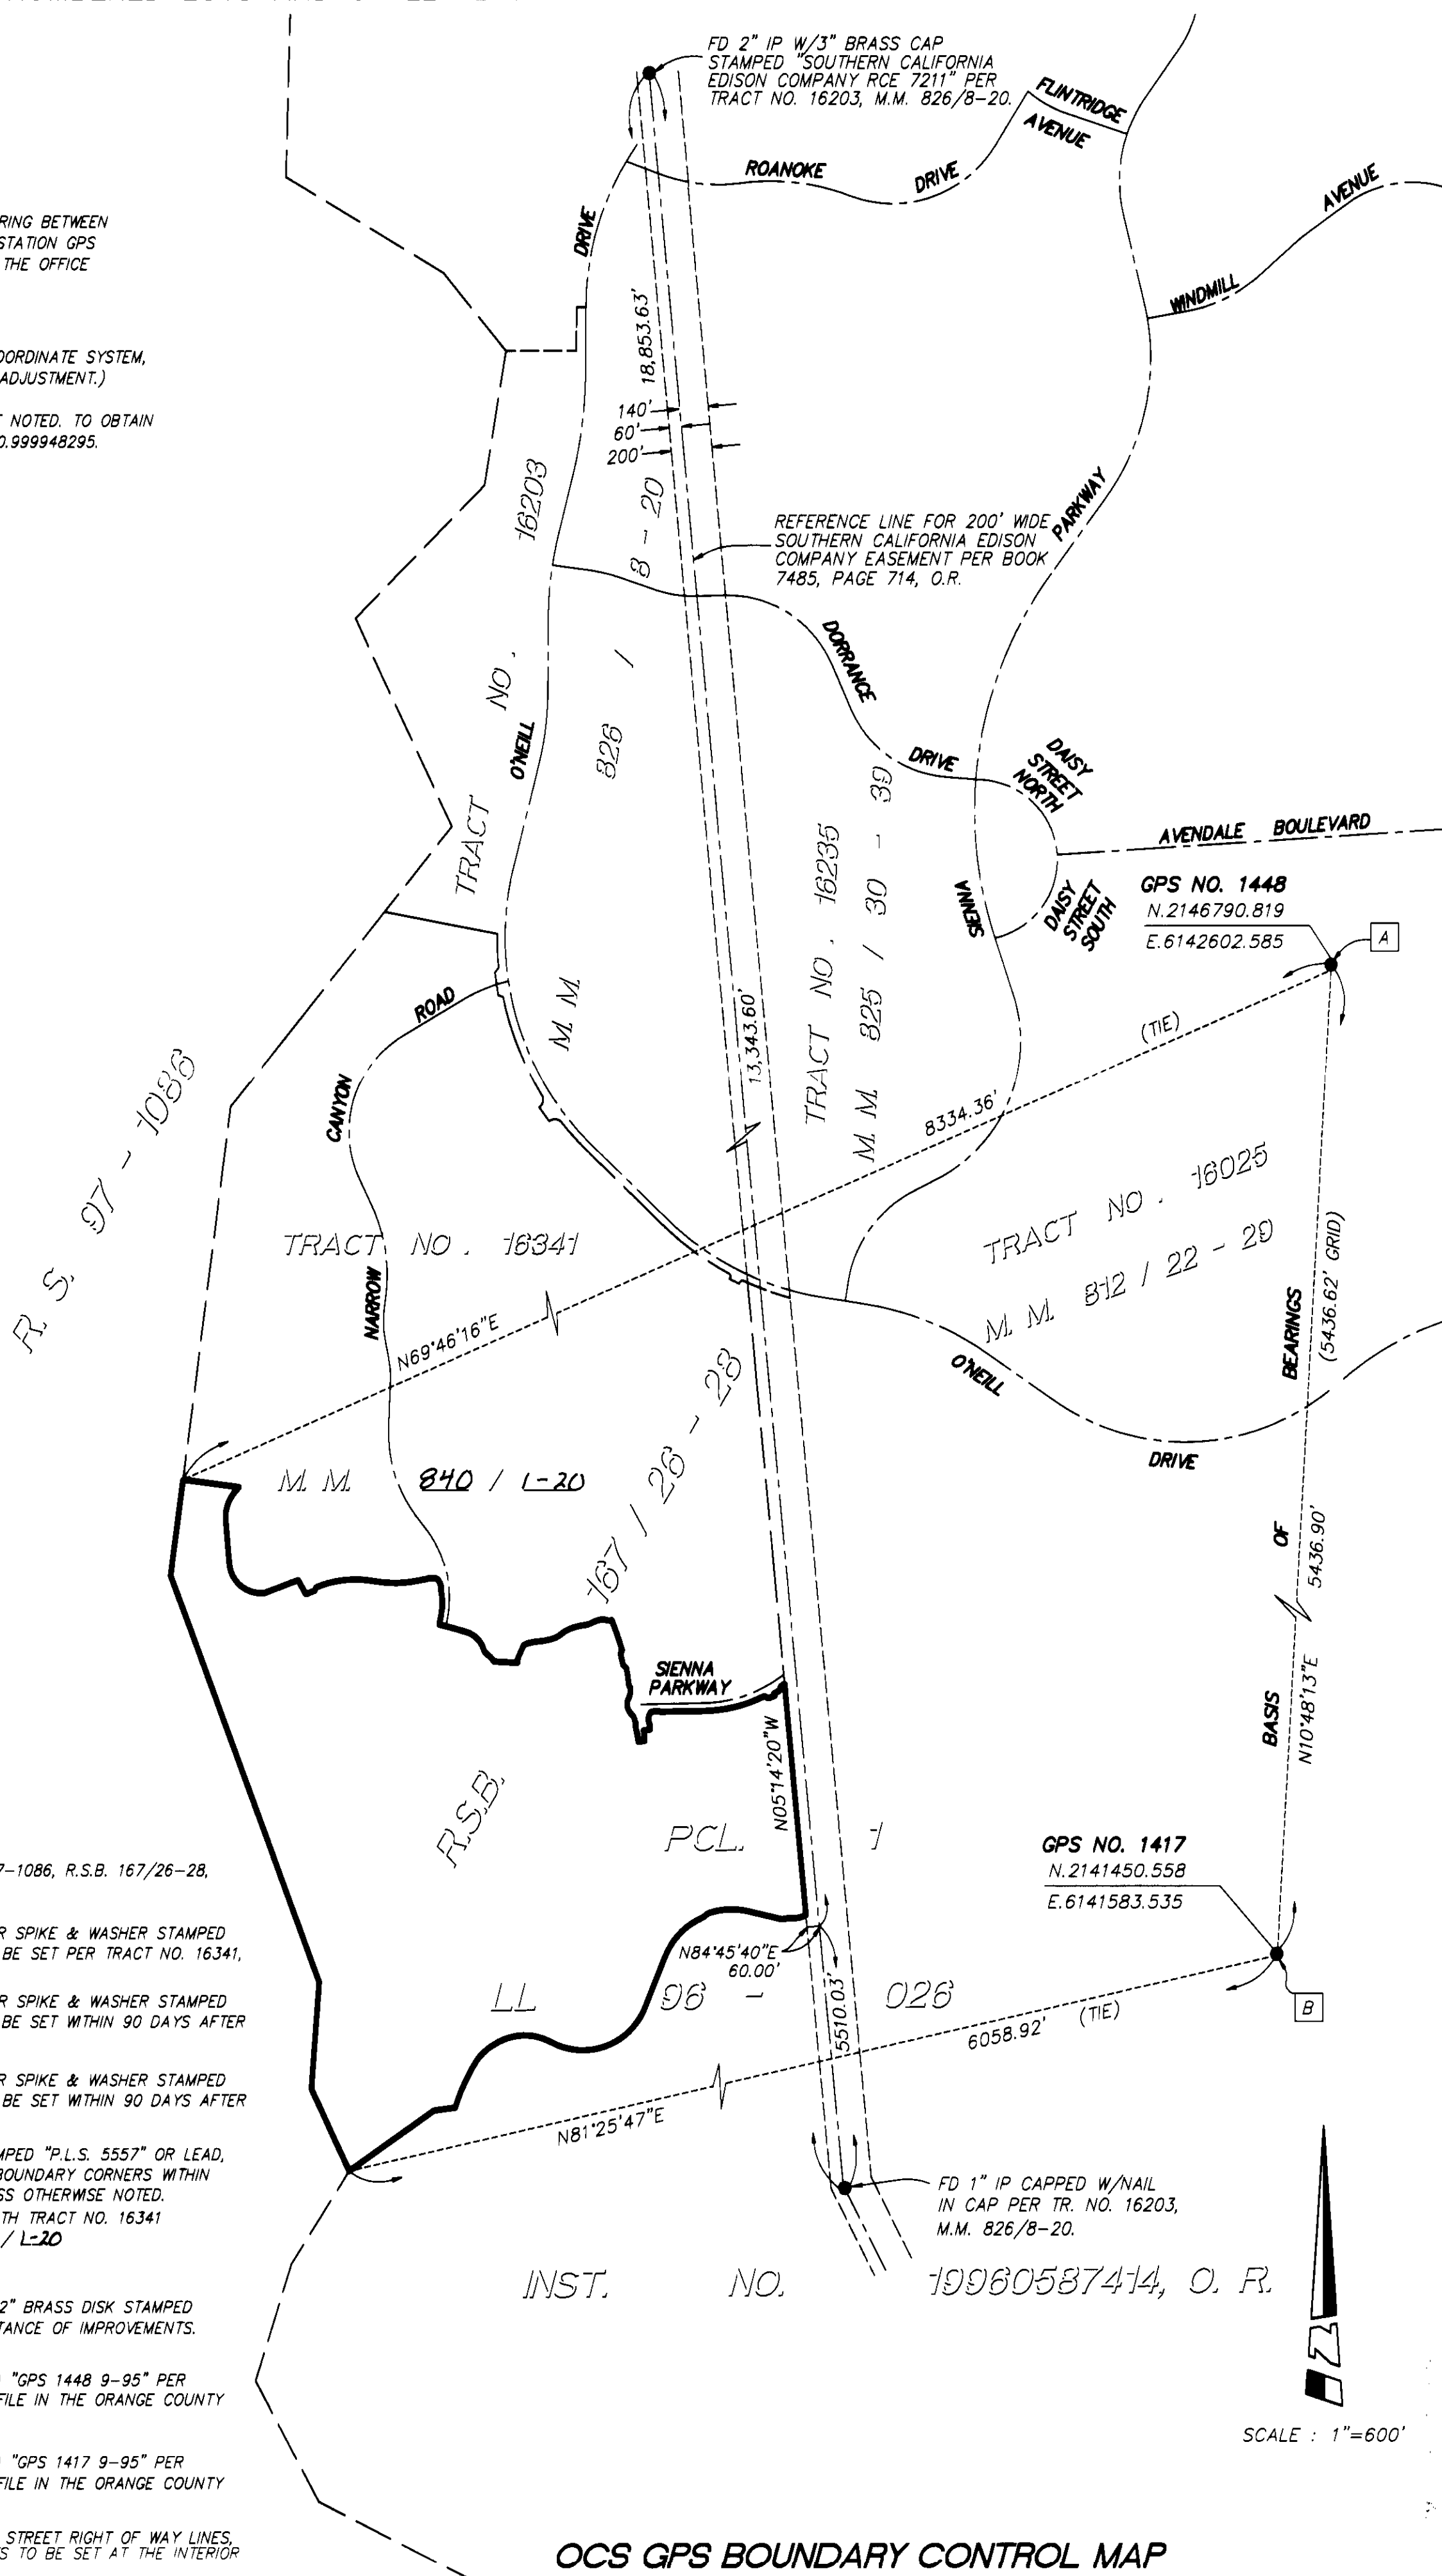

MONUMENT NOTES:

- INDICATES FD. 2" I.P. WITH TAG "LS 5557" PER R.S. 97-1086, R.S.B. 167/26-28, UNLESS OTHERWISE NOTED.
 - △ INDICATES LOCATION OF 1" I.P. TAGGED "P.L.S. 5557" OR SPIKE & WASHER STAMPED "P.L.S. 5557" OR LEAD, TACK & TAG "P.L.S. 5557" TO BE SET PER TRACT NO. 16341, M.M. 840 / L-20, UNLESS OTHERWISE NOTED.
 - INDICATES LOCATION OF 2" I.P. TAGGED "P.L.S. 5557" OR SPIKE & WASHER STAMPED "P.L.S. 5557" OR LEAD, TACK & TAG "P.L.S. 5557" TO BE SET WITHIN 90 DAYS AFTER ACCEPTANCE OF IMPROVEMENTS.
 - INDICATES LOCATION OF 1" I.P. TAGGED "P.L.S. 5557" OR SPIKE & WASHER STAMPED "P.L.S. 5557" OR LEAD, TACK & TAG "P.L.S. 5557" TO BE SET WITHIN 90 DAYS AFTER ACCEPTANCE OF IMPROVEMENTS.
- 2" I.P. TAGGED "P.L.S. 5557" OR SPIKE & WASHER STAMPED "P.L.S. 5557" OR LEAD, TACK & TAG "P.L.S. 5557" TO BE SET AT ALL TRACT BOUNDARY CORNERS WITHIN 90 DAYS AFTER ACCEPTANCE OF IMPROVEMENTS, UNLESS OTHERWISE NOTED.
- THE NORTHERLY TRACT BOUNDARY LINE CONTIGUOUS WITH TRACT NO. 16341 WILL BE MONUMENTED PER TRACT NO. 16341, M.M. 840 / L-20

- INDICATES LOCATION OF OCS WELL MONUMENT WITH A 2" BRASS DISK STAMPED "PLS 5557" TO BE SET WITHIN 90 DAYS AFTER ACCEPTANCE OF IMPROVEMENTS.

- [A] FD. 2 1/2" IRON PIPE W/2" OCS BRASS CAP STAMPED "GPS 1448 9-95" PER TRACT NO. 16203, M.M. 826/8-20 AND RECORDS ON FILE IN THE ORANGE COUNTY SURVEYORS OFFICE.
- [B] FD. 2 1/2" IRON PIPE W/2" OCS BRASS CAP STAMPED "GPS 1417 9-95" PER TRACT NO. 16203, M.M. 826/8-20 AND RECORDS ON FILE IN THE ORANGE COUNTY SURVEYORS OFFICE.

NO MONUMENTATION TO BE SET AT BC'S AND EC'S OF STREET RIGHT OF WAY LINES, UNLESS OTHERWISE SHOWN. NO ADDITIONAL MONUMENTS TO BE SET AT THE INTERIOR LOT CORNERS, OTHER THAN THOSE SHOWN.

OCS GPS BOUNDARY CONTROL MAP

SHEET 4 OF 12 SHEETS

TRACT NO. 16271

IN THE UNINCORPORATED TERRITORY OF ORANGE COUNTY, CALIFORNIA

JULY 2002

JAMES F. GILLEN, L.S. 5557



FINAL UNIT OF VESTING
TENTATIVE TRACT NO. 16271

DATE OF SURVEY:
JANUARY 1999

HUITT-ZOLLARS

10 NUMBERED LOTS AND 34 LETTERED LOTS

119.147 ACRES

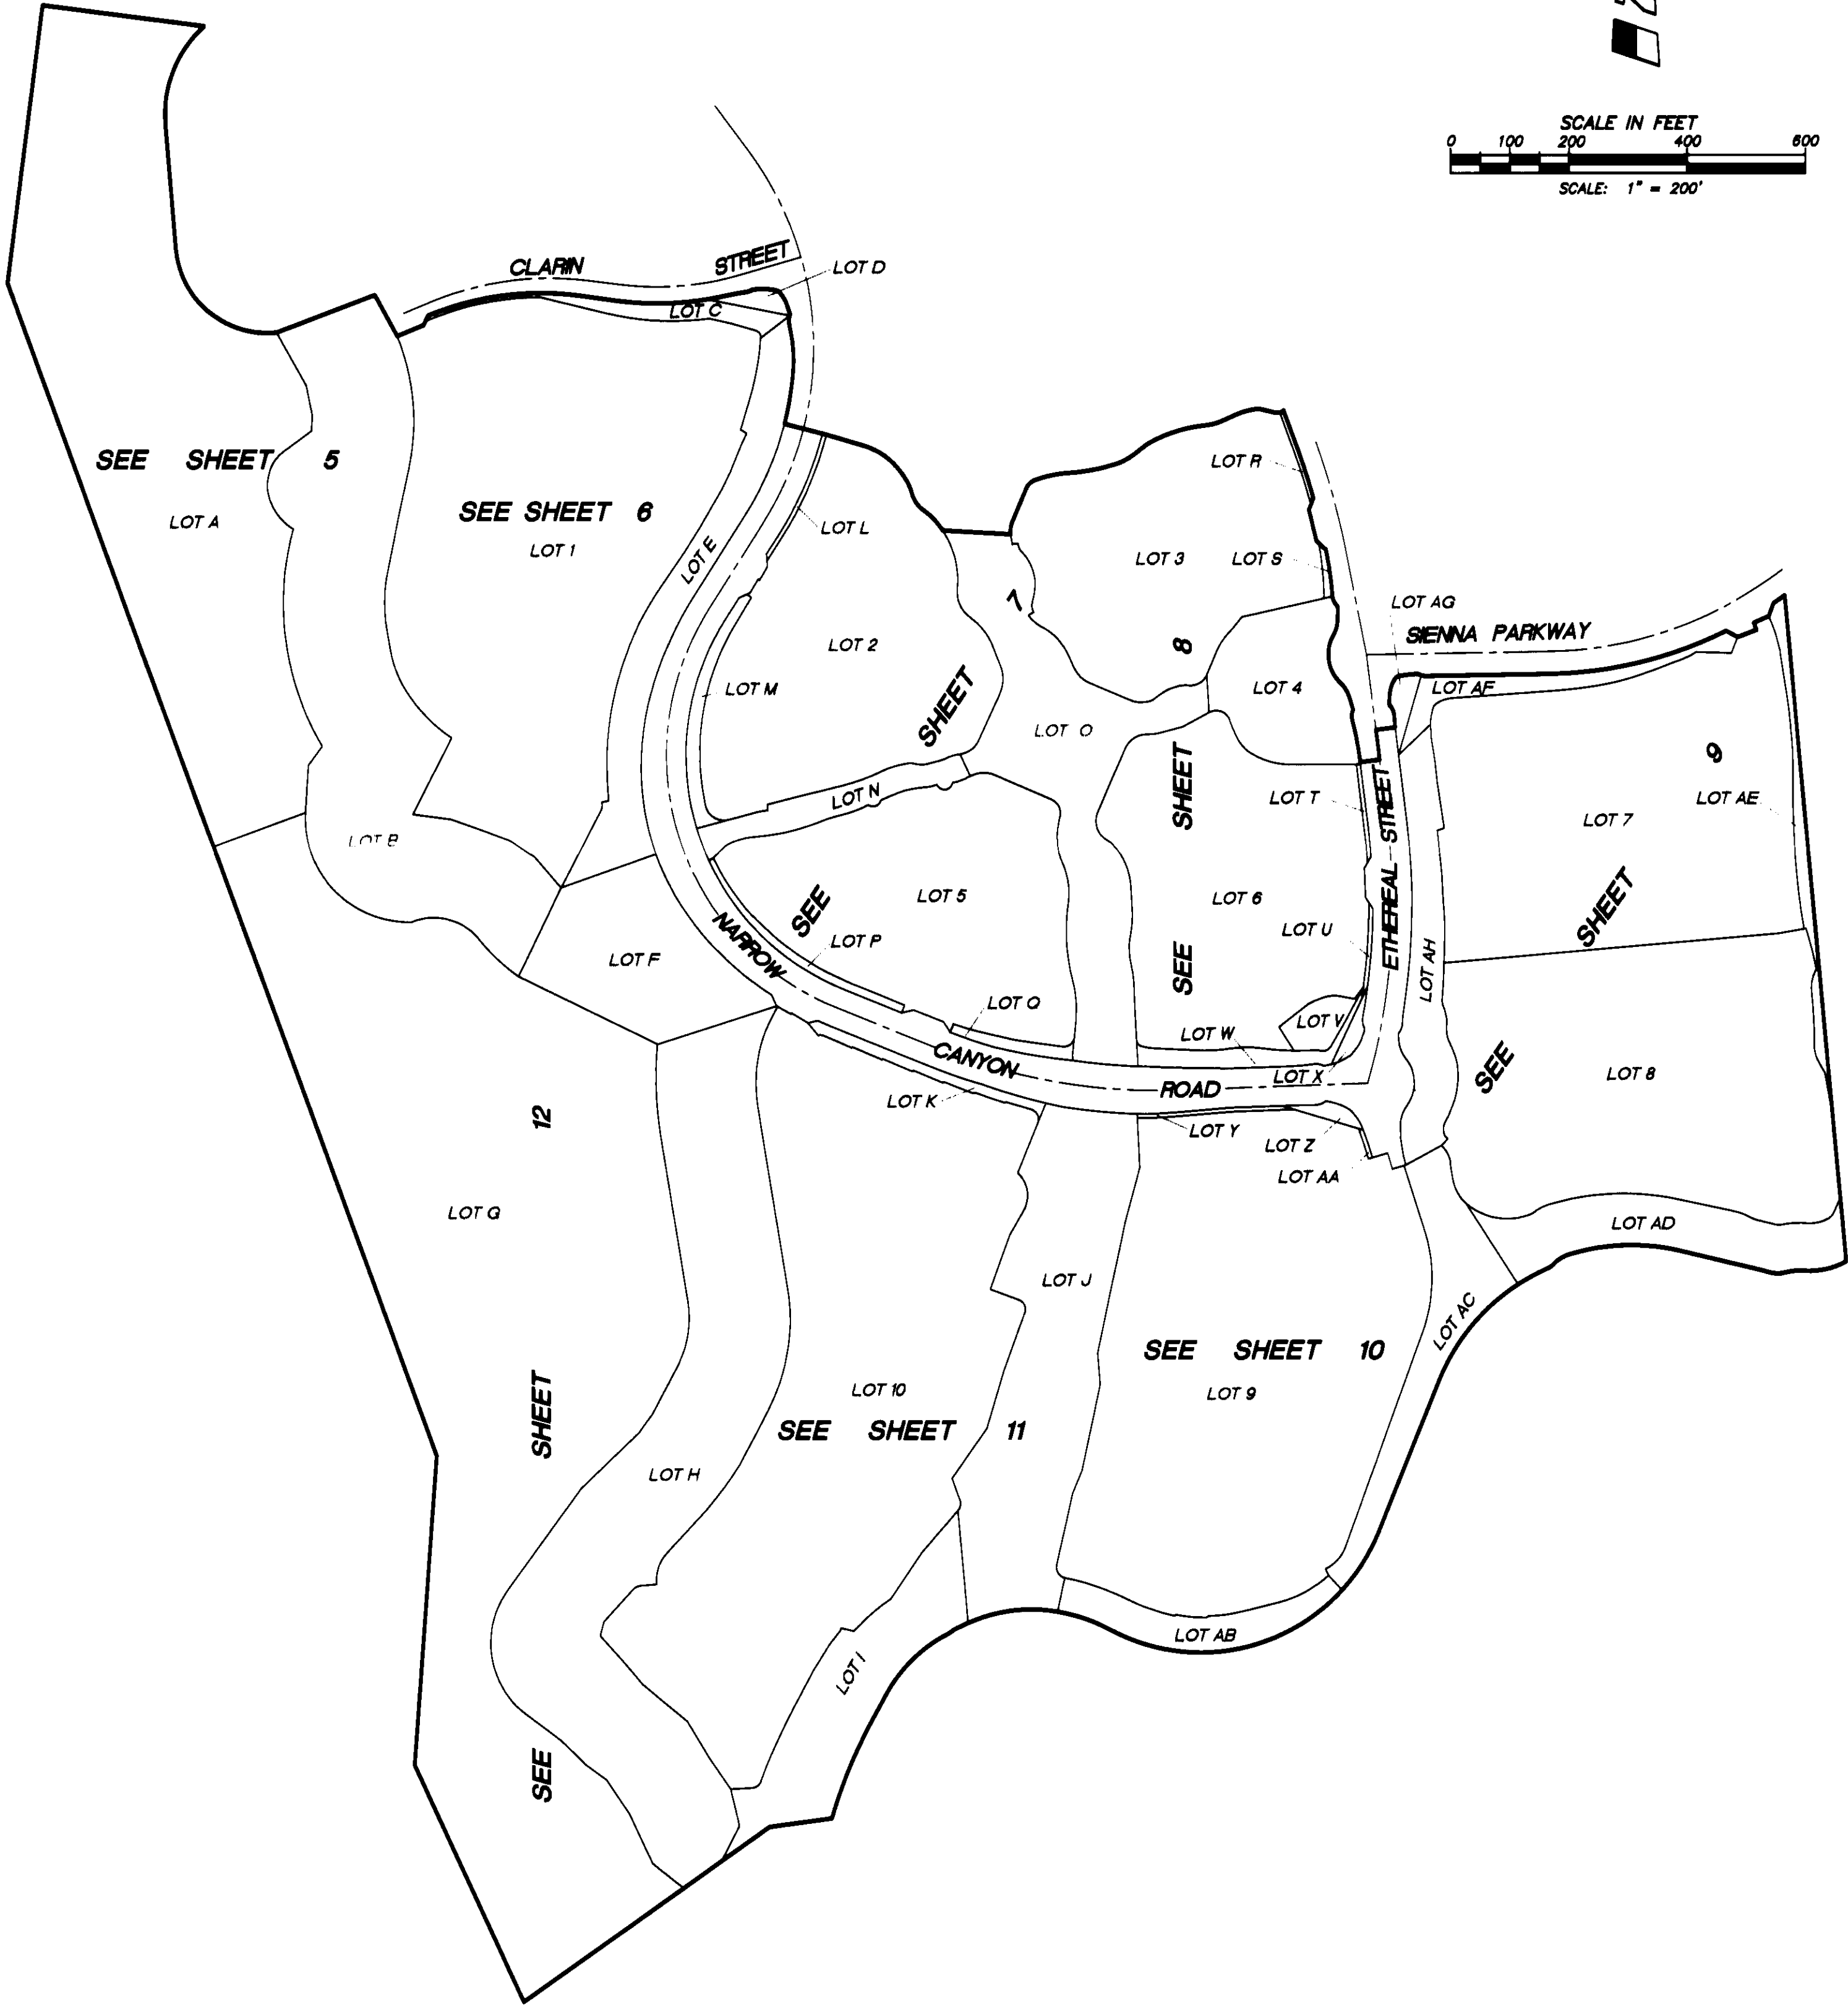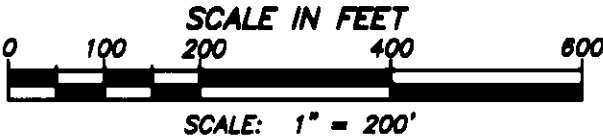

SHEET INDEX MAP

SHEET 5 OF 12 SHEETS

TRACT NO. 16271

IN THE UNINCORPORATED TERRITORY OF ORANGE COUNTY, CALIFORNIA

JULY 2002

JAMES F. GILLEN, L.S. 5557


FINAL UNIT OF VESTING
TENTATIVE TRACT NO. 16271

DATE OF SURVEY:
JANUARY 1999

HUITT-ZOLLARS

10 NUMBERED LOTS AND 34 LETTERED LOTS

119.147 ACRES

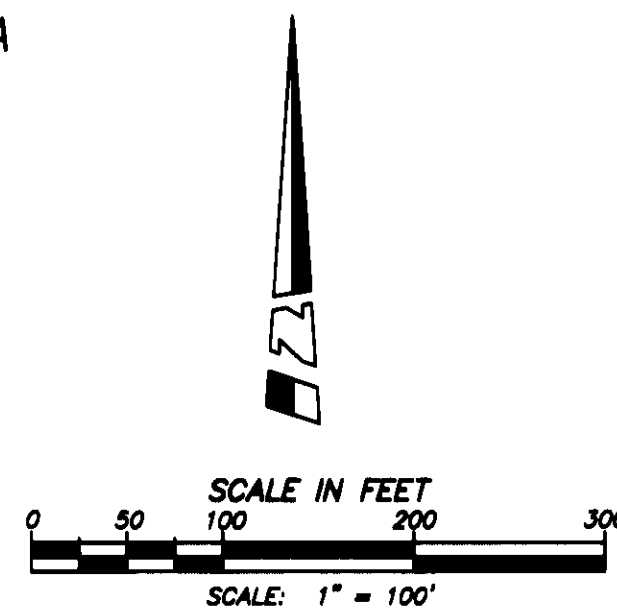

TRACT NO. 16341

M. M. 840 / 1-20

LOT 16

LOT A
9.034 AC.

LOT B
5.288 AC.



SHEET

SEE

SEE

SHEET

12

NOTES:

SEE SHEET 2 FOR EASEMENT NOTES.

SEE SHEET 3 FOR BASIS OF BEARINGS, DATUM STATEMENT,
MONUMENT NOTES AND OCS GPS BOUNDARY CONTROL MAP.

SEE SHEET 4 FOR SHEET INDEX MAP.

LOTS A THROUGH AH ARE FOR LANDSCAPING/OPEN SPACE
AND ARE NOT SEPARATE BUILDING SITES.

LOT 4 IS IRREVOCABLY OFFERED FOR DEDICATION IN FEE
SIMPLE TO THE COUNTY OF ORANGE FOR LOCAL PARK PURPOSES.

[] INDICATES MEASURED AND RECORD PER R.S. 97-1086,
R.S.B. 167/26-28.

() INDICATES MEASURED AND RECORD PER TRACT NO. 16341
M.M. 840 / 1-20

839

58

TRACT NO. 16271

IN THE UNINCORPORATED TERRITORY OF ORANGE COUNTY, CALIFORNIA

JULY 2002

JAMES F. GILLEN, L.S. 5557


HUITT-ZOLLARS

10 NUMBERED LOTS AND 34 LETTERED LOTS

119.147 ACRES

FINAL UNIT OF VESTING
TENTATIVE TRACT NO. 16271

DATE OF SURVEY:
JANUARY 1999

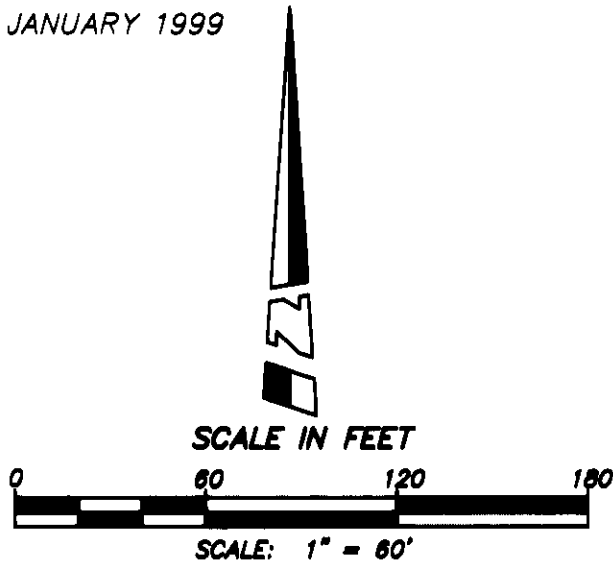

TRACT NO. 16341

LOT 16

LOT K

LOT M

M.M. 840 / 1-20


LOT L

CLARIN

STREET

VARIES

SEE DETAIL "A"
SHEET 2

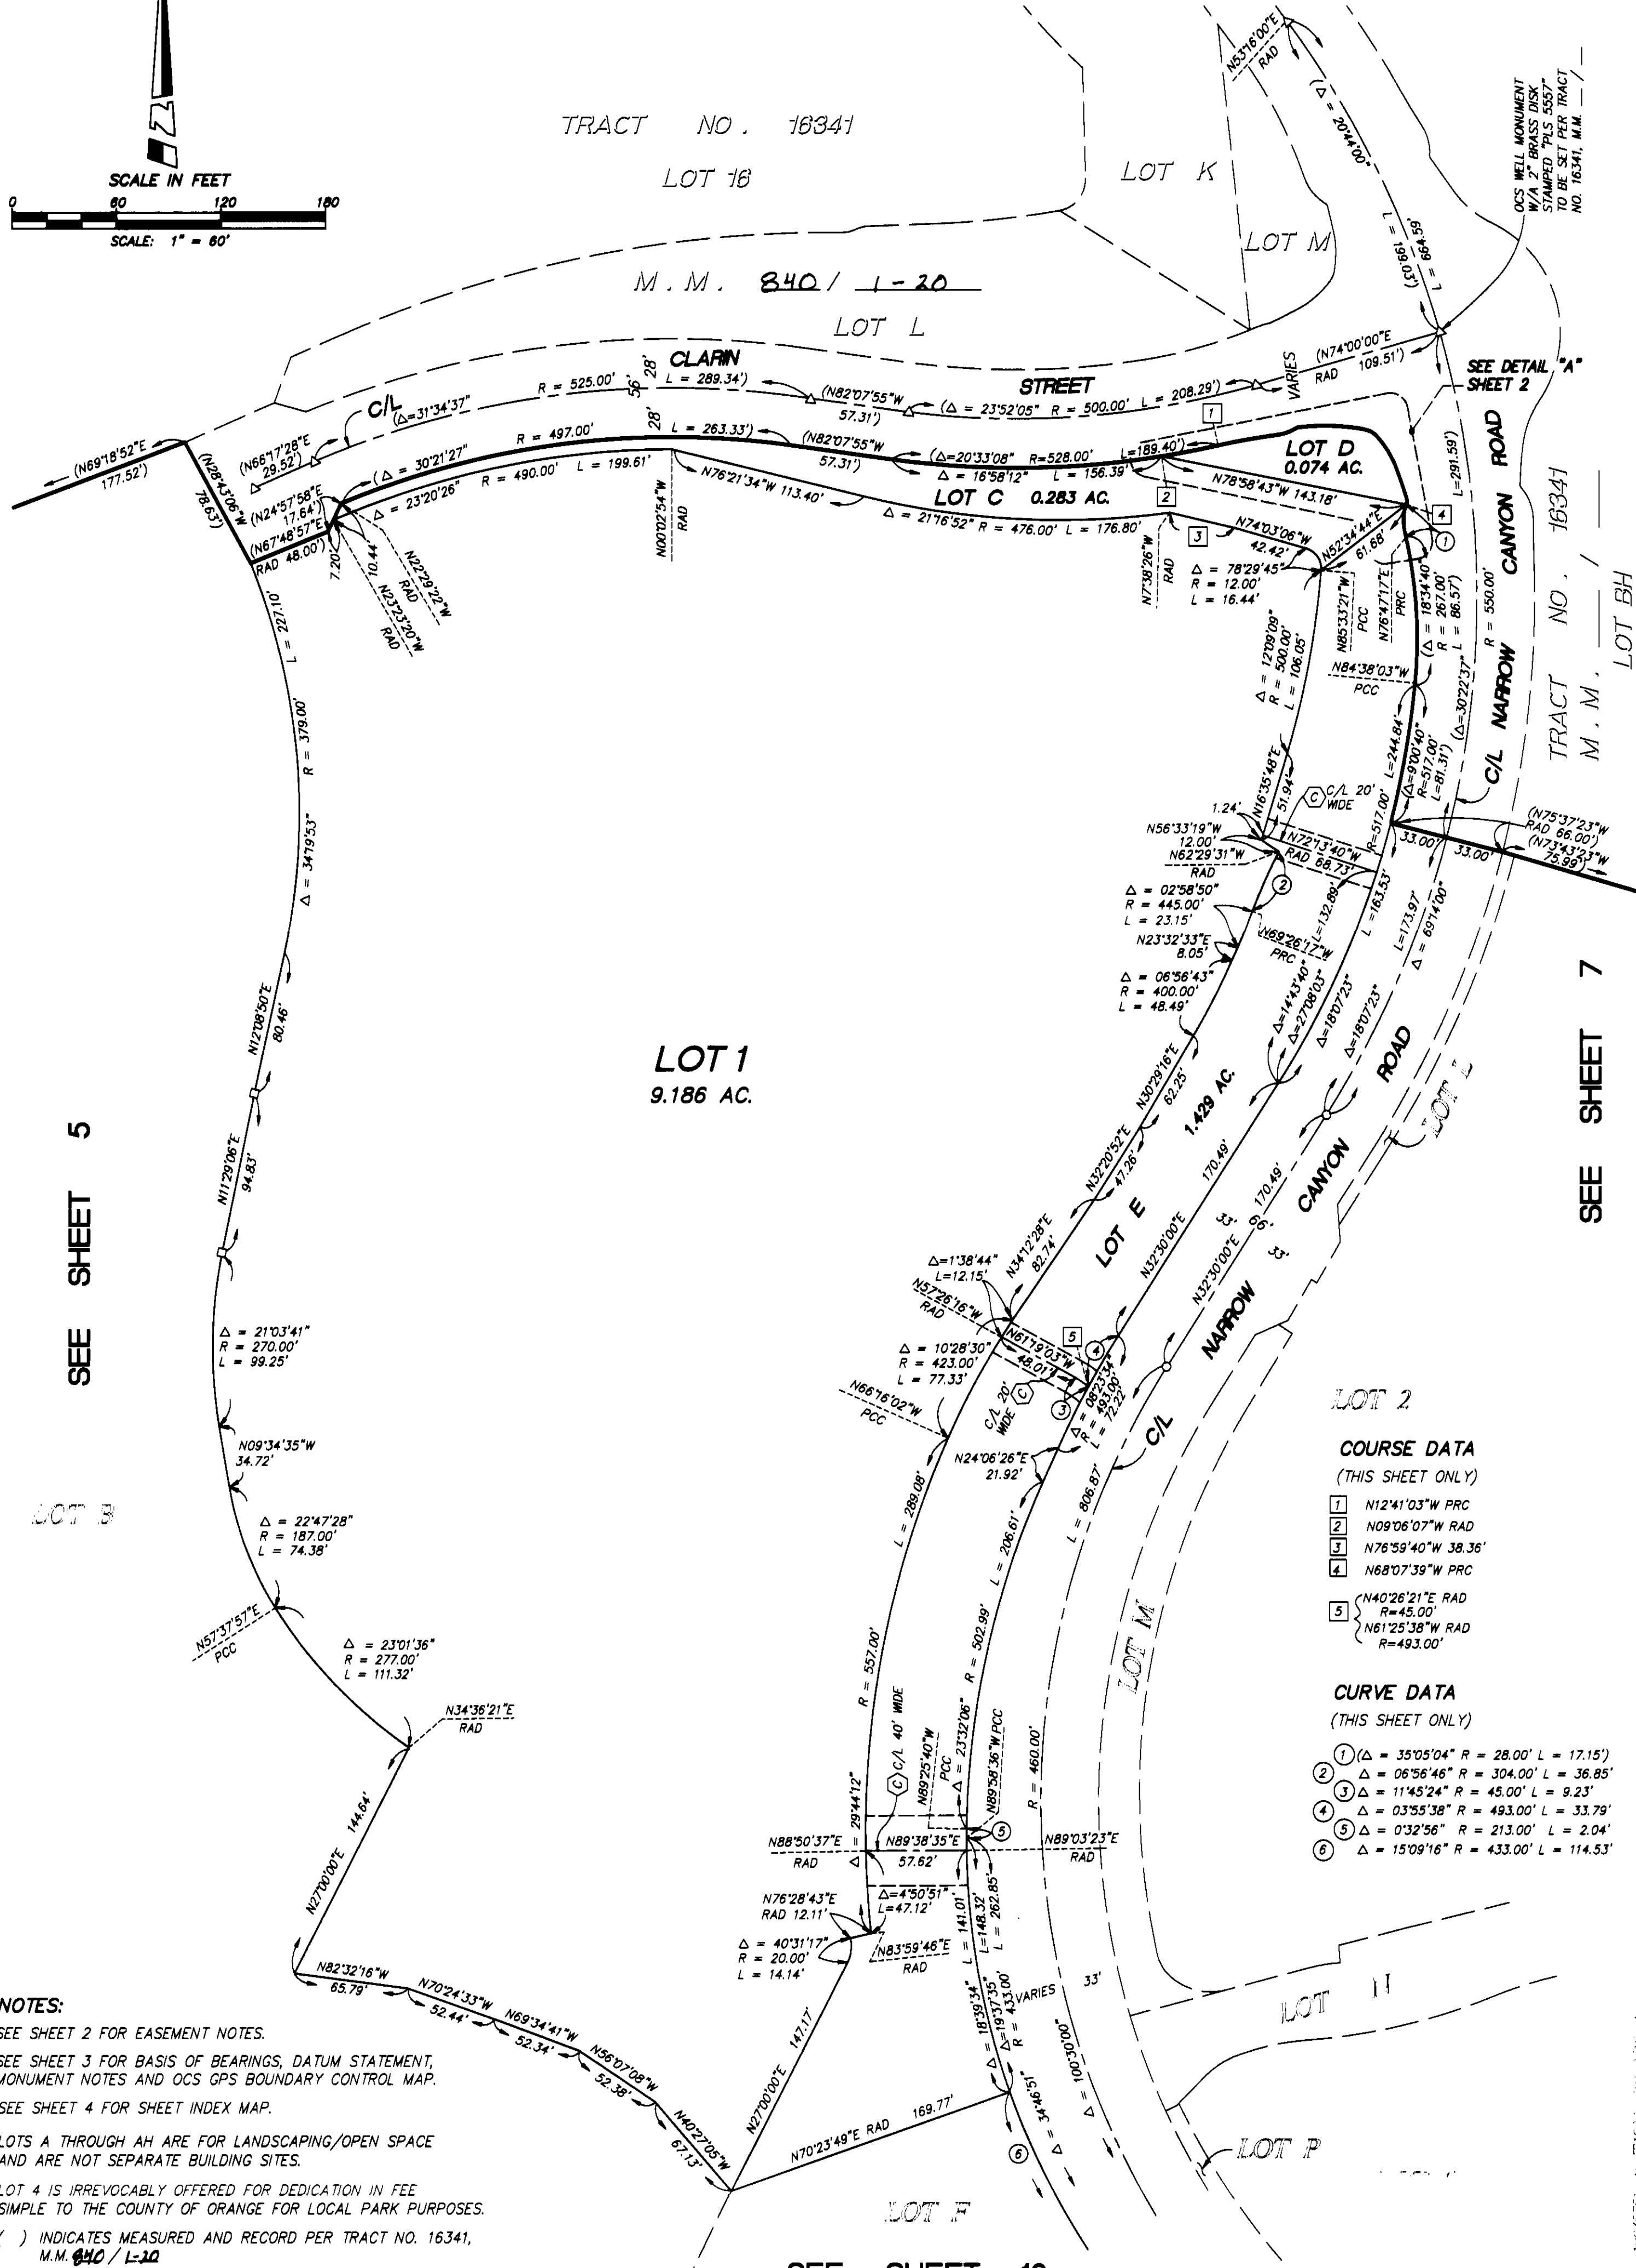

SEE SHEET 5

SEE SHEET 5

SEE SHEET 7

NOTES:

SEE SHEET 2 FOR EASEMENT NOTES.

SEE SHEET 3 FOR BASIS OF BEARINGS, DATUM STATEMENT,
MONUMENT NOTES AND OCS GPS BOUNDARY CONTROL MAP.

SEE SHEET 4 FOR SHEET INDEX MAP.

LOTS A THROUGH AH ARE FOR LANDSCAPING/OPEN SPACE
AND ARE NOT SEPARATE BUILDING SITES.

LOT 4 IS IRREVOCABLY OFFERED FOR DEDICATION IN FEE
SIMPLE TO THE COUNTY OF ORANGE FOR LOCAL PARK PURPOSES.

() INDICATES MEASURED AND RECORD PER TRACT NO. 16341,
M.M. 840 / 1-20

COURSE DATA (THIS SHEET ONLY)

- 1 N12°41'03"W PRC
- 2 N09°06'07"W RAD
- 3 N78°59'40"W 38.36'
- 4 N68°07'39"W PRC
- 5 N40°26'21"E RAD
R=45.00'
N61°25'38"W RAD
R=493.00'

CURVE DATA (THIS SHEET ONLY)

- 1 (Δ = 35°05'04" R = 28.00' L = 17.15')
- 2 (Δ = 06°56'46" R = 304.00' L = 36.85')
- 3 (Δ = 11°45'24" R = 45.00' L = 9.23')
- 4 (Δ = 03°55'38" R = 493.00' L = 33.79')
- 5 (Δ = 0°32'56" R = 213.00' L = 2.04')
- 6 (Δ = 15°09'16" R = 433.00' L = 114.53')

SEE SHEET 12

839 40

SHEET 7 OF 12 SHEETS

TRACT NO. 16271

IN THE UNINCORPORATED TERRITORY OF ORANGE COUNTY, CALIFORNIA

JULY 2002

JAMES F. GILLEN, L.S. 5557

HUITT-ZOLLARS

10 NUMBERED LOTS AND 34 LETTERED LOTS

119.147 ACRES

FINAL UNIT OF VESTING
TENTATIVE TRACT NO. 16271


DATE OF SURVEY:
JANUARY 1999

CURVE DATA (THIS SHEET ONLY)

- SEE SHEET 6
- 1 $\Delta = 07^{\circ}48'12''$ R = 427.00' L = 58.15'
 - 2 $\Delta = 25^{\circ}47'26''$ R = 50.00' L = 22.51'
 - 3 $\Delta = 15^{\circ}45'24''$ R = 150.00' L = 41.25'
 - 4 $\Delta = 03^{\circ}14'01''$ R = 87.00' L = 4.91'
 - 5 $\Delta = 02^{\circ}47'52''$ R = 63.00' L = 3.08'
 - 6 $\Delta = 91^{\circ}12'28''$ R = 18.00' L = 28.65'
 - 7 $\Delta = 15^{\circ}22'25''$ R = 404.00' L = 108.40'
 - 8 $\Delta = 48^{\circ}39'10''$ R = 20.00' L = 16.98'
 - 9 $\Delta = 02^{\circ}44'53''$ R = 1500.00' L = 71.94'
 - 10 $\Delta = 03^{\circ}38'56''$ R = 960.00' L = 61.14'
 - 11 $\Delta = 37^{\circ}04'51''$ R = 25.00' L = 16.18'
 - 12 $\Delta = 56^{\circ}34'42''$ R = 35.00' L = 34.56'
 - 13 $\Delta = 24^{\circ}08'32''$ R = 21.00' L = 8.85'
 - 14 $\Delta = 33^{\circ}35'10''$ R = 45.00' L = 26.38'
 - 15 $\Delta = 04^{\circ}54'05''$ R = 201.00' L = 17.19'
 - 16 $\Delta = 15^{\circ}23'00''$ R = 35.00' L = 9.40'

COURSE DATA (THIS SHEET ONLY)

- SEE SHEET 6
- 1 N16°45'39"E PCC
 - 2 N13°31'38"E PCC
 - 3 N05°41'33"E PRC
 - 4 N08°29'25"E PRC
 - 5 N10°56'25"W RAD R=100.00'
 - 6 N79°24'56"W RAD R=14.00'
 - 7 N01°12'55"W 7.09'
 - 8 N19°33'57"W RAD R=79.00'
 - 9 N65°41'05"E RAD R=14.00'
 - 10 N22°22'28"W RAD R=394.00'
 - 11 N74°45'34"W RAD R=14.00'
 - 12 N27°51'35"W RAD R=186.00'
 - 13 N34°30'46"E RAD R=14.00'
 - 14 N04°50'29"E RAD R=960.00'
 - 15 N89°36'01"E RAD R=1500.00'
 - 16 N44°12'20"E 23.48'
 - 17 N65°29'10"E RAD 7.00'

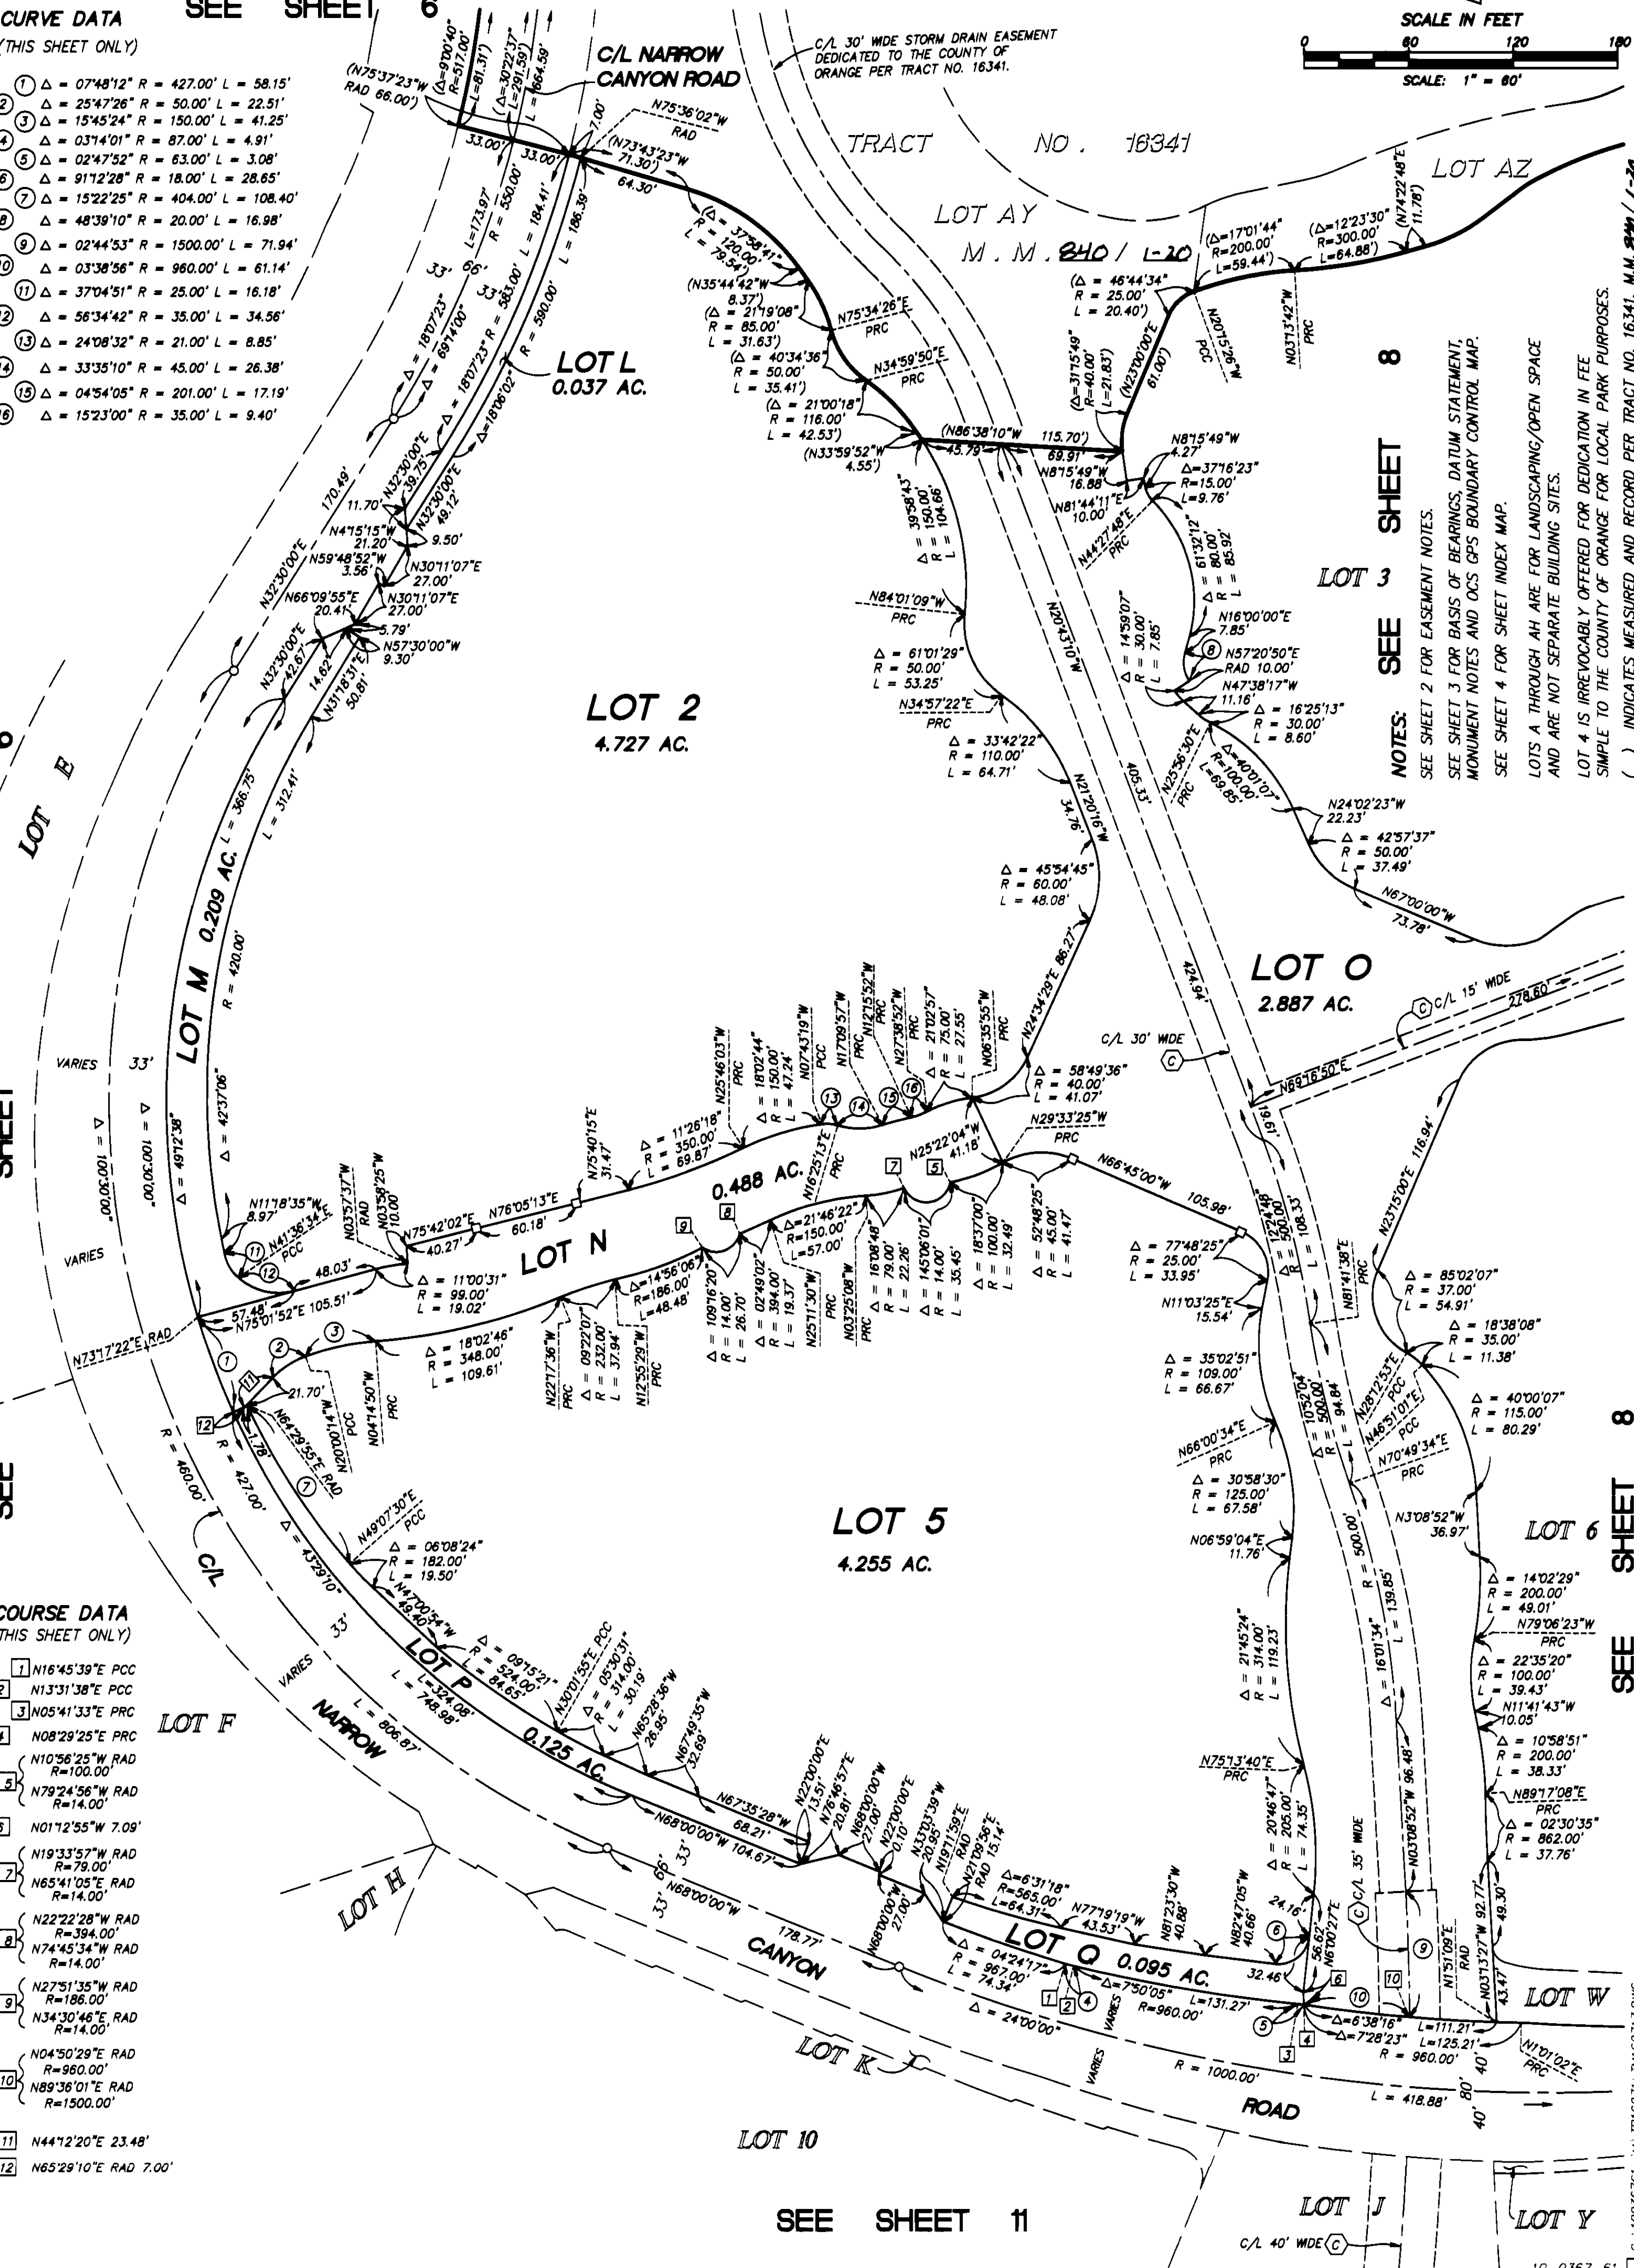

839 41

SHEET 8 OF 12 SHEETS

TRACT NO. 16271

FINAL UNIT OF VESTING
TENTATIVE TRACT NO. 16271

IN THE UNINCORPORATED TERRITORY OF ORANGE COUNTY, CALIFORNIA

JULY 2002

JAMES F. GILLEN, L.S. 5557

DATE OF SURVEY:
JANUARY 1999

HUITT-ZOLLARS

10 NUMBERED LOTS AND 34 LETTERED LOTS

119.147 ACRES

NOTES:

SEE SHEET 2 FOR EASEMENT NOTES.

SEE SHEET 3 FOR BASIS OF BEARINGS, DATUM STATEMENT,
MONUMENT NOTES AND OCS GPS BOUNDARY CONTROL MAP.

SEE SHEET 4 FOR SHEET INDEX MAP.


LOTS A THROUGH AH ARE FOR LANDSCAPING/OPEN SPACE
AND ARE NOT SEPARATE BUILDING SITES.

LOT 4 IS IRREVOCABLY OFFERED FOR DEDICATION IN FEE
SIMPLE TO THE COUNTY OF ORANGE FOR LOCAL PARK PURPOSES.

() INDICATES MEASURED AND RECORD PER TRACT NO. 16341,
M.M. 840 / 1-20

TRACT NO. 16341

M.M. 840 / 1-20

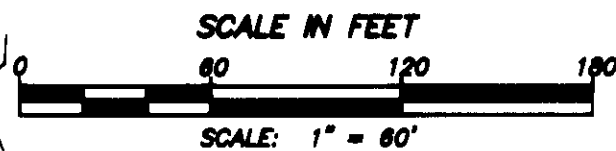


M.M. 840 / 1-20

COURSE DATA
(THIS SHEET ONLY)

- 1 N85°42'01"E PCC
- 2 N87°42'07"E PCC
- 3 (N112°00'00"W 7.91')
- 4 N43°51'30"E PRC
- 5 N68°16'17"W PRC
- 6 N81°19'58"W RAD
- 7 N27°08'34"E PRC
- 8 N01°51'09"E RAD
- 9 N82°33'21"W RAD
- 10 N80°45'00"W PCC
- 11 N77°43'41"W PRC
- 12 N60°56'46"E PRC
- 13 N74°40'35"W PCC
- 14 N73°42'06"W PCC
- 15 N46°20'14"W PCC
- 16 N35°39'43"W PCC
- 17 N12°57'03"W PCC
- 18 N11°05'43"W PCC
- 19 N08°24'03"W PRC
- 20 N01°01'02"E PRC
- 21 N03°47'21"E PRC
- 22 N33°34'05"W 22.89'
- 23 N29°36'16"E 22.89'
- 24 N04°50'29"E RAD R=960.00'
- 25 N89°36'01"E RAD R=1500.00'
- 26 N36°31'11"E 25.18'
- 27 N89°17'06"E 36.24'
- 28 N28°06'15"E 65.48'
- 29 N25°11'30"E 23.76'
- 30 (N70°00'00"E 7.00')
- 31 (N48°01'06"W 21.18')
- 32 (N20°57'06"E 21.18')
- 33 N54°17'08"E 20.63'
- 34 N82°15'09"E RAD

CURVE DATA
(THIS SHEET ONLY)

- 1 Δ = 38°14'17" R = 2.00' L = 1.33'
- 2 Δ = 69°52'23" R = 10.00' L = 12.20'
- 3 Δ = 14°12'35" R = 100.00' L = 24.80'
- 4 Δ = 48°39'10" R = 20.00' L = 16.98'
- 5 Δ = 41°50'31" R = 28.00' L = 20.45'
- 6 Δ = 43°50'37" R = 2.00' L = 1.53'
- 7 Δ = 01°02'14" R = 575.00' L = 10.41'
- 8 Δ = 06°33'17" R = 125.00' L = 14.30'
- 9 Δ = 24°35'02" R = 57.00' L = 24.46'
- 10 Δ = 07°02'01" R = 567.00' L = 69.60'
- 11 Δ = 03°26'52" R = 28.00' L = 1.69'
- 12 Δ = 38°23'39" R = 28.00' L = 18.76'
- 13 Δ = 04°17'00" R = 1167.00' L = 87.24'
- 14 Δ = 02°12'53" R = 573.00' L = 22.15'
- 15 Δ = 35°59'40" R = 28.00' L = 17.59'
- 16 Δ = 37°45'50" R = 2.00' L = 1.32'
- 17 Δ = 02°37'43" R = 1067.00' L = 48.95'
- 18 Δ = 02°44'53" R = 1500.00' L = 71.94'
- 19 Δ = 03°38'56" R = 960.00' L = 61.14'
- 20 Δ = 01°48'21" R = 1067.00' L = 33.63'
- 21 Δ = 11°51'45" R = 45.00' L = 9.32'
- 22 Δ = 71°10'31" R = 16.00' L = 19.88'
- 23 Δ = 0°01'00" R = 1167.00' L = 0.34'
- 24 Δ = 20°40'12" R = 25.00' L = 9.02'
- 25 Δ = 03°01'19" R = 367.00' L = 19.36'
- 26 Δ = 41°19'33" R = 28.00' L = 20.20'
- 27 Δ = 44°22'39" R = 2.00' L = 1.55'
- 28 Δ = 00°58'29" R = 375.00' L = 6.38'
- 29 Δ = 27°21'52" R = 87.00' L = 41.55'
- 30 Δ = 10°40'31" R = 22.00' L = 4.10'
- 31 Δ = 22°42'40" R = 87.00' L = 34.49'
- 32 Δ = 01°51'20" R = 373.00' L = 12.08'
- 33 Δ = 06°24'03" R = 367.00' L = 41.00'
- 34 Δ = 02°51'14" R = 87.00' L = 4.33'
- 35 Δ = 02°56'07" R = 960.00' L = 49.18'
- 36 Δ = 02°46'19" R = 63.00' L = 3.05'
- 37 Δ = 00°50'07" R = 960.00' L = 14.00'
- 38 Δ = 03°43'36" R = 280.00' L = 18.21'
- 39 Δ = 35°32'37" R = 28.00' L = 17.37'
- 40 Δ = 31°23'20" R = 56.00' L = 30.68'
- 41 Δ = 20°04'36" R = 43.00' L = 15.07'

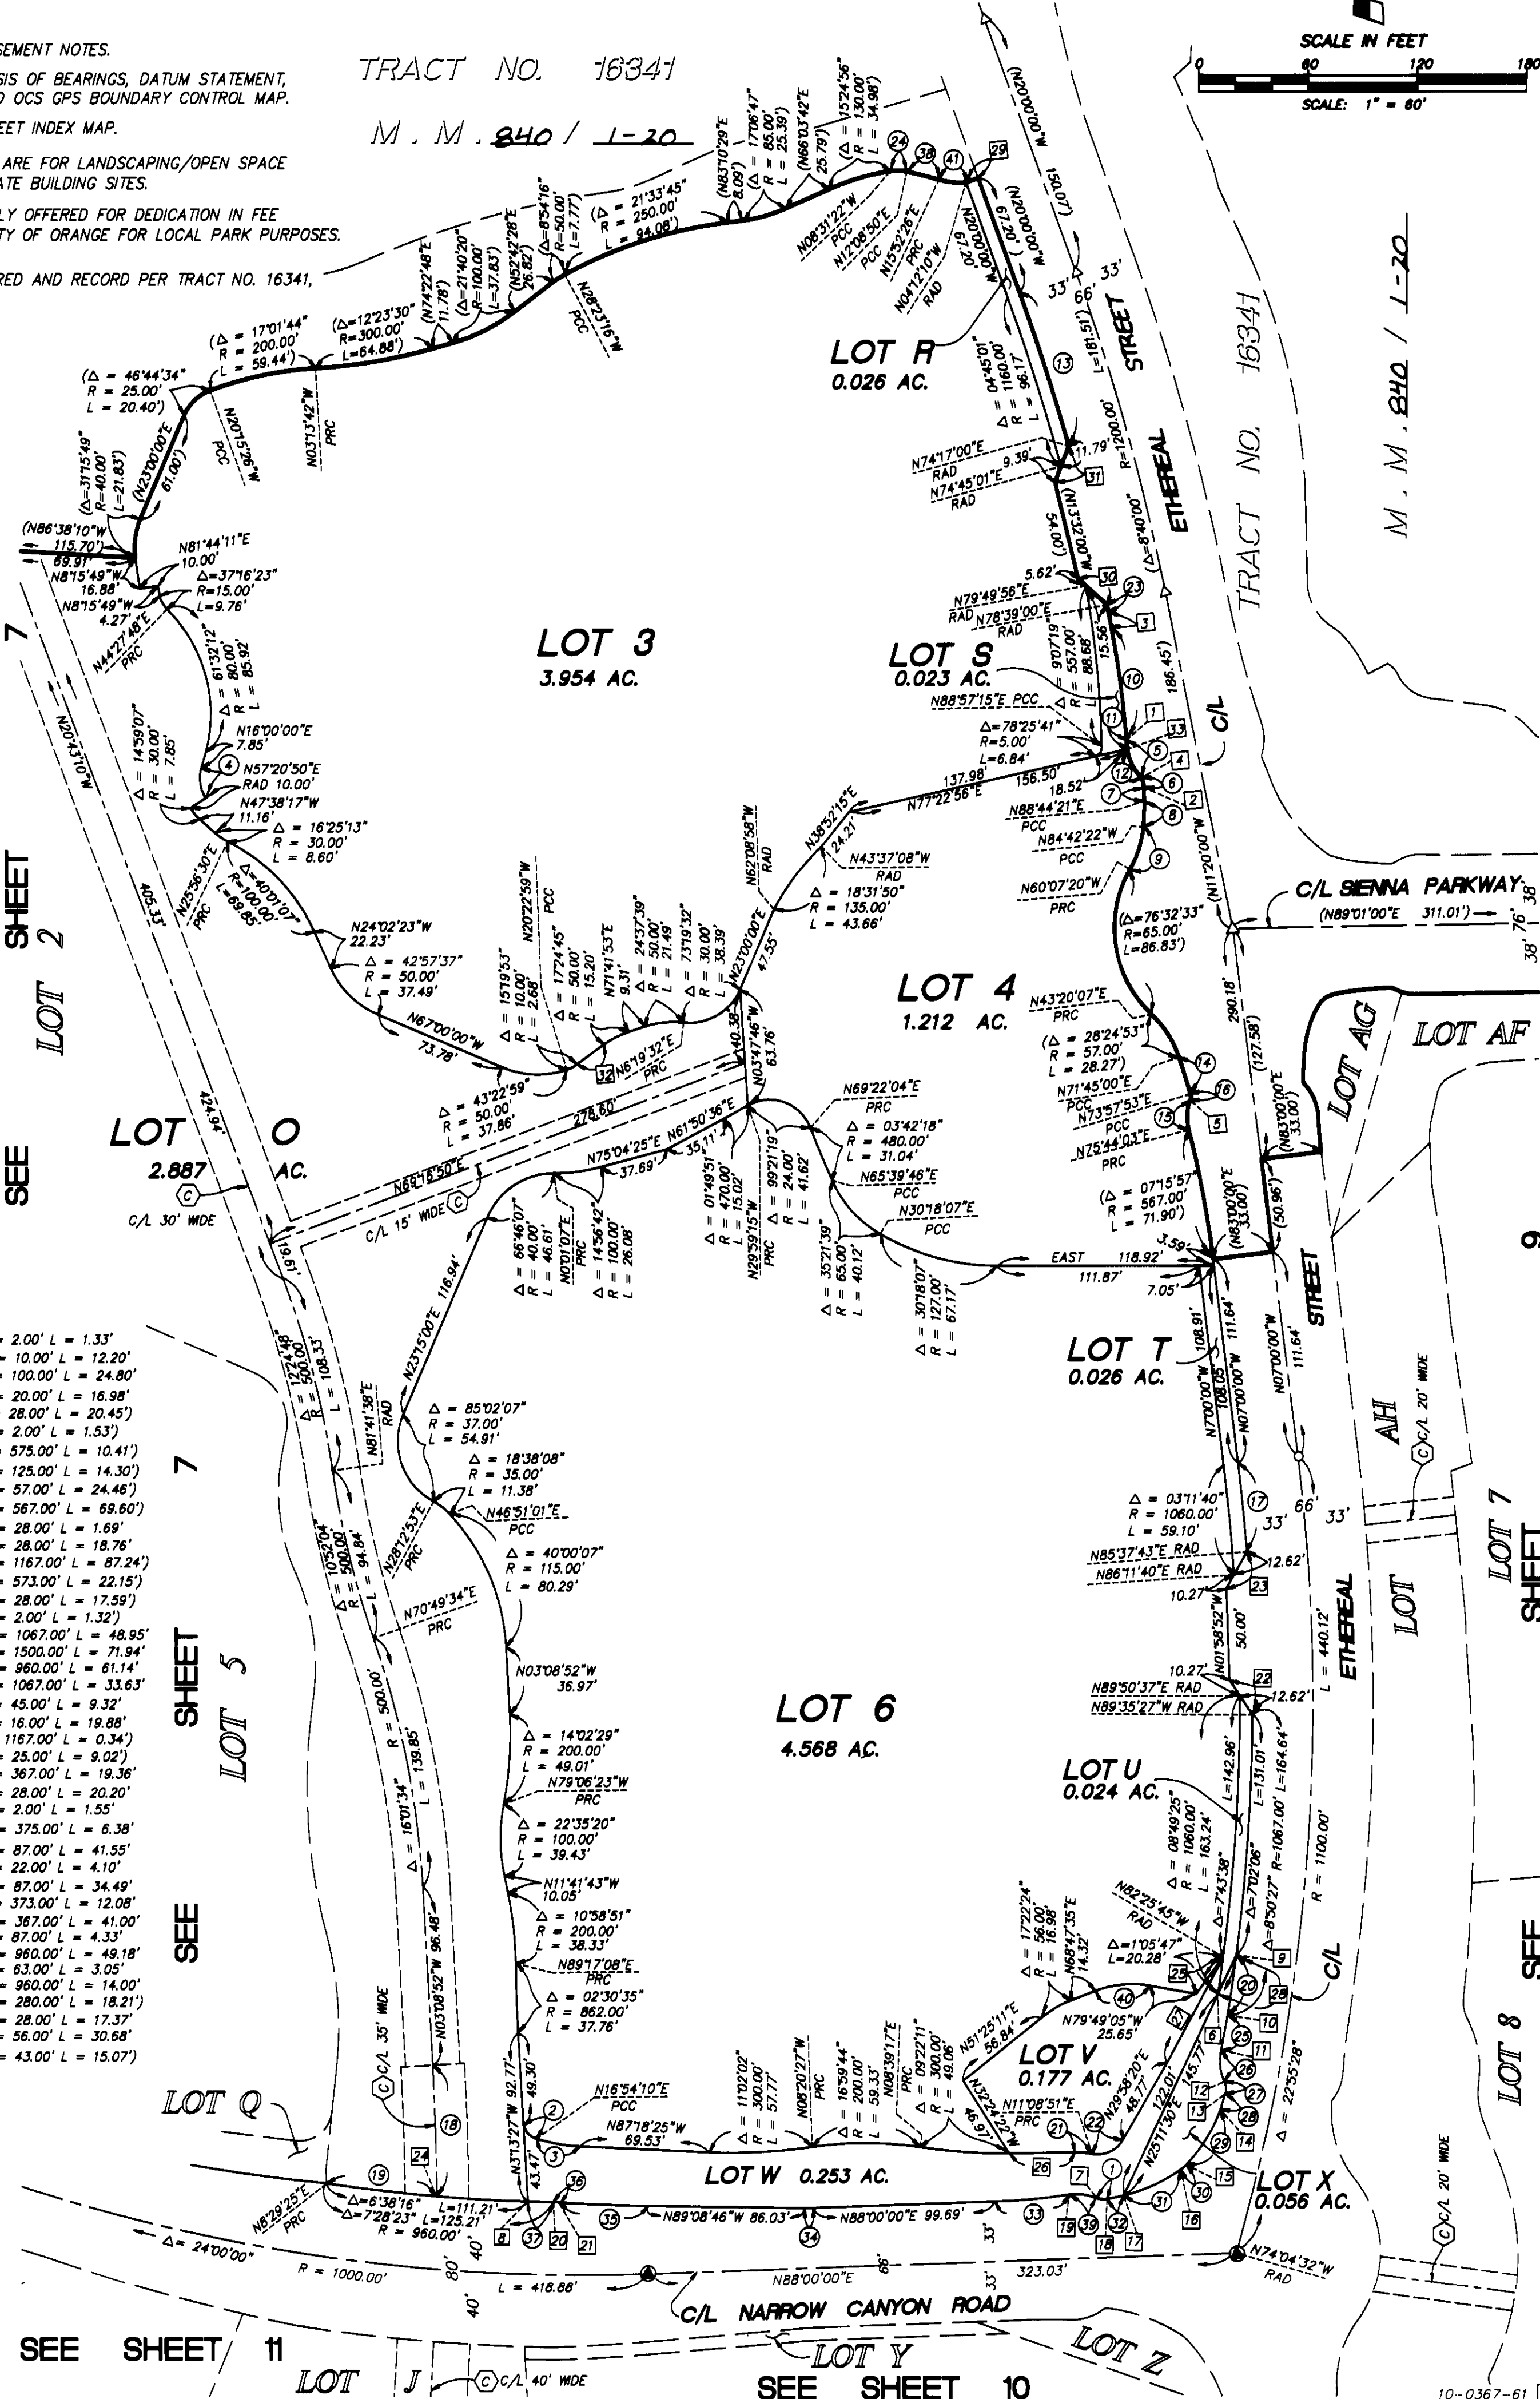

SEE SHEET 11

SEE SHEET 10

SEE SHEET 8

SEE SHEET 7

SEE SHEET 9

839 41

HUITT-ZOLLARS


10 NUMBERED LOTS AND 34 LETTERED LOTS 119.147 ACRES

NOTES:

SEE SHEET 2 FOR EASEMENT NOTES.

SEE SHEET 3 FOR BASIS OF BEARINGS, DATUM STATEMENT,
MONUMENT NOTES AND OCS GPS BOUNDARY CONTROL MAP.
SEE SHEET 4 FOR SHEET INDEX MAP.LOTS A THROUGH AH ARE FOR LANDSCAPING/OPEN SPACE
AND ARE NOT SEPARATE BUILDING SITES.LOTS 4 IS IRREVOCABLY OFFERED FOR DEDICATION IN FEE
SIMPLE TO THE COUNTY OF ORANGE FOR LOCAL PARK PURPOSES.() INDICATES MEASURED AND RECORD PER TRACT NO. 16341,
M.M. 840 / L-20TRACT NO. 16341
M.M. 840 / L-20

SEE SHEET 3

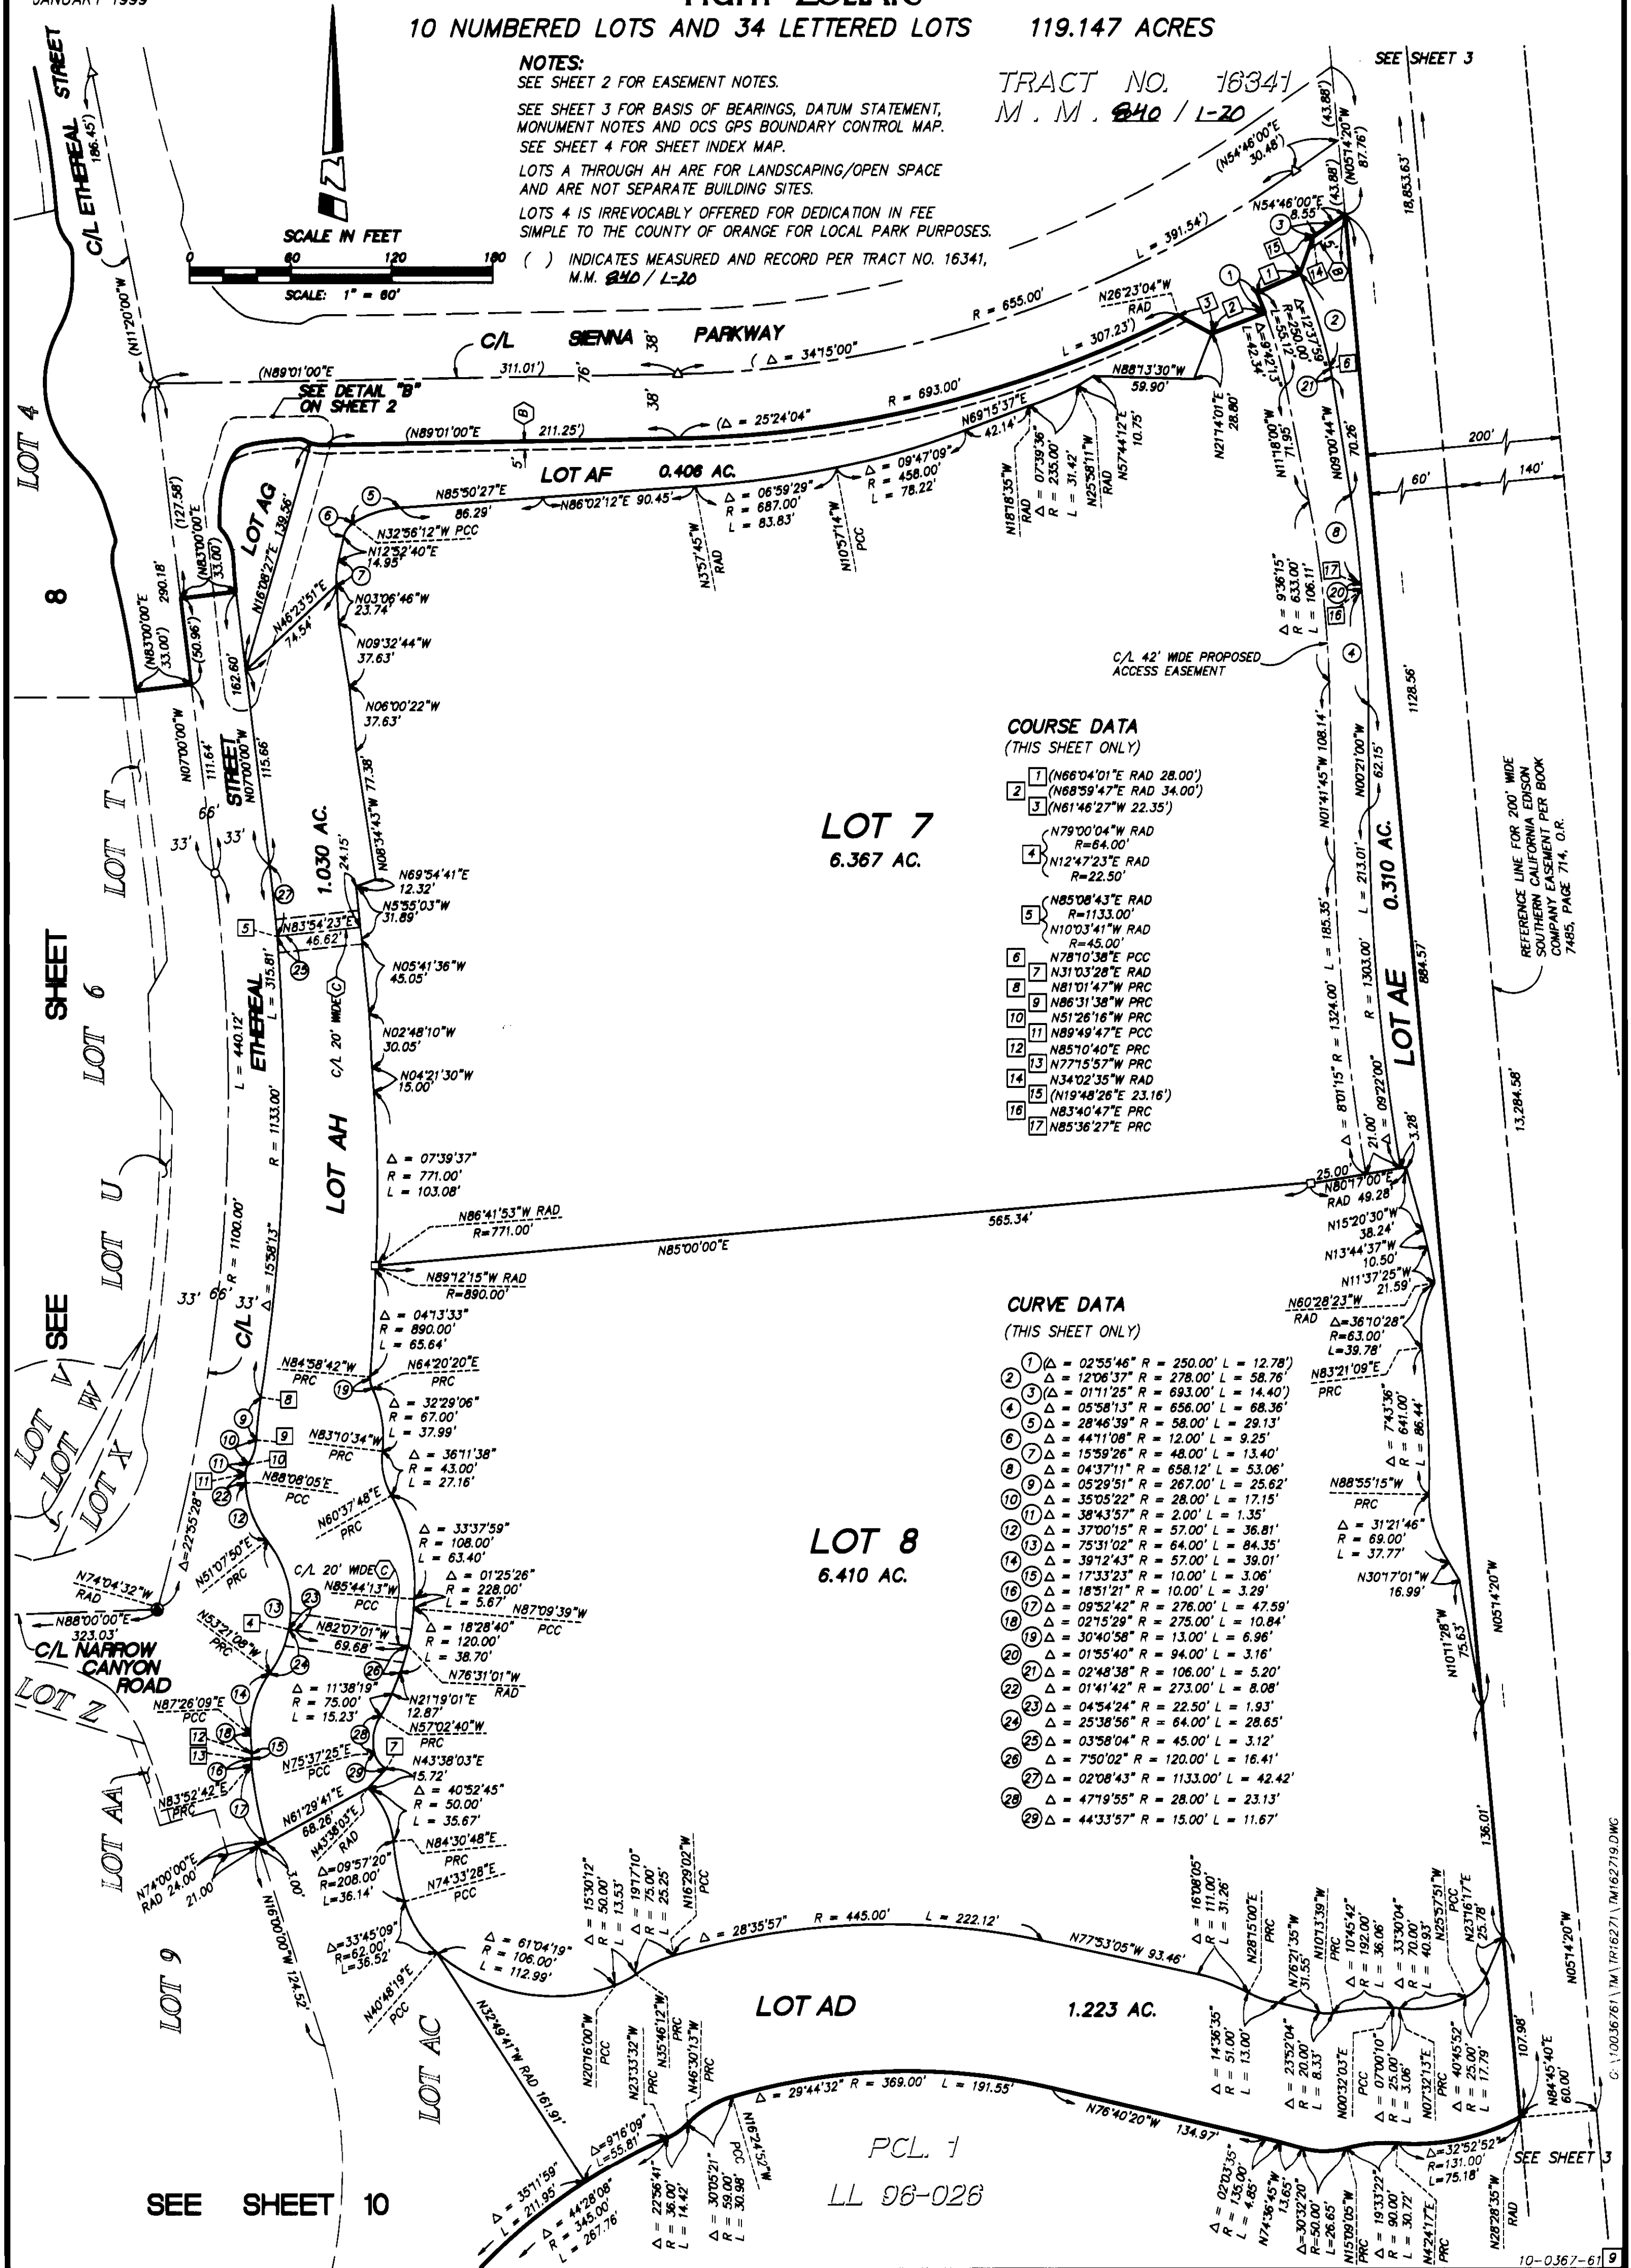REFERENCE LINE FOR 200' WIDE
SOUTHERN CALIFORNIA EDISON
COMPANY EASEMENT PER BOOK
7485, PAGE 714, O.R.

SHEET 10 OF 12 SHEETS

TRACT NO. 16271

FINAL UNIT OF VESTING
TENTATIVE TRACT NO. 16271

IN THE UNINCORPORATED TERRITORY OF ORANGE COUNTY, CALIFORNIA

JULY 2002



JAMES F. GILLEN, L.S. 5557

DATE OF SURVEY:
JANUARY 1999

HUITT-ZOLIARS

10 NUMBERED LOTS AND 34 LETTERED LOTS

119.147 ACRES

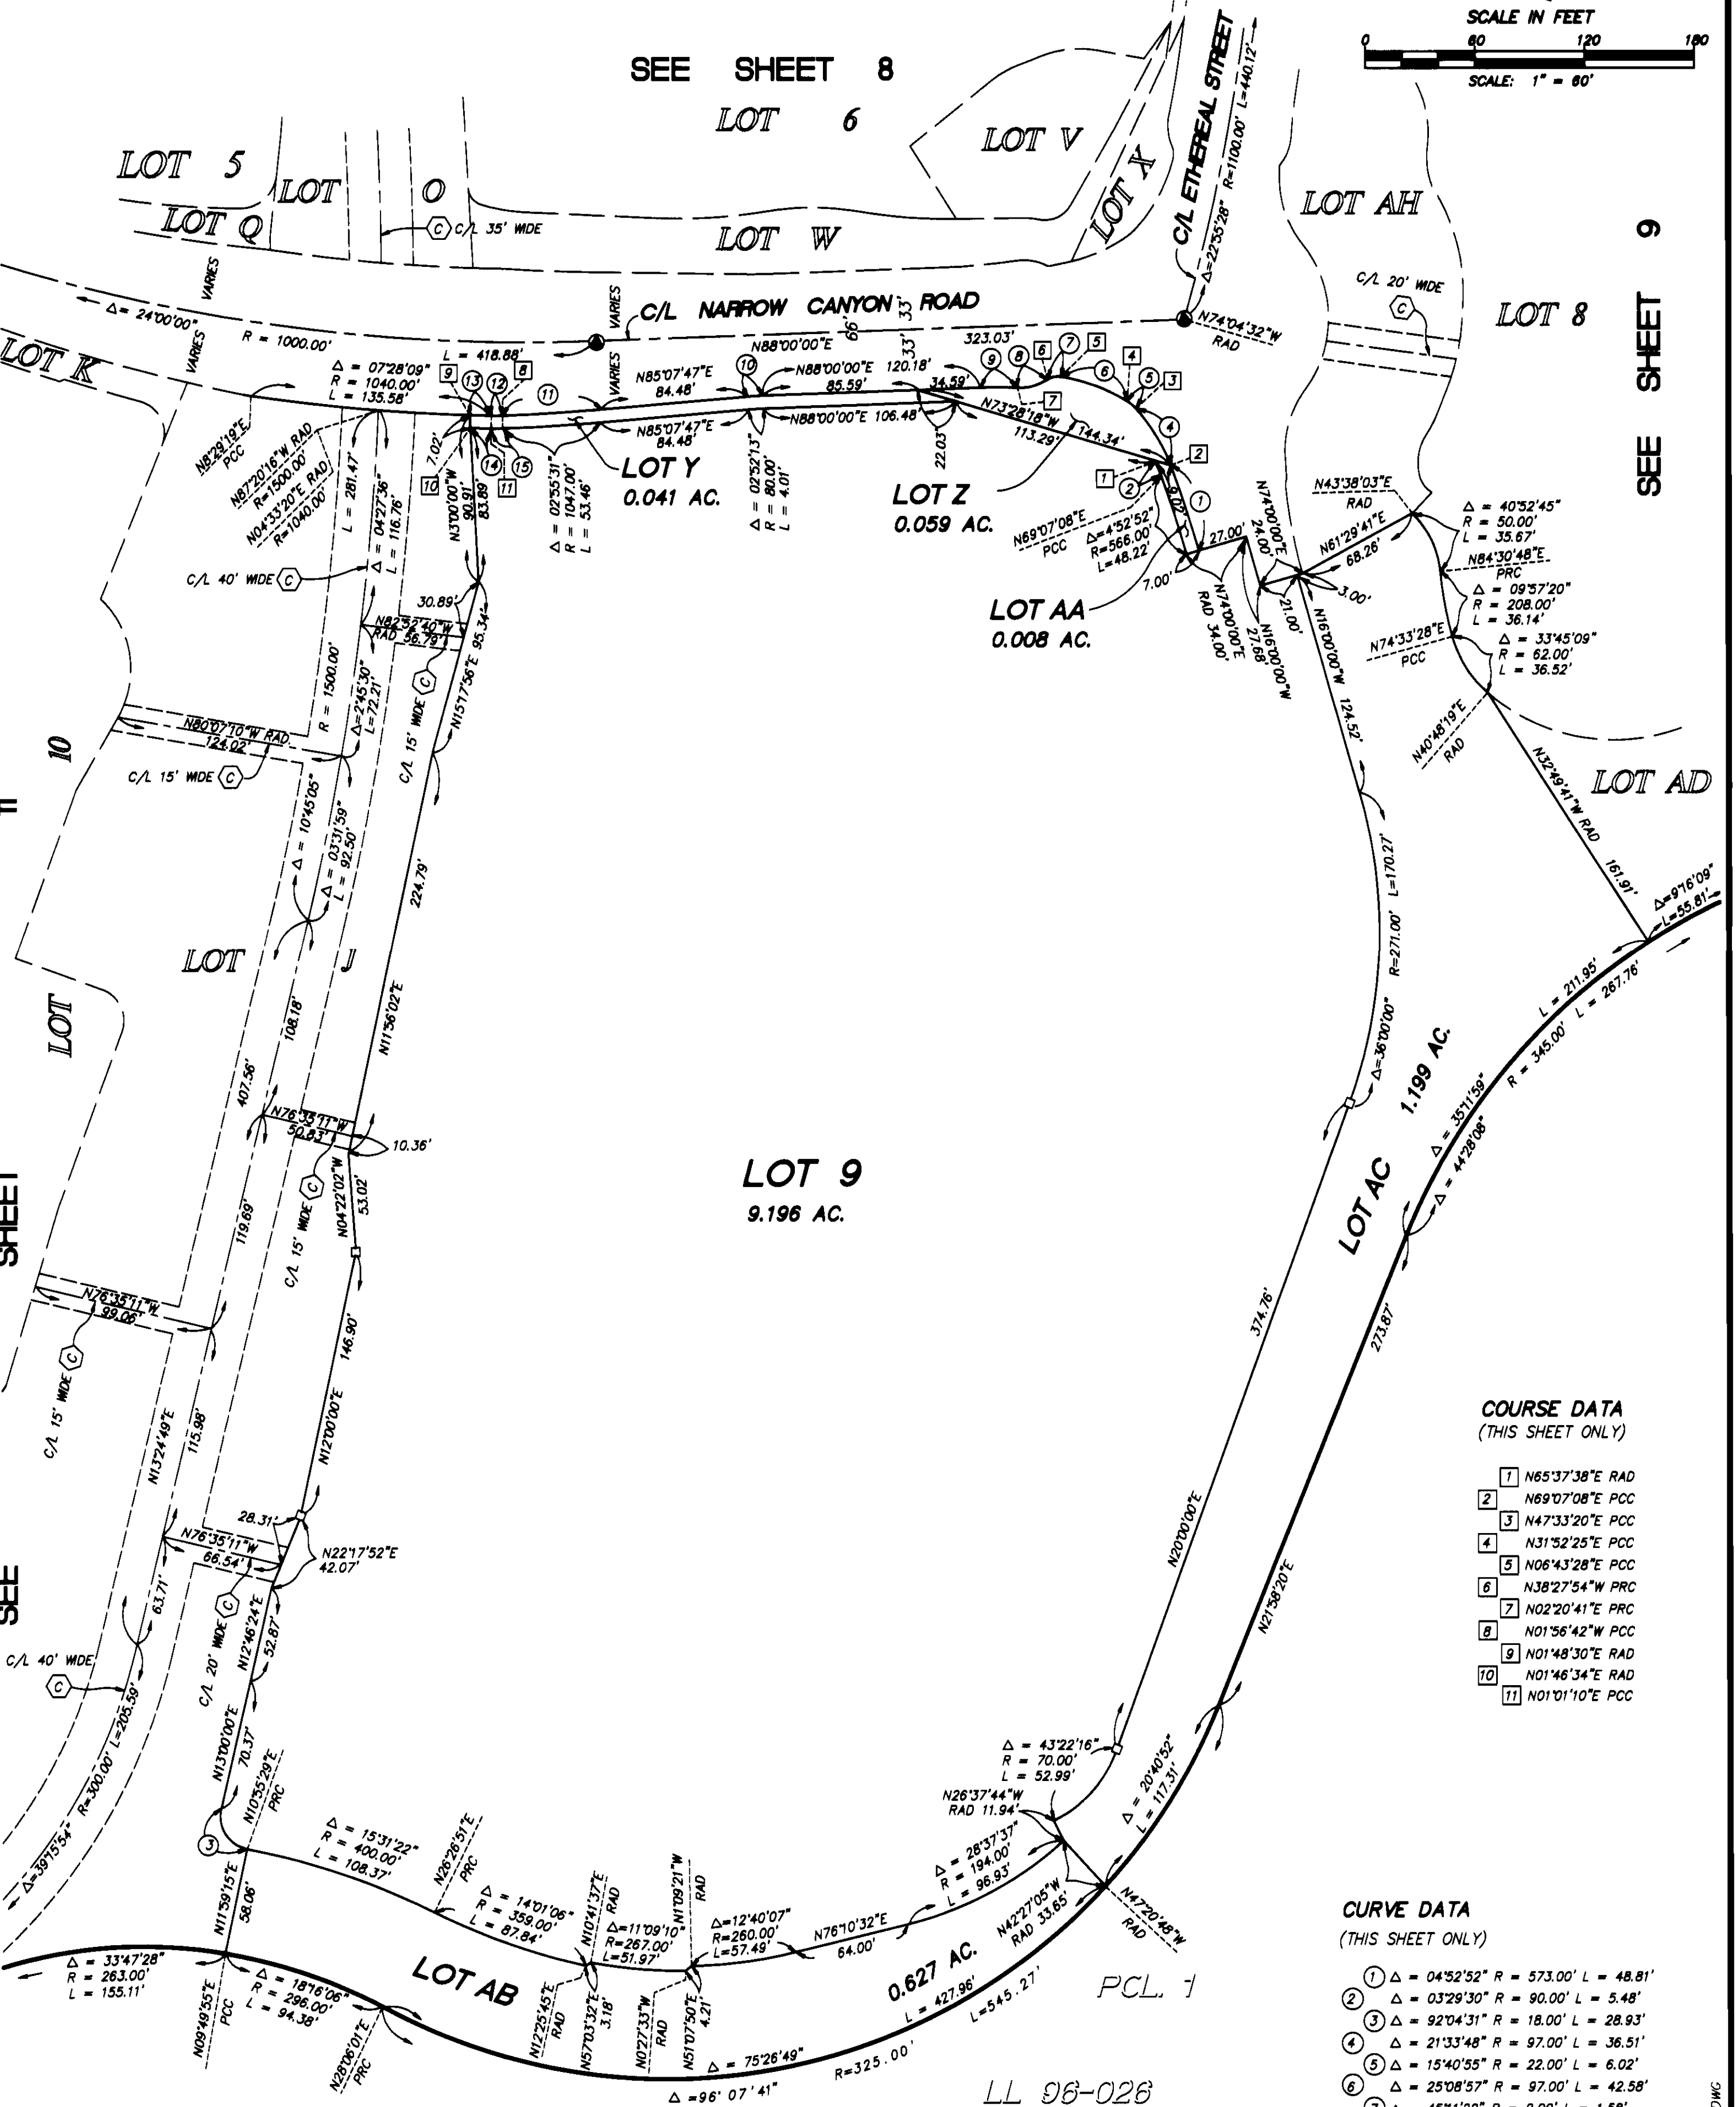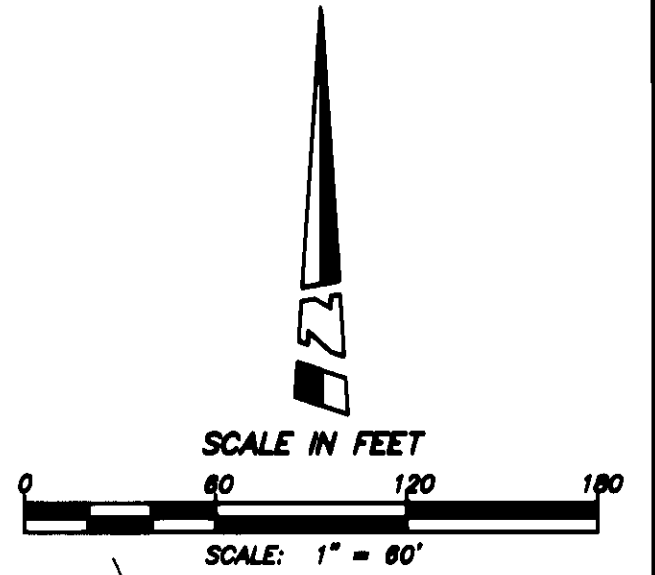

COURSE DATA (THIS SHEET ONLY)

- 1 N65°37'38"E RAD
- 2 N69°07'08"E PCC
- 3 N47°33'20"E PCC
- 4 N31°52'25"E PCC
- 5 N06°43'28"E PCC
- 6 N38°27'54"W PRC
- 7 N02°20'41"E PRC
- 8 N01°56'42"W PCC
- 9 N01°48'30"E RAD
- 10 N01°46'34"E RAD
- 11 N01°01'10"E PCC

CURVE DATA (THIS SHEET ONLY)

- 1 Δ = 04°52'52" R = 573.00' L = 48.81'
- 2 Δ = 03°29'30" R = 90.00' L = 5.48'
- 3 Δ = 92°04'31" R = 18.00' L = 28.93'
- 4 Δ = 21°33'48" R = 97.00' L = 36.51'
- 5 Δ = 15°40'55" R = 22.00' L = 6.02'
- 6 Δ = 25°08'57" R = 97.00' L = 42.58'
- 7 Δ = 45°11'22" R = 2.00' L = 1.58'
- 8 Δ = 40°48'35" R = 28.00' L = 19.94'
- 9 Δ = 04°20'41" R = 267.00' L = 20.25'
- 10 Δ = 02°52'13" R = 87.00' L = 4.36'
- 11 Δ = 02°55'31" R = 1040.00' L = 53.10'
- 12 Δ = 02°57'52" R = 63.00' L = 3.26'
- 13 Δ = 00°47'20" R = 1040.00' L = 14.32'
- 14 Δ = 00°45'24" R = 1047.00' L = 13.83'
- 15 Δ = 02°57'52" R = 70.00' L = 3.62'

NOTES:

- SEE SHEET 2 FOR EASEMENT NOTES.
- SEE SHEET 3 FOR BASIS OF BEARINGS, DATUM STATEMENT, MONUMENT NOTES AND OCS GPS BOUNDARY CONTROL MAP.
- SEE SHEET 4 FOR SHEET INDEX MAP.
- LOTS A THROUGH AH ARE FOR LANDSCAPING/OPEN SPACE AND ARE NOT SEPARATE BUILDING SITES.
- LOT 4 IS IRREVOCABLY OFFERED FOR DEDICATION IN FEE SIMPLE TO THE COUNTY OF ORANGE FOR LOCAL PARK PURPOSES.

INST. NO. 19960587414, O.R.

TRACT NO. 16271

IN THE UNINCORPORATED TERRITORY OF ORANGE COUNTY, CALIFORNIA


JULY 2002

JAMES F. GILLEN, L.S. 5557

HUITT-ZOLIARS

10 NUMBERED LOTS AND 34 LETTERED LOTS

119.147 ACRES

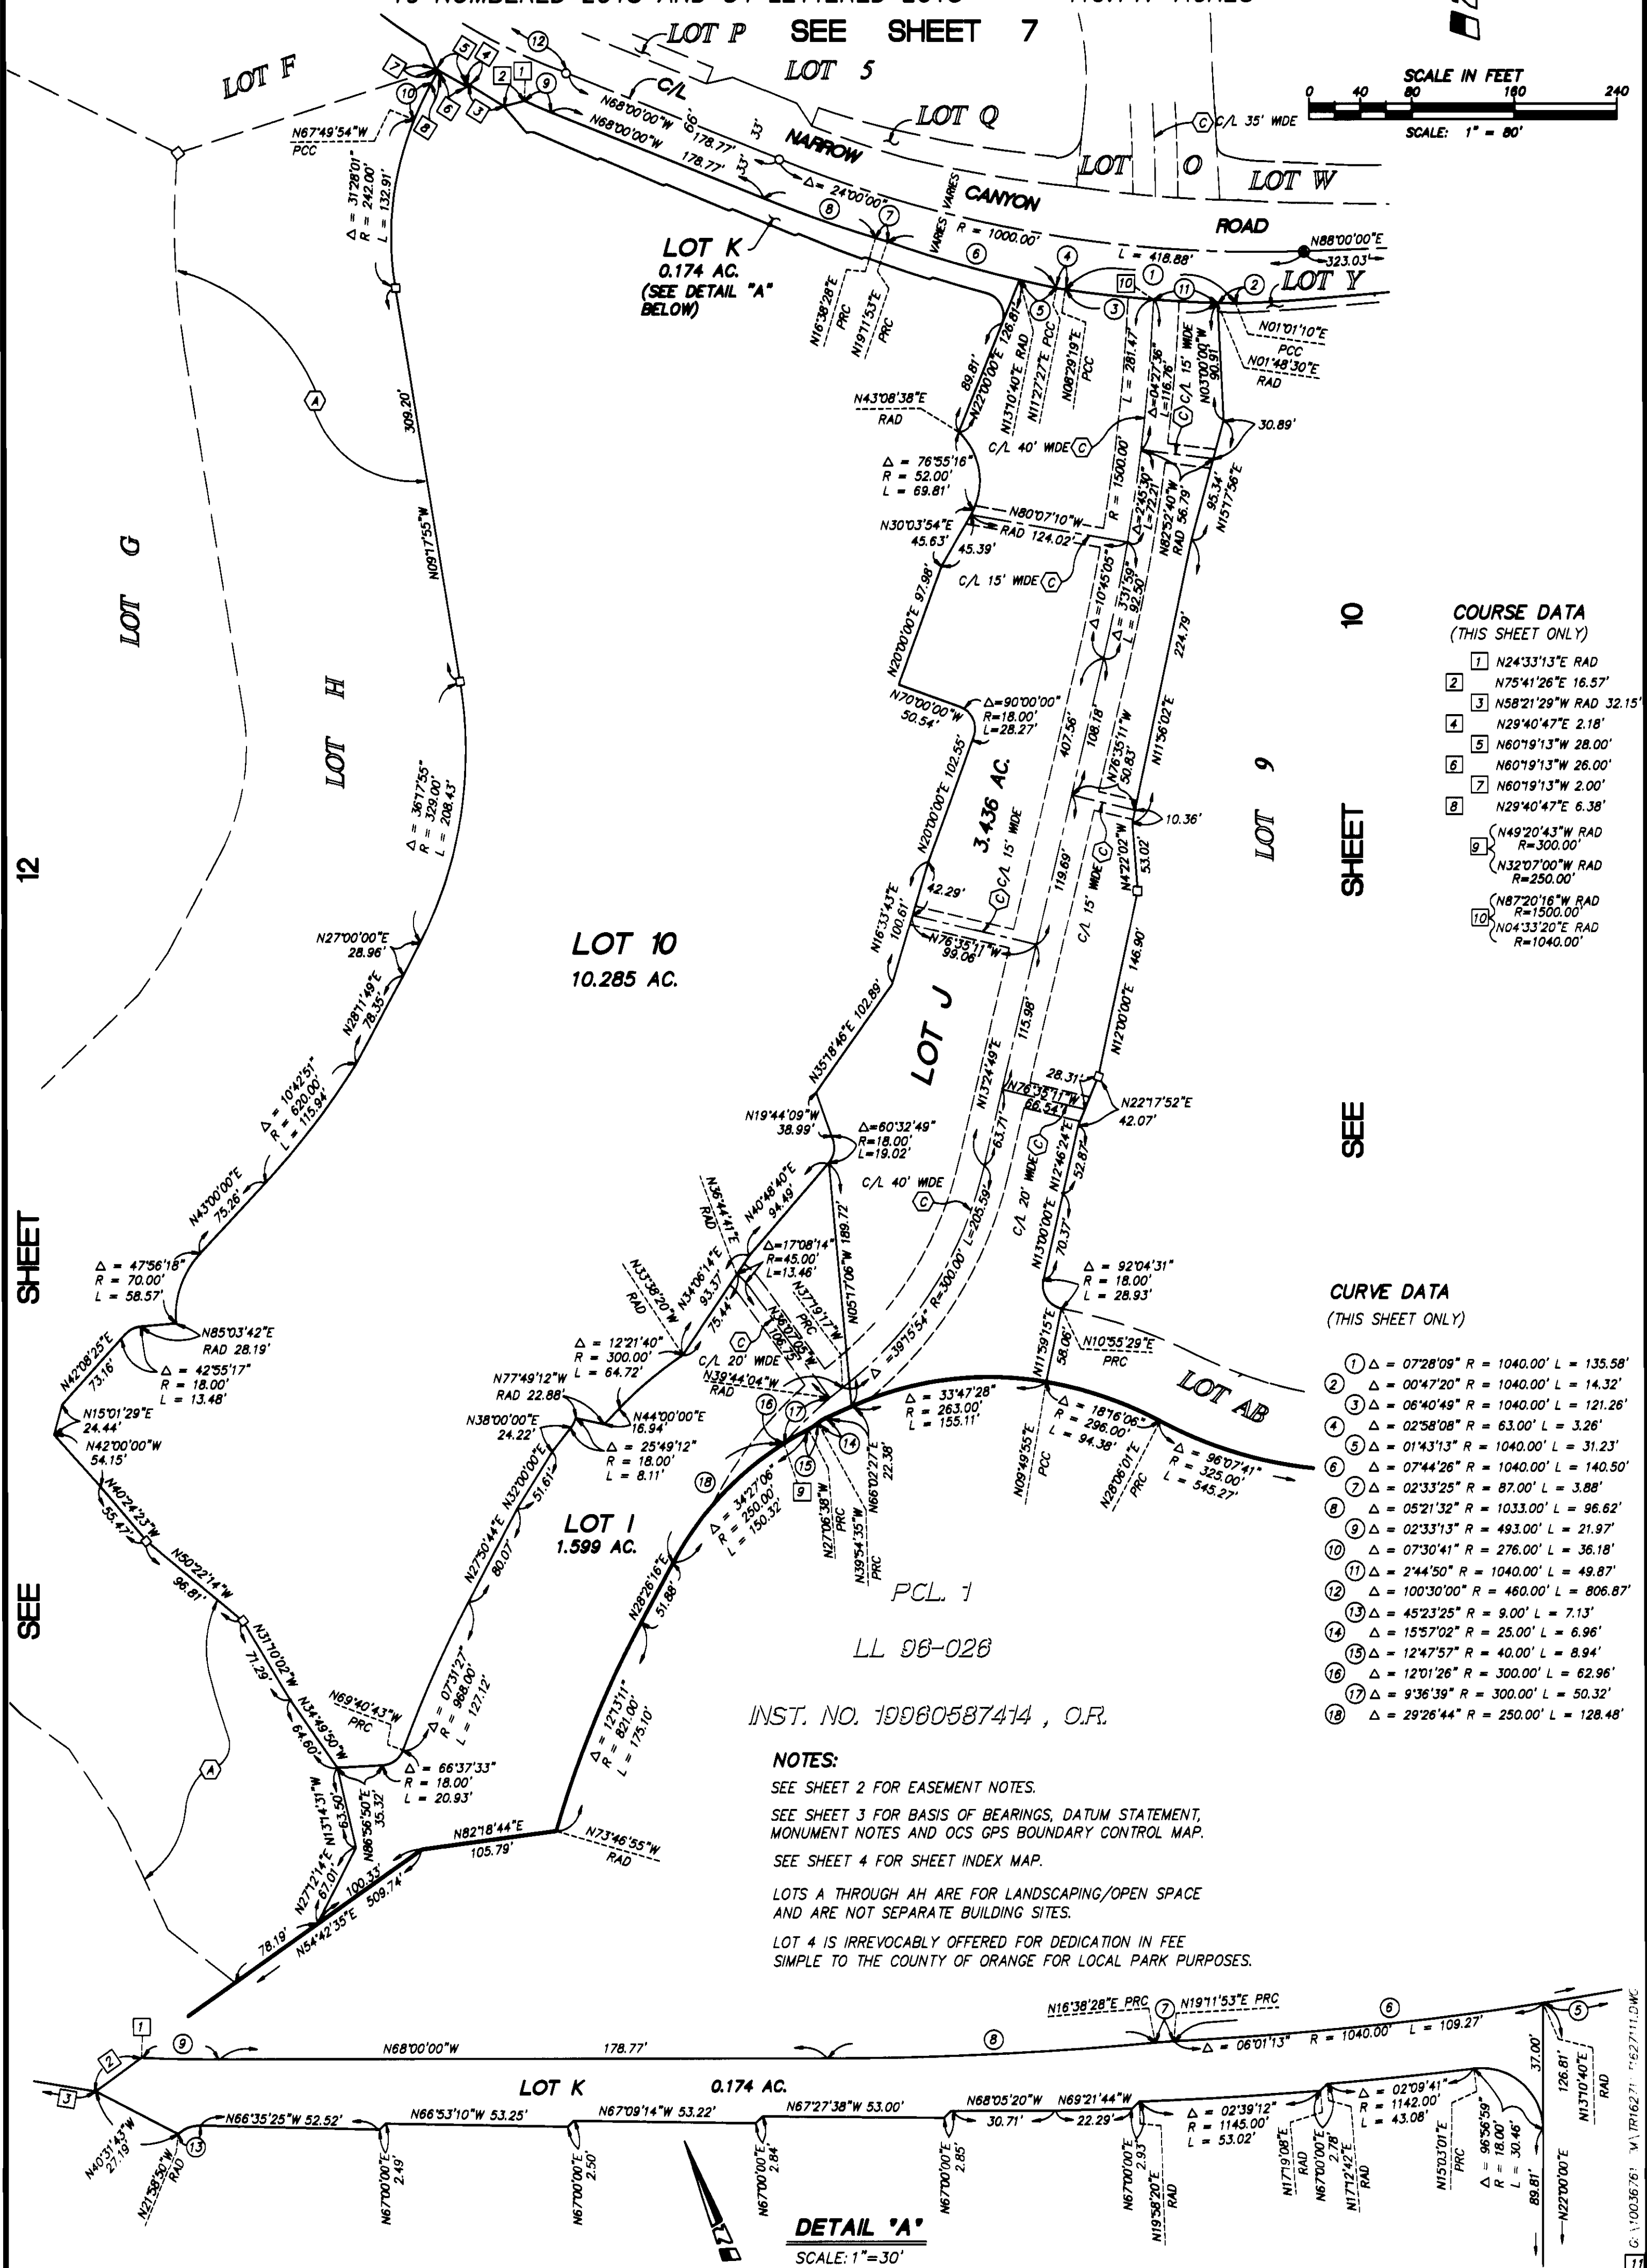LOT P SEE SHEET 7
LOT 5

INST. NO. 19960587414, O.R.

NOTES:

SEE SHEET 2 FOR EASEMENT NOTES.

SEE SHEET 3 FOR BASIS OF BEARINGS, DATUM STATEMENT, MONUMENT NOTES AND OCS GPS BOUNDARY CONTROL MAP.

SEE SHEET 4 FOR SHEET INDEX MAP.

LOTS A THROUGH AH ARE FOR LANDSCAPING/OPEN SPACE AND ARE NOT SEPARATE BUILDING SITES.

LOT 4 IS IRREVOCABLY OFFERED FOR DEDICATION IN FEE SIMPLE TO THE COUNTY OF ORANGE FOR LOCAL PARK PURPOSES.

839 45

SHEET 12 OF 12 SHEETS

TRACT NO. 16271

IN THE UNINCORPORATED TERRITORY OF ORANGE COUNTY, CALIFORNIA

JULY 2002

JAMES F. GILLEN, L.S. 5557


FINAL UNIT OF VESTING
TENTATIVE TRACT NO. 16271

DATE OF SURVEY:
JANUARY 1999

HUITT-ZOLIARS

10 NUMBERED LOTS AND 34 LETTERED LOTS

119.147 ACRES

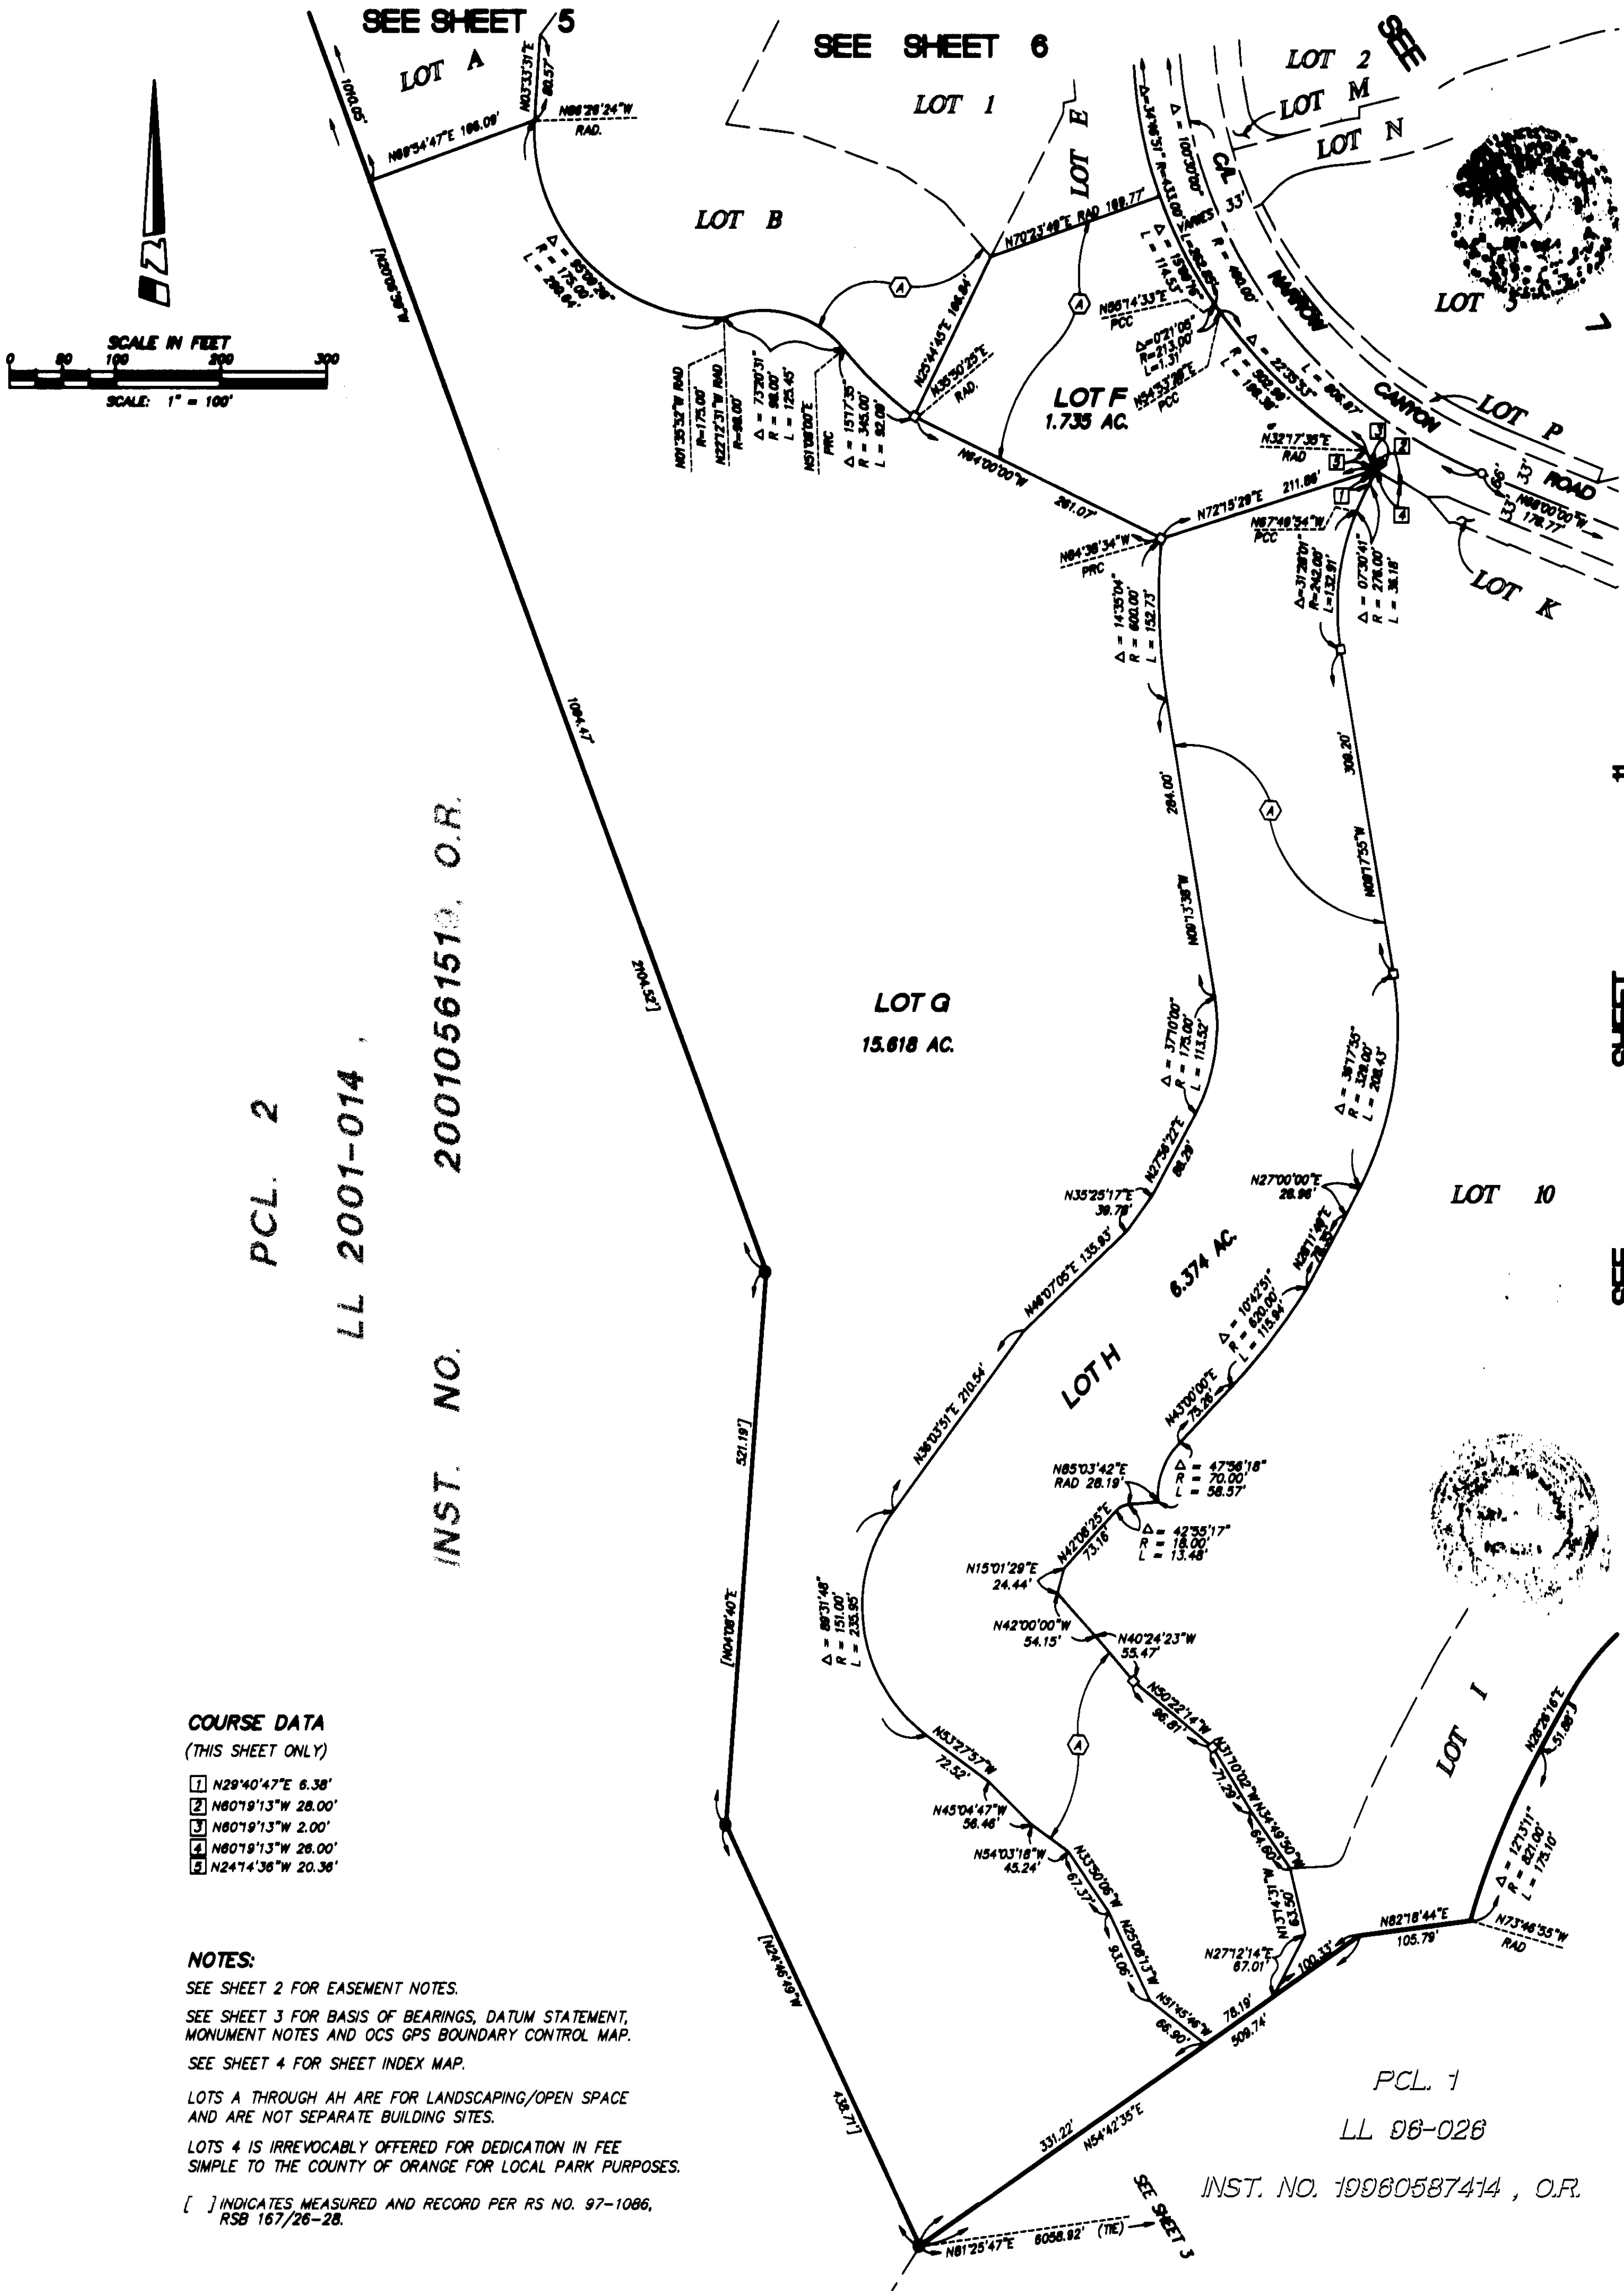

COURSE DATA (THIS SHEET ONLY)

- 1 N29°40'47"E 6.38'
- 2 N80°19'13"W 28.00'
- 3 N80°19'13"W 2.00'
- 4 N80°19'13"W 28.00'
- 5 N24°14'36"W 20.36'

NOTES:

SEE SHEET 2 FOR EASEMENT NOTES.
SEE SHEET 3 FOR BASIS OF BEARINGS, DATUM STATEMENT,
MONUMENT NOTES AND OCS GPS BOUNDARY CONTROL MAP.
SEE SHEET 4 FOR SHEET INDEX MAP.
LOTS A THROUGH AH ARE FOR LANDSCAPING/OPEN SPACE
AND ARE NOT SEPARATE BUILDING SITES.
LOTS 4 IS IRREVOCABLY OFFERED FOR DEDICATION IN FEE
SIMPLE TO THE COUNTY OF ORANGE FOR LOCAL PARK PURPOSES.
[] INDICATES MEASURED AND RECORD PER RS NO. 97-1086,
RSB 167/26-28.

PCL. 1
LL 96-026
INST. NO. 19960587414, O.R.

11
SHEET
SEE

G:\10036761\TM\16271\1627112.DWG

839 45