

A PORTION OF VESTING
TENTATIVE TRACT NO. 16271DATE OF SURVEY:
JANUARY 1999IN THE UNINCORPORATED TERRITORY OF ORANGE COUNTY, CALIFORNIA
BEING A SUBDIVISION OF A PORTION OF PARCEL 1 OF LOT LINE ADJUSTMENT NO. LL 96-026
AS SHOWN ON EXHIBIT "B" ATTACHED TO THAT CERTAIN DOCUMENT RECORDED NOVEMBER 21,
1996 AS INSTRUMENT NO. 19960587414 OF OFFICIAL RECORDS, RECORDS OF ORANGE COUNTY,
CALIFORNIA.

JUNE 2002

JAMES F. GILLEN, L.S. 5557

HUITT-ZOLLARS

17 NUMBERED LOTS AND 63 LETTERED LOTS

168.726 ACRES

ACCEPTED AND FILED AT THE
REQUEST OF

FIRST AMERICAN TITLE INSURANCE COMPANY

DATE FEBRUARY 27, 2003TIME 10:34 AM FEE \$ 45.00INSTRUMENT NO. 200300216512BOOK 840 PAGE 1-20 M/M

TOM DALY

COUNTY CLERK-RECORDER

BY [Signature]

DEPUTY

OWNERSHIP CERTIFICATE:

WE, THE UNDERSIGNED, BEING ALL PARTIES HAVING ANY RECORD TITLE INTEREST IN THE LAND COVERED BY THIS MAP, DO HEREBY CONSENT TO THE PREPARATION AND RECORDATION OF SAID MAP, AS SHOWN WITHIN THE DISTINCTIVE BORDER LINE. WE ALSO HEREBY DEDICATE TO THE PUBLIC FOR STREET PURPOSES: NARROW CANYON ROAD, ETHEREAL STREET, ETON PLACE, TRIAD LANE, GAIA LANE, CLARIN STREET, AURA LANE, SOL STREET, SIENNA PARKWAY, AND O'NEILL DRIVE.

WE ALSO HEREBY DEDICATE TO THE COUNTY OF ORANGE:

(1) THE EASEMENTS FOR SIDEWALK PURPOSES AS SHOWN ON SAID MAP.

(2) THE EASEMENTS FOR STORM DRAIN PURPOSES AS SHOWN ON SAID MAP.

(3) THE SCENIC PRESERVATION EASEMENT OVER ALL OF LOTS C, E, G, AND J, AS SHOWN ON SAID MAP FOR THE PURPOSES AND SUBJECT TO THE SAME CONDITIONS AND LIMITATIONS AS SHOWN IN THAT CERTAIN EASEMENT RECORDED OCTOBER 19, 1991 AS INSTRUMENT 91-518220 OF OFFICIAL RECORDS.

WE ALSO HEREBY RELEASE AND RELINQUISH TO THE COUNTY OF ORANGE ALL VEHICULAR ACCESS RIGHTS TO O'NEILL DRIVE AND SIENNA PARKWAY, EXCEPT AT APPROVED ACCESS LOCATIONS.

WE ALSO HEREBY DEDICATE TO THE COUNTY OF ORANGE AN EASEMENT OVER LOT 11 FOR PRIVATE LOCAL PARK PURPOSES, SUBJECT TO THE SAME TERMS AND CONDITIONS AS THAT CERTAIN DOCUMENT RECORDED OCTOBER 7, 1987 AS INSTRUMENT NO. 87-563594, OF OFFICIAL RECORDS, COUNTY OF ORANGE.

PURSUANT TO SECTION 7050 OF THE GOVERNMENT CODE, WE HEREBY IRREVOCABLY OFFER TO DEDICATE TO THE COUNTY OF ORANGE LOTS 4 AND 5 IN FEE SIMPLE FOR LOCAL PARK PURPOSES, TOGETHER WITH THE RIGHT TO GRANT EASEMENTS FOR PUBLIC UTILITIES OR OTHER ESSENTIAL PURPOSES.

DMB LADERA, L.L.C., A DELAWARE LIMITED LIABILITY COMPANY.

BY: RANCHO MISSION VEJO, L.L.C., A DELAWARE LIMITED LIABILITY COMPANY,
AS AGENT AND/OR MANAGER.BY: [Signature]
PRINT NAME: DONALD T. STARKIN
PRINT TITLE: DIRECTORBY: [Signature]
PRINT NAME: Stephen C. Schrank
PRINT TITLE: Executive Vice PresidentSTATE OF CALIFORNIA)
COUNTY OF ORANGE)

ON THIS 13th DAY OF AUGUST, 2002, BEFORE ME,
LINDA K. LEDGER, A NOTARY PUBLIC IN AND FOR SAID STATE,
PERSONALLY APPEARED DONALD T. STARKIN AND
STEPHEN C. SCHRANK, PERSONALLY KNOWN TO ME OR PROVED TO ME
ON THE BASIS OF SATISFACTORY EVIDENCE TO BE THE PERSONS WHOSE NAMES
ARE SUBSCRIBED TO THE WITHIN INSTRUMENT AND ACKNOWLEDGED TO ME THAT
THEY EXECUTED THE SAME IN THEIR AUTHORIZED CAPACITIES, AND THAT BY THEIR
SIGNATURES ON THE INSTRUMENT THE PERSONS, OR THE ENTITY UPON BEHALF
OF WHICH THE PERSONS ACTED, EXECUTED THE INSTRUMENT.

WITNESS MY HAND:

MY COMMISSION EXPIRES 3/7/03[Signature]
NOTARY PUBLIC IN AND FOR SAID STATEMY PRINCIPAL PLACE OF BUSINESS
IS IN ORANGE COUNTY.Linda K. Ledger
PRINT NAME

AUTOMATIC FIRE SPRINKLER NOTE:

ALL COMMERCIAL STRUCTURES GREATER THAN 6,000 SQUARE FEET; ALL MULTIFAMILY RESIDENTIAL STRUCTURES; ALL SINGLE-FAMILY STRUCTURES EXCEEDING 5,500 SQUARE FEET, AND ALL STRUCTURES EXCEEDING FIRE DEPARTMENT ACCESS REQUIREMENTS SHALL BE PROTECTED BY AN AUTOMATIC SPRINKLER SYSTEM.

SPECIAL FIRE PROTECTION NOTE:

PROPERTY IS IN A SPECIAL FIRE PROTECTION AREA AND MUST MEET ALL REQUIREMENTS FOR DEVELOPMENT WITHIN THE AREA.

HIGH FIRE HAZARD AREA NOTE:

THE LOTS SHOWN ON THIS MAP ARE IN A HIGH FIRE HAZARD AREA DUE TO WILD LAND EXPOSURE.

NOTE:

SEE SHEET 2 FOR SIGNATURE OMISSIONS.

SURVEYOR'S STATEMENT:

THIS MAP WAS PREPARED BY ME OR UNDER MY DIRECTION AND IS BASED UPON A FIELD SURVEY IN CONFORMANCE WITH THE REQUIREMENTS OF THE SUBDIVISION MAP ACT AND LOCAL ORDINANCES AT THE REQUEST OF RANCHO MISSION VEJO, LLC ON MARCH 2002. I HEREBY STATE THAT ALL MONUMENTS ARE OF THE CHARACTER AND OCCUPY THE POSITIONS INDICATED, OR THAT THEY WILL BE SET IN SUCH POSITIONS; AND THAT SAID MONUMENTS ARE SUFFICIENT TO ENABLE THE SURVEY TO BE RETRACED. I HEREBY STATE THAT THIS FINAL MAP SUBSTANTIALLY CONFORMS TO THE CONDITIONALLY APPROVED TENTATIVE MAP.



[Signature]
JAMES F. GILLEN
L.S. 5557
EXPIRATION DATE: 9/30/05

COUNTY SURVEYOR'S STATEMENT:

I HEREBY STATE THAT I HAVE EXAMINED THIS MAP AND HAVE FOUND IT TO BE SUBSTANTIALLY IN CONFORMANCE WITH THE TENTATIVE MAP AS FILED WITH, AMENDED AND APPROVED BY THE ORANGE COUNTY SUBDIVISION COMMITTEE; THAT ALL PROVISIONS OF THE SUBDIVISION MAP ACT AND COUNTY SUBDIVISION REGULATIONS HAVE BEEN COMPLIED WITH AND I AM SATISFIED SAID MAP IS TECHNICALLY CORRECT.

DATED THIS 7TH DAY OF FEBRUARY, 2003.

[Signature]
JOHN CANAS, COUNTY SURVEYOR
LS 4408 EXPIRATION DATE: 09-30-05

BY: MICHAEL K. SULLIVAN, DEPUTY
LS 6284 EXPIRES 03/30/03



COUNTY TREASURER-TAX COLLECTOR'S CERTIFICATE:

STATE OF CALIFORNIA)
COUNTY OF ORANGE)

I HEREBY CERTIFY THAT ACCORDING TO THE RECORDS OF MY OFFICE THERE ARE NO LIENS AGAINST THE LAND COVERED BY THIS MAP OR ANY PART THEREOF FOR UNPAID STATE, COUNTY, MUNICIPAL OR LOCAL TAXES OR SPECIAL ASSESSMENTS COLLECTED AS TAXES, EXCEPT TAXES OR SPECIAL ASSESSMENTS COLLECTED AS TAXES NOT YET PAYABLE.

AND DO ALSO HEREBY CERTIFY TO THE RECORDER OF ORANGE COUNTY THAT THE PROVISIONS OF THE SUBDIVISION MAP ACT HAVE BEEN COMPLIED WITH REGARDING DEPOSITS TO SECURE THE PAYMENT OF TAXES OR SPECIAL ASSESSMENTS COLLECTED AS TAXES ON THE LAND COVERED BY THIS MAP.

DATED THE 6TH DAY OF February, 2003.

JOHN M.W. MOORLACH
COUNTY TREASURER-TAX COLLECTOR

BY: [Signature]
DEPUTY TREASURER-TAX COLLECTOR

CLERK OF THE BOARD OF SUPERVISORS' CERTIFICATE:

STATE OF CALIFORNIA)
COUNTY OF ORANGE)

I HEREBY CERTIFY THAT THIS MAP WAS PRESENTED FOR APPROVAL TO THE BOARD OF SUPERVISORS OF ORANGE COUNTY AT A REGULAR MEETING THEREOF HELD ON THE 25th DAY OF FEBRUARY, 2003 AND THAT THEREUPON SAID BOARD DID, BY AN ORDER DULY PASSED AND ENTERED, APPROVE SAID MAP AND DID ACCEPT ON BEHALF OF THE PUBLIC, SUBJECT TO IMPROVEMENTS: THE DEDICATION FOR STREET PURPOSES OF: NARROW CANYON ROAD, ETHEREAL STREET, ETON PLACE, TRIAD LANE, GAIA LANE, CLARIN STREET, AURA LANE, SOL STREET, SIENNA PARKWAY, AND O'NEILL DRIVE.

AND DID ALSO ACCEPT ON BEHALF OF THE COUNTY OF ORANGE:

1. THE EASEMENTS FOR SIDEWALK PURPOSES AS DEDICATED.
2. THE EASEMENTS FOR STORM DRAIN PURPOSES AS DEDICATED.
3. THE EASEMENTS FOR SCENIC PRESERVATION PURPOSES AS DEDICATED.
4. THE VEHICULAR ACCESS RIGHTS TO O'NEILL DRIVE AND SIENNA PARKWAY AS RELEASED AND RELINQUISHED.

AND DID ACCEPT THE EASEMENT OVER LOT 11 FOR PRIVATE LOCAL PARK PURPOSES AS DEDICATED.

AND DID NOT ACCEPT THE IRREVOCABLE OFFER OF LOTS 4 AND 5 FOR LOCAL PARK PURPOSES AS DEDICATED.

DATED THIS 25th DAY OF FEBRUARY, 2003.

[Signature]
DARLENE J. BLOOM
CLERK OF THE BOARD OF SUPERVISORS



840 2

TRACT NO. 16341

A PORTION OF VESTING
TENTATIVE TRACT NO. 16271

IN THE UNINCORPORATED TERRITORY OF ORANGE COUNTY, CALIFORNIA

JUNE 2002

JAMES F. GILLEN, L.S. 5557

DATE OF SURVEY:
JANUARY 1999

HUITT-ZOLIARS

17 NUMBERED LOTS AND 63 LETTERED LOTS

168.726 ACRES

SIGNATURE OMISSIONS:

IN ACCORDANCE WITH THE PROVISIONS OF SECTION 664.36(a) (3) OF THE SUBDIVISION
MAP ACT, THE FOLLOWING SIGNATURES HAVE BEEN OMITTED:




1. SFPP, L.P., HOLDER OF AN EASEMENT FOR PUBLIC UTILITIES AND INCIDENTAL PURPOSES RECORDED
DECEMBER 6, 1999 AS INSTRUMENT NO. 19990831017 AS AMENDED BY A DOCUMENT RECORDED
NOVEMBER 5, 2001 AS INSTRUMENT NO. 20010787529, BOTH OF OFFICIAL RECORDS.
2. LADERA DEVELOPMENT COMPANY, L.L.C., HOLDER OF OIL, GAS, MINERAL, AND WATER RIGHTS
RECORDED DECEMBER 10, 1996 AS INSTRUMENT NO. 19960624029 OF OFFICIAL RECORDS.

EASEMENT NOTES:

- (A) INDICATES EASEMENT FOR SCENIC PRESERVATION PURPOSES DEDICATED TO THE COUNTY OF ORANGE.
- (B) INDICATES SIDEWALK EASEMENT DEDICATED TO THE COUNTY OF ORANGE.
- (C) INDICATES STORM DRAIN EASEMENT DEDICATED TO THE COUNTY OF ORANGE.
- (D) INDICATES A UTILITY EASEMENT DEDICATED TO SFPP, L.P., PER INSTRUMENT NO. 20010787529, O.R.
- (E) INDICATES EASEMENT FOR PUBLIC UTILITIES AND INCIDENTAL PURPOSES TO PACIFIC
BELL TELEPHONE COMPANY PER INSTRUMENT NO. 2002001094687, O.R.

SIGNATURE OMISSIONS: (CONTINUED)

3. PACIFIC BELL TELEPHONE COMPANY, HOLDER OF AN
EASEMENT FOR PUBLIC UTILITIES AND INCIDENTAL
PURPOSES RECORDED DECEMBER 4, 2002 AS
INSTRUMENT NO. 2002001094687 OF OFFICIAL RECORDS.

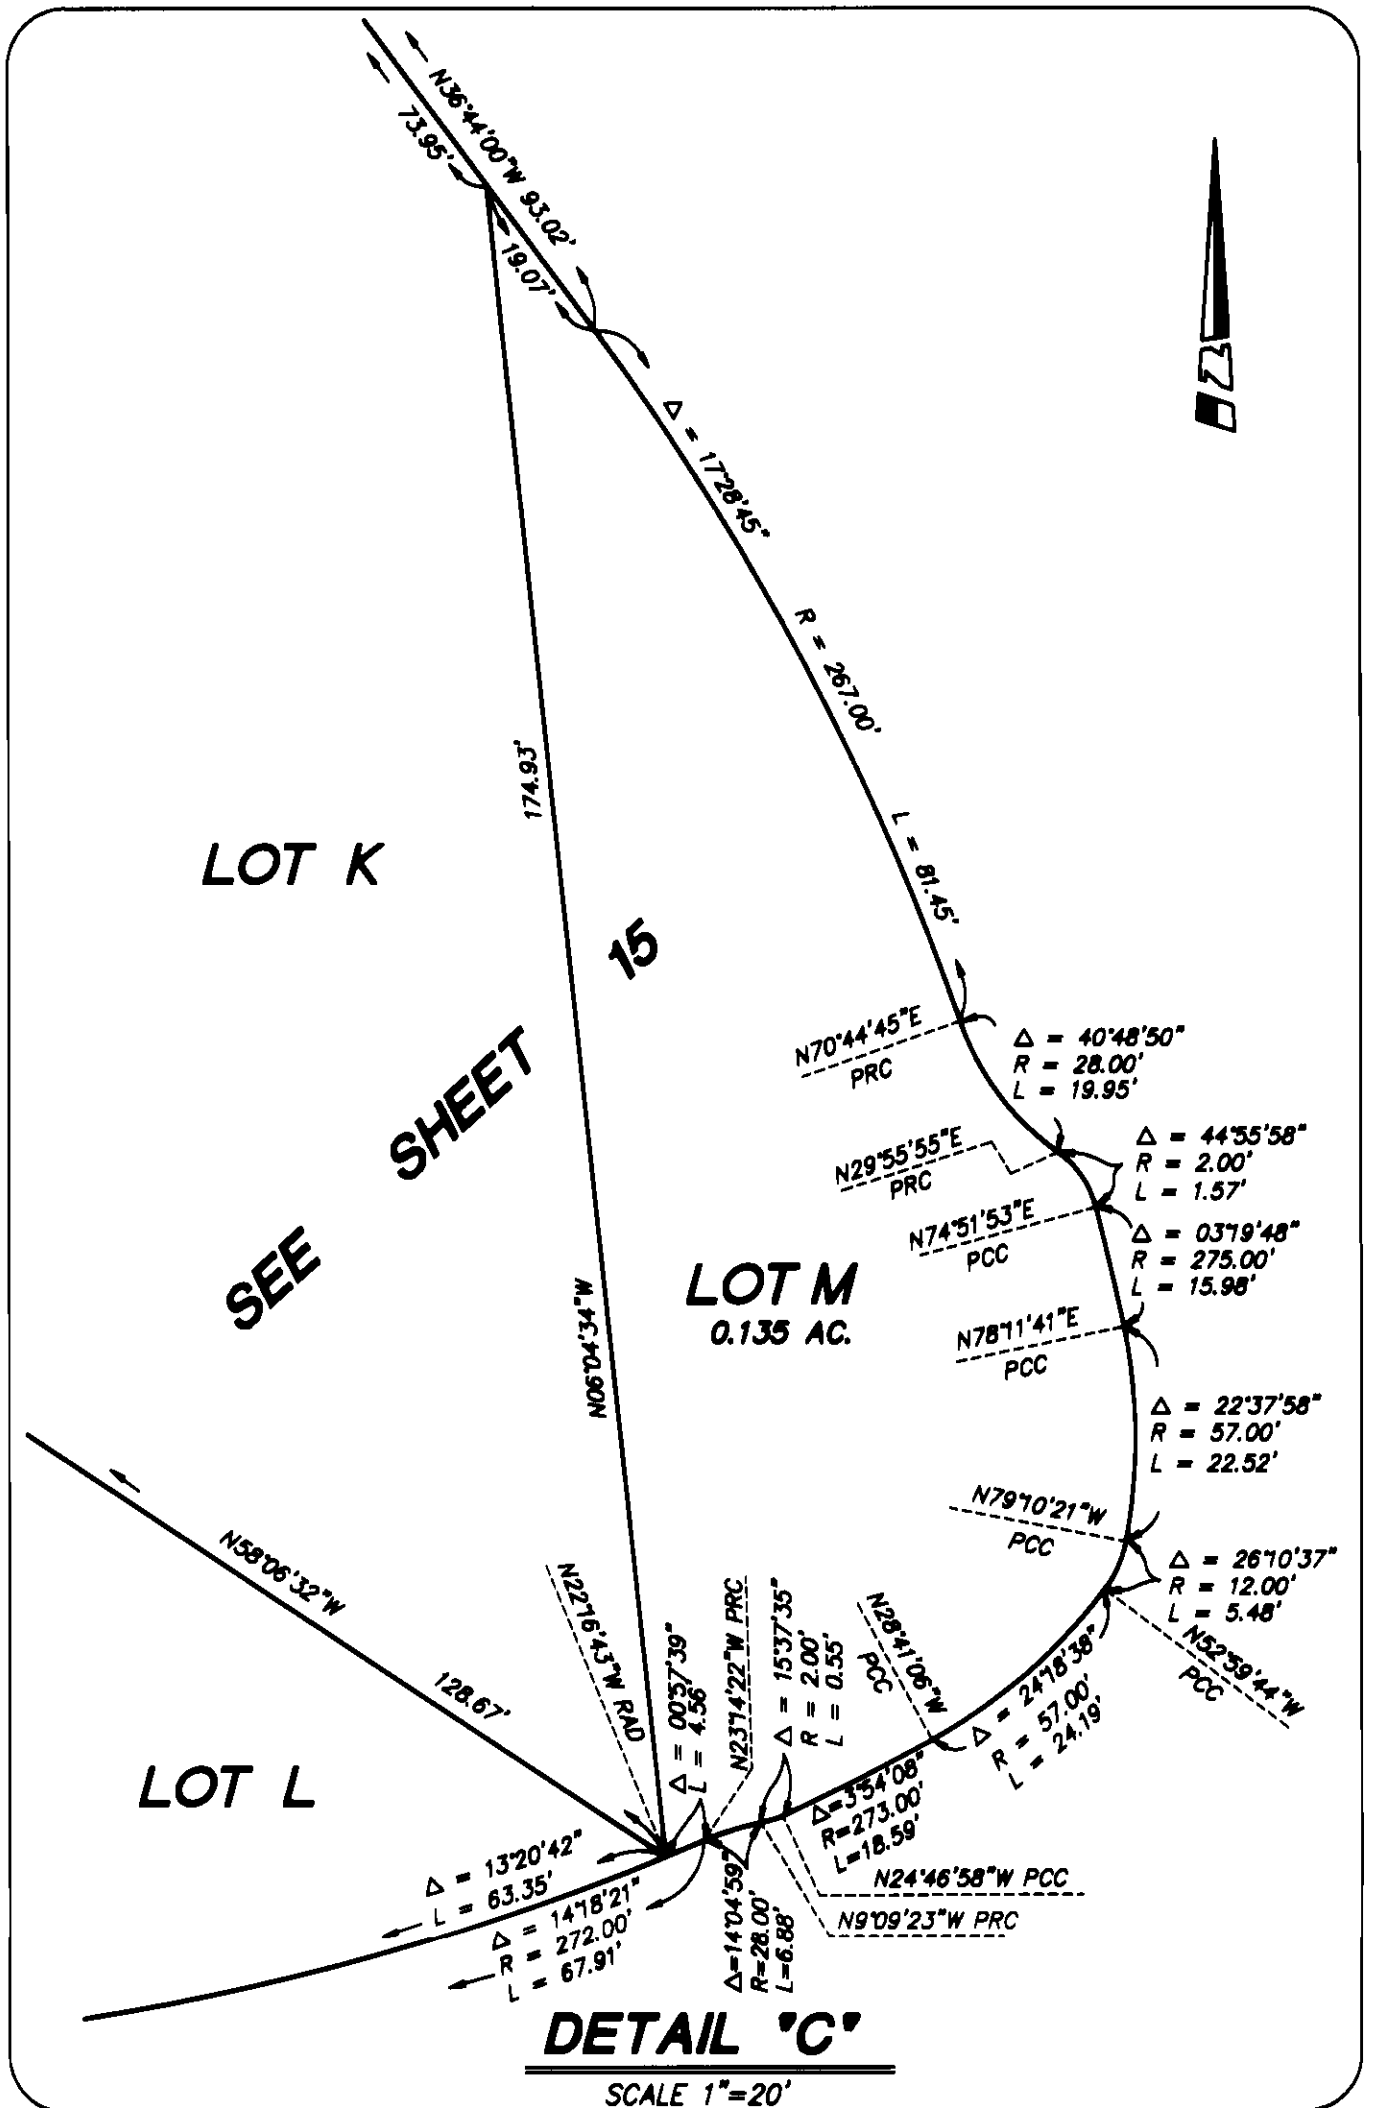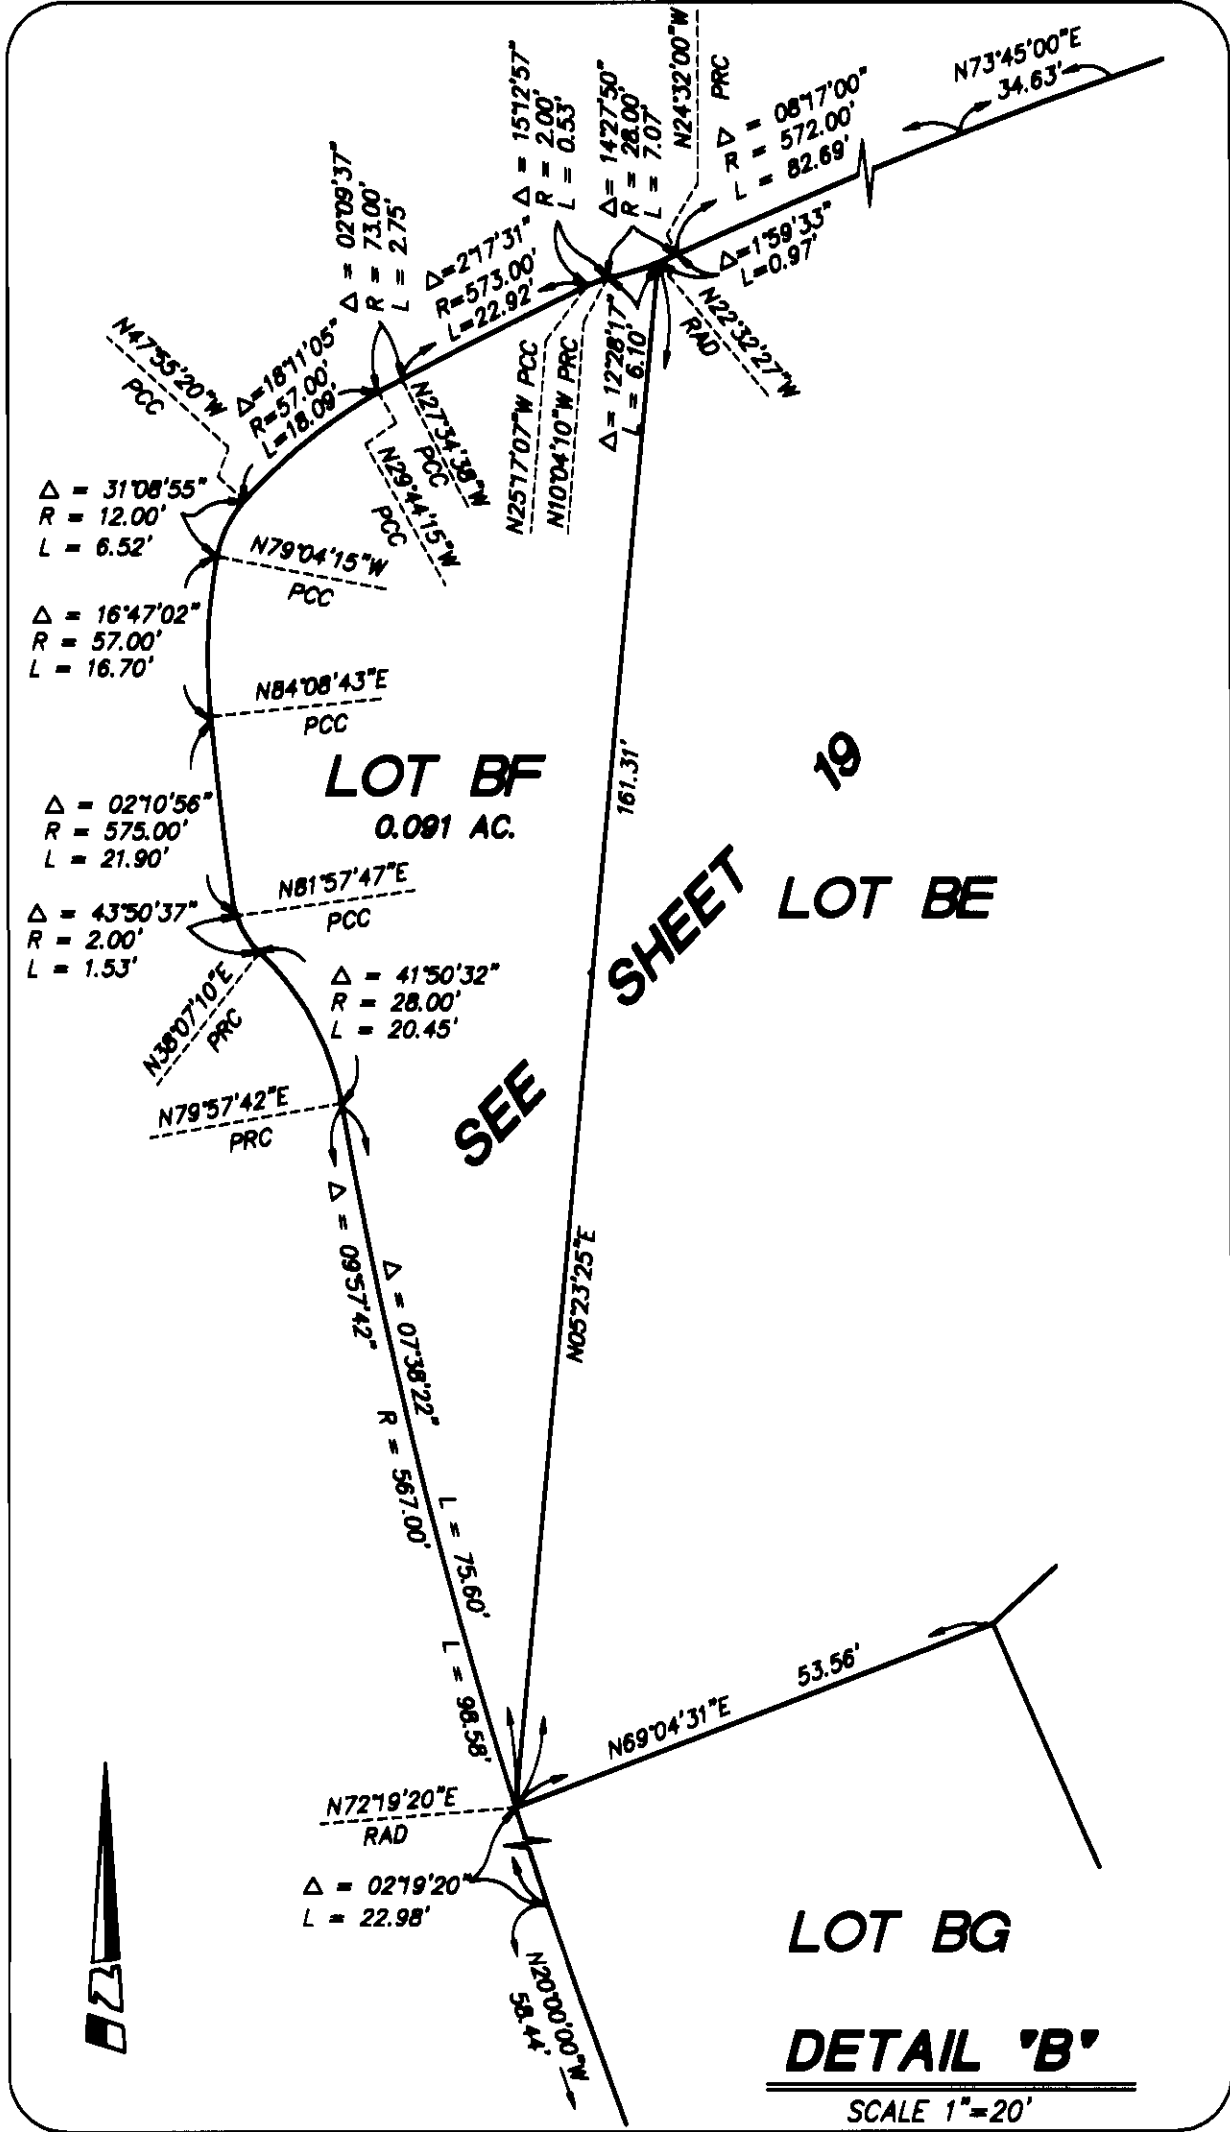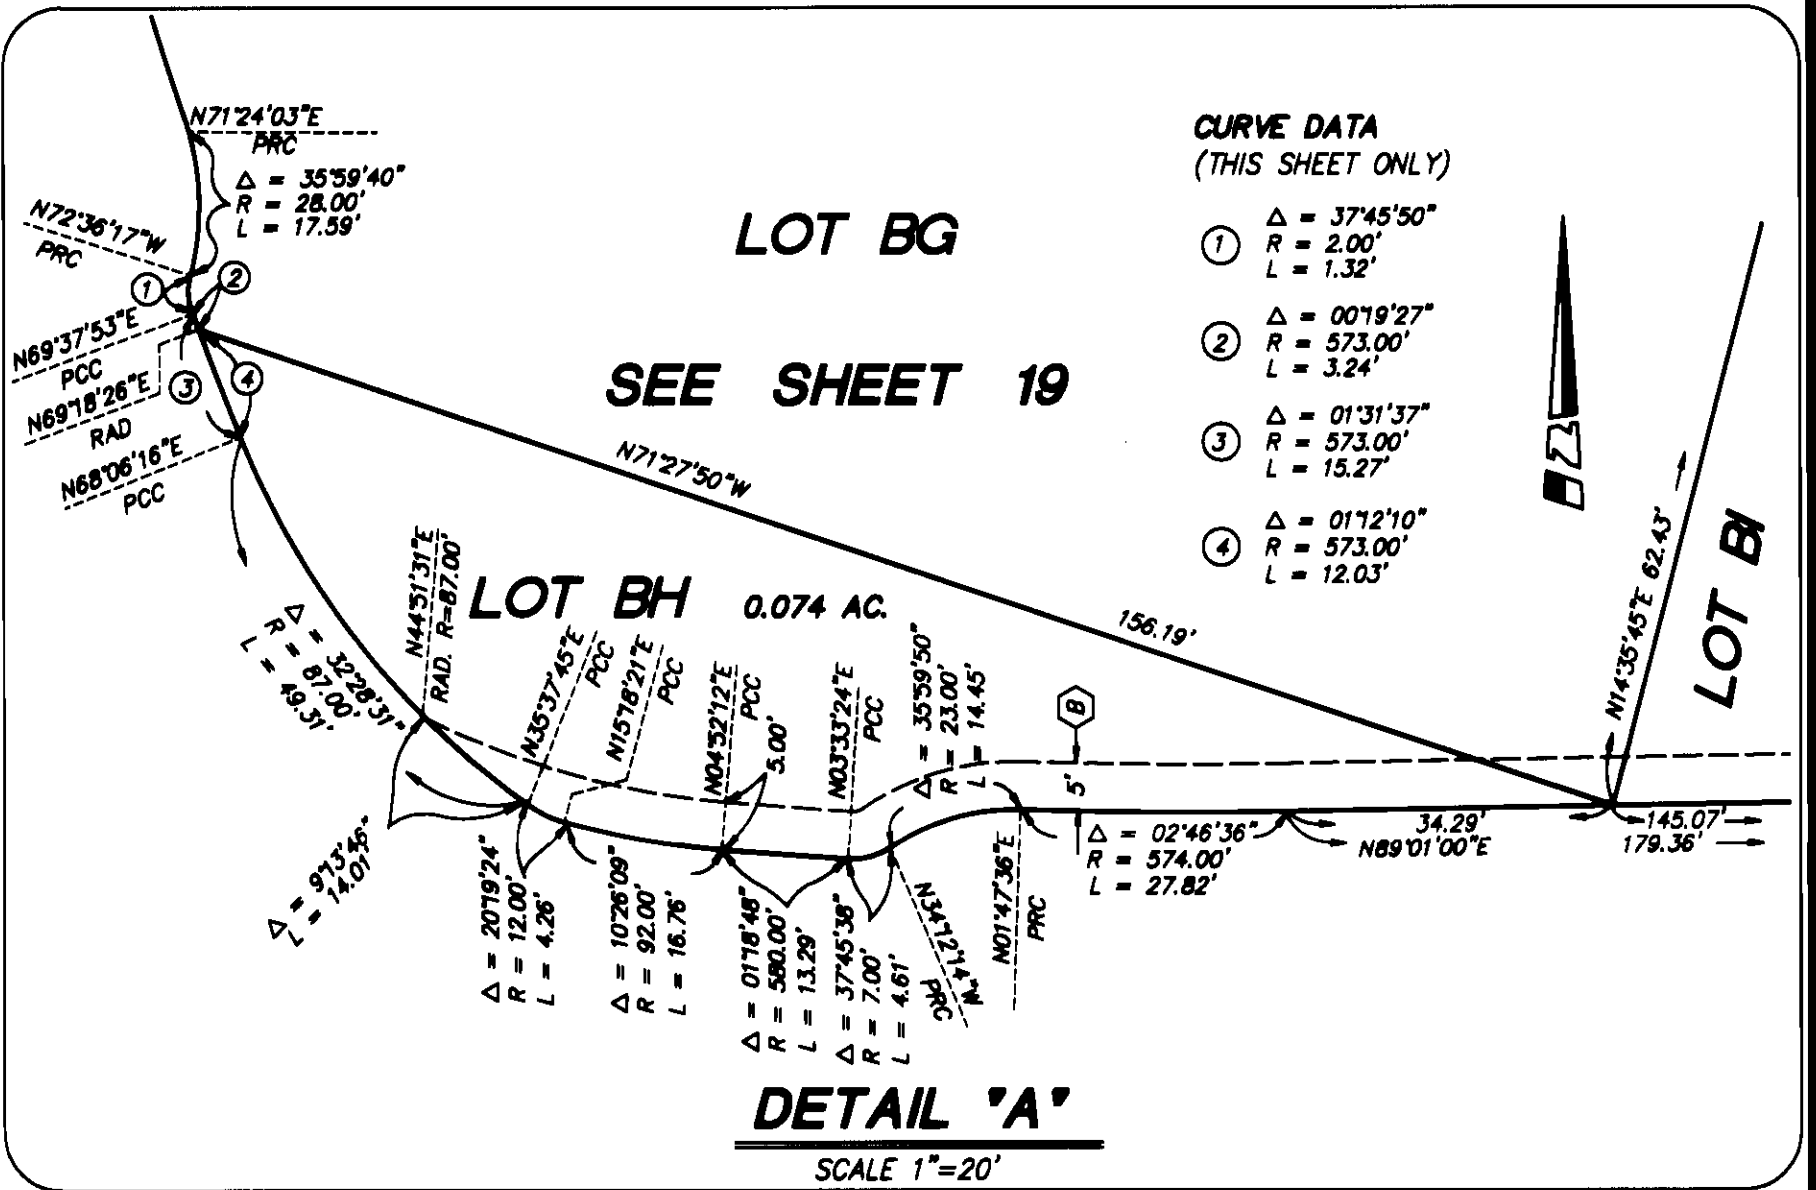

840 2

840 4

SHEET 4 OF 20 SHEETS

TRACT NO. 16341

A PORTION OF VESTING
TENTATIVE TRACT NO. 16271

IN THE UNINCORPORATED TERRITORY OF ORANGE COUNTY, CALIFORNIA

JUNE 2002


JAMES F. GILLEN, L.S. 5557

DATE OF SURVEY:
JANUARY 1999

HUITT-ZOLLARS

17 NUMBERED LOTS AND 63 LETTERED LOTS

168.726 AC.

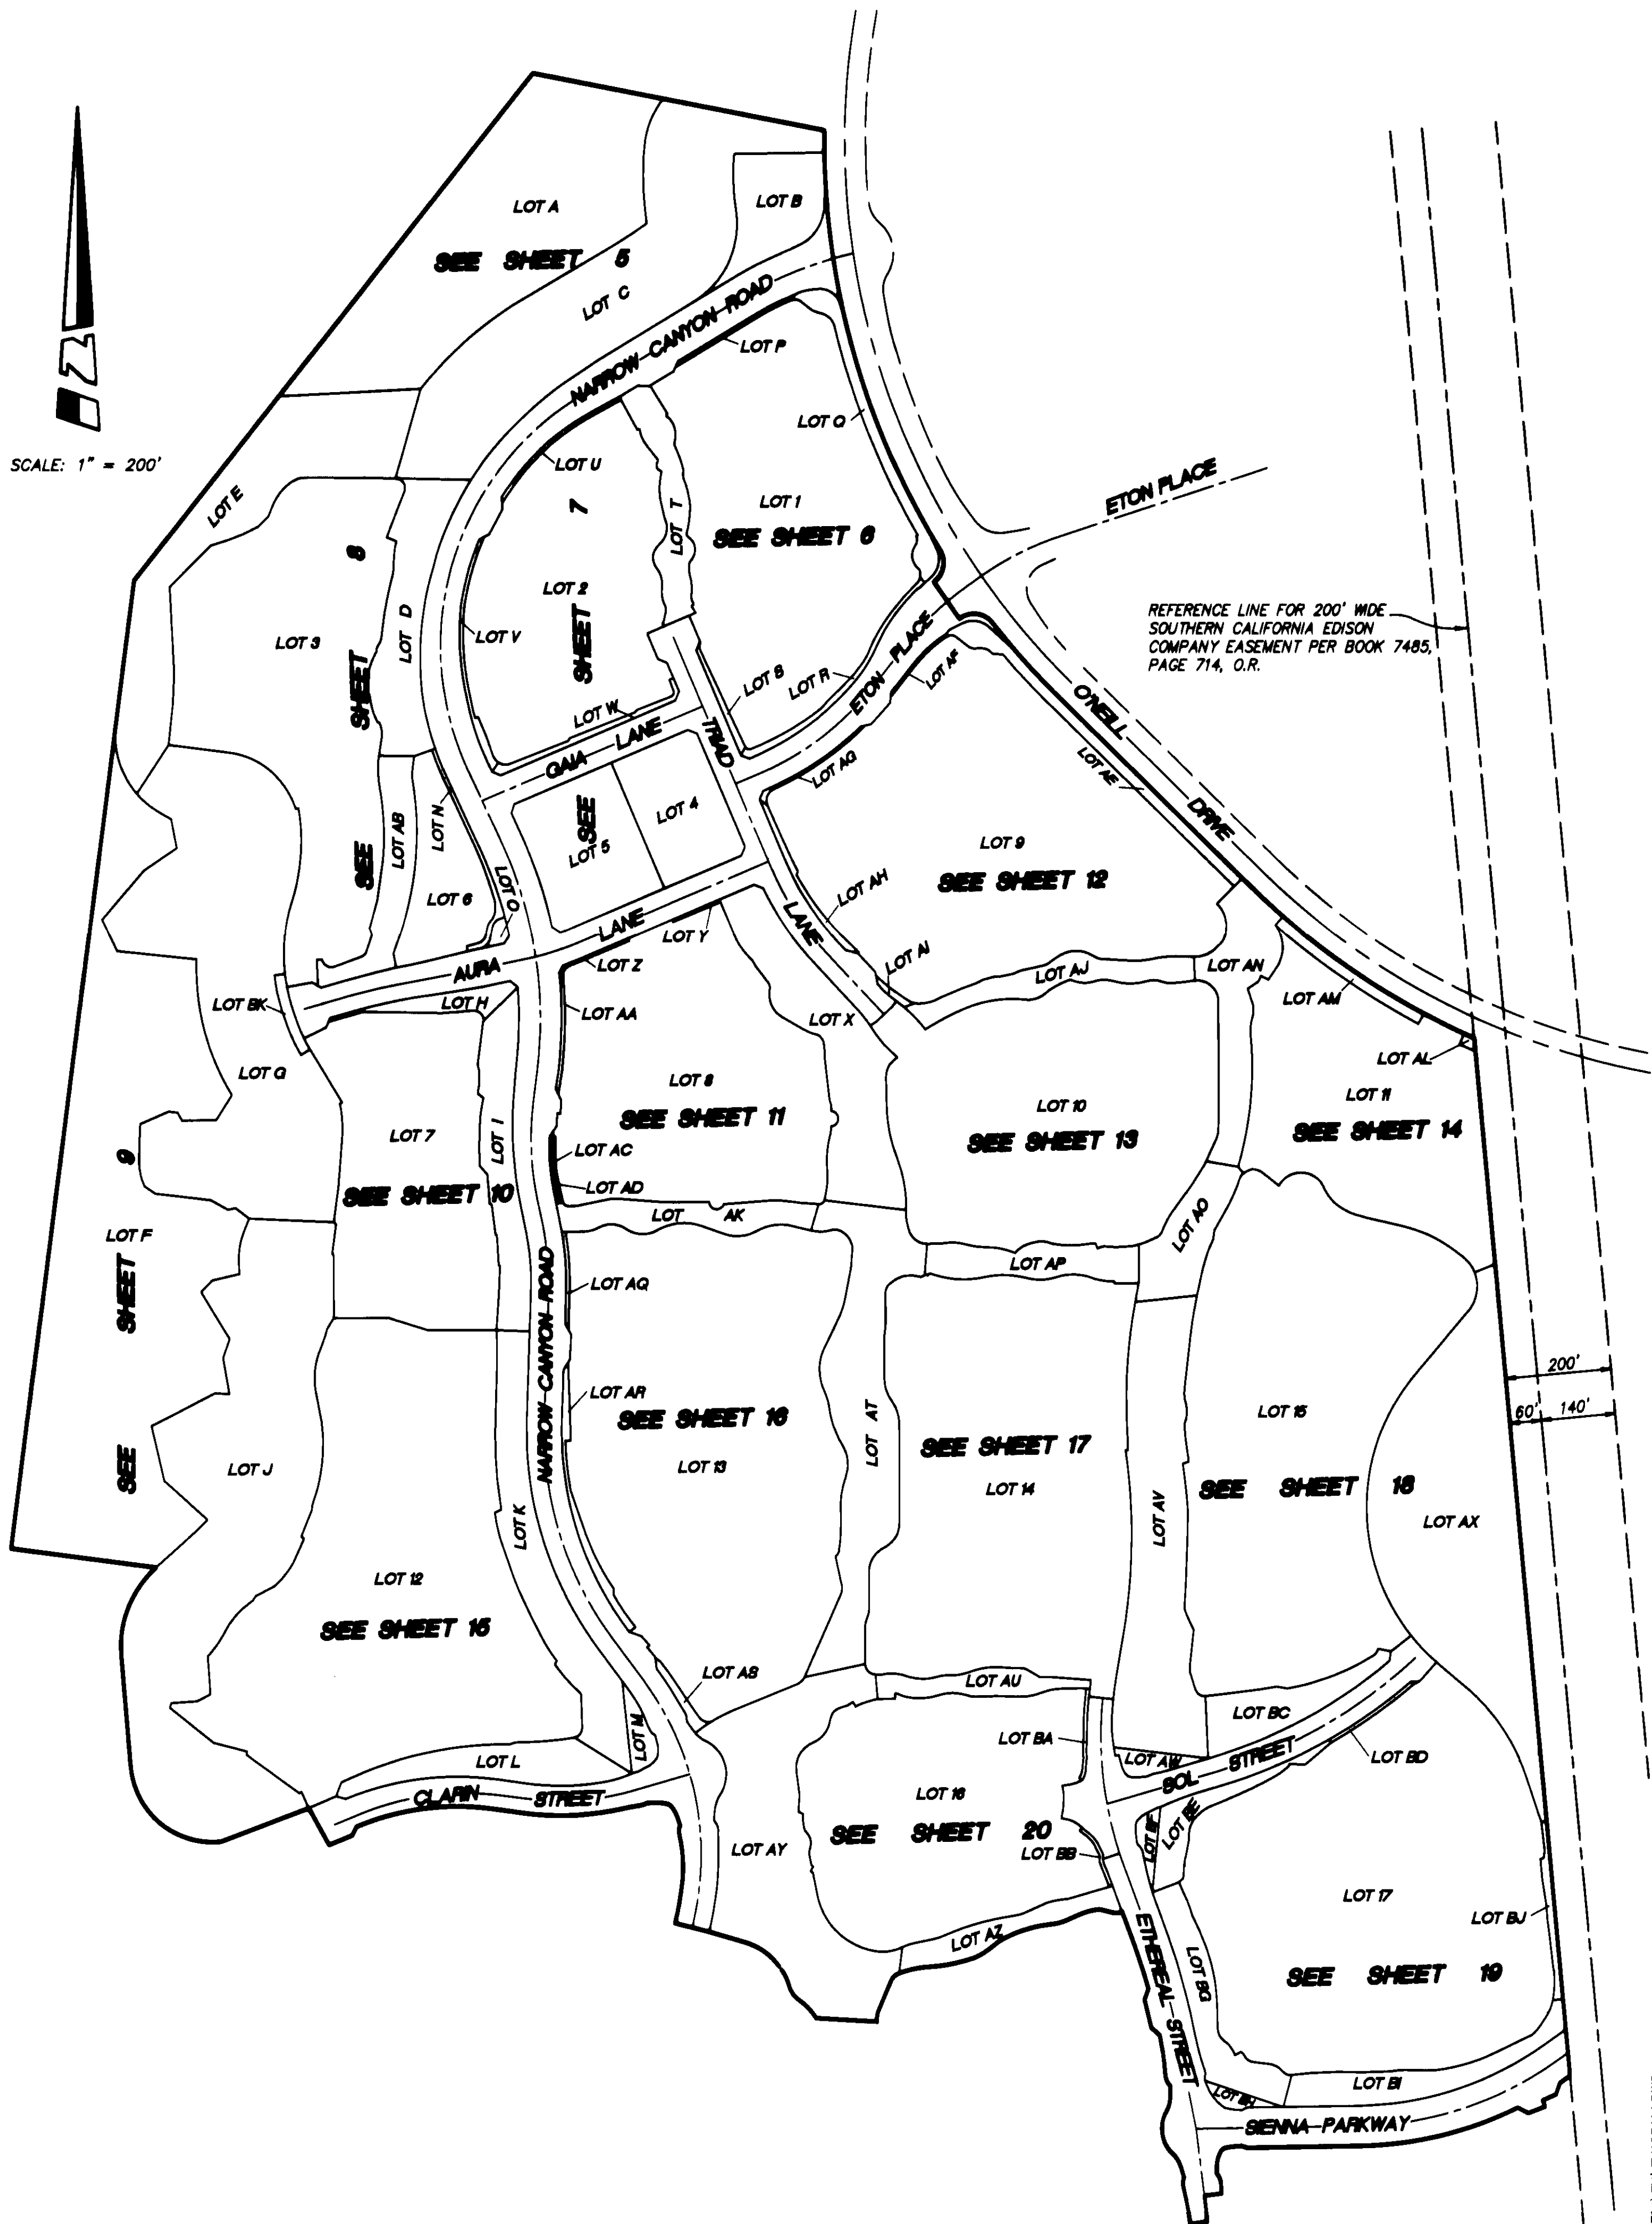

SHEET INDEX MAP

h oh8

840 S

SHEET 5 OF 20 SHEETS

TRACT NO. 16341

IN THE UNINCORPORATED TERRITORY OF ORANGE COUNTY, CALIFORNIA

JUNE 2002

JAMES F. GILLEN, L.S. 5557



A PORTION OF VESTING
TENTATIVE TRACT NO. 16271

DATE OF SURVEY:
JANUARY 1999

HUITT-ZOLLARS

17 NUMBERED LOTS AND 63 LETTERED LOTS

168.726 ACRES

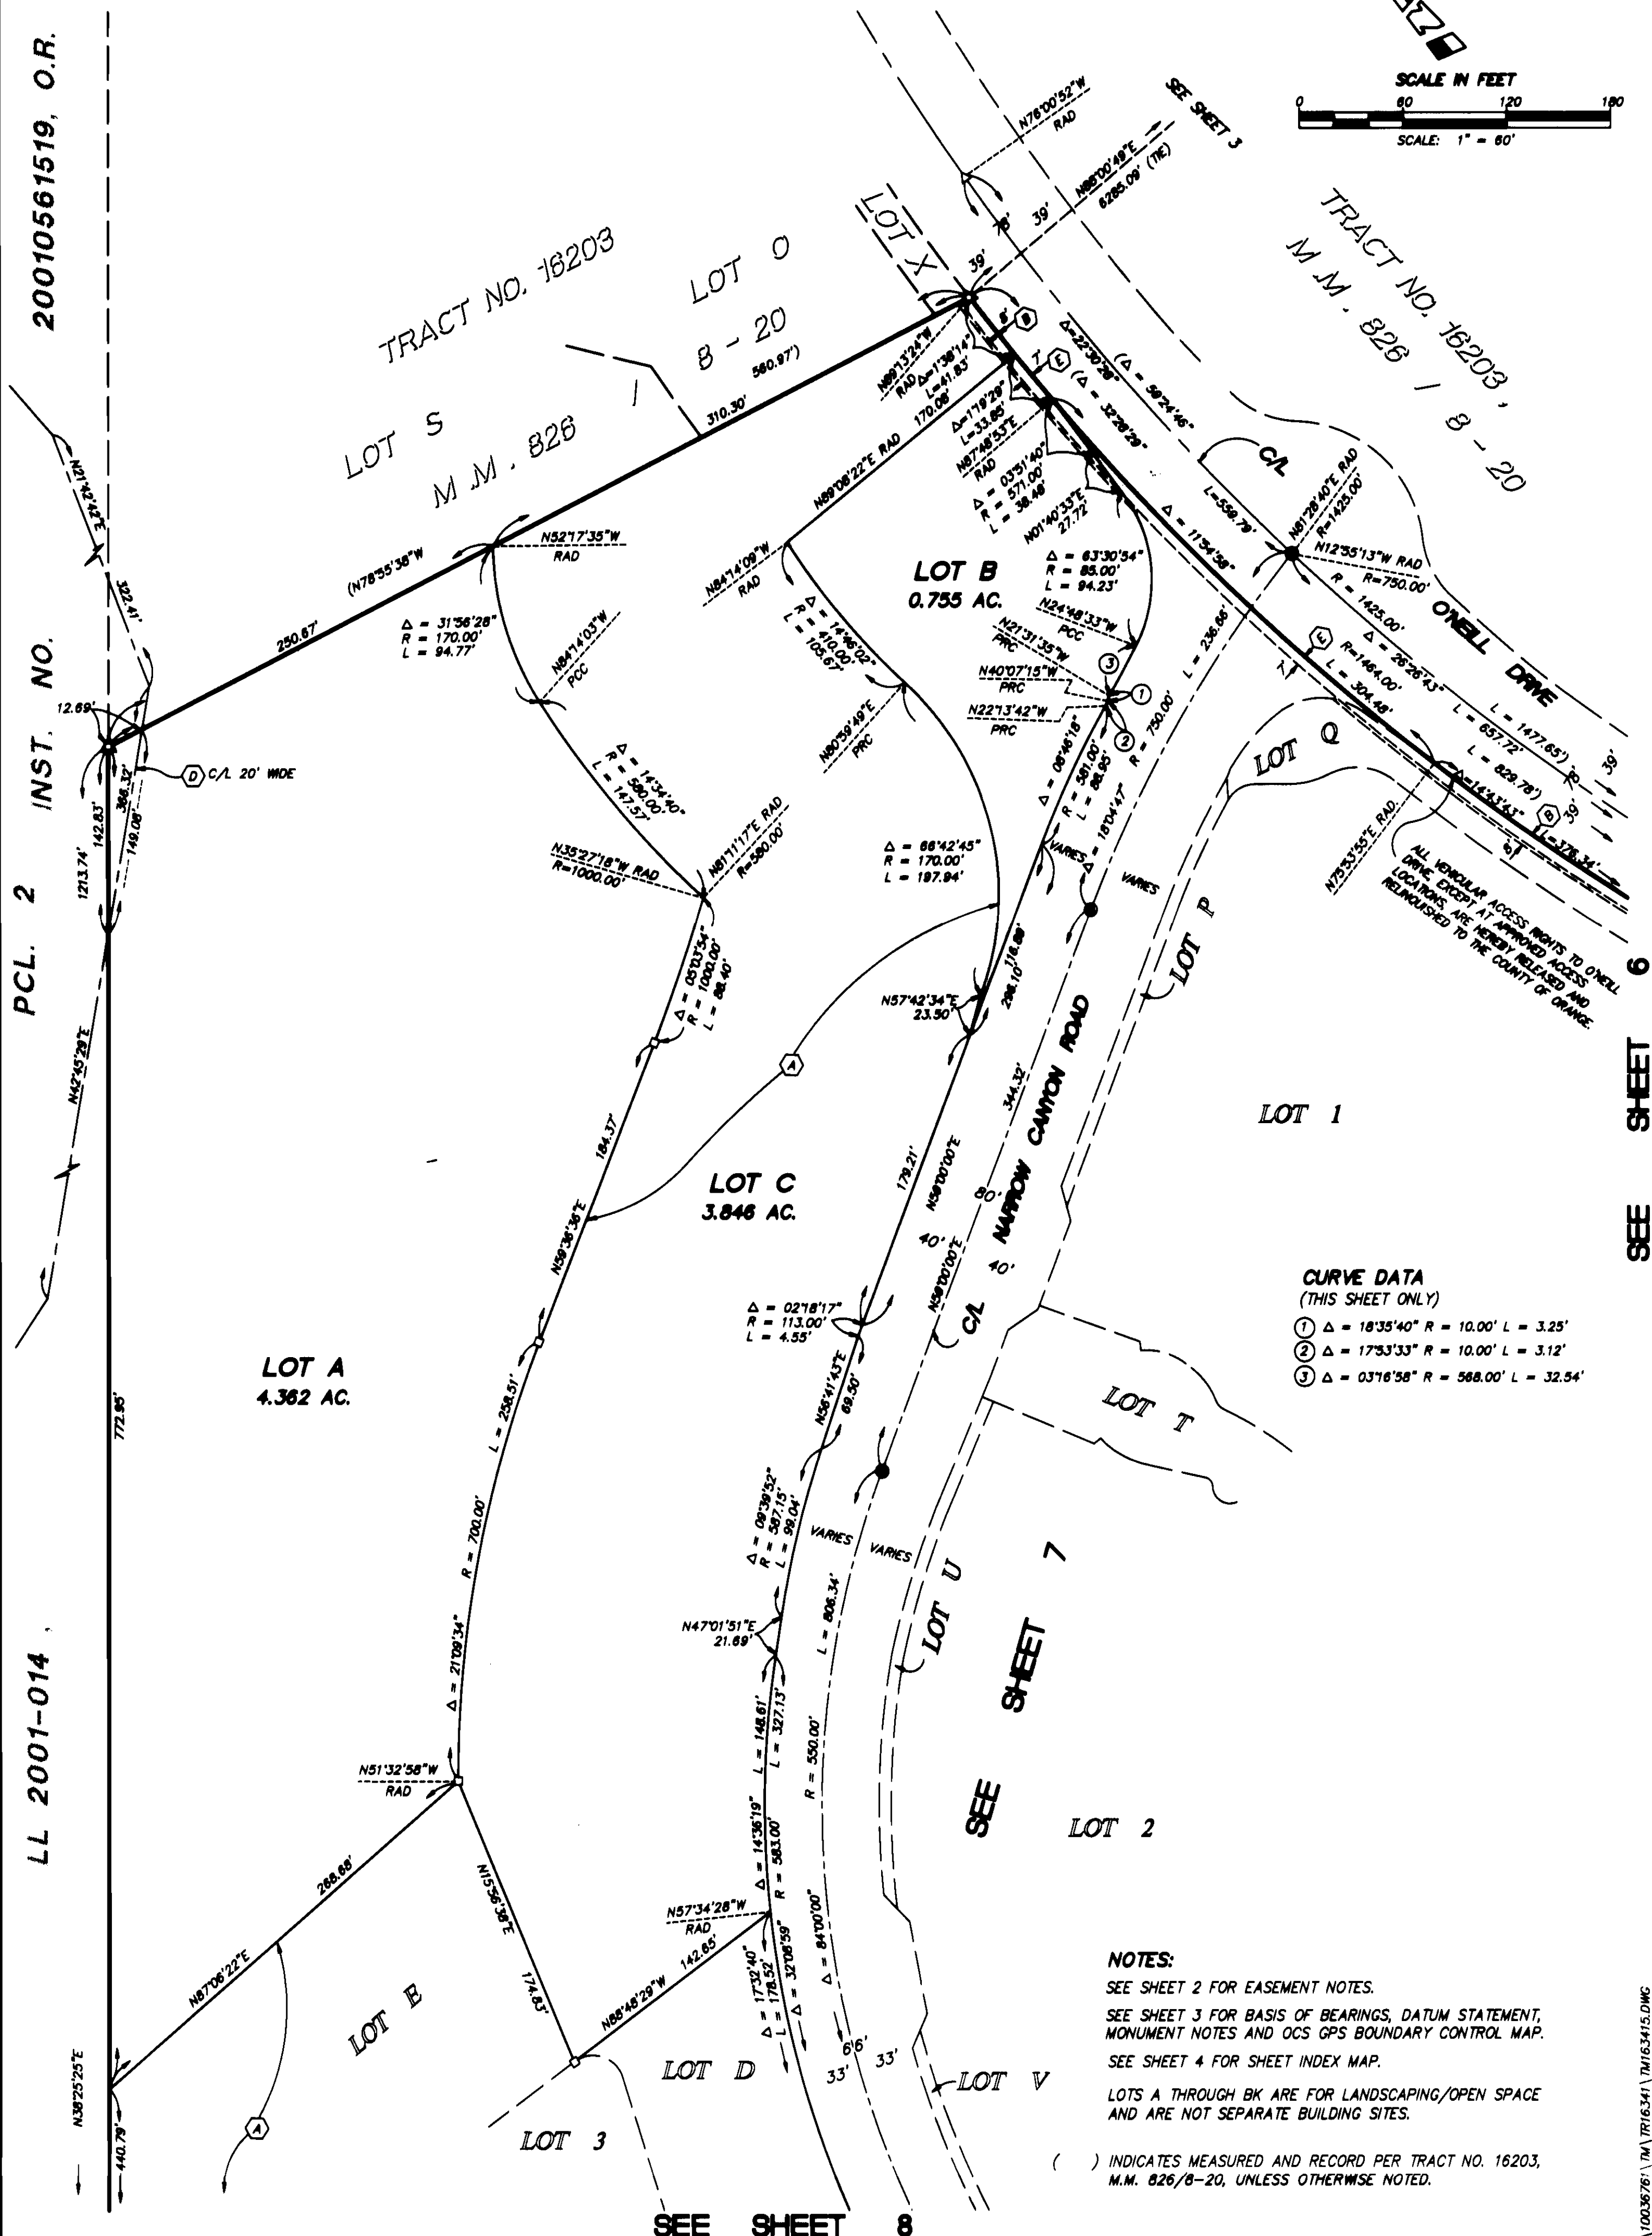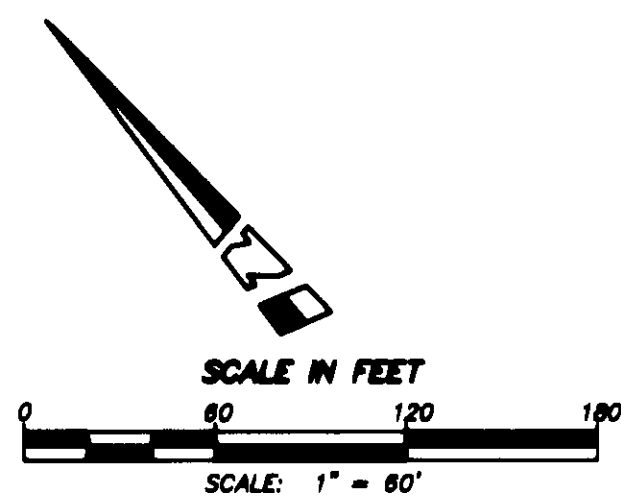

CURVE DATA
(THIS SHEET ONLY)

①	Δ = 18°35'40"	R = 10.00'	L = 3.25'
②	Δ = 17°33'33"	R = 10.00'	L = 3.12'
③	Δ = 03°16'58"	R = 588.00'	L = 32.54'

NOTES:
SEE SHEET 2 FOR EASEMENT NOTES.
SEE SHEET 3 FOR BASIS OF BEARINGS, DATUM STATEMENT,
MONUMENT NOTES AND OCS GPS BOUNDARY CONTROL MAP.
SEE SHEET 4 FOR SHEET INDEX MAP.
LOTS A THROUGH BK ARE FOR LANDSCAPING/OPEN SPACE
AND ARE NOT SEPARATE BUILDING SITES.
() INDICATES MEASURED AND RECORD PER TRACT NO. 16203,
M.M. 826/8-20, UNLESS OTHERWISE NOTED.

SEE SHEET 6

SEE SHEET 7

SEE SHEET 8

G:\10036761\TM16341\TM163415.DWG

840 S

840 6

SHEET 6 OF 20 SHEETS

TRACT NO. 16341

IN THE UNINCORPORATED TERRITORY OF ORANGE COUNTY, CALIFORNIA

JUNE 2002

JAMES F. GILLEN, L.S. 5557


A PORTION OF VESTING
TENTATIVE TRACT NO. 16271

DATE OF SURVEY:
JANUARY 1999

HUITT-ZOLLARS

17 NUMBERED LOTS AND 63 LETTERED LOTS

168.726 ACRES

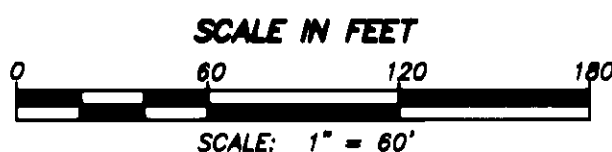

SEE SHEET 5

NOTES:

SEE SHEET 2 FOR EASEMENT NOTES.

SEE SHEET 3 FOR BASIS OF BEARINGS, DATUM STATEMENT,
MONUMENT NOTES AND OCS GPS BOUNDARY CONTROL MAP.

SEE SHEET 4 FOR SHEET INDEX MAP.

LOTS A THROUGH BK ARE FOR LANDSCAPING/OPEN SPACE
AND ARE NOT SEPARATE BUILDING SITES.

* INDICATES O'NEILL DRIVE STREET DEDICATION.

() INDICATES MEASURED AND RECORD PER TRACT NO. 16203,
M.M. 826/B-20, UNLESS OTHERWISE NOTED.

CURVE DATA (THIS SHEET ONLY)


- ① $\Delta = 16'12'47''$ R = 12.00' L = 3.40'
- ② $\Delta = 22'03'32''$ R = 110.00' L = 42.35'
- ③ $\Delta = 73'05'30''$ R = 40.00' L = 51.03'
- ④ $\Delta = 02'16'52''$ R = 571.00' L = 22.73'
- ⑤ $\Delta = 65'26'22''$ R = 35.00' L = 39.97'
- ⑥ $\Delta = 16'41'30''$ R = 10.00' L = 2.91'
- ⑦ $\Delta = 03'09'41''$ R = 571.00' L = 31.51'
- ⑧ $\Delta = 02'52'05''$ R = 1464.00' L = 73.28'
- ⑨ $\Delta = 71'43'56''$ R = 45.00' L = 56.34'
- ⑩ $\Delta = 86'43'50''$ R = 44.00' L = 66.60'
- ⑪ $\Delta = 02'53'35''$ R = 568.00' L = 28.68'
- ⑫ $\Delta = 15'55'16''$ R = 12.00' L = 3.33'
- ⑬ $\Delta = 17'45'40''$ R = 10.00' L = 3.10'
- ⑭ $\Delta = 67'08'18''$ R = 15.00' L = 17.58'
- ⑮ $\Delta = 55'71'15''$ R = 10.00' L = 9.65'
- ⑯ $\Delta = 39'56'43''$ R = 18.00' L = 12.55'
- ⑰ $\Delta = 88'19'43''$ R = 32.00' L = 49.33'
- ⑱ $\Delta = 60'47'08''$ R = 18.00' L = 19.10'
- ⑲ $\Delta = 25'27'56''$ R = 56.00' L = 24.89'
- ⑳ $\Delta = 43'25'57''$ R = 10.00' L = 7.58'
- ㉑ $\Delta = 77'23'40''$ R = 5.00' L = 6.75'
- ㉒ $\Delta = 114'04'28''$ R = 10.00' L = 19.91'
- ㉓ $\Delta = 87'42'47''$ R = 3.00' L = 4.59'
- ㉔ $\Delta = 14'18'03''$ R = 171.00' L = 42.68'
- ㉕ $\Delta = 39'55'35''$ R = 25.00' L = 17.42'
- ㉖ $\Delta = 19'38'30''$ R = 25.00' L = 8.57'
- ㉗ $\Delta = 43'11'33''$ R = 15.50' L = 11.68'
- ㉘ $\Delta = 26'12'42''$ R = 89.00' L = 40.72'
- ㉙ $\Delta = 73'45'54''$ R = 5.50' L = 7.08'
- ㉚ $\Delta = 28'07'31''$ R = 15.00' L = 7.36'
- ㉛ $\Delta = 13'23'49''$ R = 196.00' L = 45.83'
- ㉜ $\Delta = 06'02'28''$ R = 8.00' L = 12.01'
- ㉝ $\Delta = 16'17'40''$ R = 48.00' L = 13.85'
- ㉞ $\Delta = 12'22'14''$ R = 52.00' L = 11.23'
- ㉟ $\Delta = 09'44'08''$ R = 250.00' L = 42.48'
- ㊱ $\Delta = 13'25'34''$ R = 148.00' L = 34.68'
- ㊲ $\Delta = 16'03'11''$ R = 267.00' L = 74.81'
- ㊳ $\Delta = 01'04'12''$ R = 568.00' L = 10.61'
- ㊴ $\Delta = 01'49'23''$ R = 568.00' L = 18.07'
- ㊵ $\Delta = 84'00'00''$ R = 550.00' L = 806.34'

ALL VEHICULAR ACCESS RIGHTS TO O'NEILL
DRIVE, EXCEPT AT APPROVED ACCESS
LOCATIONS, ARE HEREBY RELEASED AND
RELINQUISHED TO THE COUNTY OF ORANGE.

LOT 1
6.057 AC.

COURSE DATA (THIS SHEET ONLY)

- 1 N35°09'12"E 12.81'
- 2 N16°22'57"W 29.22'
- 3 N00°31'33"E PCC
- 4 N37°44'46"W PRC
- 5 N21°03'16"W PRC
- 6 N55°58'48"E 6.00'
- 7 N21°31'59"W PCC
- 8 N75°53'55"E RAD
- 9 N25°40'07"W 35.65'
- 10 N43°56'11"W PCC
- 11 N41°02'36"W PCC
- 12 N25°07'20"W PRC
- 13 N42°53'00"W PCC
- 14 N66°03'11"W RAD
- 15 N57°11'00"W RAD
- 16 N38°55'06"E PRC
- 17 N58°18'07"E PRC
- 18 N67°00'00"E 7.00'
- 19 N28°10'50"E 18.21'
- 20 N70°77'26"E 17.69'
- 21 N13°10'30"E 11.45'
- 22 N50°00'00"W PCC

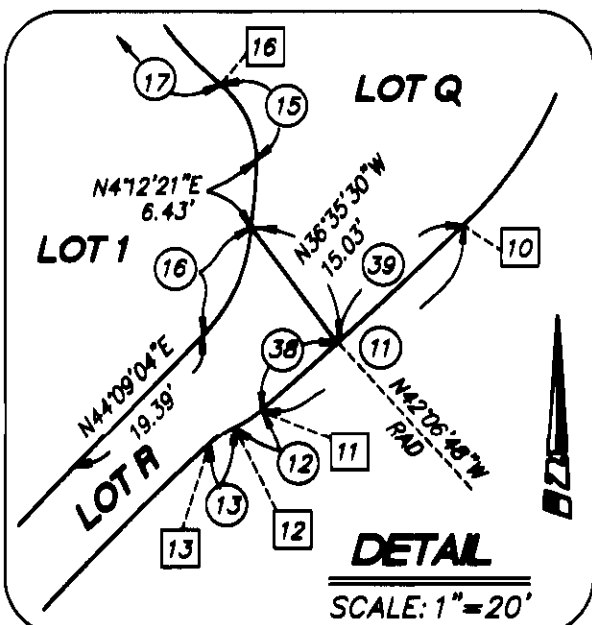

SEE SHEET 7

SEE SHEET 12

SEE SHEET 12

840 7

SHEET 7 OF 20 SHEETS

TRACT NO. 16341

IN THE UNINCORPORATED TERRITORY OF ORANGE COUNTY, CALIFORNIA

JUNE 2002

JAMES F. GILLEN, L.S. 5557

A PORTION OF VESTING
TENTATIVE TRACT NO. 16271


DATE OF SURVEY:
JANUARY 1999

HUITT-ZOLLARS

17 NUMBERED LOTS AND 63 LETTERED LOTS

168.726 ACRES

SEE SHEET 5

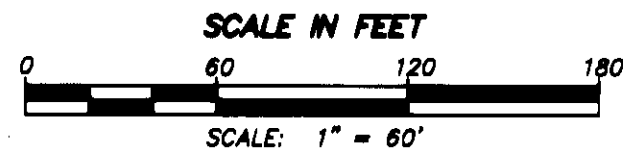

NOTES:

SEE SHEET 2 FOR EASEMENT NOTES.

SEE SHEET 3 FOR BASIS OF BEARINGS, DATUM STATEMENT,
MONUMENT NOTES AND OCS GPS BOUNDARY CONTROL MAP.

SEE SHEET 4 FOR SHEET INDEX MAP.


LOTS A THROUGH BK ARE FOR LANDSCAPING/OPEN SPACE
AND ARE NOT SEPARATE BUILDING SITES.

COURSE DATA (THIS SHEET ONLY)

- 1 N11°34'05"W 21.89'
- 2 N25°00'00"W 21.82'
- 3 N35°26'18"E 3.73'
- 4 N13°10'30"E 11.45'
- 5 N66°37'41"W 17.38'
- 6 N22°00'00"E 18.38'
- 7 N78°04'45"E RAD
- 8 N33°41'47"E RAD 20.97'

CURVE DATA (THIS SHEET ONLY)

- 1 $\Delta = 02^{\circ}50'38"$ R = 87.00' L = 4.32'
- 2 $\Delta = 02^{\circ}50'38"$ R = 80.00' L = 3.97'
- 3 $\Delta = 02^{\circ}47'11"$ R = 80.00' L = 3.89'
- 4 $\Delta = 02^{\circ}47'11"$ R = 87.00' L = 4.23'
- 5 $\Delta = 55^{\circ}06'12"$ R = 24.50' L = 23.56'
- 6 $\Delta = 39^{\circ}55'35"$ R = 25.00' L = 17.42'
- 7 $\Delta = 35^{\circ}45'09"$ R = 24.50' L = 15.29'
- 8 $\Delta = 33^{\circ}13'25"$ R = 5.00' L = 2.90'
- 9 $\Delta = 02^{\circ}54'33"$ R = 88.00' L = 4.47'
- 10 $\Delta = 00^{\circ}46'19"$ R = 517.26' L = 6.97'
- 11 $\Delta = 56^{\circ}07'25"$ R = 5.00' L = 4.90'
- 12 $\Delta = 77^{\circ}23'40"$ R = 5.00' L = 6.75'
- 13 $\Delta = 114^{\circ}04'28"$ R = 10.00' L = 19.91'
- 14 $\Delta = 87^{\circ}42'47"$ R = 3.00' L = 4.59'
- 15 $\Delta = 19^{\circ}38'30"$ R = 25.00' L = 8.57'

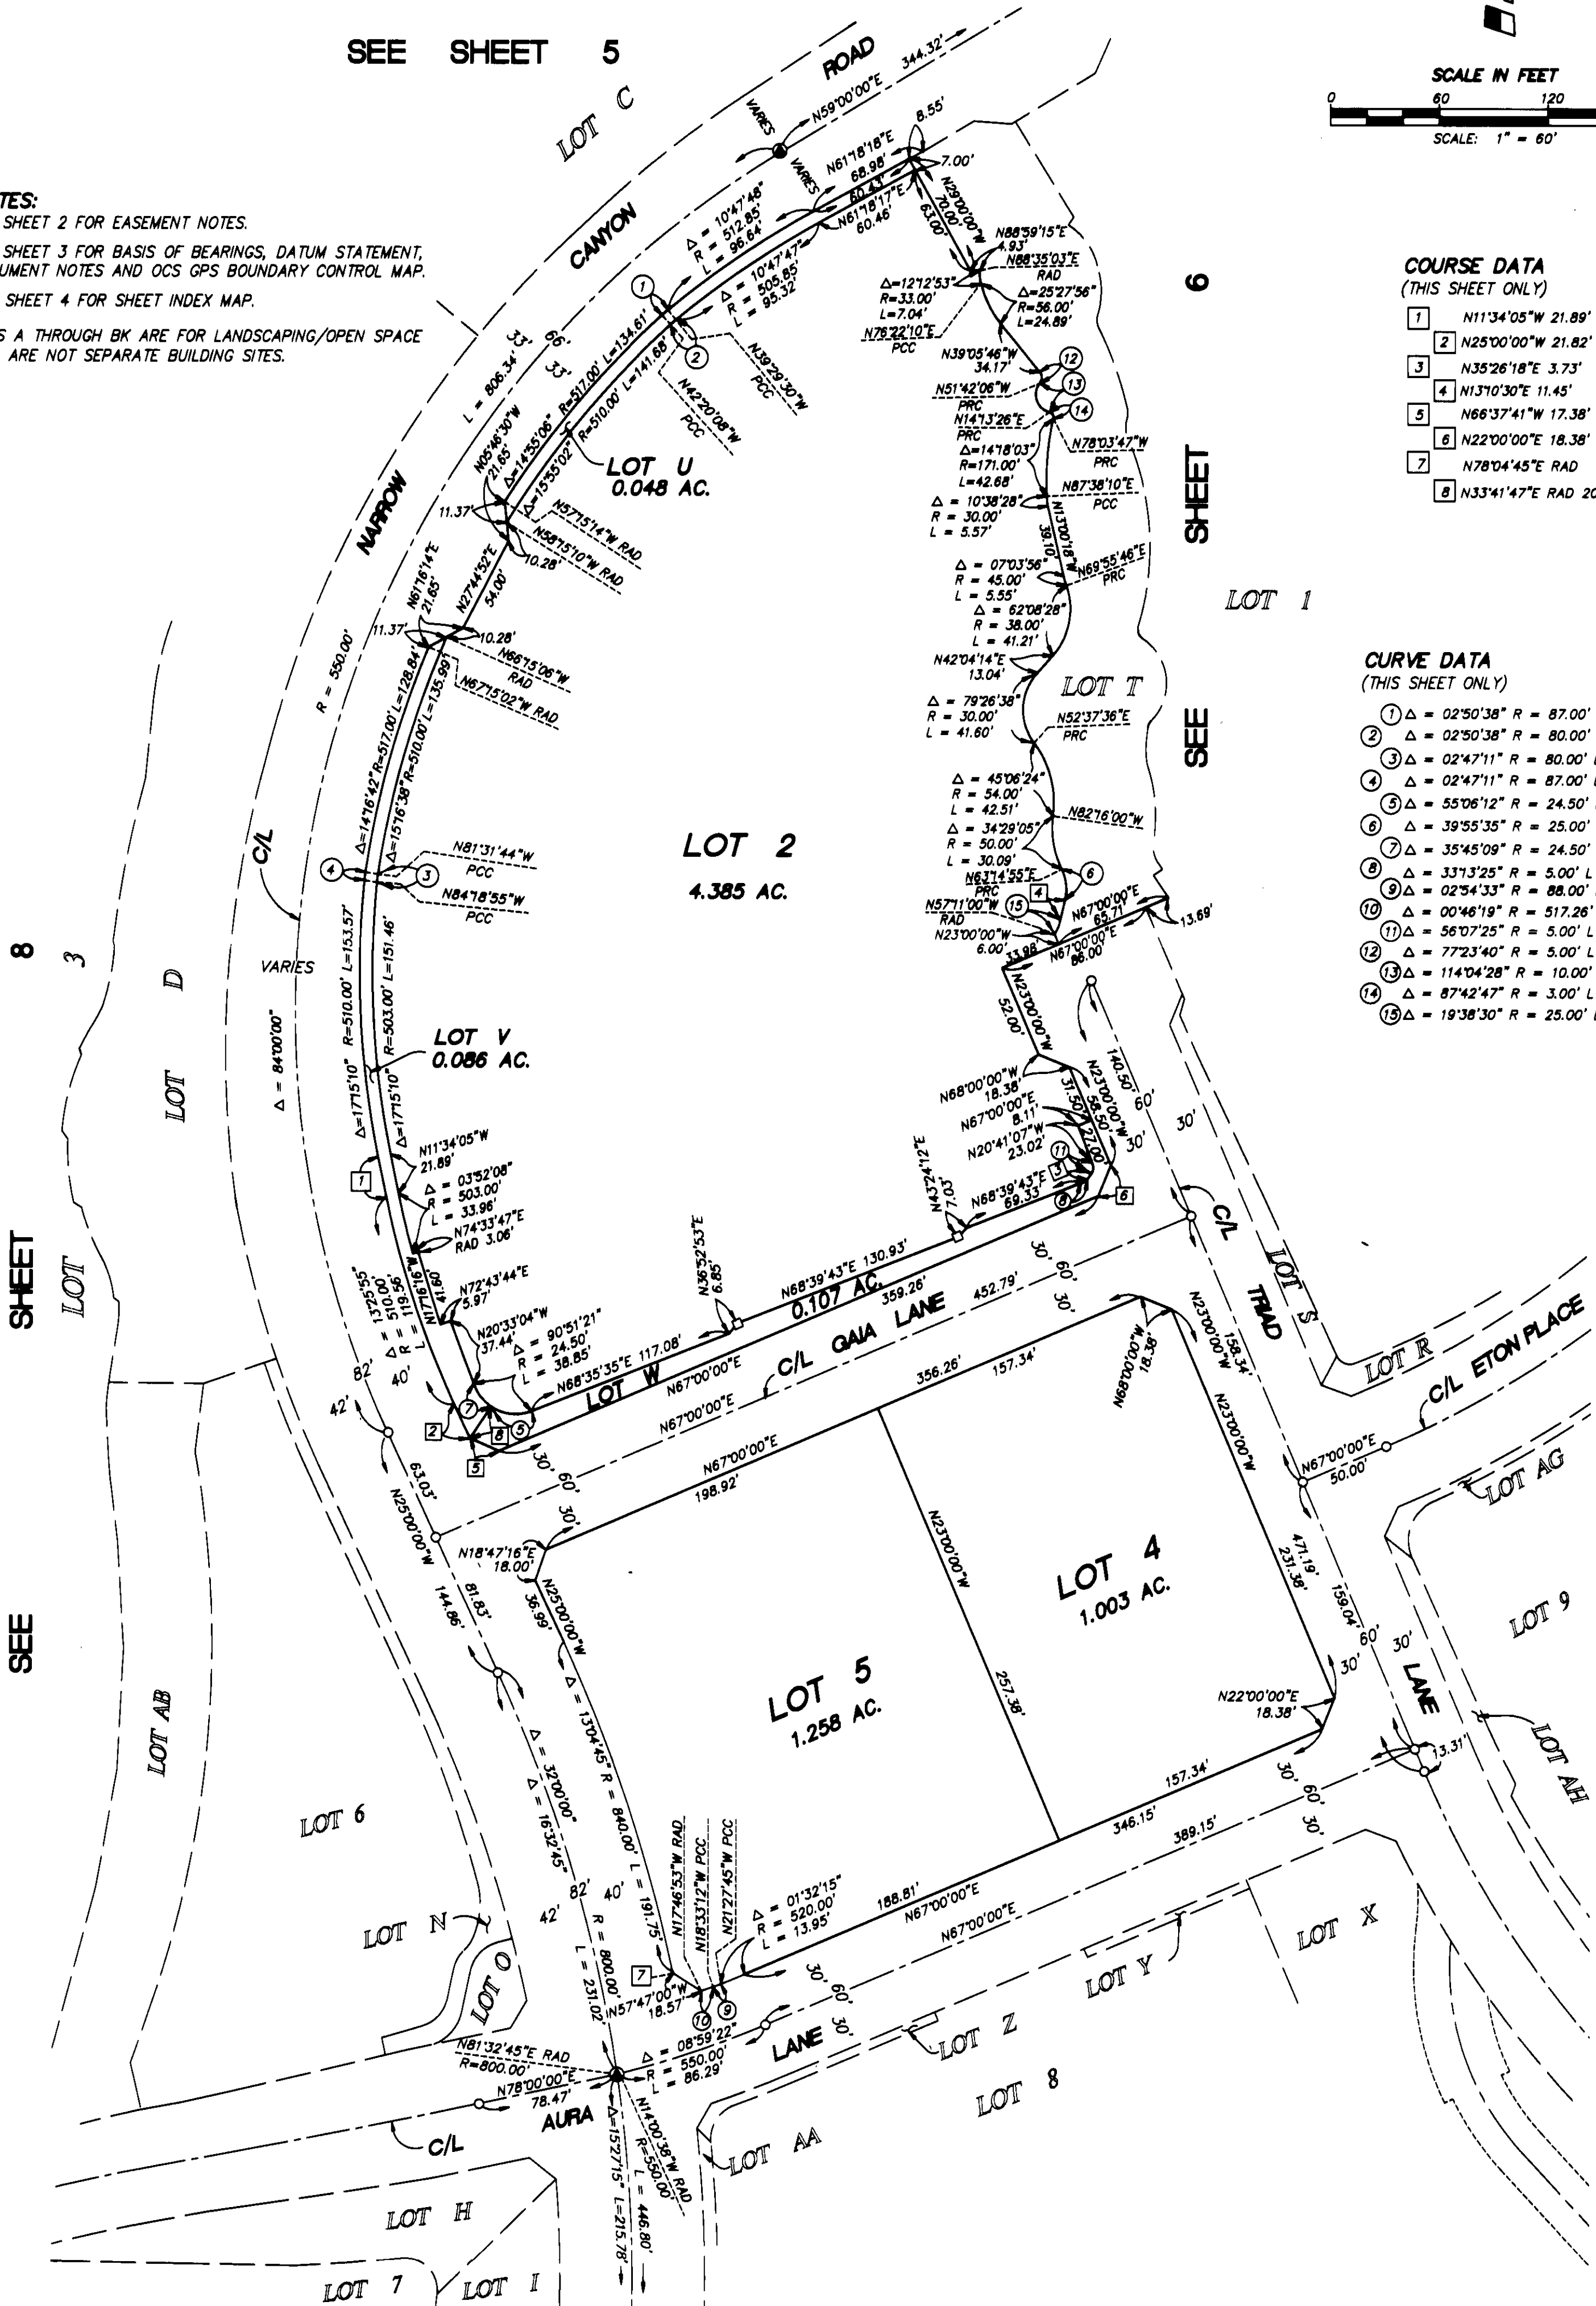

SEE SHEET 10

SEE SHEET 11

G:\00036761\1\1616341\TM16341.DWG

840 8

SHEET 8 OF 20 SHEETS

TRACT NO. 16341

A PORTION OF VESTING
TENTATIVE TRACT NO. 16271

IN THE UNINCORPORATED TERRITORY OF ORANGE COUNTY, CALIFORNIA


JUNE 2002

JAMES F. GILLEN, L.S. 5557

DATE OF SURVEY:
JANUARY 1999

HUITT-ZOLIARS

17 NUMBERED LOTS AND 63 LETTERED LOTS 168.726 ACRES

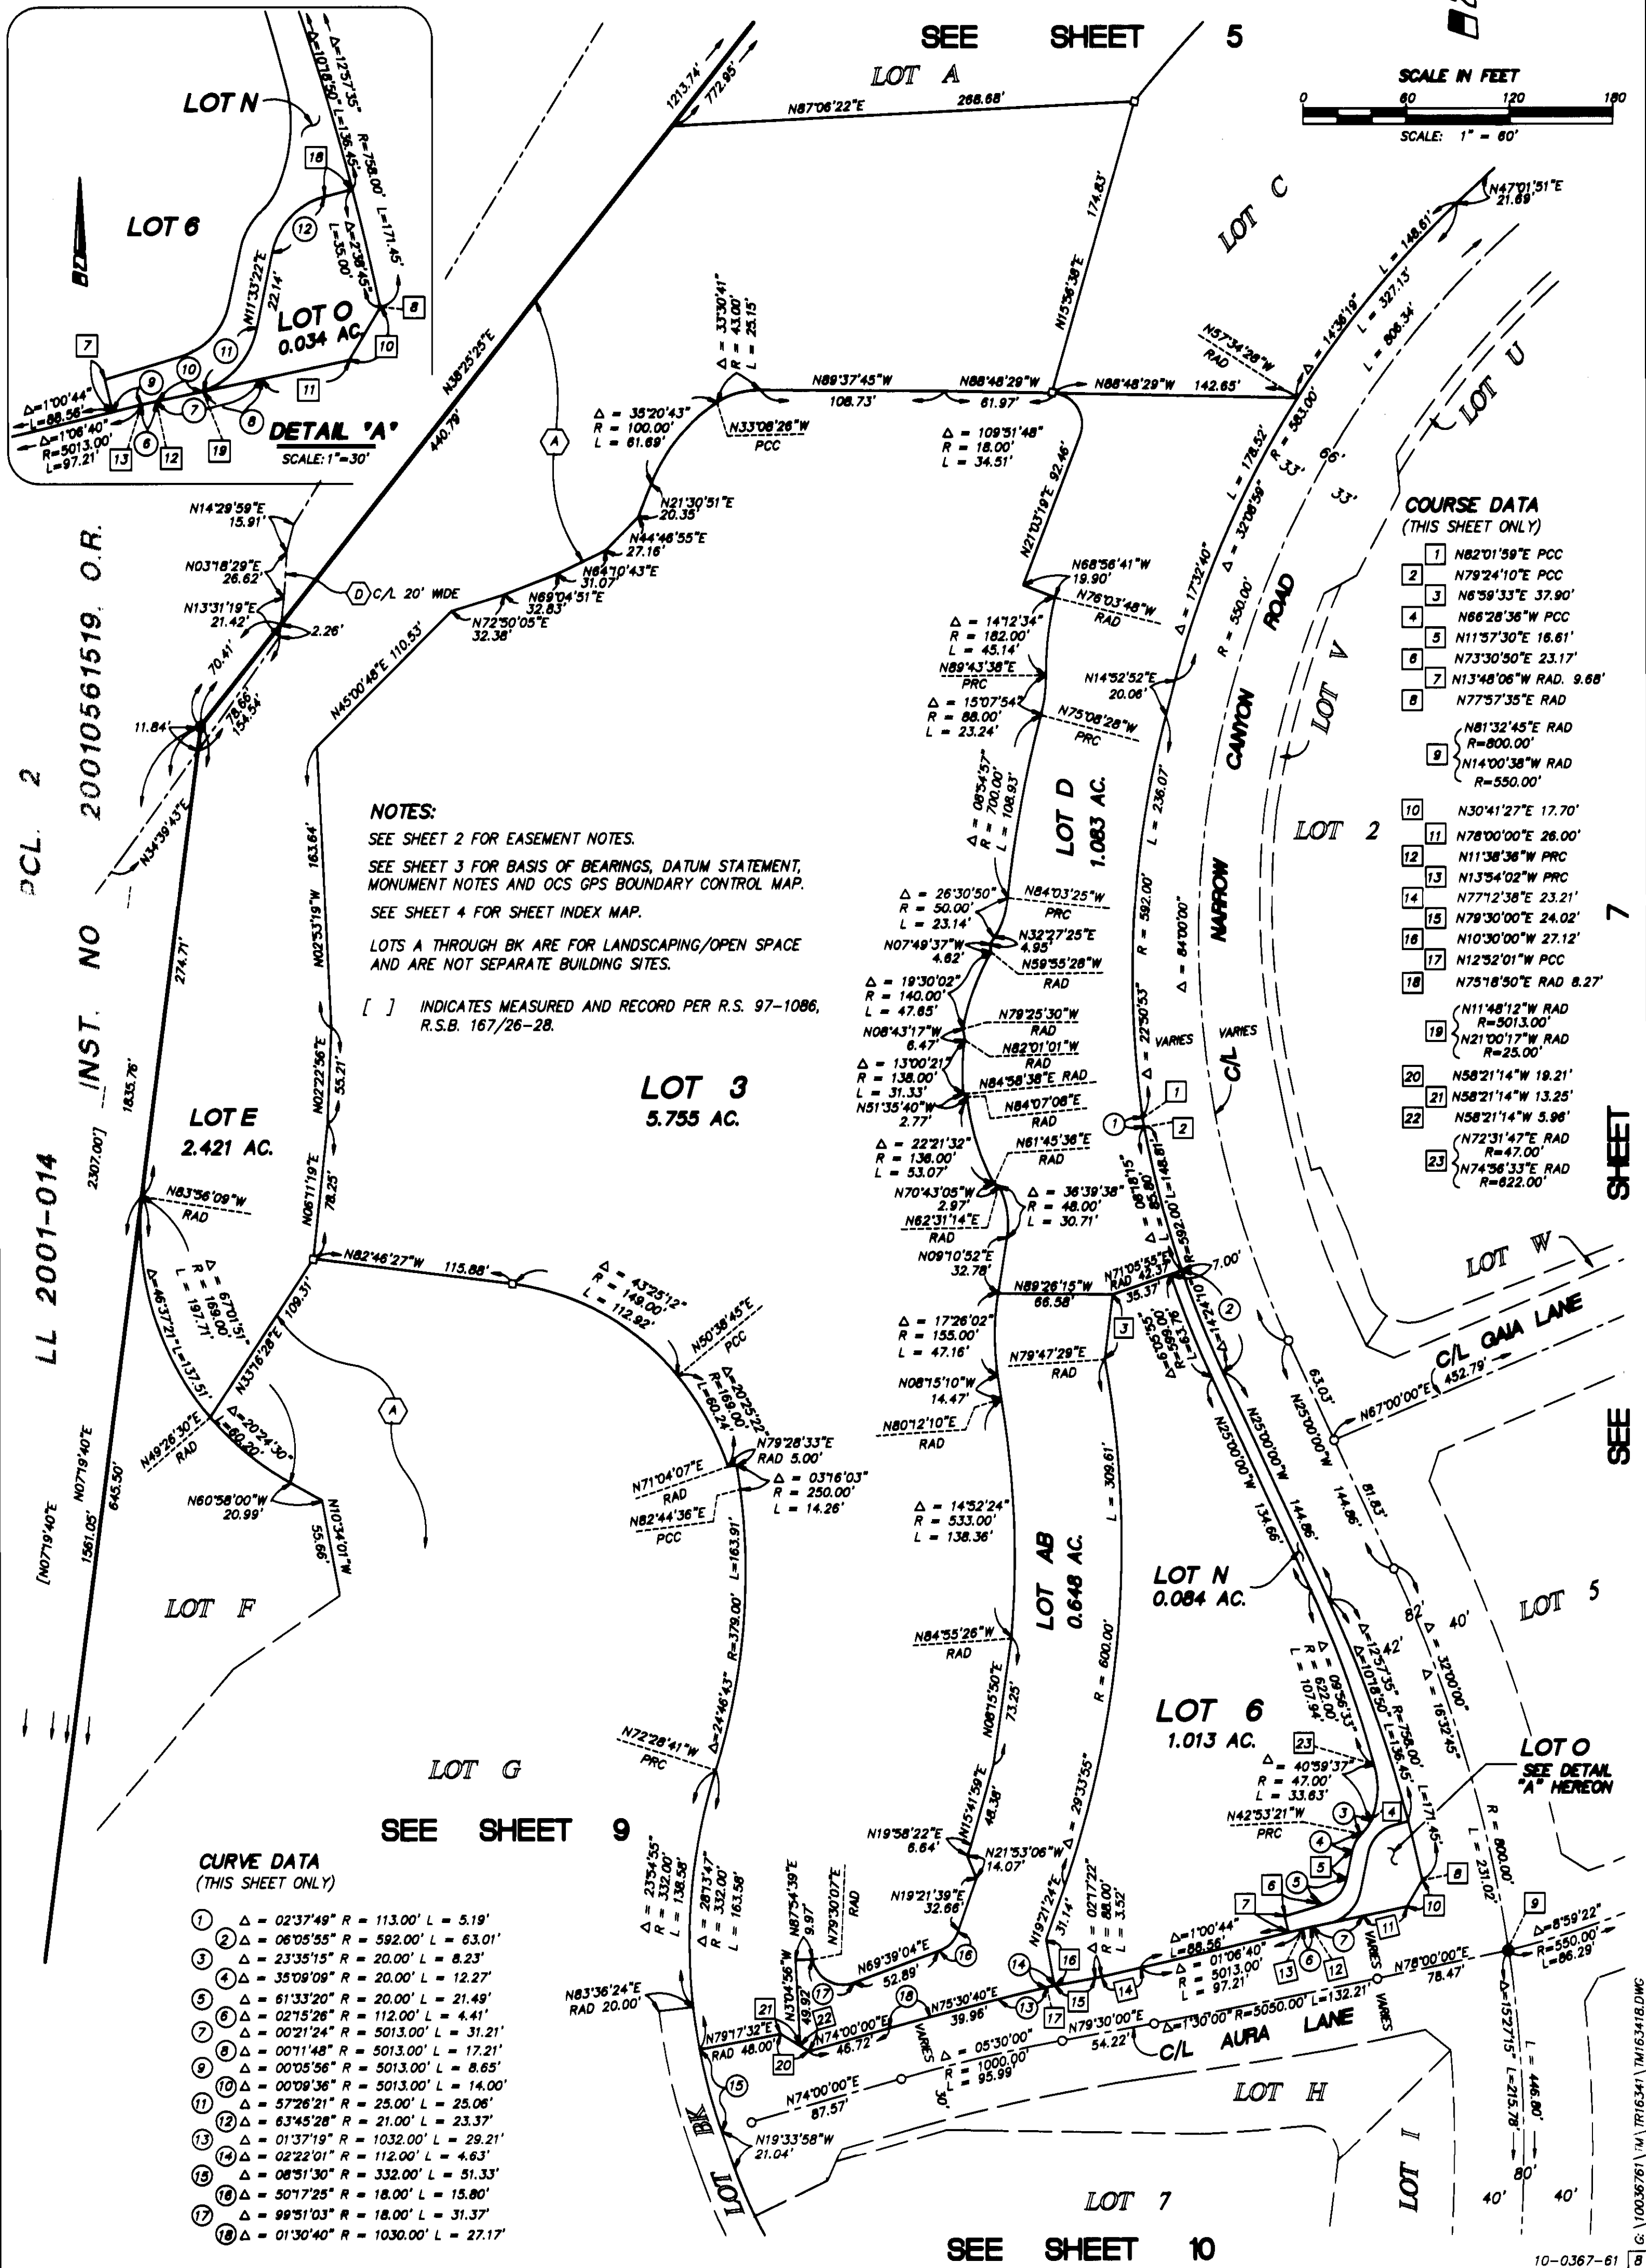

LL 2001-014
INST. NO 20010561519, O.R.
DCL. 2

NOTES:
SEE SHEET 2 FOR EASEMENT NOTES.
SEE SHEET 3 FOR BASIS OF BEARINGS, DATUM STATEMENT,
MONUMENT NOTES AND OCS GPS BOUNDARY CONTROL MAP.
SEE SHEET 4 FOR SHEET INDEX MAP.
LOTS A THROUGH BK ARE FOR LANDSCAPING/OPEN SPACE
AND ARE NOT SEPARATE BUILDING SITES.
[] INDICATES MEASURED AND RECORD PER R.S. 97-1086,
R.S.B. 167/26-28.

**COURSE DATA
(THIS SHEET ONLY)**

1	N82°01'59"E PCC
2	N79°24'10"E PCC
3	N6°59'33"E 37.90'
4	N66°28'36"W PCC
5	N11°57'30"E 16.61'
6	N73°30'50"E 23.17'
7	N13°48'06"W RAD. 9.68'
8	N77°57'35"E RAD
9	N81°32'45"E RAD R=800.00'
10	N14°00'38"W RAD R=550.00'
11	N30°41'27"E 17.70'
12	N78°00'00"E 26.00'
13	N11°38'36"W PRC
14	N13°54'02"W PRC
15	N77°12'38"E 23.21'
16	N78°30'00"E 24.02'
17	N10°30'00"W 27.12'
18	N12°52'01"W PCC
19	N75°18'50"E RAD 8.27'
20	N11°48'12"W RAD R=5013.00'
21	N21°00'17"W RAD R=25.00'
22	N58°21'14"W 19.21'
23	N58°21'14"W 13.25'
24	N58°21'14"W 5.98'
25	N72°31'47"E RAD R=47.00'
26	N74°56'33"E RAD R=622.00'


**CURVE DATA
(THIS SHEET ONLY)**

1	Δ = 02°37'49" R = 113.00' L = 5.19'
2	Δ = 06°05'55" R = 592.00' L = 63.01'
3	Δ = 23°35'15" R = 20.00' L = 8.23'
4	Δ = 35°09'09" R = 20.00' L = 12.27'
5	Δ = 61°33'20" R = 20.00' L = 21.49'
6	Δ = 02°15'28" R = 112.00' L = 4.41'
7	Δ = 00°21'24" R = 5013.00' L = 31.21'
8	Δ = 00°11'48" R = 5013.00' L = 17.21'
9	Δ = 00°05'56" R = 5013.00' L = 8.65'
10	Δ = 00°09'36" R = 5013.00' L = 14.00'
11	Δ = 57°26'21" R = 25.00' L = 25.06'
12	Δ = 63°45'28" R = 21.00' L = 23.37'
13	Δ = 01°37'19" R = 1032.00' L = 29.21'
14	Δ = 02°22'01" R = 112.00' L = 4.63'
15	Δ = 08°51'30" R = 332.00' L = 51.33'
16	Δ = 50°17'25" R = 18.00' L = 15.80'
17	Δ = 99°51'03" R = 18.00' L = 31.37'
18	Δ = 01°30'40" R = 1030.00' L = 27.17'

SEE SHEET 9

SEE SHEET 10

10-0367-61 8

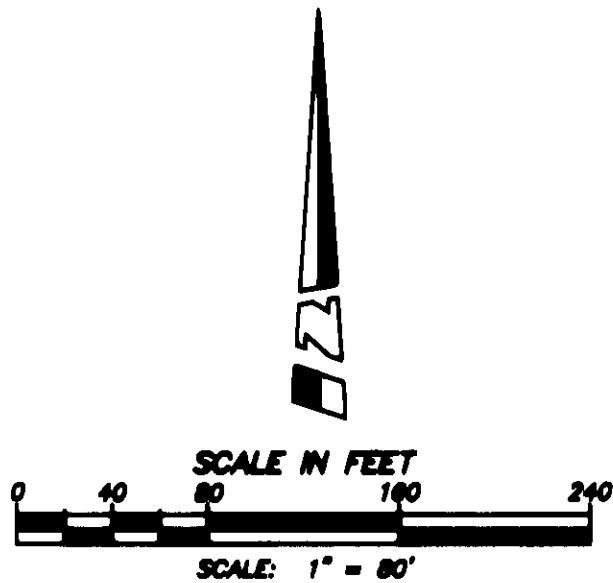

NOTES:


SEE SHEET 2 FOR EASEMENT NOTES.

SEE SHEET 3 FOR BASIS OF BEARINGS, DATUM STATEMENT,
MONUMENT NOTES AND OCS GPS BOUNDARY CONTROL MAP.

SEE SHEET 4 FOR SHEET INDEX MAP.

LOTS A THROUGH BK ARE FOR LANDSCAPING/OPEN SPACE
AND ARE NOT SEPARATE BUILDING SITES.

[] INDICATES MEASURED AND RECORD PER R.S. 97-1086,
R.S.B. 167/26-28.

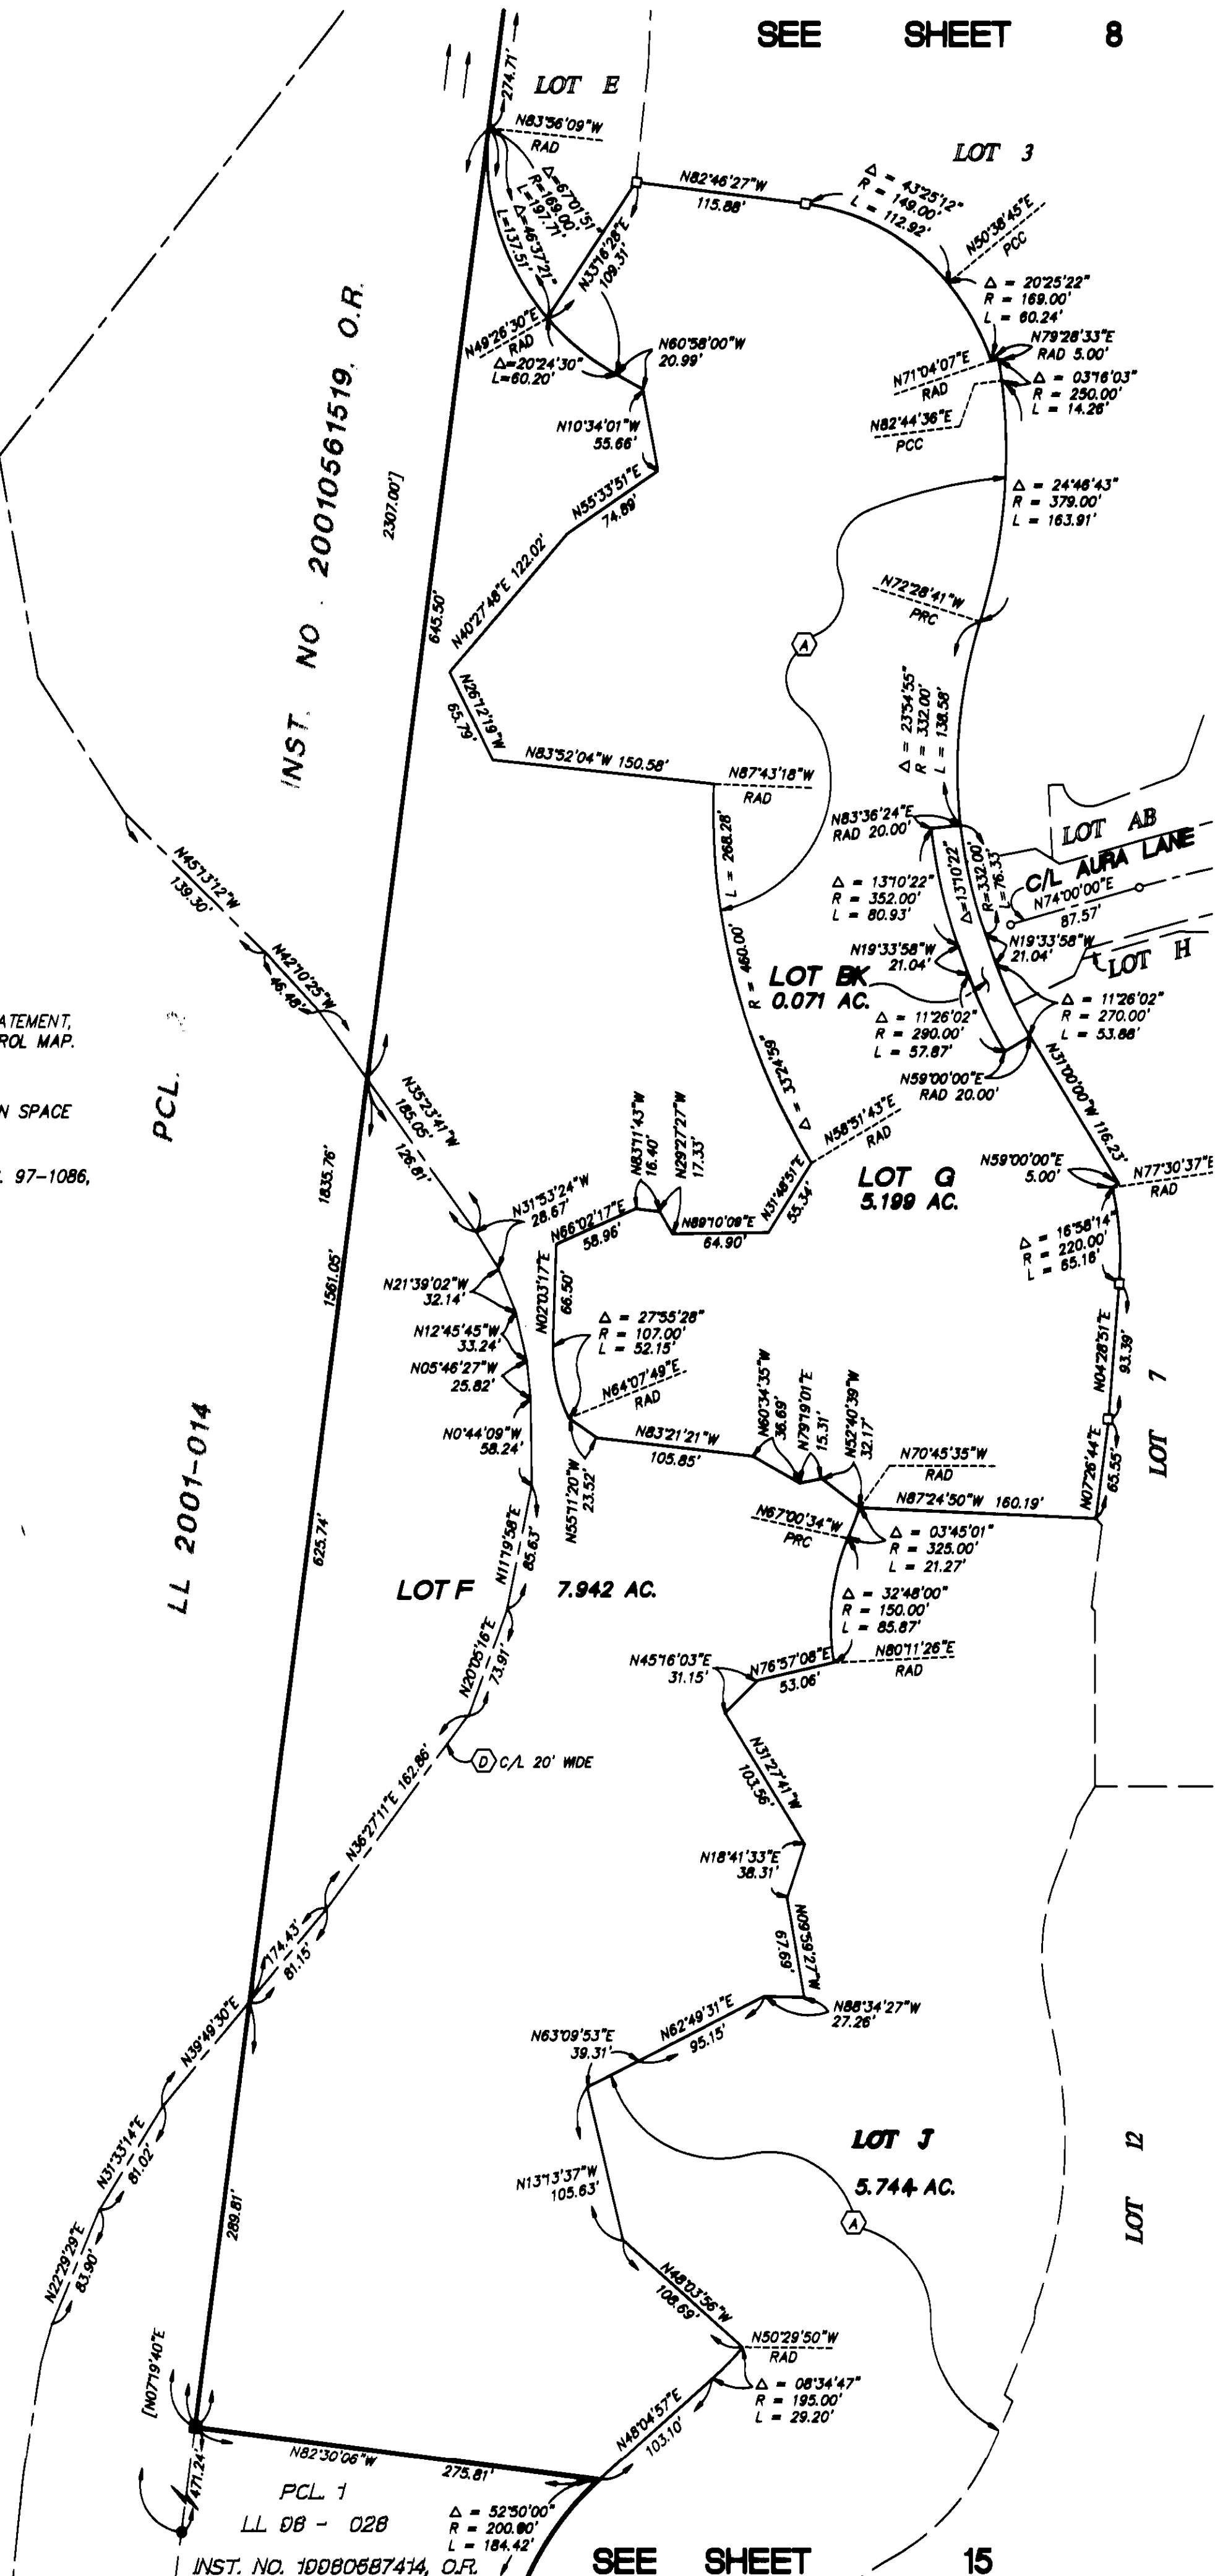

SEE SHEET 10

LOT 12

LOT 7

LOT 3

LOT 15

LOT 12

LOT 7

LOT 3

LOT E

LOT 15

LOT 12

LOT 7

LOT 3

LOT E

LOT 15

LOT 12

LOT 7

A PORTION OF VESTING
TENTATIVE TRACT NO. 16271

IN THE UNINCORPORATED TERRITORY OF ORANGE COUNTY, CALIFORNIA

JUNE 2002

JAMES F. GILLEN, L.S. 5557

DATE OF SURVEY:
JANUARY 1999

HUITT-ZOLLARS

17 NUMBERED LOTS AND 63 LETTERED LOTS

168.726 ACRES

NOTES:



SEE SHEET 2 FOR EASEMENT NOTES.

SEE SHEET 3 FOR BASIS OF BEARINGS, DATUM STATEMENT,
MONUMENT NOTES AND OCS GPS BOUNDARY CONTROL MAP.

SEE SHEET 4 FOR SHEET INDEX MAP.

LOTS A THROUGH BK ARE FOR LANDSCAPING/OPEN SPACE
AND ARE NOT SEPARATE BUILDING SITES.

SEE SHEET 8

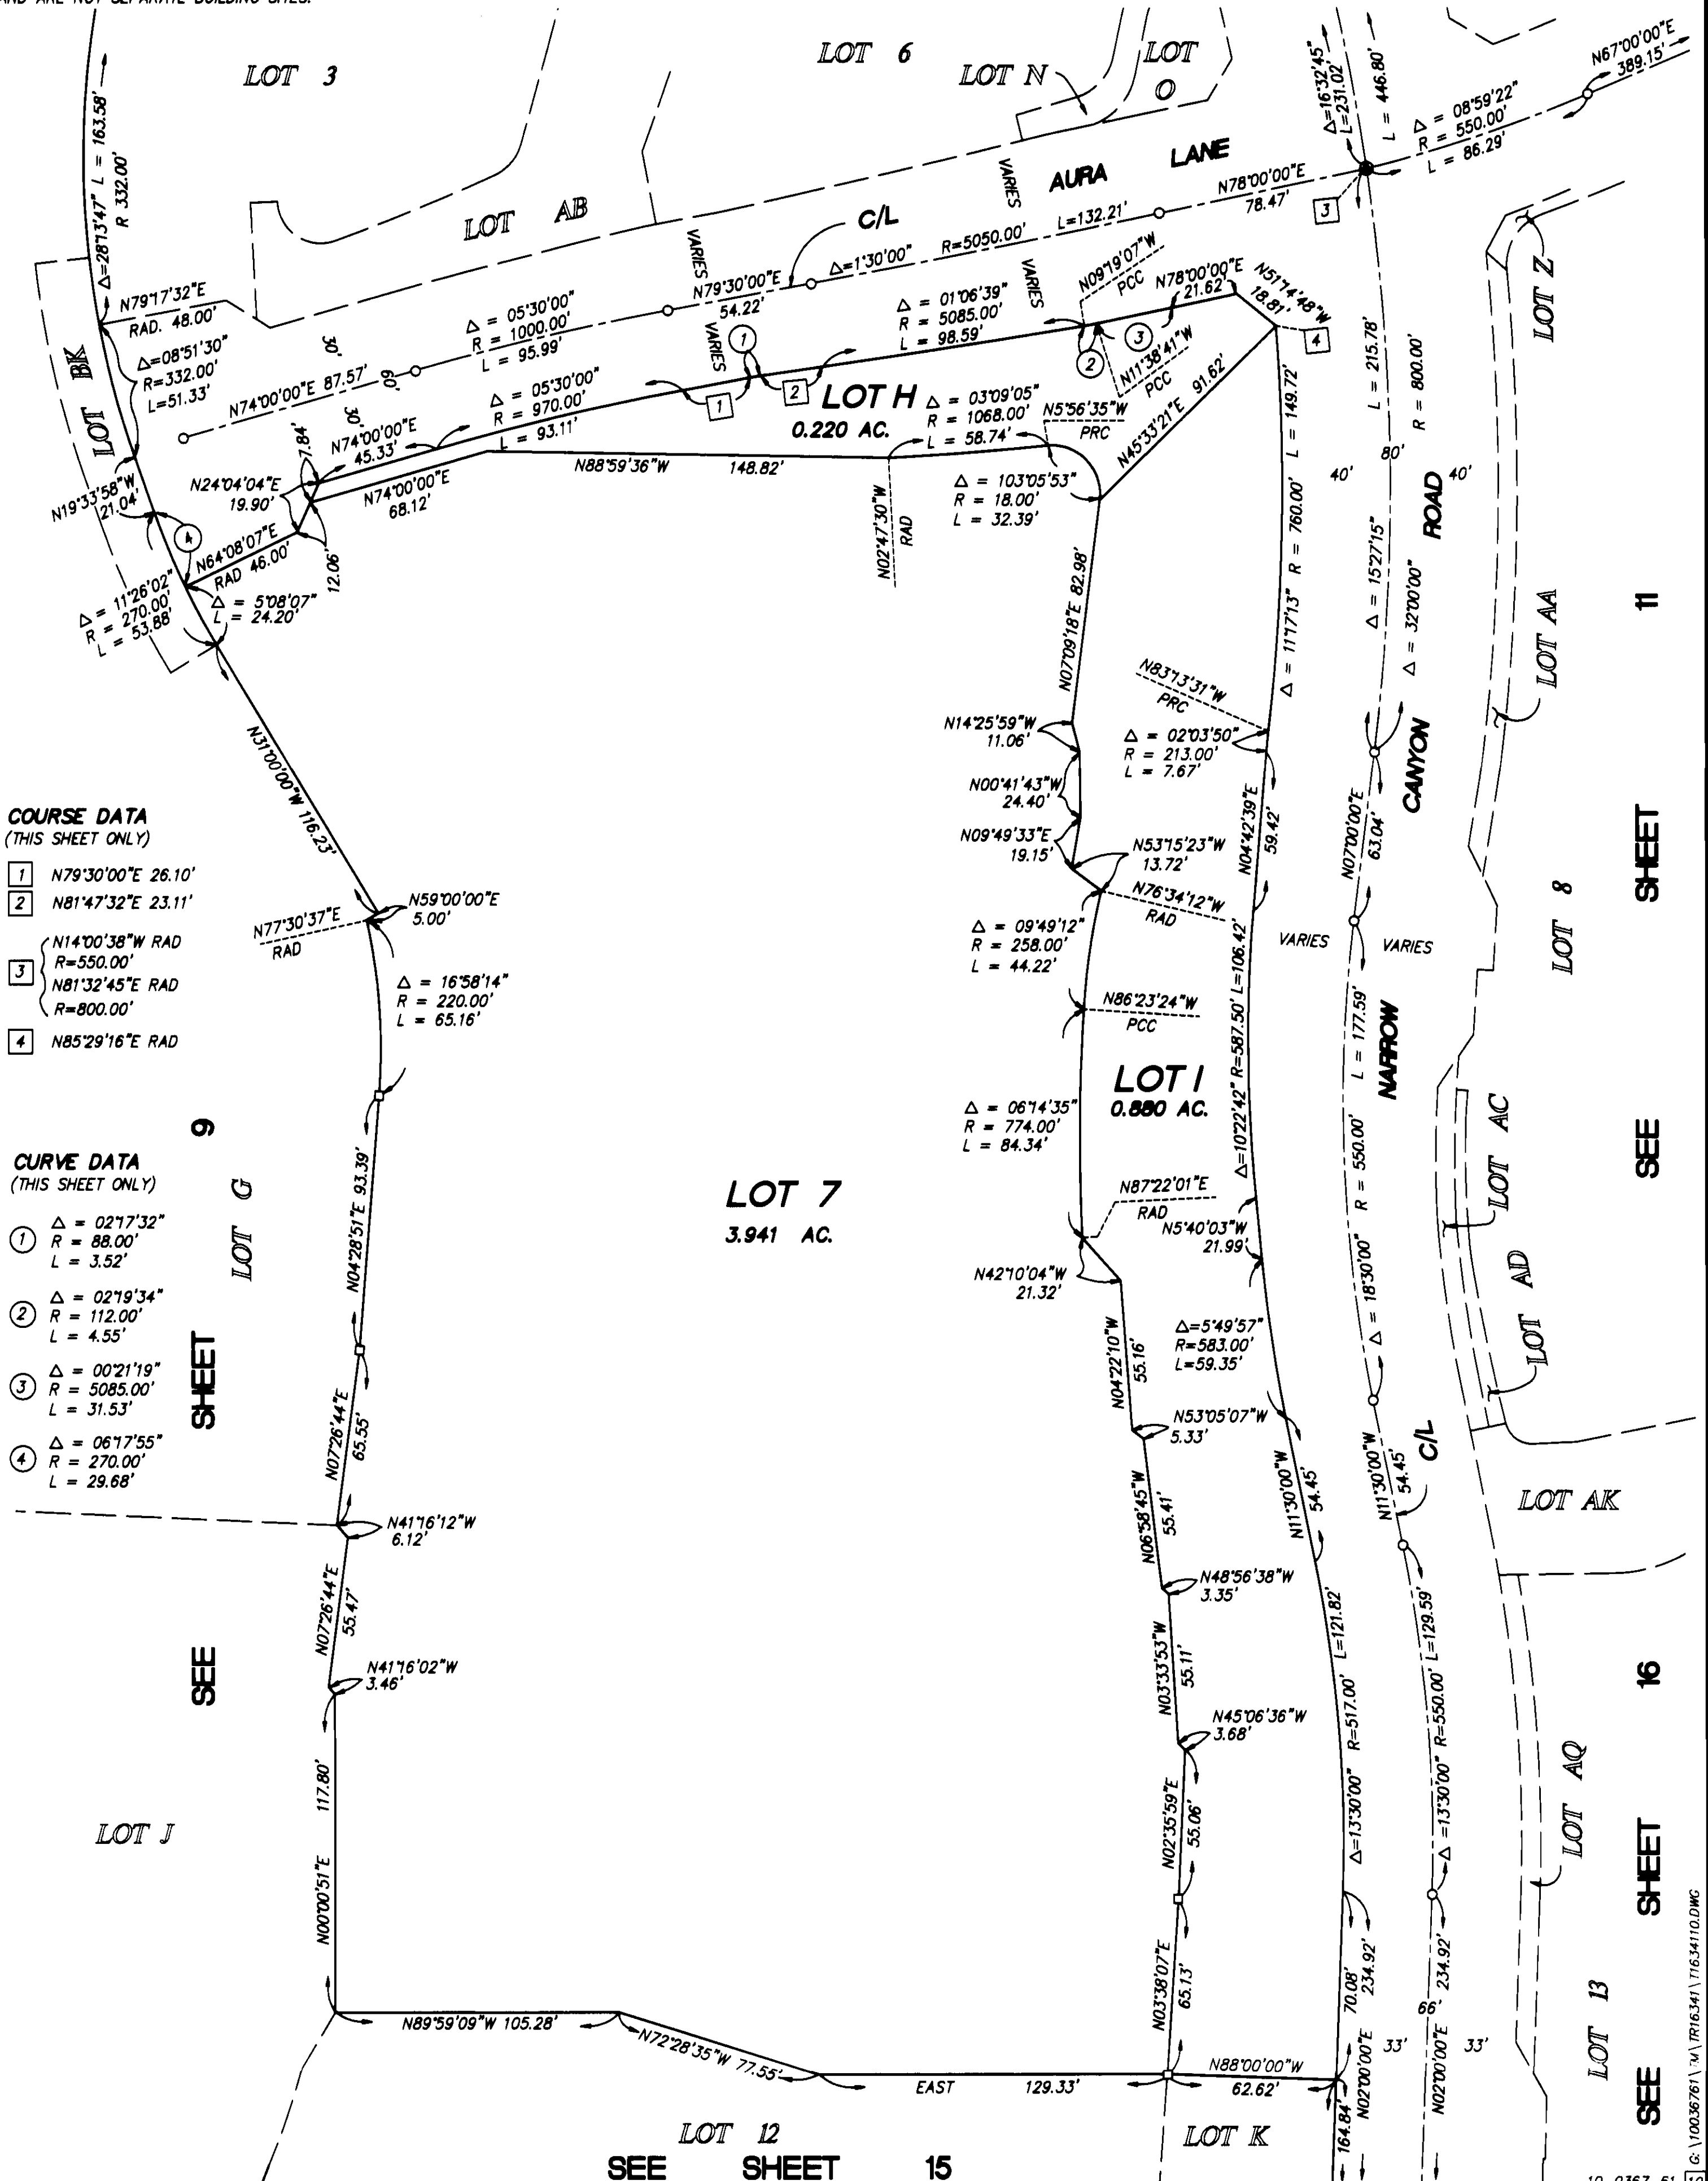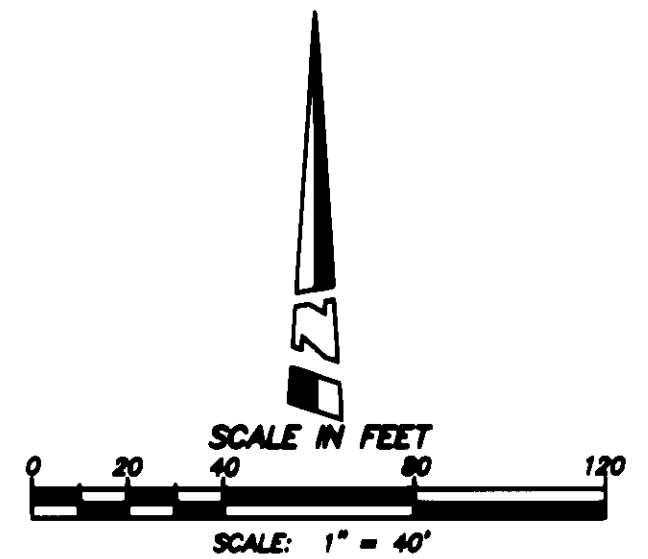

SEE SHEET 11

SEE SHEET 16

SEE SHEET 15

01 ohs

840 12

SHEET 12 OF 20 SHEETS

TRACT NO. 16341

IN THE UNINCORPORATED TERRITORY OF ORANGE COUNTY, CALIFORNIA

JUNE 2002

JAMES F. GILLEN, L.S. 5557

HUITT-ZOLLARS

17 NUMBERED LOTS AND 63 LETTERED LOTS

168.726 ACRES

A PORTION OF VESTING
TENTATIVE TRACT NO. 16271

DATE OF SURVEY:
JANUARY 1999

NOTES:

SEE SHEET 2 FOR EASEMENT NOTES.



SEE SHEET 3 FOR BASIS OF BEARINGS, DATUM STATEMENT,
MONUMENT NOTES AND OCS GPS BOUNDARY CONTROL MAP.

SEE SHEET 4 FOR SHEET INDEX MAP.

LOTS A THROUGH BK ARE FOR LANDSCAPING/OPEN SPACE
AND ARE NOT SEPARATE BUILDING SITES.

☒ INDICATES O'NEILL DRIVE STREET DEDICATION.


() INDICATES MEASURED AND RECORD PER
TRACT NO. 16203, M.M. 826/B-20,
UNLESS OTHERWISE NOTED.

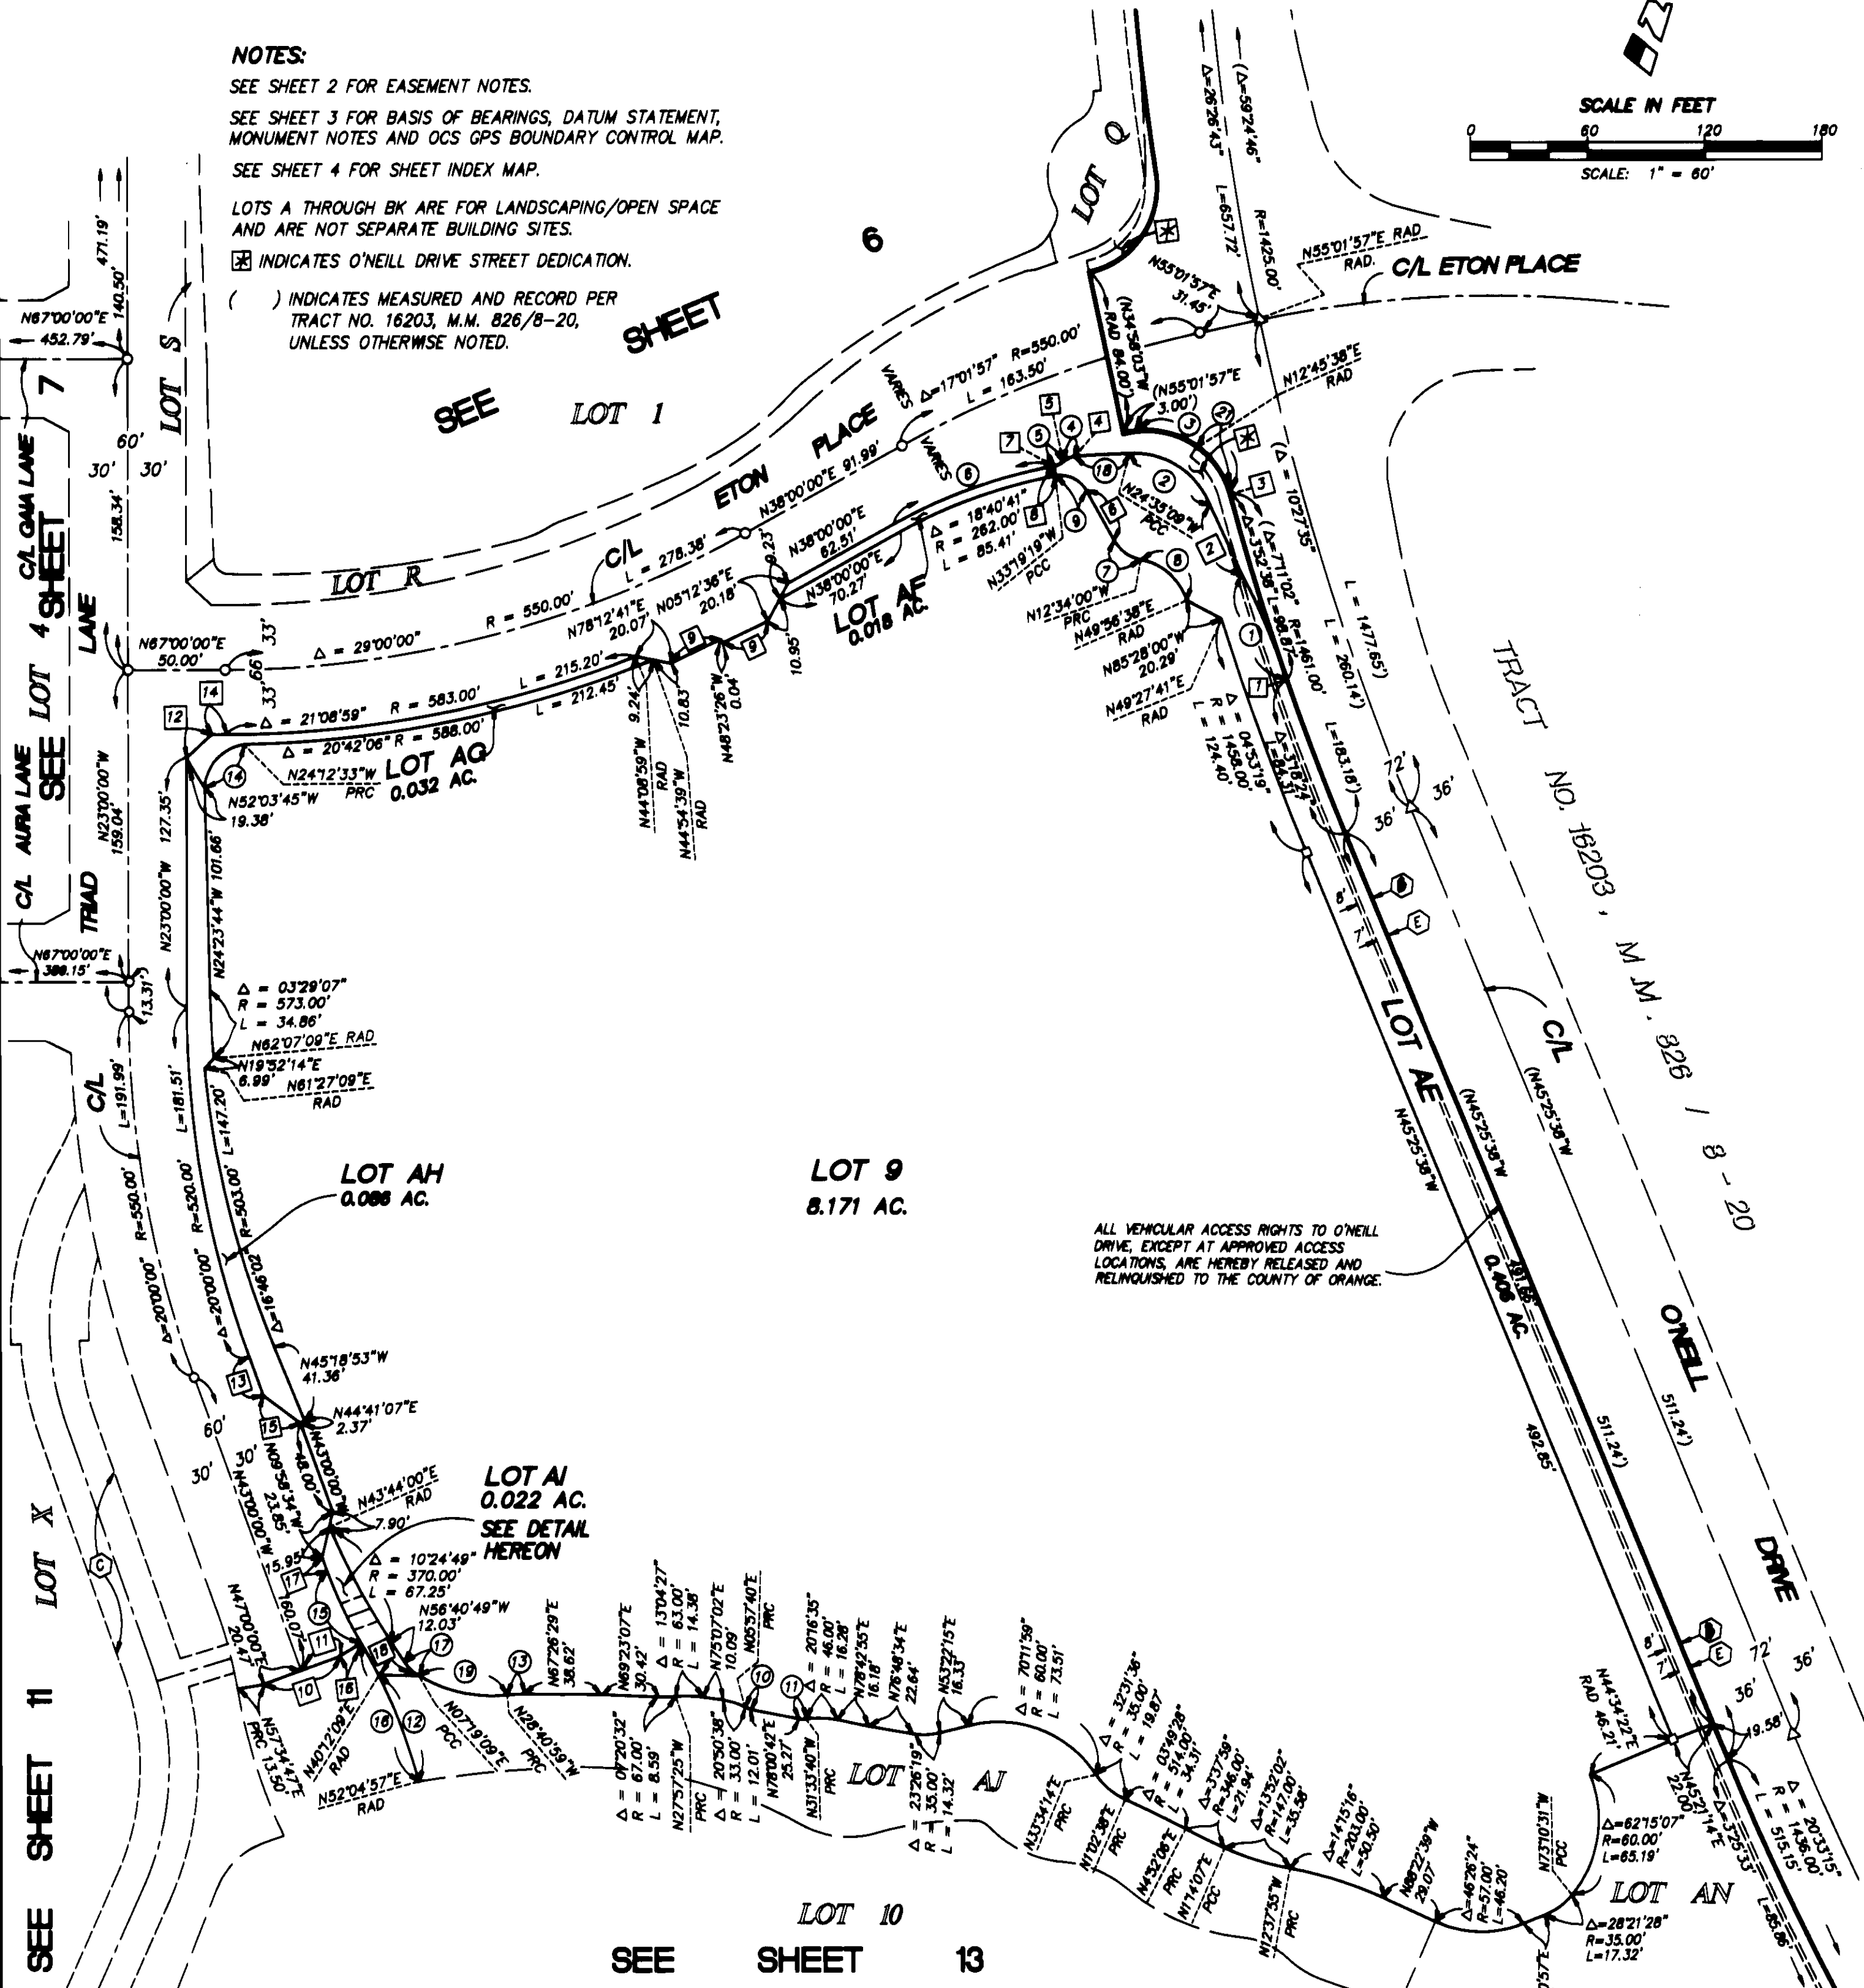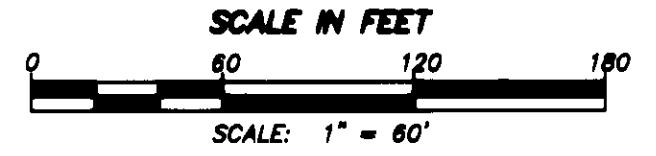

ALL VEHICULAR ACCESS RIGHTS TO O'NEILL
DRIVE, EXCEPT AT APPROVED ACCESS
LOCATIONS, ARE HEREBY RELEASED AND
RELINQUISHED TO THE COUNTY OF ORANGE.

COURSE DATA (THIS SHEET ONLY)

- 1 N47°52'46"E RAD
- 2 N47°59'02"W 38.78'
- 3 N51°45'24"E PRC
- 4 N27°36'09"W PCC
- 5 N63°10'20"W PRC
- 6 N52°13'34"W 29.08'
- 7 N33°15'15"W PRC
- 8 N29°41'41"W 5.01'
- 9 N41°36'34"E 27.00'
- 10 N47°00'00"E 40.94'
- 11 N47°00'00"E 20.47'
- 12 N24°17'26"E 17.69'
- 13 N43°00'00"W 21.78'
- 14 N67°00'00"E 7.00'
- 15 N76°01'26"W 23.85'
- 16 N36°25'13"E PRC
- 17 N43°00'00"W 7.42'
- 18 N68°10'38"E 20.75'

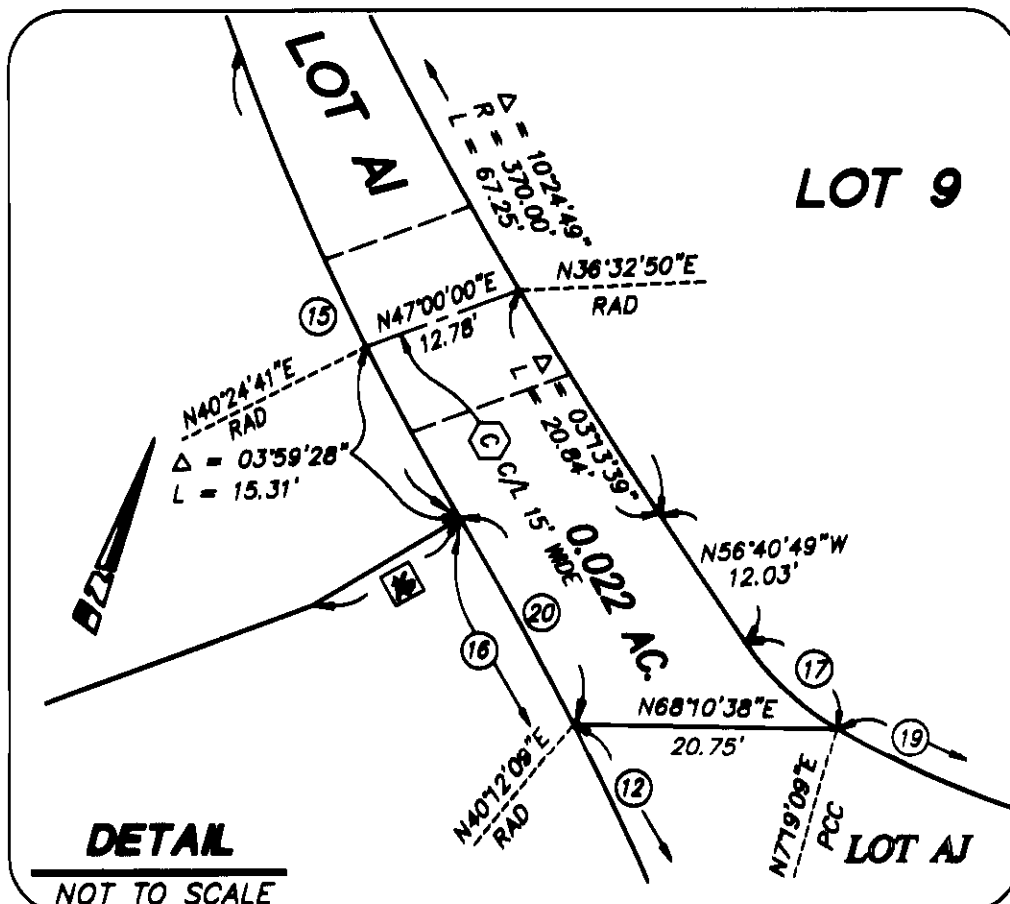

CURVE DATA (THIS SHEET ONLY)

- 1 Δ = 05°51'48" R = 571.00' L = 58.43'
- 2 Δ = 66°36'07" R = 45.00' L = 52.31'
- 3 Δ = 86°43'27" R = 44.00' L = 66.80'
- 4 Δ = 35°34'11" R = 12.00' L = 7.45'
- 5 Δ = 29°55'05" R = 10.00' L = 5.22'
- 6 Δ = 18°44'45" R = 267.00' L = 87.36'
- 7 Δ = 50°20'26" R = 20.00' L = 17.57'
- 8 Δ = 62°30'38" R = 30.00' L = 32.73'
- 9 Δ = 71°05'45" R = 15.00' L = 18.61'
- 10 Δ = 17°58'58" R = 10.00' L = 3.13'
- 11 Δ = 19°34'22" R = 10.00' L = 3.42'
- 12 Δ = 11°52'48" R = 280.00' L = 58.06'
- 13 Δ = 06°07'28" R = 81.00' L = 8.66'
- 14 Δ = 90°11'11" R = 23.50' L = 36.99'
- 15 Δ = 10°34'47" R = 220.00' L = 40.62'
- 16 Δ = 15°39'44" R = 280.00' L = 76.54'
- 17 Δ = 26°00'02" R = 22.00' L = 9.98'
- 18 Δ = 03°01'00" R = 520.00' L = 27.38'
- 19 Δ = 38°00'08" R = 75.00' L = 47.13'
- 20 Δ = 03°46'56" R = 280.00' L = 18.48'
- 21 Δ = 38°59'46" R = 44.00' L = 29.95'

SEE SHEET 13

G:\10036761\16341\1634112.DWG

840 13

SHEET 13 OF 20 SHEETS

TRACT NO. 16341

A PORTION OF VESTING
TENTATIVE TRACT NO. 16271

IN THE UNINCORPORATED TERRITORY OF ORANGE COUNTY, CALIFORNIA

JUNE 2002


JAMES F. GILLEN, L.S. 5557

DATE OF SURVEY:
JANUARY 1999


HUITT-ZOLLARS

17 NUMBERED LOTS AND 63 LETTERED LOTS

168.726 ACRES

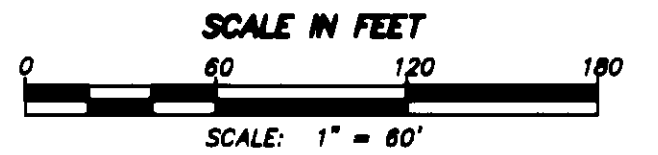

SEE SHEET 14

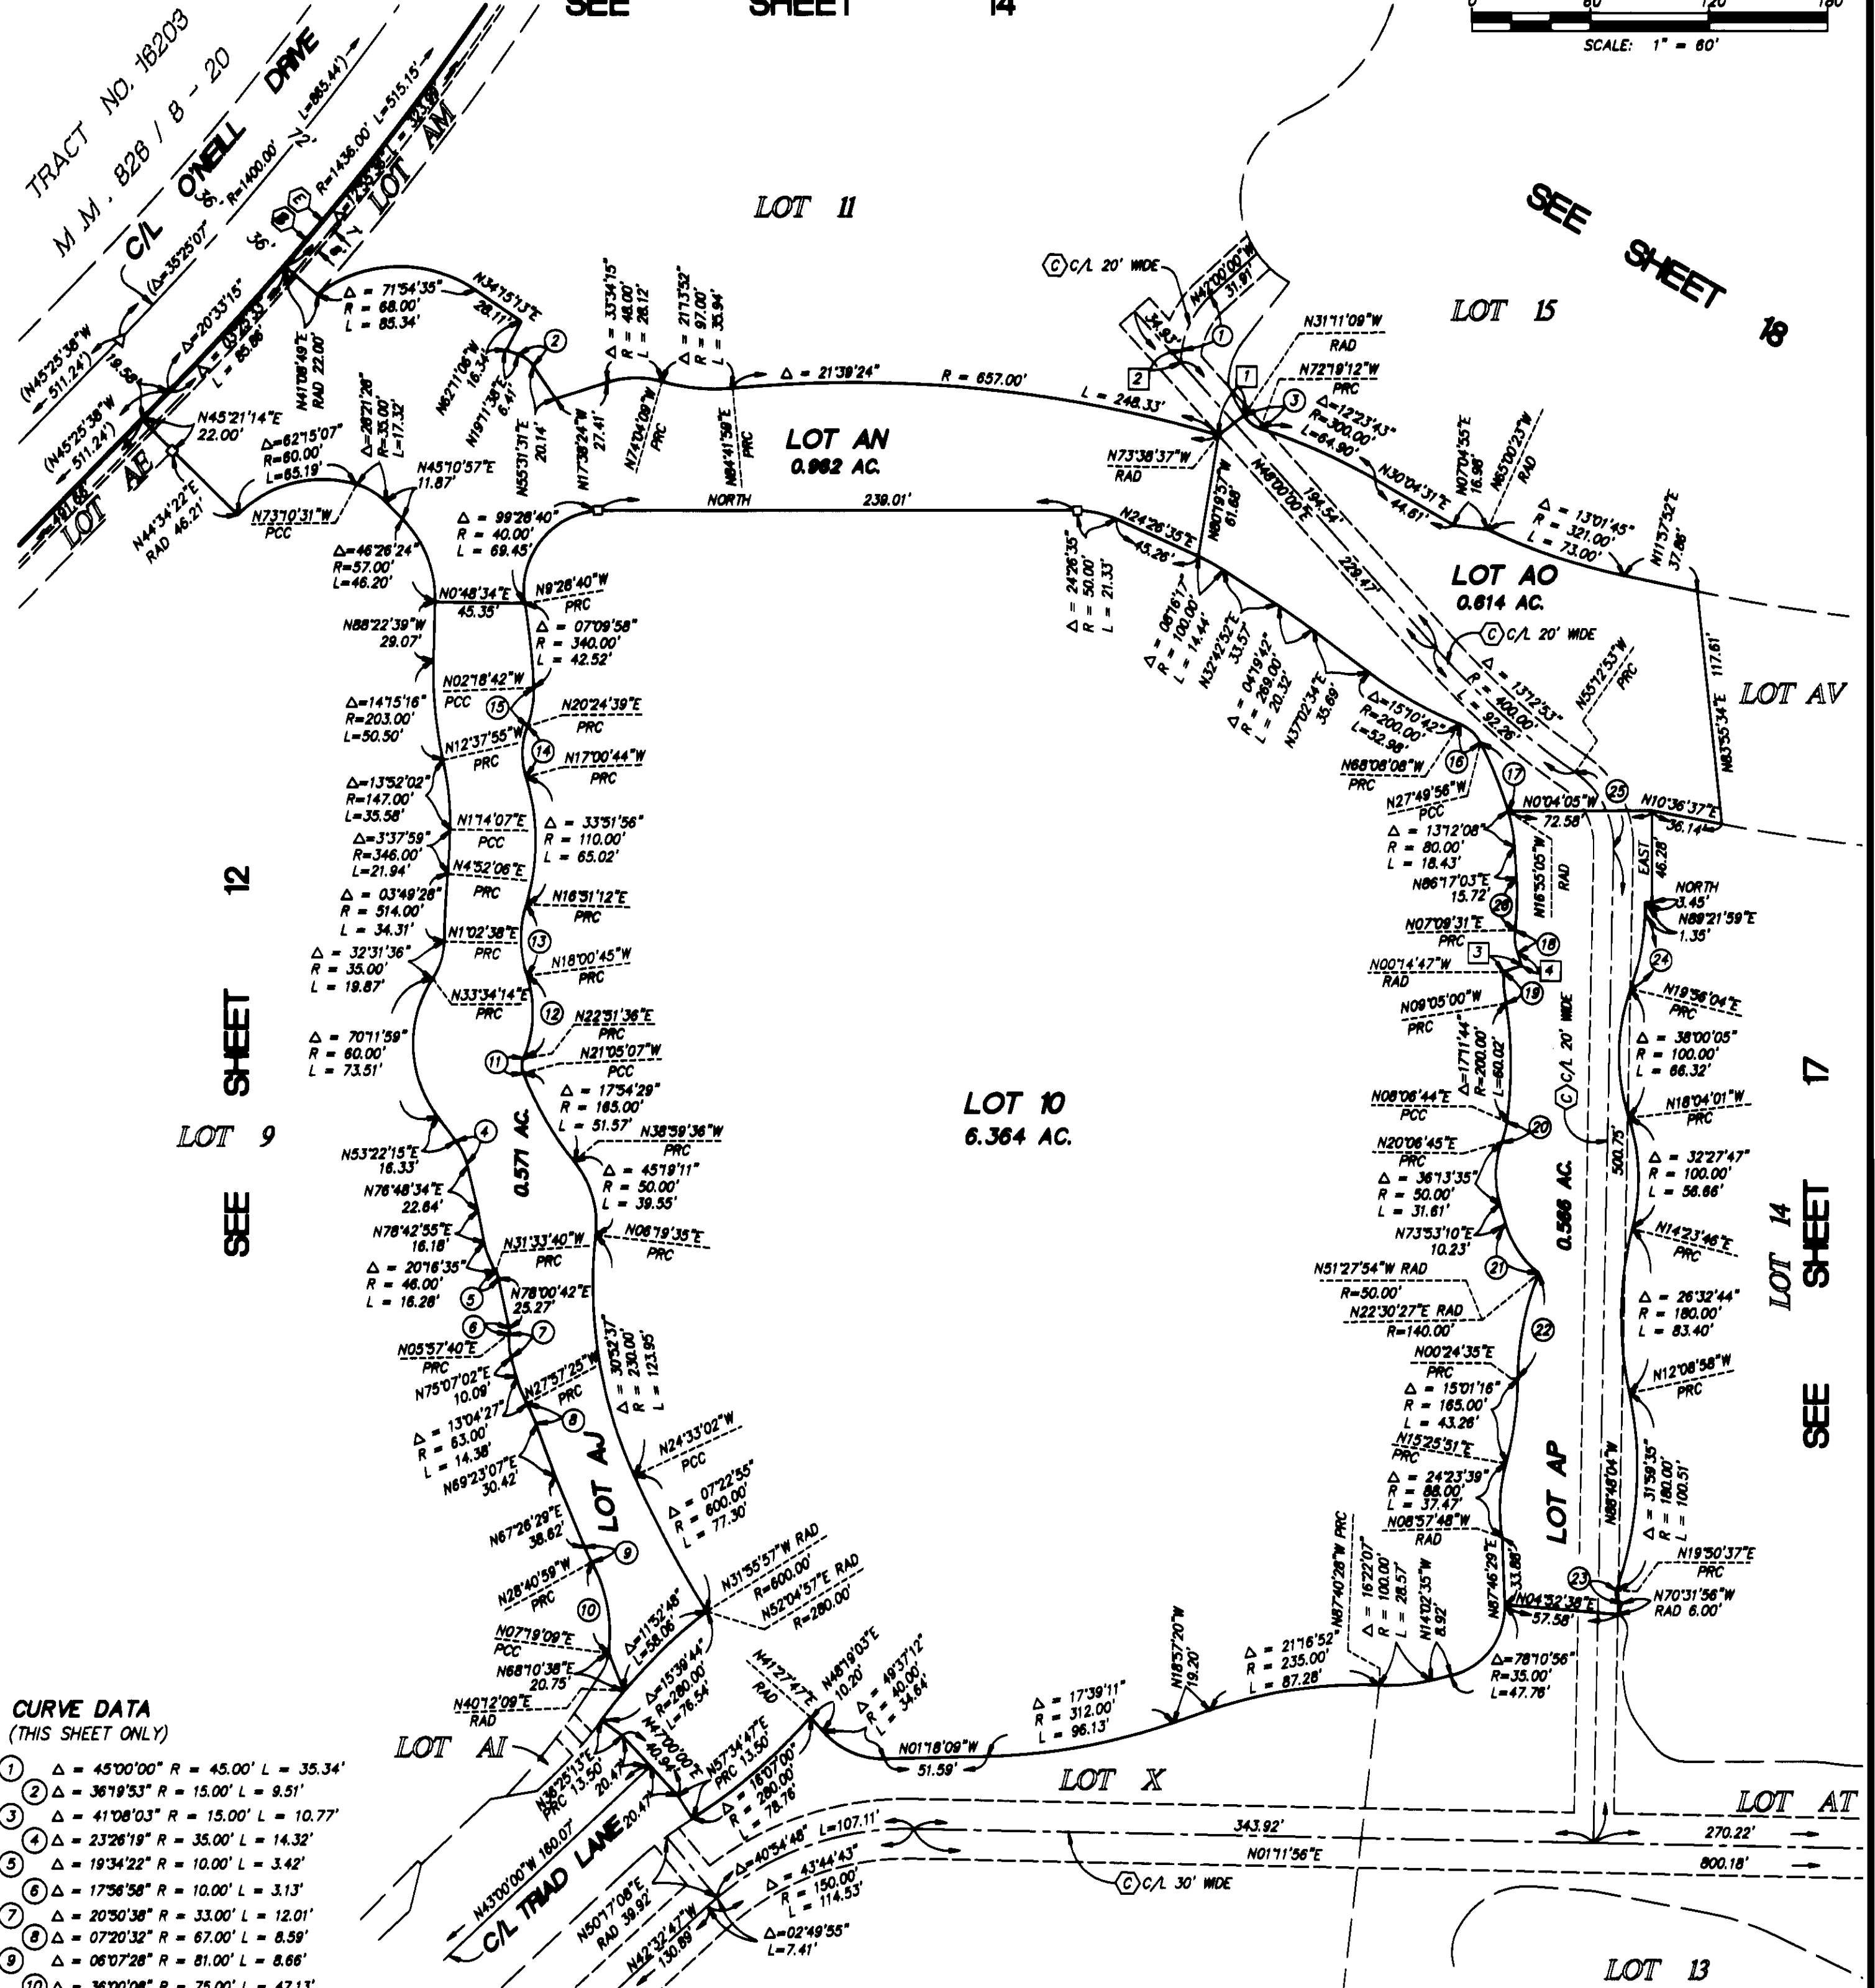

CURVE DATA (THIS SHEET ONLY)

- 1 $\Delta = 45^{\circ}00'00''$ R = 45.00' L = 35.34'
- 2 $\Delta = 36^{\circ}19'53''$ R = 15.00' L = 9.51'
- 3 $\Delta = 41^{\circ}08'03''$ R = 15.00' L = 10.77'
- 4 $\Delta = 23^{\circ}26'19''$ R = 35.00' L = 14.32'
- 5 $\Delta = 19^{\circ}34'22''$ R = 10.00' L = 3.42'
- 6 $\Delta = 17^{\circ}56'58''$ R = 10.00' L = 3.13'
- 7 $\Delta = 20^{\circ}30'38''$ R = 33.00' L = 12.01'
- 8 $\Delta = 07^{\circ}20'32''$ R = 67.00' L = 8.59'
- 9 $\Delta = 06^{\circ}07'28''$ R = 81.00' L = 8.66'
- 10 $\Delta = 36^{\circ}00'08''$ R = 75.00' L = 47.13'
- 11 $\Delta = 43^{\circ}36'43''$ R = 10.00' L = 7.67'
- 12 $\Delta = 40^{\circ}32'21''$ R = 60.00' L = 42.80'
- 13 $\Delta = 34^{\circ}31'37''$ R = 60.00' L = 36.51'
- 14 $\Delta = 37^{\circ}25'23''$ R = 40.00' L = 26.13'
- 15 $\Delta = 22^{\circ}43'21''$ R = 50.00' L = 19.83'
- 16 $\Delta = 40^{\circ}18'12''$ R = 20.00' L = 14.07'
- 17 $\Delta = 10^{\circ}34'51''$ R = 196.00' L = 37.34'
- 18 $\Delta = 26^{\circ}39'03''$ R = 25.00' L = 11.63'
- 19 $\Delta = 08^{\circ}30'13''$ R = 104.00' L = 16.04'
- 20 $\Delta = 12^{\circ}00'01''$ R = 50.00' L = 10.47'
- 21 $\Delta = 35^{\circ}21'04''$ R = 50.00' L = 30.85'
- 22 $\Delta = 22^{\circ}05'52''$ R = 140.00' L = 54.00'
- 23 $\Delta = 90^{\circ}22'33''$ R = 5.00' L = 7.89'
- 24 $\Delta = 20^{\circ}34'05''$ R = 120.00' L = 43.08'
- 25 $\Delta = 56^{\circ}24'49''$ R = 45.00' L = 44.31'
- 26 $\Delta = 10^{\circ}52'28''$ R = 139.00' L = 26.38'

COURSE DATA (THIS SHEET ONLY)

- 1 N37°48'23"W 16.09'
- 2 N87°00'00"W 2.47'
- 3 N19°29'32"W 10.00'
- 4 N70°30'28"E 6.70'

NOTES:

SEE SHEET 2 FOR EASEMENT NOTES.

SEE SHEET 3 FOR BASIS OF BEARINGS, DATUM STATEMENT, MONUMENT NOTES AND OCS GPS BOUNDARY CONTROL MAP.

SEE SHEET 4 FOR SHEET INDEX MAP.

LOTS A THROUGH BK ARE FOR LANDSCAPING/OPEN SPACE AND ARE NOT SEPARATE BUILDING SITES.

() INDICATES MEASURED AND RECORD PER TRACT NO. 16203, M.M. 826/B-20, UNLESS OTHERWISE NOTED.

DATE OF SURVEY:
JANUARY 1999

TRACT NO. 16341

IN THE UNINCORPORATED TERRITORY OF ORANGE COUNTY, CALIFORNIA


JUNE 2002

JAMES F. GILLEN, L.S. 5557

HUITT-ZOLLARS

17 NUMBERED LOTS AND 63 LETTERED LOTS

168.726 ACRES

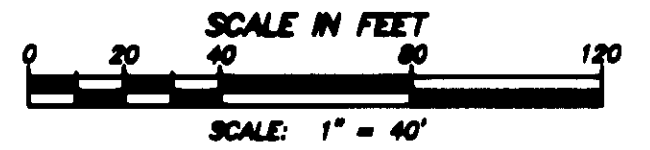

CURVE DATA
(THIS SHEET ONLY)

① $\Delta=0^{\circ}48'35''$ $R=1436.00'$ $L=20.29'$

ALL VEHICULAR ACCESS RIGHTS TO O'NEILL DRIVE, EXCEPT AT APPROVED ACCESS LOCATIONS, ARE HEREBY RELEASED AND RELINQUISHED TO THE COUNTY OF ORANGE.

LOT 11
4.213 AC.

LOT AL
0.013 AC.

REFERENCE LINE FOR 200' WIDE
SOUTHERN CALIFORNIA EDISON
COMPANY EASEMENT PER BOOK
PAGE 714, O.R.

SEE ABOVE LEFT!

NOTES:

SEE SHEET 2 FOR EASEMENT NOTES.

SEE SHEET 3 FOR BASIS OF BEARINGS, DATUM STATEMENT,
MONUMENT NOTES AND OCS GPS BOUNDARY CONTROL MAP.
SEE SHEET 4 FOR SHEET INDEX MAP.

LOTS A THROUGH BK ARE FOR LANDSCAPING/OPEN SPACE
AND ARE NOT SEPARATE BUILDING SITES.

() INDICATES MEASURED AND RECORD PER TRACT NO. 16203,
M.M. 826/8-20, UNLESS OTHERWISE NOTED.

SEE SHEET 18

2: \0036\01\IM\IR1634\11634114.DWG

14 ohz

840 15

SHEET 15 OF 20 SHEETS

TRACT NO. 16341

A PORTION OF VESTING
TENTATIVE TRACT NO. 16271

IN THE UNINCORPORATED TERRITORY OF ORANGE COUNTY, CALIFORNIA

JUNE 2002

JAMES F. GILLEN, L.S. 5557



DATE OF SURVEY:
JANUARY 1999

HUITT-ZOLIARS

17 NUMBERED LOTS AND 63 LETTERED LOTS

168.726 ACRES

SEE SHEET 10

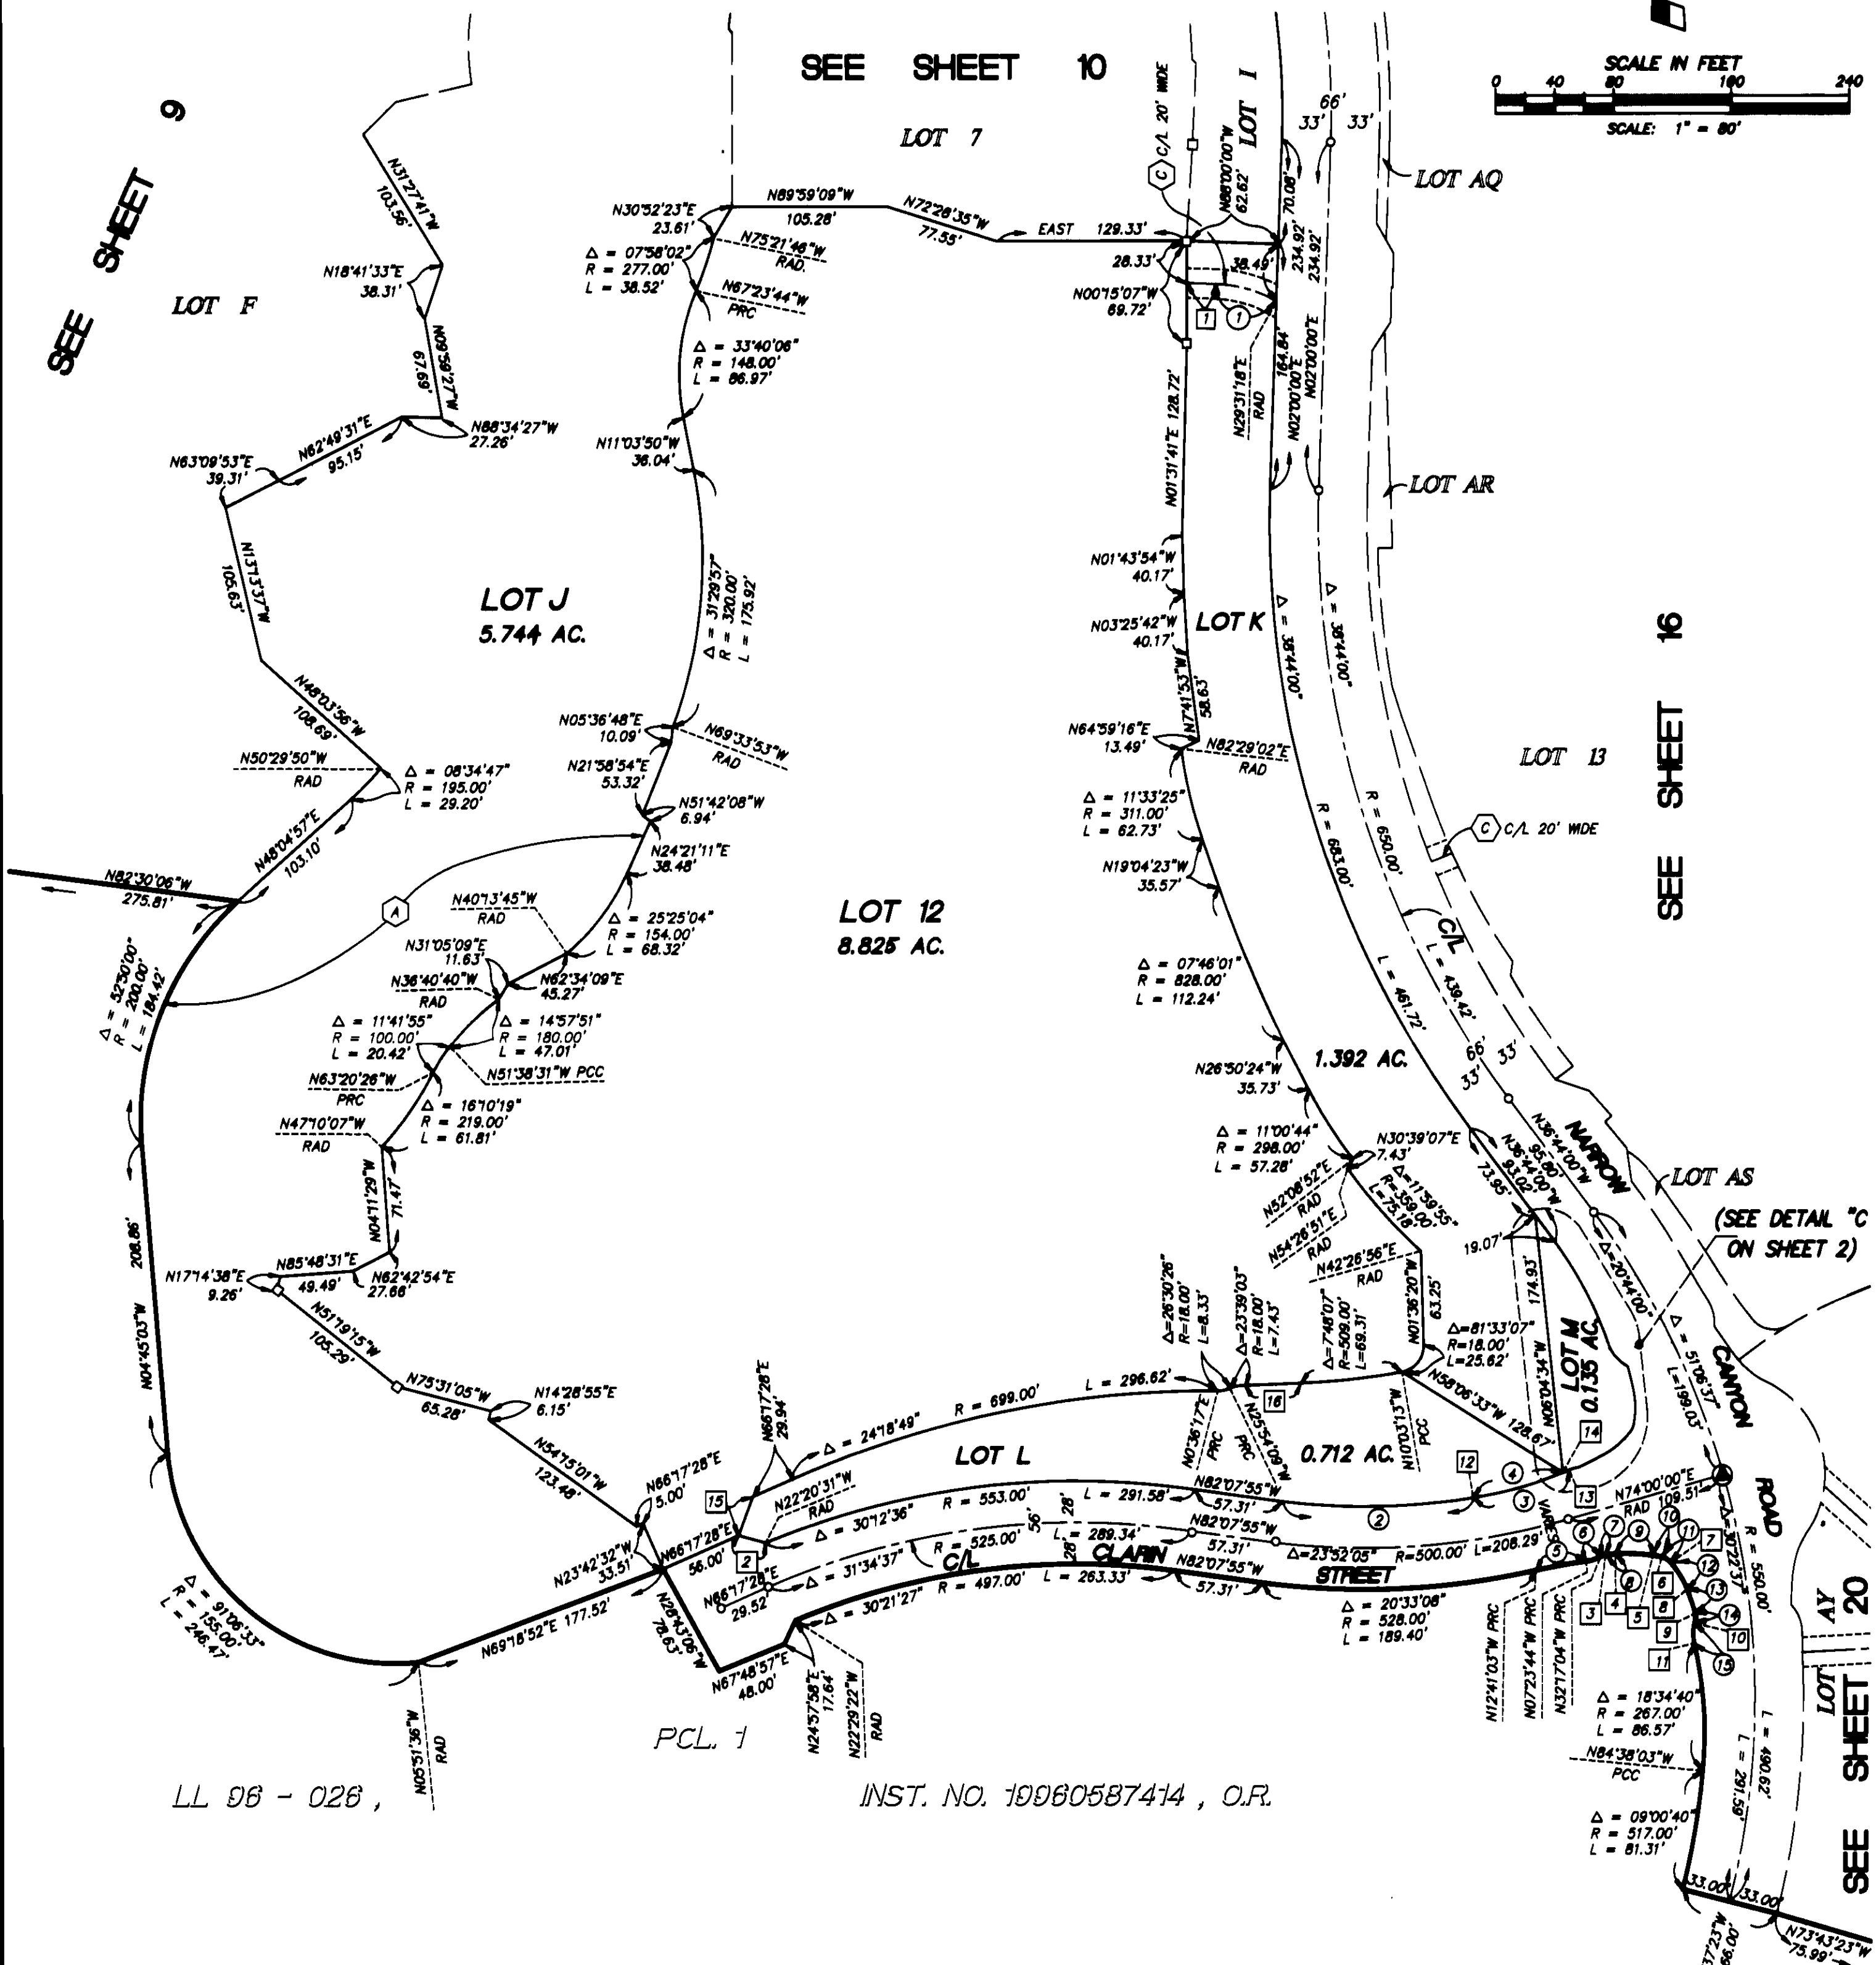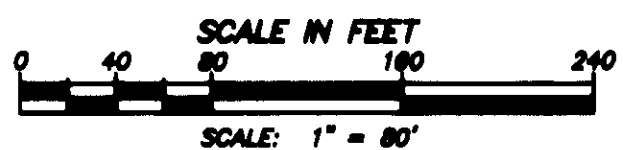

CURVE DATA (THIS SHEET ONLY)

- 1 $\Delta = 2731'18''$ $R = 90.00'$ $L = 43.23'$
- 2 $\Delta = 1648'06''$ $R = 472.00'$ $L = 138.41'$
- 3 $\Delta = 1418'21''$ $R = 272.00'$ $L = 67.91'$
- 4 $\Delta = 1320'42''$ $R = 272.00'$ $L = 63.35'$
- 5 $\Delta = 0577'19''$ $R = 372.00'$ $L = 34.34'$
- 6 $\Delta = 2453'20''$ $R = 28.00'$ $L = 12.16'$
- 7 $\Delta = 2649'44''$ $R = 2.00'$ $L = 0.94'$
- 8 $\Delta = 0052'48''$ $R = 375.00'$ $L = 5.76'$
- 9 $\Delta = 1239'40''$ $R = 125.00'$ $L = 27.62'$
- 10 $\Delta = 0558'53''$ $R = 57.00'$ $L = 5.95'$
- 11 $\Delta = 3378'02''$ $R = 12.00'$ $L = 6.97'$
- 12 $\Delta = 2143'22''$ $R = 57.00'$ $L = 21.61'$
- 13 $\Delta = 0402'58''$ $R = 273.00'$ $L = 19.29'$
- 14 $\Delta = 3843'58''$ $R = 2.00'$ $L = 1.35'$
- 15 $\Delta = 3505'04''$ $R = 28.00'$ $L = 17.15'$

COURSE DATA (THIS SHEET ONLY)

- 1 $N88^{\circ}00'00''W$ 19.92'
- 2 $N74^{\circ}31'03''W$ 18.98'
- 3 $N52^{\circ}27'20''W$ PCC
- 4 $N04^{\circ}34'32''W$ PCC
- 5 $N08^{\circ}05'08''E$ PCC
- 6 $N14^{\circ}04'01''E$ PCC
- 7 $N47^{\circ}22'03''E$ PCC
- 8 $N69^{\circ}05'25''E$ PCC
- 9 $N73^{\circ}08'23''E$ PCC
- 10 $N68^{\circ}07'39''W$ PRC
- 11 $N76^{\circ}47'17''E$ PRC
- 12 $N08^{\circ}58'01''W$ PCC
- 13 $N23^{\circ}14'22''W$ PRC
- 14 $N22^{\circ}16'43''W$ RAD
- 15 $N20^{\circ}22'53''W$ 27.77'
- 16 $N87^{\circ}44'54''E$ 40.97'

NOTES:

SEE SHEET 2 FOR EASEMENT NOTES.

SEE SHEET 3 FOR BASIS OF BEARINGS, DATUM STATEMENT, MONUMENT NOTES AND OCS GPS BOUNDARY CONTROL MAP.

SEE SHEET 4 FOR SHEET INDEX MAP.

LOTS A THROUGH BK ARE FOR LANDSCAPING/OPEN SPACE AND ARE NOT SEPARATE BUILDING SITES.

840 16

SHEET 16 OF 20 SHEETS

TRACT NO. 16341

A PORTION OF VESTING
TENTATIVE TRACT NO. 16271

IN THE UNINCORPORATED TERRITORY OF ORANGE COUNTY, CALIFORNIA

JUNE 2002


JAMES F. GILLEN, L.S. 5557

DATE OF SURVEY:
JANUARY 1999

HUITT-ZOLLARS

17 NUMBERED LOTS AND 63 LETTERED LOTS

168.726 ACRES

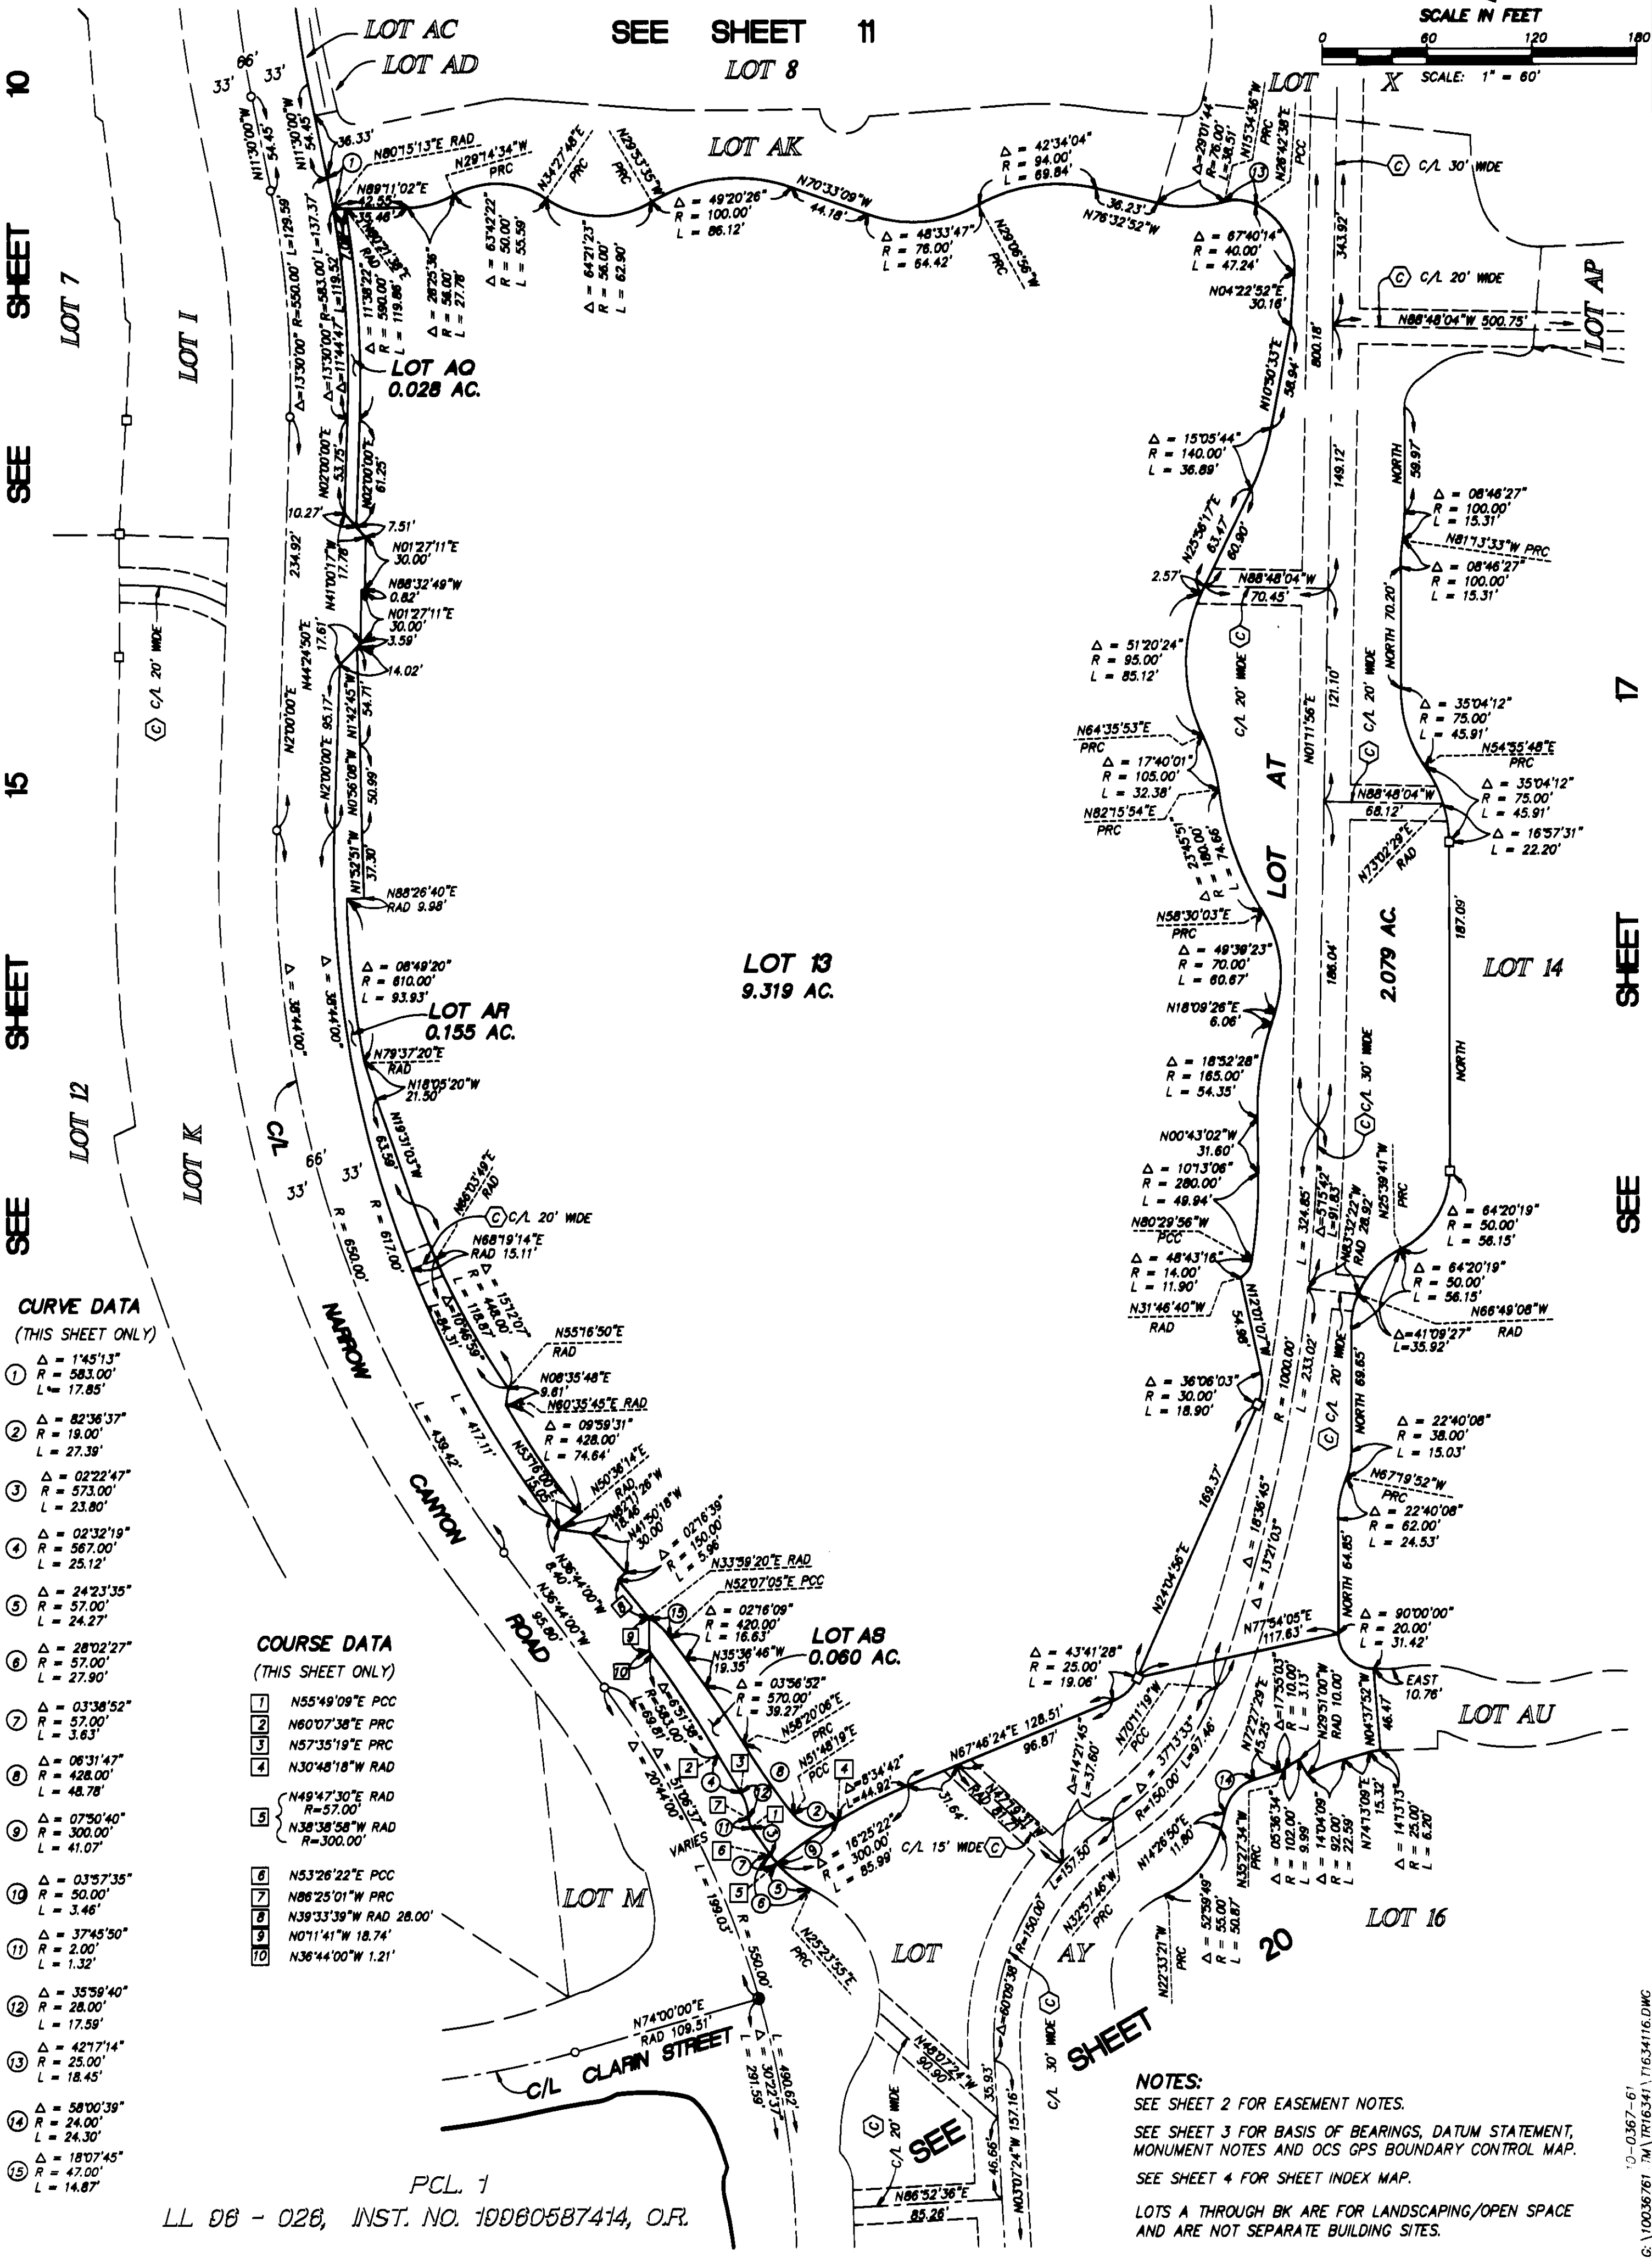


SEE SHEET 11

SEE SHEET 13

SCALE IN FEET

0 60 120 180
SCALE: 1" = 60'

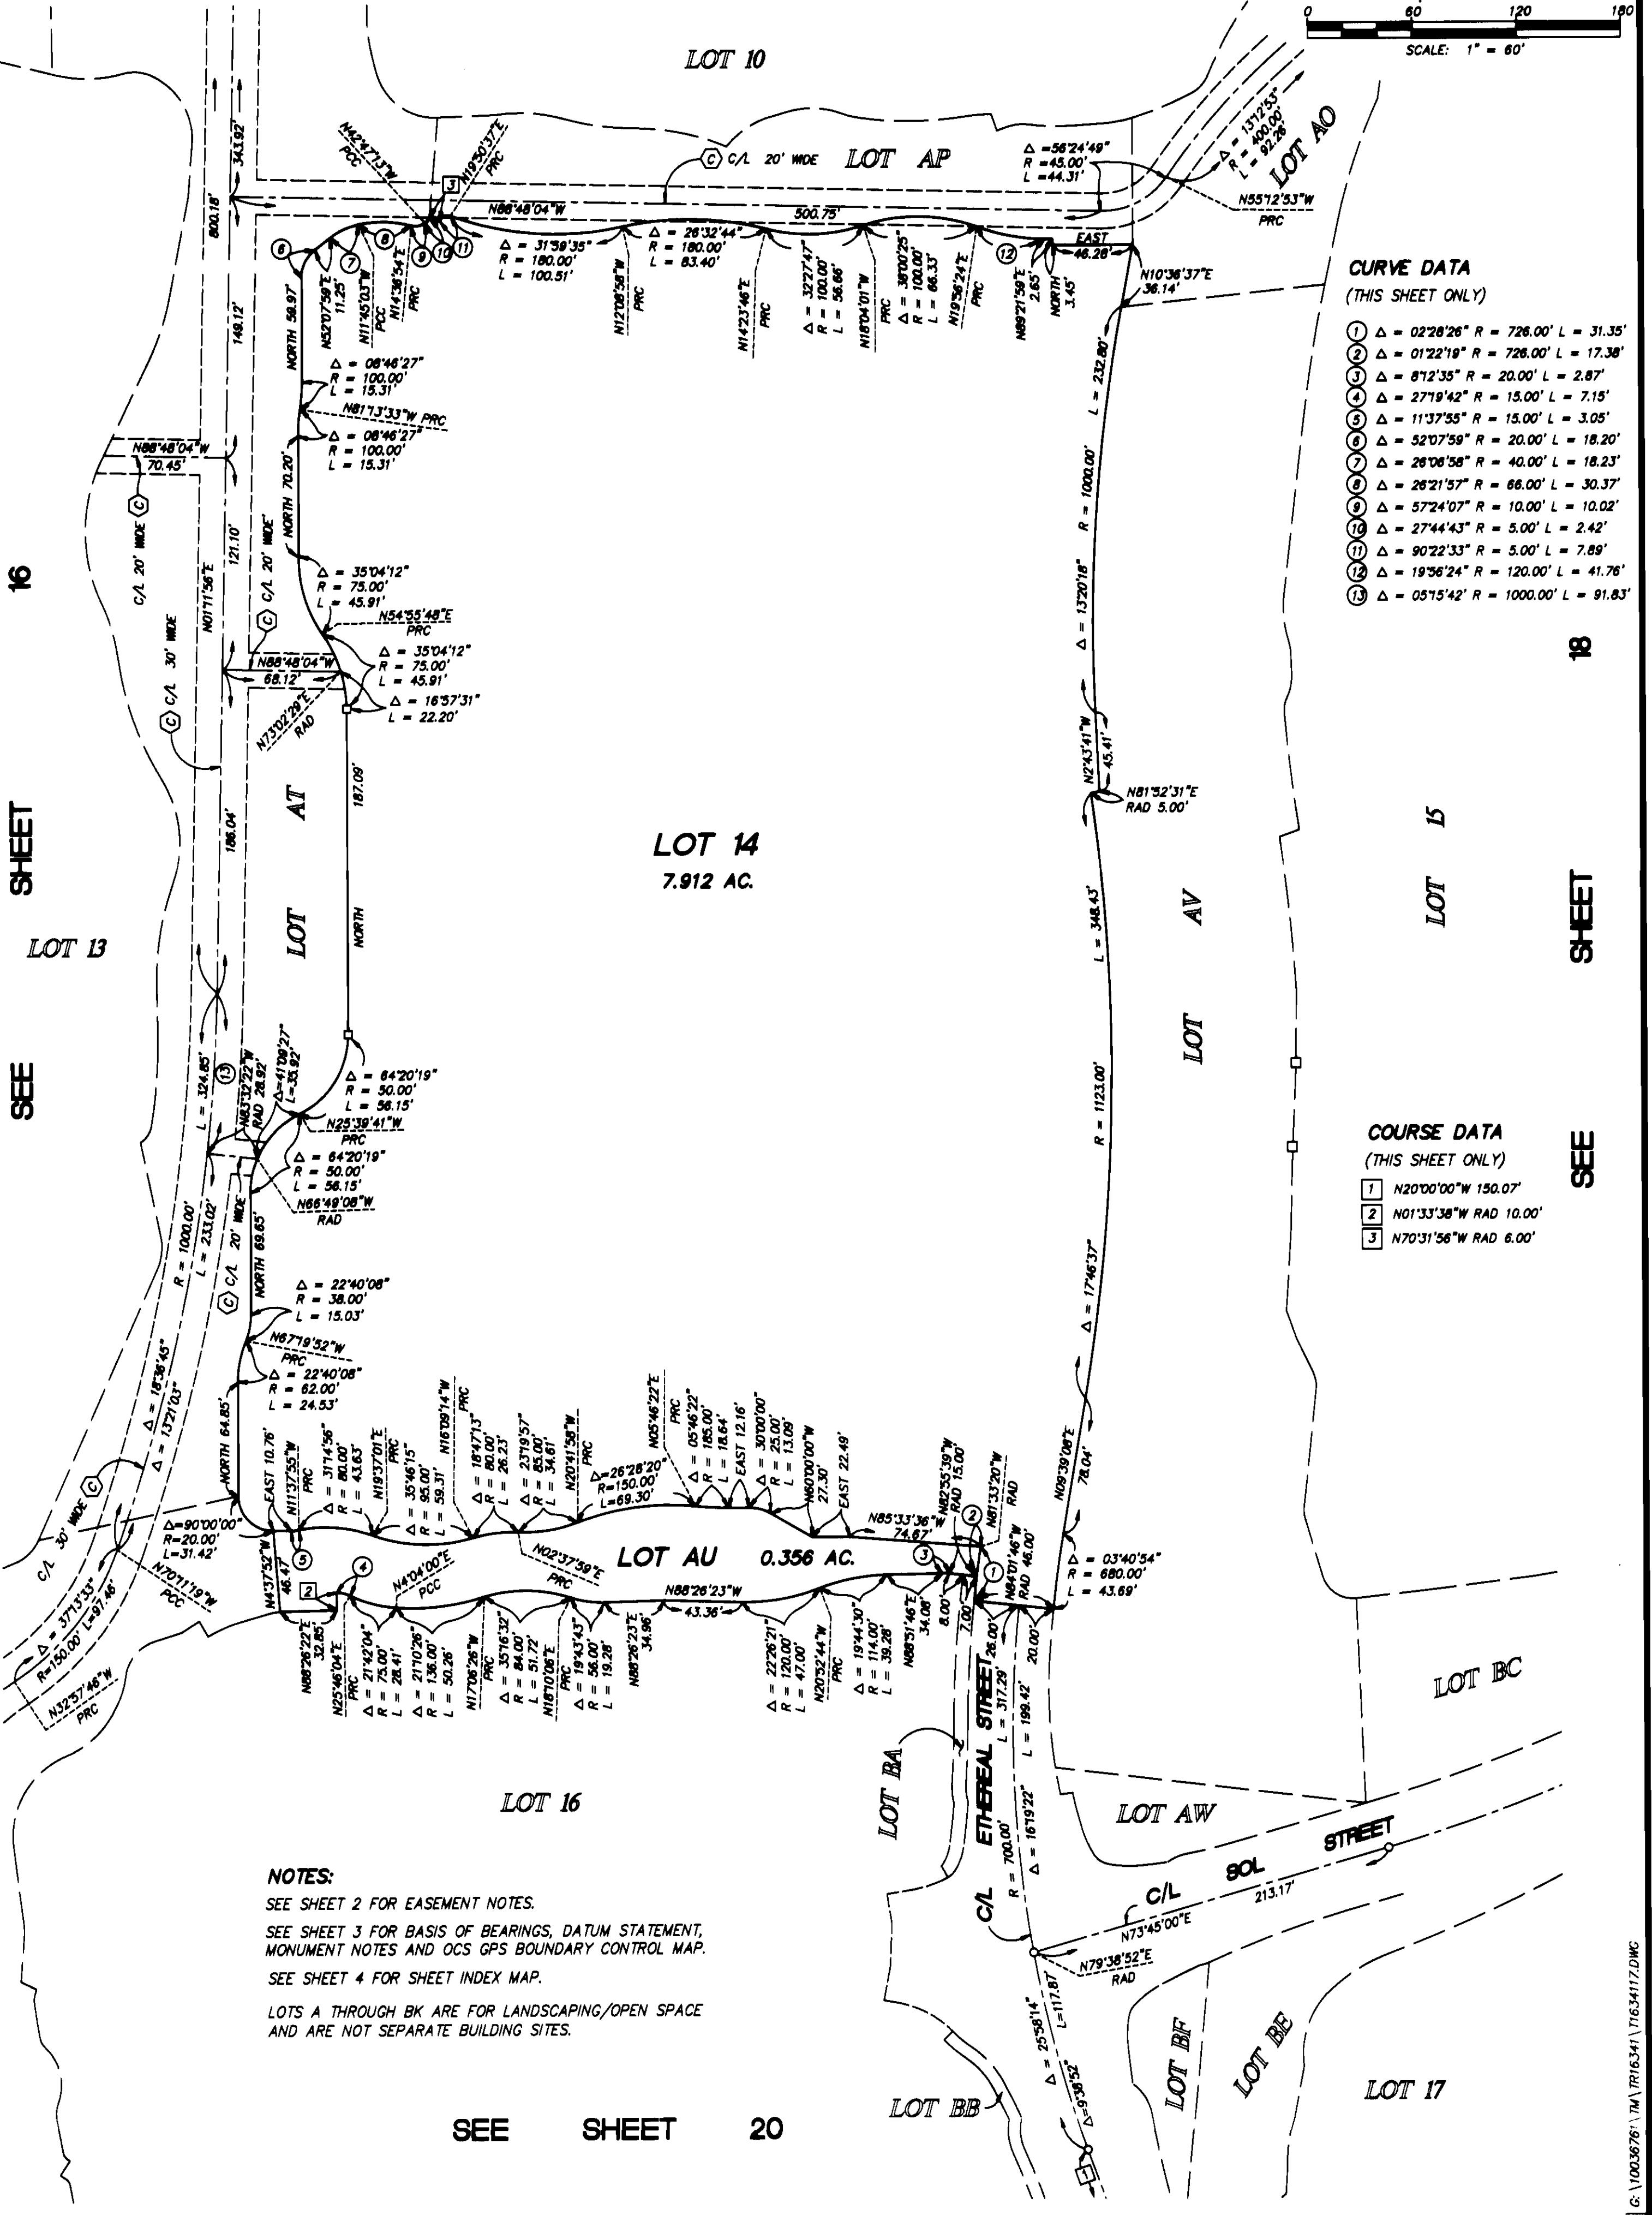

CURVE DATA
(THIS SHEET ONLY)

- 1 Δ = 02°28'26" R = 726.00' L = 31.35'
- 2 Δ = 01°22'19" R = 726.00' L = 17.38'
- 3 Δ = 01°22'35" R = 20.00' L = 2.87'
- 4 Δ = 27°19'42" R = 15.00' L = 7.15'
- 5 Δ = 11°37'55" R = 15.00' L = 3.05'
- 6 Δ = 52°07'59" R = 20.00' L = 18.20'
- 7 Δ = 26°06'58" R = 40.00' L = 18.23'
- 8 Δ = 26°21'57" R = 66.00' L = 30.37'
- 9 Δ = 57°24'07" R = 10.00' L = 10.02'
- 10 Δ = 27°44'43" R = 5.00' L = 2.42'
- 11 Δ = 90°22'33" R = 5.00' L = 7.89'
- 12 Δ = 19°36'24" R = 120.00' L = 41.76'
- 13 Δ = 05°15'42" R = 1000.00' L = 91.83'

COURSE DATA
(THIS SHEET ONLY)

- 1 N20°00'00"W 150.07'
- 2 N01°33'38"W RAD 10.00'
- 3 N70°31'56"W RAD 6.00'

NOTES:

SEE SHEET 2 FOR EASEMENT NOTES.
SEE SHEET 3 FOR BASIS OF BEARINGS, DATUM STATEMENT,
MONUMENT NOTES AND OCS GPS BOUNDARY CONTROL MAP.
SEE SHEET 4 FOR SHEET INDEX MAP.
LOTS A THROUGH BK ARE FOR LANDSCAPING/OPEN SPACE
AND ARE NOT SEPARATE BUILDING SITES.

SEE SHEET 20

840 18

SHEET 18 OF 20 SHEETS

TRACT NO. 16341

IN THE UNINCORPORATED TERRITORY OF ORANGE COUNTY, CALIFORNIA

JUNE 2002

JAMES F. GILLEN, L.S. 5557

A PORTION OF VESTING
TENTATIVE TRACT NO. 16271

DATE OF SURVEY:
JANUARY 1999



HUITT-ZOLLARS

17 NUMBERED LOTS AND 63 LETTERED LOTS

168.726 ACRES

SEE SHEET 3

SEE SHEET 14

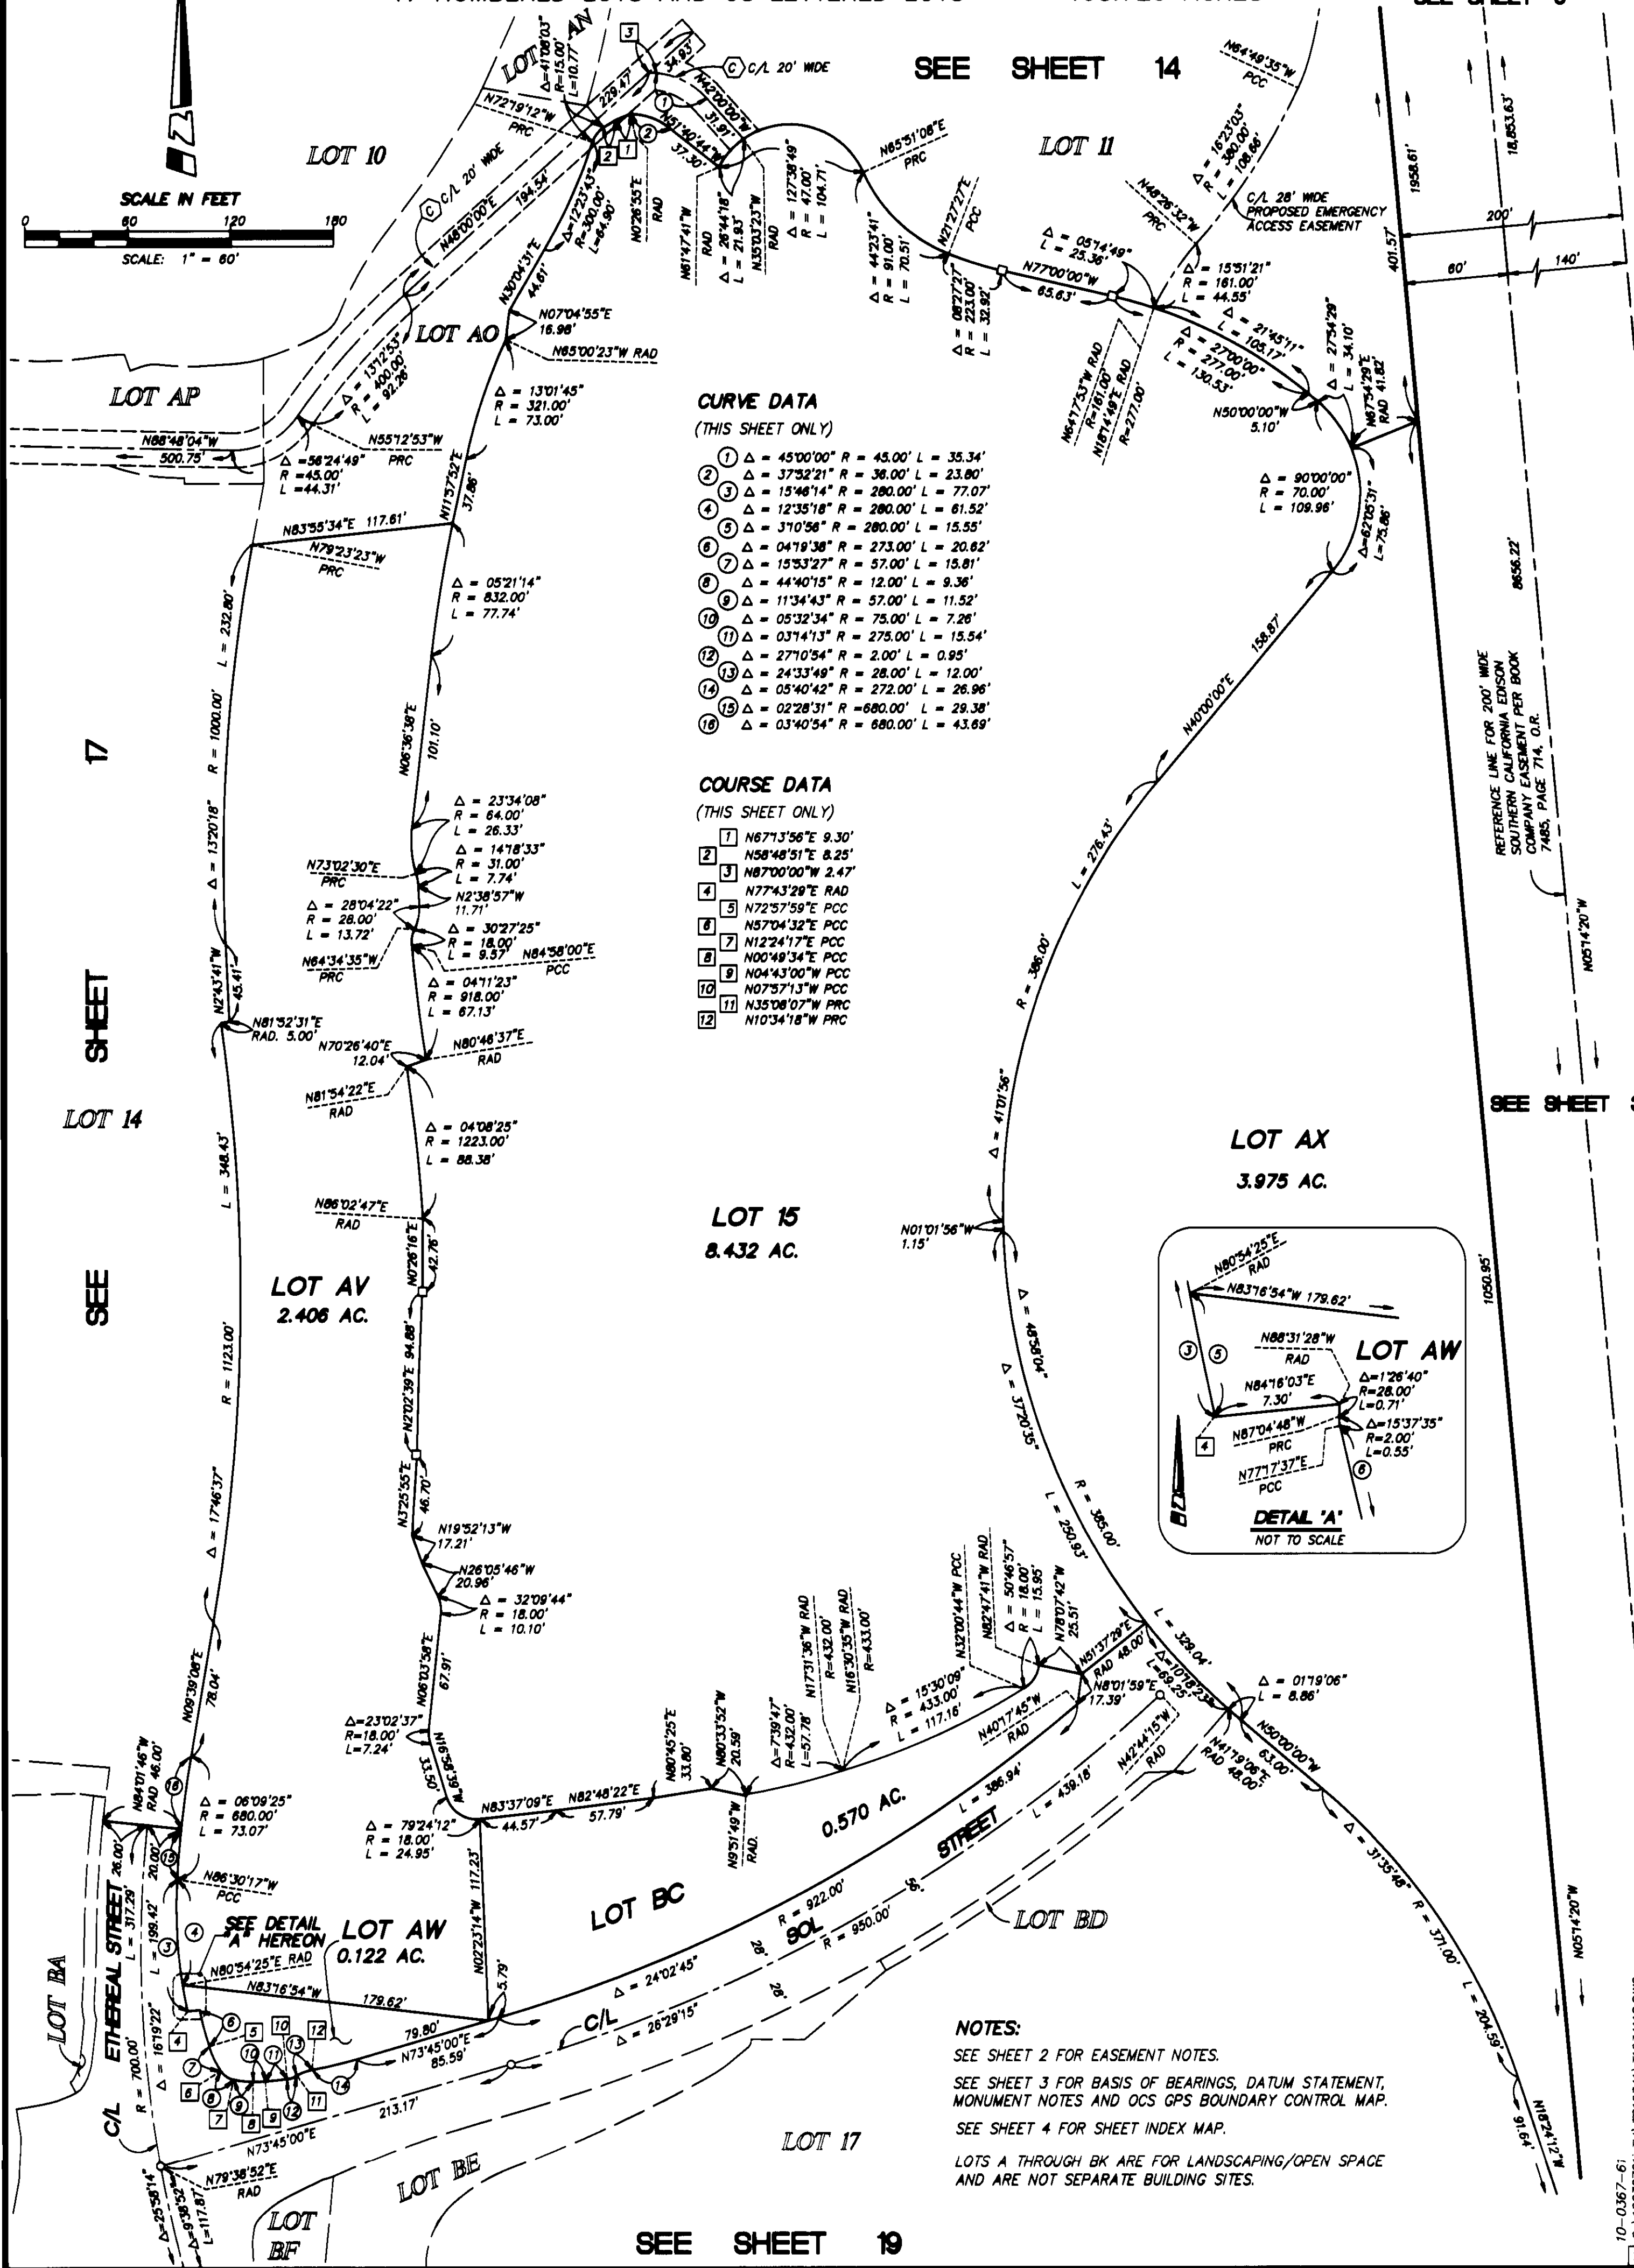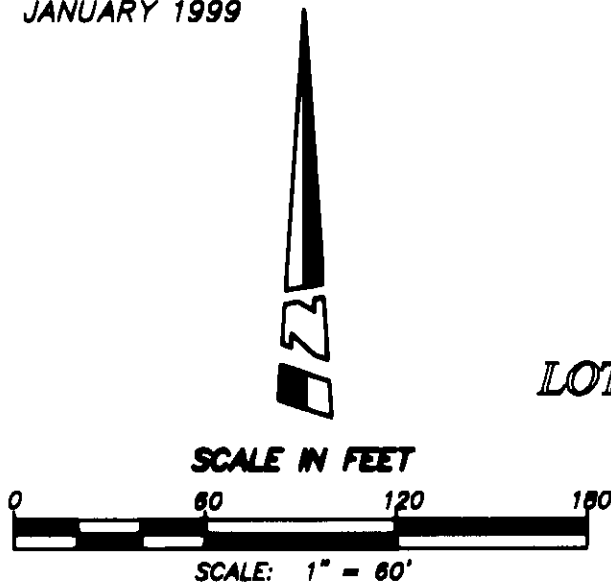


CURVE DATA (THIS SHEET ONLY)

- ① $\Delta = 45^{\circ}00'00''$ R = 45.00' L = 35.34'
- ② $\Delta = 37^{\circ}52'21''$ R = 36.00' L = 23.80'
- ③ $\Delta = 15^{\circ}46'14''$ R = 280.00' L = 77.07'
- ④ $\Delta = 12^{\circ}35'18''$ R = 280.00' L = 61.52'
- ⑤ $\Delta = 37^{\circ}05'58''$ R = 280.00' L = 15.55'
- ⑥ $\Delta = 04^{\circ}19'38''$ R = 273.00' L = 20.62'
- ⑦ $\Delta = 15^{\circ}53'27''$ R = 57.00' L = 15.81'
- ⑧ $\Delta = 44^{\circ}40'15''$ R = 12.00' L = 9.36'
- ⑨ $\Delta = 11^{\circ}34'43''$ R = 57.00' L = 11.52'
- ⑩ $\Delta = 05^{\circ}32'34''$ R = 75.00' L = 7.26'
- ⑪ $\Delta = 03^{\circ}14'13''$ R = 275.00' L = 15.54'
- ⑫ $\Delta = 27^{\circ}10'54''$ R = 2.00' L = 0.95'
- ⑬ $\Delta = 24^{\circ}33'49''$ R = 28.00' L = 12.00'
- ⑭ $\Delta = 05^{\circ}40'42''$ R = 272.00' L = 26.96'
- ⑮ $\Delta = 02^{\circ}28'31''$ R = 680.00' L = 29.38'
- ⑯ $\Delta = 03^{\circ}40'54''$ R = 680.00' L = 43.69'

COURSE DATA (THIS SHEET ONLY)

- ① N67°13'56"E 9.30'
- ② N58°48'51"E 8.25'
- ③ N87°00'00"W 2.47'
- ④ N77°43'29"E RAD
- ⑤ N72°57'59"E PCC
- ⑥ N57°04'32"E PCC
- ⑦ N12°24'17"E PCC
- ⑧ N00°49'34"E PCC
- ⑨ N04°43'00"W PCC
- ⑩ N07°57'13"W PCC
- ⑪ N35°08'07"W PCC
- ⑫ N10°34'18"W PCC

LOT AX
3.975 AC.

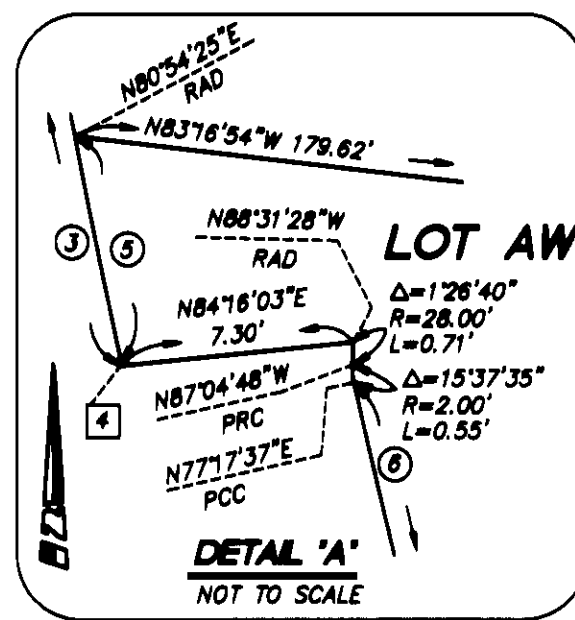

NOTES:

- SEE SHEET 2 FOR EASEMENT NOTES.
- SEE SHEET 3 FOR BASIS OF BEARINGS, DATUM STATEMENT, MONUMENT NOTES AND OCS GPS BOUNDARY CONTROL MAP.
- SEE SHEET 4 FOR SHEET INDEX MAP.
- LOTS A THROUGH BK ARE FOR LANDSCAPING/OPEN SPACE AND ARE NOT SEPARATE BUILDING SITES.

840 18

840 19

SHEET 19 OF 20 SHEETS

TRACT NO. 16341

IN THE UNINCORPORATED TERRITORY OF ORANGE COUNTY, CALIFORNIA

JUNE 2002

JAMES F. GILLEN, L.S. 5557

DATE OF SURVEY:
JANUARY 1999

HUITT-ZOLLARS


17 NUMBERED LOTS AND 63 LETTERED LOTS

168.726 ACRES

SEE SHEET 18



SHEET 20

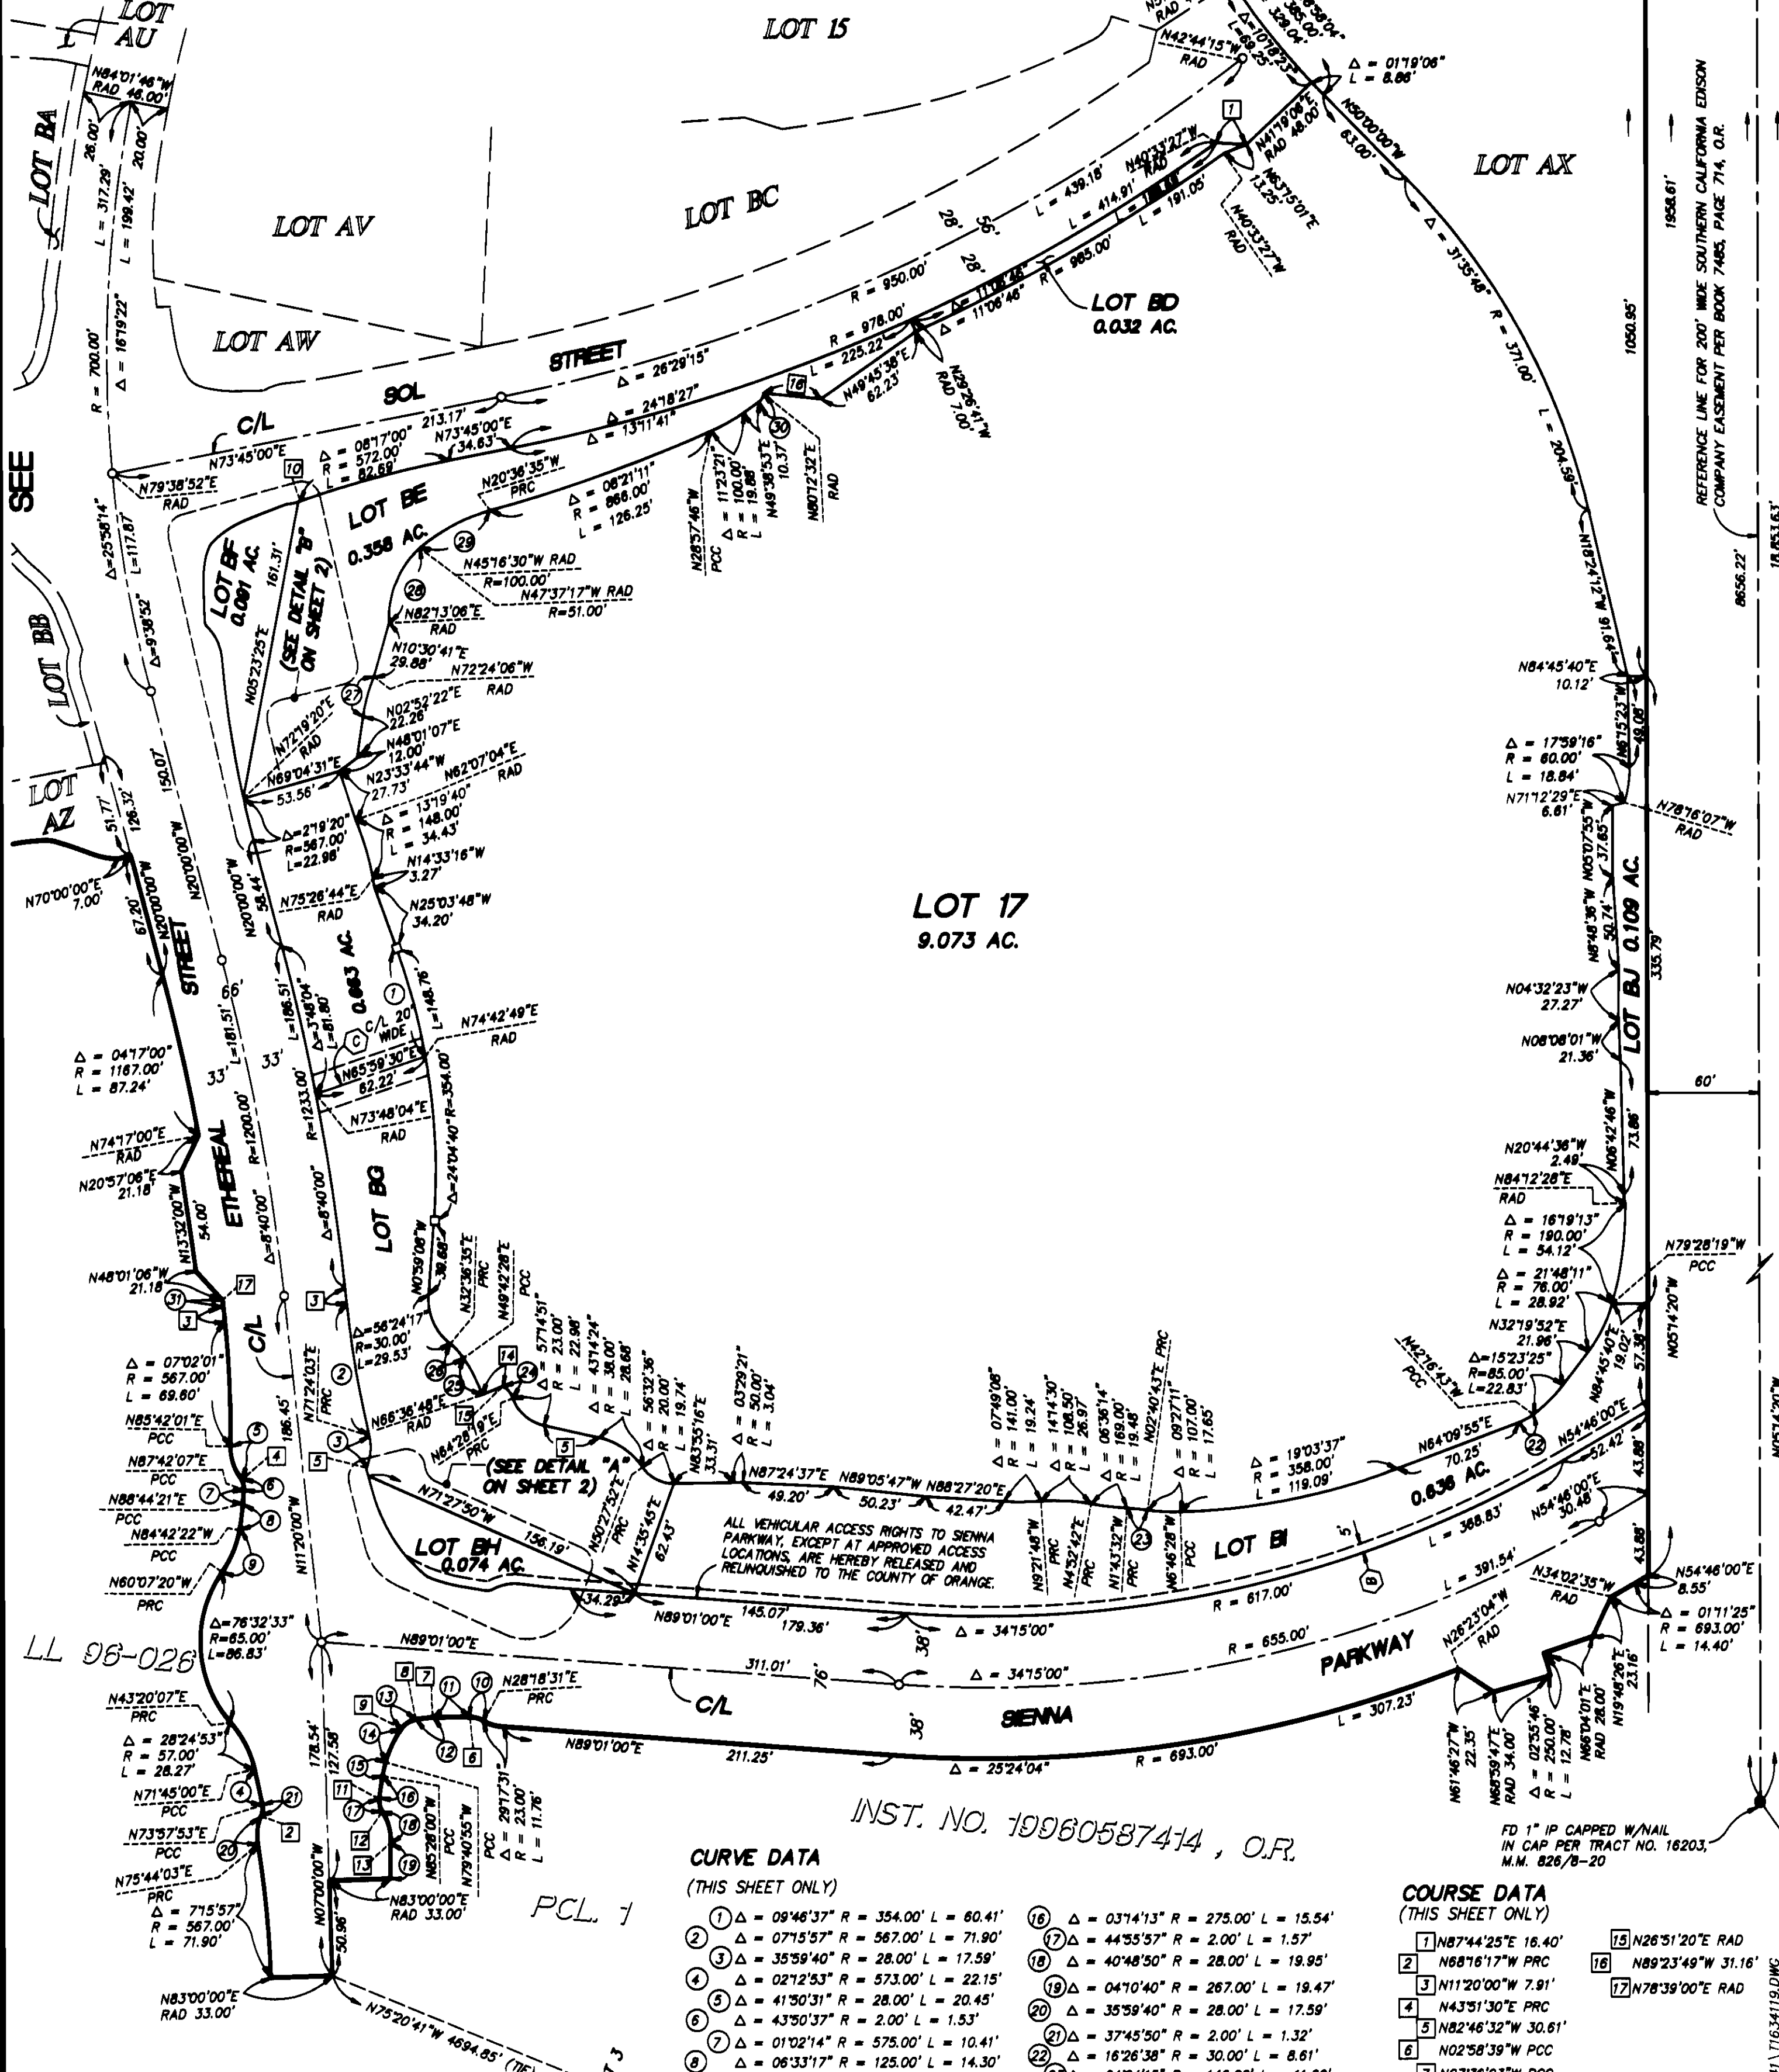

NOTES:
SEE SHEET 2 FOR EASEMENT NOTES.
SEE SHEET 3 FOR BASIS OF BEARINGS, DATUM STATEMENT, MONUMENT NOTES AND OGS GPS BOUNDARY CONTROL MAP.
SEE SHEET 4 FOR SHEET INDEX MAP.
LOTS A THROUGH BK ARE FOR LANDSCAPING/OPEN SPACE AND ARE NOT SEPARATE BUILDING SITES.

CURVE DATA (THIS SHEET ONLY)

- | | |
|---|---|
| 1 Δ = 09°46'37" R = 354.00' L = 60.41' | 16 Δ = 03°14'13" R = 275.00' L = 15.54' |
| 2 Δ = 07°15'57" R = 567.00' L = 71.90' | 17 Δ = 44°55'57" R = 2.00' L = 1.57' |
| 3 Δ = 35°59'40" R = 28.00' L = 17.59' | 18 Δ = 40°48'50" R = 28.00' L = 19.95' |
| 4 Δ = 02°12'53" R = 573.00' L = 22.15' | 19 Δ = 04°10'40" R = 267.00' L = 19.47' |
| 5 Δ = 41°30'31" R = 28.00' L = 20.45' | 20 Δ = 35°59'40" R = 28.00' L = 17.59' |
| 6 Δ = 43°50'37" R = 2.00' L = 1.53' | 21 Δ = 37°45'50" R = 2.00' L = 1.32' |
| 7 Δ = 01°02'14" R = 575.00' L = 10.41' | 22 Δ = 16°26'38" R = 30.00' L = 8.61' |
| 8 Δ = 06°33'17" R = 125.00' L = 14.30' | 23 Δ = 04°24'15" R = 146.00' L = 11.22' |
| 9 Δ = 24°35'02" R = 57.00' L = 24.46' | 24 Δ = 37°36'59" R = 13.00' L = 8.53' |
| 10 Δ = 31°17'10" R = 7.00' L = 3.82' | 25 Δ = 16°34'20" R = 75.00' L = 22.13' |
| 11 Δ = 04°37'24" R = 278.00' L = 22.43' | 26 Δ = 17°05'53" R = 35.00' L = 10.44' |
| 12 Δ = 08°26'11" R = 62.00' L = 9.13' | 27 Δ = 14°43'32" R = 87.00' L = 22.36' |
| 13 Δ = 43°26'04" R = 12.00' L = 9.10' | 28 Δ = 50°08'37" R = 51.00' L = 44.65' |
| 14 Δ = 20°12'37" R = 57.00' L = 20.11' | 29 Δ = 24°38'55" R = 100.00' L = 43.05' |
| 15 Δ = 05°47'05" R = 75.00' L = 7.57' | 30 Δ = 59°26'21" R = 5.00' L = 5.19' |
| | 31 Δ = 00°01'00" R = 1187.00' L = 0.34' |

COURSE DATA (THIS SHEET ONLY)

- | | |
|-----------------------|-----------------------|
| 1 N87°44'25"E 16.40' | 15 N26°51'20"E RAD |
| 2 N88°16'17"W PRC | 16 N89°23'49"W 31.16' |
| 3 N11°20'00"W 7.91' | 17 N78°39'00"E RAD |
| 4 N43°51'30"E PRC | |
| 5 N82°46'32"W 30.61' | |
| 6 N02°58'39"W PCC | |
| 7 N07°36'03"W PCC | |
| 8 N16°02'14"W PCC | |
| 9 N59°28'18"W PCC | |
| 10 N24°32'00"W PRC | |
| 11 N88°42'13"W PCC | |
| 12 N46°21'50"E PRC | |
| 13 N87°10'40"E PRC | |
| 14 N62°16'21"E 12.13' | |

FD 1" IP CAPPED W/NAIL
IN CAP PER TRACT NO. 16203,
M.M. 826/8-20

G:\10036761\16341\1634119.DWG

840 20

SHEET 20 OF 20 SHEETS

TRACT NO. 16341

A PORTION OF VESTING
TENTATIVE TRACT NO. 16271

IN THE UNINCORPORATED TERRITORY OF ORANGE COUNTY, CALIFORNIA

JUNE 2002



JAMES F. GILLEN, L.S. 5557

DATE OF SURVEY:
JANUARY 1999

HUITT-ZOLLARS

17 NUMBERED LOTS AND 63 LETTERED LOTS

168.726 ACRES

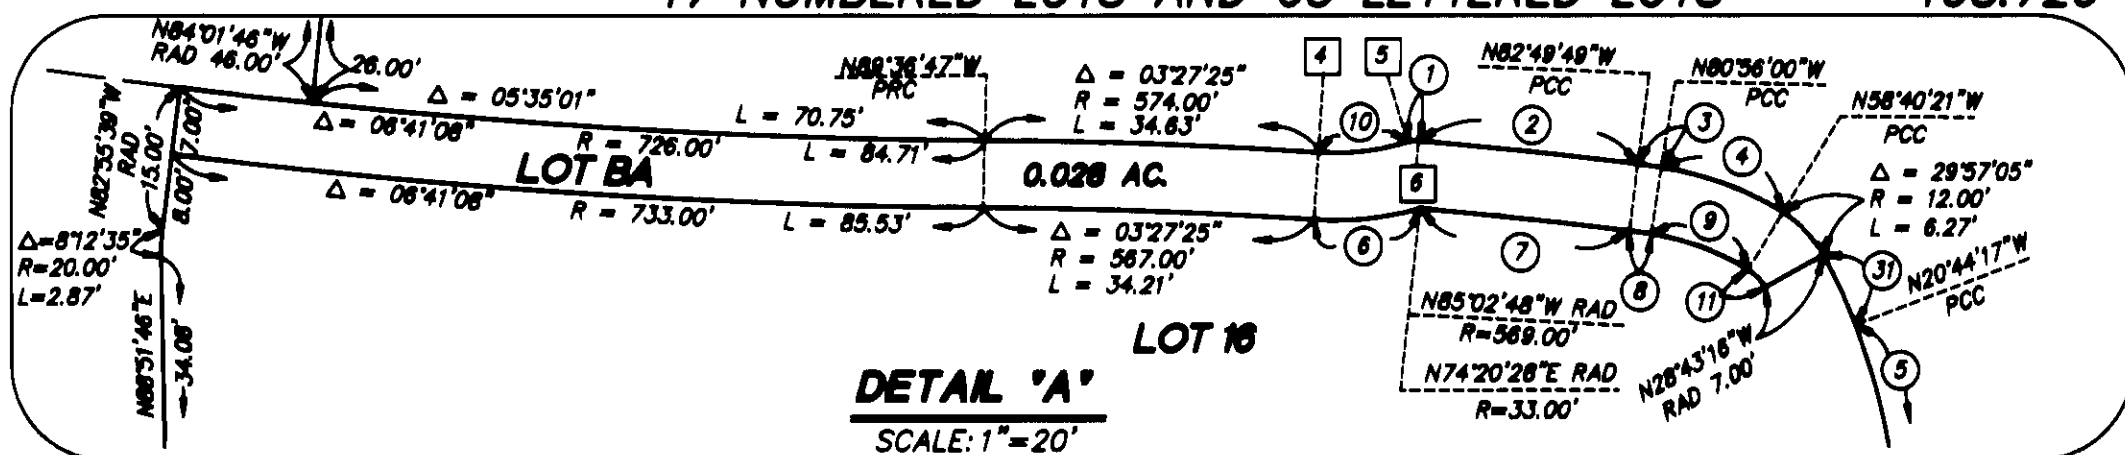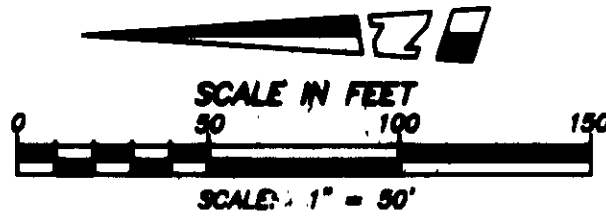

SEE SHEET 19

SEE SHEET 18

SEE SHEET 19

LOT BG

CURVE DATA
(THIS SHEET ONLY)

COURSE DATA
(THIS SHEET ONLY)

- 1 N64°30'09"E PCC
- 2 N77°44'02"W PRC
- 3 N48°01'48"E
RAD (PRC) 7.00'
- 4 N86°09'22"W PRC
- 5 N72°57'06"E PRC
- 6 N85°07'19"W PCC

- 1 Δ = 21°55'35" R = 3.00' L = 1.15'
- 2 Δ = 02°17'30" R = 576.00' L = 23.04'
- 3 Δ = 01°53'49" R = 78.00' L = 2.52'
- 4 Δ = 22°15'39" R = 35.00' L = 13.80'
- 5 Δ = 10°00'11" R = 73.00' L = 12.74'
- 6 Δ = 19°30'10" R = 33.00' L = 11.23'
- 7 Δ = 02°12'59" R = 569.00' L = 22.01'
- 8 Δ = 01°53'49" R = 69.00' L = 2.28'
- 9 Δ = 22°15'39" R = 28.00' L = 10.88'
- 10 Δ = 20°53'32" R = 26.00' L = 9.48'
- 11 Δ = 29°57'05" R = 5.00' L = 2.81'
- 12 Δ = 12°08'48" R = 65.00' L = 13.78'
- 13 Δ = 28°24'53" R = 57.00' L = 28.27'
- 14 Δ = 02°12'14" R = 573.00' L = 22.04'
- 15 Δ = 37°45'49" R = 2.00' L = 1.32'
- 16 Δ = 35°59'39" R = 28.00' L = 17.59'
- 17 Δ = 03°43'41" R = 567.00' L = 36.89'
- 18 Δ = 34°26'27" R = 57.00' L = 34.26'
- 19 Δ = 02°03'02" R = 275.00' L = 9.84'
- 20 Δ = 03°43'41" R = 560.00' L = 36.44'
- 21 Δ = 33°05'32" R = 35.00' L = 20.21'
- 22 Δ = 02°02'18" R = 566.00' L = 20.14'
- 23 Δ = 28°24'53" R = 50.00' L = 24.80'
- 24 Δ = 12°08'48" R = 72.00' L = 15.26'
- 25 Δ = 02°18'23" R = 567.00' L = 22.82'
- 26 Δ = 41°50'31" R = 28.00' L = 20.45'
- 27 Δ = 43°50'37" R = 2.00' L = 1.53'
- 28 Δ = 01°13'32" R = 575.00' L = 12.30'
- 29 Δ = 06°17'37" R = 125.00' L = 13.73'
- 30 Δ = 24°26'40" R = 57.00' L = 24.32'
- 31 Δ = 07°58'59" R = 57.00' L = 7.94'
- 32 Δ = 01°17'35" R = 567.00' L = 12.80'
- 33 Δ = 27°27'48" R = 69.00' L = 33.08'
- 34 Δ = 20°40'12" R = 25.00' L = 9.02'
- 35 Δ = 03°43'36" R = 280.00' L = 18.21'
- 36 Δ = 20°04'36" R = 43.00' L = 15.07'
- 37 Δ = 24°23'35" R = 57.00' L = 24.27'

LOT 16
5.110 AC.

PCL 1
LL 96 - 026

INST. NO. 19960587414, O.R.

NOTES:

- SEE SHEET 2 FOR EASEMENT NOTES.
- SEE SHEET 3 FOR BASIS OF BEARINGS, DATUM STATEMENT, MONUMENT NOTES AND OCS GPS BOUNDARY CONTROL MAP.
- SEE SHEET 4 FOR SHEET INDEX MAP.
- LOTS A THROUGH BK ARE FOR LANDSCAPING/OPEN SPACE AND ARE NOT SEPARATE BUILDING SITES.