

SHEET 1 OF 4 SHEETS  
36 NUMBERED LOTS AND  
LOTS A THROUGH Q INCLUSIVE  
ACREAGE: 9.767 ACRES  
(ALL OF TENTATIVE  
TRACT NO. 16342)

# TRACT NO. 16342

IN UNINCORPORATED TERRITORY OF THE COUNTY OF ORANGE,  
STATE OF CALIFORNIA

BEING A SUBDIVISION OF LOTS 3, 7 AND LETTERED LOT BK OF TRACT NO. 16341, AS  
PER MAP FILED IN BOOK 840, PAGES 1 THROUGH 20, INCLUSIVE, OF MISCELLANEOUS  
MAPS, IN THE OFFICE OF THE COUNTY RECORDER OF SAID COUNTY.

HUNSAKER AND ASSOCIATES IRVINE, INC.  
RORY S. WILLIAMS, L.S. 6654

DATE OF SURVEY: JANUARY, 2003

ACCEPTED AND FILED AT THE  
REQUEST OF

FIRST AMERICAN TITLE INS CO.

DATE: JULY 25, 2003  
TIME: 08:44AM FEE: \$13.00  
INSTRUMENT NO. 200300084502  
BOOK 847 PAGE 36-39 m/c

TOM DALY  
COUNTY CLERK - RECORDER

BY [Signature] DEPUTY

## OWNERSHIP CERTIFICATE:

WE, THE UNDERSIGNED, BEING ALL PARTIES HAVING ANY RECORD TITLE INTEREST IN THE LAND  
COVERED BY THIS MAP, DO HEREBY CONSENT TO THE PREPARATION AND RECORDATION OF SAID  
MAP, AS SHOWN WITHIN THE DISTINCTIVE BORDER LINE.

WE HEREBY DEDICATE TO THE PUBLIC FOR STREET PURPOSES: FALLOW LANE AND FOLIATE WAY.

WE ALSO HEREBY DEDICATE TO THE COUNTY OF ORANGE: THE EASEMENT FOR FUEL  
MODIFICATION ACCESS PURPOSES, AS SHOWN ON THIS MAP.

WE ALSO HEREBY DEDICATE TO THE SANTA MARGARITA WATER DISTRICT THE EASEMENTS FOR  
SEWER, WATER AND ACCESS PURPOSES, AS SHOWN ON THIS TRACT MAP, WHICH EASEMENTS  
SHALL BE SUBJECT TO THE SAME TERMS AND CONDITIONS AS SHOWN IN THAT CERTAIN EASEMENT  
RECORDED OCTOBER 6, 1980, IN BOOK 13776, PAGE 341 OF OFFICIAL RECORDS.

SHEA HOMES LIMITED PARTNERSHIP, A CALIFORNIA LIMITED PARTNERSHIP, OWNER  
OF LOTS 3 AND 7 OF TRACT NO. 16341, M.M. 840/1-20.

BY: [Signature]  
NAME: MARION P. MARCUM  
TITLE: ASSISTANT SECRETARY

BY: [Signature]  
NAME: LINDA C. TONG  
TITLE: ASSISTANT SECRETARY

DMB LADERA, LLC, A DELAWARE LIMITED LIABILITY COMPANY, AS OWNER OF LOT BK  
OF TRACT NO. 16341, M.M. 840/1-20, AND AS BENEFICIARY UNDER DEED OF  
TRUST RECORDED MARCH 28, 2003, AS INSTRUMENT NO. 2003000344006 OF  
OFFICIAL RECORDS, AND HOLDER OF EASEMENTS RESERVED IN THE DEED RECORDED  
MARCH 28, 2003, AS INSTRUMENT NO. 2003000344005 OF OFFICIAL RECORDS..

BY: RANCHO MISSION VIEJO, L.L.C., A DELAWARE LIMITED LIABILITY COMPANY, ITS  
AUTHORIZED AGENT AND MANAGER.

BY: [Signature]  
NAME: DONALD T. STALLIN  
TITLE: DIRECTOR

BY: [Signature]  
NAME: PAUL JOHNSON  
TITLE: V.P. - COMMUNITY DEVELOPMENT

## NOTARY ACKNOWLEDGMENT:

STATE OF CALIFORNIA } SS  
COUNTY OF ORANGE }

ON May 21, 2003 BEFORE ME, Beth A. Hutchinson PERSONALLY  
APPEARED Marion P. Marcum AND Linda C. Tong PERSONALLY  
KNOWN TO ME (OR PROVED TO ME ON THE BASIS OF SATISFACTORY EVIDENCE) TO BE THE PERSON(S)  
WHOSE NAME(S) IS/ARE SUBSCRIBED TO THE WITHIN INSTRUMENT AND ACKNOWLEDGED TO ME THAT  
HE/SHE/they EXECUTED THE SAME IN HIS/HER/their AUTHORIZED CAPACITY(IES), AND THAT BY  
HE/SHE/their SIGNATURE(S) ON THE INSTRUMENT THE PERSON(S), OR ENTITY UPON BEHALF OF  
WHICH THE PERSON(S) ACTED, EXECUTED THE INSTRUMENT.

WITNESS MY HAND:

SIGNATURE [Signature]  
NOTARY PUBLIC IN AND FOR SAID STATE  
Beth A. Hutchinson  
(NAME PRINTED)

MY PRINCIPAL PLACE OF BUSINESS IS  
IN Orange COUNTY.  
MY COMMISSION EXPIRES: 5-8-05

STATE OF CALIFORNIA } SS  
COUNTY OF ORANGE }

ON May 23, 2003 BEFORE ME, Tina T. Baker, Notary Public PERSONALLY  
APPEARED Donna T. Stahl AND Paul Stahl PERSONALLY  
KNOWN TO ME (OR PROVED TO ME ON THE BASIS OF SATISFACTORY EVIDENCE) TO BE THE PERSON(S)  
WHOSE NAME(S) IS/ARE SUBSCRIBED TO THE WITHIN INSTRUMENT AND ACKNOWLEDGED TO ME THAT  
HE/SHE/they EXECUTED THE SAME IN HIS/HER/their AUTHORIZED CAPACITY(IES), AND THAT BY  
HE/SHE/their SIGNATURE(S) ON THE INSTRUMENT THE PERSON(S), OR ENTITY UPON BEHALF OF  
WHICH THE PERSON(S) ACTED, EXECUTED THE INSTRUMENT.

WITNESS MY HAND:

SIGNATURE [Signature]  
NOTARY PUBLIC IN AND FOR SAID STATE  
Tina T. Baker  
(NAME PRINTED)

MY PRINCIPAL PLACE OF BUSINESS IS  
IN Orange COUNTY.  
MY COMMISSION EXPIRES: 8/29/04

## AUTOMATIC FIRE SPRINKLER NOTE:

ALL COMMERCIAL STRUCTURES GREATER THAN 6,000 SQUARE FEET, ALL MULTIFAMILY  
RESIDENTIAL STRUCTURES, ALL SINGLE-FAMILY STRUCTURES EXCEEDING 5,500 SQUARE FEET,  
AND ALL STRUCTURES EXCEEDING FIRE DEPARTMENT ACCESS REQUIREMENTS SHALL BE  
PROTECTED BY AN AUTOMATIC FIRE SPRINKLER SYSTEM.

## SPECIAL FIRE PROTECTION NOTE:

SUBJECT PROPERTY IS IN A SPECIAL FIRE PROTECTION AREA AND MUST MEET ALL  
REQUIREMENTS FOR DEVELOPMENT WITHIN THE AREA.

## HIGH FIRE HAZARD AREA NOTE:

THE LOTS SHOWN ON THIS MAP ARE IN A HIGH FIRE HAZARD AREA DUE TO WILDLAND  
EXPOSURE.

## SURVEYOR'S STATEMENT:

THIS MAP WAS PREPARED BY ME OR UNDER MY DIRECTION AND IS BASED UPON A FIELD SURVEY  
IN CONFORMANCE WITH THE REQUIREMENTS OF THE SUBDIVISION MAP ACT AND LOCAL ORDINANCE  
AT THE REQUEST OF DMB LADERA, L.L.C., IN JANUARY, 2003. I HEREBY STATE THAT ALL  
MONUMENTS ARE OF THE CHARACTER AND OCCUPY THE POSITIONS INDICATED, OR THAT THEY  
WILL BE SET IN SUCH POSITIONS; AND THAT SAID MONUMENTS ARE SUFFICIENT TO ENABLE THE  
SURVEY TO BE RETRACED. I HEREBY STATE THAT THIS FINAL MAP SUBSTANTIALLY CONFORMS TO  
THE CONDITIONALLY APPROVED TENTATIVE MAP.

[Signature] 5/16/03  
RORY S. WILLIAMS, L.S. 6654 DATE  
LICENSE EXPIRES: 12/31/03



## COUNTY SURVEYOR'S STATEMENT

I HEREBY STATE THAT I HAVE EXAMINED THIS MAP AND HAVE FOUND IT TO BE SUBSTANTIALLY  
IN CONFORMANCE WITH THE TENTATIVE MAP AS FILED WITH, AMENDED AND APPROVED BY THE  
ORANGE COUNTY SUBDIVISION COMMITTEE; THAT ALL PROVISIONS OF THE SUBDIVISION MAP ACT  
AND COUNTY SUBDIVISION REGULATIONS HAVE BEEN COMPLIED WITH AND I AM SATISFIED SAID  
MAP IS TECHNICALLY CORRECT.

DATED THIS 30TH DAY OF JUNE, 2003.

[Signature]  
JOHN CANAS, COUNTY SURVEYOR  
LS 4408, EXPIRATION DATE: 9-30-05 BY: MICHAEL K. SULLIVAN, DEPUTY  
LS 6254 EXPIRES 6/30/06



## COUNTY TREASURER-TAX COLLECTOR'S CERTIFICATE:

STATE OF CALIFORNIA } SS  
COUNTY OF ORANGE }

I HEREBY CERTIFY THAT ACCORDING TO THE RECORDS OF MY OFFICE THERE ARE NO LIENS  
AGAINST THE LAND COVERED BY THIS MAP OR ANY PART THEREOF FOR UNPAID STATE,  
COUNTY, MUNICIPAL OR LOCAL TAXES OR SPECIAL ASSESSMENTS COLLECTED AS TAXES,  
EXCEPT TAXES OR SPECIAL ASSESSMENTS COLLECTED AS TAXES NOT YET PAYABLE.

AND DO CERTIFY TO THE RECORDER OF ORANGE COUNTY THAT THE PROVISIONS OF  
THE SUBDIVISION MAP ACT HAVE BEEN COMPLIED WITH REGARDING DEPOSITS TO SECURE  
PAYMENT OF TAXES OR SPECIAL ASSESSMENTS COLLECTED AS TAXES ON THE LAND  
COVERED BY THIS MAP.

DATED THIS 4 DAY OF June, 2003.

[Signature]  
JOHN M.W. MOORLACH COUNTY TREASURER-TAX COLLECTOR BY: [Signature] DEPUTY TREASURER-TAX COLLECTOR

## CLERK OF THE BOARD OF SUPERVISORS' CERTIFICATE:

STATE OF CALIFORNIA } SS  
COUNTY OF ORANGE }

I HEREBY CERTIFY THAT THIS MAP WAS PRESENTED FOR APPROVAL TO THE BOARD OF  
SUPERVISORS OF THE COUNTY OF ORANGE AT REGULAR MEETING THEREOF HELD ON  
THE 22nd DAY OF July, 2003, AND THAT THEREUPON SAID  
BOARD DID, BY AN ORDER DULY PASSED AND ENTERED, APPROVE SAID MAP.

AND DID ACCEPT ON BEHALF OF THE PUBLIC, SUBJECT TO IMPROVEMENTS, THE  
DEDICATION FOR STREET PURPOSES OF: FALLOW LANE AND FOLIATE WAY.

AND DID ALSO ACCEPT, ON BEHALF OF THE COUNTY OF ORANGE: THE EASEMENT FOR  
FUEL MODIFICATION ACCESS PURPOSES, AS DEDICATED.

AND DID ALSO APPROVE SUBJECT MAP PURSUANT TO THE PROVISIONS OF SECTION  
66436 (a)(3)(A) OF THE SUBDIVISION MAP ACT.

DATED THIS 22nd DAY OF July, 2003.

[Signature]  
CLERK OF THE BOARD OF SUPERVISORS  
DARLENE J. BLOOM



## CERTIFICATE OF ACCEPTANCE - SANTA MARGARITA WATER DISTRICT

THE UNDERSIGNED, BEING THE DULY APPOINTED AGENT OF THE SANTA MARGARITA WATER  
DISTRICT, A PUBLIC CORPORATION IN ORANGE COUNTY, CALIFORNIA, PURSUANT TO ITS  
RESOLUTION NO. 88-10-2, DOES HEREBY ACCEPT ON BEHALF OF SAID DISTRICT, THE EASEMENTS  
FOR SEWER, WATER AND ACCESS PURPOSES AS DEDICATED AND SHOWN ON THIS TRACT MAP, BY  
AND BETWEEN THE SANTA MARGARITA WATER DISTRICT AND DMB LADERA, L.L.C., A DELAWARE  
LIMITED LIABILITY COMPANY, AND DOES HEREBY CERTIFY THAT THE GRANTEE CONSENTS TO THE  
RECORDATION OF SAID TRACT MAP.

[Signature]  
DANIEL R. FERONS, CHIEF ENGINEER  
SANTA MARGARITA WATER DISTRICT

## NOTARY ACKNOWLEDGMENT - SANTA MARGARITA WATER DISTRICT

STATE OF CALIFORNIA } SS  
COUNTY OF ORANGE }

ON June 2, 2003 BEFORE ME, Andrea M. Evans, Notary Public PERSONALLY  
APPEARED DANIEL R. FERONS, PERSONALLY KNOWN TO ME (OR PROVED TO ME ON THE BASIS  
OF SATISFACTORY EVIDENCE) TO BE THE PERSON WHOSE NAME IS SUBSCRIBED TO THE WITHIN  
INSTRUMENT AND ACKNOWLEDGED TO ME THAT HE EXECUTED THE SAME IN HIS AUTHORIZED  
CAPACITY, AND THAT BY HIS SIGNATURE ON THE INSTRUMENT THE PERSON, OR ENTITY UPON  
BEHALF OF WHICH THE PERSON ACTED, EXECUTED THE INSTRUMENT.

WITNESS MY HAND:

SIGNATURE [Signature]  
NOTARY PUBLIC IN AND FOR SAID STATE  
ANDREA M. EVANS  
(NAME PRINTED)

MY PRINCIPAL PLACE OF BUSINESS IS  
IN Orange COUNTY.  
MY COMMISSION EXPIRES: April 8, 2004

## SIGNATURE OMISSIONS:

PURSUANT TO THE PROVISIONS OF SECTION 66436 (a)(3)(A) AND (C) OF THE SUBDIVISION MAP  
ACT, THE FOLLOWING SIGNATURES HAVE BEEN OMITTED:

LADERA DEVELOPMENT COMPANY, L.L.C., HOLDER OF OIL, GAS AND MINERAL RIGHTS RECORDED  
DECEMBER 10, 1996, AS INSTRUMENT NO. 19960624029 OF OFFICIAL RECORDS.

847 36

847 37

SHEET 2 OF 4 SHEETS  
SCALE: 1" = 100'  
36 NUMBERED LOTS AND  
LOTS A THROUGH Q, INCLUSIVE  
ACREAGE: 9.767 ACRES  
(ALL OF TENTATIVE  
TRACT NO. 16342)

# TRACT NO. 16342

IN UNINCORPORATED TERRITORY OF THE COUNTY OF ORANGE,  
STATE OF CALIFORNIA

HUNSAKER AND ASSOCIATES IRVINE, INC.

## SHEET INDEX AND GPS CONTROL MAP

3 INDICATES SHEET NUMBER

### BASIS OF BEARINGS:

THE BEARINGS SHOWN HEREON ARE BASED ON THE BEARING BETWEEN  
O.C.S. HORIZONTAL CONTROL STATION GPS NO. 1417 AND STATION  
GPS NO. 1448 BEING N10°48'13"E PER RECORDS ON FILE IN THE  
OFFICE OF THE ORANGE COUNTY SURVEYOR.

### DATUM STATEMENT:

COORDINATES SHOWN ARE BASED ON THE CALIFORNIA COORDINATE SYSTEM (CCS83), ZONE  
VI, 1983 NAD, (1991.35 EPOCH OCS GPS ADJUSTMENT). ALL DISTANCES SHOWN ARE GROUND,  
UNLESS OTHERWISE NOTED. TO OBTAIN GRID DISTANCE, MULTIPLY GROUND DISTANCE BY  
0.999948295. THIS COMBINATION FACTOR IS PROJECT SPECIFIC.

### NOTES:

LOTS A THROUGH G, INCLUSIVE, ARE FOR LANDSCAPE/OPEN SPACE PURPOSES, AND ARE NOT  
SEPARATE BUILDING SITES.

R1 - INDICATES RECORD DATA PER TRACT NO. 16341, M.M. 840/1-20.

### EASEMENT NOTES:


- (A) INDICATES AN EASEMENT FOR STORM DRAIN PURPOSES  
DEDICATED TO THE COUNTY OF ORANGE PER TRACT NO. 16341,  
M.M. 840/1-20.
- (B) INDICATES AN EASEMENT FOR SEWER, WATER AND ACCESS  
PURPOSES DEDICATED HEREON TO THE SANTA MARGARITA WATER  
DISTRICT.
- (C) INDICATES AN EASEMENT FOR FUEL MODIFICATION ACCESS  
PURPOSES DEDICATED HEREON TO THE COUNTY OF ORANGE.

### MONUMENT NOTES:

- 2" I.P. TAGGED L.S. 6654 OR LEAD, TACK & TAG L.S. 6654 OR NAIL & TAG L.S. 6654 OR 8"  
S&W STAMPED L.S. 6654 TO BE SET AT ALL TRACT BOUNDARY CORNERS WITHIN 90 DAYS  
AFTER ACCEPTANCE OF IMPROVEMENTS, UNLESS OTHERWISE NOTED.
- 1" I.P. TAGGED L.S. 6654 OR LEAD, TACK & TAG L.S. 6654 OR NAIL & TAG L.S. 6654 OR 8"  
S&W STAMPED L.S. 6654 TO BE SET AT ALL LOT CORNERS, EXCEPT LOT CORNERS THAT  
ARE THE INTERSECTION OF SIDE LOT LINES WITH STREET RIGHT OF WAY, WITHIN 90 DAYS  
AFTER ACCEPTANCE OF IMPROVEMENTS, UNLESS OTHERWISE NOTED.
- 8" S&W STAMPED L.S. 6654 OR LEAD, TACK & TAG L.S. 6654 OR 1" I.P. TAGGED L.S. 6654  
TO BE SET AT ALL STREET CENTERLINE POINTS OF CONTROL, WITHIN 90 DAYS AFTER  
ACCEPTANCE OF IMPROVEMENTS, UNLESS OTHERWISE NOTED.

LEAD, TACK & TAG L.S. 6654 TO BE SET IN TOP OF CURB AT AN OFFSET OF 0.25' ALONG  
FRONT SIDE LOT LINES PRODUCED, IN LIEU OF AT FRONT LOT CORNERS, WITHIN 90 DAYS  
AFTER ACCEPTANCE OF IMPROVEMENTS, UNLESS OTHERWISE NOTED. FOR ALL SIDE LOT LINES  
NON-RADIAL OR NON-PERPENDICULAR TO STREET RIGHT OF WAY, OR NOT AT AN OFFSET  
OF 0.25' BEARING AND DISTANCE OF PRODUCTION IS AS NOTED HEREON.

- INDICATES LOCATION OF MONUMENT SET, AS NOTED.
- INDICATES NOTHING TO BE SET.
- ▲ INDICATES FOUND ORANGE COUNTY SURVEYOR GPS CONTROL MONUMENT AS NOTED.
- P# INDICATES BEARING AND DISTANCE OF LOT LINE PRODUCTION FROM LOT CORNER TO  
MONUMENT.
- 1 INDICATES LOCATION OF 1" I.P. TAGGED "P.L.S. 5557" OR SPIKE & WASHER STAMPED  
"P.L.S. 5557" OR LEAD, TACK & TAG "P.L.S. 5557" TO BE SET PER TRACT NO. 16341,  
M.M. 840/1-20.
- 2 INDICATES LOCATION OF 2" I.P. TAGGED "P.L.S. 5557" OR SPIKE & WASHER STAMPED  
"P.L.S. 5557" OR LEAD, TACK & TAG "P.L.S. 5557" TO BE SET PER TRACT NO. 16341,  
M.M. 840/1-20.
- 3 INDICATES SET 2" I.P. TAGGED L.S. 6654 PRIOR TO MAP RECORDATION.
- 4 INDICATES LOCATION OF OCS WELL MONUMENT WITH A 2" BRASS DISK STAMPED  
"P.L.S. 5557" TO BE SET PER TRACT NO. 16341, M.M. 840/1-20.

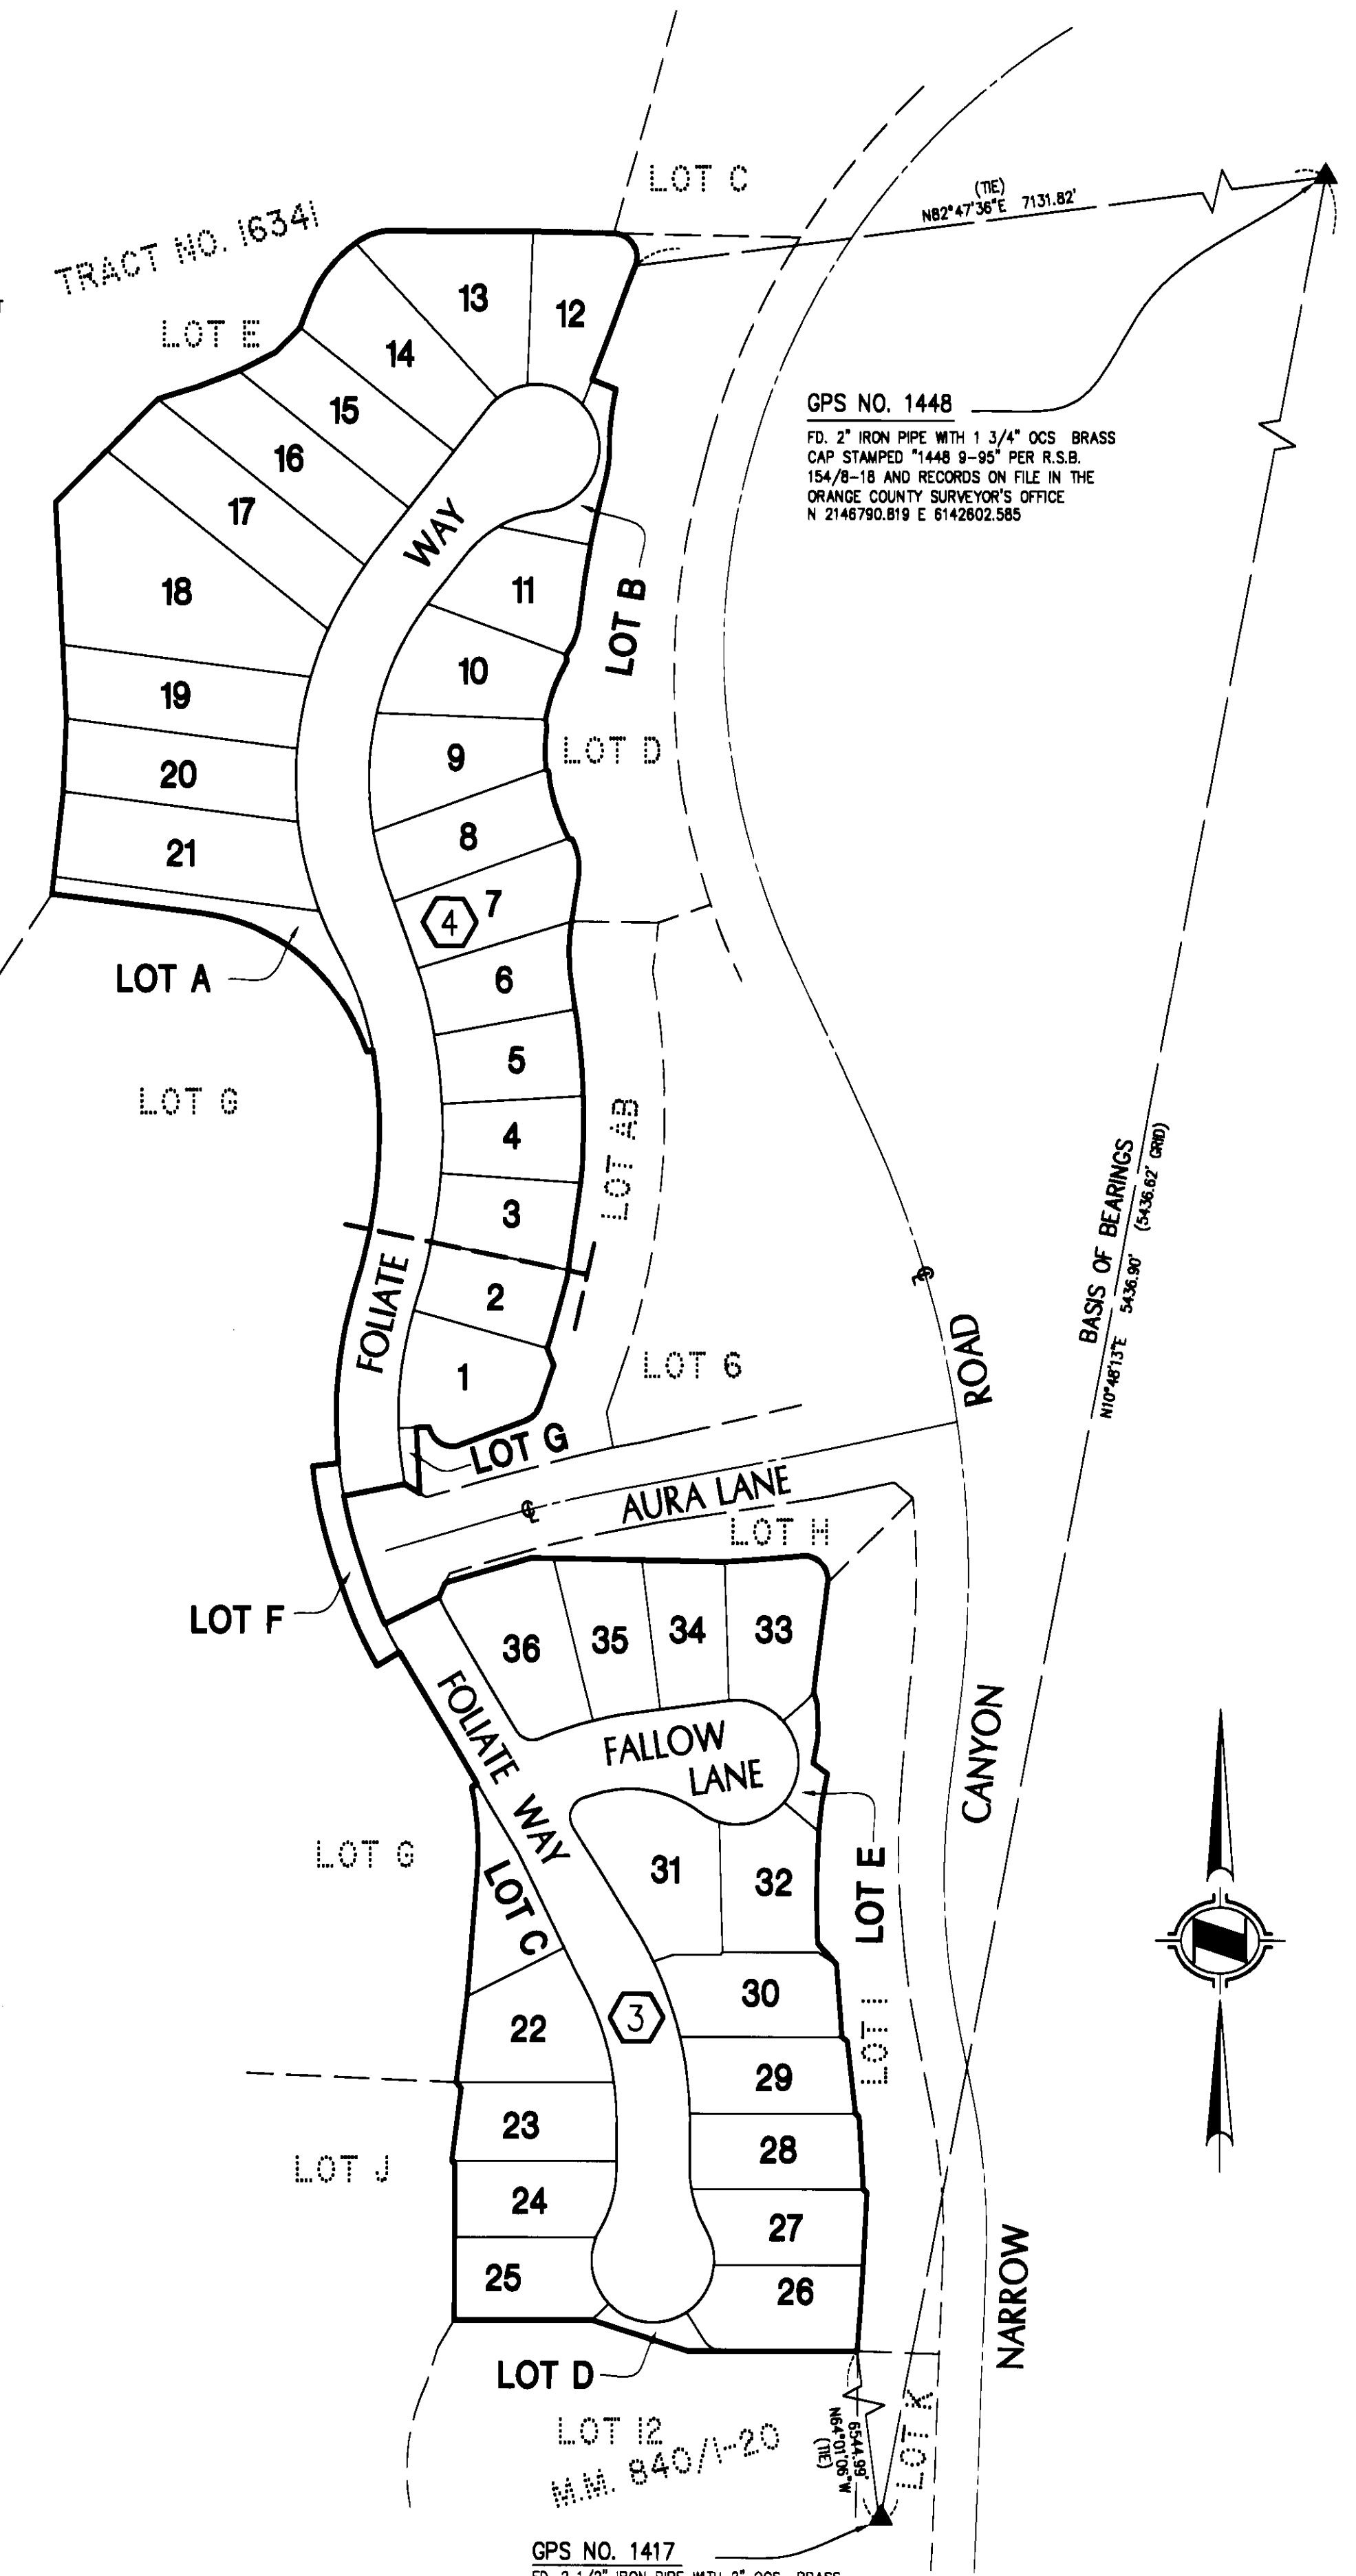

GPS NO. 1417  
FD. 2 1/2" IRON PIPE WITH 2" OCS BRASS  
CAP STAMPED "GPS 1417 9-95" PER R.S.B.  
154/8-18 AND RECORDS ON FILE IN THE  
ORANGE COUNTY SURVEYOR'S OFFICE.  
N 2141450.558 E 8141583.535

847 37




SHEET 3 OF 4 SHEETS  
SCALE: 1" = 40'  
36 NUMBERED LOTS AND  
LOTS A THROUGH Q, INCLUSIVE  
ACREAGE: 9.767 ACRES  
(ALL OF TENTATIVE  
TRACT NO. 16342)

# TRACT NO. 16342

IN UNINCORPORATED TERRITORY OF THE COUNTY OF ORANGE,  
STATE OF CALIFORNIA

HUNSAKER AND ASSOCIATES IRVINE, INC.

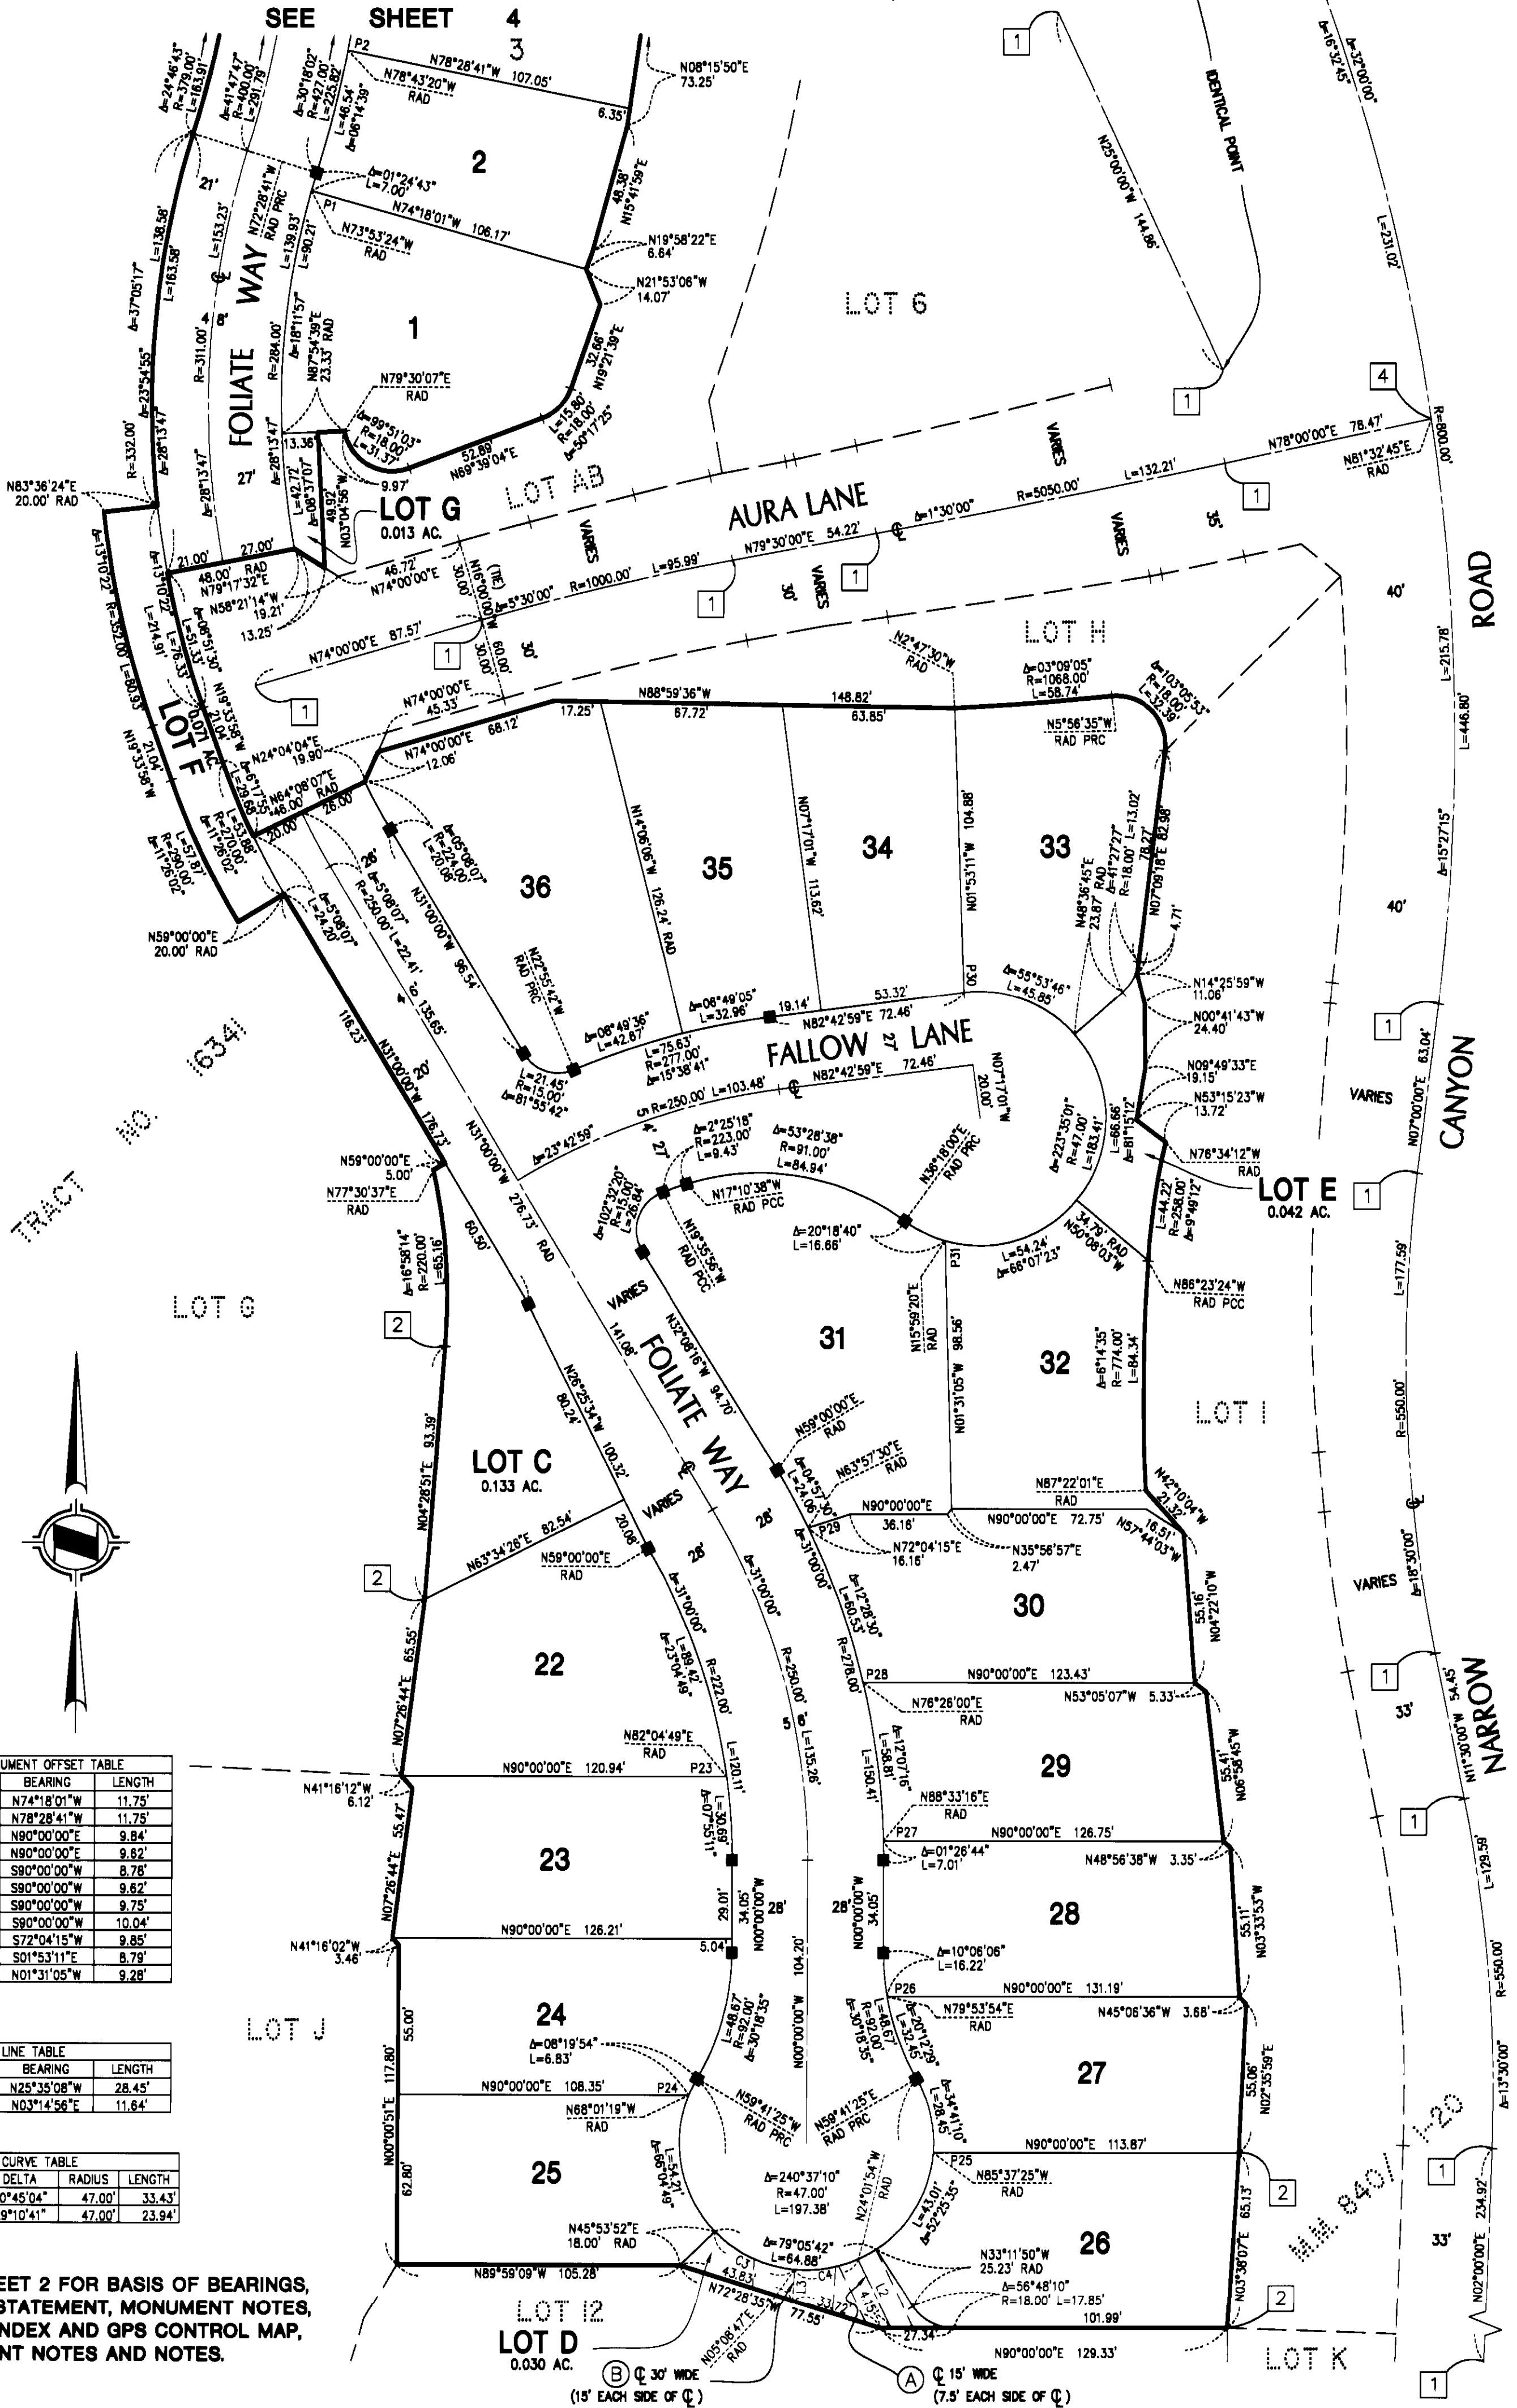

| MONUMENT OFFSET TABLE |             |        |
|-----------------------|-------------|--------|
| LINE                  | BEARING     | LENGTH |
| P1                    | N74°18'01"W | 11.75' |
| P2                    | N78°28'41"W | 11.75' |
| P23                   | N90°00'00"E | 9.84'  |
| P24                   | N90°00'00"E | 9.82'  |
| P25                   | S90°00'00"W | 8.78'  |
| P26                   | S90°00'00"W | 9.82'  |
| P27                   | S90°00'00"W | 9.75'  |
| P28                   | S90°00'00"W | 10.04' |
| P29                   | S72°04'15"W | 9.85'  |
| P30                   | S01°53'11"E | 8.79'  |
| P31                   | N01°31'05"W | 9.28'  |

| LINE TABLE |             |        |
|------------|-------------|--------|
| LINE       | BEARING     | LENGTH |
| L2         | N25°35'08"W | 28.45' |
| L3         | N03°14'56"E | 11.64' |

| CURVE TABLE |           |        |        |
|-------------|-----------|--------|--------|
| CURVE       | DELTA     | RADIUS | LENGTH |
| C3          | 40°45'04" | 47.00' | 33.43' |
| C4          | 29°10'41" | 47.00' | 23.94' |

SEE SHEET 2 FOR BASIS OF BEARINGS,  
DATUM STATEMENT, MONUMENT NOTES,  
SHEET INDEX AND GPS CONTROL MAP,  
EASEMENT NOTES AND NOTES.

