

SHEET 1 OF 4 SHEETS

8.825 ACRES

36 NUMBERED LOTS AND
LETTERED LOTS "A" THROUGH "E"
DATE OF SURVEY: JANUARY 2003
(ALL OF VESTING TENTATIVE
TRACT No. 16346)

TRACT NO. 16346

IN THE UNINCORPORATED TERRITORY OF THE COUNTY OF ORANGE, STATE OF CALIFORNIA.

BEING A SUBDIVISION OF LOT 12 OF TRACT No. 16341, AS SHOWN ON THE MAP THEREOF FILED
IN BOOK 840 AT PAGES 1 THROUGH 20, INCLUSIVE, OF MISCELLANEOUS MAPS,
IN THE OFFICE OF THE COUNTY RECORDER OF ORANGE COUNTY, CALIFORNIA.

FUSCOE ENGINEERING, INC.
JERRY L. USELTON, L.S. 5347 JANUARY 2003

ACCEPTED AND FILED AT THE
REQUEST OF

FIRST AMERICAN TITLE CO.

DATE AUGUST 18, 2003TIME 10:07AM FEE \$ 13.00INSTRUMENT # 200300037228BOOK 848 PAGE 1518TOM DALY
COUNTY CLERK-RECORDERBY: [Signature]
DEPUTY

OWNERSHIP CERTIFICATE:

WE THE UNDERSIGNED, BEING ALL PARTIES HAVING ANY RECORD TITLE INTEREST
IN THE LAND COVERED BY THIS MAP, DO HEREBY CONSENT TO THE PREPARATION
AND RECORDATION OF SAID MAP, AS SHOWN WITHIN THE DISTINCTIVE BORDER LINE.
WE ALSO HEREBY DEDICATE TO THE PUBLIC FOR STREET PURPOSES: SNOW BUSH STREET,
GARDENIA STREET; AND GREVILLEA COURT.

WE ALSO HEREBY DEDICATE TO THE COUNTY OF ORANGE:

1. THE EASEMENTS FOR STORM DRAIN PURPOSES AS SHOWN ON SAID MAP.

WE ALSO HEREBY DEDICATE TO THE SANTA MARGARITA WATER DISTRICT PIPELINE EASEMENTS
FOR SEWER, WATER AND ACCESS PURPOSES AS SHOWN ON SAID MAP, WHICH EASEMENTS SHALL
BE SUBJECT TO THE SAME TERMS AND CONDITIONS AS ARE SHOWN IN THAT CERTAIN EASEMENT
RECORDED OCTOBER 6, 1980 IN BOOK 13776, PAGE 341 OF OFFICIAL RECORDS, COUNTY OF
ORANGE. THE SANTA MARGARITA WATER DISTRICT SHALL RESTORE OTHER IMPROVEMENTS OR
FACILITIES LOCATED WITHIN THE EASEMENT, IF IT HAS CONSENTED TO THE LOCATION OF
SUCH IMPROVEMENTS OR FACILITIES TO THE EXTENT THAT THE EXERCISE OF ITS RIGHTS IN
THE CONNECTION WITH THE EASEMENT IMPACTS OTHER IMPROVEMENTS OR FACILITIES LOCATED
WITHIN THE EASEMENT; HOWEVER, IN NO EVENT SHALL SANTA MARGARITA WATER DISTRICT BE
RESPONSIBLE FOR THE COST OF RELOCATING ITS FACILITIES IN THE EVENT OF CONFLICTS WITH
SUCH OTHER IMPROVEMENTS OR FACILITIES.

PARDEE HOMES, A CALIFORNIA CORPORATION, OWNER

BY: [Signature]
THEODORE J. CULLEN
SR. VICE PRESIDENT

BY: [Signature]
NANCY TROJAN
ASSISTANT SECRETARY

DMB LADERA, LLC, A DELAWARE LIMITED LIABILITY COMPANY,
BENEFICIARY UNDER A DEED OF TRUST RECORDED APRIL 4, 2003 AS INSTRUMENT
No. 2003000377227, OF OFFICIAL RECORDS OF ORANGE COUNTY, CALIFORNIA

BY: RANCHO MISSION VIEJO, L.L.C., A DELAWARE LIMITED LIABILITY COMPANY,
ITS AUTHORIZED AGENT AND MANAGER.

BY: [Signature]
PRINT NAME DANIEL R. FERONS
PRINT TITLE CHIEF ENGINEER

BY: [Signature]
PRINT NAME PAUL JOHNSON
PRINT TITLE VP - COMMUNITY DEVELOPMENT

STATE OF CALIFORNIA } SS
COUNTY OF ORANGE }

ON THIS 24TH DAY OF JUNE, 2003, BEFORE ME, GRACY L. BOY

PERSONALLY APPEARED THEODORE J. CULLEN AND NANCY TROJAN
PERSONALLY KNOWN TO ME (OR PROVED TO ME ON THE BASIS OF SATISFACTORY EVIDENCE) TO BE THE
PERSON(S) WHOSE NAME(S) IS/ARE SUBSCRIBED TO THE WITHIN INSTRUMENT AND ACKNOWLEDGED TO ME THAT
HE/SHE/they EXECUTED THE SAME IN HIS/HER/their AUTHORIZED CAPACITY(IES), AND THAT BY
HIS/HER/their SIGNATURE(S) ON THE INSTRUMENT THE PERSON(S), OR THE ENTITY UPON BEHALF OF WHICH
THE PERSON(S) ACTED, EXECUTED THE INSTRUMENT.

MY PRINCIPAL PLACE OF BUSINESS
IS IN LOS ANGELES COUNTY.

WITNESS MY HAND:

(SIGNATURE)

NOTARY PUBLIC IN AND FOR SAID STATE

GRACY L. BOY
(PRINT NAME)

MY COMMISSION EXPIRES: 12/3/04

STATE OF CALIFORNIA } SS
COUNTY OF ORANGE }

ON THIS 12TH DAY OF JUNE, 2003, BEFORE ME, Jeannine Carta-Hanson

PERSONALLY APPEARED DANIEL R. FERONS and Paul Johnson
PERSONALLY KNOWN TO ME (OR PROVED TO ME ON THE BASIS OF SATISFACTORY EVIDENCE) TO BE THE
PERSON(S) WHOSE NAME(S) IS/ARE SUBSCRIBED TO THE WITHIN INSTRUMENT AND ACKNOWLEDGED TO ME THAT
HE/SHE/they EXECUTED THE SAME IN HIS/HER/their AUTHORIZED CAPACITY(IES), AND THAT BY
HIS/HER/their SIGNATURE(S) ON THE INSTRUMENT THE PERSON(S), OR THE ENTITY UPON BEHALF OF WHICH
THE PERSON(S) ACTED, EXECUTED THE INSTRUMENT.

MY PRINCIPAL PLACE OF BUSINESS
IS IN Orange COUNTY.

WITNESS MY HAND:

(SIGNATURE)

NOTARY PUBLIC IN AND FOR SAID STATE

Jeannine Carta-Hanson
(PRINT NAME)

MY COMMISSION EXPIRES: Feb. 29, 2007SANTA MARGARITA WATER DISTRICT
CERTIFICATE OF ACCEPTANCE:

THE UNDERSIGNED BEING THE DULY APPOINTED AGENT OF THE SANTA MARGARITA WATER
DISTRICT, A PUBLIC CORPORATION IN ORANGE COUNTY, CALIFORNIA, PURSUANT TO ITS
RESOLUTION NO. 88-10-2, DOES HEREBY ACCEPT ON BEHALF OF SAID DISTRICT THE
PIPELINE EASEMENTS FOR SEWER, WATER AND ACCESS PURPOSES, AS DEDICATED AND AS
SHOWN ON THIS TRACT MAP, BY AND BETWEEN THE SANTA MARGARITA WATER DISTRICT AND
PARDEE HOMES, AND DOES HEREBY CERTIFY THAT THE GRANTEE CONSENTS TO THE
RECORDATION OF SAID TRACT MAP.

[Signature]
DANIEL R. FERONS, CHIEF ENGINEER
SANTA MARGARITA WATER DISTRICT

STATE OF CALIFORNIA } SS
COUNTY OF ORANGE }

ON THIS 13TH DAY OF JUNE, 2003, BEFORE ME, Cindy R. Lane

PERSONALLY APPEARED DANIEL R. FERONS
PERSONALLY KNOWN TO ME (OR PROVED TO ME ON THE BASIS OF SATISFACTORY EVIDENCE) TO BE THE
PERSON(S) WHOSE NAME(S) IS/ARE SUBSCRIBED TO THE WITHIN INSTRUMENT AND ACKNOWLEDGED TO ME THAT
HE/SHE/they EXECUTED THE SAME IN HIS/HER/their AUTHORIZED CAPACITY(IES), AND THAT BY
HIS/HER/their SIGNATURE(S) ON THE INSTRUMENT THE PERSON(S), OR THE ENTITY UPON BEHALF OF WHICH
THE PERSON(S) ACTED, EXECUTED THE INSTRUMENT.

MY PRINCIPAL PLACE OF BUSINESS
IS IN ORANGE COUNTY.

WITNESS MY HAND:

(SIGNATURE)

NOTARY PUBLIC IN AND FOR SAID STATE


CINDY R. LANE
(PRINT NAME)

MY COMMISSION EXPIRES: 2/20/05

SURVEYOR'S STATEMENT:

THIS MAP WAS PREPARED BY ME OR UNDER MY DIRECTION AND IS BASED ON A
FIELD SURVEY IN CONFORMANCE WITH THE REQUIREMENTS OF THE SUBDIVISION
MAP ACT AND LOCAL ORDINANCE AT THE REQUEST OF PARDEE HOMES, INC., ON
JANUARY 2003. I HEREBY STATE THAT ALL MONUMENTS ARE OF THE CHARACTER
AND OCCUPY THE POSITIONS INDICATED, OR THAT THEY WILL BE SET IN SUCH
POSITIONS; AND THAT SAID MONUMENTS ARE SUFFICIENT TO ENABLE THE SURVEY
TO BE RETRACED. I HEREBY STATE THAT THIS FINAL MAP SUBSTANTIALLY CONFORMS
TO THE CONDITIONALLY APPROVED TENTATIVE MAP.

[Signature]
JERRY L. USELTON, L.S. 5347
LICENSE EXPIRES 12/31/03

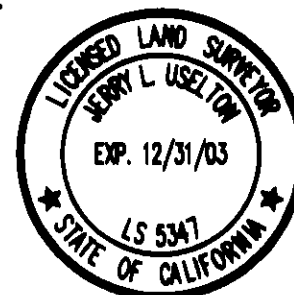


COUNTY SURVEYOR'S STATEMENT:

I HEREBY STATE THAT I HAVE EXAMINED THIS MAP AND FOUND IT TO BE
SUBSTANTIALLY IN CONFORMANCE WITH THE TENTATIVE MAP, AS FILED WITH,
AMENDED AND APPROVED BY THE ORANGE COUNTY SUBDIVISION COMMITTEE;
THAT ALL PROVISIONS OF THE SUBDIVISION MAP ACT AND COUNTY SUBDIVISION
REGULATIONS HAVE BEEN COMPLIED WITH AND I AM SATISFIED SAID MAP IS
TECHNICALLY CORRECT.

DATED THIS 25TH DAY OF JULY, 2003.

[Signature]
JOHN CANAS, COUNTY SURVEYOR
L.S. 4408, EXPIRATION DATE: 9/30/05

BY: MICHAEL K. SULLIVAN, DEPUTY
L.S. 6284 EXPIRES 8/30/05

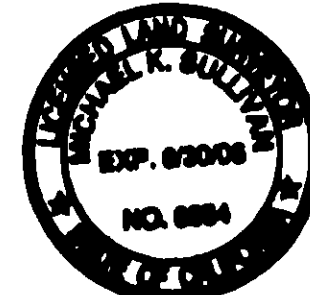

COUNTY TREASURER-TAX COLLECTOR'S CERTIFICATE:

STATE OF CALIFORNIA } SS
COUNTY OF ORANGE }

I HEREBY CERTIFY THAT ACCORDING TO THE RECORDS OF MY OFFICE THERE ARE
NO LIENS AGAINST THE LAND COVERED BY THIS MAP OR ANY PART THEREOF FOR
UNPAID STATE, COUNTY, MUNICIPAL OR LOCAL TAXES OR SPECIAL ASSESSMENTS
COLLECTED AS TAXES, EXCEPT TAXES OR SPECIAL ASSESSMENTS COLLECTED AS
TAXES NOT YET PAYABLE.
AND DO ALSO CERTIFY TO THE RECORDER OF ORANGE COUNTY THAT THE
PROVISIONS OF THE SUBDIVISION MAP ACT HAVE BEEN COMPLIED WITH
REGARDING DEPOSITS TO SECURE THE PAYMENT OF TAXES OR SPECIAL
ASSESSMENTS COLLECTED AS TAXES ON THE LAND COVERED BY THIS MAP.

DATED THIS 17 DAY OF JUNE, 2003.

JOHN M. W. MOORLACH
COUNTY TREASURER-TAX COLLECTOR

BY: [Signature]
DEPUTY TREASURER-TAX COLLECTOR

CLERK OF THE BOARD OF SUPERVISOR'S CERTIFICATE:

STATE OF CALIFORNIA } SS
COUNTY OF ORANGE }

I HEREBY CERTIFY THAT THIS MAP WAS PRESENTED FOR APPROVAL TO THE
BOARD OF SUPERVISORS OF ORANGE COUNTY AT A REGULAR MEETING
THEREOF HELD ON THE 12TH DAY OF AUGUST, 2003,
AND THAT THEREUPON SAID BOARD DID, BY AN ORDER DULY PASSED AND ENTERED,
APPROVE SAID MAP AND DID ACCEPT ON BEHALF OF THE PUBLIC, SUBJECT TO
IMPROVEMENTS: THE DEDICATION FOR STREET PURPOSES OF: SNOW BUSH STREET,
GARDENIA STREET; AND GREVILLEA COURT.

AND DID ALSO ACCEPT ON BEHALF OF THE COUNTY OF ORANGE;
1. THE EASEMENTS FOR STORM DRAIN PURPOSES AS DEDICATED.

DATED THIS 12TH DAY OF AUGUST, 2003.

[Signature]
DARLENE J. BLOOM
CLERK OF THE BOARD OF SUPERVISORS
OF ORANGE COUNTY, CALIFORNIA



SIGNATURE OMISSION NOTES:

IN ACCORDANCE WITH THE PROVISIONS OF SECTION 66436(d)(3) OF THE
SUBDIVISION MAP ACT, THE FOLLOWING SIGNATURES HAVE BEEN OMITTED:

- 1.) LADERA DEVELOPMENT COMPANY, L.L.C. HOLDER OF OIL, GAS, AND MINERAL
RIGHTS RECORDED DECEMBER 10, 1996, AS INSTRUMENT NO.
19960624029 OF OFFICIAL RECORDS.
- 2.) DMB LADERA LLC, A DELAWARE LIMITED LIABILITY COMPANY, HOLDER
OF EASEMENTS RESERVED IN THE DEED RECORDED APRIL 4, 2003 AS
INSTRUMENT NO. 2003000377228 OF OFFICIAL RECORDS.
(SAID EASEMENTS NOT PLOTTABLE PER THE RECORD)

SHEET 2 OF 4 SHEETS

8.825 ACRES

38 NUMBERED LOTS AND

LETTERED LOTS "A" THROUGH "E"

DATE OF SURVEY: JANUARY 2003

(ALL OF VESTING TENTATIVE

TRACT No. 16346)

TRACT NO. 16346

IN THE UNINCORPORATED TERRITORY OF THE COUNTY OF ORANGE, STATE OF CALIFORNIA.

FUSCOE ENGINEERING, INC.

JERRY L. USELTON, L.S. 5347 JANUARY 2003

BASIS OF BEARINGS:

THE BEARINGS SHOWN HEREON ARE BASED ON THE BEARING BETWEEN O.C.S. HORIZONTAL CONTROL STATION GPS No. 1417 AND STATION GPS No. 1448 BEING NORTH 10°48'13" EAST PER RECORDS ON FILE IN THE OFFICE OF THE ORANGE COUNTY SURVEYOR.

DATUM STATEMENT:

COORDINATES SHOWN ARE BASED ON THE CALIFORNIA COORDINATE SYSTEM (CCS83), ZONE VI, 1983 NAD, (1991.36 EPOCH OCS GPS ADJUSTMENT). ALL DISTANCES SHOWN ARE GROUND, UNLESS OTHERWISE NOTED. TO OBTAIN GRID DISTANCES MULTIPLY GROUND DISTANCE BY 0.999948286 (NOTE: THIS COMBINATION FACTOR IS NOT AN AVERAGE OF THE COMBINATION FACTORS OF THE TWO CONTROL POINTS, BUT IS SPECIFIC TO THIS PROJECT)

MONUMENT NOTES:

● INDICATES FOUND OCS GPS MONUMENT AS NOTED:

A N=2146780.818
E=6145805.888
FOUND 2 1/2" IRON PIPE WITH 1-3/4" OCS BRASS CAP STAMPED "GPS 1448 8-96" PER TRACT No. 16203, M.M. 826/8-20 AND RECORDS ON FILE IN THE ORANGE COUNTY SURVEYOR'S OFFICE.

B N=2141490.558
E=6141883.536
FOUND 2 1/2" IRON PIPE WITH 2" OCS BRASS CAP STAMPED "GPS 1417 8-96" PER TRACT No. 16203, M.M. 826/8-20 AND RECORDS ON FILE IN THE ORANGE COUNTY SURVEYOR'S OFFICE.

■ INDICATES 2" I.P. TAGGED "L.S. 5347" OR SPIKE AND WASHER STAMPED "L.S. 5347" OR LEAD AND TAG "L.S. 5347" TO BE SET PRIOR TO RECORDATION OF THIS TRACT

□ INDICATES 2" I.P. TAGGED "L.S. 5557" OR SPIKE AND WASHER STAMPED "L.S. 5557" OR LEAD AND TAG "L.S. 5557" TO BE SET WITHIN 90 DAYS AFTER ACCEPTANCE OF IMPROVEMENTS PER TRACT 16341, M.M. 840/1-20

○ INDICATES 1" I.P. TAGGED "L.S. 5557" OR SPIKE AND WASHER STAMPED "L.S. 5557" OR LEAD AND TAG "L.S. 5557" TO BE SET WITHIN 90 DAYS AFTER ACCEPTANCE OF IMPROVEMENTS PER TRACT 16341, M.M. 840/1-20

2" I.P. TAGGED "L.S. 5347", OR SPIKE AND WASHER "L.S. 5347", OR LEAD TACK AND TAG "L.S. 5347" TO BE SET AT ALL TRACT BOUNDARY CORNERS WITHIN 90 DAYS AFTER ACCEPTANCE OF IMPROVEMENTS, UNLESS NOTED OTHERWISE.

1" I.P. TAGGED "L.S. 5347", OR SPIKE AND WASHER "L.S. 5347", OR NAIL AND TAG "L.S. 5347" TO BE SET AT ALL LOT CORNERS WITHIN 90 DAYS AFTER ACCEPTANCE OF IMPROVEMENTS, EXCEPT B.C.s, E.C.s, P.R.C.s, AND P.C.C.s WHICH ABUT A STREET AND ARE NOT LOT CORNERS MARKING SIDE LOT LINES, ALSO EXCEPT AT FRONT LOT CORNERS SET LEAD TACK AND TAG "L.S. 5347" IN TOP OF CURB ALONG PROJECTED SIDE LOT LINE, UNLESS NOTED OTHERWISE.

1" I.P. TAGGED "L.S. 5347" OR SPIKE AND WASHER "L.S. 5347" TO BE SET AT ALL STREET CENTERLINE POINTS OF CONTROL WITHIN 90 DAYS AFTER ACCEPTANCE OF IMPROVEMENTS, UNLESS NOTED OTHERWISE.

SURVEYOR'S NOTES:

DATA SHOWN ALONG THIS TRACT BOUNDARY ARE MEASURED AND RECORD PER TRACT No. 16341, M.M. 840/1-20, UNLESS NOTED OTHERWISE.

ALL LETTERED LOTS SHOWN HEREON ARE NOT SEPARATE BUILDING SITES. LOTS "A", "B", "C", "D", AND "E" ARE FOR SLOPE AND LANDSCAPE PURPOSES AND ARE TO BE CONVEYED TO THE APPROPRIATE HOMEOWNERS ASSOCIATION.

AUTOMATIC FIRE SPRINKLER NOTE:

ALL COMMERCIAL STRUCTURES OVER 6,000 SQUARE FEET; ALL MULTIFAMILY RESIDENTIAL STRUCTURES; ALL DETACHED, SINGLE-FAMILY STRUCTURES EXCEEDING 5,500 SQUARE FEET, AND, ALL STRUCTURES EXCEEDING FIRE AUTHORITY ACCESS REQUIREMENTS SHALL BE PROTECTED BY AN AUTOMATIC SPRINKLER SYSTEM, IN A MANNER MEETING THE APPROVAL OF THE FIRE CHIEF.

SPECIAL FIRE PROTECTION NOTE:

PROPERTY IS IN A SPECIAL FIRE PROTECTION AREA AND MUST MEET ALL REQUIREMENTS FOR DEVELOPMENT IN THE AREA

HIGH FIRE HAZARD AREA NOTE:


THE LOTS SHOWN ON THIS MAP ARE IN A HIGH FIRE HAZARD AREA DUE TO WILDLAND EXPOSURE.

EASEMENT NOTES:

A DENOTES THE EASEMENT FOR WATER, SEWER, AND ACCESS PURPOSES DEDICATED TO THE SANTA MARGARITA WATER DISTRICT HEREON.

B DENOTES THE EASEMENT FOR STORM DRAIN PURPOSES DEDICATED TO THE COUNTY OF ORANGE HEREON.

VICINITY MAP AND OCS GPS CONTROL SCHEME

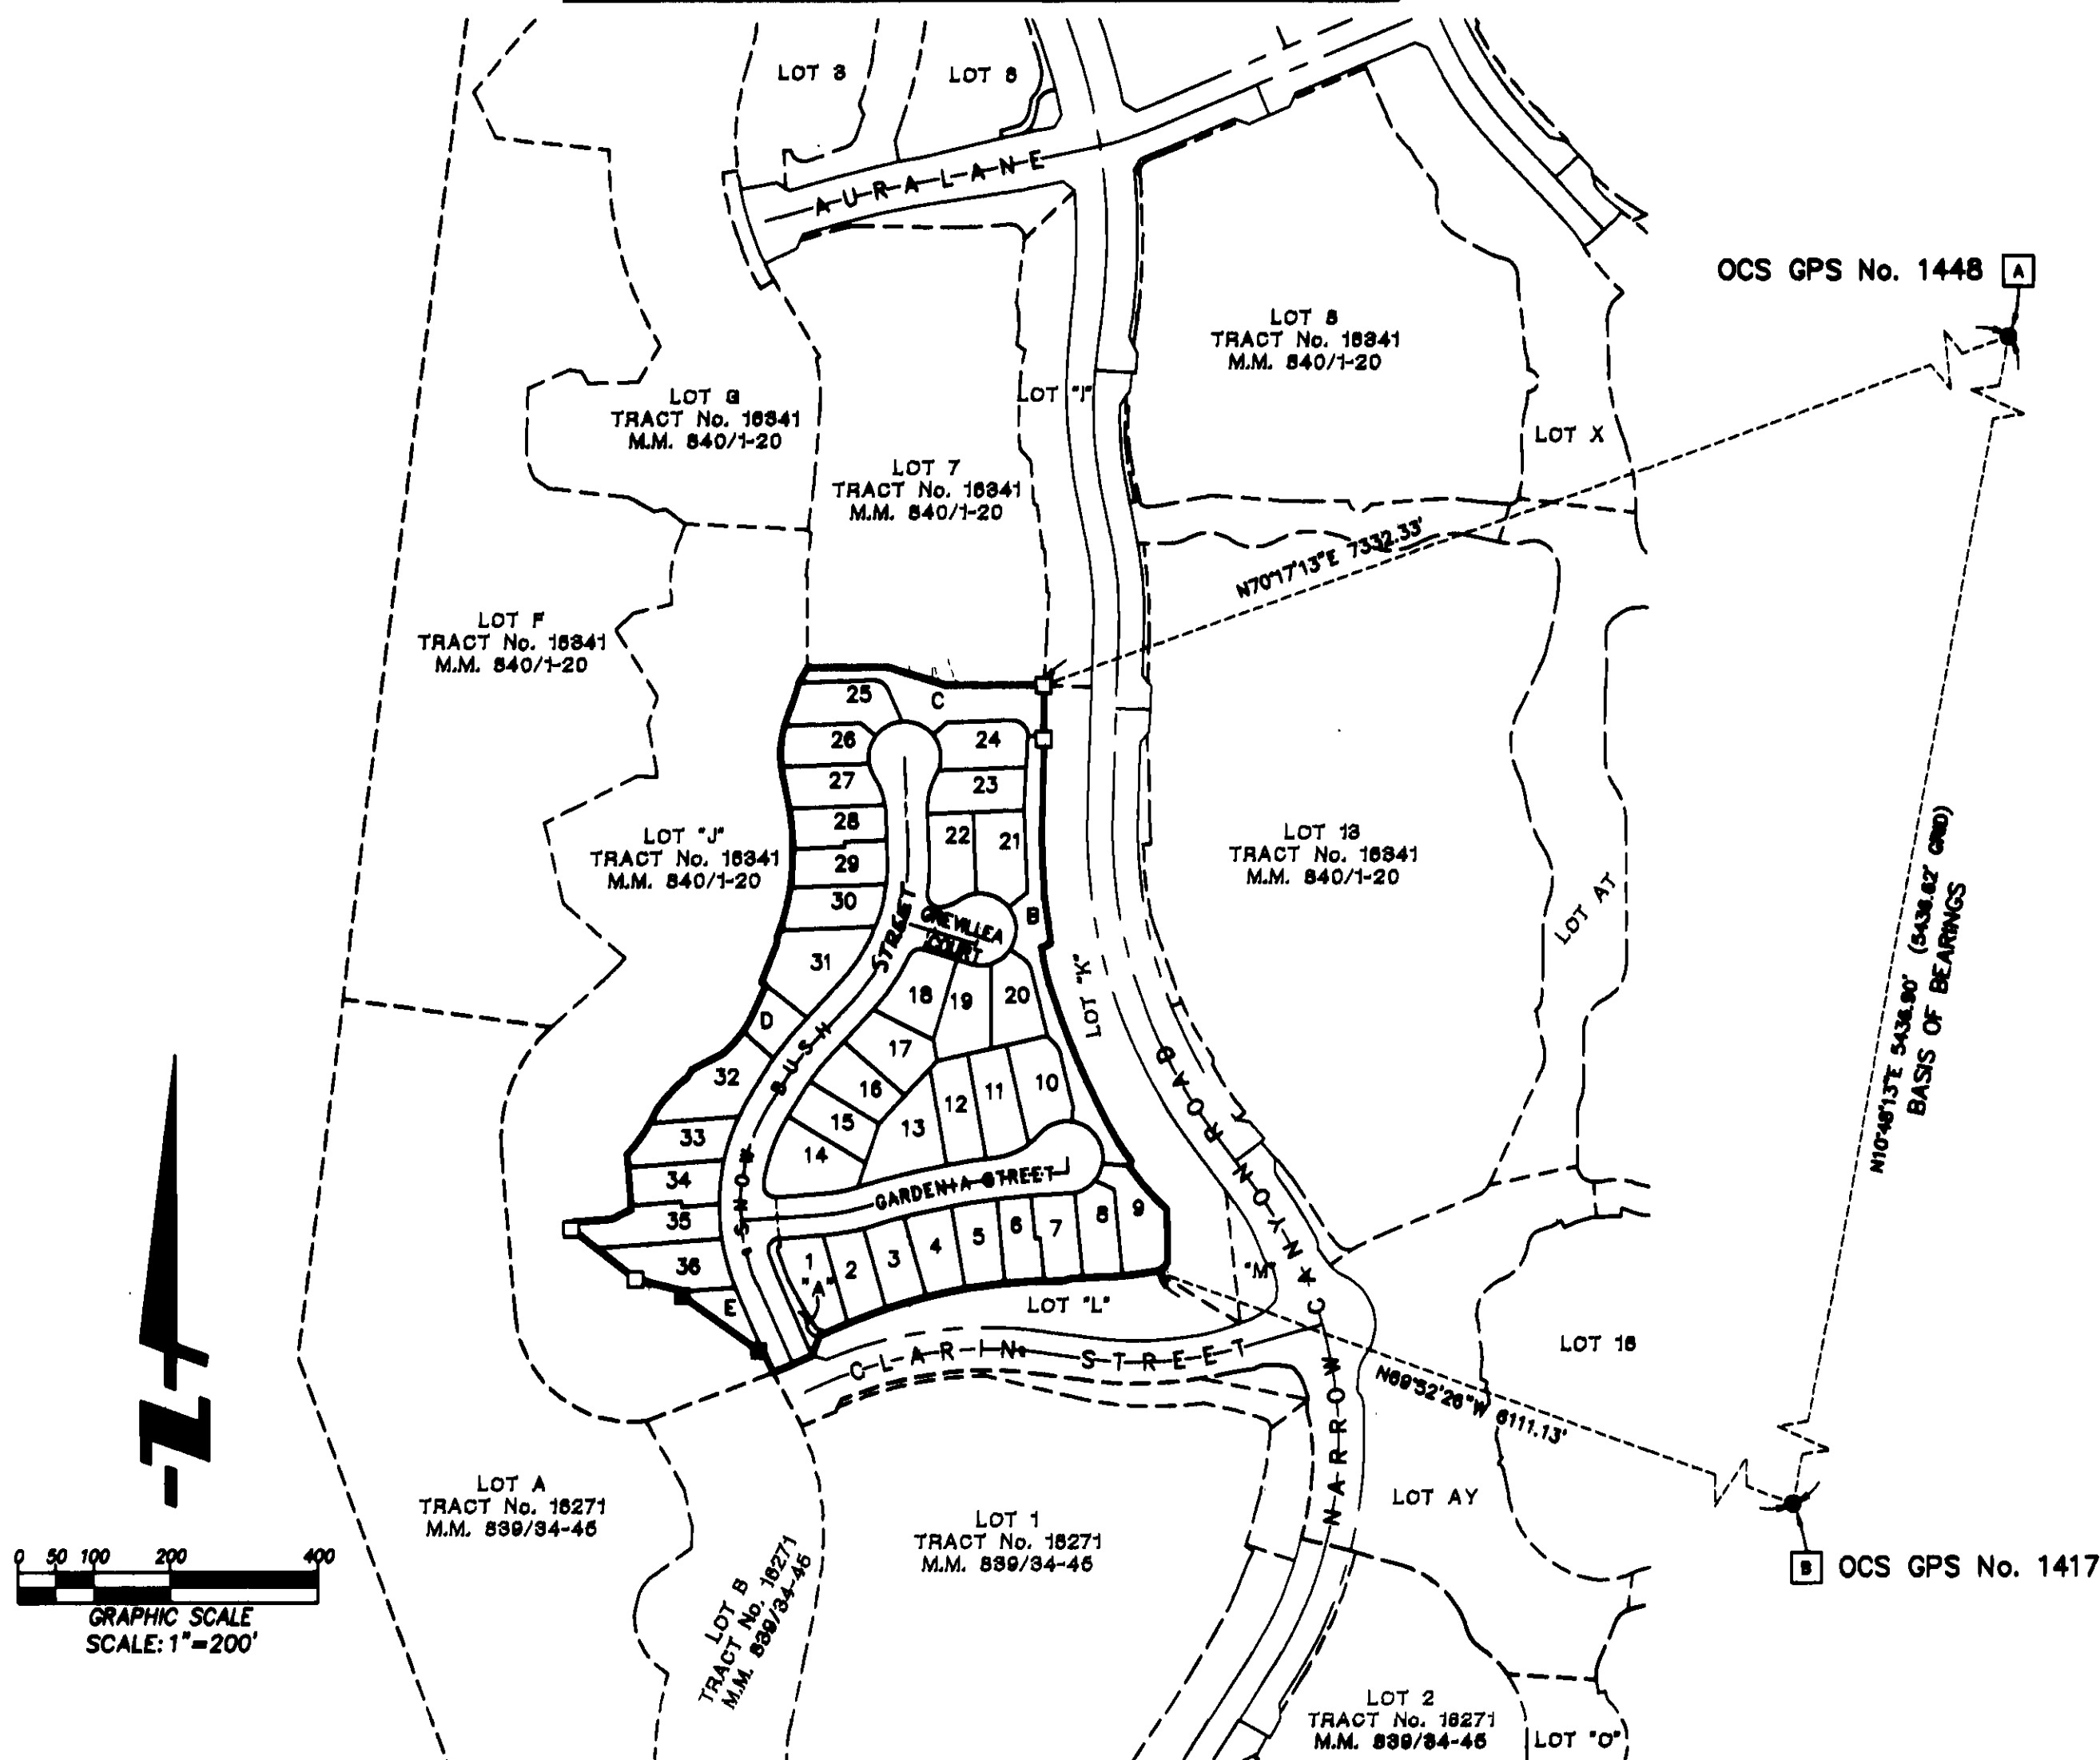


848 17

TRACT NO. 16346

IN THE UNINCORPORATED TERRITORY OF THE COUNTY OF ORANGE, STATE OF CALIFORNIA.
FUSCOE ENGINEERING, INC.
JERRY L. USELTON, L.S. 5347 JANUARY 2003

SHEET 3 OF 4 SHEETS
8.825 ACRES
36 NUMBERED LOTS AND
LETTERED LOTS "A" THROUGH "E"
DATE OF SURVEY: JANUARY 2003
(ALL OF VESTING TENTATIVE)
TRACT No. 16346)

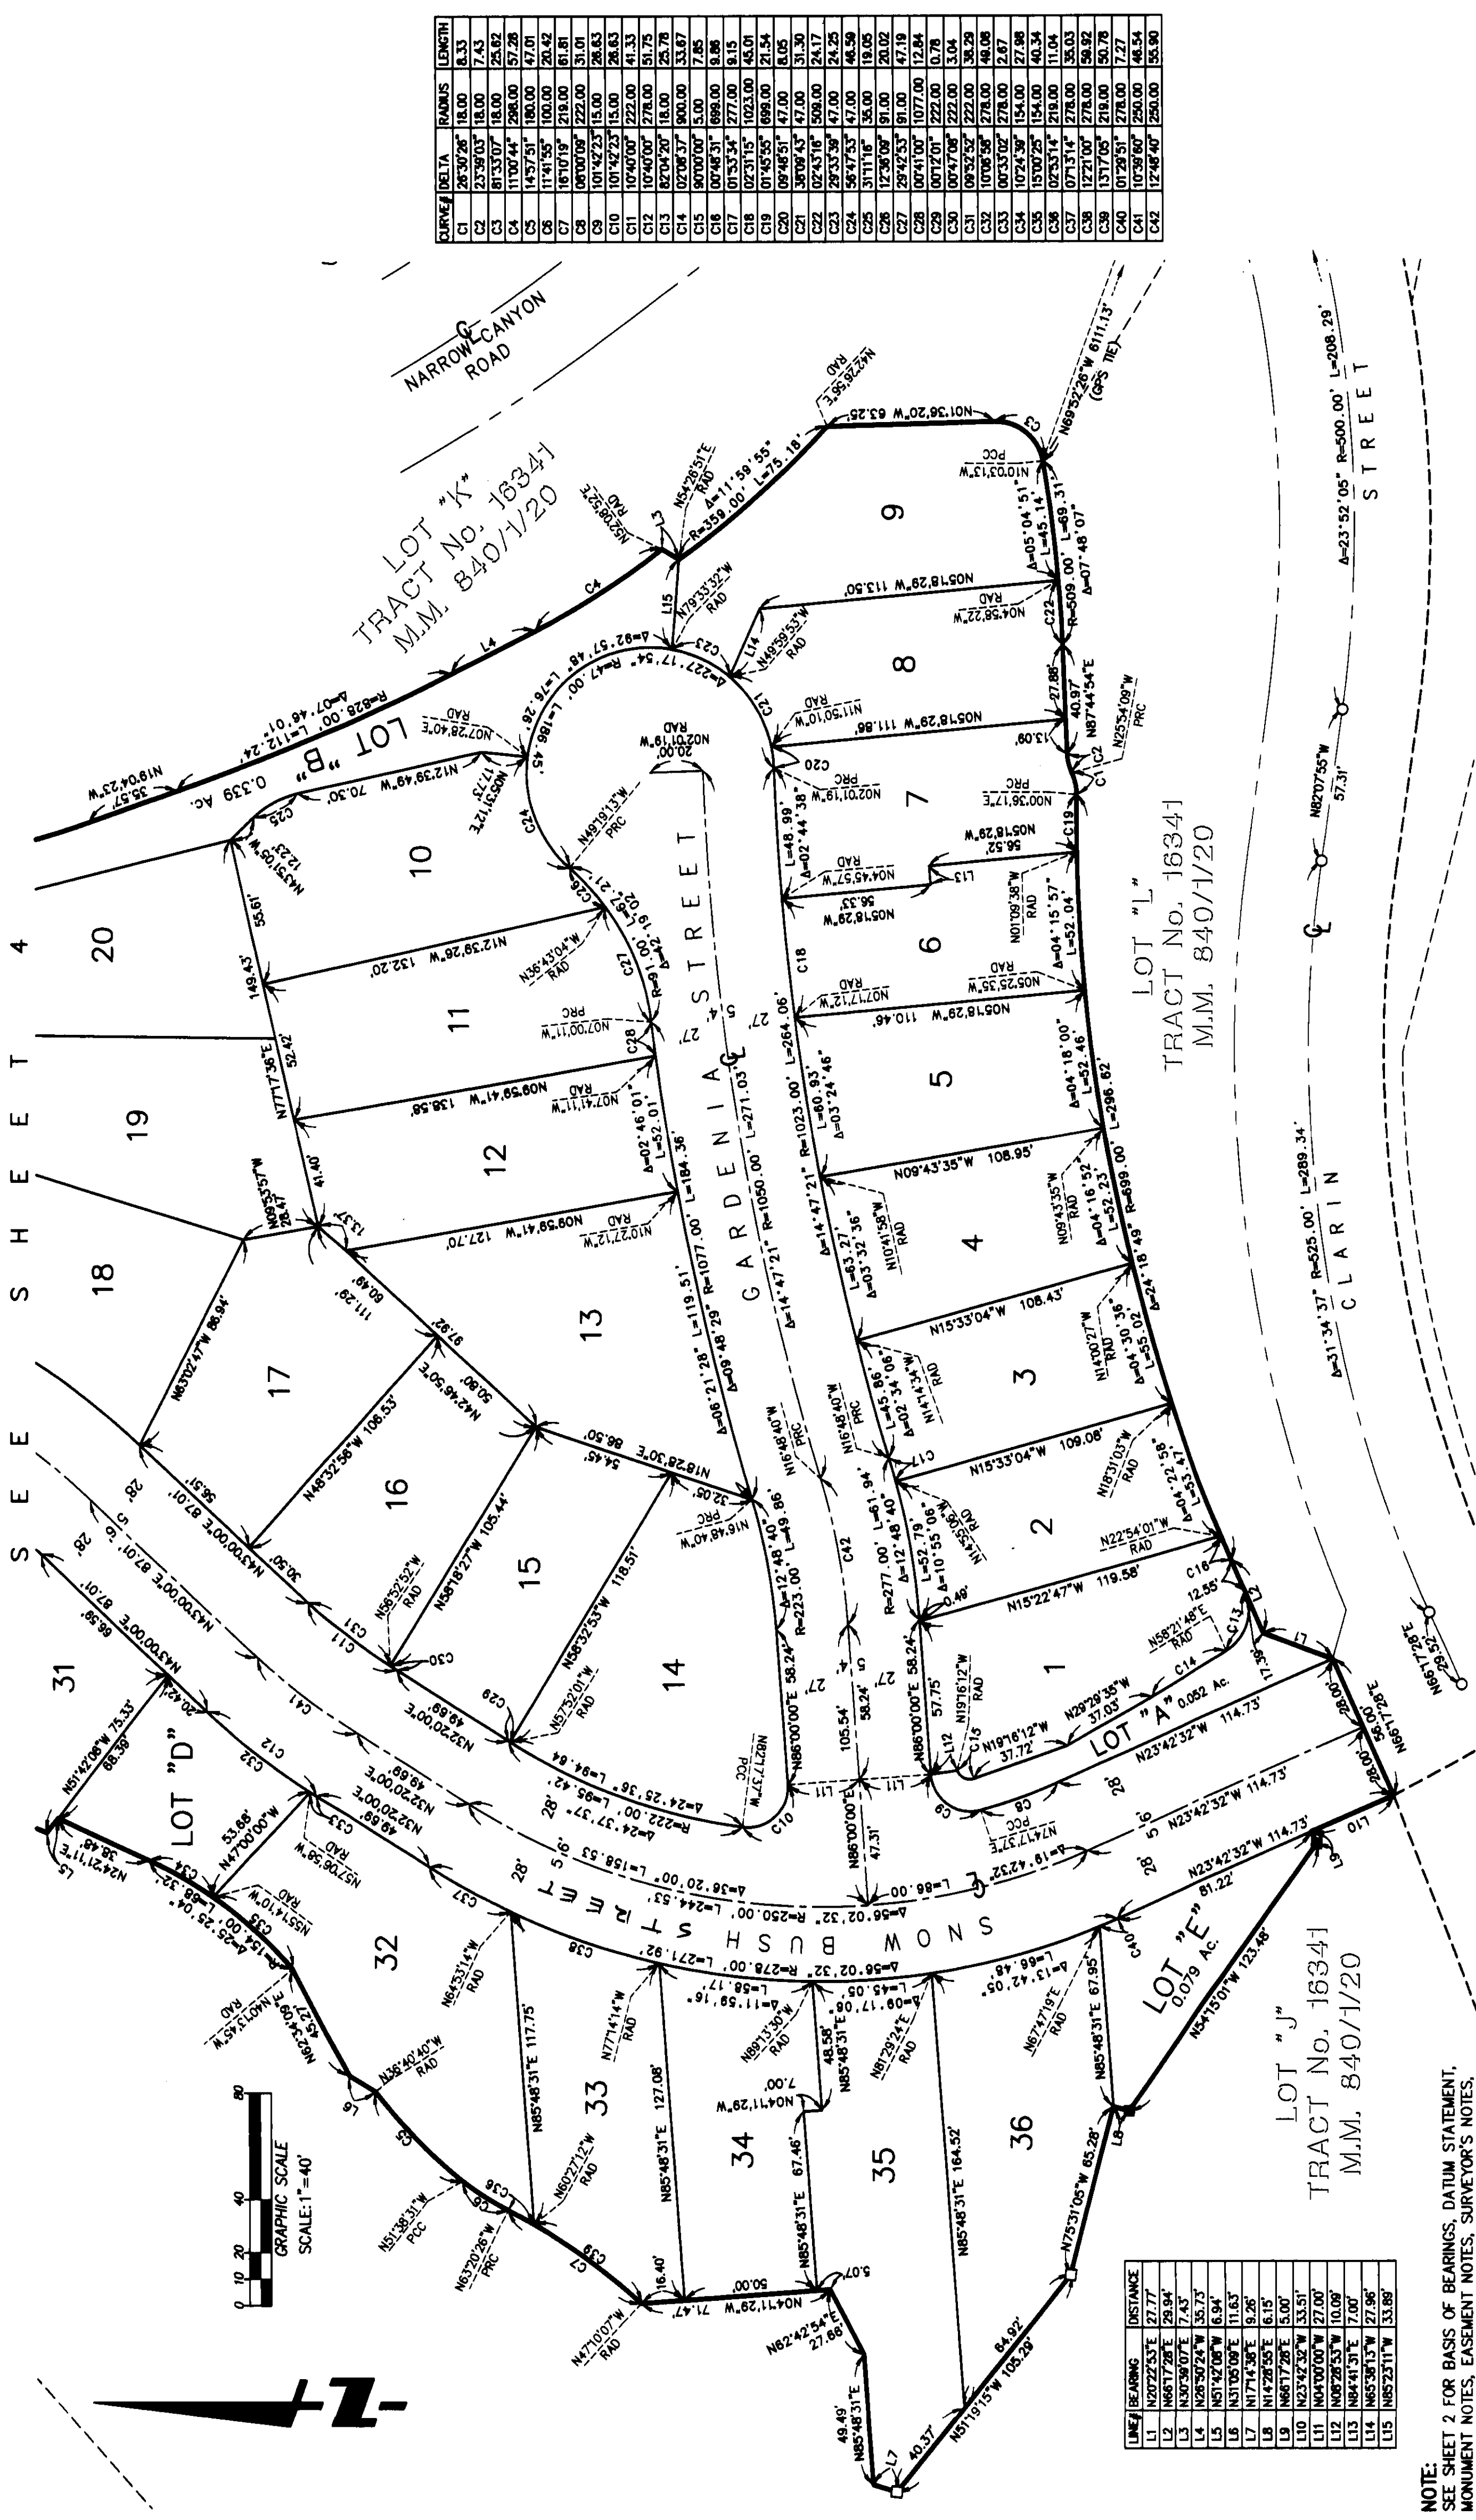

CURVE	DELTA	RADIUS	LENGTH
C1	28°30'28"	18.00	8.33
C2	23°39'03"	18.00	7.43
C3	81°33'07"	18.00	25.62
C4	11°00'44"	288.00	57.28
C5	14°57'51"	180.00	47.01
C6	11°41'55"	100.00	20.42
C7	16°10'18"	218.00	61.81
C8	08°00'08"	222.00	51.01
C9	101°42'23"	15.00	26.63
C10	101°42'23"	15.00	26.63
C11	10°40'00"	222.00	41.33
C12	10°40'00"	278.00	51.75
C13	82°04'20"	18.00	25.78
C14	02°08'37"	800.00	33.67
C15	80°00'00"	5.00	7.85
C16	00°48'31"	698.00	8.86
C17	01°53'34"	277.00	9.15
C18	02°31'15"	1023.00	45.01
C19	01°45'55"	699.00	21.54
C20	08°48'51"	47.00	8.05
C21	38°09'43"	47.00	31.30
C22	02°43'16"	508.00	24.25
C23	28°33'38"	47.00	46.59
C24	56°47'53"	47.00	18.05
C25	31°11'16"	35.00	19.05
C26	12°36'08"	81.00	20.02
C27	38°42'53"	81.00	47.18
C28	00°41'00"	1077.00	12.84
C29	00°12'01"	222.00	0.78
C30	00°47'08"	222.00	3.04
C31	09°52'52"	222.00	38.29
C32	10°05'58"	278.00	48.06
C33	00°33'02"	278.00	2.67
C34	07°24'38"	154.00	27.98
C35	15°00'25"	154.00	40.34
C36	02°53'14"	218.00	11.04
C37	07°13'14"	278.00	35.03
C38	12°21'00"	278.00	50.92
C39	13°17'05"	218.00	50.78
C40	01°28'51"	278.00	7.27
C41	10°39'40"	250.00	48.54
C42	12°48'40"	250.00	55.90

LINE	BEARING	DISTANCE
L1	N20°22'43"E	27.77
L2	N68°17'28"E	29.94
L3	N30°38'07"E	7.43
L4	N28°50'24"W	35.73
L5	N51°42'08"W	6.94
L6	N31°05'09"E	11.63
L7	N17°14'38"E	9.26
L8	N14°28'55"E	6.15
L9	N68°17'28"E	5.00
L10	N23°42'32"W	33.51
L11	N04°00'00"W	27.00
L12	N08°28'53"W	10.09
L13	N84°41'31"E	7.00
L14	N65°38'15"W	27.96
L15	N85°23'11"W	33.88



NOTE:
SEE SHEET 2 FOR BASIS OF BEARINGS, DATUM STATEMENT,
MONUMENT NOTES, EASEMENT NOTES, SURVEYOR'S NOTES,
NOTES, AND VICINITY MAP AND OCS GPS CONTROL SCHEME.

848 18

TRACT NO. 16346

IN THE UNINCORPORATED TERRITORY OF THE COUNTY OF ORANGE, STATE OF CALIFORNIA.
FUSCOE ENGINEERING, INC.
JERRY L. USELTON, L.S. 5347 JANUARY 2003

SHEET 4 OF 4 SHEETS
8.825 ACRES
36 NUMBERED LOTS AND
LETTERED LOTS "A" THROUGH "E"
DATE OF SURVEY: JANUARY 2003
(ALL OF VESTING TENTATIVE)
TRACT No. 16346)

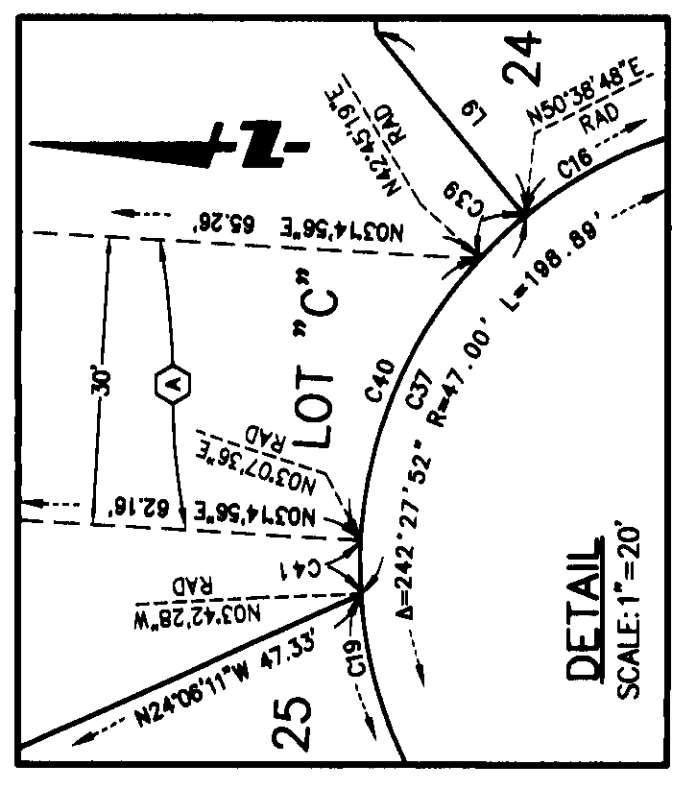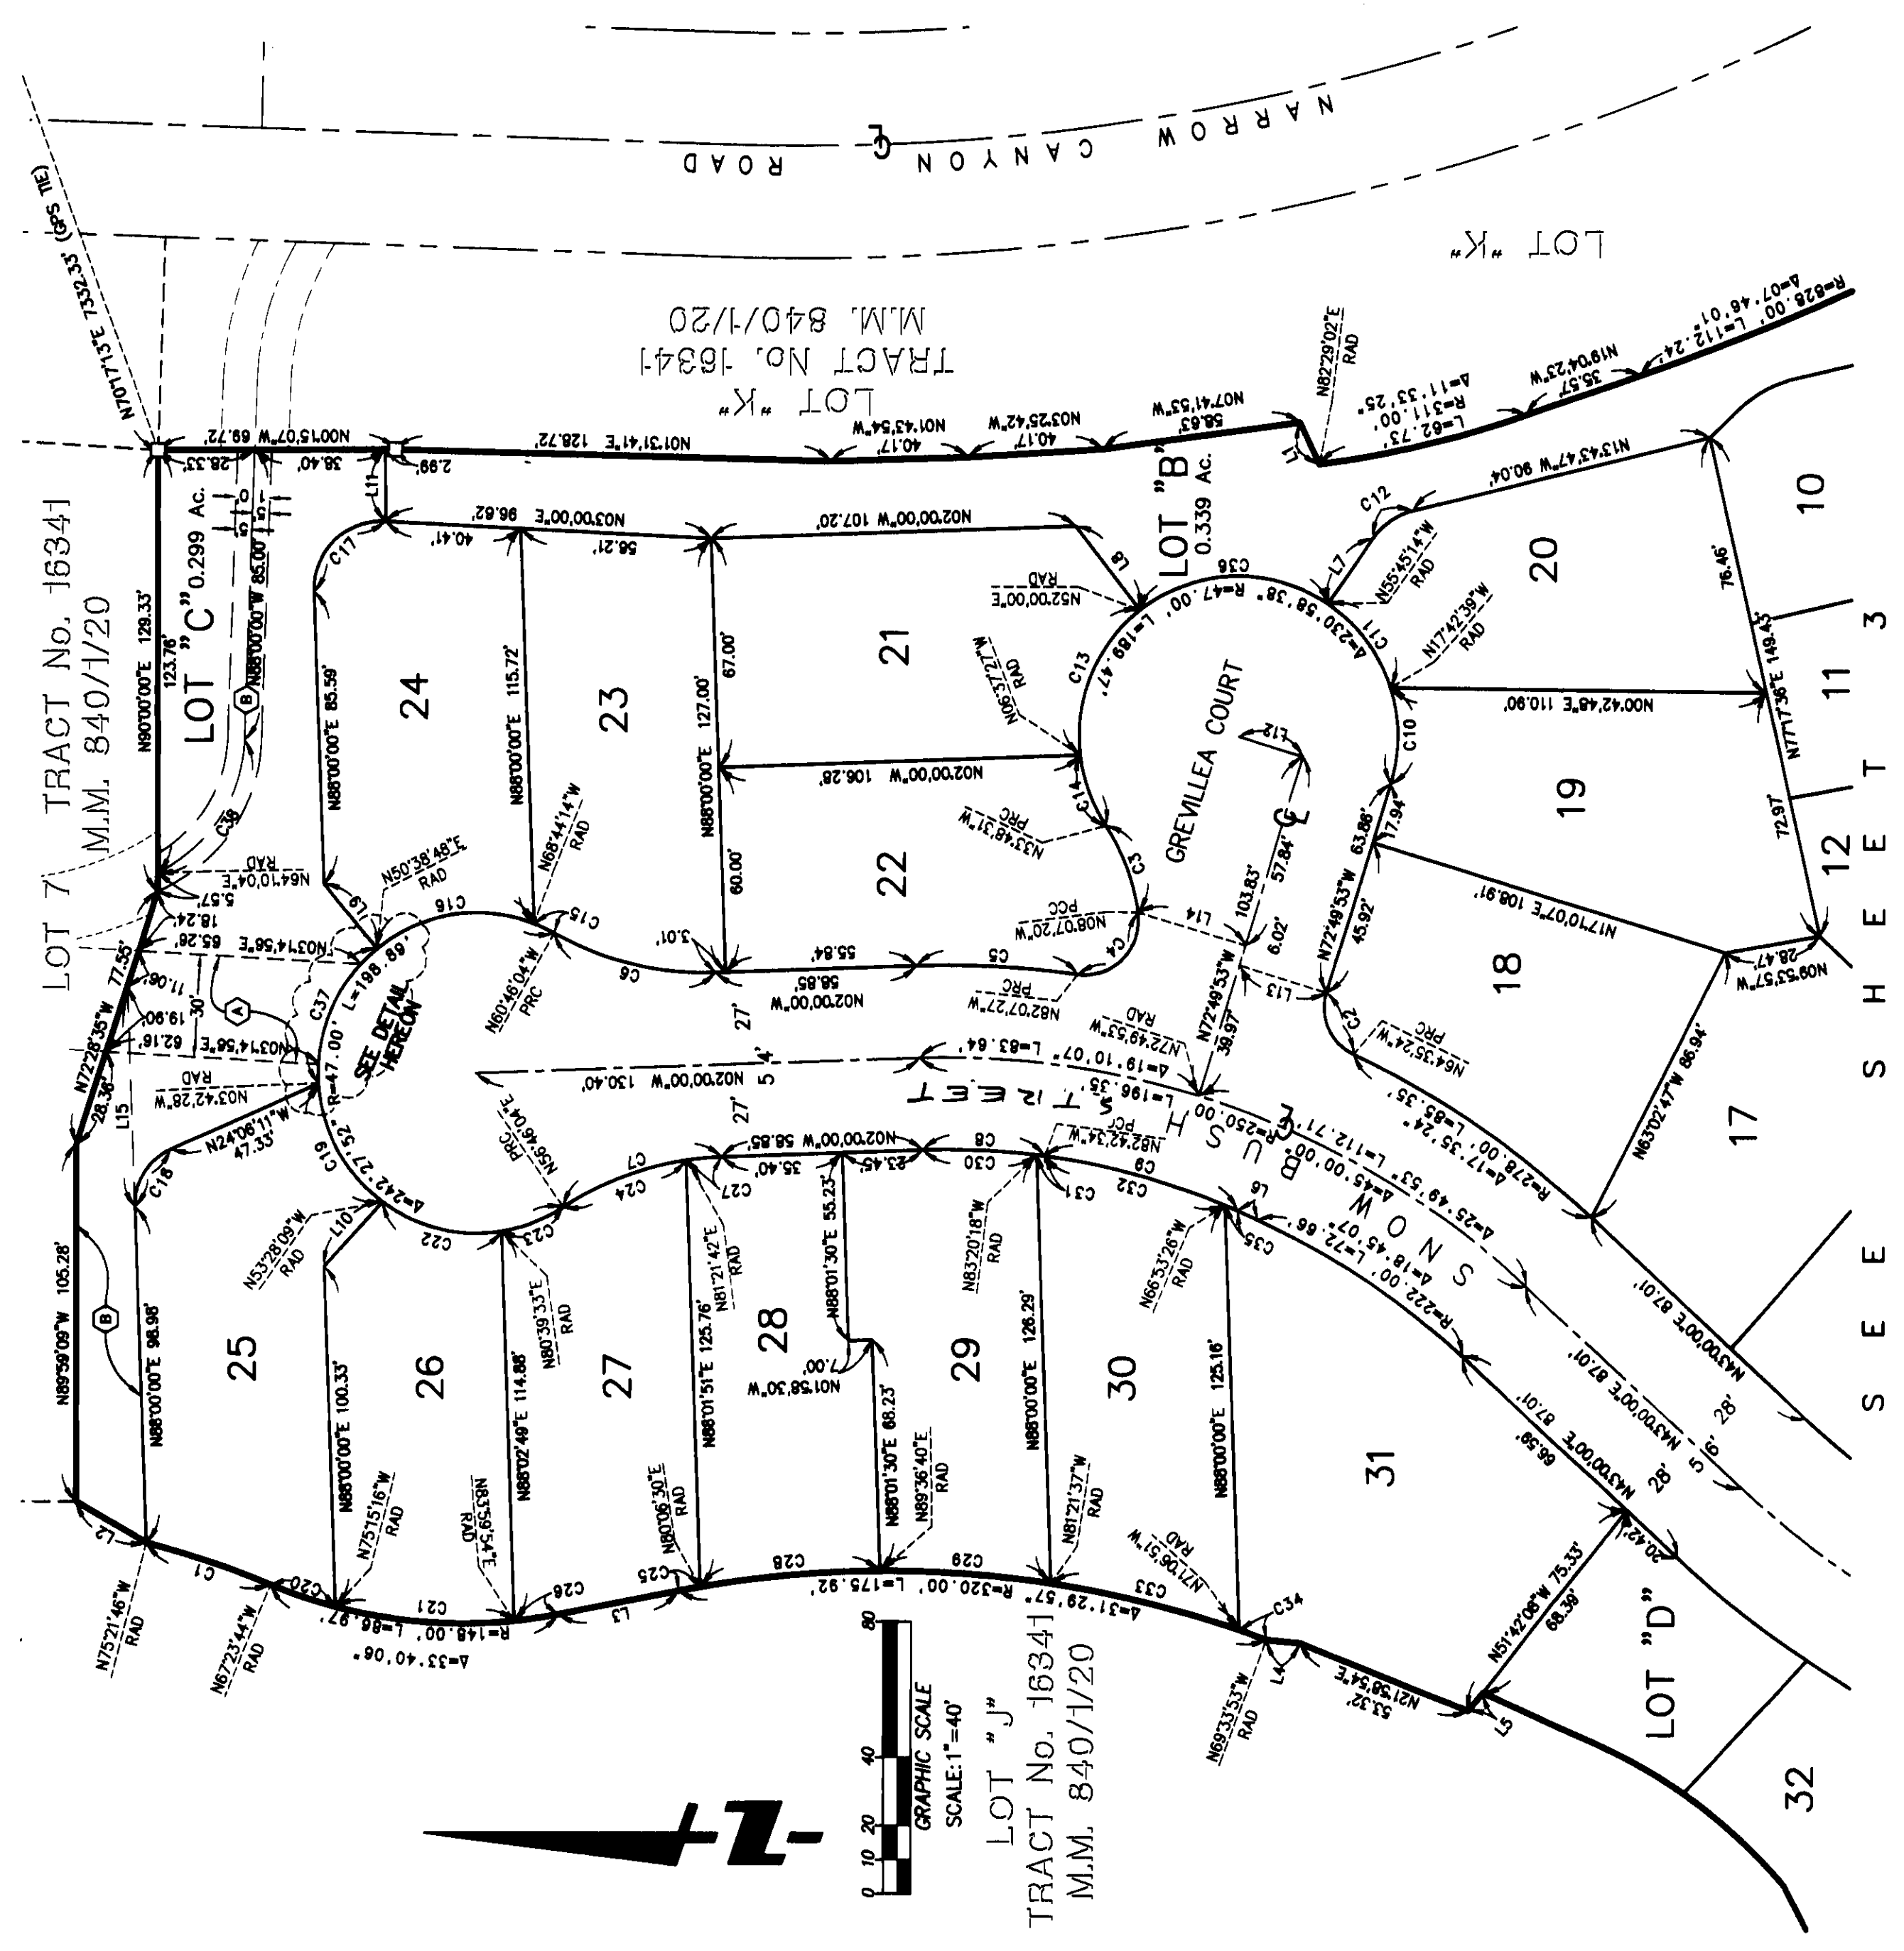

CURVE#	DELTA	RADIUS	LENGTH
C1	07°38'02"	277.00	58.52
C2	61°45'31"	15.00	21.40
C3	28°41'11"	61.00	27.35
C4	105°59'53"	16.00	28.60
C5	09°52'33"	277.00	47.75
C6	31°13'58"	91.00	48.80
C7	31°13'58"	91.00	48.80
C8	09°17'26"	223.00	58.16
C9	16°57'27"	200.00	58.19
C10	34°52'46"	47.00	28.61
C11	36°02'35"	47.00	31.21
C12	41°45'04"	20.00	14.57
C13	56°37'27"	47.00	48.09
C14	27°11'04"	47.00	22.30
C15	07°58'10"	47.00	8.54
C16	60°36'58"	47.00	48.72
C17	95°00'00"	20.00	33.16
C18	67°53'49"	18.00	21.33
C19	48°45'41"	47.00	40.82
C20	07°51'32"	148.00	20.30

CURVE#	DELTA	RADIUS	LENGTH
C21	20°44'50"	148.00	53.59
C22	45°52'18"	47.00	37.63
C23	23°53'28"	47.00	19.60
C24	24°35'38"	91.00	39.06
C25	01°10'20"	320.00	6.55
C26	05°03'44"	148.00	13.08
C27	05°03'44"	91.00	10.54
C28	09°30'10"	320.00	53.07
C29	09°01'43"	320.00	50.43
C30	06°39'42"	223.00	33.71
C31	00°37'44"	223.00	2.45
C32	15°49'08"	200.00	55.22
C33	10°14'48"	320.00	57.22
C34	01°32'58"	320.00	6.85
C35	01°08'19"	200.00	3.97
C36	72°14'46"	47.00	58.26
C37	54°21'16"	47.00	44.58
C38	62°10'04"	45.00	48.83
C39	07°53'30"	47.00	6.47
C40	38°37'43"	47.00	32.51
C41	06°50'03"	47.00	5.61

NOTE:
SEE SHEET 2 FOR BASIS OF BEARINGS, DATUM STATEMENT, MONUMENT NOTES, EASEMENT NOTES,
SURVEYOR'S NOTES, NOTES, AND VICINITY MAP AND GCS CONTROL SCHEME.