

TRACT NO. 16347

ACCEPTED AND FILED AT THE
REQUEST OF

FIDELITY NATIONAL TITLE COMPANY

ALL OF VESTING TENTATIVE TRACT
MAP NO. 16347
TOTAL LOTS: NUMBERED LOTS 1 THROUGH 65
AND LETTERED LOTS A THROUGH V
TOTAL ACREAGE: 9.319 ACRES

IN THE UNINCORPORATED TERRITORY OF THE COUNTY OF ORANGE,
STATE OF CALIFORNIA

BEING A SUBDIVISION OF LOT 13, AS SHOWN ON TRACT NO. 16341
FILED IN BOOK 840, PAGES 1 THROUGH 20 OF MISCELLANEOUS MAPS,
IN THE OFFICE OF THE COUNTY RECORDER OF SAID COUNTY, STATE OF CALIFORNIA

ADAMS - STREETER CIVIL ENGINEERS, INC. JAN A. ADAMS, R.C.E. 21687

DATE OF SURVEY: APRIL, 2003

DATE SEPTEMBER 19, 2003TIME 08:46 AM FEE \$ 23.00INSTRUMENT # 2003001150117BOOK 849 PAGE 31-31 1/2TOM DALY
COUNTY CLERK-RECORDERBY [Signature]
DEPUTY

OWNERSHIP CERTIFICATE

WE, THE UNDERSIGNED, BEING ALL PARTIES HAVING ANY RECORD TITLE INTEREST IN THE LAND COVERED
BY THIS MAP, DO HEREBY CONSENT TO THE PREPARATION AND RECORDATION OF SAID MAP, AS SHOWN
WITHIN THE DISTINCTIVE BORDER LINE.

WE HEREBY DEDICATE TO THE COUNTY OF ORANGE:

1. AN EASEMENT FOR EMERGENCY AND PUBLIC SERVICE VEHICULAR INGRESS-EGRESS PURPOSES
AS SHOWN ON THIS MAP.

WE ALSO DEDICATE TO THE SANTA MARGARITA WATER DISTRICT, THE EASEMENTS FOR SEWER, WATER
PIPELINE AND ACCESS PURPOSES AS SHOWN ON THIS MAP, WHICH EASEMENTS SHALL BE SUBJECT TO
THE SAME TERMS AND CONDITIONS AS ARE SHOWN IN THAT CERTAIN EASEMENT RECORDED OCTOBER 6,
1980, IN BOOK 13776, PAGE 341, OF OFFICIAL RECORDS, COUNTY OF ORANGE.

WILLIAM LYON HOMES, INC., A CALIFORNIA CORPORATION

BY: [Signature]
PRINT NAME: Gary S. Wangler
PRINT TITLE: Vice President

BY: [Signature]
PRINT NAME: Thomas G. Grable
PRINT TITLE: Assistant Secretary

RESIDENTIAL FUNDING CORPORATION, A DELAWARE CORPORATION, BENEFICIARY UNDER A
DEED OF TRUST RECORDED APRIL 4, 2003 AS INSTRUMENT NO. 2003000372402 OF OFFICIAL RECORDS.

BY: [Signature]
PRINT NAME: DONALD V. PIERCE
PRINT TITLE: MANAGING DIRECTOR

BY: [Signature]
PRINT NAME: MICHAEL FRANTA
PRINT TITLE: MANAGING DIRECTOR

DMB LADERA, LLC, A DELAWARE LIMITED LIABILITY COMPANY, BENEFICIARY UNDER A DEED OF
TRUST RECORDED APRIL 4, 2003 AS INSTRUMENT NO. 2003000372402 OF OFFICIAL RECORDS.

BY: [Signature]
PRINT NAME: DONALD T. SPARKIN
PRINT TITLE: VICE PRESIDENT

BY: [Signature]
PRINT NAME: PAUL JOHNSON
PRINT TITLE: SENIOR VICE PRESIDENT

STATE OF CALIFORNIA)
COUNTY OF ORANGE)

ON THIS 30th DAY OF June, 2003, BEFORE ME, Diana L. Birks A NOTARY
PUBLIC IN AND FOR SAID STATE, PERSONALLY APPEARED Donald T. Sparkin AND Paul Johnson
PERSONALLY KNOWN TO ME (OR PROVED TO ME ON THE BASIS OF SATISFACTORY EVIDENCE) TO BE
THE PERSONS WHOSE NAMES ARE SUBSCRIBED TO THE WITHIN INSTRUMENT AND ACKNOWLEDGED TO ME
THAT THEY EXECUTED THE SAME IN THEIR AUTHORIZED CAPACITIES, AND THAT BY THEIR SIGNATURES ON
THE INSTRUMENT THE PERSONS, OR THE ENTITY UPON BEHALF OF WHICH THE PERSONS ACTED, EXECUTED
THE INSTRUMENT.

WITNESS MY HAND:

Diana L. Birks
NOTARY PUBLIC IN AND FOR SAID STATE
Diana L. Birks
PRINT NAME

MY PRINCIPAL PLACE OF BUSINESS
IS IN Orange COUNTY

MY COMMISSION EXPIRES December 12, 2006

STATE OF California)
COUNTY OF Orange)

ON THIS 23rd DAY OF June, 2003, BEFORE ME, Sheryl L. Alworth A NOTARY
PUBLIC IN AND FOR SAID STATE, PERSONALLY APPEARED Gary S. Wangler AND Thomas G. Grable
PERSONALLY KNOWN TO ME (OR PROVED TO ME ON THE BASIS OF SATISFACTORY EVIDENCE) TO BE
THE PERSONS WHOSE NAMES ARE SUBSCRIBED TO THE WITHIN INSTRUMENT AND ACKNOWLEDGED TO ME
THAT THEY EXECUTED THE SAME IN THEIR AUTHORIZED CAPACITIES, AND THAT BY THEIR SIGNATURES ON
THE INSTRUMENT THE PERSONS, OR THE ENTITY UPON BEHALF OF WHICH THE PERSONS ACTED, EXECUTED
THE INSTRUMENT.

WITNESS MY HAND:

Sheryl L. Alworth
NOTARY PUBLIC IN AND FOR SAID STATE
Sheryl L. Alworth
PRINT NAME

MY PRINCIPAL PLACE OF BUSINESS
IS IN Orange COUNTY

MY COMMISSION EXPIRES January 12, 2006

STATE OF CALIFORNIA) Minnesota
COUNTY OF Orange) Hennepin

ON THIS 24 DAY OF June, 2003, BEFORE ME, Kari J. Miller A NOTARY
PUBLIC IN AND FOR SAID STATE, PERSONALLY APPEARED Donald T. Sparkin AND Michael Franta
PERSONALLY KNOWN TO ME (OR PROVED TO ME ON THE BASIS OF SATISFACTORY EVIDENCE) TO BE
THE PERSONS WHOSE NAMES ARE SUBSCRIBED TO THE WITHIN INSTRUMENT AND ACKNOWLEDGED TO ME
THAT THEY EXECUTED THE SAME IN THEIR AUTHORIZED CAPACITIES, AND THAT BY THEIR SIGNATURES ON
THE INSTRUMENT THE PERSONS, OR THE ENTITY UPON BEHALF OF WHICH THE PERSONS ACTED, EXECUTED
THE INSTRUMENT.

WITNESS MY HAND:

Kari J. Miller
NOTARY PUBLIC IN AND FOR SAID STATE
Kari Miller
PRINT NAME

MY PRINCIPAL PLACE OF BUSINESS
IS IN Hennepin COUNTY


MY COMMISSION EXPIRES Jan 31, 2006

SEE SHEET 2 FOR SIGNATURE OMISSIONS

ENGINEER'S STATEMENT

THIS MAP WAS PREPARED BY ME OR UNDER MY DIRECTION AND IS BASED UPON A FIELD SURVEY IN
CONFORMANCE WITH THE REQUIREMENTS OF THE SUBDIVISION MAP ACT AND LOCAL ORDINANCE AT
THE REQUEST OF DMB LADERA, LLC, IN APRIL, 2003. I HEREBY STATE THAT ALL MONUMENTS
ARE OF THE CHARACTER AND OCCUPY THE POSITIONS INDICATED, OR THAT THEY WILL BE SET
IN SUCH POSITIONS; AND THAT SAID MONUMENTS ARE SUFFICIENT TO ENABLE THE SURVEY TO BE
RETRACTED. I HEREBY STATE THAT THIS FINAL MAP SUBSTANTIALLY CONFORMS TO THE CONDITIONALLY
APPROVED TENTATIVE MAP.

[Signature]
JAN A. ADAMS, R.C.E. 21687
EXPIRES: 9/30/05

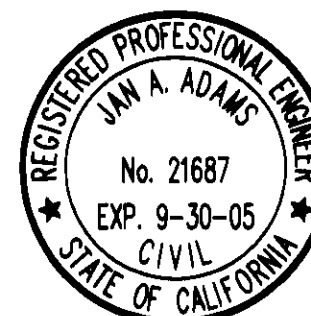


COUNTY SURVEYOR'S STATEMENT

I HEREBY STATE THAT I HAVE EXAMINED THIS MAP AND HAVE FOUND IT TO BE SUBSTANTIALLY IN
CONFORMANCE WITH THE TENTATIVE MAP AS FILED WITH, AMENDED AND APPROVED BY THE ORANGE
COUNTY SUBDIVISION COMMITTEE; THAT ALL PROVISIONS OF THE SUBDIVISION MAP ACT AND COUNTY
SUBDIVISION REGULATIONS HAVE BEEN COMPLIED WITH AND I AM SATISFIED SAID MAP IS TECHNICALLY
CORRECT.

DATED THIS 2nd DAY OF September, 2003

[Signature]
JOHN CANAS COUNTY SURVEYOR
LS 4408 EXPIRATION DATE: 9-30-05

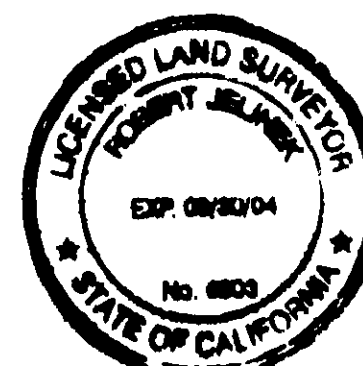

COUNTY TREASURER - TAX COLLECTOR'S CERTIFICATE

STATE OF CALIFORNIA)
COUNTY OF ORANGE)

I HEREBY CERTIFY THAT ACCORDING TO THE RECORDS OF MY OFFICE, THERE ARE NO LIENS AGAINST THE
LAND COVERED BY THIS MAP OR ANY PART THEREOF FOR UNPAID STATE, COUNTY, MUNICIPAL OR LOCAL
TAXES OR SPECIAL ASSESSMENTS COLLECTED AS TAXES, EXCEPT TAXES OR SPECIAL ASSESSMENTS
COLLECTED AS TAXES NOT YET PAYABLE.

AND DO ALSO CERTIFY TO THE RECORDER OF ORANGE COUNTY THAT THE PROVISIONS OF THE
SUBDIVISION MAP ACT HAVE BEEN COMPLIED WITH REGARDING DEPOSITS TO SECURE PAYMENT OF
TAXES OR SPECIAL ASSESSMENTS COLLECTED AS TAXES ON THE LAND COVERED BY THIS MAP.

DATED THIS 21st DAY OF August, 2003

JOHN M. W. MOORLACH
COUNTY TREASURER - TAX COLLECTOR

BY: [Signature]
DEPUTY TREASURER - TAX COLLECTOR

CLERK OF THE BOARD OF SUPERVISORS CERTIFICATE

STATE OF CALIFORNIA)
COUNTY OF ORANGE)


I HEREBY CERTIFY THAT THIS MAP WAS PRESENTED FOR APPROVAL TO THE BOARD OF SUPERVISORS OF
ORANGE COUNTY AT A REGULAR MEETING THEREOF HELD ON THE 16th DAY OF September
2003, AND THAT THEREUPON SAID BOARD DID, BY AN ORDER DULY PASSED AND ENTERED, APPROVE
SAID MAP.

AND DID ACCEPT ON BEHALF OF THE COUNTY OF ORANGE:

1. THE EASEMENT FOR EMERGENCY AND PUBLIC SERVICE VEHICULAR INGRESS-EGRESS, AS DEDICATED.

DATED THIS 16th DAY OF September, 2003.

[Signature]
DARLENE J. BLOOM, CLERK OF THE BOARD OF SUPERVISORS

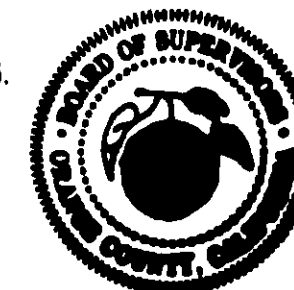

CERTIFICATE OF ACCEPTANCE

THE UNDERSIGNED, BEING THE DULY APPOINTED AGENT OF THE SANTA MARGARITA WATER DISTRICT,
A PUBLIC CORPORATION OF ORANGE COUNTY, CALIFORNIA, PURSUANT TO ITS RESOLUTION NO. 88-10-2,
DOES HEREBY ACCEPT ON BEHALF OF SAID DISTRICT THE EASEMENTS FOR SEWER, WATER AND ACCESS
PURPOSES, AS DEDICATED AND AS SHOWN ON THIS TRACT MAP, BY AND BETWEEN THE SANTA MARGARITA
WATER DISTRICT AND DMB LADERA, LLC, AND DOES HEREBY CERTIFY THAT THE GRANTEE CONSENTS
TO THE RECORDATION OF SAID TRACT.

BY: [Signature]
DANIEL R. FERONS, CHIEF ENGINEER
SANTA MARGARITA WATER DISTRICT

STATE OF CALIFORNIA)
COUNTY OF ORANGE)

ON THIS 11th DAY OF July, 2003, BEFORE ME, Andrea M. Evans A NOTARY
PUBLIC IN AND FOR SAID STATE, PERSONALLY APPEARED Daniel Ferons, PERSONALLY KNOWN TO ME
(OR PROVED TO ME ON THE BASIS OF SATISFACTORY EVIDENCE) TO BE THE PERSON WHOSE NAME IS
SUBSCRIBED TO THE WITHIN INSTRUMENT AND ACKNOWLEDGED TO ME THAT HE EXECUTED THE SAME IN
HIS AUTHORIZED CAPACITY AND THAT BY HIS SIGNATURE ON THE INSTRUMENT THE PERSON, OR THE
ENTITY UPON BEHALF OF WHICH THE PERSON ACTED, EXECUTED THE INSTRUMENT.

WITNESS MY HAND:

[Signature]
NOTARY PUBLIC IN AND FOR SAID STATE
Andrea M. Evans
PRINT NAME

MY PRINCIPAL PLACE OF BUSINESS
IS IN ORANGE COUNTY

MY COMMISSION EXPIRES April 8, 2004

TRACT NO. 16347

ALL OF VESTING TENTATIVE TRACT
MAP NO. 16347

TOTAL LOTS: NUMBERED LOTS 1 THROUGH 65
AND LETTERED LOTS A THROUGH V
TOTAL ACREAGE: 9.319 ACRES

IN THE UNINCORPORATED TERRITORY OF THE COUNTY OF ORANGE,
STATE OF CALIFORNIA

ADAMS - STREETER CIVIL ENGINEERS, INC. JAN A. ADAMS, R.C.E. 21687
DATE OF SURVEY: APRIL, 2003

BASIS OF BEARINGS

THE BEARINGS SHOWN HEREON ARE BASED ON THE BEARING BETWEEN ORANGE COUNTY SURVEYOR'S HORIZONTAL CONTROL STATION GPS NO. 1417 AND STATION GPS NO. 1448 BEING N10°48'13"E PER TRACT NO. 16341, MM 840/1-20, RECORDS OF ORANGE COUNTY, CALIFORNIA.

DATUM STATEMENT

COORDINATES SHOWN ARE BASED ON THE CALIFORNIA COORDINATE SYSTEM (CCS83), ZONE VI, 1983 NAD (1991.35 EPOCH O.C.S. GPS ADJUSTMENT).

ALL DISTANCES SHOWN ARE GROUND, UNLESS OTHERWISE NOTED. TO OBTAIN GRID DISTANCES MULTIPLY THE GROUND DISTANCE BY THE COMBINATION FACTOR 0.999948295 SPECIFIC TO THIS PROJECT.

MONUMENT NOTES

- ③ INDICATES FOUND O.C.S. HORIZONTAL CONTROL STATION AS NOTED.
- INDICATES LOCATION OF 2" IRON PIPE TAGGED "P.L.S. 5557", OR SPIKE AND WASHER STAMPED "P.L.S. 5557", OR LEAD, TACK AND TAG "P.L.S. 5557" TO BE SET PER TRACT NO. 16341, MM 840/1-20.
- INDICATES LOCATION OF 1" IRON PIPE TAGGED "P.L.S. 5557", OR SPIKE AND WASHER STAMPED "P.L.S. 5557", OR LEAD, TACK AND TAG "P.L.S. 5557" TO BE SET PER TRACT NO. 16341, MM 840/1-20, UNLESS OTHERWISE NOTED.
- INDICATES SET 2" IRON PIPE TAGGED "RCE 21687" PRIOR TO RECORDATION OF THIS MAP.
- 2" IRON PIPE TAGGED "RCE 21687", OR SPIKE AND WASHER STAMPED "RCE 21687", OR LEAD, TACK AND TAG STAMPED "RCE 21687", OR NAIL AND TAG STAMPED "RCE 21687", OR A TAG STAMPED "RCE 21687" SECURED WITH EPOXY TO BE SET AT ALL TRACT BOUNDARY CORNERS, UNLESS OTHERWISE NOTED.
- 1" IRON PIPE TAGGED "RCE 21687", OR SPIKE AND WASHER STAMPED "RCE 21687", OR LEAD, TACK AND TAG STAMPED "RCE 21687", OR NAIL AND TAG STAMPED "RCE 21687", OR A TAG STAMPED "RCE 21687" SECURED WITH EPOXY TO BE SET AT ALL CORNERS, EXCEPT AT THOSE LOT CORNERS:
 - THAT ADJUT A SIDEWALK, IN WHICH CASE, LEAD, TACK AND TAG STAMPED "RCE 21687" WILL BE SET ON THE PROLONGATION OF THE SIDE LOT LINE, 0.50 FEET FROM THE TRUE LOT CORNER, IN THE ADJACENT CONCRETE SIDEWALK;
 - THAT ARE LOCATED IN THE FACE OF THE CONCRETE CURB, IN WHICH CASE, LEAD, TACK AND TAG STAMPED "RCE 21687" WILL BE SET ON THE SIDE LOT LINE, 0.25 FEET FROM THE TRUE LOT CORNER, IN THE TOP OF THE CONCRETE CURB, AND;
 - THAT ARE OBSTRUCTED BY ANY PHYSICAL IMPROVEMENT THAT PREVENTS THE SETTING OF THE ABOVE MENTIONED MONUMENTS, IN WHICH CASE, ONE OF THOSE MONUMENTS WILL BE SET ON THE PROLONGATION OF THE SIDE LOT LINE, 1.0 FOOT FROM THE TRUE LOT CORNER.
- 8" SPIKE AND WASHER STAMPED "RCE 21687" TO BE SET AT ALL STREET CENTERLINE POINTS OF CONTROL, UNLESS OTHERWISE NOTED.
- ALL MONUMENTS WILL BE SET WITHIN 90 DAYS AFTER THE ACCEPTANCE OF IMPROVEMENTS.
- ALL TRACT BOUNDARY DATA IS MEASURED AND RECORD PER TRACT NO. 16341, MM 840/1-20, UNLESS OTHERWISE NOTED.

EASEMENT NOTES

- AN EASEMENT FOR EMERGENCY AND PUBLIC SERVICE VEHICULAR INGRESS-EGRESS DEDICATED TO THE COUNTY OF ORANGE.
- AN EASEMENT FOR SEWER, WATER PIPELINE AND ACCESS PURPOSES DEDICATED TO THE SANTA MARGARITA WATER DISTRICT.

LOT TABULATION

LOT A	PRIVATE STREET	0.736	ACRES	LOT L	OPEN SPACE	0.298	ACRES
LOT B	PRIVATE DRIVE	0.055	ACRES	LOT M	OPEN SPACE	0.275	ACRES
LOT C	PRIVATE DRIVE	0.233	ACRES	LOT N	OPEN SPACE	0.220	ACRES
LOT D	PRIVATE DRIVE	0.138	ACRES	LOT O	OPEN SPACE	0.080	ACRES
LOT E	PRIVATE DRIVE	0.130	ACRES	LOT P	OPEN SPACE	0.171	ACRES
LOT F	PRIVATE DRIVE	0.107	ACRES	LOT Q	OPEN SPACE	0.218	ACRES
LOT G	PRIVATE DRIVE	0.142	ACRES	LOT R	OPEN SPACE	0.126	ACRES
LOT H	PRIVATE STREET	0.183	ACRES	LOT S	OPEN SPACE	0.217	ACRES
LOT I	PRIVATE DRIVE	0.277	ACRES	LOT T	OPEN SPACE	0.249	ACRES
LOT J	PRIVATE DRIVE	0.086	ACRES	LOT U	OPEN SPACE	0.074	ACRES
LOT K	PRIVATE DRIVE	0.122	ACRES	LOT V	OPEN SPACE	0.014	ACRES

NOTES

- LETTERED LOTS ARE NOT SEPARATE BUILDING SITES.
- LOTS SHOWN AS "OPEN SPACE" ARE FOR LANDSCAPE PURPOSES AND WILL BE MAINTAINED BY THE HOMEOWNER'S ASSOCIATION.

ⓧ SHEET NUMBER

ADDITIONAL INFORMATION

PURSUANT TO THE PROVISIONS OF SECTION 66434.2 OF THE SUBDIVISION MAP ACT, THE FOLLOWING IS PROVIDED FOR INFORMATIONAL PURPOSES ONLY, AND IS NOT INTENDED TO AFFECT RECORD TITLE INTEREST:


- THIS MAP IS NOT WITHIN OR ADJOINING A SPECIAL FIRE PROTECTION AREA.
- THE PRIVATE STREETS CONSTRUCTED WITHIN THIS MAP SHALL BE OWNED, OPERATED AND MAINTAINED BY THE DEVELOPER, SUCCESSORS OR ASSIGNS. THE COUNTY OF ORANGE SHALL HAVE NO RESPONSIBILITY THEREFORE UNLESS PURSUANT TO APPROPRIATE SECTIONS OF THE STREETS AND HIGHWAYS CODE OF THE STATE OF CALIFORNIA, THE SAID PRIVATE STREETS HAVE BEEN ACCEPTED INTO THE COUNTY ROAD SYSTEM BY APPROPRIATE RESOLUTION OF THE ORANGE COUNTY BOARD OF SUPERVISORS.

SIGNATURE OMISSIONS

PURSUANT TO THE PROVISIONS OF SECTION 66436 (a) (3) (A) (C) OF THE SUBDIVISION MAP ACT, THE FOLLOWING SIGNATURES HAVE BEEN OMITTED:

LADERA DEVELOPMENT COMPANY, LLC, HOLDER OF OIL, GAS AND MINERAL RIGHTS RECORDED DECEMBER 10, 1996 AS INSTRUMENT NO. 19960624029 OF OFFICIAL RECORDS.


DMB LADERA, LLC, A DELAWARE LIMITED LIABILITY COMPANY, HOLDER OF EASEMENTS RESERVED IN THE DEED RECORDED APRIL 4, 2003 AS INSTRUMENT NO. 2003000372399 OF OFFICIAL RECORDS.

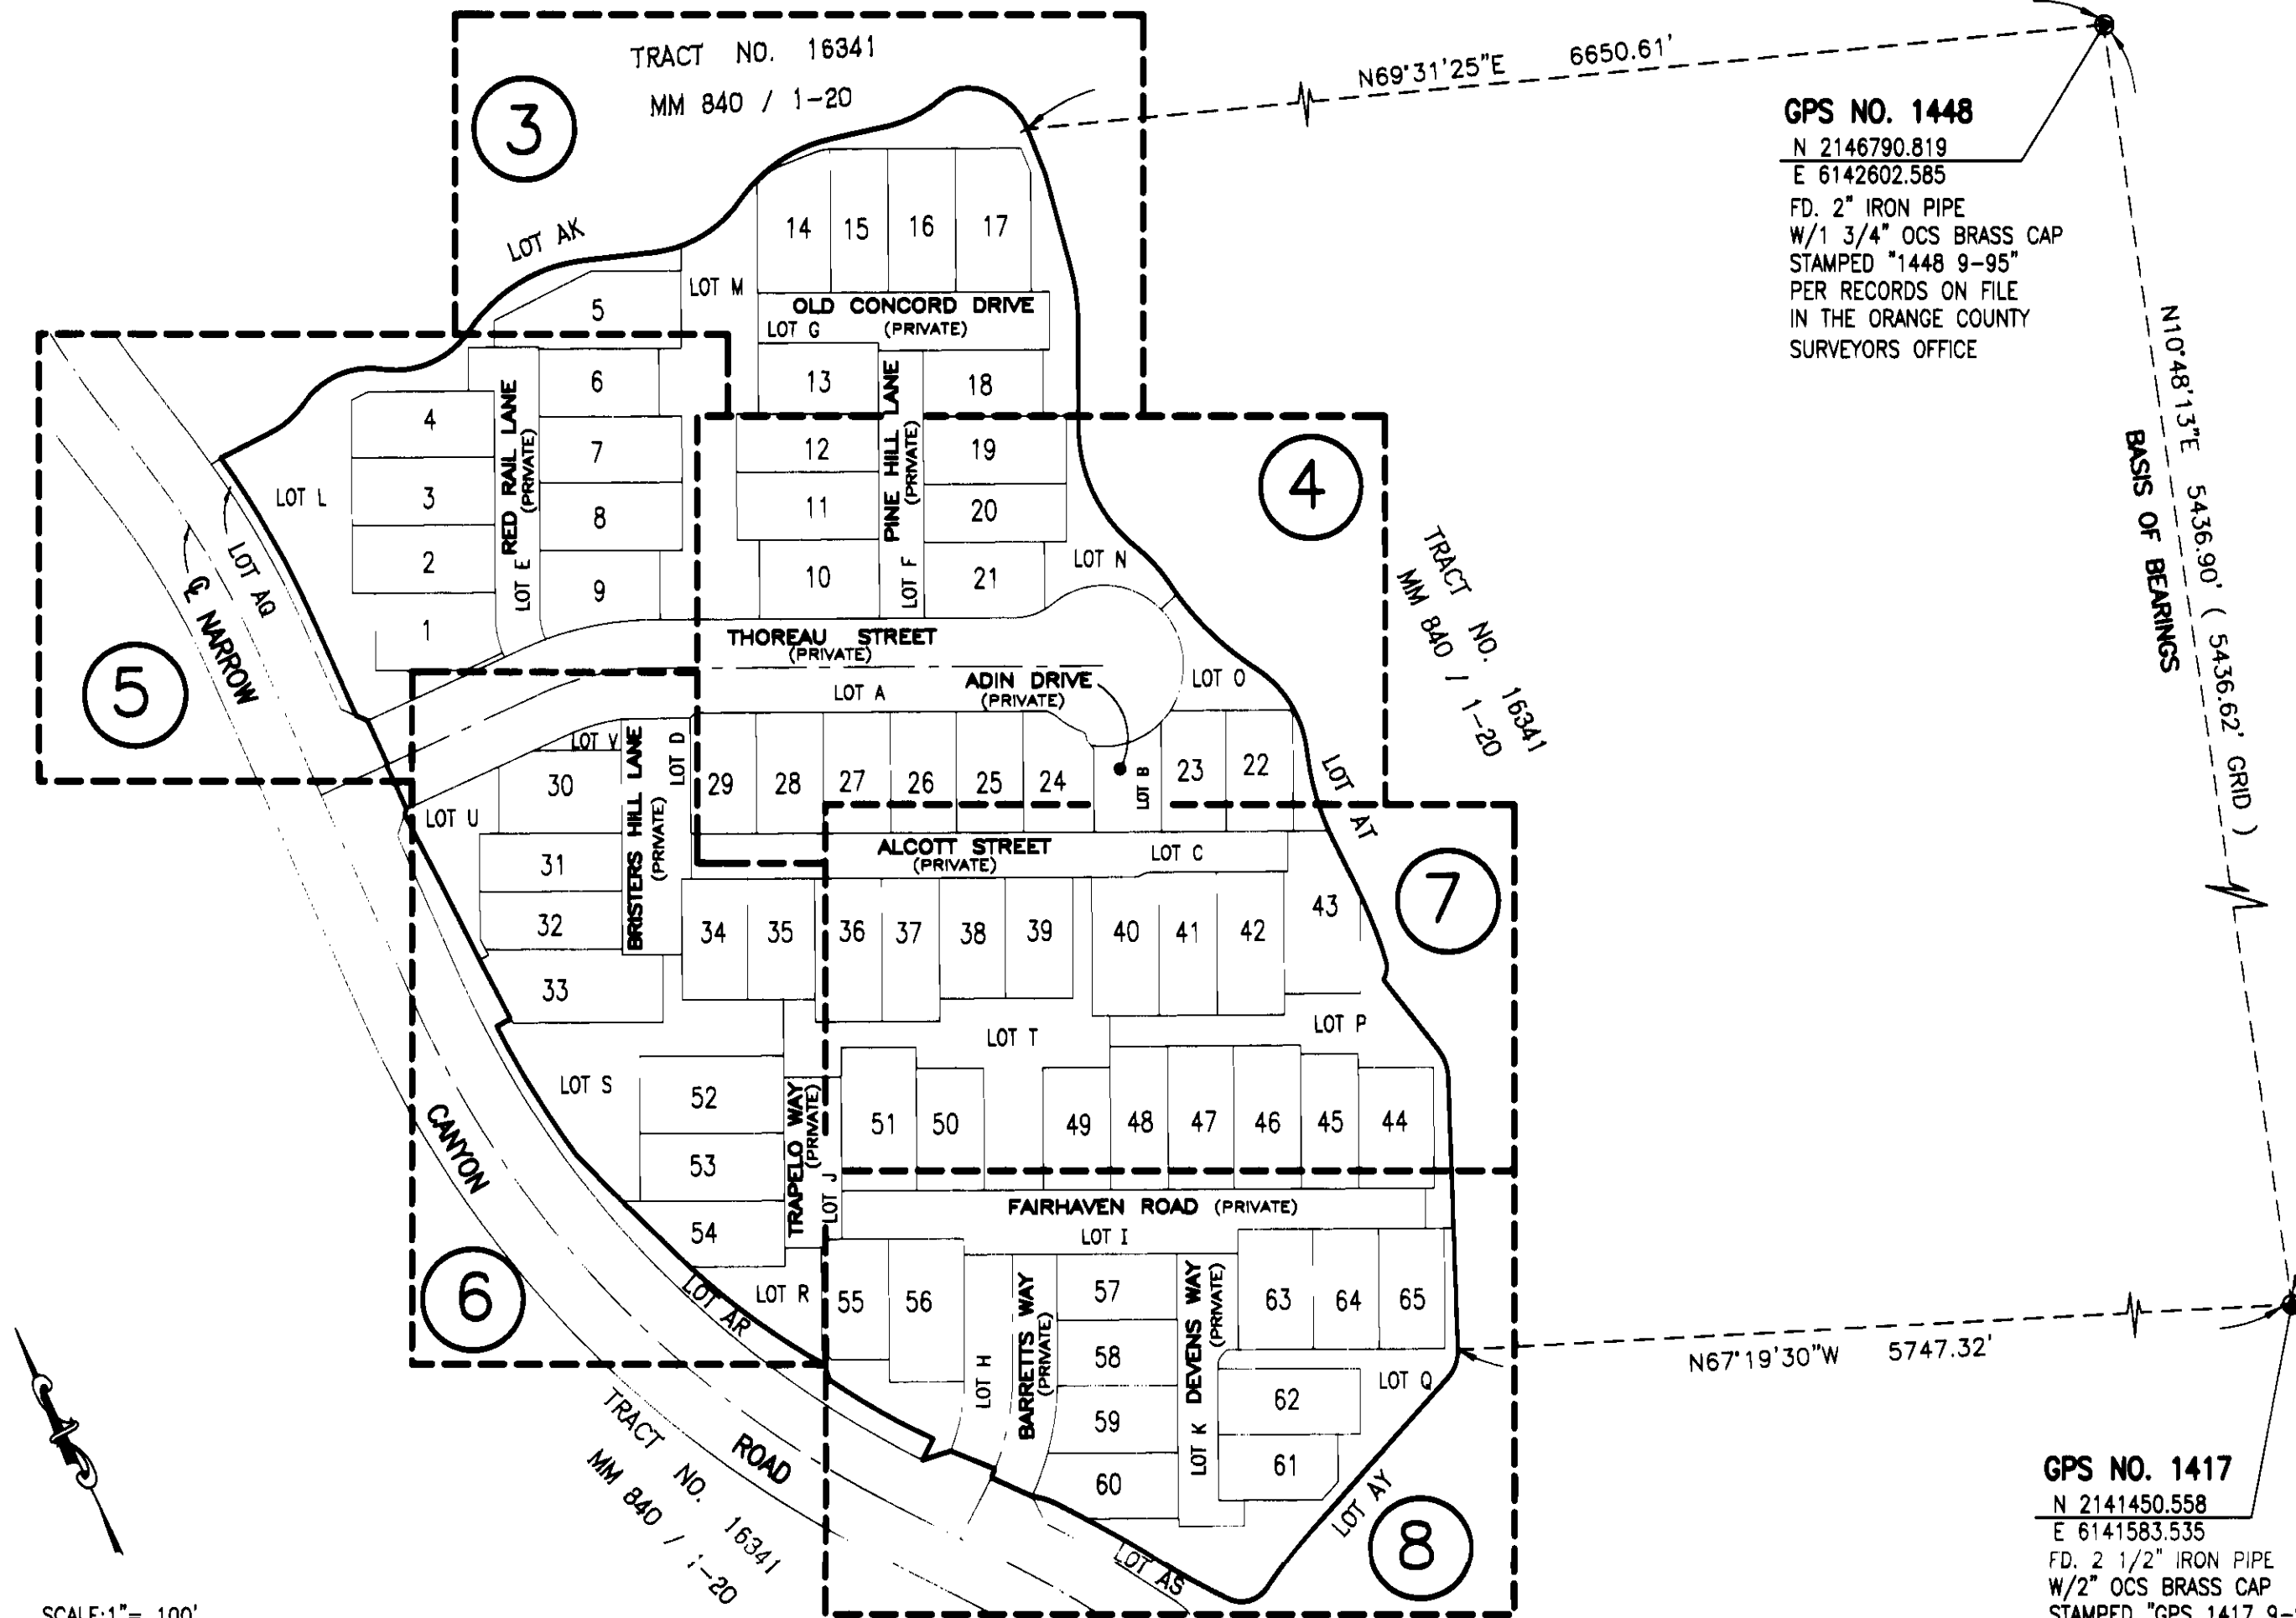


BOUNDARY CONTROL AND SHEET INDEX

SHEET 3 OF 9 SHEETS
ALL OF VESTING TENTATIVE TRACT
MAP NO. 16347
TOTAL LOTS: NUMBERED LOTS 1 THROUGH 65
AND LETTERED LOTS A THROUGH V
TOTAL ACREAGE: 9.319 ACRES

TRACT NO. 16347
IN THE UNINCORPORATED TERRITORY OF THE COUNTY OF ORANGE,
STATE OF CALIFORNIA
ADAMS - STREETER CIVIL ENGINEERS, INC. JAN A. ADAMS, R.C.E. 21687
DATE OF SURVEY: APRIL, 2003

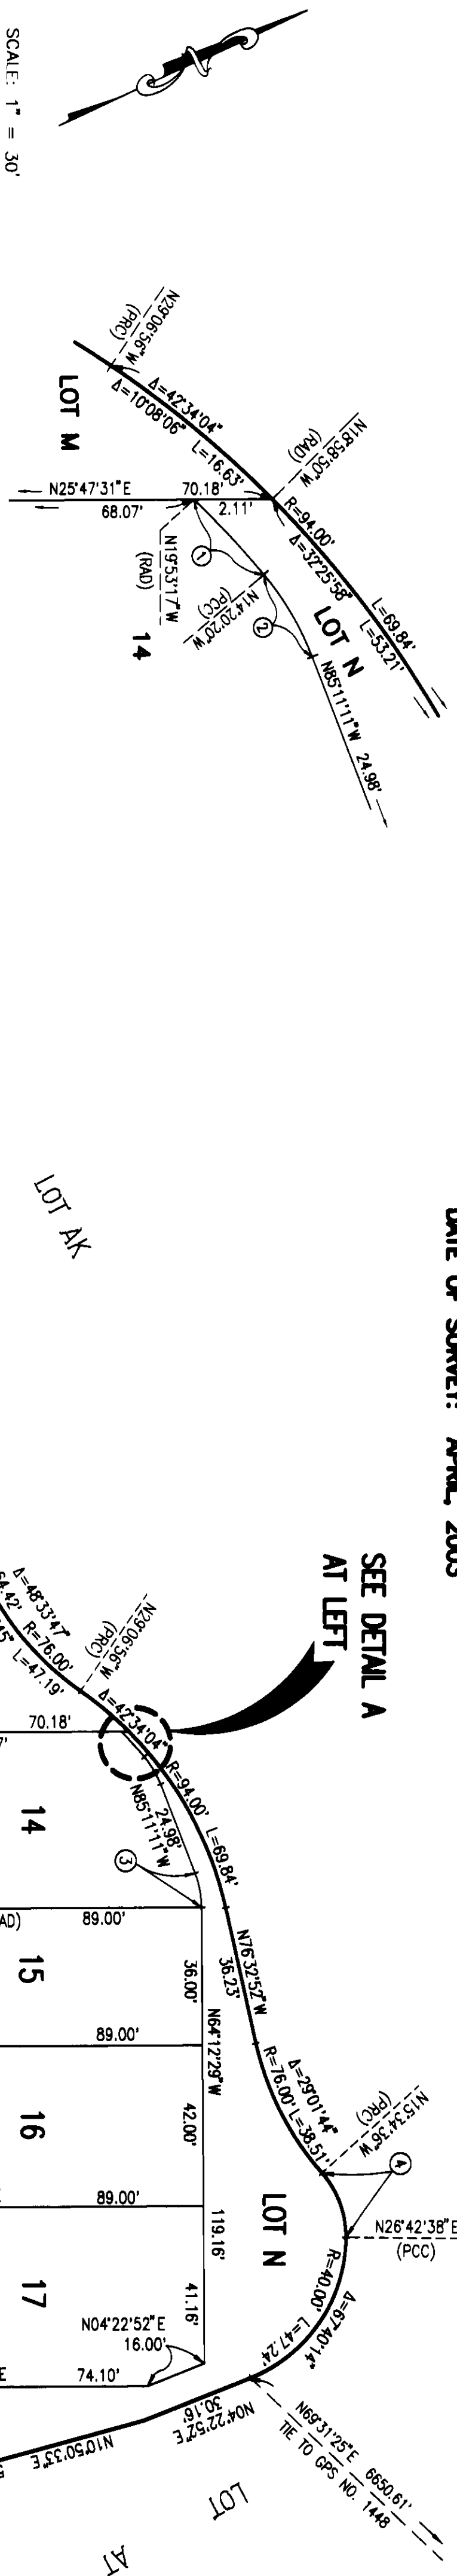

DETAIL A
NOT TO SCALE

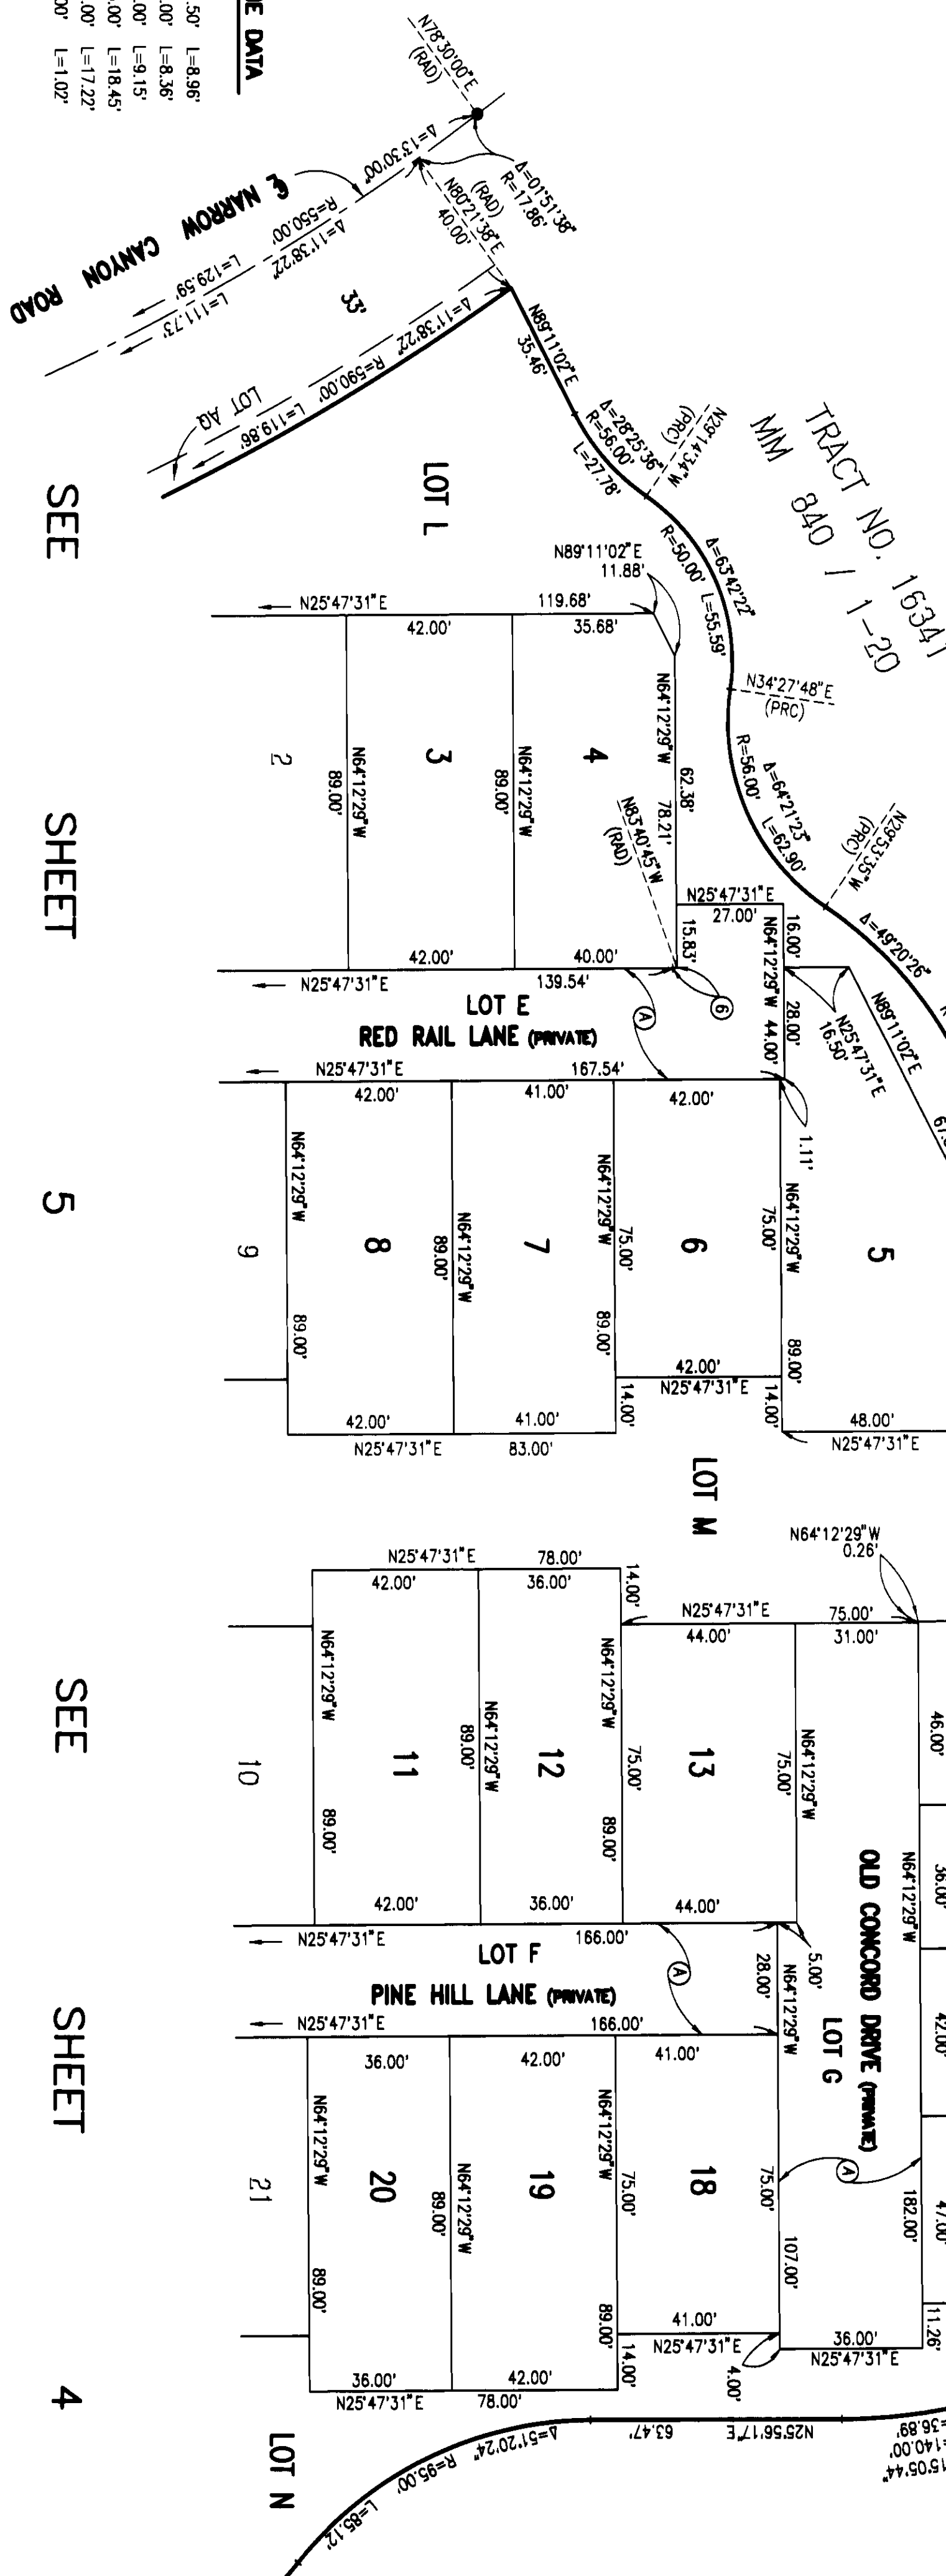

CURVE AND LINE DATA

- ①—A=05°32'57" R=92.50' L=8.96'
- ②—A=19°09'09" R=25.00' L=8.36'
- ③—A=20°58'42" R=25.00' L=9.15'
- ④—A=42°17'14" R=25.00' L=18.45'
- ⑤—A=12°59'02" R=76.00' L=17.22'
- ⑥—A=19°28'16" R=3.00' L=1.02'

NOTES:

1. SEE SHEET 2 FOR BOUNDARY CONTROL, SHEET INDEX, BASIS OF BEARINGS, DATUM STATEMENT, MONUMENT NOTES, EASEMENT NOTES AND LOT TABULATION.
2. SEE SHEET 9 FOR EASEMENT DETAILS.

SEE SHEET

5

SEE SHEET

4

SHEET 4 OF 9 SHEETS

ALL OF VESTING TENTATIVE TRACT
MAP NO. 16347
TOTAL LOTS: NUMBERED LOTS 1 THROUGH 65
AND LETTERED LOTS A THROUGH V
TOTAL ACREAGE: 9.319 ACRES


TRACT NO. 16347

IN THE UNINCORPORATED TERRITORY OF THE COUNTY OF ORANGE,

STATE OF CALIFORNIA

ADAMS - STREETER CIVIL ENGINEERS, INC. JAN A. ADAMS, R.C.E. 21687

DATE OF SURVEY: APRIL, 2003

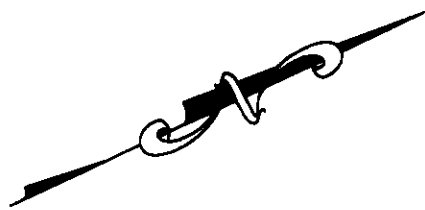


SCALE: 1" = 30'

CURVE AND LINE DATA

- ① $\Delta=10727.1'$ $L=9.12'$
- ② $\Delta=021222'$ $R=180.00'$ $L=6.93'$
- ③ $\Delta=4036.13'$ $R=3.00'$ $L=2.13'$
- ④ $\Delta=144842'$ W $2.02'$
- ⑤ $\Delta=144842'$ W $4.43'$
- ⑥ $\Delta=200915'$ E $2.58'$
- ⑦ $\Delta=655914'$ $R=3.00'$ $L=3.46'$
- ⑧ $\Delta=210132'$ $R=43.00'$ $L=15.78'$
- ⑨ $\Delta=102644'$ $R=43.00'$ $L=8.20'$
- ⑩ $\Delta=285718'$ $R=5.00'$ $L=2.53'$
- ⑪ $\Delta=314718'$ $R=10.00'$ $L=5.55'$
- ⑫ $\Delta=022647'$ $R=165.00'$ $L=7.04'$
- ⑬ $\Delta=174949'$ (RAD) $13.81'$

NOTES:

1. SEE SHEET 2 FOR BOUNDARY CONTROL, SHEET INDEX, BASIS OF BEARINGS, DATUM STATEMENT, MONUMENT NOTES, EASEMENT NOTES AND LOT TABULATION.
2. SEE SHEET 9 FOR EASEMENT DETAILS.

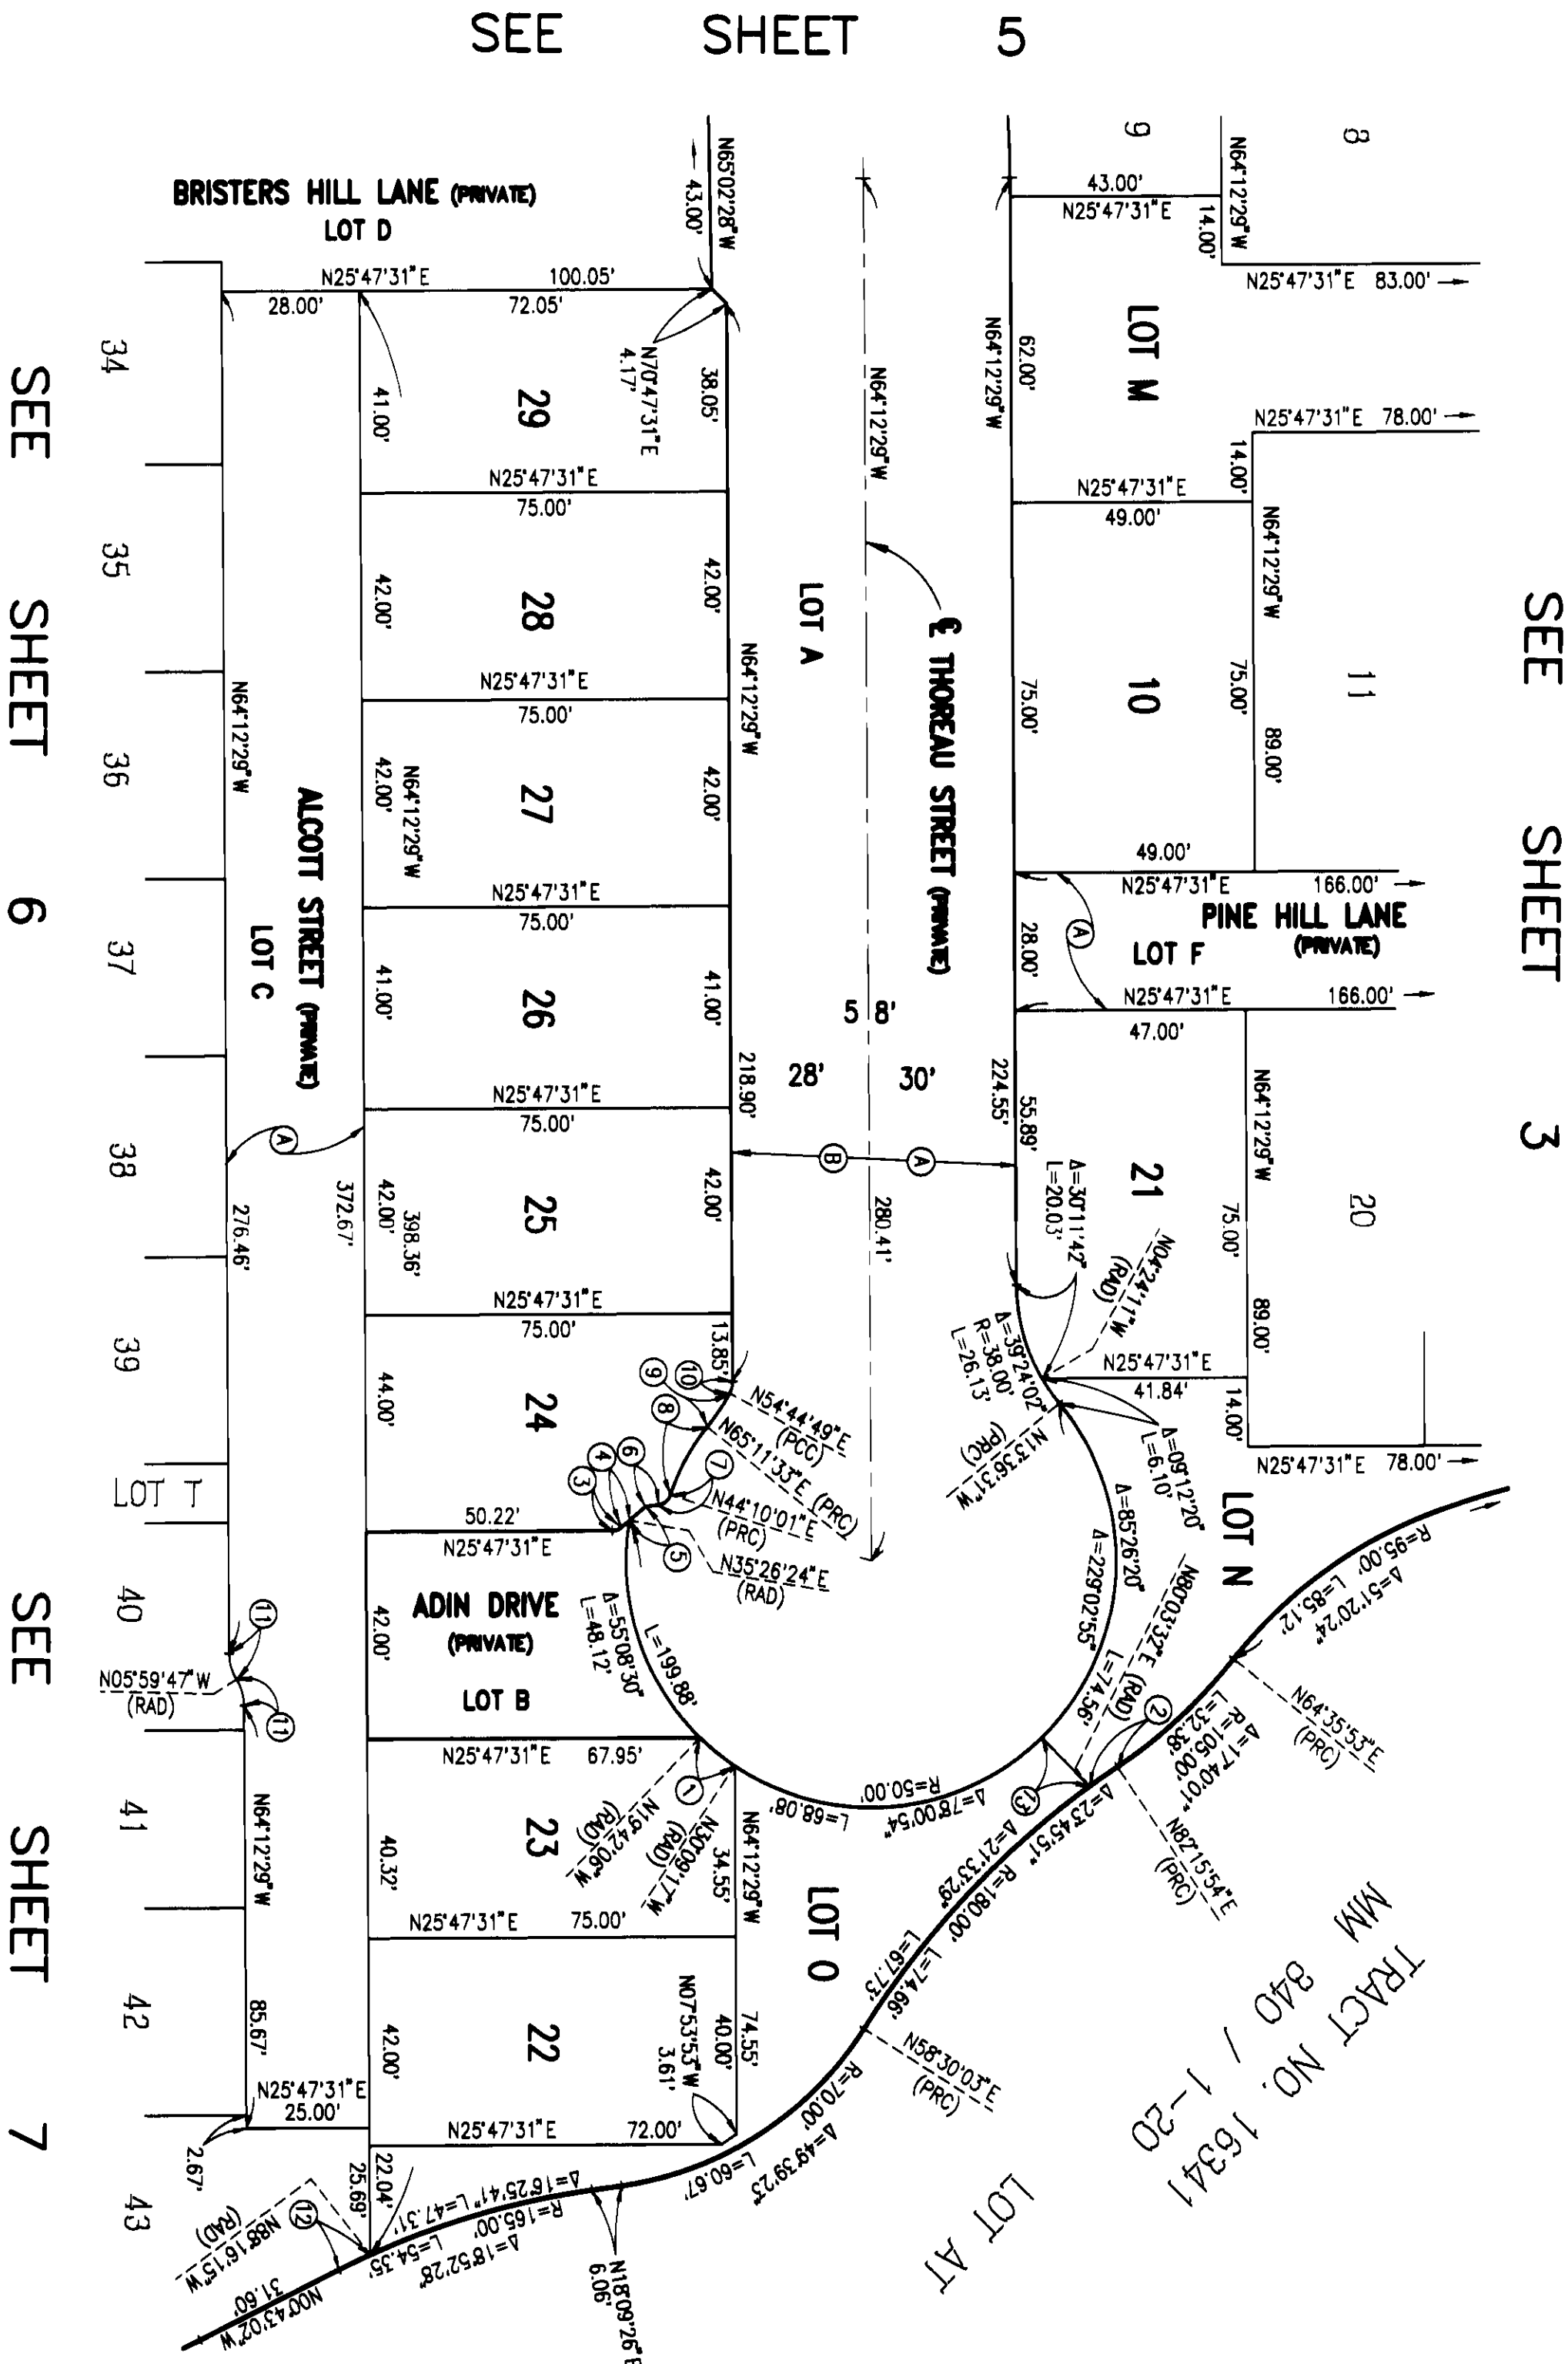

SHEET 5 OF 9 SHEETS

ALL OF VESTING TENTATIVE TRACT
MAP NO. 16347
TOTAL LOTS: NUMBERED LOTS 1 THROUGH 65
AND LETTERED LOTS A THROUGH V
TOTAL ACREAGE: 9.319 ACRES


TRACT NO. 16347

IN THE UNINCORPORATED TERRITORY OF THE COUNTY OF ORANGE,

STATE OF CALIFORNIA



ADAMS - STREETER CIVIL ENGINEERS, INC. JAN A. ADAMS, R.C.E. 21687

DATE OF SURVEY: APRIL, 2003

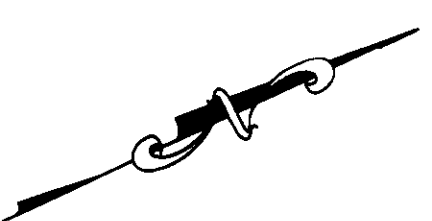

SCALE: 1" = 30'

SEE SHEET 3

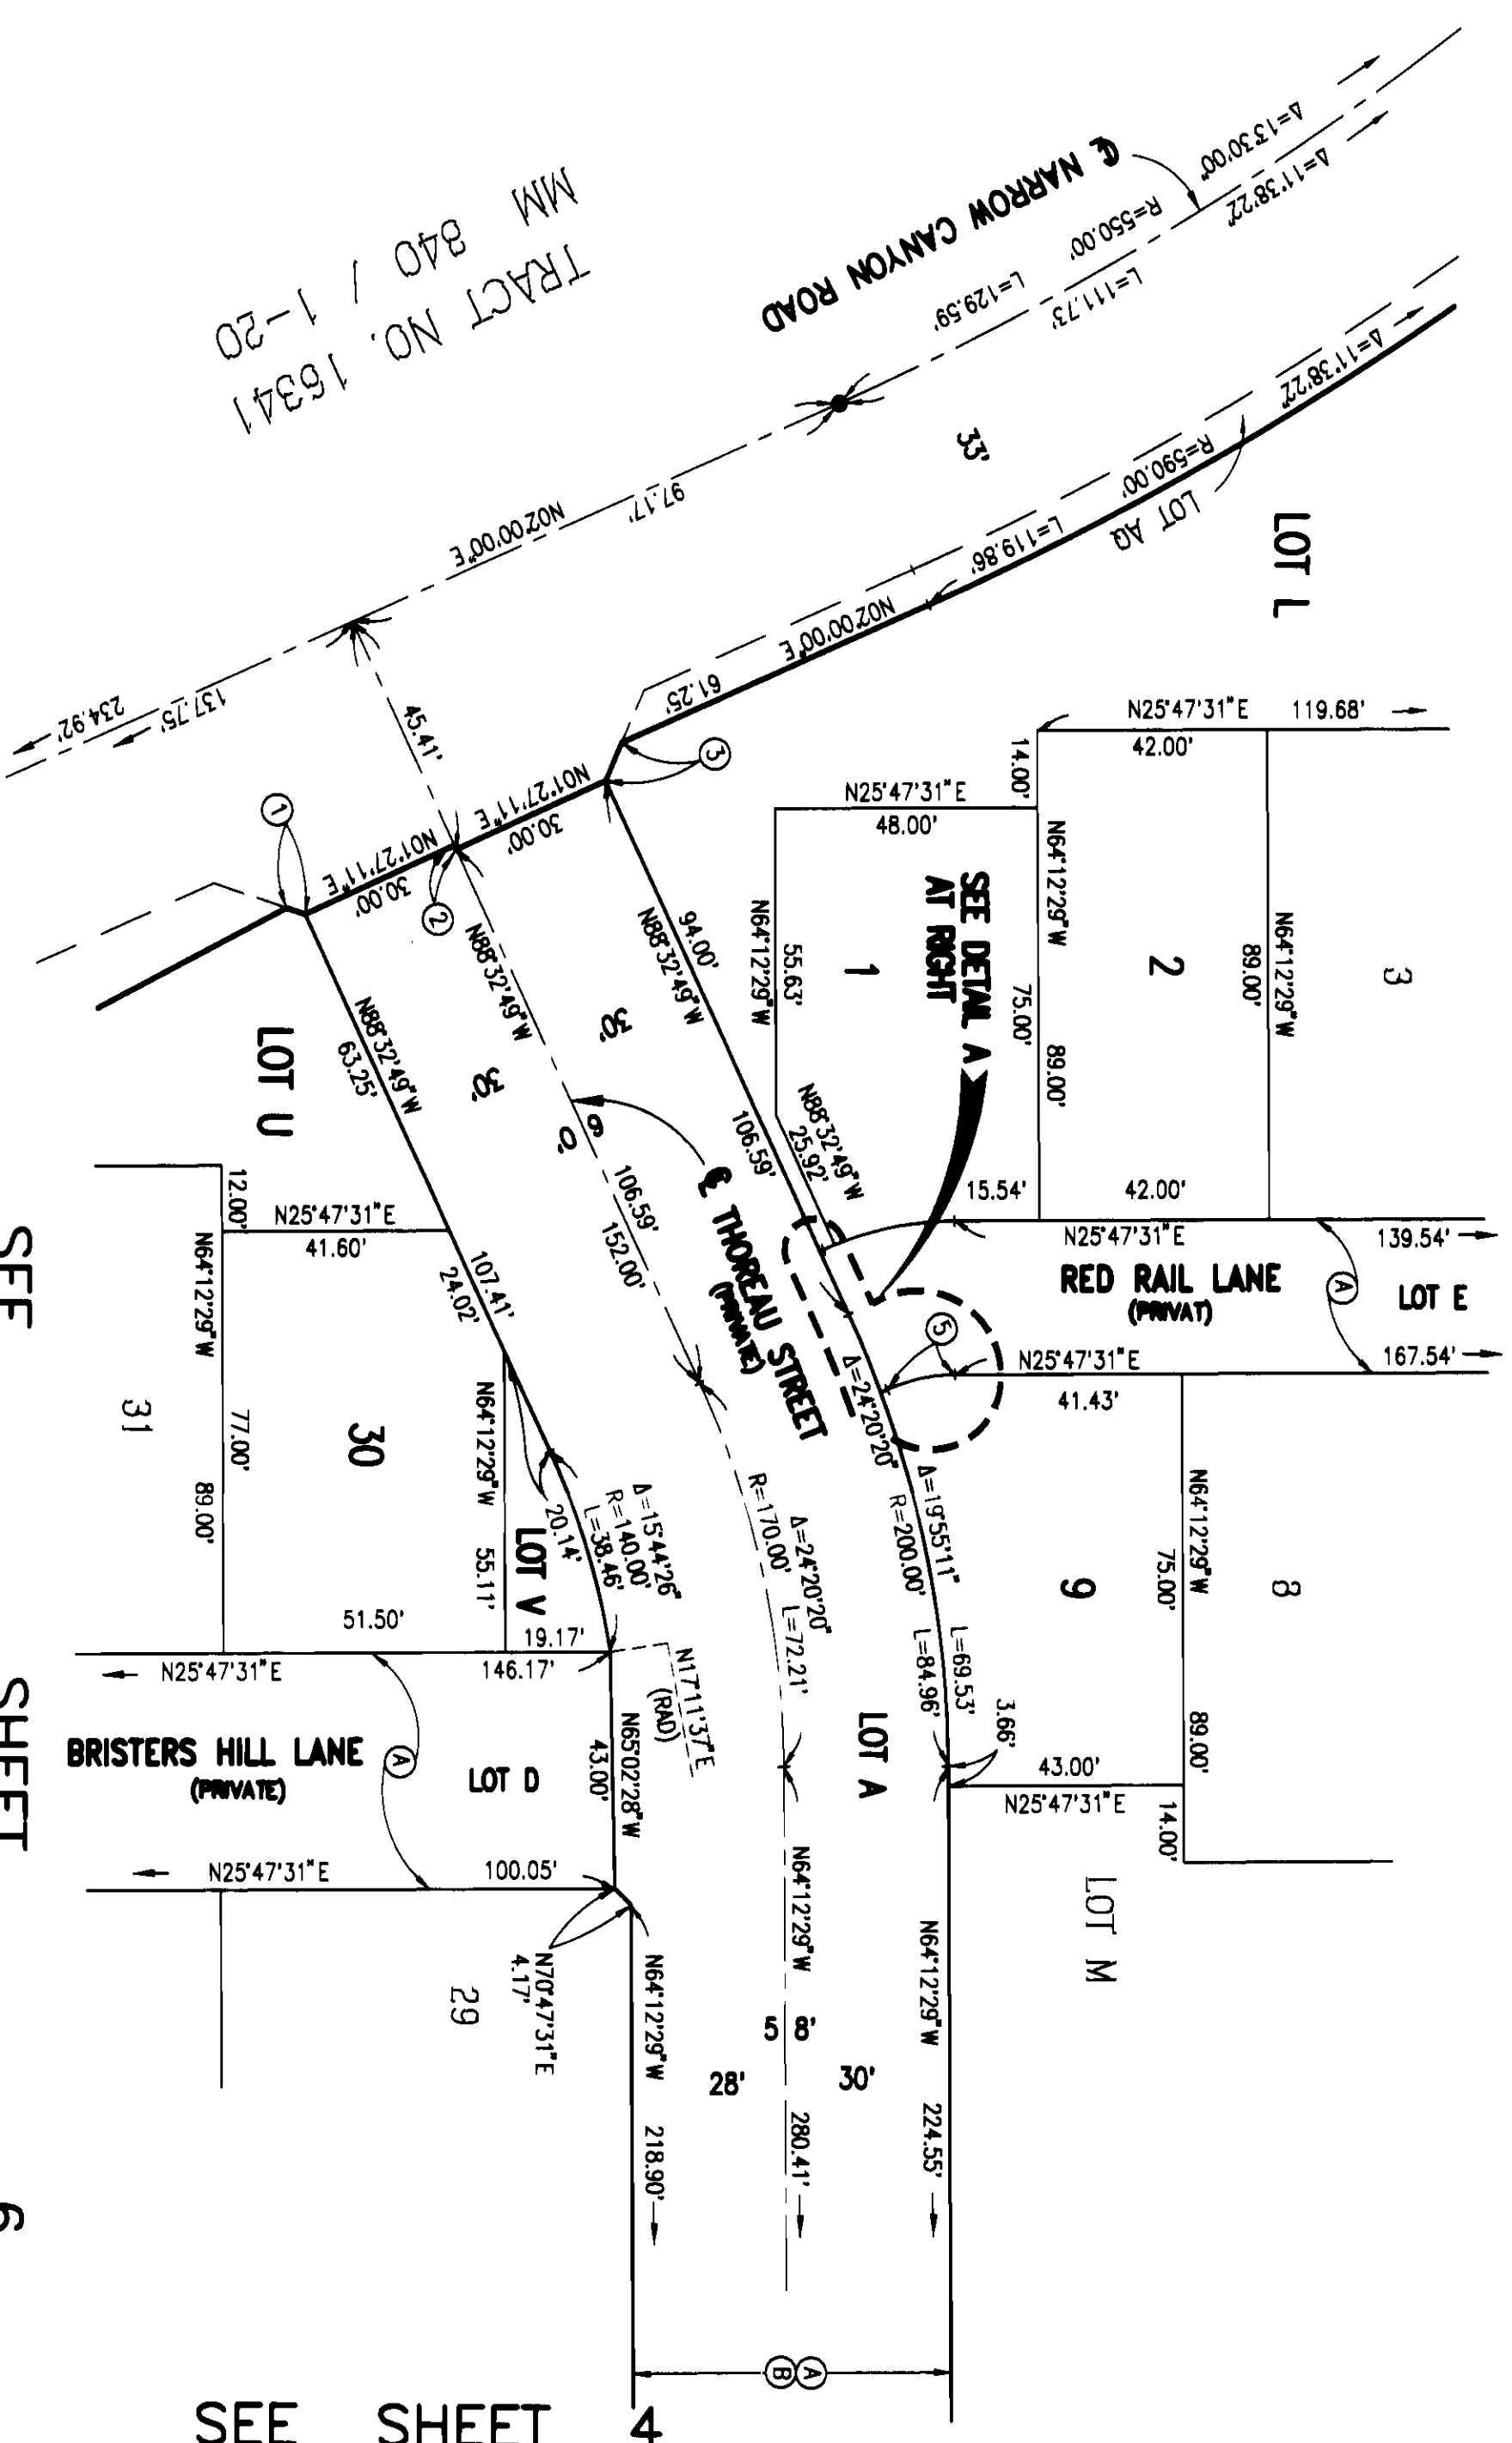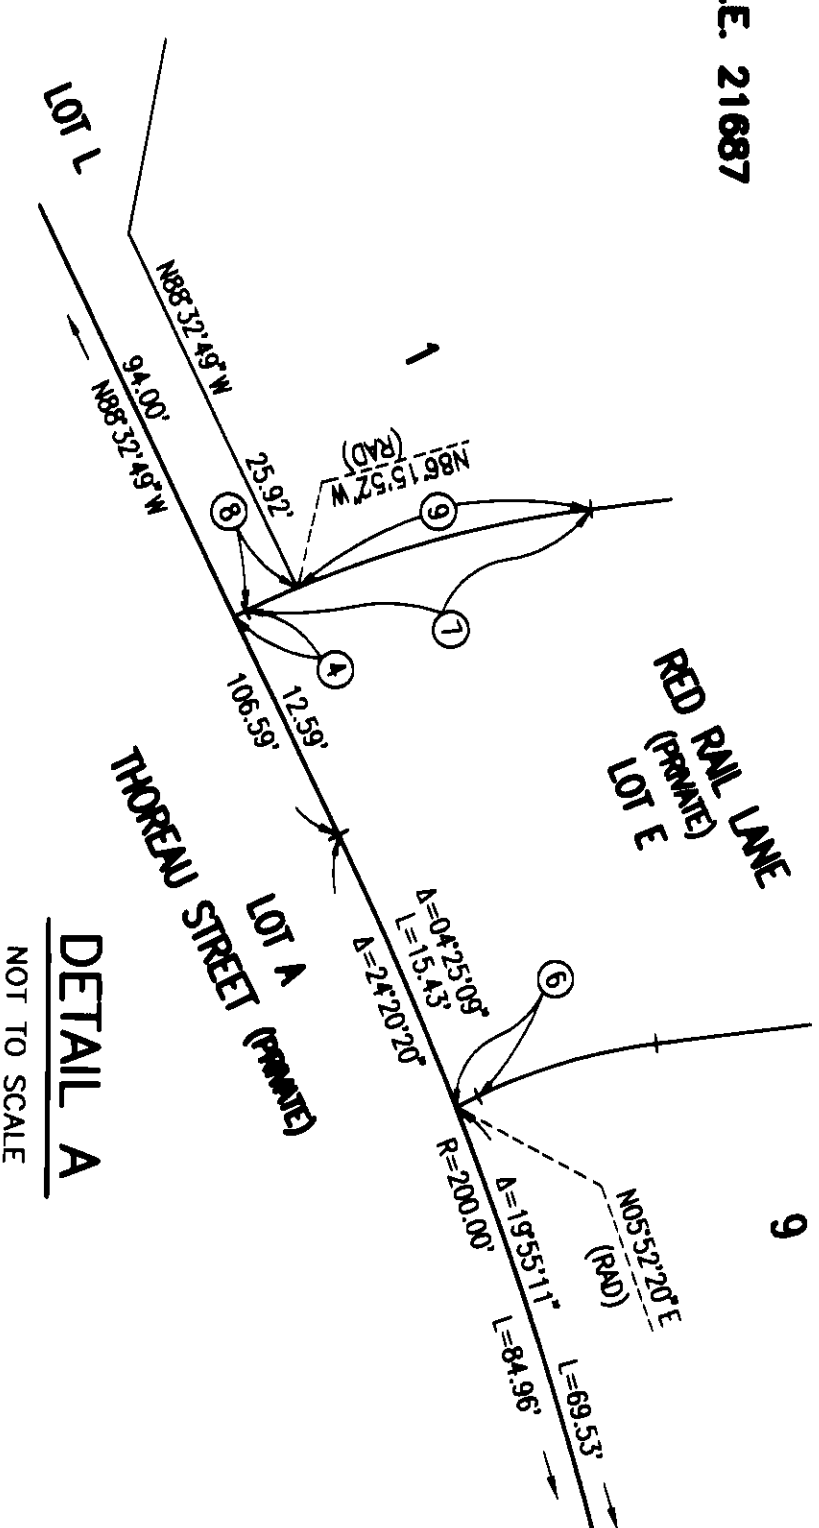

CURVE AND LINE DATA

1. N44°24'50"E 3.59'
2. N88°32'49"W 0.82'
3. N41°00'17"W 7.51'
4. N01°27'11"E 0.69'
5. A=24°20'20" R=30.00' L=12.74'
6. N01°27'11"E 1.29'
7. A=24°20'20" R=58.00' L=24.64'
8. A=02°16'57" R=58.00' L=2.31'
9. A=22°03'23" R=58.00' L=22.33'

NOTES:

1. SEE SHEET 2 FOR BOUNDARY CONTROL, SHEET INDEX, BASIS OF BEARINGS, DATUM STATEMENT, MONUMENT NOTES, EASEMENT NOTES AND LOT TABULATION.
2. SEE SHEET 9 FOR EASEMENT DETAILS.

SHEET 6 OF 9 SHEETS

ALL OF VESTING TENTATIVE TRACT
MAP NO. 16347
TOTAL LOTS: NUMBERED LOTS 1 THROUGH 65
AND LETTERED LOTS A THROUGH V
TOTAL ACRES: 9,319 ACRES


TRACT NO. 16347

IN THE UNINCORPORATED TERRITORY OF THE COUNTY OF ORANGE,

STATE OF CALIFORNIA

ADAMS - STREETER CIVIL ENGINEERS, INC. JAN A. ADAMS, R.C.E. 21697

DATE OF SURVEY: APRIL, 2003

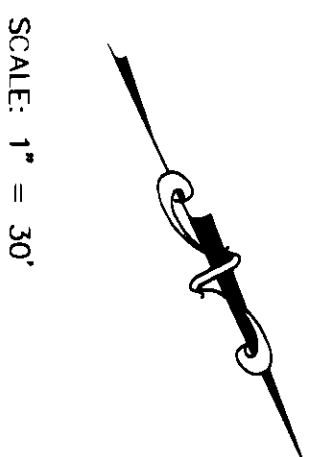


SCALE: 1" = 30'

CURVE AND LINE DATA

- ① $\Delta=0^{\circ}50'16"$ $R=448.00'$ $L=14.37'$
- ② $\Delta=0^{\circ}52'51"$ $R=3.94'$
- ③ $\Delta=0^{\circ}35'46"$ $R=9.61'$
- ④ $\Delta=2^{\circ}47'31"$ $R=0.24'$
- ⑤ $\Delta=9^{\circ}00'00"$ $R=5.00'$ $L=7.85'$
- ⑥ $\Delta=11^{\circ}12'29"$ $R=8.95'$
- ⑦ $\Delta=44^{\circ}24'50"$ $R=3.59'$
- ⑧ $\Delta=88^{\circ}07'09"$ $R=6.33'$
- ⑨ $\Delta=88^{\circ}26'47"$ (RAD) $R=9.98'$
- ⑩ $\Delta=0^{\circ}52'51"$ $R=11.33'$
- ⑪ $\Delta=0^{\circ}56'08"$ $R=3.93'$

- NOTES:
1. SEE SHEET 2 FOR BOUNDARY CONTROL, SHEET INDEX, BASIS OF BEARINGS, DATUM STATEMENT, MONUMENT NOTES, EASEMENT NOTES AND LOT TABULATION.
 2. SEE SHEET 9 FOR EASEMENT DETAILS.

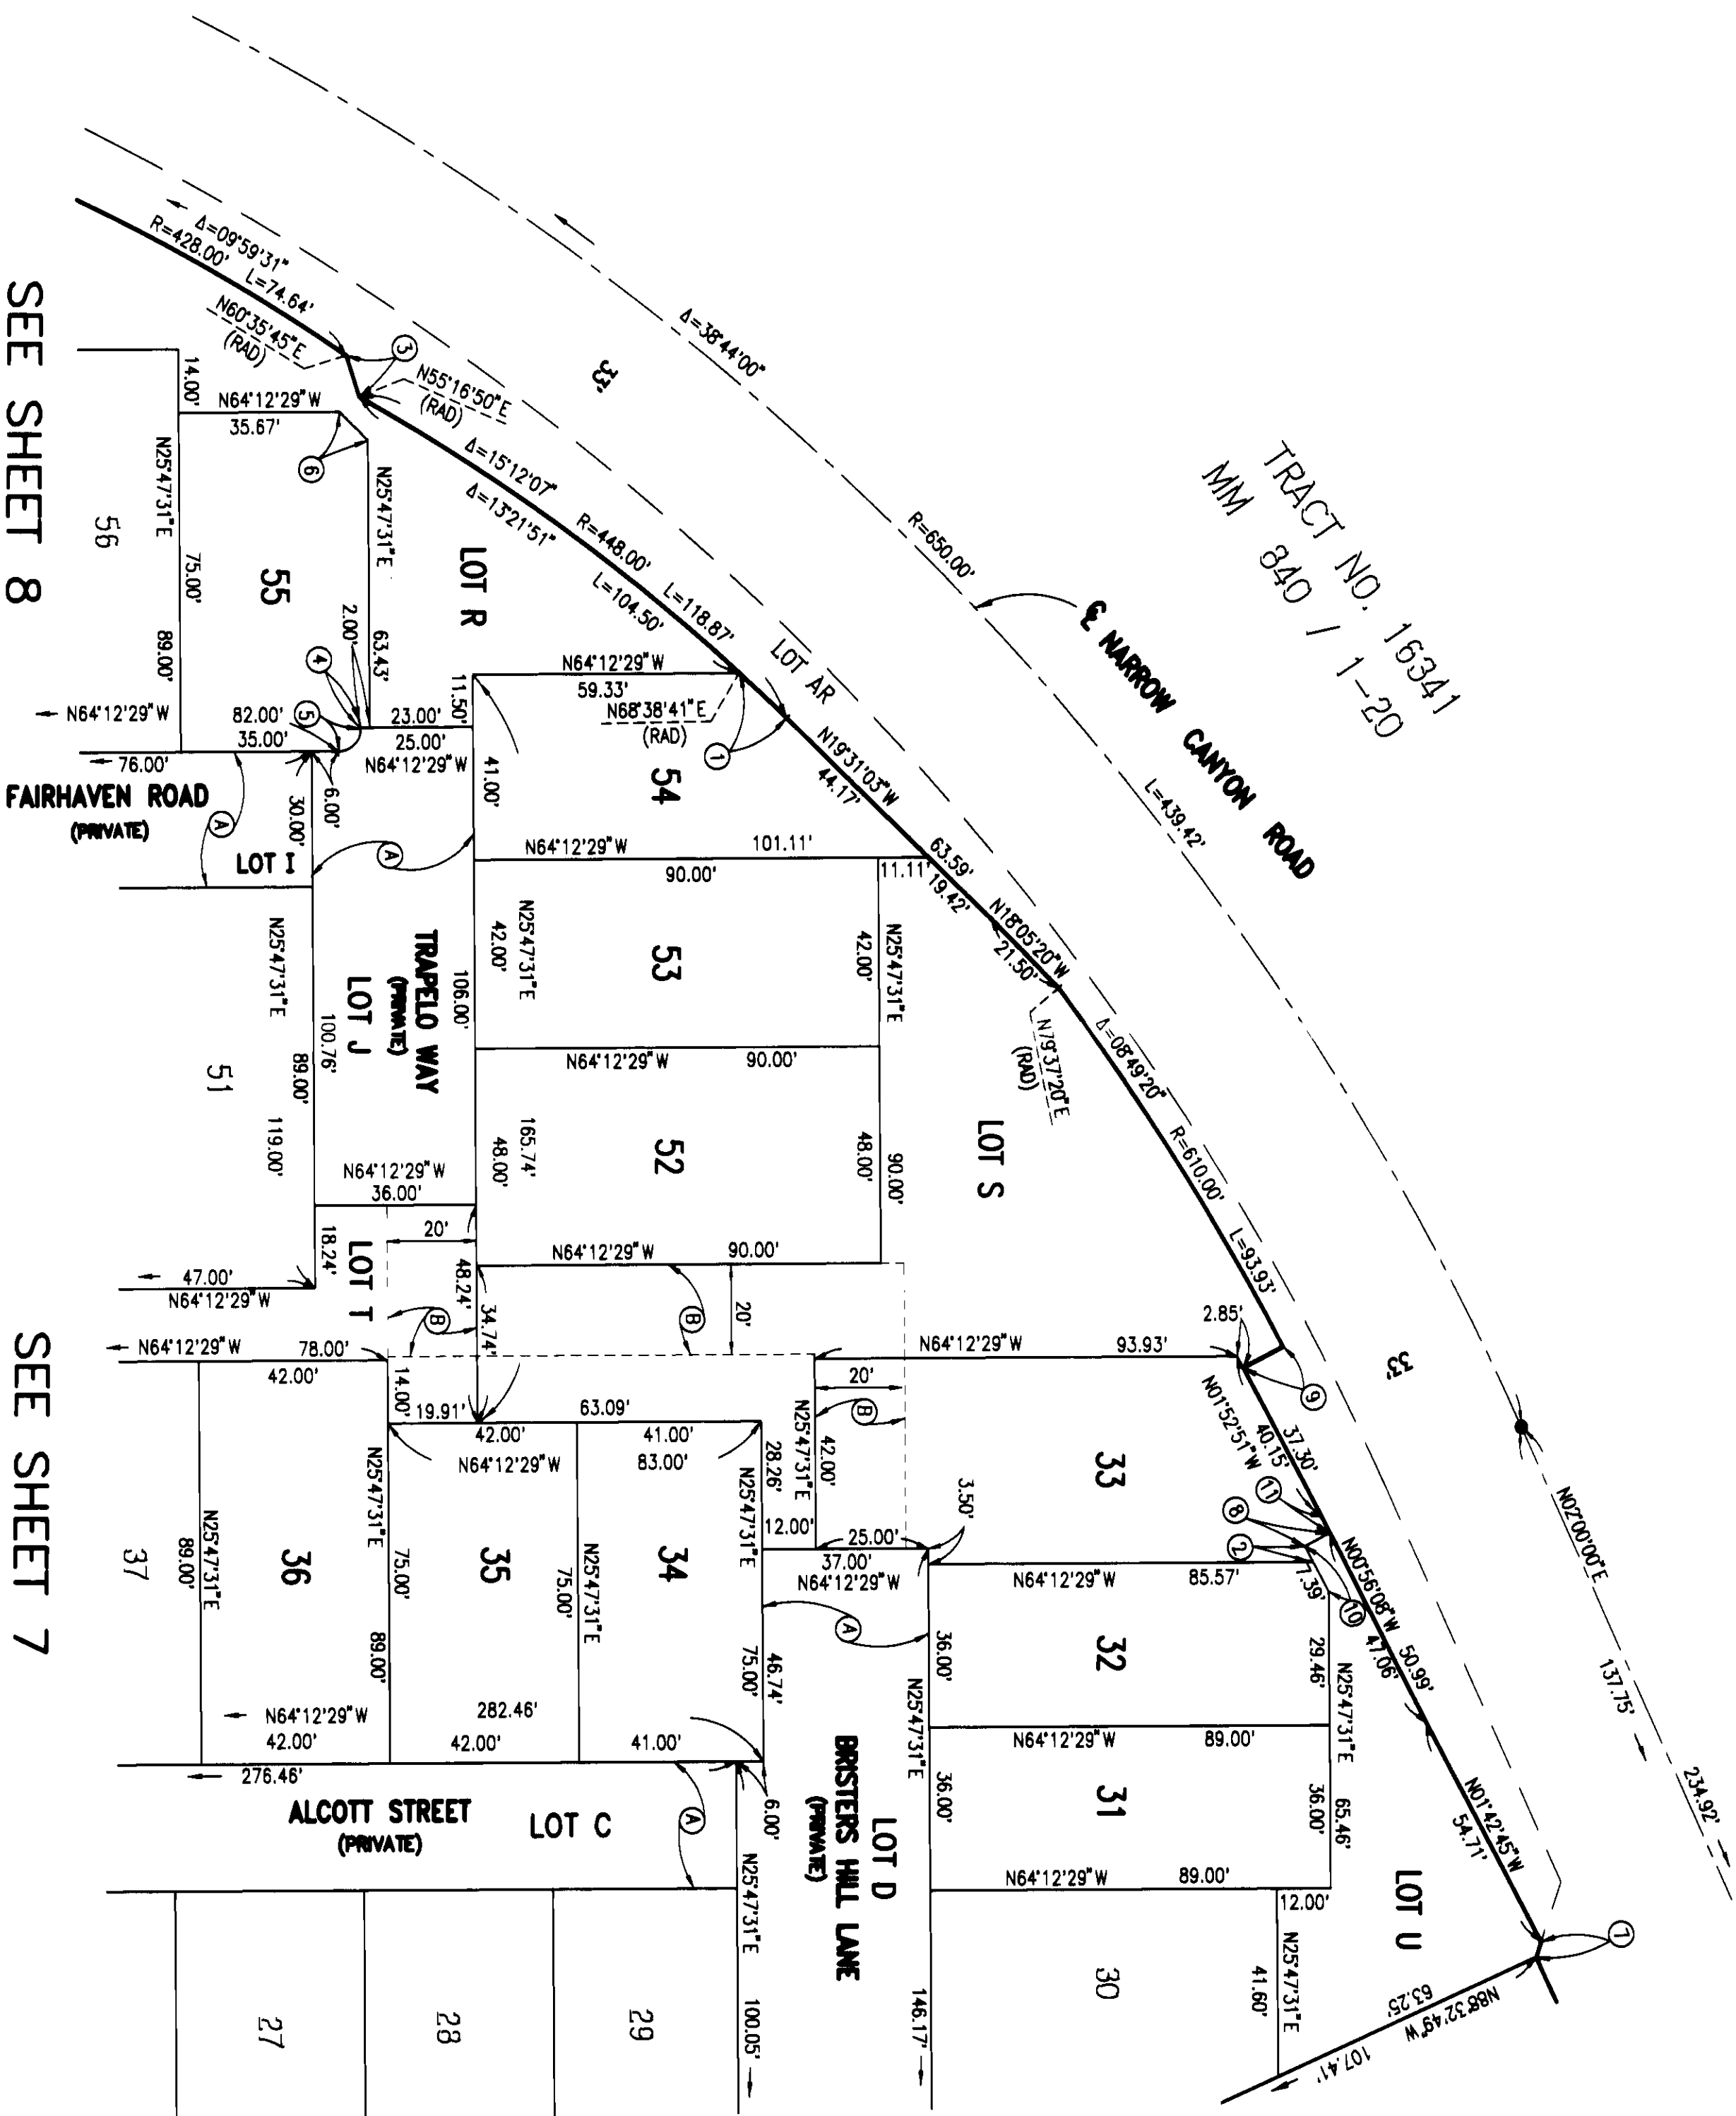

SEE SHEET 8

SEE SHEET 7

SEE SHEET 4

SEE SHEET 5


SHEET 7 OF 9 SHEETS

ALL OF VESTING TENTATIVE TRACT
MAP NO. 16347
TOTAL LOTS: NUMBERED LOTS 1 THROUGH 65
AND LETTERED LOTS A THROUGH V
TOTAL ACREAGE: 9.319 ACRES


TRACT NO. 16347
IN THE UNINCORPORATED TERRITORY OF THE COUNTY OF ORANGE,
STATE OF CALIFORNIA
ADAMS - STREETER CIVIL ENGINEERS, INC. JAN A ADAMS, R.C.E. 21687
DATE OF SURVEY: APRIL, 2003

SEE SHEET 4

SCALE: 1" = 30'

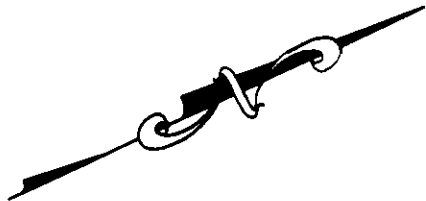

SEE SHEET 6

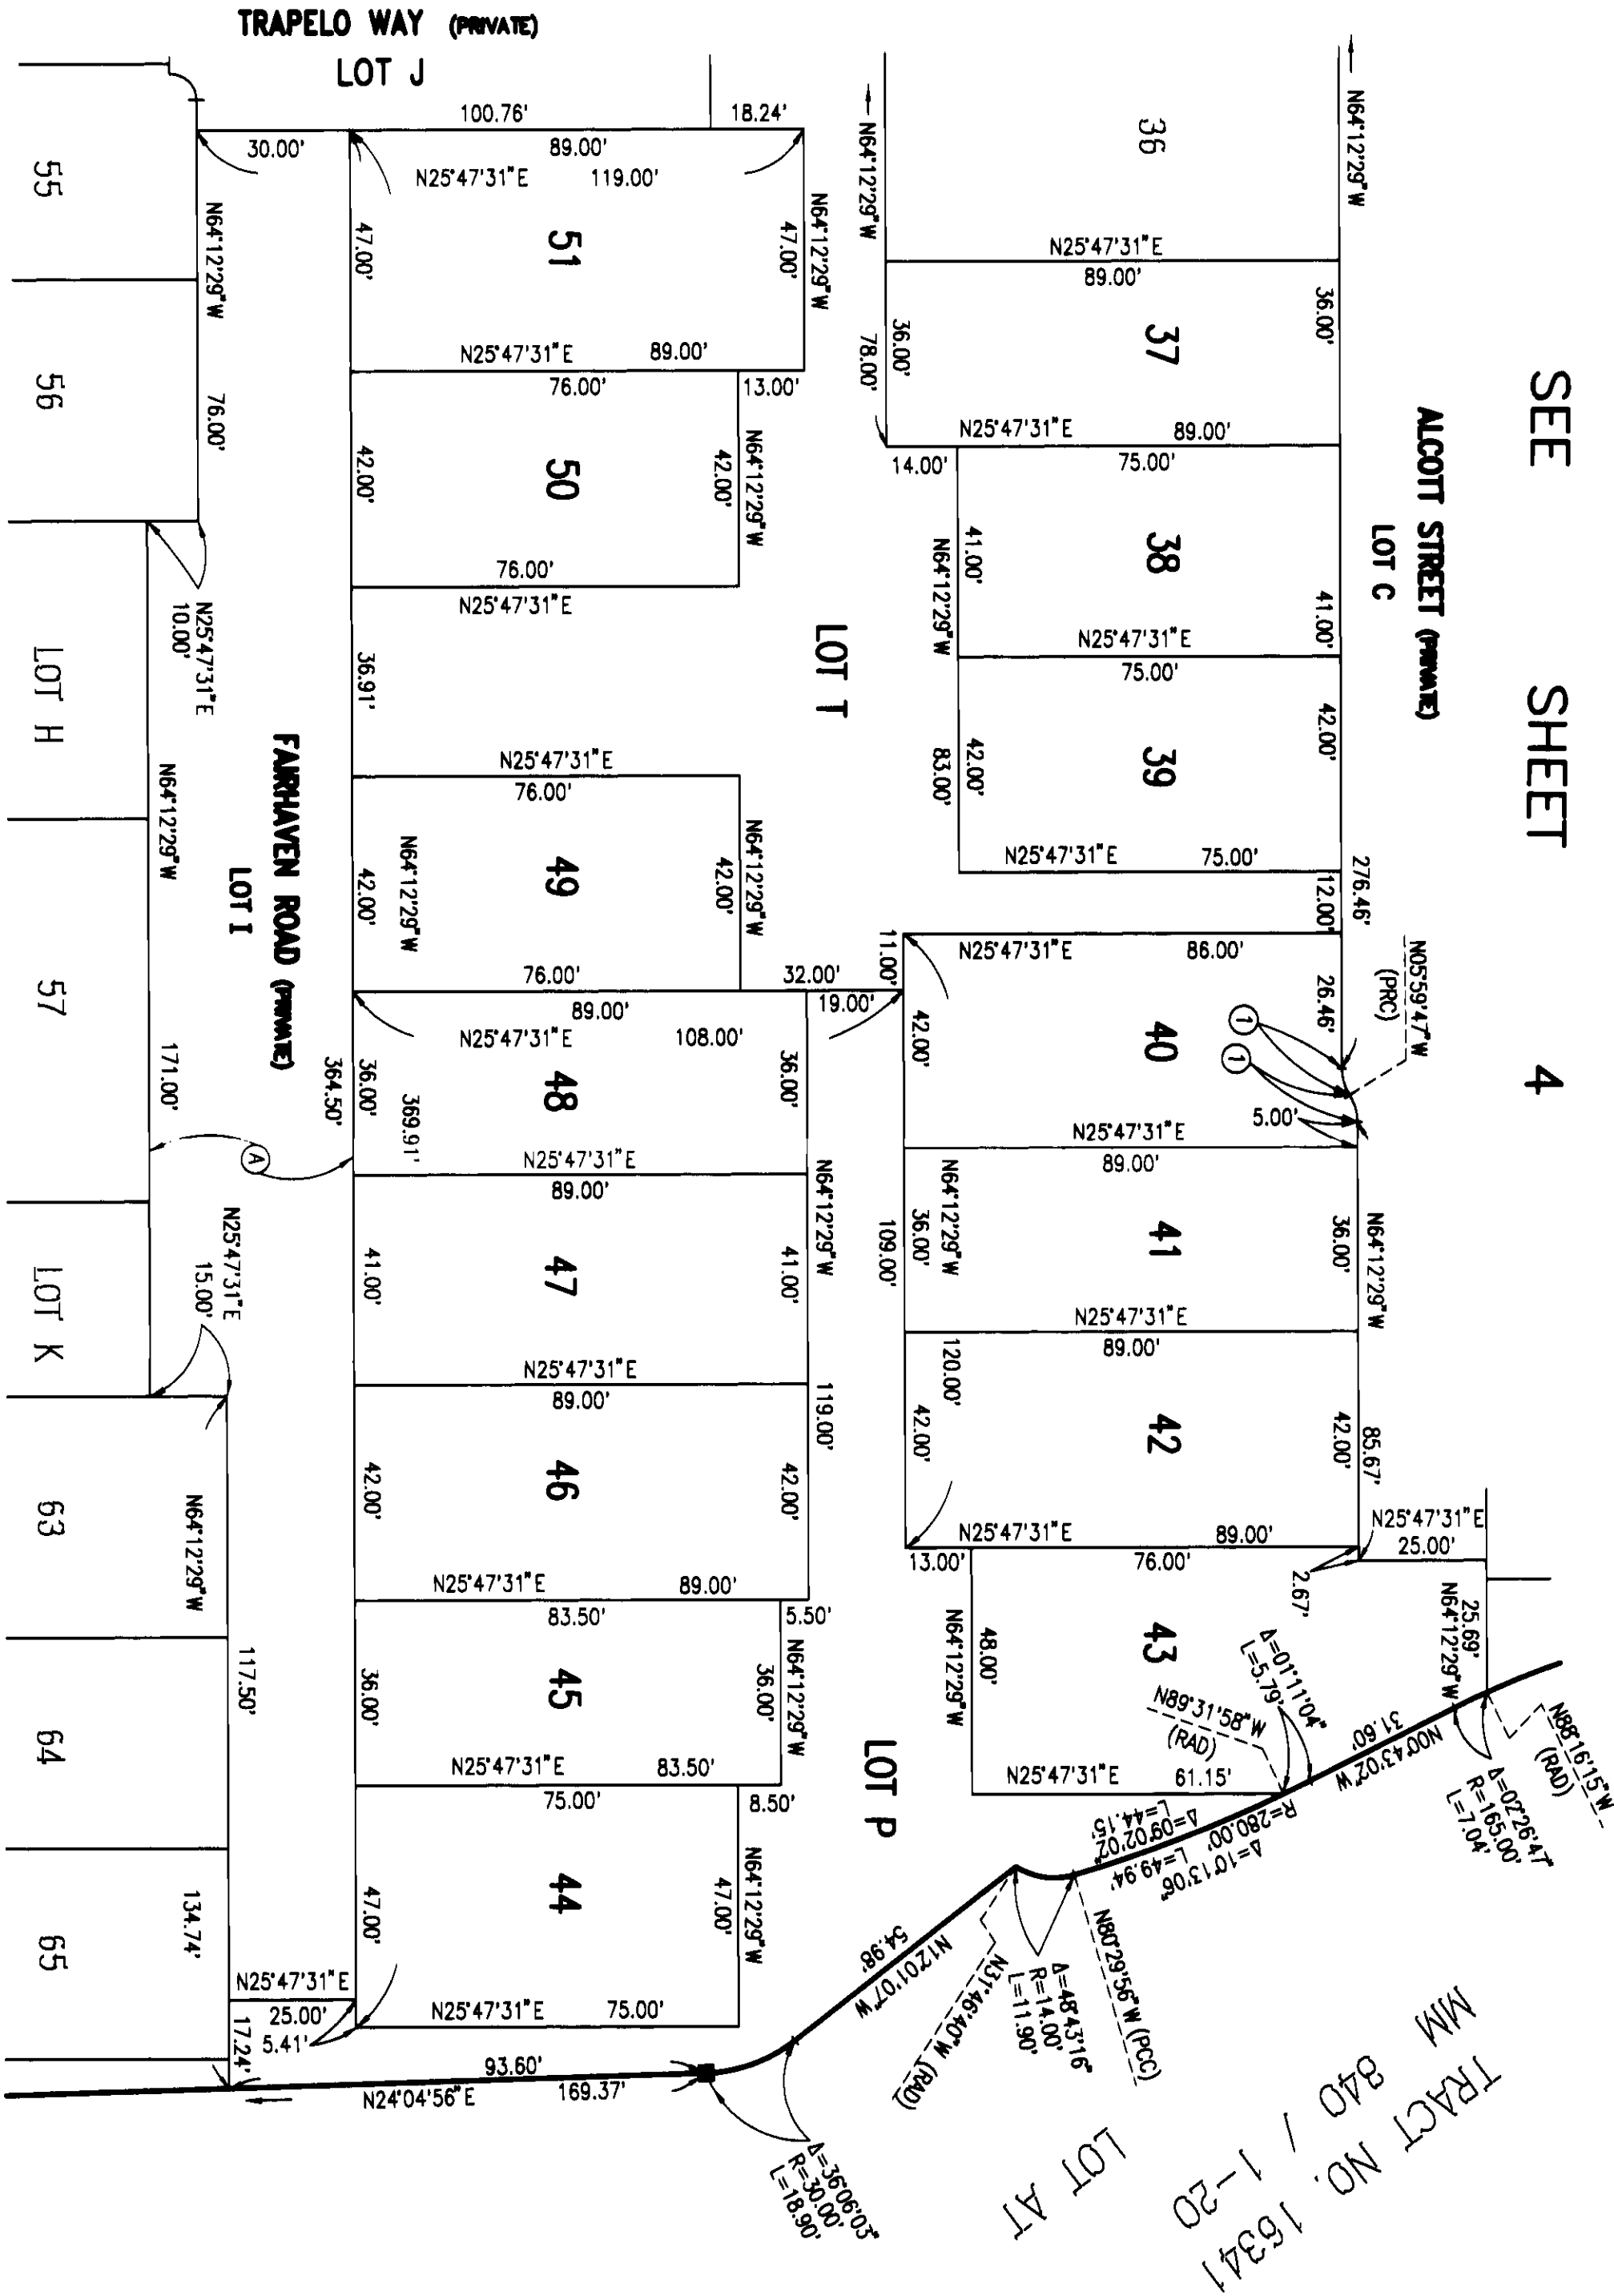

CURVE AND LINE DATA

① A=31°47'18" R=10.00' L=5.55'

NOTES:

1. SEE SHEET 2 FOR BOUNDARY CONTROL, SHEET INDEX, BASIS OF BEARINGS, DATUM STATEMENT, MONUMENT NOTES, EASEMENT NOTES AND LOT TABULATION.
2. SEE SHEET 9 FOR EASEMENT DETAILS.


SEE SHEET 8

SHEET 8 OF 9 SHEETS

ALL OF VESTING TENTATIVE TRACT
MAP NO. 16347
TOTAL LOTS: NUMBERED LOTS 1 THROUGH 65
AND LETTERED LOTS A THROUGH V
TOTAL ACREAGE: 9.319 ACRES


TRACT NO. 16347
IN THE UNINCORPORATED TERRITORY OF THE COUNTY OF ORANGE,
STATE OF CALIFORNIA
ADAMS - STREETER CIVIL ENGINEERS, INC. JAN A ADAMS, R.C.E. 21687
DATE OF SURVEY: APRIL, 2003

SEE SHEET 7

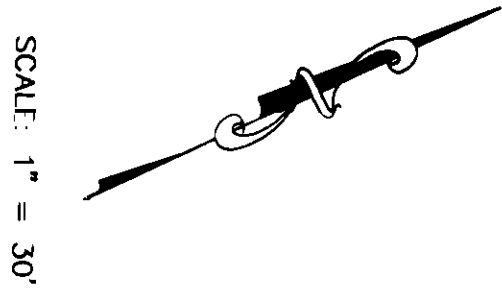

SCALE: 1" = 30'

SEE SHEET 6

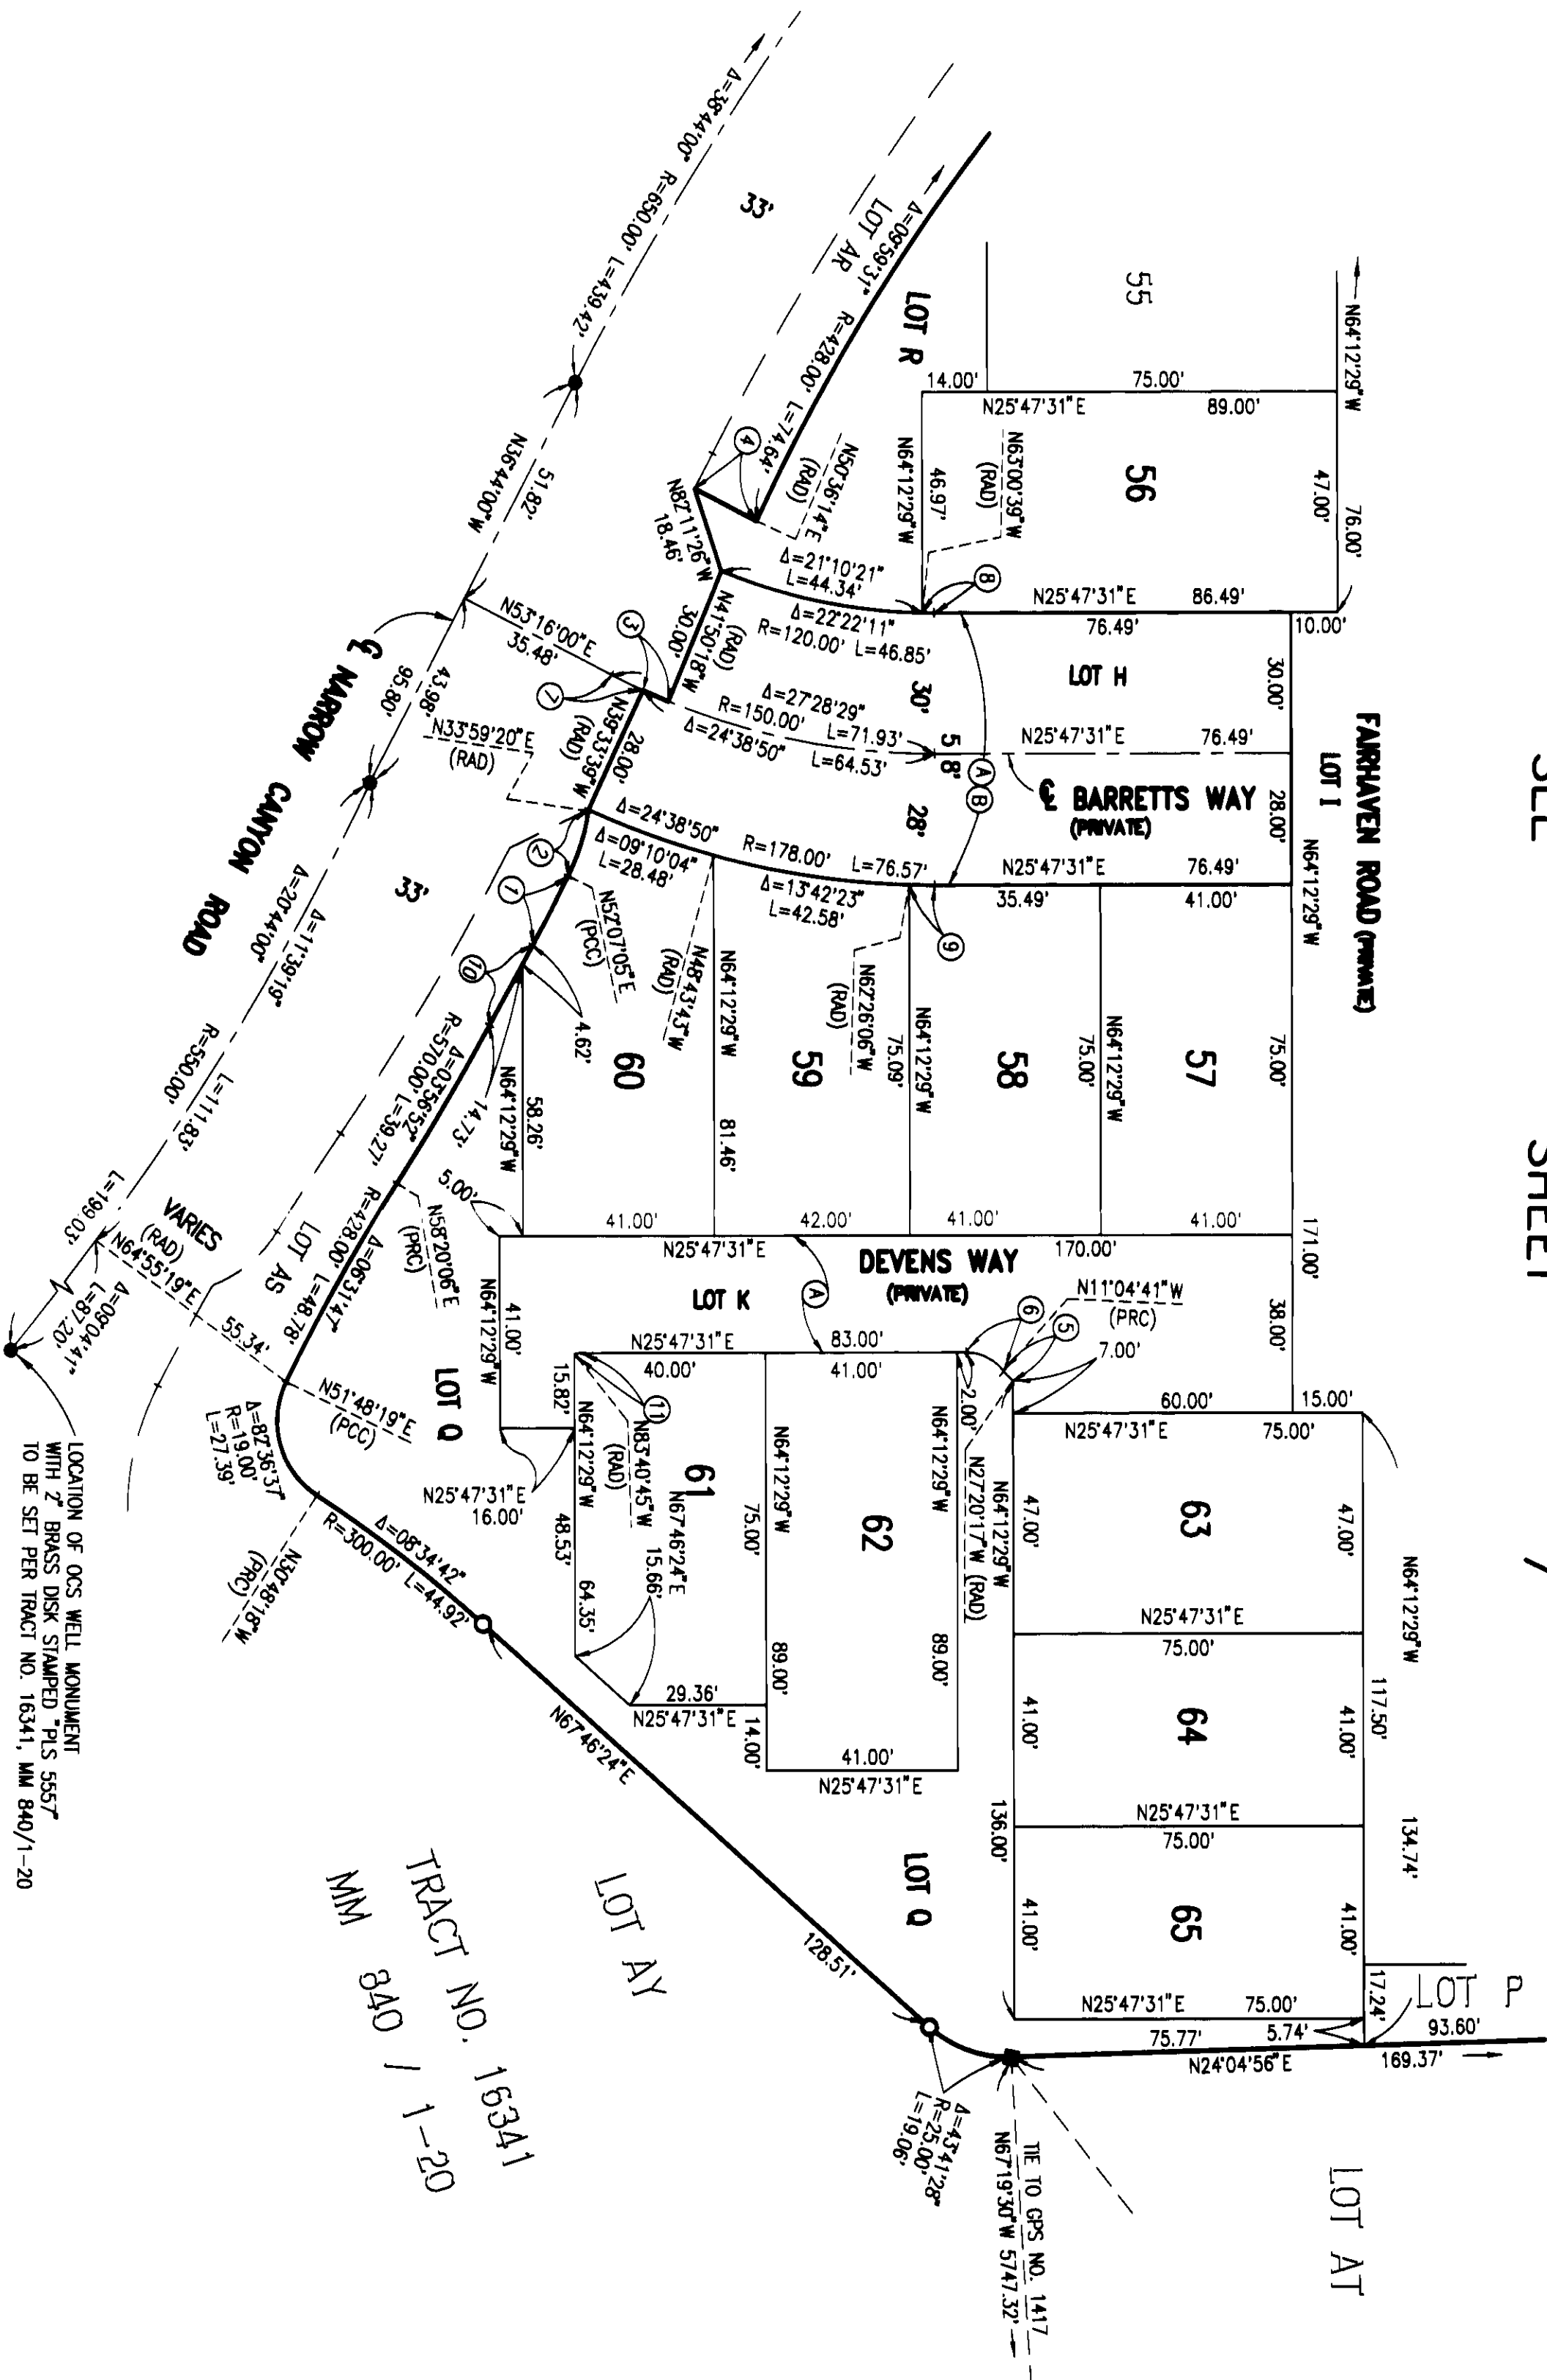

CURVE AND LINE DATA

- ① $\Delta=02^{\circ}16'09''$ $R=420.00'$ $L=16.63''$
- ② $\Delta=18^{\circ}07'45''$ $R=47.00'$ $L=14.87''$
- ③ $\Delta=02^{\circ}16'39''$ $R=150.00'$ $L=5.96''$
- ④ $\Delta=03^{\circ}16'00''$ $R=15.05'$
- ⑤ $\Delta=16^{\circ}15'36''$ $R=10.00'$ $L=2.84''$
- ⑥ $\Delta=53^{\circ}07'48''$ $R=10.00'$ $L=9.27''$
- ⑦ $\Delta=02^{\circ}49'39''$ $R=150.00'$ $L=7.40''$
- ⑧ $\Delta=01^{\circ}11'50''$ $R=120.00'$ $L=2.51''$
- ⑨ $\Delta=01^{\circ}46'25''$ $R=178.00'$ $L=5.51''$
- ⑩ $\Delta=03^{\circ}36'46''$ $R=19.35'$
- ⑪ $\Delta=19^{\circ}28'16''$ $R=3.00'$ $L=1.02''$

NOTES:

1. SEE SHEET 2 FOR BOUNDARY CONTROL, SHEET INDEX, BASIS OF BEARINGS, DATUM STATEMENT, MONUMENT NOTES, EASEMENT NOTES AND LOT TABULATION.
2. SEE SHEET 9 FOR EASEMENT DETAILS.


SHEET 9 OF 9 SHEETS

ALL OF VESTING TENTATIVE TRACT
MAP NO. 16347
TOTAL LOTS: NUMBERED LOTS 1 THROUGH 65
AND LETTERED LOTS A THROUGH V
TOTAL ACREAGE: 9.319 ACRES

TRACT NO. 16347

IN THE UNINCORPORATED TERRITORY OF THE COUNTY OF ORANGE,
STATE OF CALIFORNIA

ADAMS - STREETER CIVIL ENGINEERS, INC. JAN A. ADAMS, R.C.E. 21687
DATE OF SURVEY: APRIL, 2003

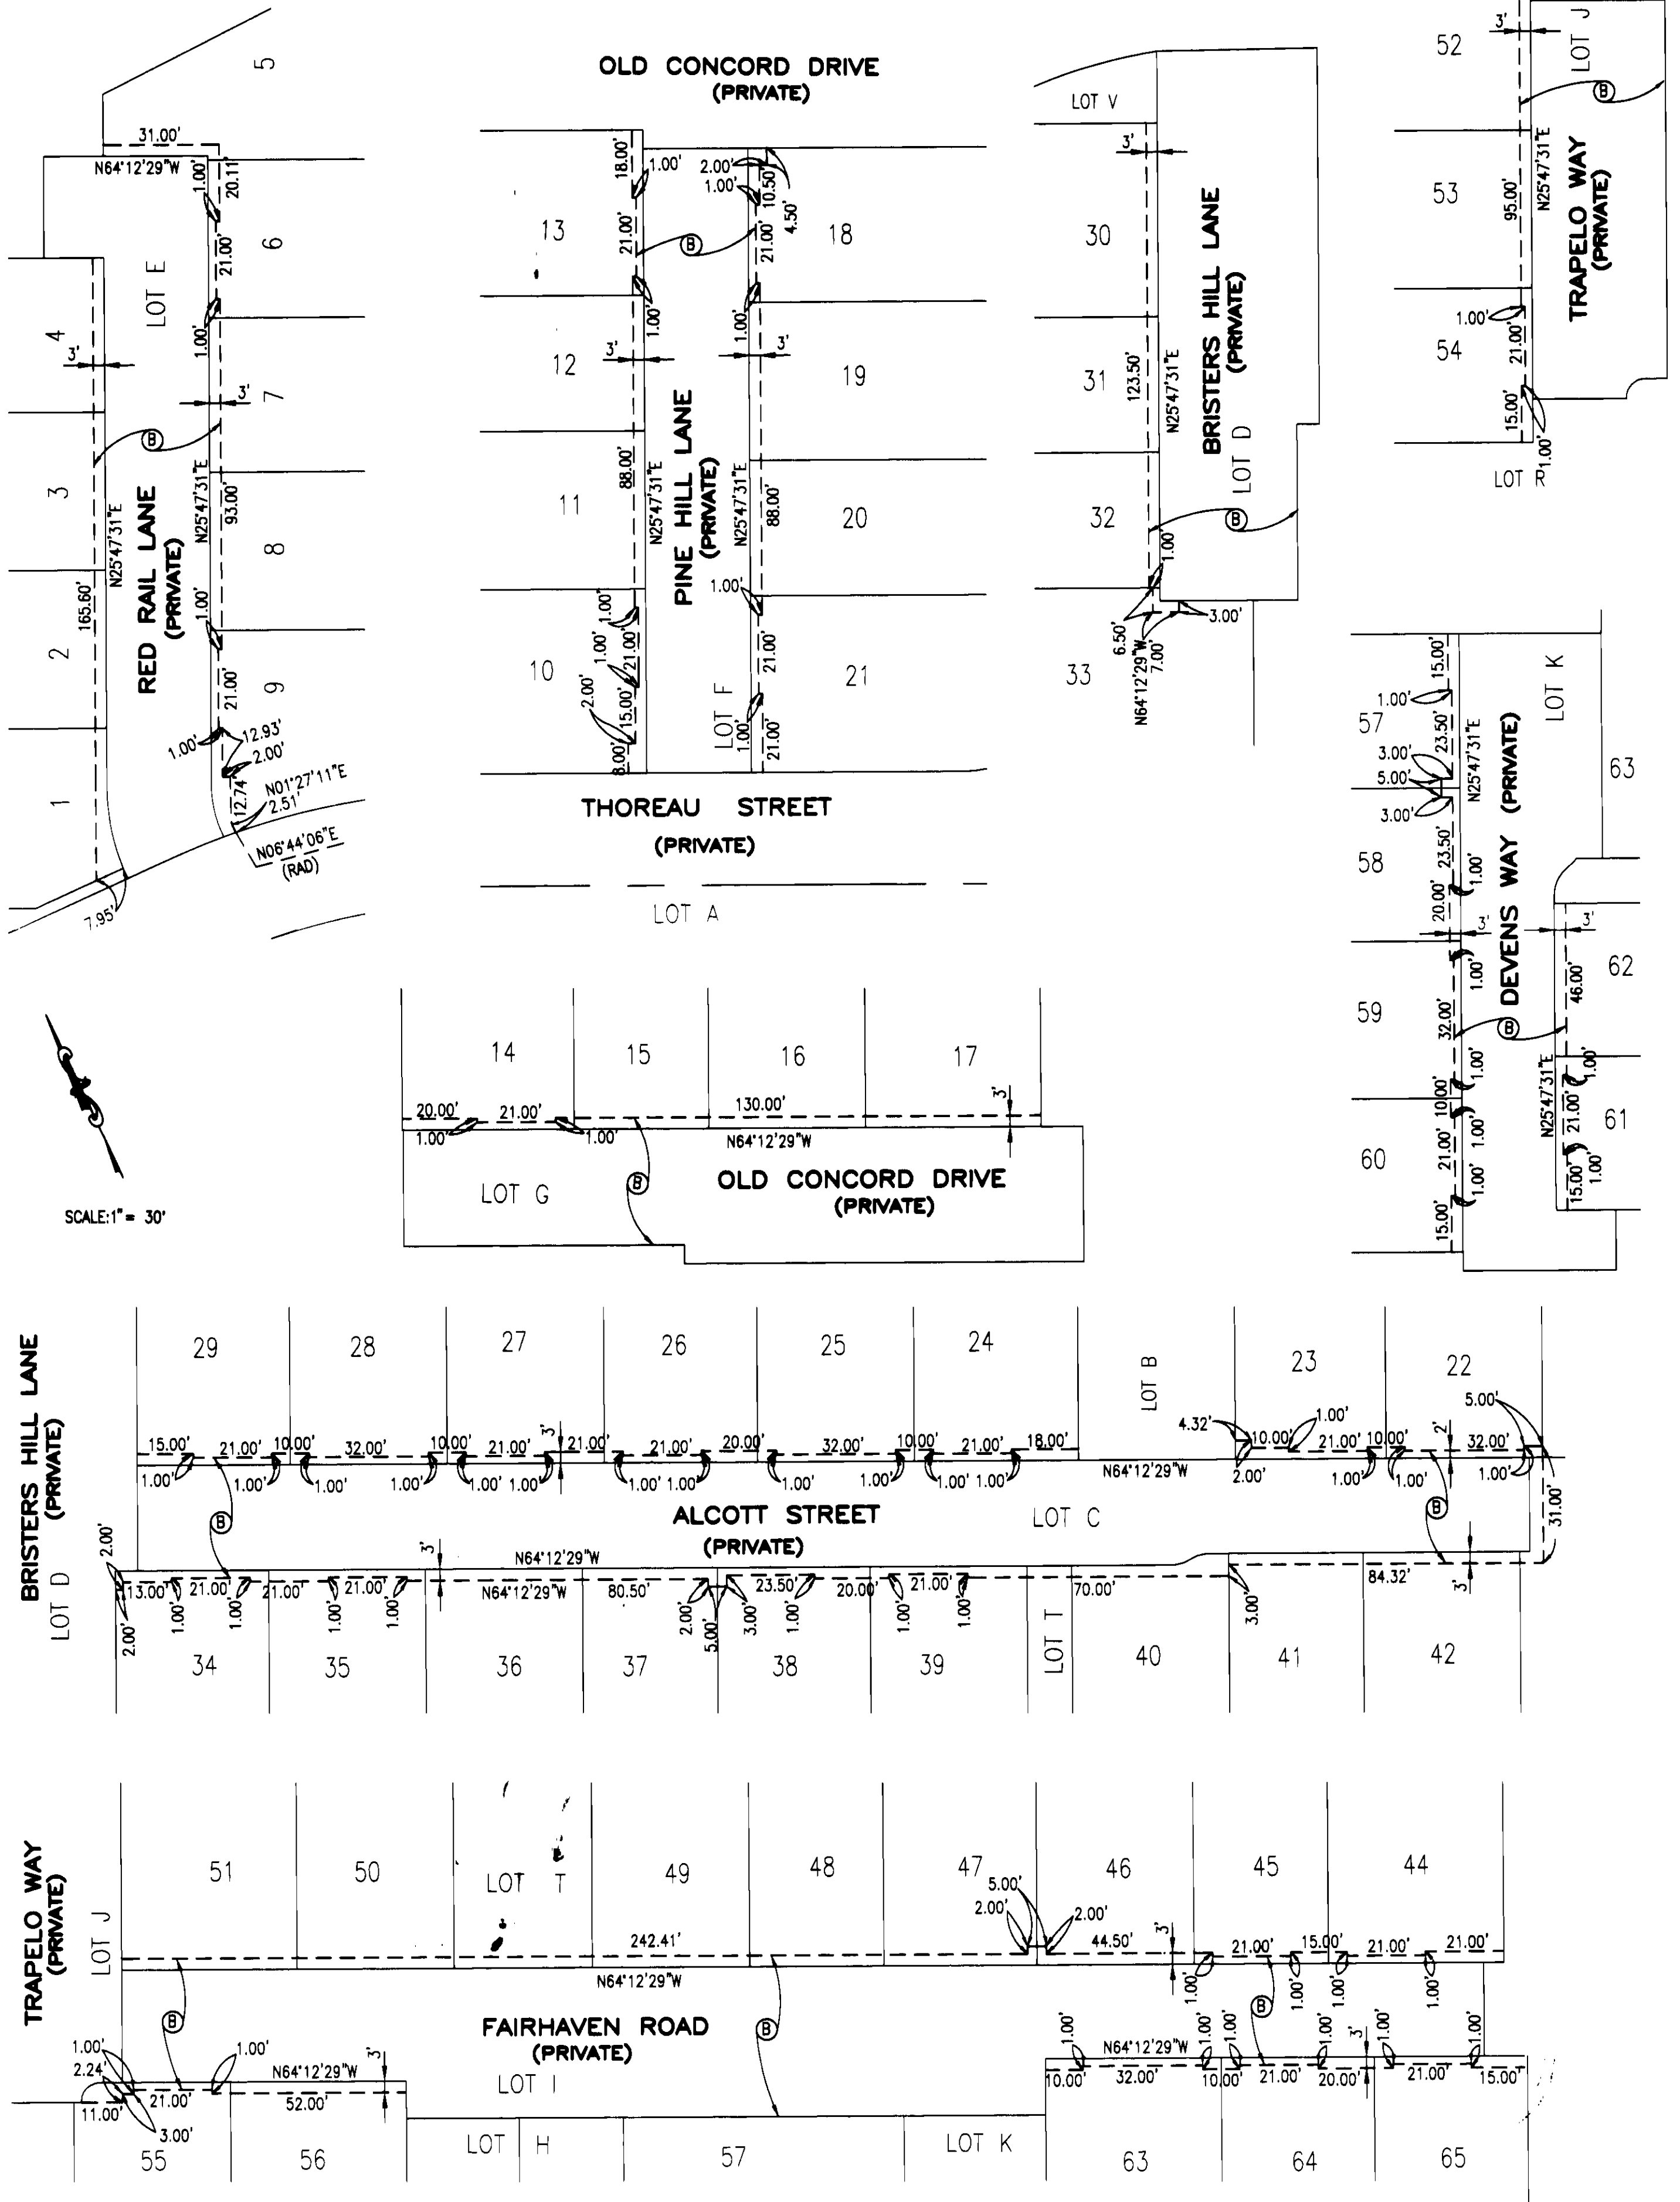

NOTES:

1. SEE SHEET 2 FOR BOUNDARY CONTROL, SHEET INDEX, BASIS OF BEARINGS, DATUM STATEMENT, MONUMENT NOTES, EASEMENT NOTES AND LOT TABULATION.
2. ALL EASEMENT LINES INTERSECT AT RIGHT ANGLES UNLESS OTHERWISE NOTED OR APPARENT.

EASEMENT DETAILS