

SHEET 1 OF 8 SHEETS
65 NUMBERED LOTS AND
LOTS A THROUGH V, INCLUSIVE
ACREAGE = 7.912 ACRES
A PORTION OF TENTATIVE
TRACT NO. 16341
DATE OF SURVEY: DEC. 2002

TRACT NO. 16348

IN THE UNINCORPORATED TERRITORY OF THE COUNTY OF ORANGE,
STATE OF CALIFORNIA

BEING A SUBDIVISION OF LOT 14, AS SHOWN ON TRACT MAP NO. 16341
FILED IN BOOK 840, PAGES 1 THROUGH 20, INCLUSIVE OF MISCELLANEOUS MAPS,
IN THE OFFICE OF THE COUNTY RECORDER OF SAID COUNTY, STATE OF CALIFORNIA
ADAMS - STREETER CIVIL ENGINEERS, INC. JAN A. ADAMS, R.C.E. 21687

ACCEPTED AND FILED AT THE
REQUEST OF

FIRST AMERICAN TITLE INSURANCE COMPANY

DATE AUGUST 18, 2003
TIME 09:51 AM FEE \$17.00
INSTRUMENT # 2003000994048
BOOK 848 PAGE 23-28

TOM DALY
COUNTY - CLERK RECORDER
BY [Signature]
DEPUTY

OWNER'S CERTIFICATE:

WE, THE UNDERSIGNED, BEING ALL PARTIES HAVING ANY RECORD TITLE INTEREST IN THE LAND COVERED BY THIS MAP, DO HEREBY CONSENT TO THE PREPARATION AND RECORDATION OF SAID MAP, AS SHOWN WITHIN THE DISTINCTIVE BORDER LINE.

WE ALSO HEREBY DEDICATE TO THE COUNTY OF ORANGE:

1. AN EASEMENT FOR PUBLIC UTILITY PURPOSES, AS SHOWN HEREON.

WE ALSO DEDICATE TO THE SANTA MARGARITA WATER DISTRICT, THE EASEMENTS FOR SEWER, WATER AND ACCESS PURPOSES AS SHOWN ON SAID MAP, WHICH EASEMENTS SHALL BE SUBJECT TO THE SAME TERMS AND CONDITIONS AS ARE SHOWN IN THAT CERTAIN EASEMENT RECORDED OCTOBER 6, 1980, IN BOOK 13776, PAGE 341, OF OFFICIAL RECORDS, COUNTY OF ORANGE.

RICHMOND AMERICAN HOMES OF CALIFORNIA, INC., A COLORADO CORPORATION

[Signature]
NAME: ROBERT T. SHIOTA
TITLE: REGIONAL PRESIDENT

[Signature]
NAME: ALFREDO F. ARUYAO
TITLE: DIVISION MANAGER

DMB LADERA, LLC., A DELAWARE LIMITED LIABILITY COMPANY AS BENEFICIARY UNDER A DEED OF TRUST RECORDED JUNE 2, 2003 AS INSTRUMENT NO. 2003000639857 OF OFFICIAL RECORDS. EASEMENTS RECORDED JUNE 2, 2003 AS INSTRUMENT NO. 2003000639855 OF OFFICIAL RECORDS.

BY: RANCHO MISSION VIEJO, LLC., A DELAWARE LIMITED LIABILITY COMPANY AS ITS AUTHORIZING AGENT AND MANAGER.

[Signature]
NAME: DONALD T. STAHKIN
TITLE: VICE PRESIDENT

[Signature]
NAME: PAUL JOHNSON
TITLE: SENIOR VICE PRESIDENT

NOTARY ACKNOWLEDGMENTS

STATE OF CALIFORNIA }
COUNTY OF Orange } ss

ON THIS 11th DAY OF June, 2003, BEFORE ME, Sara Koenig, A NOTARY PUBLIC IN AND FOR SAID STATE, PERSONALLY APPEARED Robert T. Shiota and Alfredo F. Aruyao PERSONALLY KNOWN TO ME (OR PROVED TO ME ON THE BASIS OF SATISFACTORY EVIDENCE) TO BE THE PERSONS WHOSE NAMES ARE SUBSCRIBED TO THE WITHIN INSTRUMENT AND ACKNOWLEDGED TO ME THAT THEY EXECUTED THE SAME IN THEIR AUTHORIZED CAPACITIES AND THAT BY THEIR SIGNATURES ON THE INSTRUMENT THE PERSON OR THE ENTITY UPON BEHALF OF WHICH THE PERSONS ACTED, EXECUTED THE INSTRUMENT.

WITNESS MY HAND:

[Signature]
NOTARY PUBLIC IN AND FOR SAID STATE
Sara Koenig
PRINT NAME

MY PRINCIPAL PLACE OF BUSINESS
IS IN Orange COUNTY

MY COMMISSION EXPIRES 6/18/06

STATE OF CALIFORNIA }
COUNTY OF Orange } ss

ON THIS 25th DAY OF June, 2003, BEFORE ME, Diana L. Binks, A NOTARY PUBLIC IN AND FOR SAID STATE, PERSONALLY APPEARED Donald T. Stahkin and Paul Johnson PERSONALLY KNOWN TO ME (OR PROVED TO ME ON THE BASIS OF SATISFACTORY EVIDENCE) TO BE THE PERSONS WHOSE NAMES ARE SUBSCRIBED TO THE WITHIN INSTRUMENT AND ACKNOWLEDGED TO ME THAT THEY EXECUTED THE SAME IN THEIR AUTHORIZED CAPACITIES AND THAT BY THEIR SIGNATURES ON THE INSTRUMENT THE PERSON OR THE ENTITY UPON BEHALF OF WHICH THE PERSONS ACTED, EXECUTED THE INSTRUMENT.

WITNESS MY HAND:

[Signature]
NOTARY PUBLIC IN AND FOR SAID STATE
Diana L. Binks
PRINT NAME

MY PRINCIPAL PLACE OF BUSINESS
IS IN Orange COUNTY

MY COMMISSION EXPIRES 12/12/06

PRIVATE STREETS NOTE

THE PRIVATE STREETS CONSTRUCTED WITHIN THIS MAP SHALL BE OWNED, OPERATED AND MAINTAINED BY THE DEVELOPER, SUCCESSORS OR ASSIGNS. THE COUNTY OF ORANGE SHALL HAVE NO RESPONSIBILITY THEREFORE UNLESS PURSUANT TO APPROPRIATE SECTIONS OF THE STREETS AND HIGHWAYS CODE OF THE STATE OF CALIFORNIA, THE SAID PRIVATE STREETS HAVE BEEN ACCEPTED INTO THE COUNTY ROAD SYSTEM BY APPROPRIATE RESOLUTION OF THE ORANGE COUNTY BOARD OF SUPERVISORS.

SIGNATURE OMISSIONS

PURSUANT TO THE PROVISIONS OF SECTION 66436 (a)(3)(A)(C) OF THE SUBDIVISION MAP ACT, THE FOLLOWING SIGNATURES HAVE BEEN OMITTED:

LADERA DEVELOPMENT COMPANY, LLC, HOLDER OF OIL, GAS AND MINERAL RIGHTS RECORDED AS INSTRUMENT NO. 19960624029 OF OFFICIAL RECORDS.
COUNTY OF ORANGE, HOLDER OF AN EASEMENT FOR STORM DRAIN PURPOSES AS DEDICATED ON TR. 16341, M.M. 840/1-20.

SPECIAL FIRE PROTECTION NOTE:

PROPERTY IS CONDITIONALLY EXCLUDED FROM A SPECIAL FIRE PROTECTION AREA ALL REQUIREMENTS FOR DEVELOPMENT AND CONSTRUCTION WITHIN A "SPECIAL FIRE PROTECTION AREA" INCLUDING INCREASED STREET WIDTHS AND CLASS A ROOF ASSEMBLIES WILL BE MET.

ENGINEER'S STATEMENT

THIS MAP WAS PREPARED BY ME OR UNDER MY DIRECTION AND IS BASED UPON A FIELD SURVEY IN CONFORMANCE WITH THE REQUIREMENTS OF THE SUBDIVISION MAP ACT AND LOCAL ORDINANCE AT THE REQUEST OF RICHMOND AMERICAN HOMES OF CALIFORNIA, INC., IN DECEMBER 2002. I HEREBY STATE THAT ALL MONUMENTS ARE OF THE CHARACTER AND OCCUPY THE POSITIONS INDICATED, OR THAT THEY WILL BE SET IN SUCH POSITIONS; AND THAT SAID MONUMENTS ARE SUFFICIENT TO ENABLE THE SURVEY TO BE RETRACED. I HEREBY STATE THAT THIS MAP SUBSTANTIALLY CONFORMS TO THE CONDITIONALLY APPROVED TENTATIVE MAP.

[Signature]
JAN A. ADAMS, R.C.E. 21687
EXPIRES: 9/30/05



COUNTY SURVEYOR'S STATEMENT

I HEREBY STATE THAT I HAVE EXAMINED THIS MAP AND HAVE FOUND IT TO BE SUBSTANTIALLY IN CONFORMANCE WITH THE TENTATIVE MAP AS FILED WITH, AMENDED AND APPROVED BY THE ORANGE COUNTY SUBDIVISION COMMITTEE; THAT ALL PROVISIONS OF THE SUBDIVISION MAP ACT AND COUNTY SUBDIVISION REGULATIONS HAVE BEEN COMPLIED WITH AND I AM SATISFIED SAID MAP IS TECHNICALLY CORRECT.

DATED THIS 22nd DAY OF July, 2003

[Signature]
JOHN CANAS, COUNTY SURVEYOR
LS 4408 EXPIRATION DATE: 9-30-05 BY: MICHAEL K. SULLIVAN, DEPUTY
LS 6254 EXPIRES 6/30/06



COUNTY TREASURER - TAX COLLECTOR'S CERTIFICATE

STATE OF CALIFORNIA }
COUNTY OF ORANGE } ss

I HEREBY CERTIFY THAT ACCORDING TO THE RECORDS OF MY OFFICE THERE ARE NO LIENS AGAINST THE LAND COVERED BY THIS MAP OR ANY PART THEREOF FOR UNPAID STATE, COUNTY, MUNICIPAL OR LOCAL TAXES OR SPECIAL ASSESSMENTS COLLECTED AS TAXES, EXCEPT TAXES OR SPECIAL ASSESSMENTS COLLECTED AS TAXES NOT YET PAYABLE.

AND DO ALSO CERTIFY TO THE RECORDER OF ORANGE COUNTY THAT THE PROVISIONS OF THE SUBDIVISION MAP ACT HAVE BEEN COMPLIED WITH REGARDING DEPOSITS TO SECURE THE PAYMENT OF TAXES OR SPECIAL ASSESSMENTS COLLECTED AS TAXES ON THE LAND COVERED BY THIS MAP.

DATED THIS 13th DAY OF June, 2003

JOHN M. W. MOORLACH
COUNTY TREASURER - TAX COLLECTOR BY [Signature]
DEPUTY TREASURER - TAX COLLECTOR

CLERK OF THE BOARD OF SUPERVISOR'S CERTIFICATE

STATE OF CALIFORNIA }
COUNTY OF ORANGE } ss

I HEREBY CERTIFY THAT THIS MAP WAS PRESENTED FOR APPROVAL TO THE BOARD OF SUPERVISORS OF ORANGE COUNTY AT A REGULAR MEETING THEREOF HELD ON THE 12th DAY OF August, 2003, AND THAT THEREUPON SAID BOARD DID, BY AN ORDER DULY PASSED AND ENTERED, APPROVE SAID MAP.

AND DID ACCEPT ON BEHALF OF THE COUNTY OF ORANGE:

1. THE EASEMENT FOR PUBLIC UTILITY PURPOSES, AS DEDICATED.

AND DID ALSO APPROVE SUBJECT MAP PURSUANT TO THE PROVISIONS OF SECTION 66436 (a)(3)(A) OF THE SUBDIVISION MAP ACT.

DATED THIS 12th DAY OF August, 2003

[Signature]
DARLENE J. BLOOM, CLERK OF THE BOARD OF SUPERVISORS



CERTIFICATE OF ACCEPTANCE

THE UNDERSIGNED, BEING THE DULY APPOINTED AGENT OF THE SANTA MARGARITA WATER DISTRICT, A PUBLIC CORPORATION OF ORANGE COUNTY, CALIFORNIA, PURSUANT TO ITS RESOLUTION NO. 88-10-2, DOES HEREBY ACCEPT ON BEHALF OF SAID DISTRICT THE EASEMENTS FOR SEWER, WATER AND ACCESS PURPOSES, AS DEDICATED AND AS SHOWN ON THIS TRACT MAP, BY AND BETWEEN THE SANTA MARGARITA WATER DISTRICT AND RICHMOND AMERICAN HOMES OF CALIFORNIA, INC. DOES HEREBY CERTIFY THAT THE GRANTEE CONSENTS TO THE RECORDATION OF SAID TRACT.

[Signature]
DANIEL R. FERONS, CHIEF ENGINEER
SANTA MARGARITA WATER DISTRICT

STATE OF CALIFORNIA }
COUNTY OF ORANGE } ss

ON THIS 28th DAY OF June, 2003, BEFORE ME, Andrea M. Evans, A NOTARY PUBLIC IN AND FOR SAID STATE, PERSONALLY APPEARED Daniel Ferons, PERSONALLY KNOWN TO ME (OR PROVED TO ME ON THE BASIS OF SATISFACTORY EVIDENCE) TO BE THE PERSON WHOSE NAME IS SUBSCRIBED TO THE WITHIN INSTRUMENT AND ACKNOWLEDGED TO ME THAT HE EXECUTED THE SAME IN HIS AUTHORIZED CAPACITY AND THAT BY HIS SIGNATURE ON THE INSTRUMENT THE PERSON, OR THE ENTITY UPON BEHALF OF WHICH THE PERSON ACTED, EXECUTED THE INSTRUMENT.

WITNESS MY HAND:

[Signature]
NOTARY PUBLIC IN AND FOR SAID STATE
ANDREA M. EVANS
PRINT NAME

MY PRINCIPAL PLACE OF BUSINESS
IS IN ORANGE COUNTY


MY COMMISSION EXPIRES April 8, 2004

848 24

SHEET 2 OF 6 SHEETS
65 NUMBERED LOTS AND
LOTS A THROUGH V, INCLUSIVE
ACREAGE = 7.912 ACRES
A PORTION OF TENTATIVE
TRACT NO. 16341

TRACT NO. 16348

IN THE UNINCORPORATED TERRITORY OF THE COUNTY OF ORANGE,
STATE OF CALIFORNIA
ADAMS - STREETER CIVIL ENGINEERS, INC. JAN A. ADAMS, R.C.E. 21687
DATE OF SURVEY: DEC. 2002

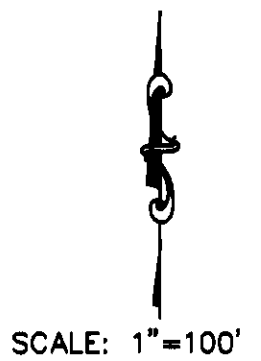

MONUMENT NOTES:

1. ● 2" IRON PIPE, TAGGED "R.C.E. 21687" TO BE SET PRIOR TO RECORDATION.
2. ■ 2" IRON PIPE, TAGGED "LS 5557", OR SPIKE AND WASHER, STAMPED "LS 5557", OR LEAD, TACK AND TAG "LS 5557" TO BE SET PER TRACT NO. 16341, MM 840/1-20, UNLESS OTHERWISE NOTED.
3. ■ 8" SPIKE AND WASHER STAMPED "LS. 5557" IN ASPHALT PAVING OR LEAD, TACK AND TAG "LS. 5557" IN CONCRETE OR 1" IRON PIPE, TAGGED "LS. 5557" TO BE SET PER TRACT 16341, MM 840/1-20.
4. 1" IRON PIPE, TAGGED "R.C.E. 21687", OR SPIKE AND WASHER, STAMPED "R.C.E. 21687", OR LEAD, TACK AND TAG "R.C.E. 21687" TO BE SET AT ALL LOT CORNERS, EXCEPT AT LOT CORNERS THAT ABUT A STREET, WHICH WILL BE SET ON A 9.75' OFFSET OUTSIDE THE TRUE LOT CORNER ON A PROLONGATION OF THE SIDE LOT LINE BY A LEAD, TACK AND TAG "R.C.E. 21687" IN THE TOP OF ADJACENT CONCRETE CURB, UNLESS OTHERWISE NOTED.
5. 8" SPIKE AND WASHER STAMPED "RCE 21687" IN ASPHALT PAVING OR LEAD, TACK AND TAG "R.C.E. 21687" IN CONCRETE OR 1" IRON PIPE, TAGGED "RCE 21687" TO BE SET AT ALL CENTERLINE INTERSECTIONS, B.C.'S, E.C.'S AND ALL OTHER CENTERLINE POINTS OF CONTROL, UNLESS OTHERWISE NOTED.
6. ALL MONUMENTS SHOWN AS "TO BE SET" WILL BE SET 90 DAYS AFTER THE ACCEPTANCE OF THE FINAL IMPROVEMENTS.
7. NO MONUMENTS TO BE SET AT BC'S AND EC'S OF STREET RIGHT OF WAY LINES.
8. ▲ FOUND GPS HORIZONTAL CONTROL POINT PER RECORDS ON FILE IN THE ORANGE COUNTY SURVEYOR'S OFFICE.

SIDEYARD EASEMENT NOTE:

CERTAIN LOTS WILL BE BENEFITED AND/OR BURDENED BY EASEMENTS FOR SIDEYARD AND/OR INGRESS/EGRESS PURPOSES, SUCH EASEMENTS WILL BE MORE PARTICULARLY SET FORTH IN SEPARATE DOCUMENTS TO BE RECORDED LATER.

EASEMENT NOTES:

- A. AN EASEMENT FOR EMERGENCY AND PUBLIC SERVICE VEHICULAR INGRESS-EGRESS DEDICATED TO THE COUNTY OF ORANGE.
- B. AN EASEMENT FOR SEWER AND WATER PIPELINE AND ACCESS PURPOSES DEDICATED TO THE SANTA MARGARITA WATER DISTRICT HEREON.
- C. AN EXISTING EASEMENT FOR STORM DRAIN PURPOSES DEDICATED TO THE COUNTY OF ORANGE. ON TRACT NO. 16341 M.M. 840/1-20.
- D. AN EXISTING EASEMENT "5-10" IN FAVOR OF SANTA MARGARITA WATER DISTRICT PER DOCUMENT RECORDED AS INST. NO. 2003000602372, O.R.

BASIS OF BEARINGS

THE BEARINGS SHOWN HEREON ARE BASED ON THE BEARING BETWEEN ORANGE COUNTY SURVEYOR'S HORIZONTAL CONTROL STATION "GPS NO. 1417" AND "GPS NO. 1448", BEING N. 10°48'13" E., PER RECORDS ON FILE IN THE OFFICE OF THE ORANGE COUNTY SURVEYOR.

DATUM STATEMENT

COORDINATES SHOWN HEREON ARE BASED ON THE CALIFORNIA COORDINATE SYSTEM (CCS83) ZONE VI, 1983 NAD (1991.35 EPOCH, O.C.S. GPS ADJUSTMENT). ALL DISTANCES SHOWN HEREON ARE GROUND, UNLESS OTHERWISE NOTED. TO OBTAIN GRID DISTANCE MULTIPLY GROUND DISTANCE BY 0.99993286.


AUTOMATIC FIRE SPRINKLER NOTE:

ALL RESIDENTIAL STRUCTURES EXCEEDING 5,500 SQUARE FEET AND ALL STRUCTURES EXCEEDING FIRE DEPARTMENT ACCESS REQUIREMENTS SHALL BE PROTECTED BY AN AUTOMATIC FIRE SPRINKLER SYSTEM, IN A MANNER MEETING THE APPROVAL OF THE FIRE CHIEF.

GPS NO. 1448

FOUND 2 1/2" IRON PIPE W/2" BRASS CAP
STAMPED "GPS 1448 9-95" PER TRACT
NO. 16025, MM 812/22-29 AND RECORDS
ON FILE IN THE ORANGE COUNTY SURVEYOR'S
OFFICE.
N 2146790.819
E 6142602.585

T. R. 1 6 3 4 1 LOT AP M. M. 840/1-20

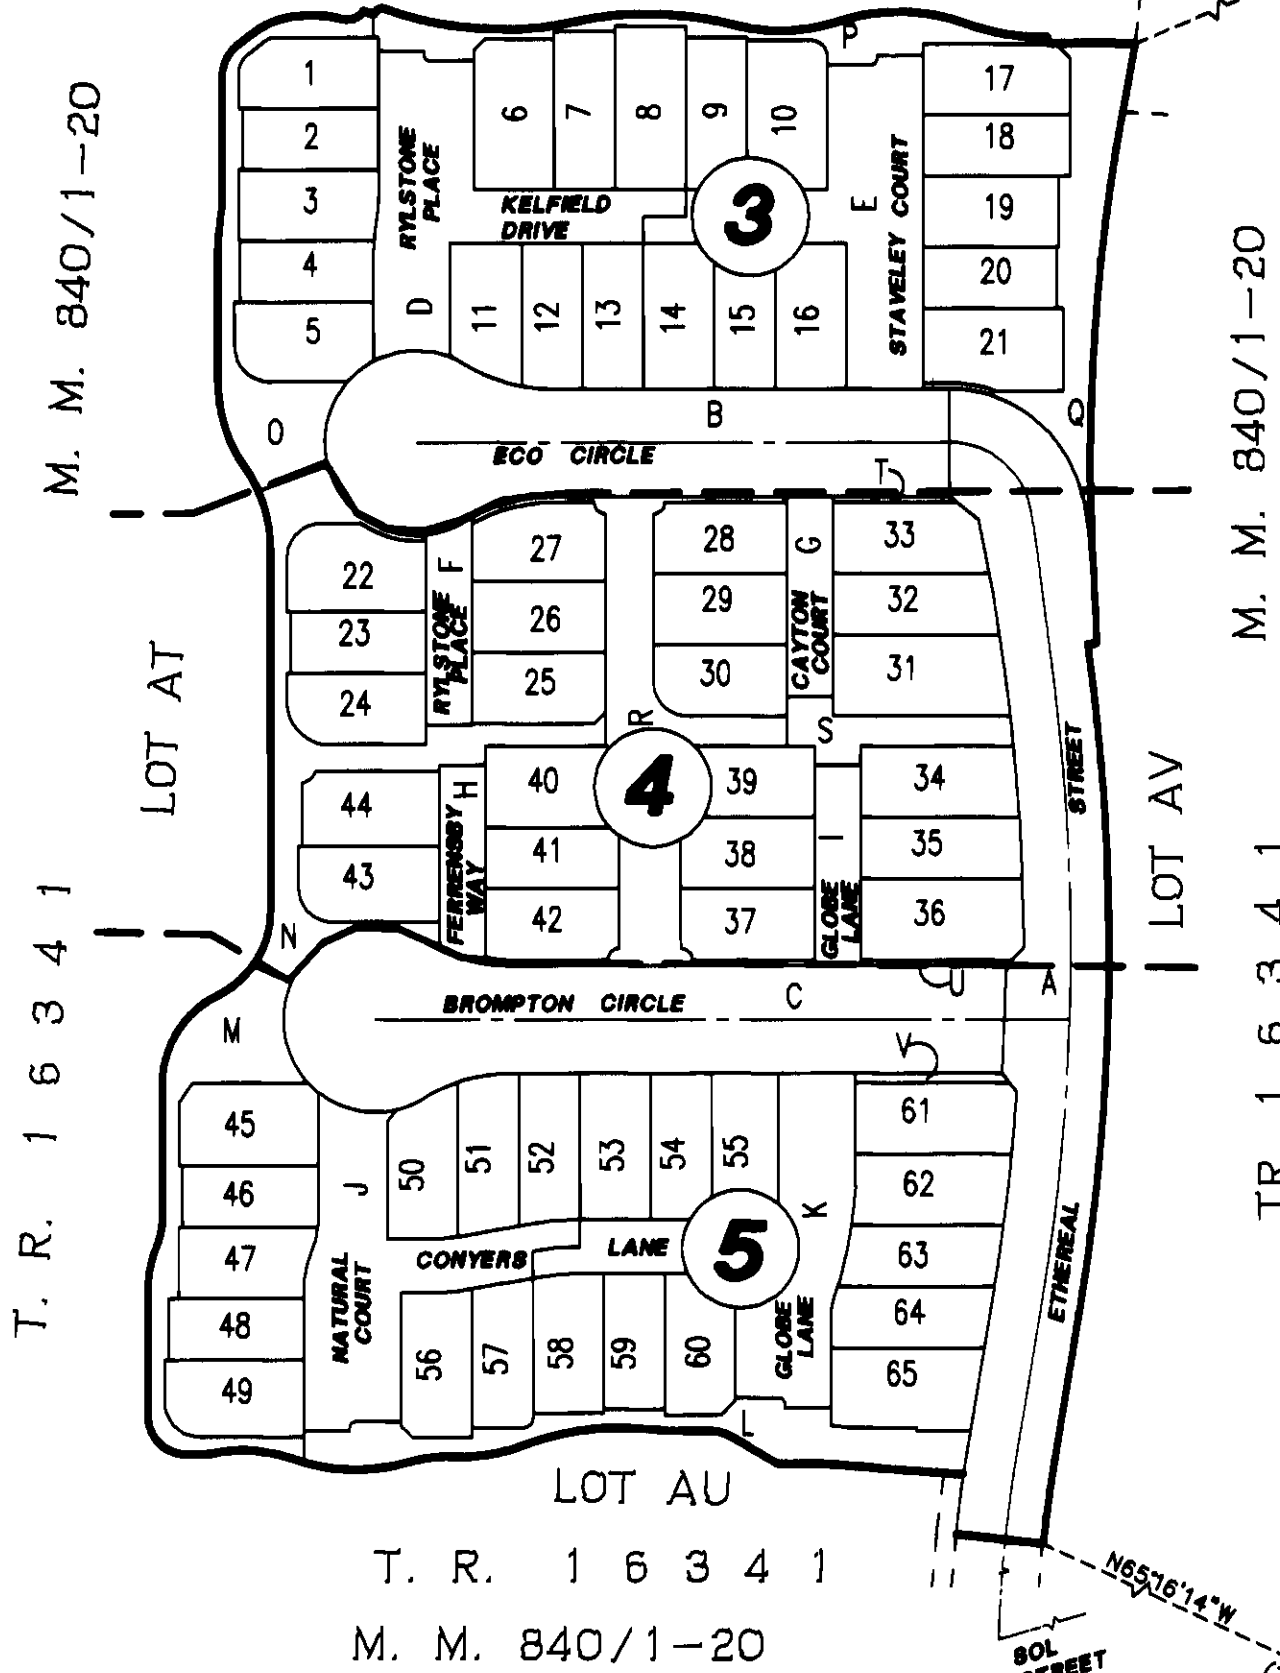

M. M. 840/1-20

TR. 1 6 3 4 1


T. R. 1 6 3 4 1
M. M. 840/1-20

SHEET INDEX AND GPS CONTROL

GPS NO. 1417

FOUND 2 1/2" IRON PIPE W/2" BRASS CAP
STAMPED "GPS 1417 9-95" PER TRACT
NO. 16025, MM 812/22-29 AND RECORDS
ON FILE IN THE ORANGE COUNTY SURVEYOR'S
OFFICE.
N 2141450.558
E 6141583.535

(X) - INDICATES SHEET NUMBER.

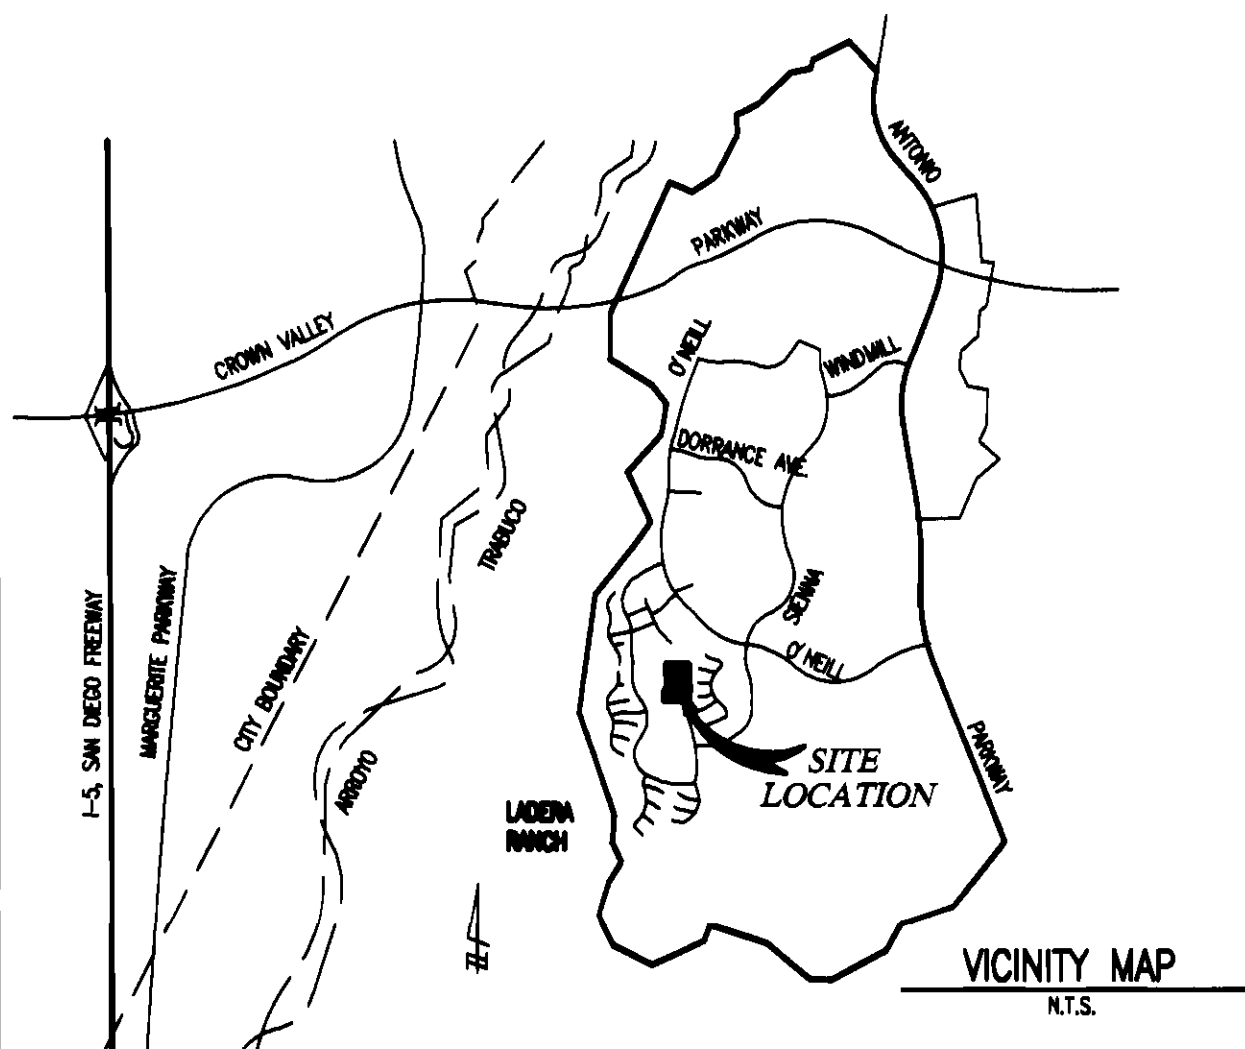


848 24

848 25

TRACT NO. 16348
IN THE UNINCORPORATED TERRITORY OF ORANGE COUNTY,
STATE OF CALIFORNIA
ADAMS-STREETER CIVIL ENGINEERS, INC. JAN A. ADAMS R.C.E. 21687
FEBRUARY 2003

SHEET 3 OF 6
SCALE: 1" = 30'
65 NUMBERED LOTS AND
LOTS A THROUGH V, INCLUSIVE
ACREAGE = 7.912 ACRES
A PORTION OF TENTATIVE
TRACT NO. 16341
DATE OF SURVEY: DECEMBER 2002

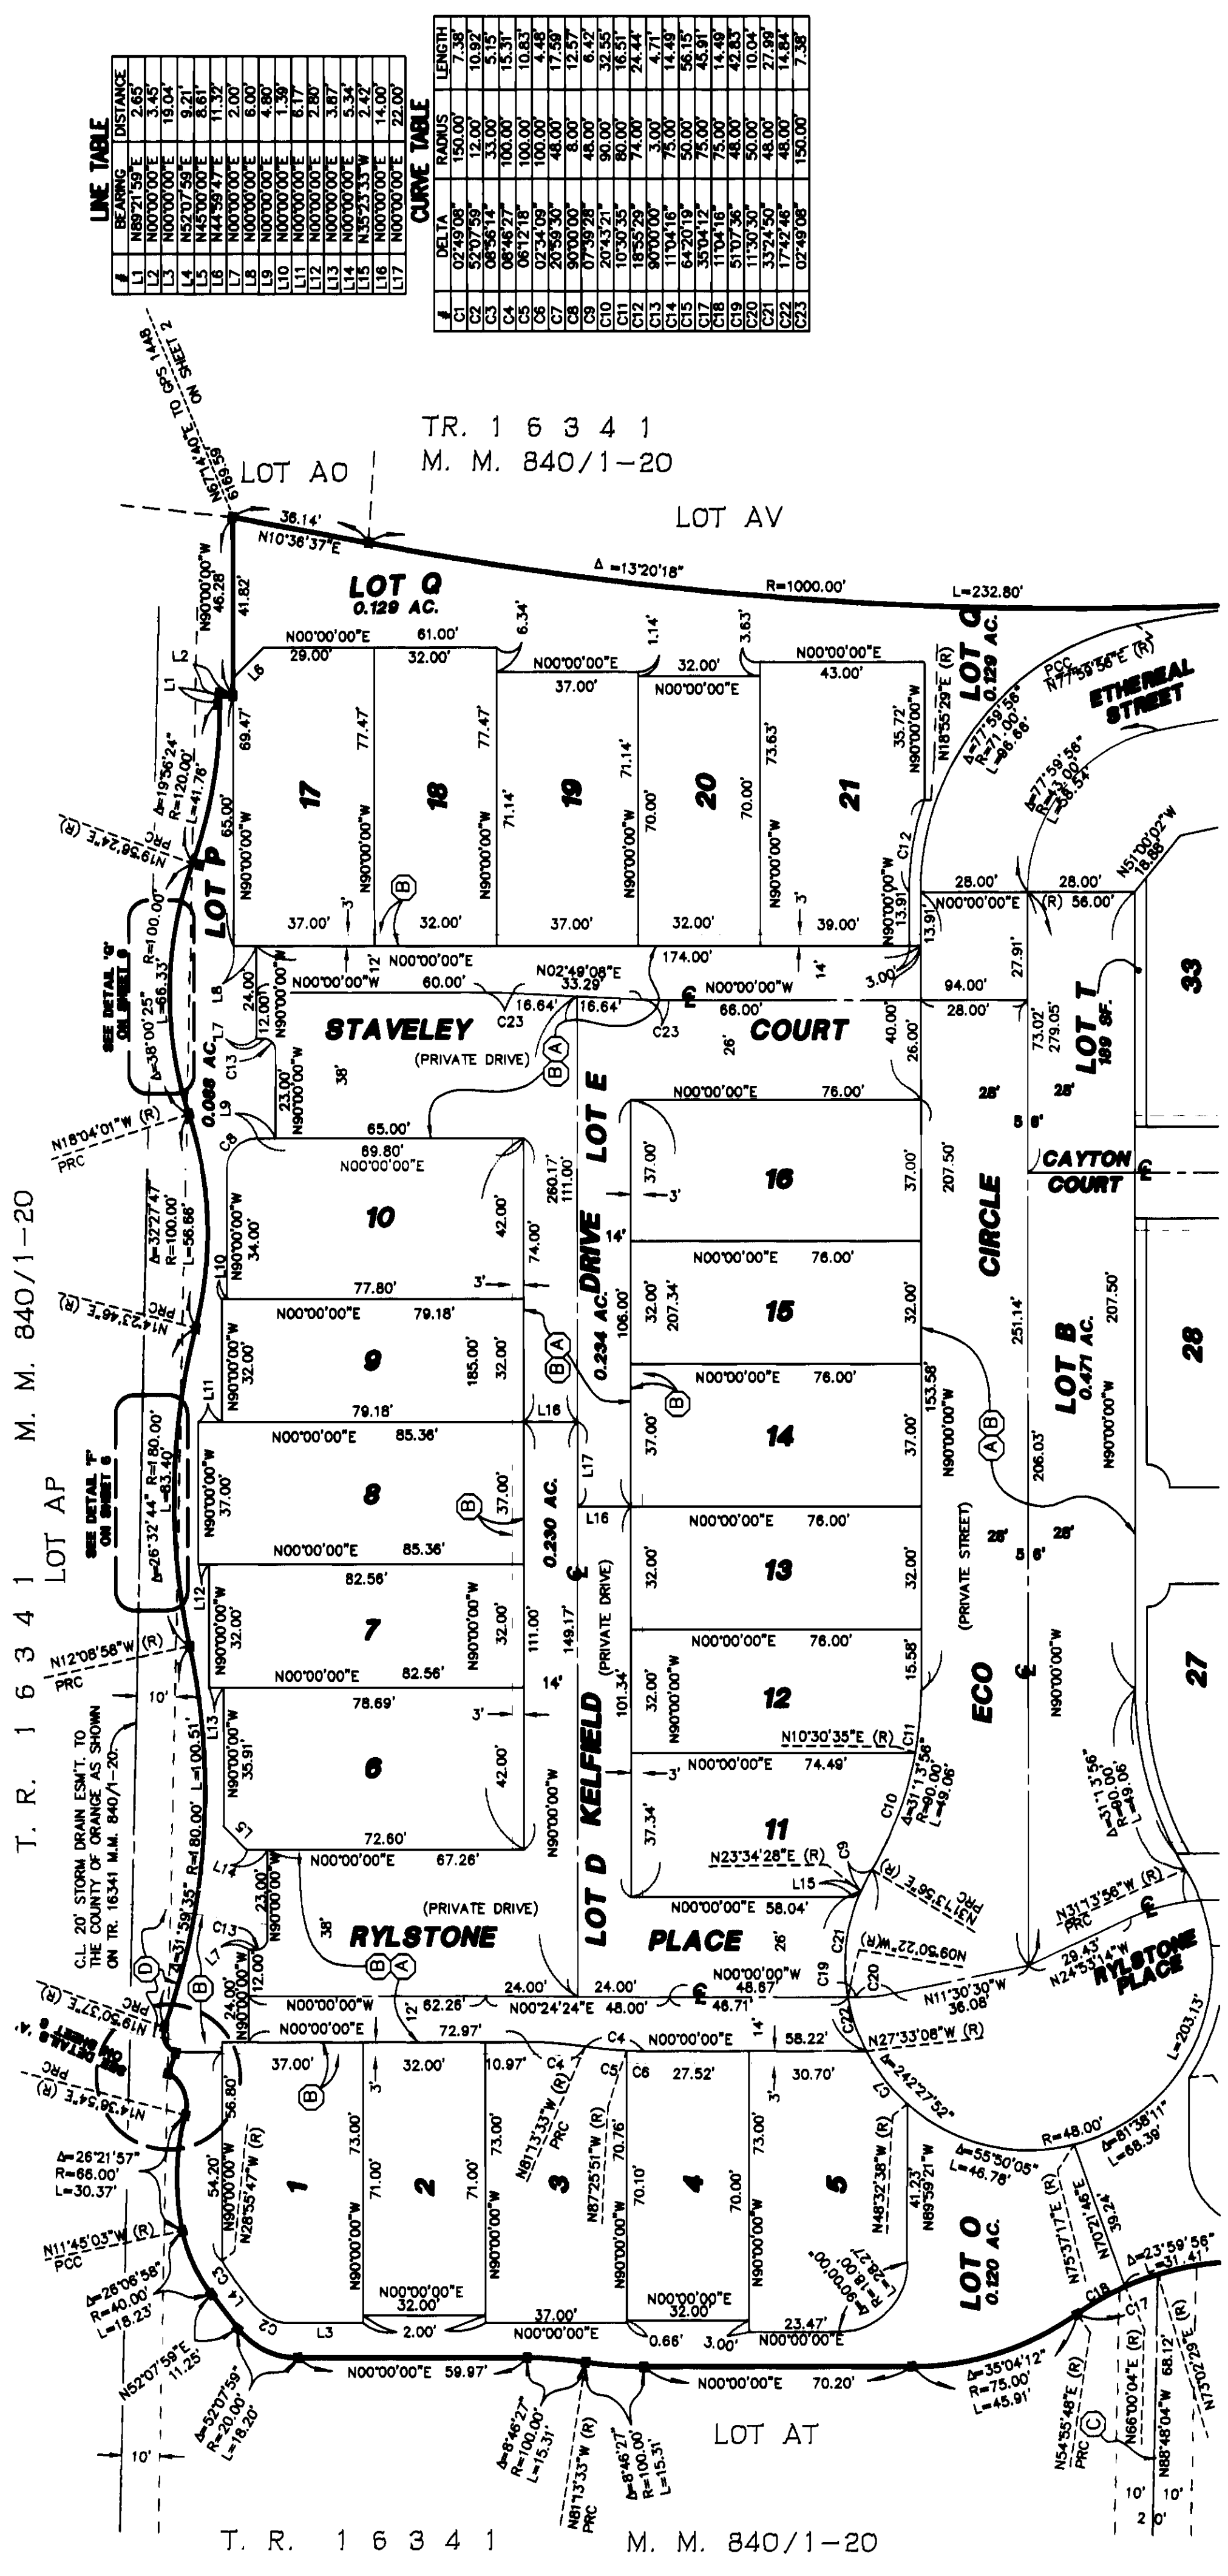

LINE TABLE

#	BEARING	DISTANCE
L1	N89°21'59"E	2.65
L2	N00°00'00"E	3.45
L3	N00°00'00"E	18.04
L4	N52°07'59"E	9.21
L5	N45°00'00"E	8.61
L6	N44°59'47"E	11.32
L7	N00°00'00"E	2.00
L8	N00°00'00"E	6.00
L9	N00°00'00"E	4.80
L10	N00°00'00"E	1.39
L11	N00°00'00"E	6.17
L12	N00°00'00"E	2.80
L13	N00°00'00"E	3.87
L14	N00°00'00"E	5.34
L15	N38°23'33"W	2.42
L16	N00°00'00"E	14.00
L17	N00°00'00"E	22.00

CURVE TABLE

#	DELTA	RADIUS	LENGTH
C1	02°49'08"	150.00	7.38
C2	52°07'59"	12.00	10.92
C3	08°56'14"	33.00	5.15
C4	08°46'27"	100.00	15.31
C5	08°12'18"	100.00	10.83
C6	02°34'09"	100.00	4.48
C7	20°59'30"	48.00	17.59
C8	90°00'00"	8.00	12.57
C9	07°59'28"	48.00	6.42
C10	20°43'21"	90.00	32.55
C11	10°30'35"	80.00	16.51
C12	18°55'29"	74.00	24.44
C13	90°00'00"	3.00	4.71
C14	11°04'16"	75.00	14.49
C15	64°20'19"	50.00	56.15
C16	35°04'12"	75.00	45.91
C17	11°04'16"	75.00	14.49
C18	51°07'36"	48.00	42.83
C19	11°30'30"	50.00	10.04
C20	33°24'50"	48.00	27.99
C21	17°42'46"	48.00	14.84
C22	02°49'08"	150.00	7.38

NOTE: SEE SHEET 2 FOR GPS CONTROL, SHEET INDEX, MONUMENT NOTES, EASEMENT NOTES, BASIS OF BEARINGS AND DATUM STATEMENTS.

LOTS A-C ARE NOT SEPARATE BUILDING SITES AND ARE FOR PRIVATE STREETS.

LOTS D-K ARE NOT SEPARATE BUILDING SITES AND ARE FOR PRIVATE DRIVES.

LOTS L-V ARE NOT SEPARATE BUILDING SITES AND ARE FOR LANDSCAPING PURPOSES.

ALL BEARINGS AND DISTANCES SHOWN ALONG THE MAP BOUNDARY ARE MEASURED AND RECORD PER TR. 16341 M.M. 840/1-20

SHEET 4 OF 6
SCALE: 1" = 30'
65 NUMBERED LOTS AND
LOTS A THROUGH V, INCLUSIVE
ACREAGE = 7.912 ACRES
A PORTION OF TENTATIVE
TRACT NO. 16341
DATE OF SURVEY: DECEMBER 2002

TRACT NO. 16348

IN THE UNINCORPORATED TERRITORY OF ORANGE COUNTY,
STATE OF CALIFORNIA


ADAMS-STREETER CIVIL ENGINEERS, INC. JAN A. ADAMS R.C.E. 21687
FEBRUARY 2003

SEE LEAF 3

NOTE: SEE SHEET 2 FOR GPS CONTROL, SHEET INDEX, MONUMENT NOTES, EASEMENT NOTES, BASIS OF BEARINGS AND DATUM STATEMENTS.

ALL BEARINGS AND DISTANCES SHOWN ALONG THE MAP BOUNDARY ARE MEASURED AND
RECORDED PER TR. 16341 N.M. 840/1-20



LOTS A-C ARE NOT SEPARATE BUILDING SITES AND ARE FOR PRIVATE STREETS.
LOTS D-K ARE NOT SEPARATE BUILDING SITES AND ARE FOR PRIVATE DRIVES.
LOTS L-V ARE NOT SEPARATE BUILDING SITES AND ARE FOR LANDSCAPING PURPOSES.

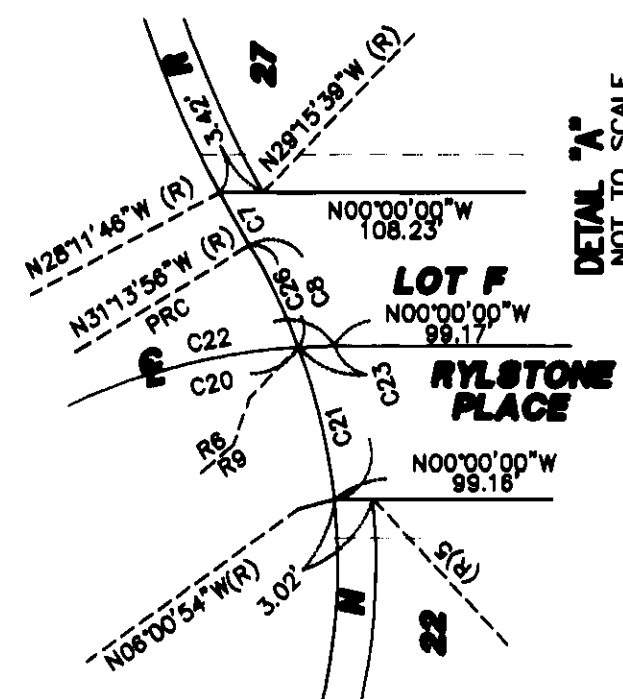

#	BEARING
R1	N30°42'44"E
R2	N83°16'04"E
R3	N61°56'34"W
R4	N19°27'15"W
R5	N05°39'36"W
R6	N20°40'40"W R=48'
R7	N08°39'33"E
R8	N16°29'33"E
R9	N86°45'02"E R=50'

#	BEARING	DISTANCE
L1	N 45°00'00"E	4.24'
L2	N 00°00'00"E	16.00'
L3	N 00°00'00"E	9.10'
L4	N 00°00'00"E	10.00'
L5	N 00°00'00"E	14.28'
L6	N 90°00'00"W	24.00'
L7	N 90°00'00"W	12.00'

	δ	DELTA	RADIUS	LENGTH
C1	90.0000	90.0000	6.00	9.42
C2	90.0000	90.0000	6.00	9.42
C3	45.0000	45.0000	18.00	14.14
C4	32.3320	32.3320	17.00	9.88
C5	08.5737	08.5737	87.00	13.61
C6	42.2918	42.2918	13.25	9.83
C7	03.0210	03.0210	90.00	4.77
C8	25.1302	25.1302	48.00	21.13
C9	16.3130	16.3130	90.00	26.48
C10	26.3619	26.3619	10.00	4.99
C11	05.4233	05.4233	90.00	8.38
C12	28.1148	28.1148	44.29	44.29
C13	08.3933	08.3933	90.00	13.60
C14	00.3056	00.3056	1078.00	15.97
C15	04.3873	04.3873	90.00	7.29
C16	00.3733	00.3733	500.00	8.37
C17	35.0412	35.0412	75.00	45.91
C18	11.0416	11.0416	75.00	14.49
C19	41.0927	41.0927	50.00	35.92
C20	21.3816	21.3816	50.00	18.88
C21	20.3816	20.3816	50.00	12.28
C22	24.8314	24.8314	50.00	21.72
C23	03.1458	03.1458	50.00	2.84
C24	09.0130	09.0130	90.00	14.18
C25	07.5600	07.5600	90.00	12.30
C26	10.3316	10.3316	48.00	8.84
C27	00.3316	00.3316	48.00	8.84

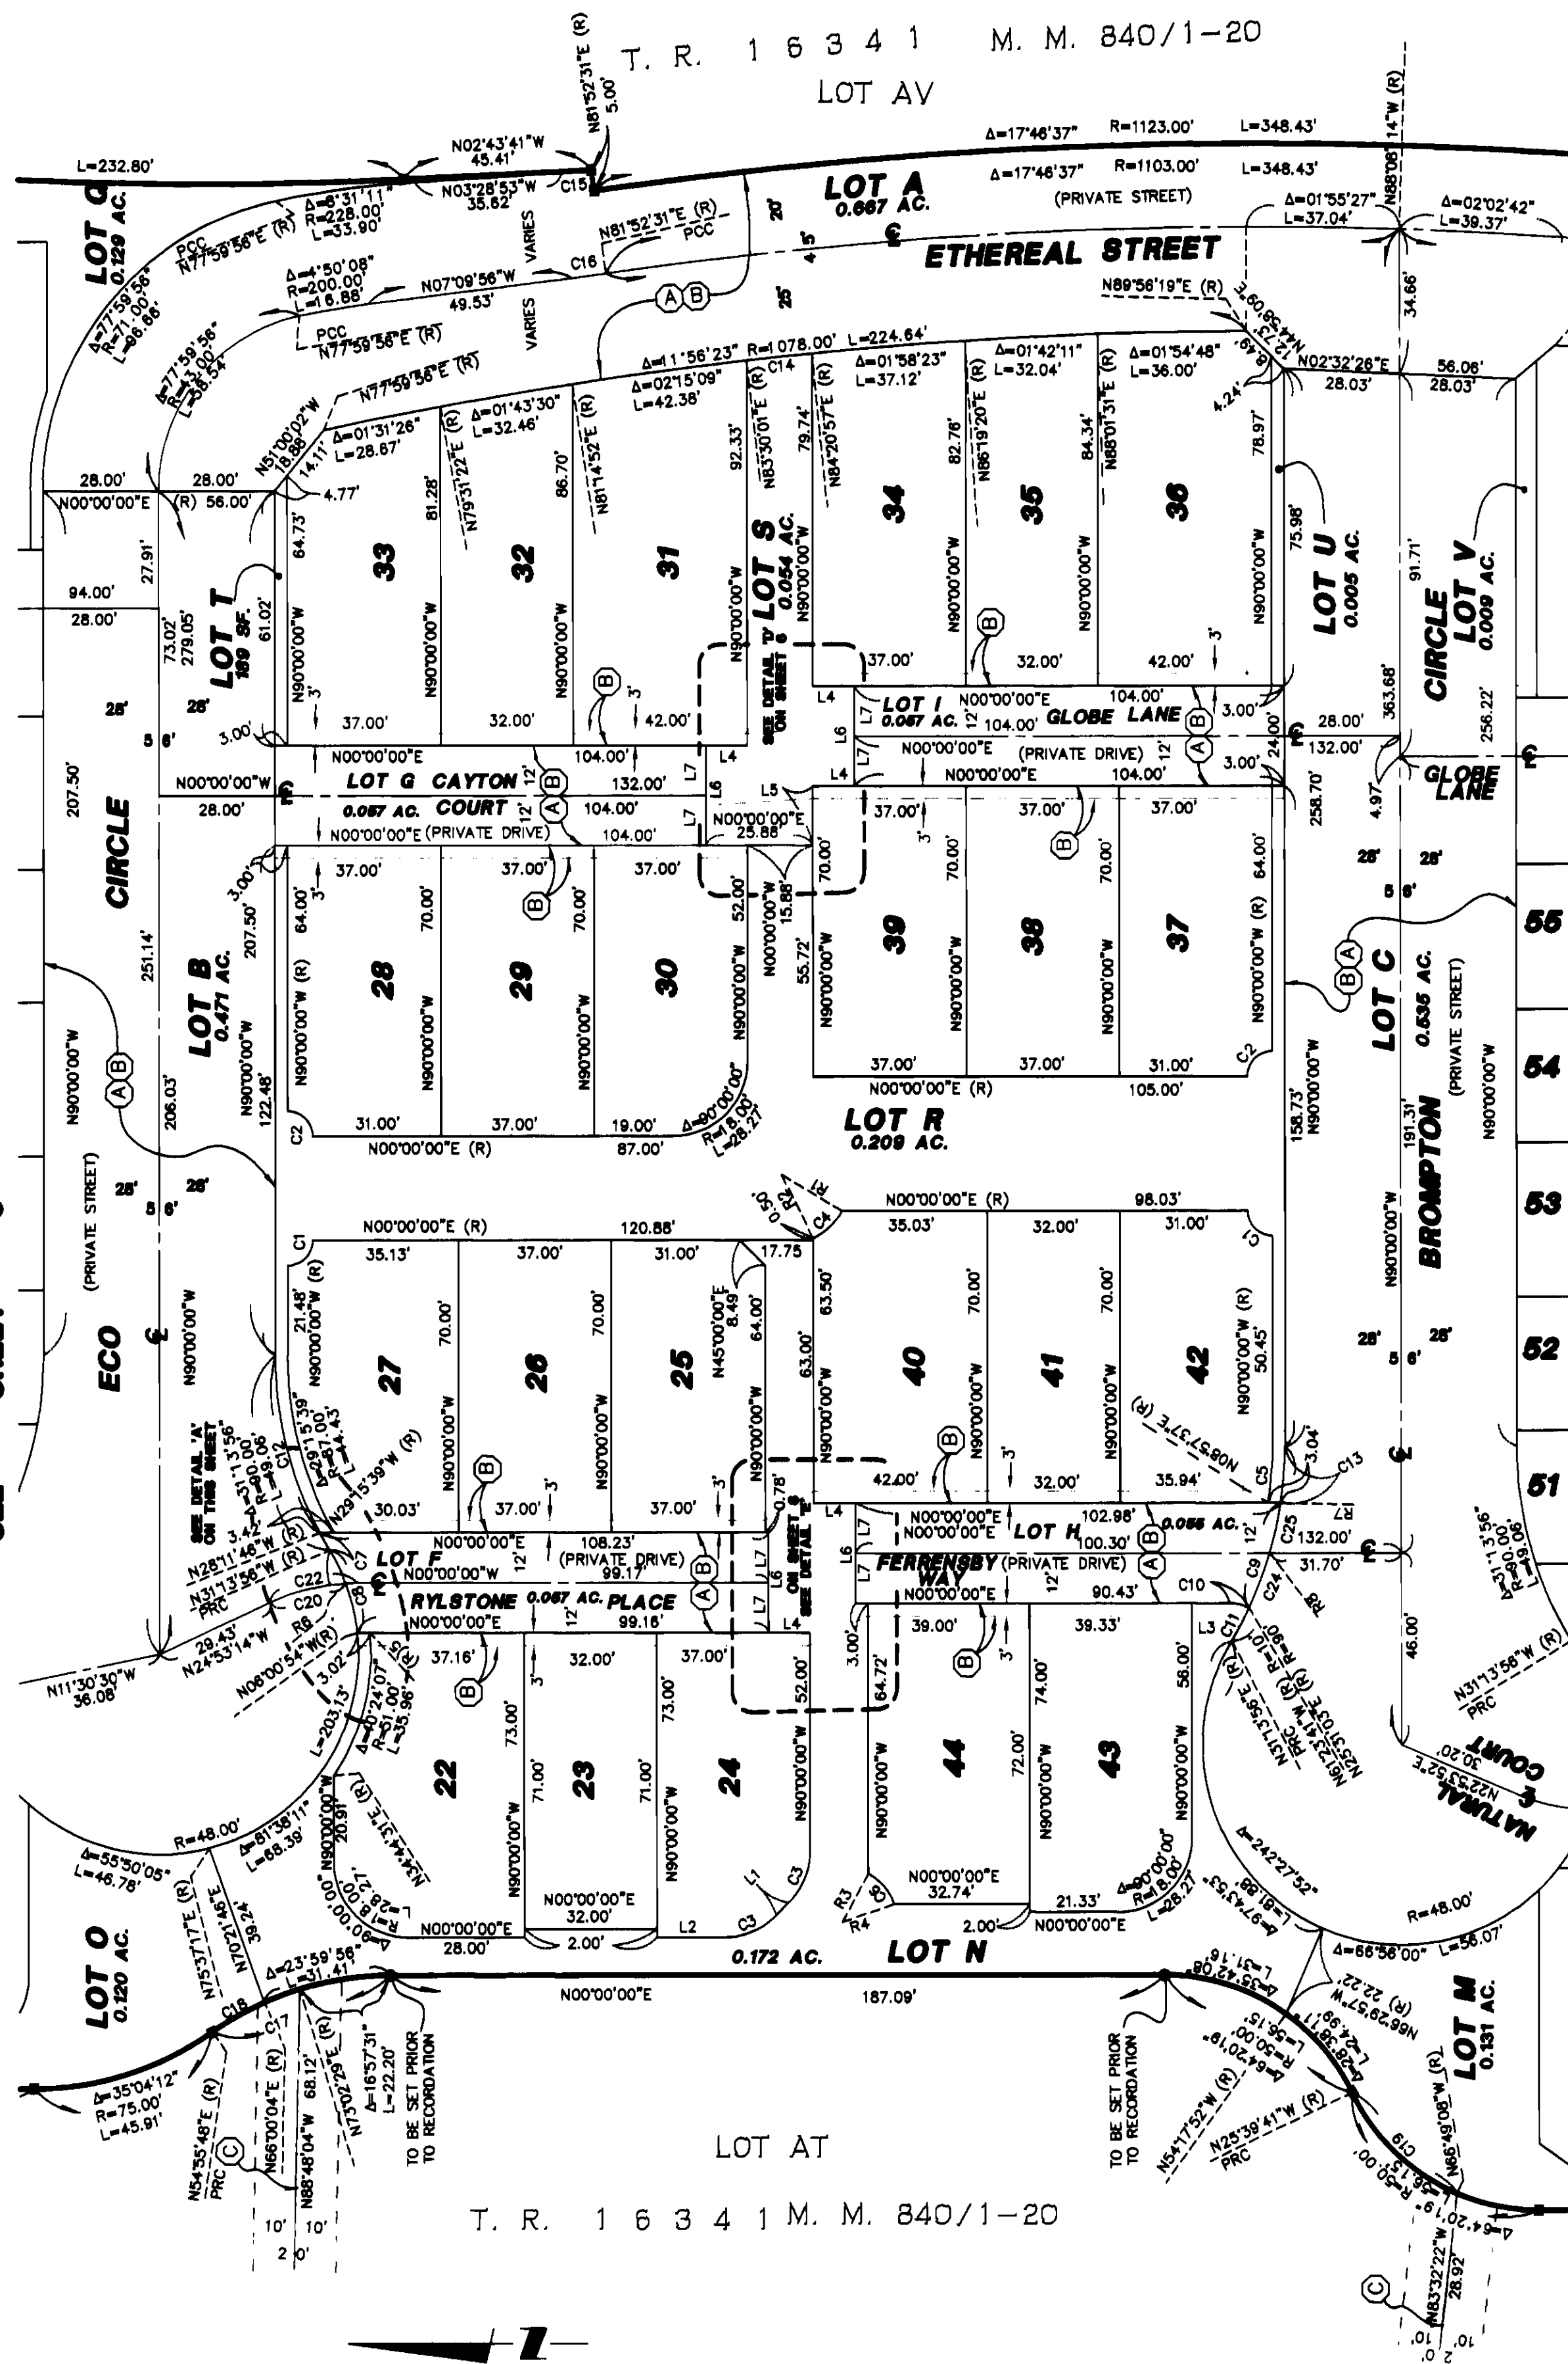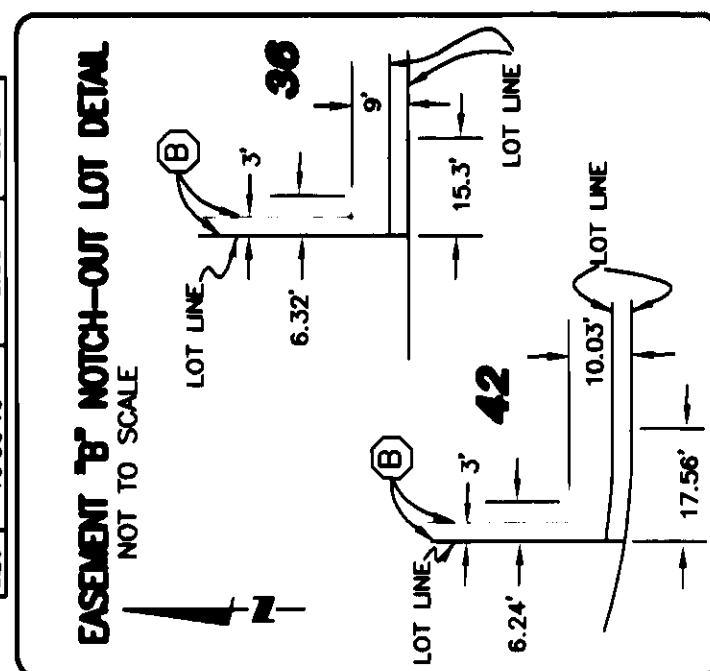

revised: 6-13-03

848 27

SHEET 5 OF 6

SCALE: 1" = 30'

65 NUMBERED LOTS AND
LOTS A THROUGH V, INCLUSIVE
ACREAGE = 7.912 ACRES
A PORTION OF TENTATIVE
TRACT NO. 16341

DATE OF SURVEY: DECEMBER 2002

TRACT NO. 16348


IN THE UNINCORPORATED TERRITORY OF ORANGE COUNTY,
STATE OF CALIFORNIA

ADAMS-STREETER CIVIL ENGINEERS, INC. JAN A. ADAMS R.C.E. 21687
FEBRUARY 2003

SEE SHEET 4

NOTE: SEE SHEET 2 FOR GPS CONTROL, SHEET INDEX, MONUMENT NOTES,
EASEMENT NOTES, BASIS OF BEARINGS AND DATUM STATEMENTS.

LOTS A-C ARE NOT SEPARATE BUILDING SITES AND ARE FOR PRIVATE STREETS.
LOTS D-K ARE NOT SEPARATE BUILDING SITES AND ARE FOR PRIVATE DRIVES.
LOTS L-V ARE NOT SEPARATE BUILDING SITES AND ARE FOR LANDSCAPING PURPOSES.
ALL BEARINGS AND DISTANCES SHOWN ALONG THE MAP BOUNDARY ARE MEASURED AND
RECORD PER TR. 16341 M.M. 840/1-20

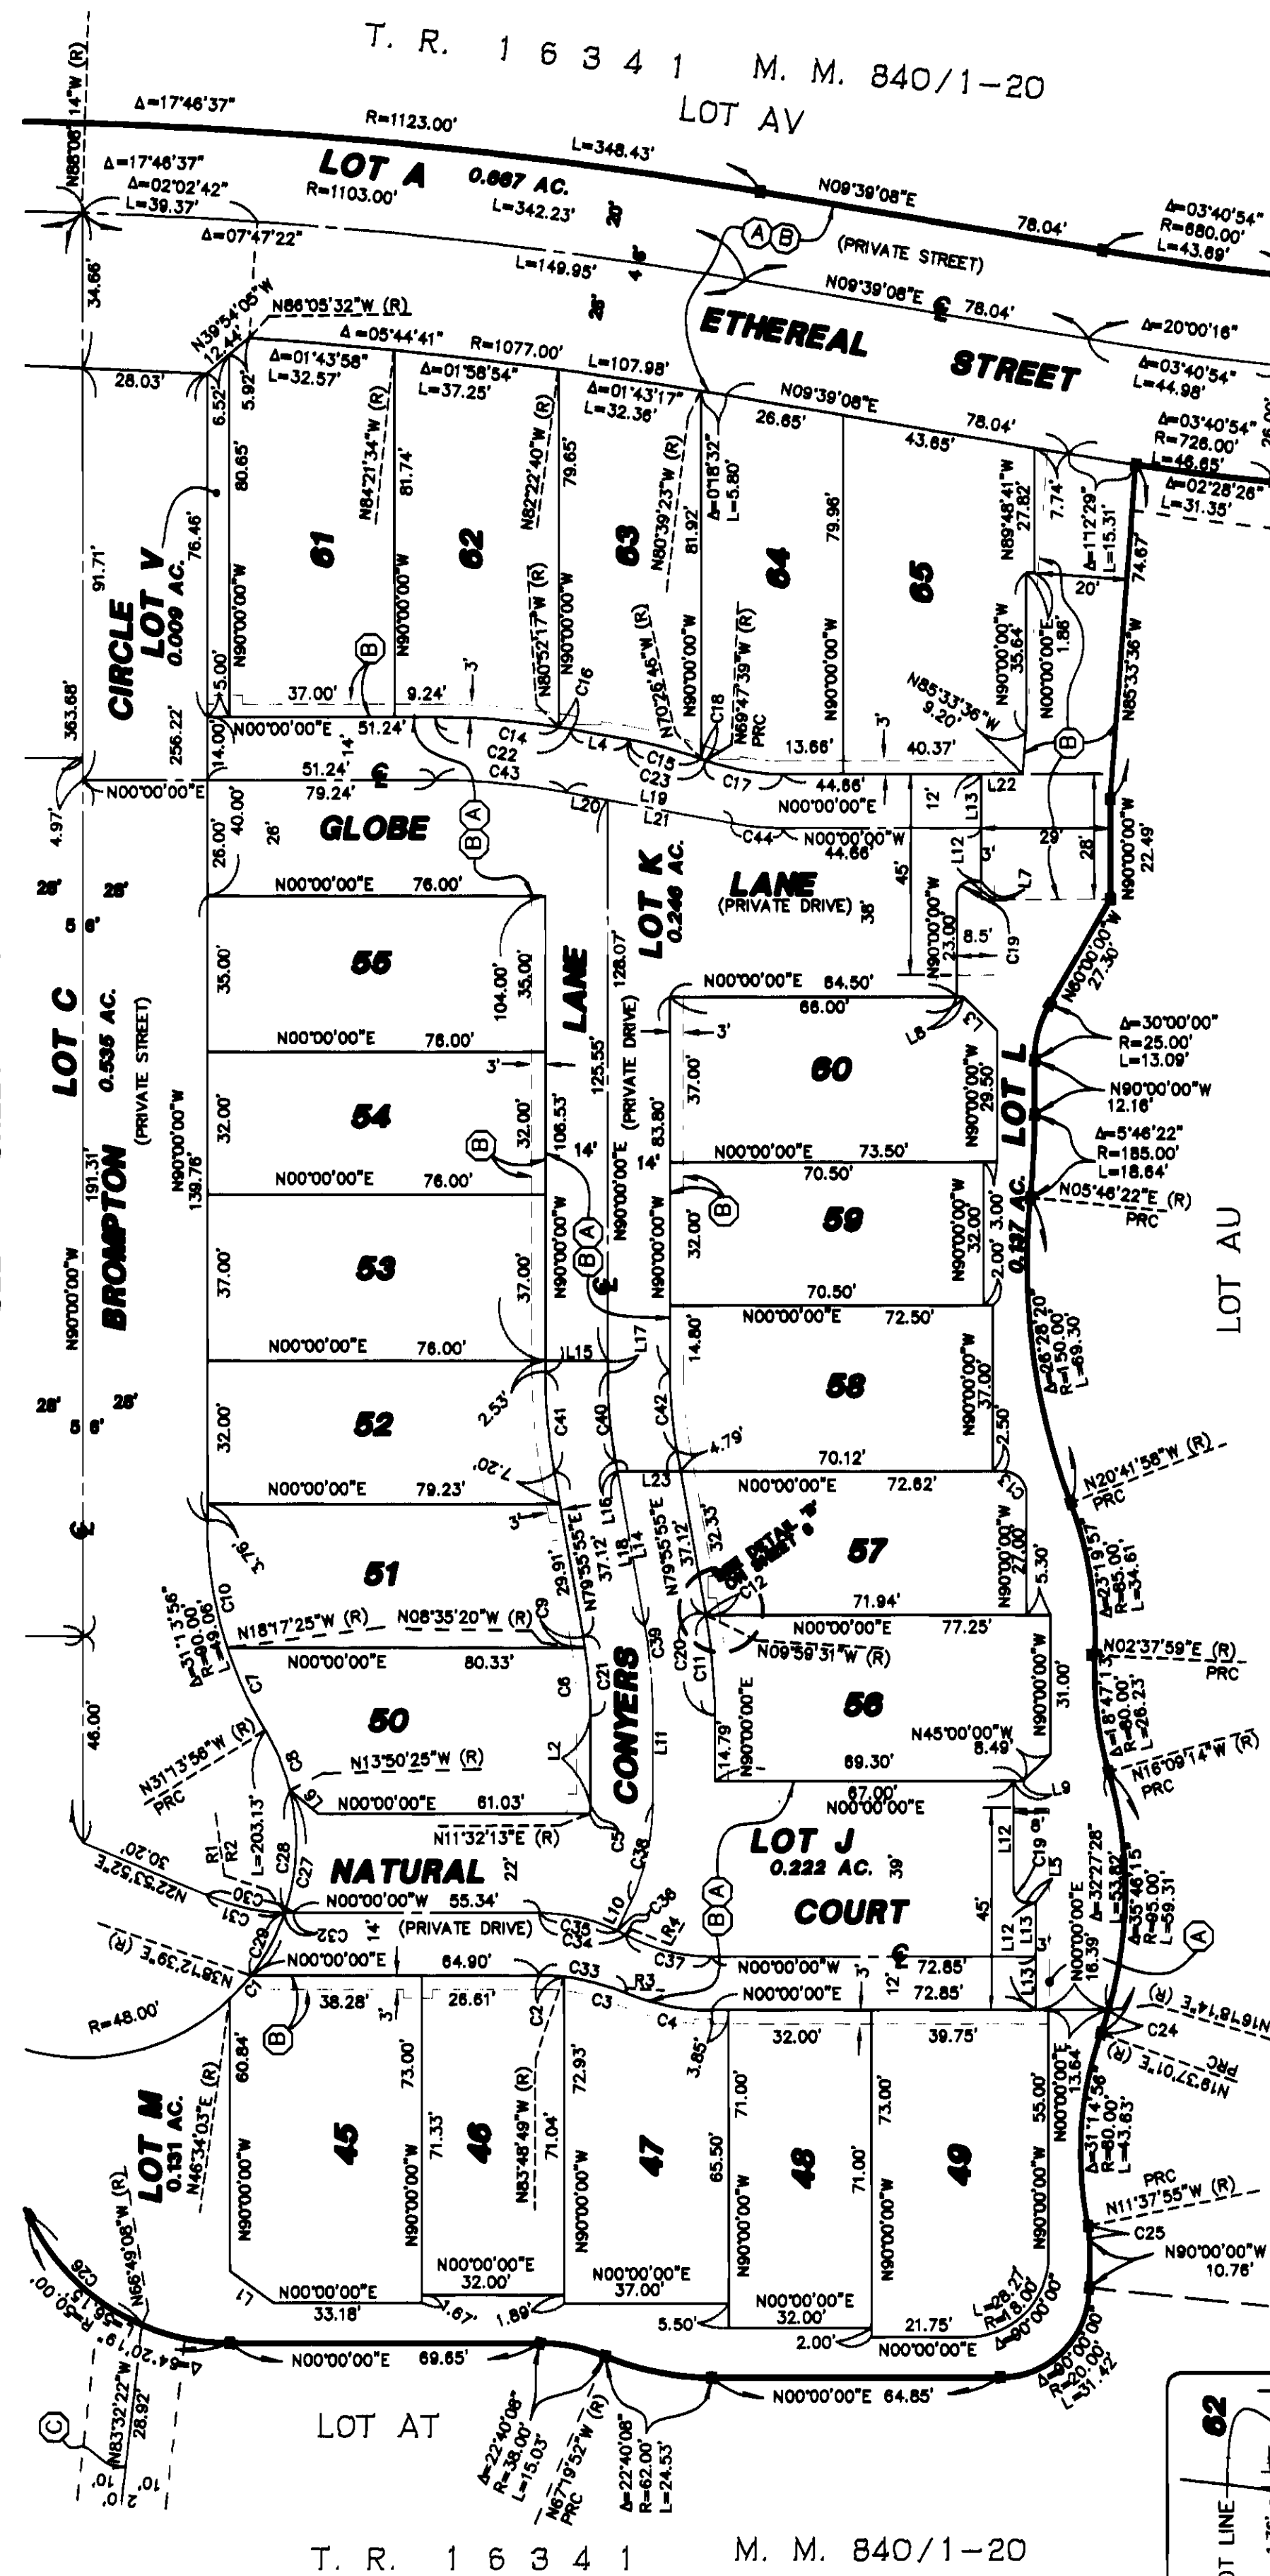

RADIAL TABLE


#	BEARING	DISTANCE
R1	N19°02'04"E	R=48.00'
R2	N87°48'21"W	R=50.00'
R3	N67°19'52"W	PRC
R4	N81°40'31"W	PRC

LINE TABLE

#	BEARING	DISTANCE
L1	N35°27'02"E	12.06'
L2	N90°00'00"W	20.07'
L3	N43°50'00"E	10.81'
L4	N10°03'39"E	13.40'
L5	N00°00'00"E	2.00'
L6	N40°00'00"W	8.05'
L7	N00°00'00"E	2.50'
L8	N00°00'00"E	1.50'
L9	N00°00'00"E	2.30'
L10	N64°32'17"W	7.14'
L11	N00°00'00"W	20.07'
L12	N00°00'00"W	21.00'
L13	N90°00'00"W	12.00'
L14	N79°55'55"W	37.12'
L15	N00°00'00"E	14.00'
L16	N79°55'55"W	2.30'
L17	N90°00'00"W	2.53'
L18	N79°55'55"W	34.82'
L19	N10°34'13"E	37.84'
L20	N10°34'13"E	9.39'
L21	N10°34'13"E	28.45'
L22	N00°00'00"E	9.37'
L23	N00°00'00"E	14.22'

CURVE TABLE

#	DELTA	RADIUS	LENGTH
C1	08°21'24"	48.00'	7.00'
C2	08°11'11"	50.00'	5.40'
C3	16°28'57"	50.00'	14.38'
C4	22°40'08"	50.00'	18.78'
C5	11°32'13"	10.00'	2.01'
C6	08°35'20"	100.00'	14.89'
C7	12°28'31"	90.00'	20.33'
C8	17°23'31"	48.00'	14.37'
C9	01°28'45"	100.00'	2.38'
C10	18°17'25"	90.00'	24.73'
C11	09°58'31"	128.00'	22.97'
C12	00°04'43"	128.00'	0.17'
C13	30°00'00"	5.00'	7.85'
C14	30°00'00"	15.00'	27.88'
C15	09°07'34"	100.00'	19.87'
C16	09°58'31"	100.00'	9.58'
C17	20°12'31"	50.00'	17.83'
C18	30°00'00"	100.00'	1.14'
C19	30°00'00"	3.00'	4.71'
C20	10°03'39"	18.00'	29.49'
C21	10°03'39"	100.00'	17.37'
C22	10°03'39"	173.00'	30.73'
C23	10°08'42"	100.00'	17.78'
C24	03°18'47"	93.00'	3.08'
C25	11°37'35"	18.00'	3.85'
C26	41°09'27"	30.00'	33.92'
C27	32°03'04"	48.00'	13.81'
C28	19°10'35"	48.00'	16.07'
C29	32°32'29"	48.00'	27.54'
C30	22°53'52"	50.00'	19.98'
C31	20°43'13"	50.00'	18.08'
C32	02°10'39"	50.00'	1.90'
C33	22°40'08"	50.00'	19.78'
C34	28°19'29"	40.81'	20.08'
C35	25°27'43"	40.81'	18.05'
C36	02°51'45"	40.81'	2.03'
C37	28°19'29"	40.81'	20.08'
C38	25°27'43"	50.00'	20.03'
C39	10°04'05"	114.00'	20.03'
C40	10°04'05"	128.00'	22.49'
C41	10°04'05"	100.00'	17.57'
C42	10°04'05"	161.00'	28.70'
C43	10°34'13"	62.00'	11.44'

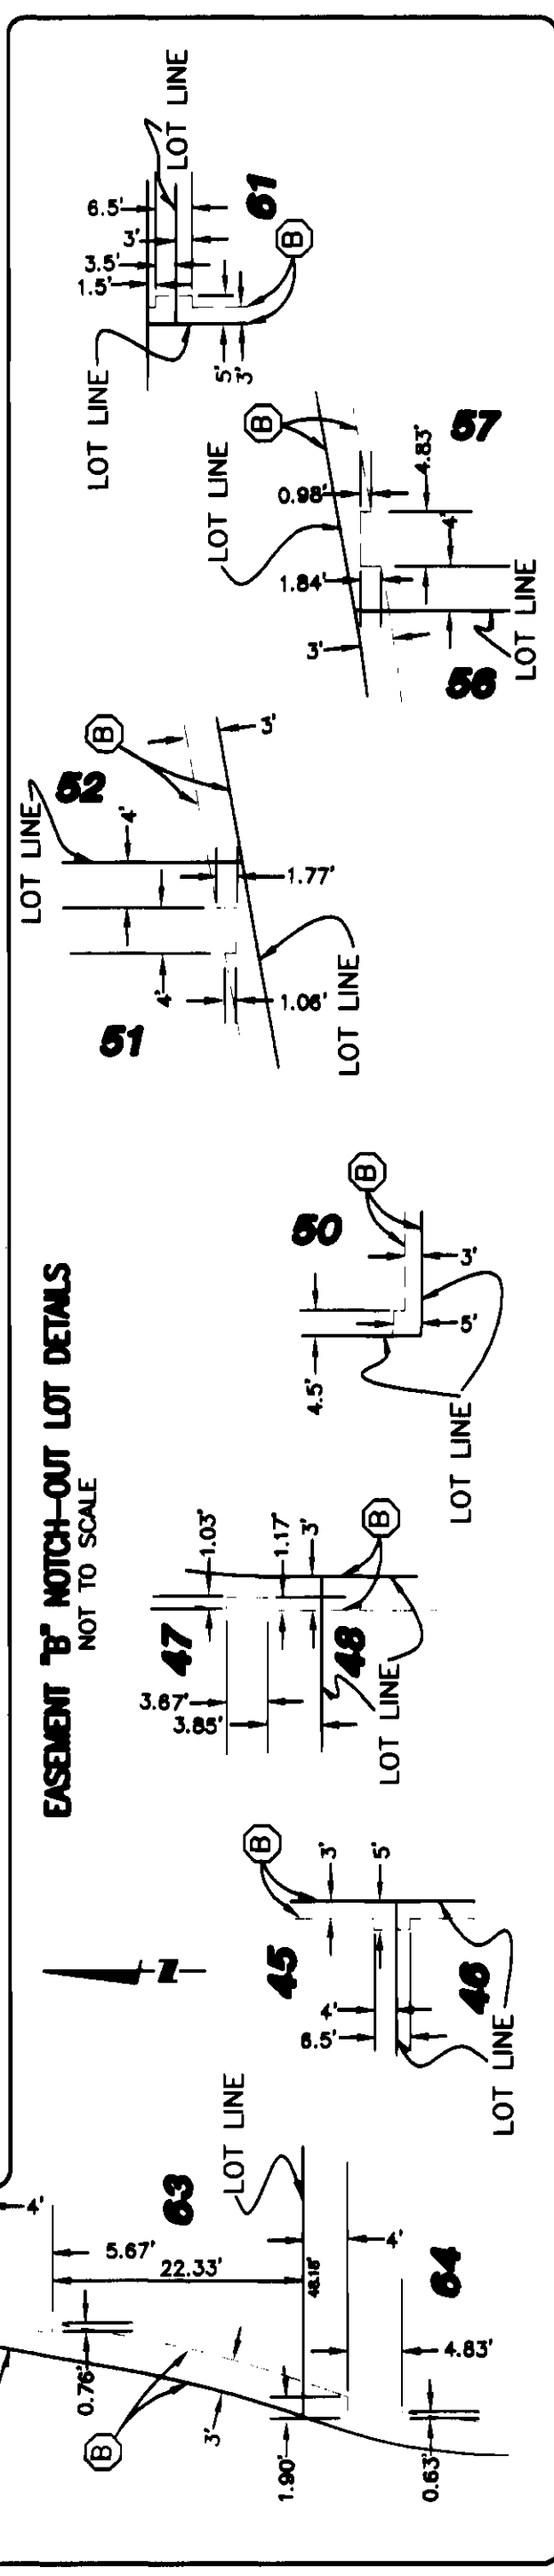

848 28

TRACT NO. 16348

IN THE UNINCORPORATED TERRITORY OF ORANGE COUNTY,
STATE OF CALIFORNIA

65 NUMBERED LOTS AND
LOTS A THROUGH V, INCLUSIVE

ACREAGE = 7.912 ACRES

A PORTION OF TENTATIVE
TRACT NO. 16341

DATE OF SURVEY: DECEMBER 2002


ADAMS-STREETER CIVIL ENGINEERS, INC.

JAN A. ADAMS R.C.E. 21687


FEBRUARY

2003


DETAIL SHEET

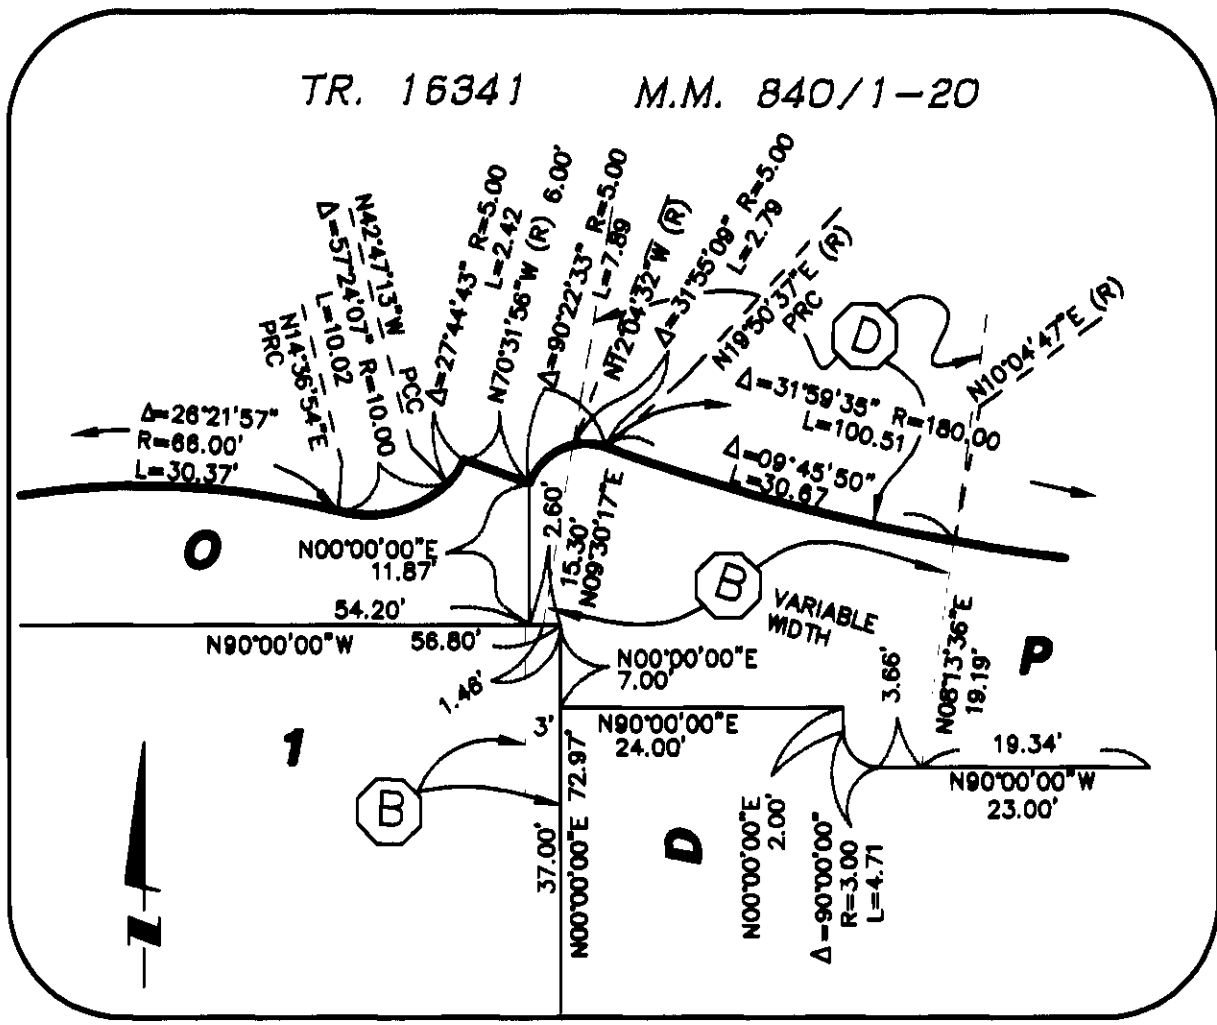


DETAIL 'A'
NOT TO SCALE
(SHEET 3)

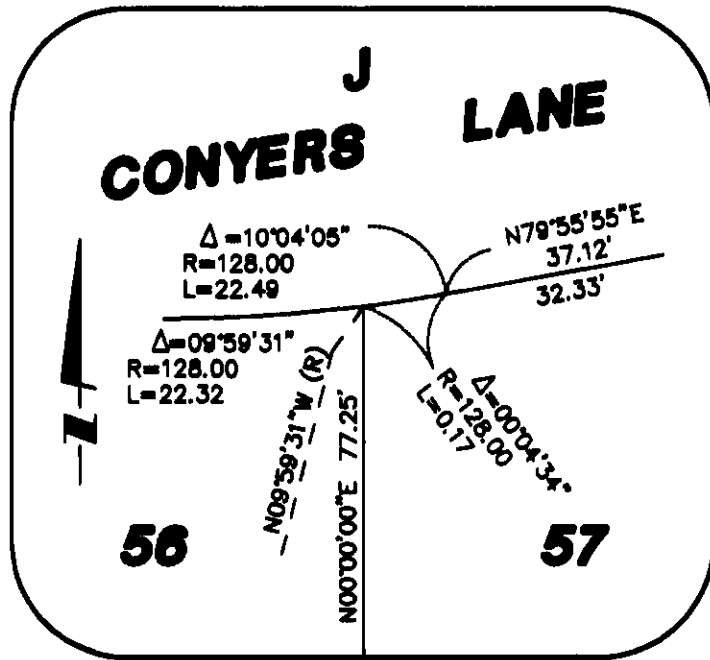

DETAIL 'B'
NOT TO SCALE
(SHEET 5)

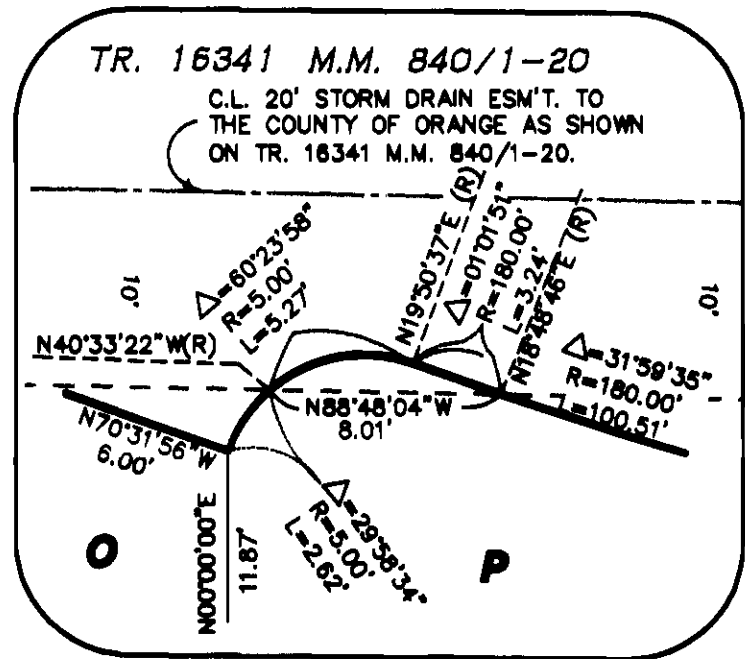


DETAIL 'C'
NOT TO SCALE
(SHEET 3)

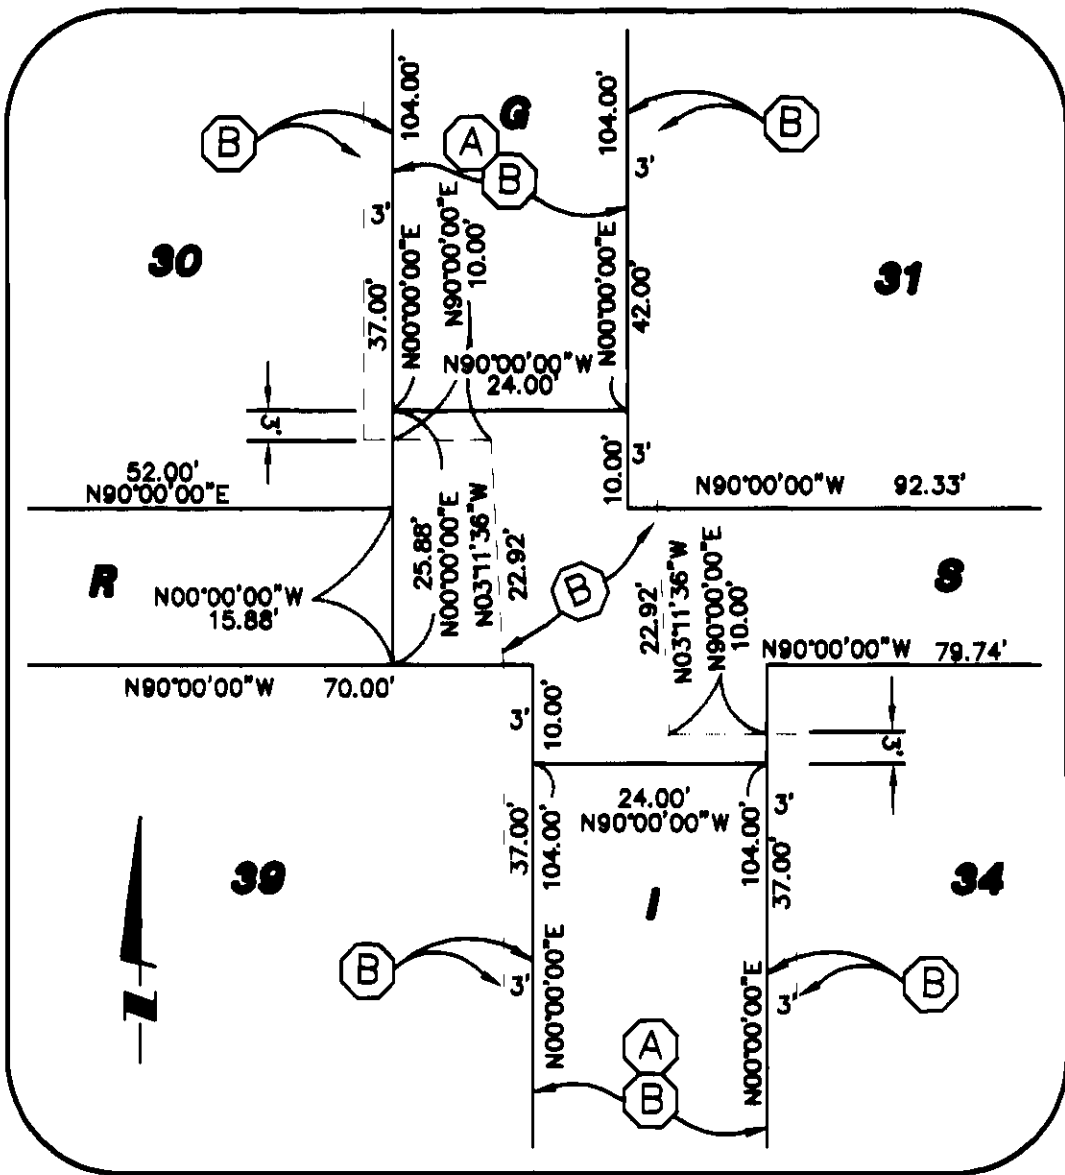


STREET CENTERLINES HAVE BEEN REMOVED FOR CLARITY

DETAIL 'D'
NOT TO SCALE
(SHEET 4)

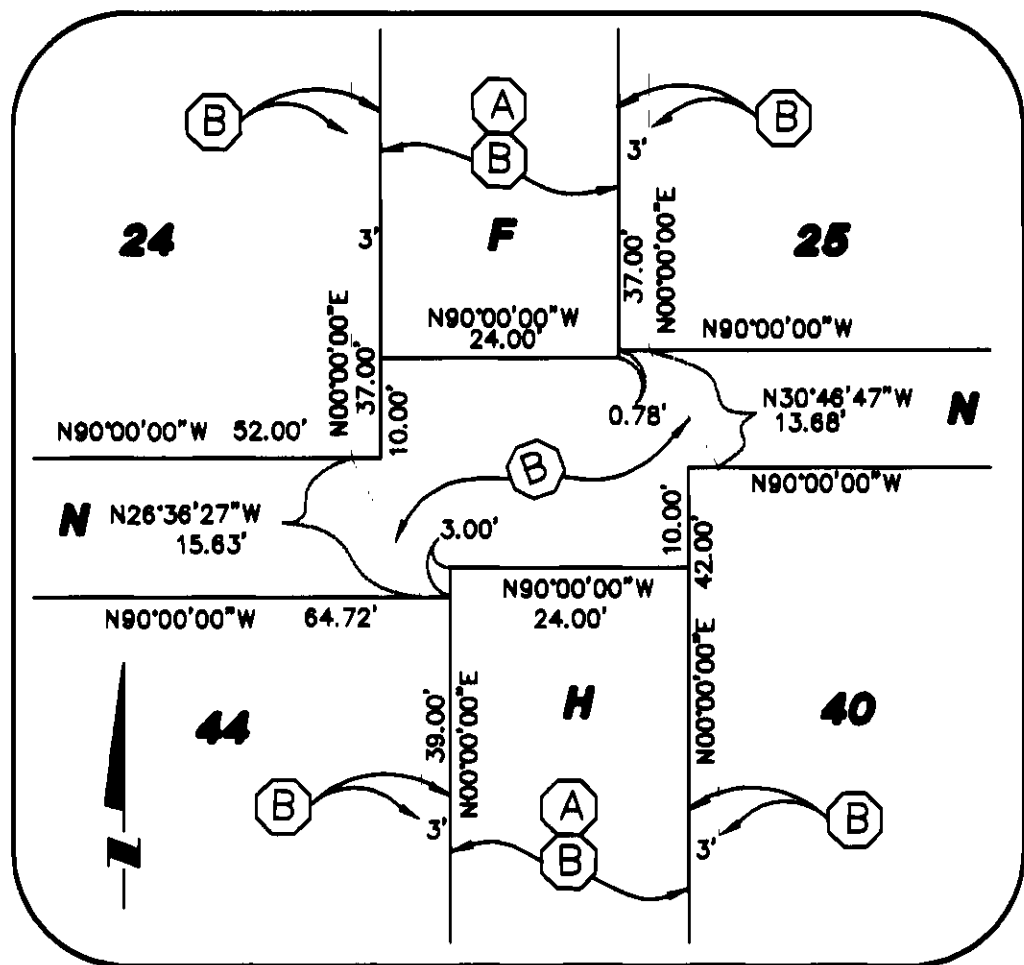


STREET CENTERLINES HAVE BEEN REMOVED FOR CLARITY

DETAIL 'E'
NOT TO SCALE
(SHEET 4)

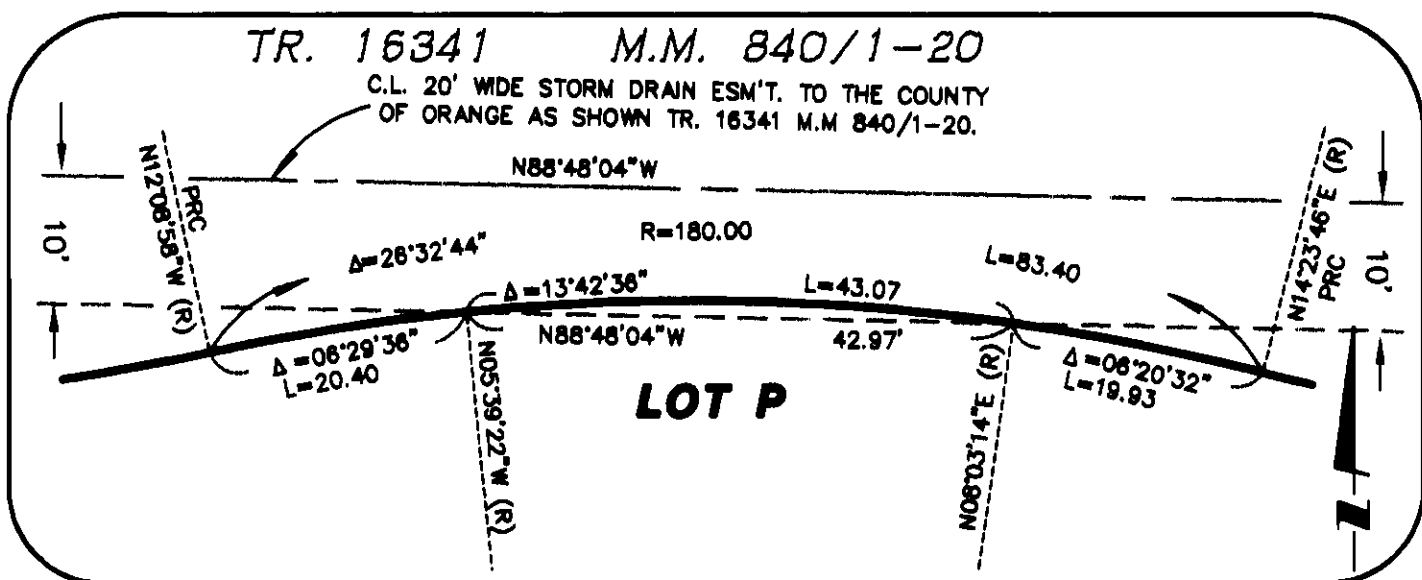

DETAIL 'F'
NOT TO SCALE
(SHEET 3)

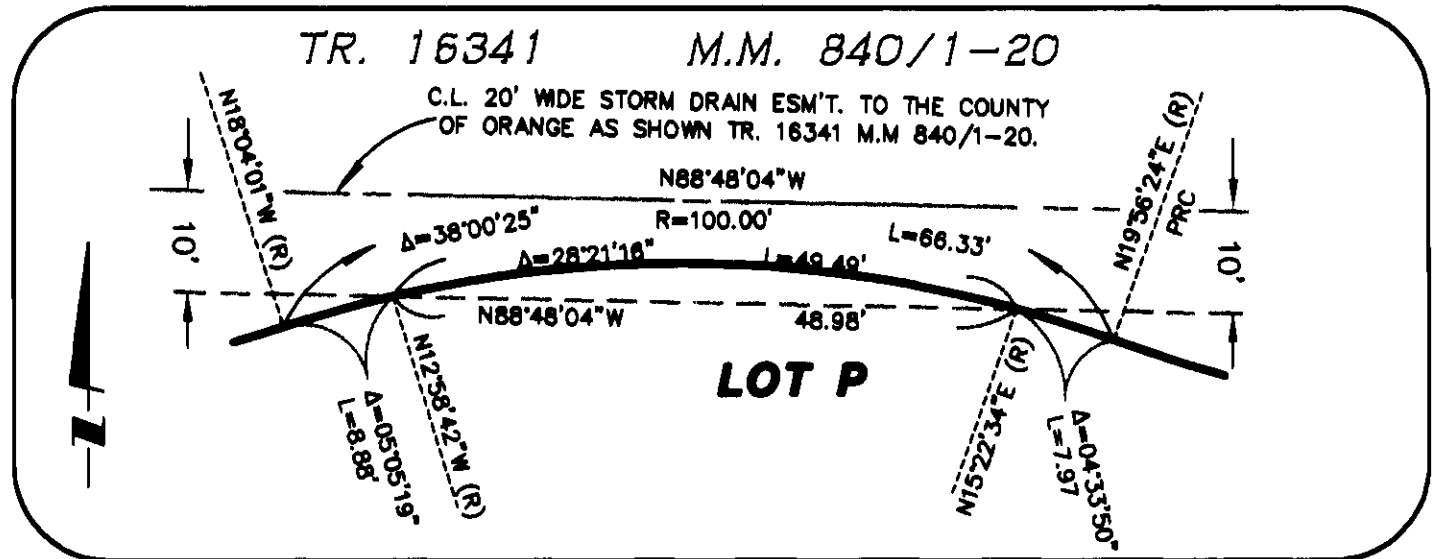

DETAIL 'G'
NOT TO SCALE
(SHEET 3)

NOTE: SEE SHEET 2 FOR GPS CONTROL, SHEET INDEX, MONUMENT NOTES,
EASEMENT NOTES, BASIS OF BEARINGS AND DATUM STATEMENTS.

848 28