

SHEET 1 OF 5 SHEETS

9.186 ACRES

41 NUMBERED LOTS AND  
LETTERED LOTS "A" AND "B"

DATE OF SURVEY: MARCH 2003

(ALL OF VESTING TENTATIVE  
TRACT No. 16351)

## TRACT NO. 16351

IN THE UNINCORPORATED TERRITORY OF THE COUNTY OF ORANGE, STATE OF CALIFORNIA.

BEING A SUBDIVISION OF LOT 1 OF TRACT No. 16271, AS SHOWN ON THE MAP THEREOF FILED  
IN BOOK 839 AT PAGES 34 THROUGH 45, INCLUSIVE, OF MISCELLANEOUS MAPS,  
IN THE OFFICE OF THE COUNTY RECORDER OF ORANGE COUNTY, CALIFORNIA.FUSCOE ENGINEERING, INC.  
JERRY L. USELTON, L.S. 5347 MARCH 2003ACCEPTED AND FILED AT THE  
REQUEST OF

FIRST AMERICAN TITLE

DATE OCTOBER 31, 2003TIME 01:22PM FEE \$ 15.00INSTRUMENT # 200300340068BOOK 850 PAGE 28-32 nTOM DALY  
COUNTY CLERK-RECORDERBY: [Signature] DEPUTY

## OWNERSHIP CERTIFICATE:

WE THE UNDERSIGNED, BEING ALL PARTIES HAVING ANY RECORD TITLE INTEREST  
IN THE LAND COVERED BY THIS MAP, DO HEREBY CONSENT TO THE PREPARATION  
AND RECORDATION OF SAID MAP, AS SHOWN WITHIN THE DISTINCTIVE BORDER LINE.  
WE ALSO HEREBY DEDICATE TO THE PUBLIC FOR STREET PURPOSES: SNOW BUSH STREET;  
SEA GRAPE ROAD; CALLIANDRA STREET.

WE ALSO HEREBY DEDICATE TO THE COUNTY OF ORANGE:


1. THE EASEMENTS FOR STORM DRAIN PURPOSES AS SHOWN ON SAID MAP.

WE ALSO HEREBY DEDICATE TO THE SANTA MARGARITA WATER DISTRICT PIPELINE EASEMENTS  
FOR SEWER, WATER AND ACCESS PURPOSES AS SHOWN ON SAID MAP, WHICH EASEMENTS SHALL  
BE SUBJECT TO THE SAME TERMS AND CONDITIONS AS ARE SHOWN IN THAT CERTAIN EASEMENT  
RECORDED OCTOBER 6, 1980 IN BOOK 13776, PAGE 341 OF OFFICIAL RECORDS, COUNTY OF  
ORANGE. THE SANTA MARGARITA WATER DISTRICT SHALL RESTORE OTHER IMPROVEMENTS OR  
FACILITIES LOCATED WITHIN THE EASEMENT, IF IT HAS CONSENTED TO THE LOCATION OF  
SUCH IMPROVEMENTS OR FACILITIES TO THE EXTENT THAT THE EXERCISE OF ITS RIGHTS IN  
THE CONNECTION WITH THE EASEMENT IMPACTS OTHER IMPROVEMENTS OR FACILITIES LOCATED  
WITHIN THE EASEMENT; HOWEVER, IN NO EVENT SHALL SANTA MARGARITA WATER DISTRICT BE  
RESPONSIBLE FOR THE COST OF RELOCATING ITS FACILITIES IN THE EVENT OF CONFLICTS WITH  
SUCH OTHER IMPROVEMENTS OR FACILITIES.


PARDEE HOMES, A CALIFORNIA CORPORATION, OWNER

BY: [Signature]  
THEODORE J. CULLEN  
SR. VICE PRESIDENTBY: [Signature]  
NANCY TROJAN  
ASSISTANT SECRETARYDMB LADERA, LLC, A DELAWARE LIMITED LIABILITY COMPANY,  
BENEFICIARY UNDER A DEED OF TRUST RECORDED APRIL 4, 2003 AS INSTRUMENT  
No. 2003000377227, OF OFFICIAL RECORDS OF ORANGE COUNTY, CALIFORNIABY: RANCHO MISSION VIEJO, L.L.C., A DELAWARE LIMITED LIABILITY COMPANY,  
ITS AUTHORIZED AGENT AND MANAGER.BY: [Signature]  
PRINT NAME DONALD T. STABLIN  
PRINT TITLE VICE PRESIDENTBY: [Signature]  
PRINT NAME PAUL JOHANSON  
PRINT TITLE SENIOR VICE PRESIDENTSTATE OF CALIFORNIA } SS  
COUNTY OF ORANGEON THIS 20th DAY OF JUNE, 2003, BEFORE ME, GRADY L. BOYPERSONALLY APPEARED THEODORE J. CULLEN AND NANCY TROJAN  
PERSONALLY KNOWN TO ME (OR PROVED TO ME ON THE BASIS OF SATISFACTORY EVIDENCE) TO BE THE  
PERSON(S) WHOSE NAME(S) IS/ARE SUBSCRIBED TO THE WITHIN INSTRUMENT AND ACKNOWLEDGED TO ME THAT  
HE/SHE/they EXECUTED THE SAME IN HIS/HER/their AUTHORIZED CAPACITY(IES), AND THAT BY  
HIS/HER/their SIGNATURE(S) ON THE INSTRUMENT THE PERSON(S), OR THE ENTITY UPON BEHALF OF WHICH  
THE PERSON(S) ACTED, EXECUTED THE INSTRUMENT.MY PRINCIPAL PLACE OF BUSINESS  
IS IN 603 ANGELES COUNTY.WITNESS MY HAND:  
[Signature]  
(SIGNATURE)  
NOTARY PUBLIC IN AND FOR SAID STATE  
GRADY L. BOY  
(PRINT NAME)MY COMMISSION EXPIRES: 12/3/04STATE OF CALIFORNIA } SS  
COUNTY OF ORANGEON THIS 20th DAY OF JUNE, 2003, BEFORE ME, Diana L. Binks, Notary PublicPERSONALLY APPEARED Donald T. Stablin and Paul Johanson  
PERSONALLY KNOWN TO ME (OR PROVED TO ME ON THE BASIS OF SATISFACTORY EVIDENCE) TO BE THE  
PERSON(S) WHOSE NAME(S) IS/ARE SUBSCRIBED TO THE WITHIN INSTRUMENT AND ACKNOWLEDGED TO ME THAT  
HE/SHE/they EXECUTED THE SAME IN HIS/HER/their AUTHORIZED CAPACITY(IES), AND THAT BY  
HIS/HER/their SIGNATURE(S) ON THE INSTRUMENT THE PERSON(S), OR THE ENTITY UPON BEHALF OF WHICH  
THE PERSON(S) ACTED, EXECUTED THE INSTRUMENT.MY PRINCIPAL PLACE OF BUSINESS  
IS IN Orange COUNTY.WITNESS MY HAND:  
Diana L. Binks  
(SIGNATURE)  
NOTARY PUBLIC IN AND FOR SAID STATE  
Diana L. Binks  
(PRINT NAME)MY COMMISSION EXPIRES: 12/12/06SANTA MARGARITA WATER DISTRICT  
CERTIFICATE OF ACCEPTANCE:THE UNDERSIGNED BEING THE DULY APPOINTED AGENT OF THE SANTA MARGARITA WATER  
DISTRICT, A PUBLIC CORPORATION IN ORANGE COUNTY, CALIFORNIA, PURSUANT TO ITS  
RESOLUTION NO. 88-10-2, DOES HEREBY ACCEPT ON BEHALF OF SAID DISTRICT THE  
PIPELINE EASEMENTS FOR SEWER, WATER AND ACCESS PURPOSES, AS DEDICATED AND AS  
SHOWN ON THIS TRACT MAP, BY AND BETWEEN THE SANTA MARGARITA WATER DISTRICT AND  
PARDEE HOMES, INC., AND DOES HEREBY CERTIFY THAT THE GRANTEE CONSENTS TO THE  
RECORDATION OF SAID TRACT MAP.[Signature]  
DANIEL R. FERONS, CHIEF ENGINEER  
SANTA MARGARITA WATER DISTRICTSTATE OF CALIFORNIA } SS  
COUNTY OF ORANGEON THIS 17th DAY OF July, 2003, BEFORE ME, Andrea M. Evans, Notary PublicPERSONALLY APPEARED DANIEL R. FERONS  
PERSONALLY KNOWN TO ME (OR PROVED TO ME ON THE BASIS OF SATISFACTORY EVIDENCE) TO BE THE  
PERSON(S) WHOSE NAME(S) IS/ARE SUBSCRIBED TO THE WITHIN INSTRUMENT AND ACKNOWLEDGED TO ME THAT  
HE/SHE/they EXECUTED THE SAME IN HIS/HER/their AUTHORIZED CAPACITY(IES), AND THAT BY  
HIS/HER/their SIGNATURE(S) ON THE INSTRUMENT THE PERSON(S), OR THE ENTITY UPON BEHALF OF WHICH  
THE PERSON(S) ACTED, EXECUTED THE INSTRUMENT.MY PRINCIPAL PLACE OF BUSINESS  
IS IN Orange COUNTY.WITNESS MY HAND:  
[Signature]  
(SIGNATURE)  
NOTARY PUBLIC IN AND FOR SAID STATE  
ANDREA M. EVANS  
(PRINT NAME)MY COMMISSION EXPIRES: April 8, 2004

## SURVEYOR'S STATEMENT:

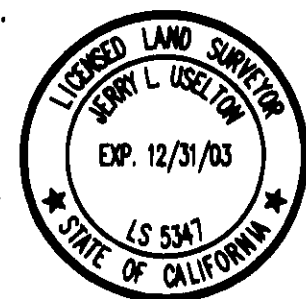THIS MAP WAS PREPARED BY ME OR UNDER MY DIRECTION AND IS BASED ON A  
FIELD SURVEY IN CONFORMANCE WITH THE REQUIREMENTS OF THE SUBDIVISION  
MAP ACT AND LOCAL ORDINANCE AT THE REQUEST OF PARDEE HOMES, INC., ON  
MARCH 2003. I HEREBY STATE THAT ALL MONUMENTS ARE OF THE CHARACTER AND  
OCCUPY THE POSITIONS INDICATED, OR THAT THEY WILL BE SET IN SUCH  
POSITIONS; AND THAT SAID MONUMENTS ARE SUFFICIENT TO ENABLE THE SURVEY  
TO BE RETRACED. I HEREBY STATE THAT THIS FINAL MAP SUBSTANTIALLY CONFORMS  
TO THE CONDITIONALLY APPROVED TENTATIVE MAP.[Signature]  
JERRY L. USELTON, L.S. 5347  
LICENSE EXPIRES 12/31/03

## COUNTY SURVEYOR'S STATEMENT:

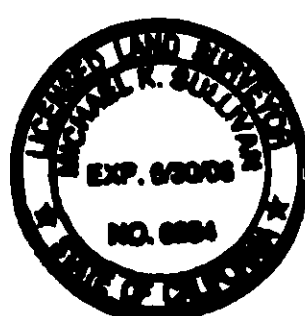I HEREBY STATE THAT I HAVE EXAMINED THIS MAP AND FOUND IT TO BE  
SUBSTANTIALLY IN CONFORMANCE WITH THE TENTATIVE MAP, AS FILED WITH,  
AMENDED AND APPROVED BY THE ORANGE COUNTY SUBDIVISION COMMITTEE;  
THAT ALL PROVISIONS OF THE SUBDIVISION MAP ACT AND COUNTY SUBDIVISION  
REGULATIONS HAVE BEEN COMPLIED WITH AND I AM SATISFIED SAID MAP IS  
TECHNICALLY CORRECT.DATED THIS 8th DAY OF OCTOBER, 2003[Signature]  
JOHN CANAS, COUNTY SURVEYOR  
L.S. 4408, EXPIRATION DATE: 9/30/05BY: MICHAEL K. SULLIVAN, DEPUTY  
L.S. 6884 EXPIRES 6/30/06

## COUNTY TREASURER-TAX COLLECTOR'S CERTIFICATE:

STATE OF CALIFORNIA } SS  
COUNTY OF ORANGEI HEREBY CERTIFY THAT ACCORDING TO THE RECORDS OF MY OFFICE THERE ARE  
NO LIENS AGAINST THE LAND COVERED BY THIS MAP OR ANY PART THEREOF FOR  
UNPAID STATE, COUNTY, MUNICIPAL OR LOCAL TAXES OR SPECIAL ASSESSMENTS  
COLLECTED AS TAXES, EXCEPT TAXES OR SPECIAL ASSESSMENTS COLLECTED AS  
TAXES NOT YET PAYABLE.  
AND DO ALSO CERTIFY TO THE RECORDER OF ORANGE COUNTY THAT THE  
PROVISIONS OF THE SUBDIVISION MAP ACT HAVE BEEN COMPLIED WITH  
REGARDING DEPOSITS TO SECURE THE PAYMENT OF TAXES OR SPECIAL  
ASSESSMENTS COLLECTED AS TAXES ON THE LAND COVERED BY THIS MAP.DATED THIS 50 DAY OF July, 2003JOHN M. W. MOORLACH  
COUNTY TREASURER-TAX COLLECTORBY: [Signature]  
DEPUTY TREASURER-TAX COLLECTOR

## CLERK OF THE BOARD OF SUPERVISOR'S CERTIFICATE:

STATE OF CALIFORNIA } SS  
COUNTY OF ORANGEI HEREBY CERTIFY THAT THIS MAP WAS PRESENTED FOR APPROVAL TO THE  
BOARD OF SUPERVISORS OF ORANGE COUNTY AT A REGULAR MEETING  
THEREOF HELD ON THE 20th DAY OF October, 2003,  
AND THAT THEREUPON SAID BOARD DID, BY AN ORDER DULY PASSED AND ENTERED,  
APPROVE SAID MAP AND DID ACCEPT ON BEHALF OF THE PUBLIC, SUBJECT TO  
IMPROVEMENTS: THE DEDICATION FOR STREET PURPOSES OF: SNOW BUSH STREET;  
SEA GRAPE ROAD; AND CALLIANDRA STREET.AND DID ALSO ACCEPT ON BEHALF OF THE COUNTY OF ORANGE;  
1. THE EASEMENTS FOR STORM DRAIN PURPOSES AS DEDICATED.DATED THIS 28th DAY OF OCTOBER, 2003.[Signature]  
DARLENE J. BLOOM  
CLERK OF THE BOARD OF SUPERVISORS  
OF ORANGE COUNTY, CALIFORNIA

## SIGNATURE OMISSION NOTES:

IN ACCORDANCE WITH THE PROVISIONS OF SECTION 66436(a)(3)(A)(C) OF THE  
SUBDIVISION MAP ACT, THE FOLLOWING SIGNATURES HAVE BEEN OMITTED:

- 1.) LADERA DEVELOPMENT COMPANY, L.L.C. HOLDER OF OIL, GAS, MINERAL, AND  
WATER RIGHTS RECORDED DECEMBER 10, 1996, AS INSTRUMENT NO.  
19960624029 OF OFFICIAL RECORDS.
- 2.) LADERA RANCH MAINTENANCE CORPORATION, HOLDER OF EASEMENTS AS  
RESERVED IN THE DEED RECORDED APRIL 4, 2003 AS INSTRUMENT  
NO. 2003000377228 OF OFFICIAL RECORDS.
- 3.) SOUTHERN CALIFORNIA GAS COMPANY, HOLDER OF A NON-EXCLUSIVE EASEMENT FOR  
PIPELINES AND CONDUITS PER DOCUMENT RECORDED JULY 10, 2003 AS INST. NO.  
2003 000 00344 OF OFFICIAL RECORDS (SAID EASEMENT IS BLANKET IN NATURE)

SHEET 2 OF 5 SHEETS

9.186 ACRES  
41 NUMBERED LOTS AND  
LETTERED LOTS "A" AND "B"  
DATE OF SURVEY: MARCH 2003  
(ALL OF VESTING TENTATIVE  
TRACT No. 16351)

## TRACT NO. 16351

IN THE UNINCORPORATED TERRITORY OF THE COUNTY OF ORANGE, STATE OF CALIFORNIA.

FUSCOE ENGINEERING, INC.

JERRY L. USELTON, L.S. 5347 MARCH 2003

**BASIS OF BEARINGS:**

THE BEARINGS SHOWN HEREON ARE BASED ON THE BEARING BETWEEN O.C.S. HORIZONTAL CONTROL STATION GPS No. 1417 AND STATION GPS No. 1448 BEING NORTH 10°48'13" EAST PER RECORDS ON FILE IN THE OFFICE OF THE ORANGE COUNTY SURVEYOR.

**DATUM STATEMENT:**

COORDINATES SHOWN ARE BASED ON THE CALIFORNIA COORDINATE SYSTEM (CCS83), ZONE VI, 1983 NAD, (1981.35 EPOCH OSC GPS ADJUSTMENT). ALL DISTANCES SHOWN ARE GROUND, UNLESS OTHERWISE NOTED. TO OBTAIN GRID DISTANCES MULTIPLY GROUND DISTANCE BY 0.999948295 (NOTE: THIS COMBINATION FACTOR IS NOT AN AVERAGE OF THE COMBINATION FACTORS OF THE TWO CONTROL POINTS, BUT IS SPECIFIC TO THIS PROJECT)

**MONUMENT NOTES:**

- INDICATES FOUND OCS GPS MONUMENT AS NOTED:

N=2146780.819  
E=6142602.585

FOUND 2" IRON PIPE WITH 1-3/4" OCS BRASS CAP STAMPED "GPS 1448 9-95" PER TRACT No. 16203, M.M. 826/8-20 AND RECORDS ON FILE IN THE ORANGE COUNTY SURVEYORS OFFICE.

N=2141450.558  
E=6141583.535

FOUND 2" IRON PIPE WITH 2" OCS BRASS CAP STAMPED "GPS 1417 9-95" PER TRACT No. 16203, M.M. 826/8-20 AND RECORDS ON FILE IN THE ORANGE COUNTY SURVEYORS OFFICE.

- INDICATES 2" I.P. TAGGED "L.S. 5347" OR SPIKE AND WASHER STAMPED "L.S. 5347" OR LEAD AND TAG "L.S. 5347" TO BE SET PRIOR TO RECORDATION OF THIS TRACT

- INDICATES 2" I.P. TAGGED "L.S. 5557" OR SPIKE AND WASHER STAMPED "L.S. 5557" OR LEAD AND TAG "L.S. 5557" TO BE SET WITHIN 90 DAYS AFTER ACCEPTANCE OF IMPROVEMENTS PER TRACT 16271, M.M. 839/34-45

2" I.P. TAGGED "L.S. 5347", OR SPIKE AND WASHER "L.S. 5347", OR LEAD TACK AND TAG "L.S. 5347" TO BE SET AT ALL TRACT BOUNDARY CORNERS WITHIN 90 DAYS AFTER ACCEPTANCE OF IMPROVEMENTS, UNLESS NOTED OTHERWISE.

1" I.P. TAGGED "L.S. 5347", OR SPIKE AND WASHER "L.S. 5347", OR NAIL AND TAG "L.S. 5347" TO BE SET AT ALL LOT CORNERS WITHIN 90 DAYS AFTER ACCEPTANCE OF IMPROVEMENTS, EXCEPT B.C.s, E.C.s, P.R.C.s, AND P.C.C.s WHICH ABUT A STREET AND ARE NOT LOT CORNERS MARKING SIDE LOT LINES, ALSO EXCEPT AT FRONT LOT CORNERS SET LEAD TACK AND TAG "L.S. 5347" IN TOP OF CURB ALONG PROJECTED SIDE LOT LINE, UNLESS NOTED OTHERWISE.

1" I.P. TAGGED "L.S. 5347" OR SPIKE AND WASHER "L.S. 5347" TO BE SET AT ALL STREET CENTERLINE POINTS OF CONTROL WITHIN 90 DAYS AFTER ACCEPTANCE OF IMPROVEMENTS, UNLESS NOTED OTHERWISE.

**SURVEYOR'S NOTES:**

DATA SHOWN ALONG THIS TRACT BOUNDARY ARE MEASURED AND RECORD PER TRACT No. 16271, M.M. 839/34-45, UNLESS NOTED OTHERWISE.

ALL LETTERED LOTS SHOWN HEREON ARE NOT SEPARATE BUILDING SITES. LOTS "A" AND "B" ARE FOR SLOPE AND LANDSCAPE PURPOSES AND ARE TO BE CONVEYED TO THE APPROPRIATE HOMEOWNERS ASSOCIATION.

**AUTOMATIC FIRE SPRINKLER NOTE:**

ALL COMMERCIAL STRUCTURES OVER 6,000 SQUARE FEET; ALL MULTIFAMILY RESIDENTIAL STRUCTURES; ALL DETACHED, SINGLE-FAMILY STRUCTURES EXCEEDING 5,500 SQUARE FEET, AND, ALL STRUCTURES EXCEEDING FIRE AUTHORITY ACCESS REQUIREMENTS SHALL BE PROTECTED BY AN AUTOMATIC SPRINKLER SYSTEM, IN A MANNER MEETING THE APPROVAL OF THE FIRE CHIEF.

**SPECIAL FIRE PROTECTION NOTE:**

PROPERTY IS IN A SPECIAL FIRE PROTECTION AREA AND MUST MEET ALL REQUIREMENTS FOR DEVELOPMENT IN THE AREA


**HIGH FIRE HAZARD AREA NOTE:**

THE LOTS SHOWN ON THIS MAP ARE IN A HIGH FIRE HAZARD AREA DUE TO WILDLAND EXPOSURE.

**EASEMENT NOTES:**

(A) DENOTES THE EASEMENT FOR WATER, SEWER, AND ACCESS PURPOSES DEDICATED TO THE SANTA MARGARITA WATER DISTRICT HEREON.

(B) DENOTES THE EASEMENT FOR STORM DRAIN PURPOSES DEDICATED TO THE COUNTY OF ORANGE HEREON.


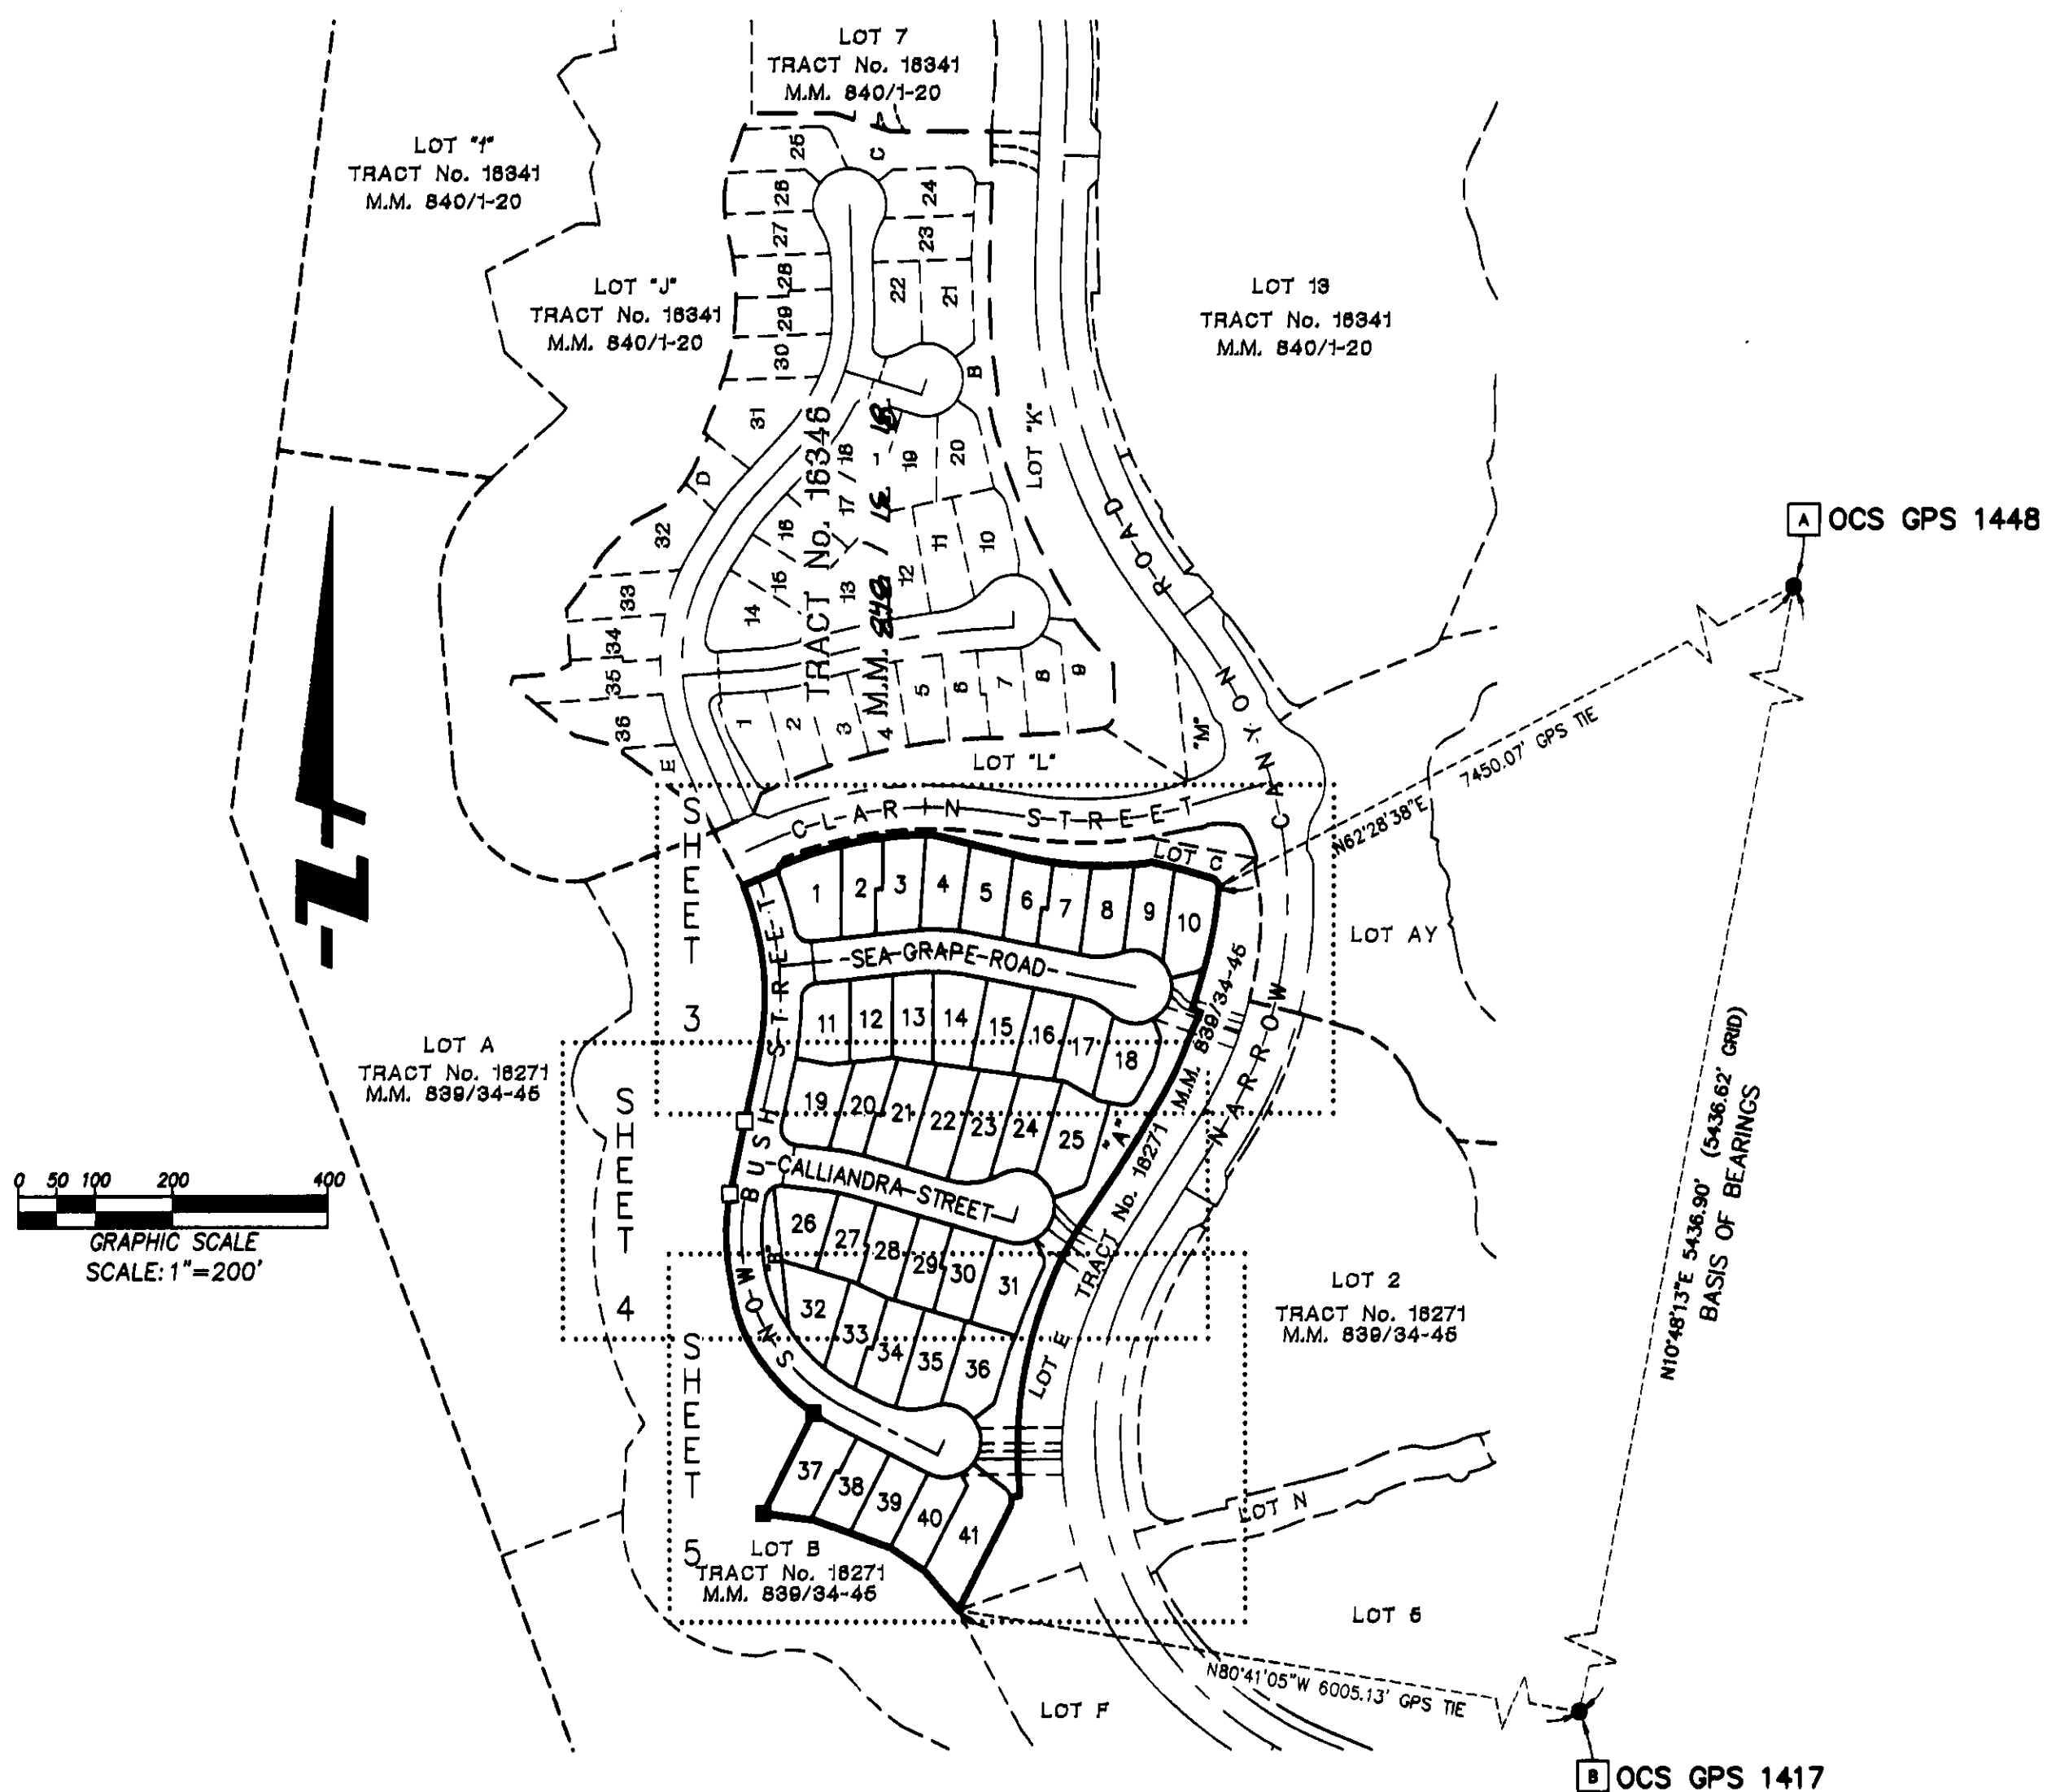
**INDEX/VICINITY MAP AND OCS GPS CONTROL SCHEME**



SHEET 3 OF 5 SHEETS  
9.108 ACRES  
41 NUMBERED LOTS AND  
LETTERED LOTS "A" AND "B"  
DATE OF SURVEY: MARCH 2003  
(ALL OF VESTING TENTATIVE  
TRACT No. 16351)

# TRACT NO. 16351

IN THE UNINCORPORATED TERRITORY OF THE COUNTY OF ORANGE, STATE OF CALIFORNIA.  
FUSCOE ENGINEERING, INC.  
JERRY L. USELTON, L.S. 5347 MARCH 2003

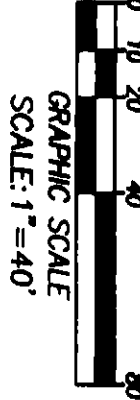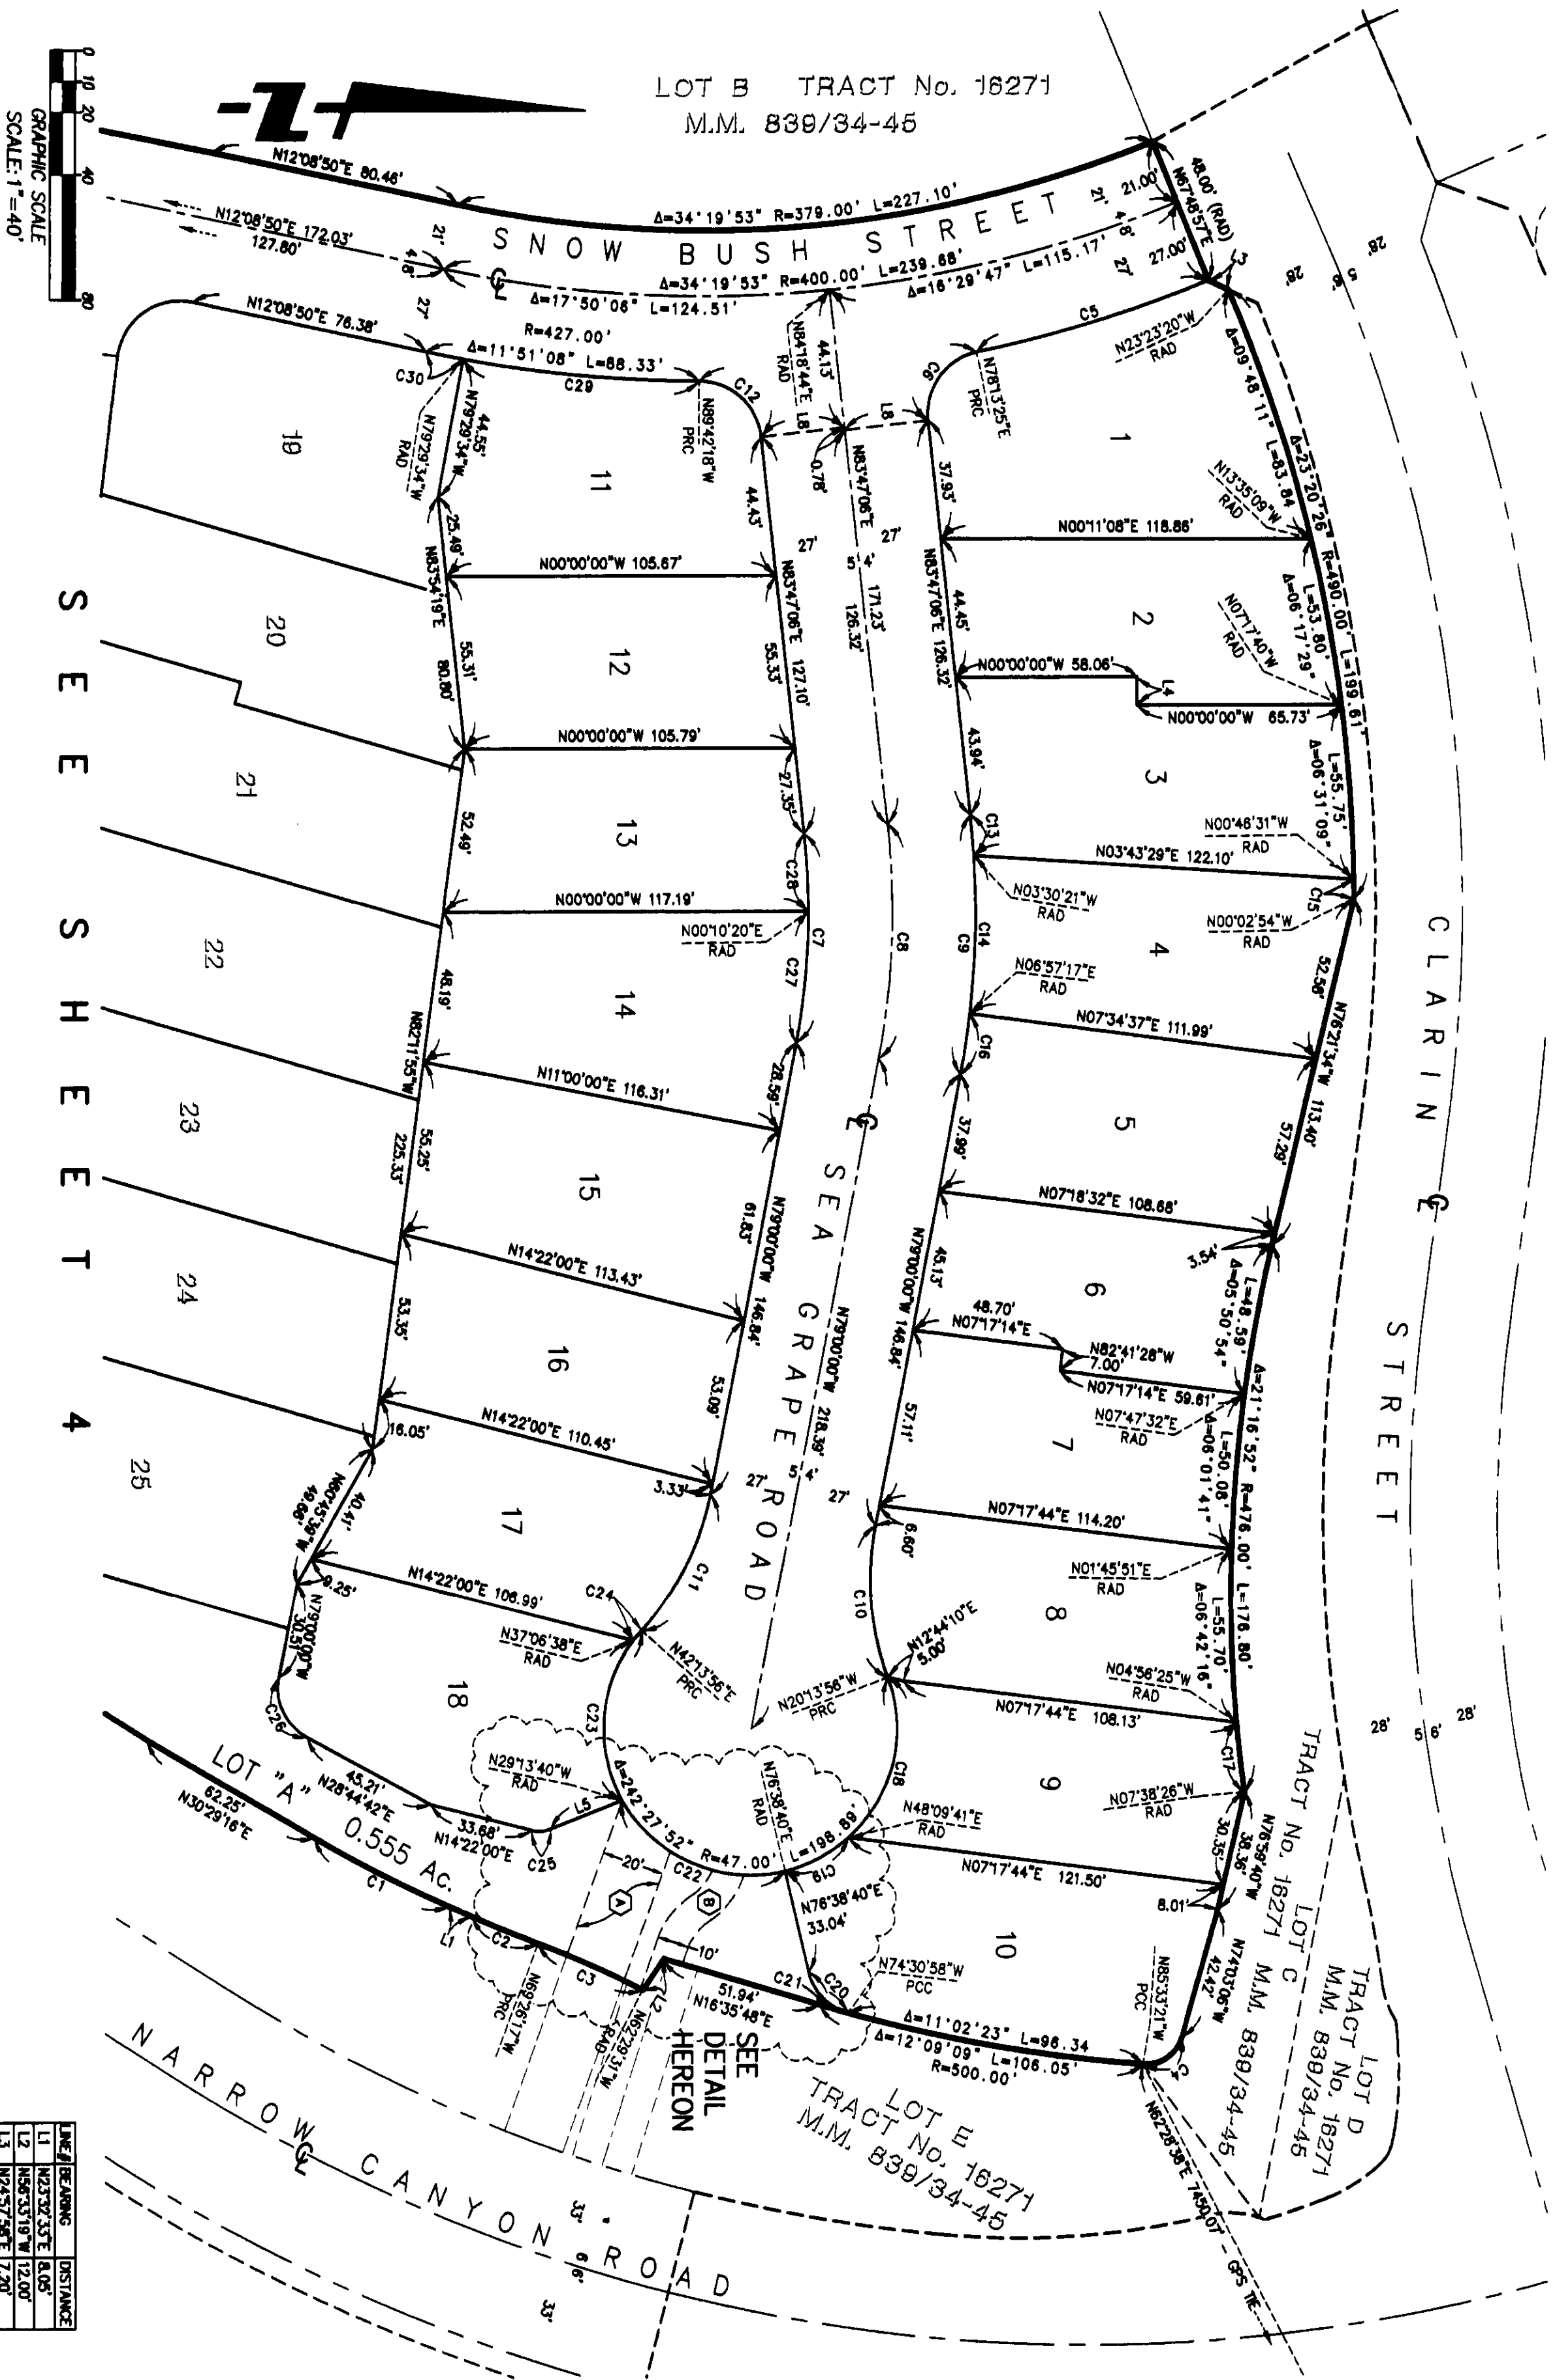


NOTE:  
SEE SHEET 2 FOR BASIS OF BEARINGS, DATUM STATEMENT, MONUMENT NOTES, EASEMENT NOTES,  
SURVEYOR'S NOTES, NOTES, AND VICINITY MAP AND OCS GPS CONTROL SCHEME.


MapInfo 2003/03/27/17:05:00 JLMC June 4, 2003

| LINE# | BEARING     | DISTANCE |
|-------|-------------|----------|
| 11    | N23°32'33"E | 8.05'    |
| 12    | N86°33'18"W | 12.00'   |
| 13    | N24°57'58"E | 7.20'    |
| 14    | N80°00'00"E | 9.08'    |
| 15    | N21°33'27"W | 24.75'   |
| 16    | N71°17'11"W | 4.81'    |
| 17    | N71°17'11"W | 16.53'   |
| 18    | N06°12'54"W | 27.00'   |


| CURVE# | DELTA     | RADIUS  | LENGTH |
|--------|-----------|---------|--------|
| C1     | 06°56'43" | 400.00' | 48.49' |
| C2     | 02°56'50" | 445.00' | 23.15' |
| C3     | 06°56'46" | 304.00' | 36.86' |
| C4     | 78°29'45" | 12.00'  | 18.44' |
| C5     | 10°24'26" | 427.00' | 77.56' |
| C6     | 84°28'19" | 20.00'  | 28.47' |
| C7     | 17°12'54" | 223.00' | 67.00' |
| C8     | 17°12'54" | 223.00' | 75.11' |
| C9     | 17°12'54" | 277.00' | 83.23' |
| C10    | 31°13'56" | 91.00'  | 49.60' |
| C11    | 31°13'56" | 91.00'  | 49.60' |
| C12    | 83°29'24" | 20.00'  | 28.14' |
| C13    | 02°42'35" | 277.00' | 13.10' |
| C14    | 10°27'36" | 277.00' | 50.57' |
| C15    | 00°43'37" | 490.00' | 6.22'  |
| C16    | 04°02'43" | 277.00' | 19.56' |
| C17    | 02°42'01" | 478.00' | 22.43' |
| C18    | 88°23'57" | 47.00'  | 23.36' |
| C19    | 28°28'59" | 47.00'  | 23.36' |
| C20    | 61°09'36" | 18.00'  | 19.21' |
| C21    | 01°08'46" | 500.00' | 9.71'  |
| C22    | 74°07'40" | 47.00'  | 54.42' |
| C23    | 66°20'16" | 47.00'  | 60.61' |
| C24    | 05°07'16" | 47.00'  | 4.20'  |
| C25    | 35°35'27" | 10.00'  | 6.27'  |
| C26    | 72°15'16" | 18.00'  | 22.70' |
| C27    | 10°49'40" | 223.00' | 42.14' |
| C28    | 06°23'14" | 223.00' | 24.86' |
| C29    | 10°12'44" | 427.00' | 78.11' |
| C30    | 01°39'24" | 427.00' | 12.22' |
| C31    | 01°53'22" | 304.00' | 10.02' |
| C32    | 03°46'53" | 304.00' | 20.06' |
| C33    | 01°07'26" | 304.00' | 3.98'  |
| C34    | 00°08'05" | 304.00' | 0.80'  |
| C35    | 27°38'44" | 47.00'  | 22.66' |
| C36    | 17°48'30" | 47.00'  | 14.61' |
| C37    | 17°24'46" | 47.00'  | 10.18' |
| C38    | 16°15'37" | 47.00'  | 13.34' |
| C39    | 34°37'07" | 17.50'  | 10.67' |
| C40    | 39°21'25" | 17.50'  | 18.88' |
| C41    | 37°59'49" | 17.50'  | 11.59' |
| C42    | 37°59'49" | 17.50'  | 18.21' |

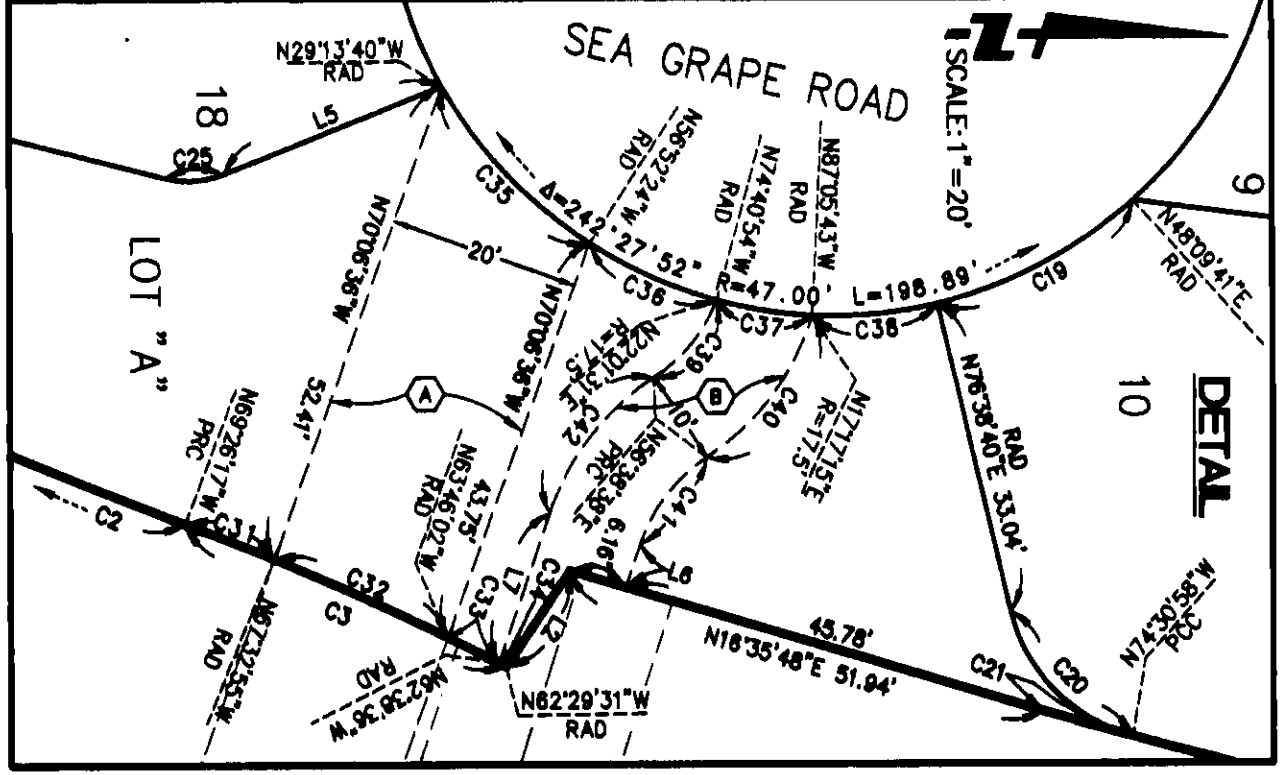

**TRACT NO. 16351**  
IN THE UNINCORPORATED TERRITORY OF THE COUNTY OF ORANGE, STATE OF CALIFORNIA.  
FUSCOE ENGINEERING, INC.  
JERRY L. USELTON, L.S. 5347 MARCH 2003

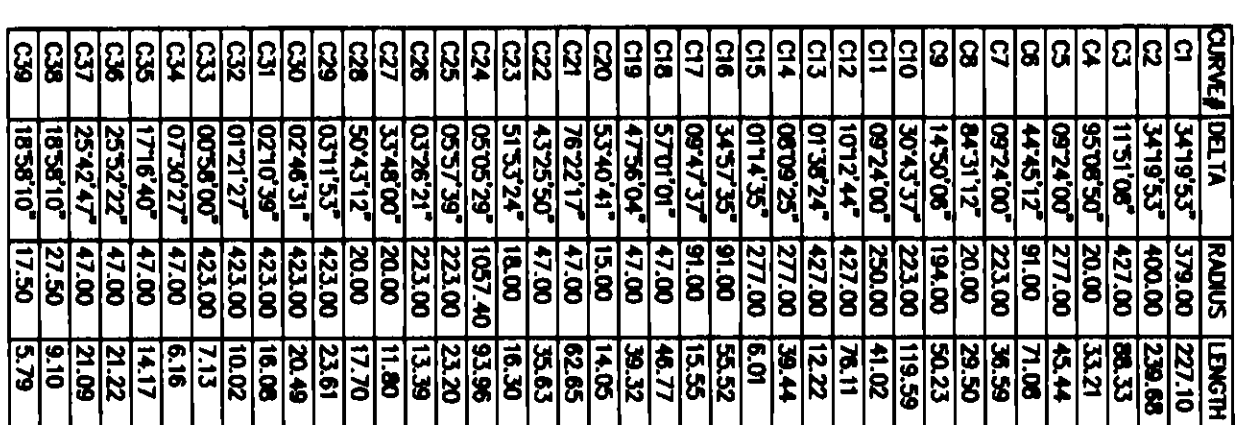

| LINE# | BEARING     | DISTANCE |
|-------|-------------|----------|
| L1    | N32°16'23"W | 7.68'    |
| L2    | N16°23'60"E | 20.00'   |
| L3    | N18°02'20"E | 5.00'    |
| L4    | N7°00'41"E  | 37.34'   |
| L5    | N27°01'50"W | 23.98'   |
| L6    | N04°36'26"W | 5.00'    |
| L7    | N42°20'53"W | 24.49'   |
| L8    | N61°19'03"W | 4.71'    |
| L9    | N61°19'03"W | 5.38'    |
| L10   | N07°00'00"E | 27.00'   |

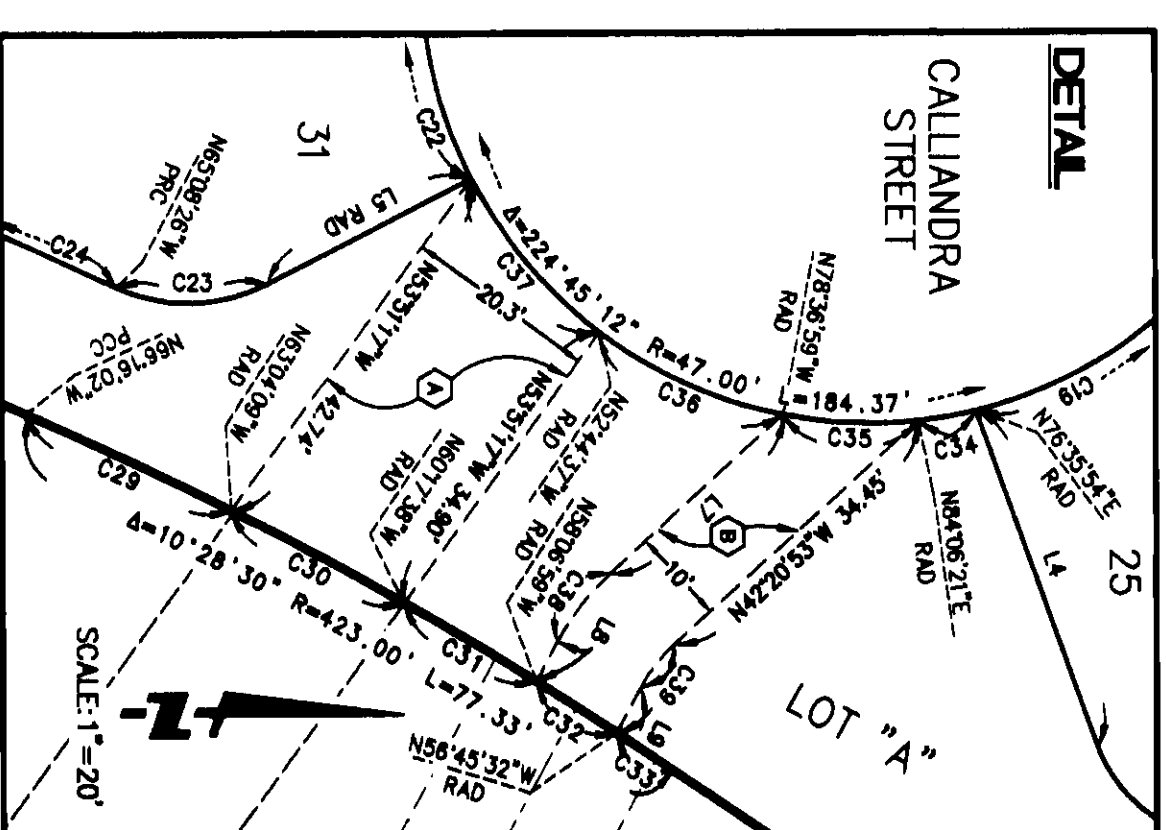

\\FPM6\512\02\1616351.DMS June 4, 2003




SHEET 5 OF 5 SHEETS  
9.188 ACRES  
41 NUMBERED LOTS AND  
LETTERED LOTS "A" AND "B"  
DATE OF SURVEY: MARCH 2003  
(ALL OF WESTING TENTATIVE  
TRACT No. 16351)

# TRACT NO. 16351


IN THE UNINCORPORATED TERRITORY OF THE COUNTY OF ORANGE, STATE OF CALIFORNIA.  
FUSCOE ENGINEERING, INC.  
JERRY L. USELTON, L.S. 5347 MARCH 2003

S E E S H E E T 4

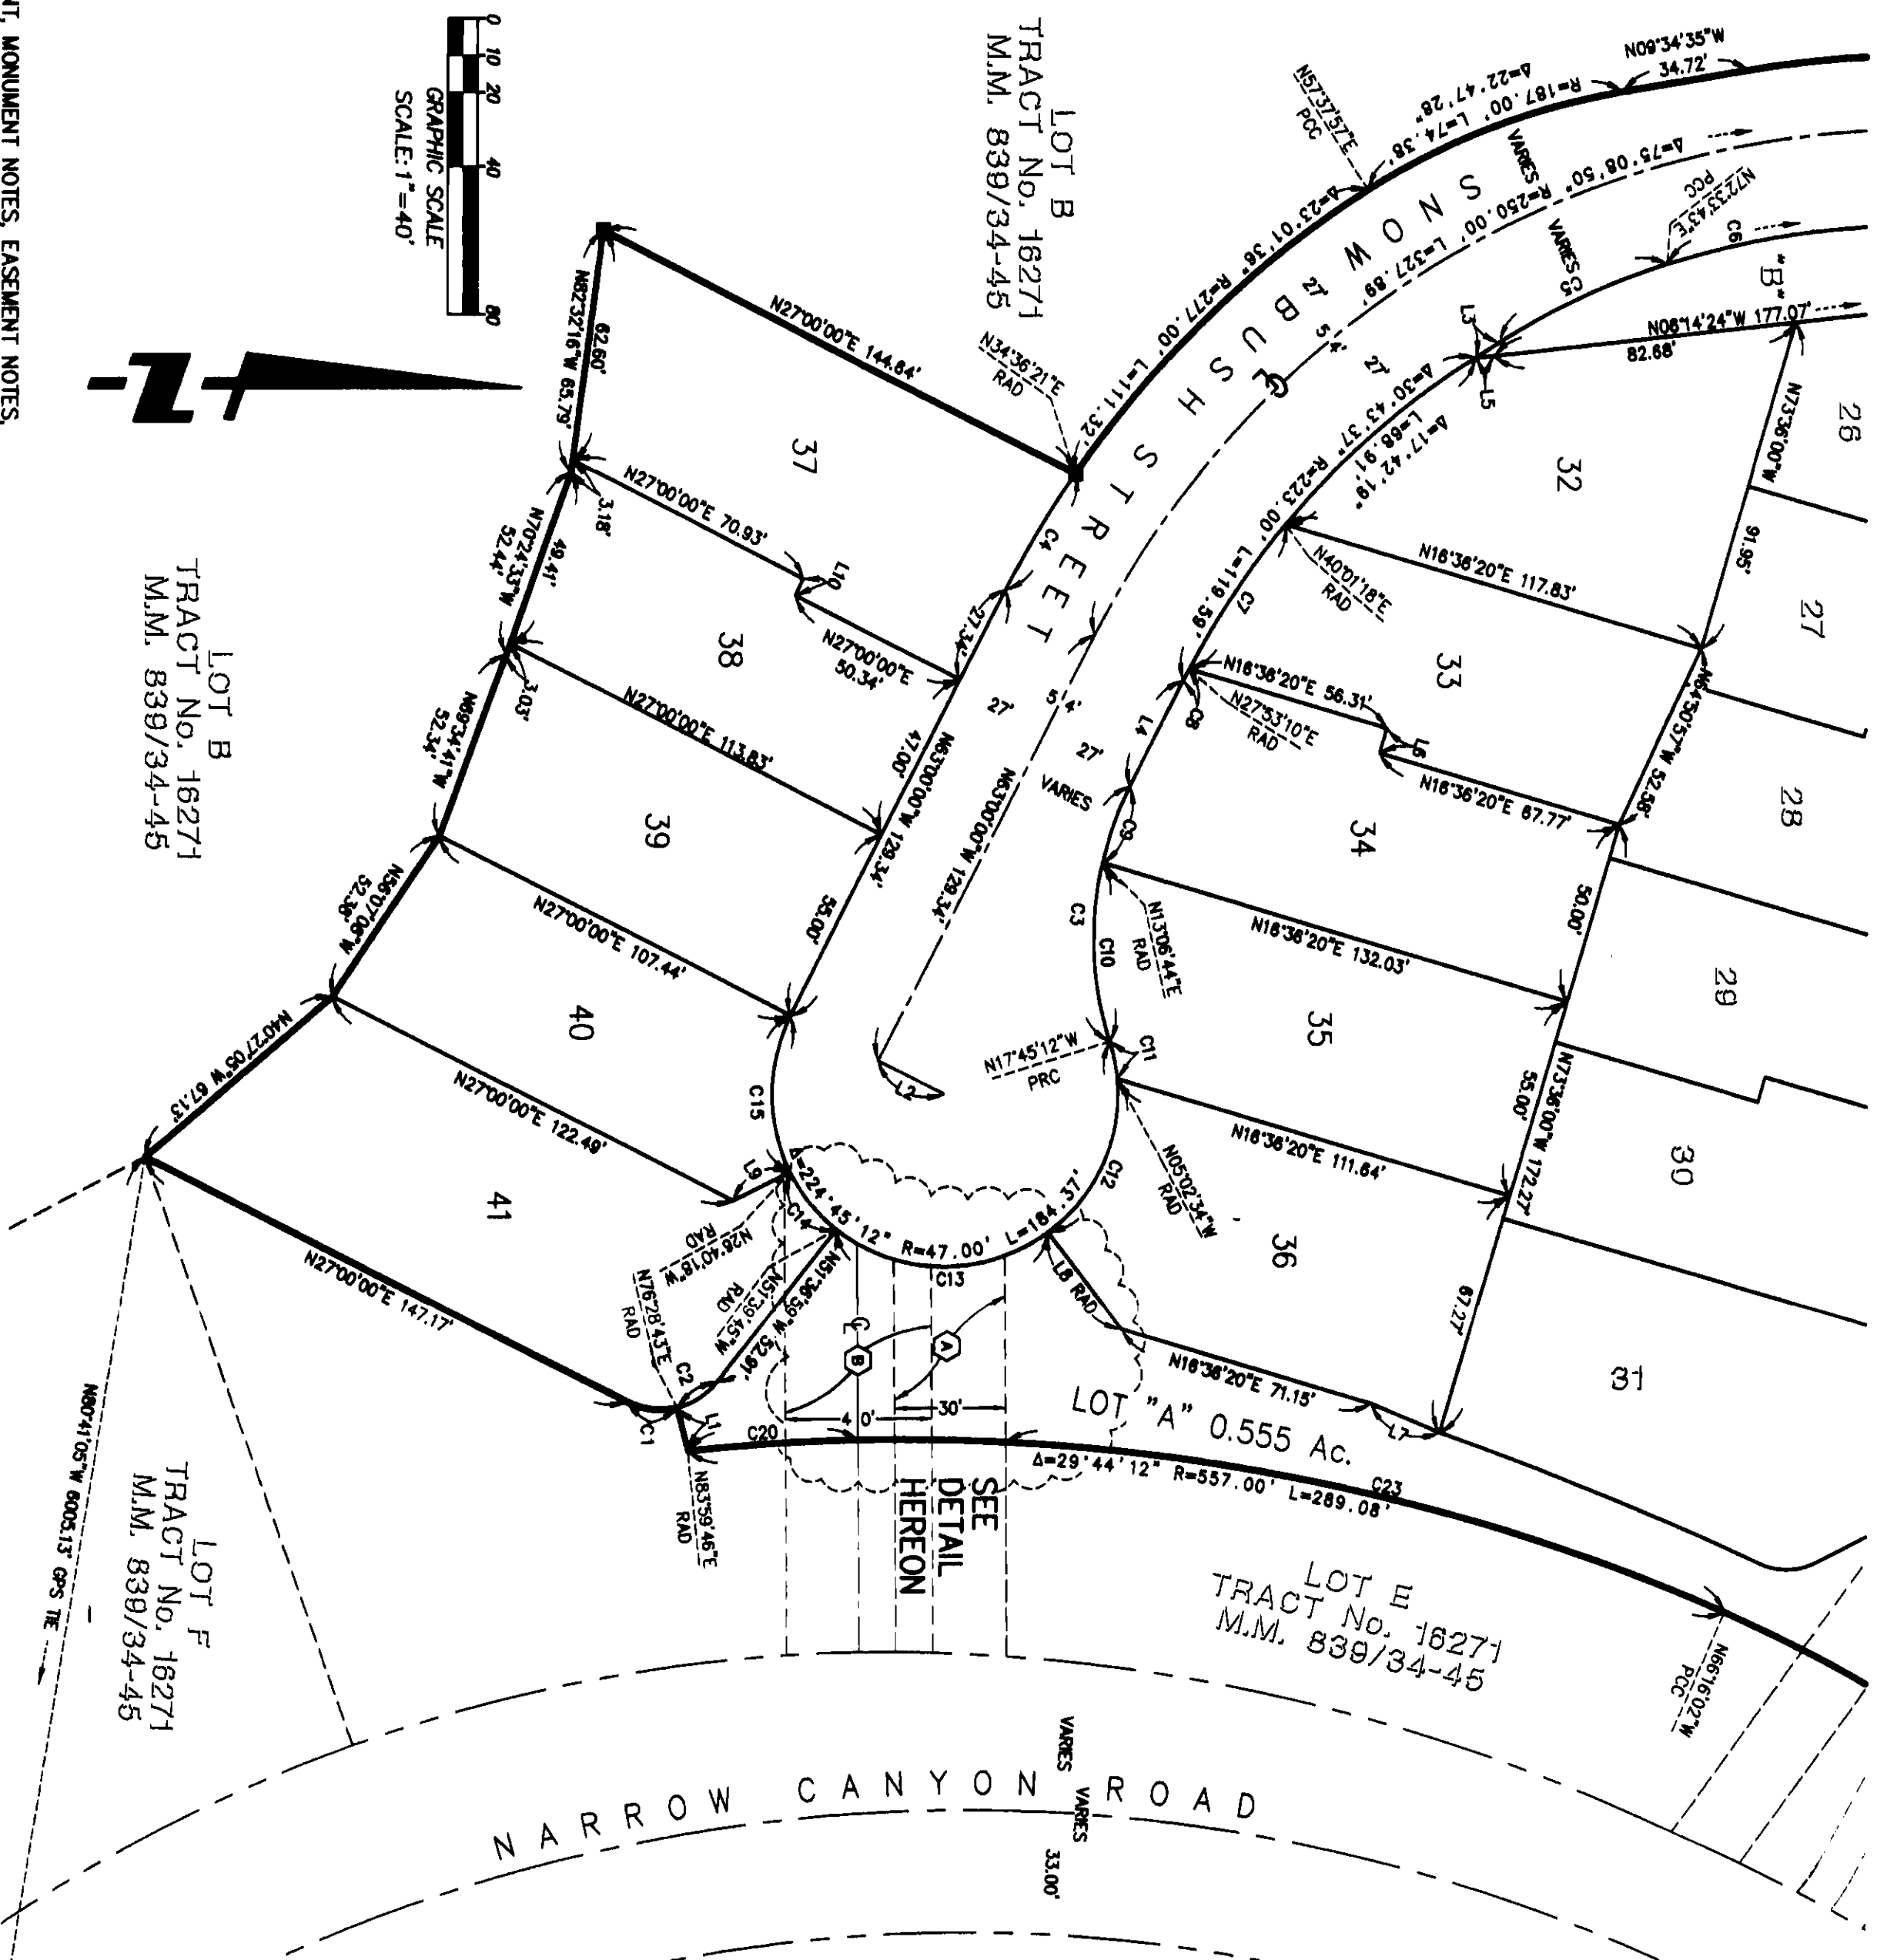

| CURVED | DELTA     | BEARINGS | LENGTH |
|--------|-----------|----------|--------|
| C1     | 40°31'7"  | 20.00    | 14.14  |
| C2     | 36°05'42" | 20.00    | 13.30  |
| C3     | 44°45'12" | 91.00    | 71.08  |
| C4     | 07°36'21" | 277.00   | 36.77  |
| C5     | 14°30'08" | 194.00   | 50.23  |
| C6     | 28°35'04" | 224.00   | 116.97 |
| C7     | 17°08'08" | 223.00   | 47.23  |
| C8     | 00°53'10" | 223.00   | 3.45   |
| C9     | 13°53'16" | 91.00    | 22.06  |
| C10    | 30°51'55" | 91.00    | 49.02  |
| C11    | 12°42'38" | 47.00    | 10.43  |
| C12    | 56°10'08" | 47.00    | 47.72  |
| C13    | 75°12'40" | 47.00    | 61.70  |
| C14    | 28°59'27" | 47.00    | 20.50  |
| C15    | 55°40'18" | 47.00    | 44.03  |
| C16    | 16°16'32" | 47.00    | 13.35  |
| C17    | 37°14'19" | 47.00    | 30.55  |
| C18    | 13°26'24" | 47.00    | 10.94  |
| C19    | 08°21'35" | 47.00    | 6.86   |
| C20    | 04°50'31" | 557.00   | 47.13  |
| C21    | 01°01'44" | 557.00   | 10.00  |
| C22    | 03°05'16" | 557.00   | 30.02  |
| C23    | 20°46'21" | 557.00   | 201.34 |

| LINE | BEARING     | DISTANCE |
|------|-------------|----------|
| L1   | N76°26'43"E | 12.11'   |
| L2   | N27°00'00"E | 20.00'   |
| L3   | N82°16'23"W | 7.68'    |
| L4   | N04°36'28"W | 5.00'    |
| L5   | N73°23'40"W | 7.00'    |
| L6   | N23°00'16"E | 20.21'   |
| L7   | N23°07'55"E | 33.05'   |
| L8   | N26°40'18"W | 17.54'   |
| L9   | N26°40'18"W | 5.00'    |
| L10  | N63°00'00"W | 5.00'    |

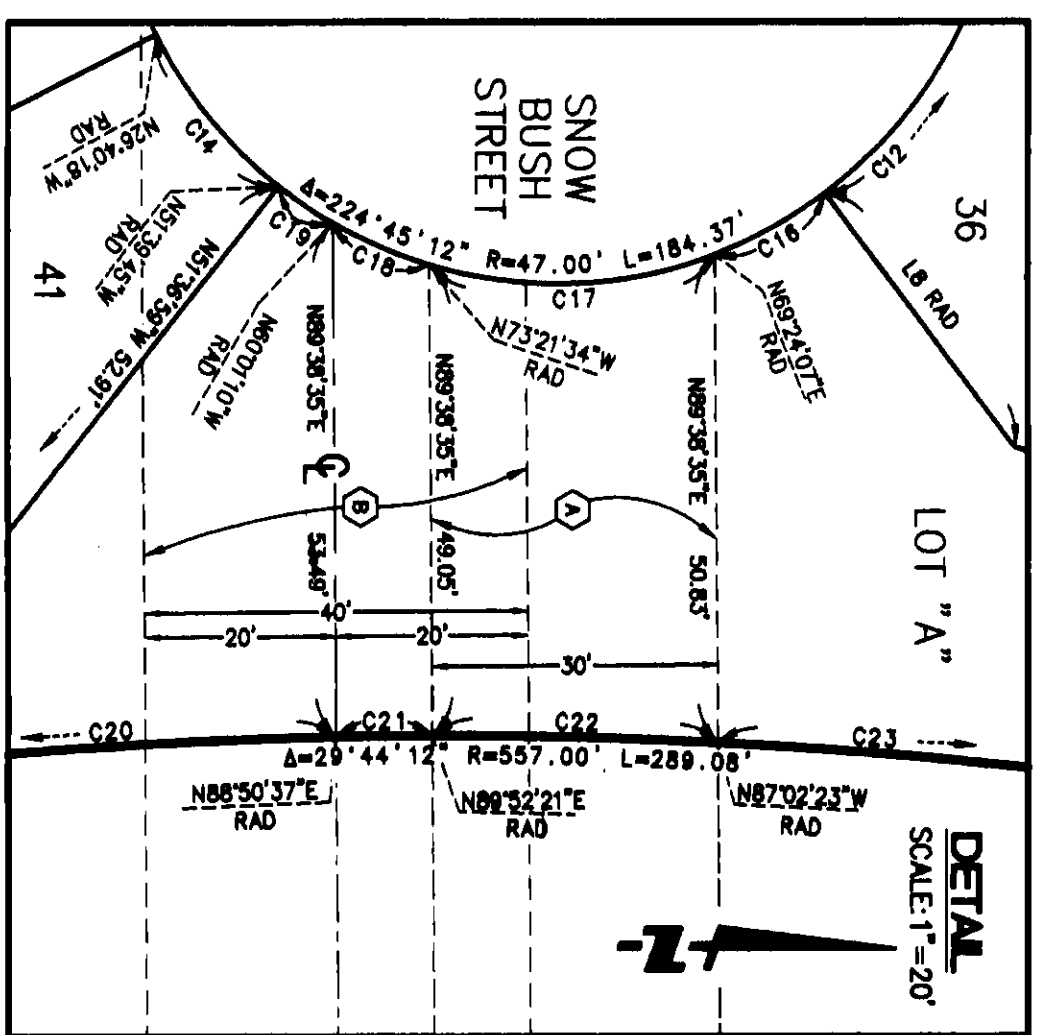

NOTE:  
SEE SHEET 2 FOR BASIS OF BEARINGS, DATUM STATEMENT, MONUMENT NOTES, EASEMENT NOTES,  
SURVEYOR'S NOTES, NOTES, AND VICINITY MAP AND OCS GPS CONTROL SCHEME.