

SHEET 1 OF 5 SHEETS

39 NUMBERED LOTS AND
LOTS A THROUGH N, INCLUSIVE
ACREAGE = 4.255 ACRES
A PORTION OF TENTATIVE
TRACT NO. 16271
DATE OF SURVEY: DEC. 2002

TRACT NO. 16352

IN THE UNINCORPORATED TERRITORY OF THE COUNTY OF ORANGE,
STATE OF CALIFORNIA

BEING A SUBDIVISION OF LOT 5, AS SHOWN ON TRACT MAP NO. 16271
FILED IN BOOK 839, PAGES 34 THROUGH 45, INCLUSIVE OF MISCELLANEOUS MAPS,
IN THE OFFICE OF THE COUNTY RECORDER OF SAID COUNTY, STATE OF CALIFORNIA

ADAMS - STREETER CIVIL ENGINEERS, INC. JAN A. ADAMS, R.C.E. 21687

ACCEPTED AND FILED AT THE
REQUEST OF

FIRST AMERICAN TITLE INSURANCE COMPANY

DATE OCTOBER 31, 2003TIME 09:44 AM FEE \$15.00INSTRUMENT # 2003001340100BOOK 850 PAGE 33-37 m/hTOM DALY
COUNTY CLERK RECORDERBY Rab
DEPUTY

OWNER'S CERTIFICATE:

WE, THE UNDERSIGNED, BEING ALL PARTIES HAVING ANY RECORD TITLE INTEREST IN THE LAND COVERED
BY THIS MAP, DO HEREBY CONSENT TO THE PREPARATION AND RECORDATION OF SAID MAP, AS SHOWN
WITHIN THE DISTINCTIVE BORDER LINE.

WE ALSO HEREBY DEDICATE TO THE COUNTY OF ORANGE:

AN EASEMENT FOR EMERGENCY AND PUBLIC SERVICE VEHICULAR INGRESS-EGRESS
DEDICATED TO THE COUNTY OF ORANGE.

WE ALSO DEDICATE TO THE SANTA MARGARITA WATER DISTRICT, THE EASEMENTS FOR SEWER, WATER
AND ACCESS PURPOSES AS SHOWN ON SAID MAP, WHICH EASEMENTS SHALL BE SUBJECT TO THE
SAME TERMS AND CONDITIONS AS ARE SHOWN IN THAT CERTAIN EASEMENT RECORDED OCTOBER 6, 1980,
IN BOOK 13776, PAGE 341, OF OFFICIAL RECORDS, COUNTY OF ORANGE.

RICHMOND AMERICAN HOMES OF CALIFORNIA, INC., A COLORADO CORPORATION

Alfredo F. Ayuyao
NAME: ALFREDO F. AYUYAO
TITLE: Division President

Jon H. Sasaki
NAME: JON H. SASAKI
TITLE: REGIONAL V.P. FINANCE

DMB LADERA, LLC., A DELAWARE LIMITED LIABILITY COMPANY AS BENEFICIARY UNDER A
DEED OF TRUST RECORDED JUNE 02, 2003, AS INSTRUMENT NO. 2003000639857, OFFICIAL
RECORDS.

BY: RANCHO MISSION VIEJO, LLC., A DELAWARE LIMITED LIABILITY COMPANY
AS ITS AUTHORIZING AGENT AND MANAGER.

Donald T. Stahlin
NAME: DONALD T. STAHLIN
TITLE: Vice President

Gregory S. Edwards
NAME: Gregory S. Edwards
TITLE: Chief Financial Officer

NOTARY ACKNOWLEDGMENTS

STATE OF CALIFORNIA }
COUNTY OF ORANGE } ss

ON THIS 3rd DAY OF SEPTEMBER, 2003, BEFORE ME, Lise M. Cowderoy, A NOTARY
PUBLIC IN AND FOR SAID STATE, PERSONALLY APPEARED ALFREDO F. AYUYAO & Jon H. Sasaki
PERSONALLY KNOWN TO ME (OR PROVED TO ME ON THE BASIS OF SATISFACTORY EVIDENCE) TO BE
THE PERSONS WHOSE NAMES ARE SUBSCRIBED TO THE WITHIN INSTRUMENT AND ACKNOWLEDGED TO ME
THAT THEY EXECUTED THE SAME IN THEIR AUTHORIZED CAPACITIES AND THAT BY THEIR SIGNATURES ON
THE INSTRUMENT THE PERSON OR THE ENTITY UPON BEHALF OF WHICH THE PERSONS ACTED, EXECUTED
THE INSTRUMENT.

WITNESS MY HAND:

Lise M. Cowderoy
NOTARY PUBLIC IN AND FOR SAID STATE
LISE M. COWDEROY
PRINT NAME

MY PRINCIPAL PLACE OF BUSINESS
IS IN ORANGE COUNTY

MY COMMISSION EXPIRES MAY 21, 2006

STATE OF CALIFORNIA }
COUNTY OF Orange } ss

ON THIS 9th DAY OF September, 2003, BEFORE ME, Diana L. Binks, A NOTARY
PUBLIC IN AND FOR SAID STATE, PERSONALLY APPEARED Donald T. Stahlin and Gregory S. Edwards
PERSONALLY KNOWN TO ME (OR PROVED TO ME ON THE BASIS OF SATISFACTORY EVIDENCE) TO BE
THE PERSONS WHOSE NAMES ARE SUBSCRIBED TO THE WITHIN INSTRUMENT AND ACKNOWLEDGED TO ME
THAT THEY EXECUTED THE SAME IN THEIR AUTHORIZED CAPACITIES AND THAT BY THEIR SIGNATURES ON
THE INSTRUMENT THE PERSON OR THE ENTITY UPON BEHALF OF WHICH THE PERSONS ACTED, EXECUTED
THE INSTRUMENT.

WITNESS MY HAND:

Diana L. Binks
NOTARY PUBLIC IN AND FOR SAID STATE
Diana L. Binks
PRINT NAME

MY PRINCIPAL PLACE OF BUSINESS
IS IN Orange COUNTY

MY COMMISSION EXPIRES December 12, 2006

PRIVATE STREETS NOTE

THE PRIVATE STREETS CONSTRUCTED WITHIN THIS MAP SHALL BE OWNED, OPERATED AND
MAINTAINED BY THE DEVELOPER, SUCCESSORS OR ASSIGNS. THE COUNTY OF ORANGE SHALL
HAVE NO RESPONSIBILITY THEREFORE UNLESS PURSUANT TO APPROPRIATE SECTIONS OF THE
STREETS AND HIGHWAYS CODE OF THE STATE OF CALIFORNIA, THE SAID PRIVATE STREETS
HAVE BEEN ACCEPTED INTO THE COUNTY ROAD SYSTEM BY APPROPRIATE RESOLUTION OF
THE ORANGE COUNTY BOARD OF SUPERVISORS.

SIGNATURE OMISSIONS

PURSUANT TO THE PROVISIONS OF SECTION 66436 (a)(3)(A)(C) OF THE SUBDIVISION MAP ACT,
THE FOLLOWING SIGNATURES HAVE BEEN OMITTED:

LADERA DEVELOPMENT COMPANY, LLC, HOLDER OF OIL, GAS AND MINERAL RIGHTS RECORDED AS
INSTRUMENT NO. 19960624029 OF OFFICIAL RECORDS.

DMB LADERA, L.L.C., A DELAWARE LIMITED LIABILITY COMPANY, HOLDER OF EASEMENTS AS RESERVED
IN THE DEED RECORDED AS INSTRUMENT NO. 2003000955381 OF OFFICIAL RECORDS.


SPECIAL FIRE PROTECTION NOTE:

PROPERTY IS CONDITIONALLY EXCLUDED FROM A SPECIAL FIRE PROTECTION AREA.
ALL REQUIREMENTS FOR DEVELOPMENT AND CONSTRUCTION WITHIN A "SPECIAL FIRE PROTECTION AREA"
INCLUDING INCREASED STREET WIDTHS AND CLASS A ROOF ASSEMBLIES WILL BE MET.

ENGINEER'S STATEMENT

THIS MAP WAS PREPARED BY ME OR UNDER MY DIRECTION AND IS BASED UPON A FIELD SURVEY IN
CONFORMANCE WITH THE REQUIREMENTS OF THE SUBDIVISION MAP ACT AND LOCAL ORDINANCE AT THE
REQUEST OF RICHMOND AMERICAN HOMES OF CALIFORNIA, INC., IN DECEMBER 2002. I HEREBY STATE THAT
ALL MONUMENTS ARE OF THE CHARACTER AND OCCUPY THE POSITIONS INDICATED, OR THAT THEY WILL BE
SET IN SUCH POSITIONS; AND THAT SAID MONUMENTS ARE SUFFICIENT TO ENABLE THE SURVEY TO BE
RETRACED. I HEREBY STATE THAT THIS MAP SUBSTANTIALLY CONFORMS TO THE CONDITIONALLY APPROVED
TENTATIVE MAP.

Jan A. Adams
JAN A. ADAMS, R.C.E. 21687
EXPIRES: 8/30/05

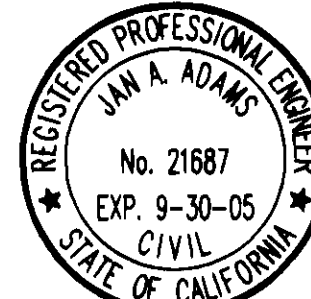

COUNTY SURVEYOR'S STATEMENT

I HEREBY STATE THAT I HAVE EXAMINED THIS MAP AND HAVE FOUND IT TO BE SUBSTANTIALLY IN
CONFORMANCE WITH THE TENTATIVE MAP AS FILED WITH, AMENDED AND APPROVED BY THE ORANGE
COUNTY SUBDIVISION COMMITTEE; THAT ALL PROVISIONS OF THE SUBDIVISION MAP ACT AND COUNTY
SUBDIVISION REGULATIONS HAVE BEEN COMPLIED WITH AND I AM SATISFIED SAID MAP IS TECHNICALLY
CORRECT.

DATED THIS 8TH DAY OF OCTOBER, 2003

Michael K. Sullivan
JOHN CANAS, COUNTY SURVEYOR
LS 4408 EXPIRATION DATE: 9-30-05

BY: MICHAEL K. SULLIVAN, DEPUTY
LS 6284 EXPIRES 6/30/06

COUNTY TREASURER - TAX COLLECTOR'S CERTIFICATE

STATE OF CALIFORNIA }
COUNTY OF ORANGE } ss

I HEREBY CERTIFY THAT ACCORDING TO THE RECORDS OF MY OFFICE THERE ARE NO LIENS AGAINST THE
LAND COVERED BY THIS MAP OR ANY PART THEREOF FOR UNPAID STATE, COUNTY, MUNICIPAL OR LOCAL
TAXES OR SPECIAL ASSESSMENTS COLLECTED AS TAXES, EXCEPT TAXES OR SPECIAL ASSESSMENTS
COLLECTED AS TAXES NOT YET PAYABLE.

AND DO ALSO CERTIFY TO THE RECORDER OF ORANGE COUNTY THAT THE PROVISIONS OF THE
SUBDIVISION MAP ACT HAVE BEEN COMPLIED WITH REGARDING DEPOSITS TO SECURE THE PAYMENT OF
TAXES OR SPECIAL ASSESSMENTS COLLECTED AS TAXES ON THE LAND COVERED BY THIS MAP.

DATED THIS 17th DAY OF September, 2003

JOHN M. W. MOORLACH
COUNTY TREASURER - TAX COLLECTOR

BY Joe Jorgensen
DEPUTY TREASURER - TAX COLLECTOR

CLERK OF THE BOARD OF SUPERVISOR'S CERTIFICATE

STATE OF CALIFORNIA }
COUNTY OF ORANGE } ss

I HEREBY CERTIFY THAT THIS MAP WAS PRESENTED FOR APPROVAL TO THE BOARD OF SUPERVISORS OF
ORANGE COUNTY AT A REGULAR MEETING THEREOF HELD ON THE 28th DAY OF October,
2003, AND THAT THEREUPON SAID BOARD DID, BY AN ORDER DULY PASSED AND ENTERED, APPROVE
SAID MAP.

AND DID ACCEPT ON BEHALF OF THE COUNTY OF ORANGE:

AN EASEMENT FOR EMERGENCY AND PUBLIC SERVICE VEHICULAR INGRESS-EGRESS AS DEDICATED.

AND DID ALSO APPROVE SUBJECT MAP PURSUANT TO THE PROVISIONS OF SECTION 66436 (a)(3)(A) OF
THE SUBDIVISION MAP ACT.

DATED THIS 28th DAY OF OCTOBER, 2003

Darlene J. Bloom
DARLENE J. BLOOM, CLERK OF THE BOARD OF SUPERVISORS



CERTIFICATE OF ACCEPTANCE

THE UNDERSIGNED, BEING THE DULY APPOINTED AGENT OF THE SANTA MARGARITA WATER DISTRICT,
A PUBLIC CORPORATION OF ORANGE COUNTY, CALIFORNIA, PURSUANT TO ITS RESOLUTION NO. 88-10-2,
DOES HEREBY ACCEPT ON BEHALF OF SAID DISTRICT THE EASEMENTS FOR SEWER, WATER AND ACCESS
PURPOSES, AS DEDICATED AND AS SHOWN ON THIS TRACT MAP, BY AND BETWEEN THE SANTA MARGARITA
WATER DISTRICT AND RICHMOND AMERICAN HOMES OF CALIFORNIA, INC. DOES HEREBY CERTIFY THAT THE
GRANTEE CONSENTS TO THE RECORDATION OF SAID TRACT.

Daniel R. Ferons
BY: DANIEL R. FERONS, CHIEF ENGINEER
SANTA MARGARITA WATER DISTRICT

STATE OF CALIFORNIA }
COUNTY OF ORANGE } ss

ON THIS 11th DAY OF September, 2003, BEFORE ME Cindy R. Lane, A NOTARY
PUBLIC IN AND FOR SAID STATE, PERSONALLY APPEARED Daniel R. Ferons PERSONALLY KNOWN TO ME
(OR PROVED TO ME ON THE BASIS OF SATISFACTORY EVIDENCE) TO BE THE PERSON WHOSE NAME IS
SUBSCRIBED TO THE WITHIN INSTRUMENT AND ACKNOWLEDGED TO ME THAT HE EXECUTED THE SAME IN
HIS AUTHORIZED CAPACITY AND THAT BY HIS SIGNATURE ON THE INSTRUMENT THE PERSON, OR THE
ENTITY UPON BEHALF OF WHICH THE PERSON ACTED, EXECUTED THE INSTRUMENT.

WITNESS MY HAND:

Cindy R. Lane
NOTARY PUBLIC IN AND FOR SAID STATE
CINDY R. LANE
PRINT NAME

MY PRINCIPAL PLACE OF BUSINESS
IS IN ORANGE COUNTY

MY COMMISSION EXPIRES FEB. 20, 2005

850 34

SHEET 2 OF 5 SHEETS
39 NUMBERED LOTS AND
LOTS A THROUGH N, INCLUSIVE
ACREAGE = 4.255 ACRES
A PORTION OF TENTATIVE
TRACT NO. 16271

TRACT MAP NO. 16352

IN THE UNINCORPORATED TERRITORY OF THE COUNTY OF ORANGE,
STATE OF CALIFORNIA
ADAMS - STREETER CIVIL ENGINEERS, INC. JAN A. ADAMS, R.C.E. 21687
DATE OF SURVEY: DEC. 2002

MONUMENT NOTES:

1. ● 2" IRON PIPE, TAGGED "R.C.E. 21687" TO BE SET PRIOR TO RECORDATION.
2. ■ 2" IRON PIPE, TAGGED "LS 5557", OR SPIKE AND WASHER, STAMPED "LS 5557", OR LEAD, TACK AND TAG "LS 5557" TO BE SET PER TRACT NO. 16271, MM 839/34-45, UNLESS OTHERWISE NOTED.
3. ■ 8" SPIKE AND WASHER STAMPED "LS. 5557" IN ASPHALT PAVING OR LEAD, TACK AND TAG "LS. 5557" IN CONCRETE OR 1" IRON PIPE, TAGGED "LS. 5557" TO BE SET PER TRACT 16271, MM 839/34-45.
4. 1" IRON PIPE, TAGGED "R.C.E. 21687", OR SPIKE AND WASHER, STAMPED "R.C.E. 21687", OR LEAD, TACK AND TAG "R.C.E. 21687" TO BE SET AT ALL LOT CORNERS, EXCEPT AT LOT CORNERS THAT ABUT A STREET, WHICH WILL BE SET ON A 9.75' OFFSET OUTSIDE THE TRUE LOT CORNER ON A PROLONGATION OF THE SIDE LOT LINE BY A LEAD, TACK AND TAG "R.C.E. 21687" IN THE TOP OF ADJACENT CONCRETE CURB, UNLESS OTHERWISE NOTED.
5. 8" SPIKE AND WASHER STAMPED "RCE 21687" IN ASPHALT PAVING OR LEAD, TACK AND TAG "R.C.E. 21687" IN CONCRETE OR 1" IRON PIPE, TAGGED "RCE 21687" TO BE SET AT ALL CENTERLINE INTERSECTIONS, B.C.'S, E.C.'S AND ALL OTHER CENTERLINE POINTS OF CONTROL, UNLESS OTHERWISE NOTED.
6. ALL MONUMENTS SHOWN AS "TO BE SET" WILL BE SET 90 DAYS AFTER THE ACCEPTANCE OF THE FINAL IMPROVEMENTS.
7. NO MONUMENTS TO BE SET AT BC'S AND EC'S OF STREET RIGHT OF WAY LINES.
8. ▲ FOUND GPS HORIZONTAL CONTROL POINT PER RECORDS ON FILE IN THE ORANGE COUNTY SURVEYOR'S OFFICE.

BASIS OF BEARINGS

THE BEARINGS SHOWN HEREON ARE BASED ON THE BEARING BETWEEN ORANGE COUNTY SURVEYOR'S HORIZONTAL CONTROL STATION "GPS NO. 1417" AND "GPS NO. 1448", BEING N. 10°48'13" E., PER RECORDS ON FILE IN THE OFFICE OF THE ORANGE COUNTY SURVEYOR.

DATUM STATEMENT


COORDINATES SHOWN HEREON ARE BASED ON THE CALIFORNIA COORDINATE SYSTEM (CCS83) ZONE VI, 1983 NAD (1991.35 EPOCH, O.C.S. GPS ADJUSTMENT). ALL DISTANCES SHOWN HEREON ARE GROUND, UNLESS OTHERWISE NOTED. TO OBTAIN GRID DISTANCE MULTIPLY GROUND DISTANCE BY 0.99993286.

AUTOMATIC FIRE SPRINKLER NOTE:

ALL RESIDENTIAL STRUCTURES EXCEEDING 5,500 SQUARE FEET AND ALL STRUCTURES EXCEEDING FIRE DEPARTMENT ACCESS REQUIREMENTS SHALL BE PROTECTED BY AN AUTOMATIC FIRE SPRINKLER SYSTEM, IN A MANNER MEETING THE APPROVAL OF THE FIRE CHIEF.

EASEMENT NOTES:

- A. AN EASEMENT FOR EMERGENCY AND PUBLIC SERVICE VEHICULAR INGRESS-EGRESS DEDICATED TO THE COUNTY OF ORANGE.
- B. AN EASEMENT FOR SEWER AND WATER PIPELINE AND ACCESS PURPOSES IN FAVOR OF THE SANTA MARGARITA WATER DISTRICT.

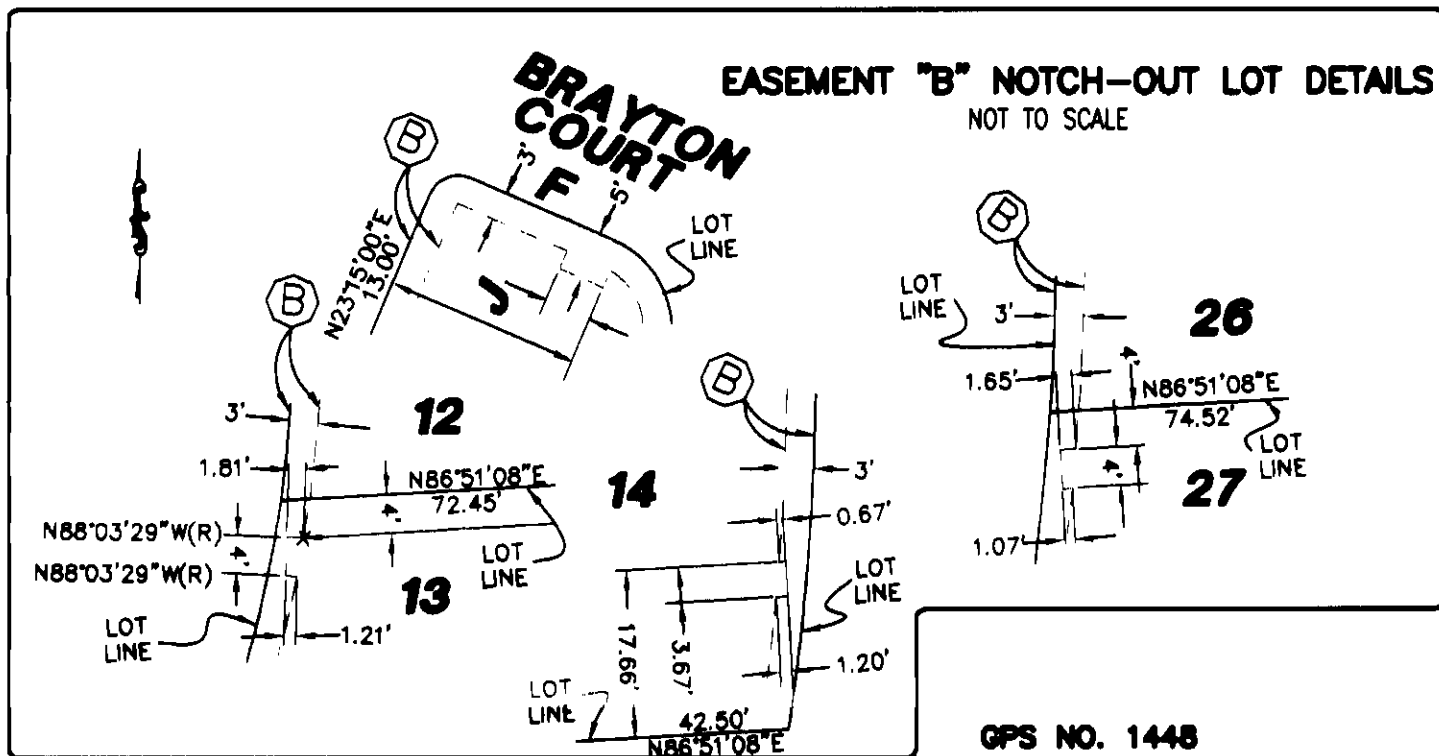


GPS NO. 1448

FOUND 2 1/2" IRON PIPE W/2" BRASS CAP STAMPED "GPS 1448 9-95" PER TRACT NO. 16025, MM 812/22-29 AND RECORDS ON FILE IN THE ORANGE COUNTY SURVEYOR'S OFFICE.

N 2146790.819
E 6142602.585

SHEET INDEX AND GPS CONTROL

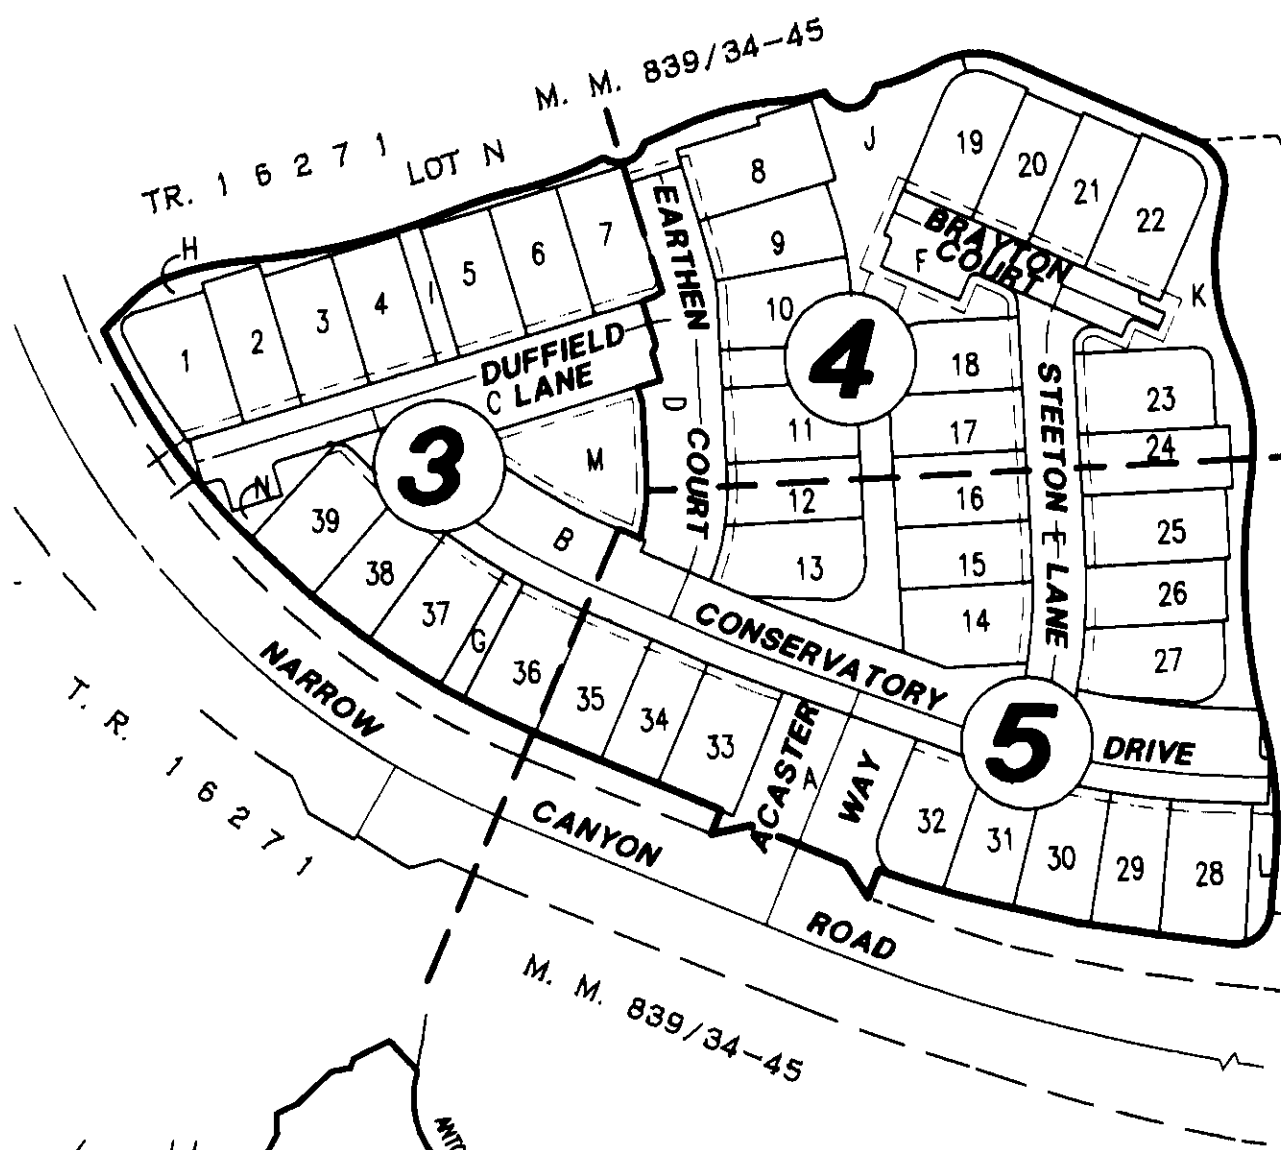


SCALE: 1"=100'

GPS NO. 1417

FOUND 2 1/2" IRON PIPE W/2" BRASS CAP STAMPED "GPS 1417 9-95" PER TRACT NO. 16025, MM 812/22-29 AND RECORDS ON FILE IN THE ORANGE COUNTY SURVEYOR'S OFFICE.

N 2141450.558
E 6141583.535

(X) - INDICATES SHEET NUMBER.

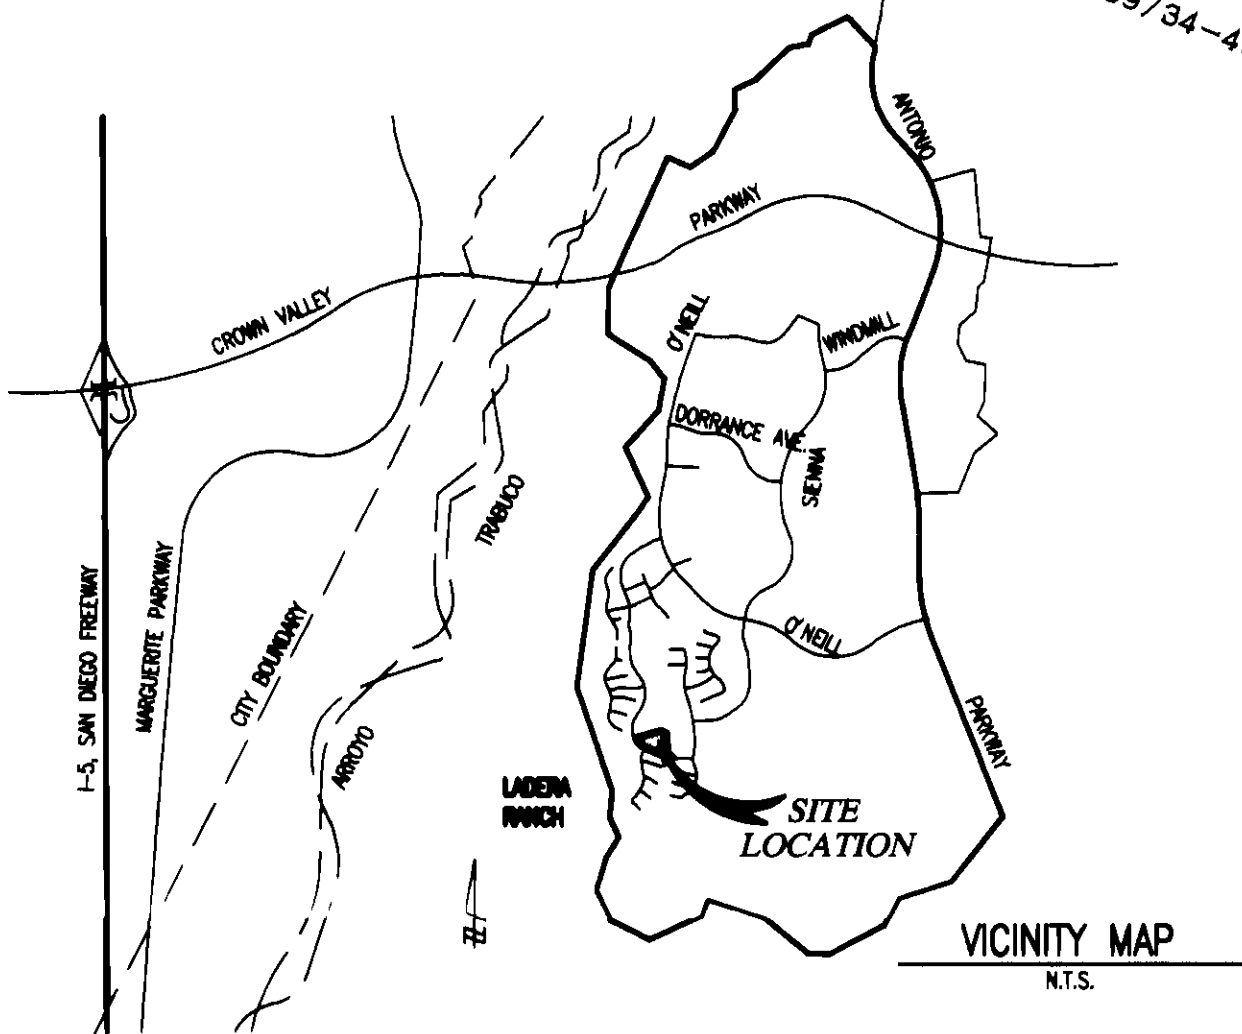

850 34

850 35

SHEET 3 OF 5

SCALE: 1" = 20'
39 NUMBERED LOTS AND
LOTS A THROUGH N, INCLUSIVE
ACREAGE = 4.255 ACRES
A PORTION OF TENTATIVE
TRACT NO. 16271
DATE OF SURVEY: DEC. 2002


TRACT NO. 16352

IN THE UNINCORPORATED TERRITORY OF ORANGE COUNTY,
STATE OF CALIFORNIA

ADAMS-STREETER CIVIL ENGINEERS, INC. JAN A. ADAMS R.C.E. 21687



NOTE: SEE SHEET 2 FOR GPS CONTROL, SHEET INDEX, MONUMENT NOTES,
EASEMENT NOTES, BASIS OF BEARINGS AND DATUM STATEMENTS.
LOTS A-F ARE NOT SEPARATE BUILDING SITES AND ARE FOR PRIVATE STREETS.
LOTS G-N ARE NOT SEPARATE BUILDING SITES AND ARE FOR LANDSCAPING PURPOSES.
ALL BEARINGS AND DISTANCES SHOWN ALONG THE MAP BOUNDARY ARE MEASURED AND
RECORD PER TR. 16271 M.M. 839/34-45

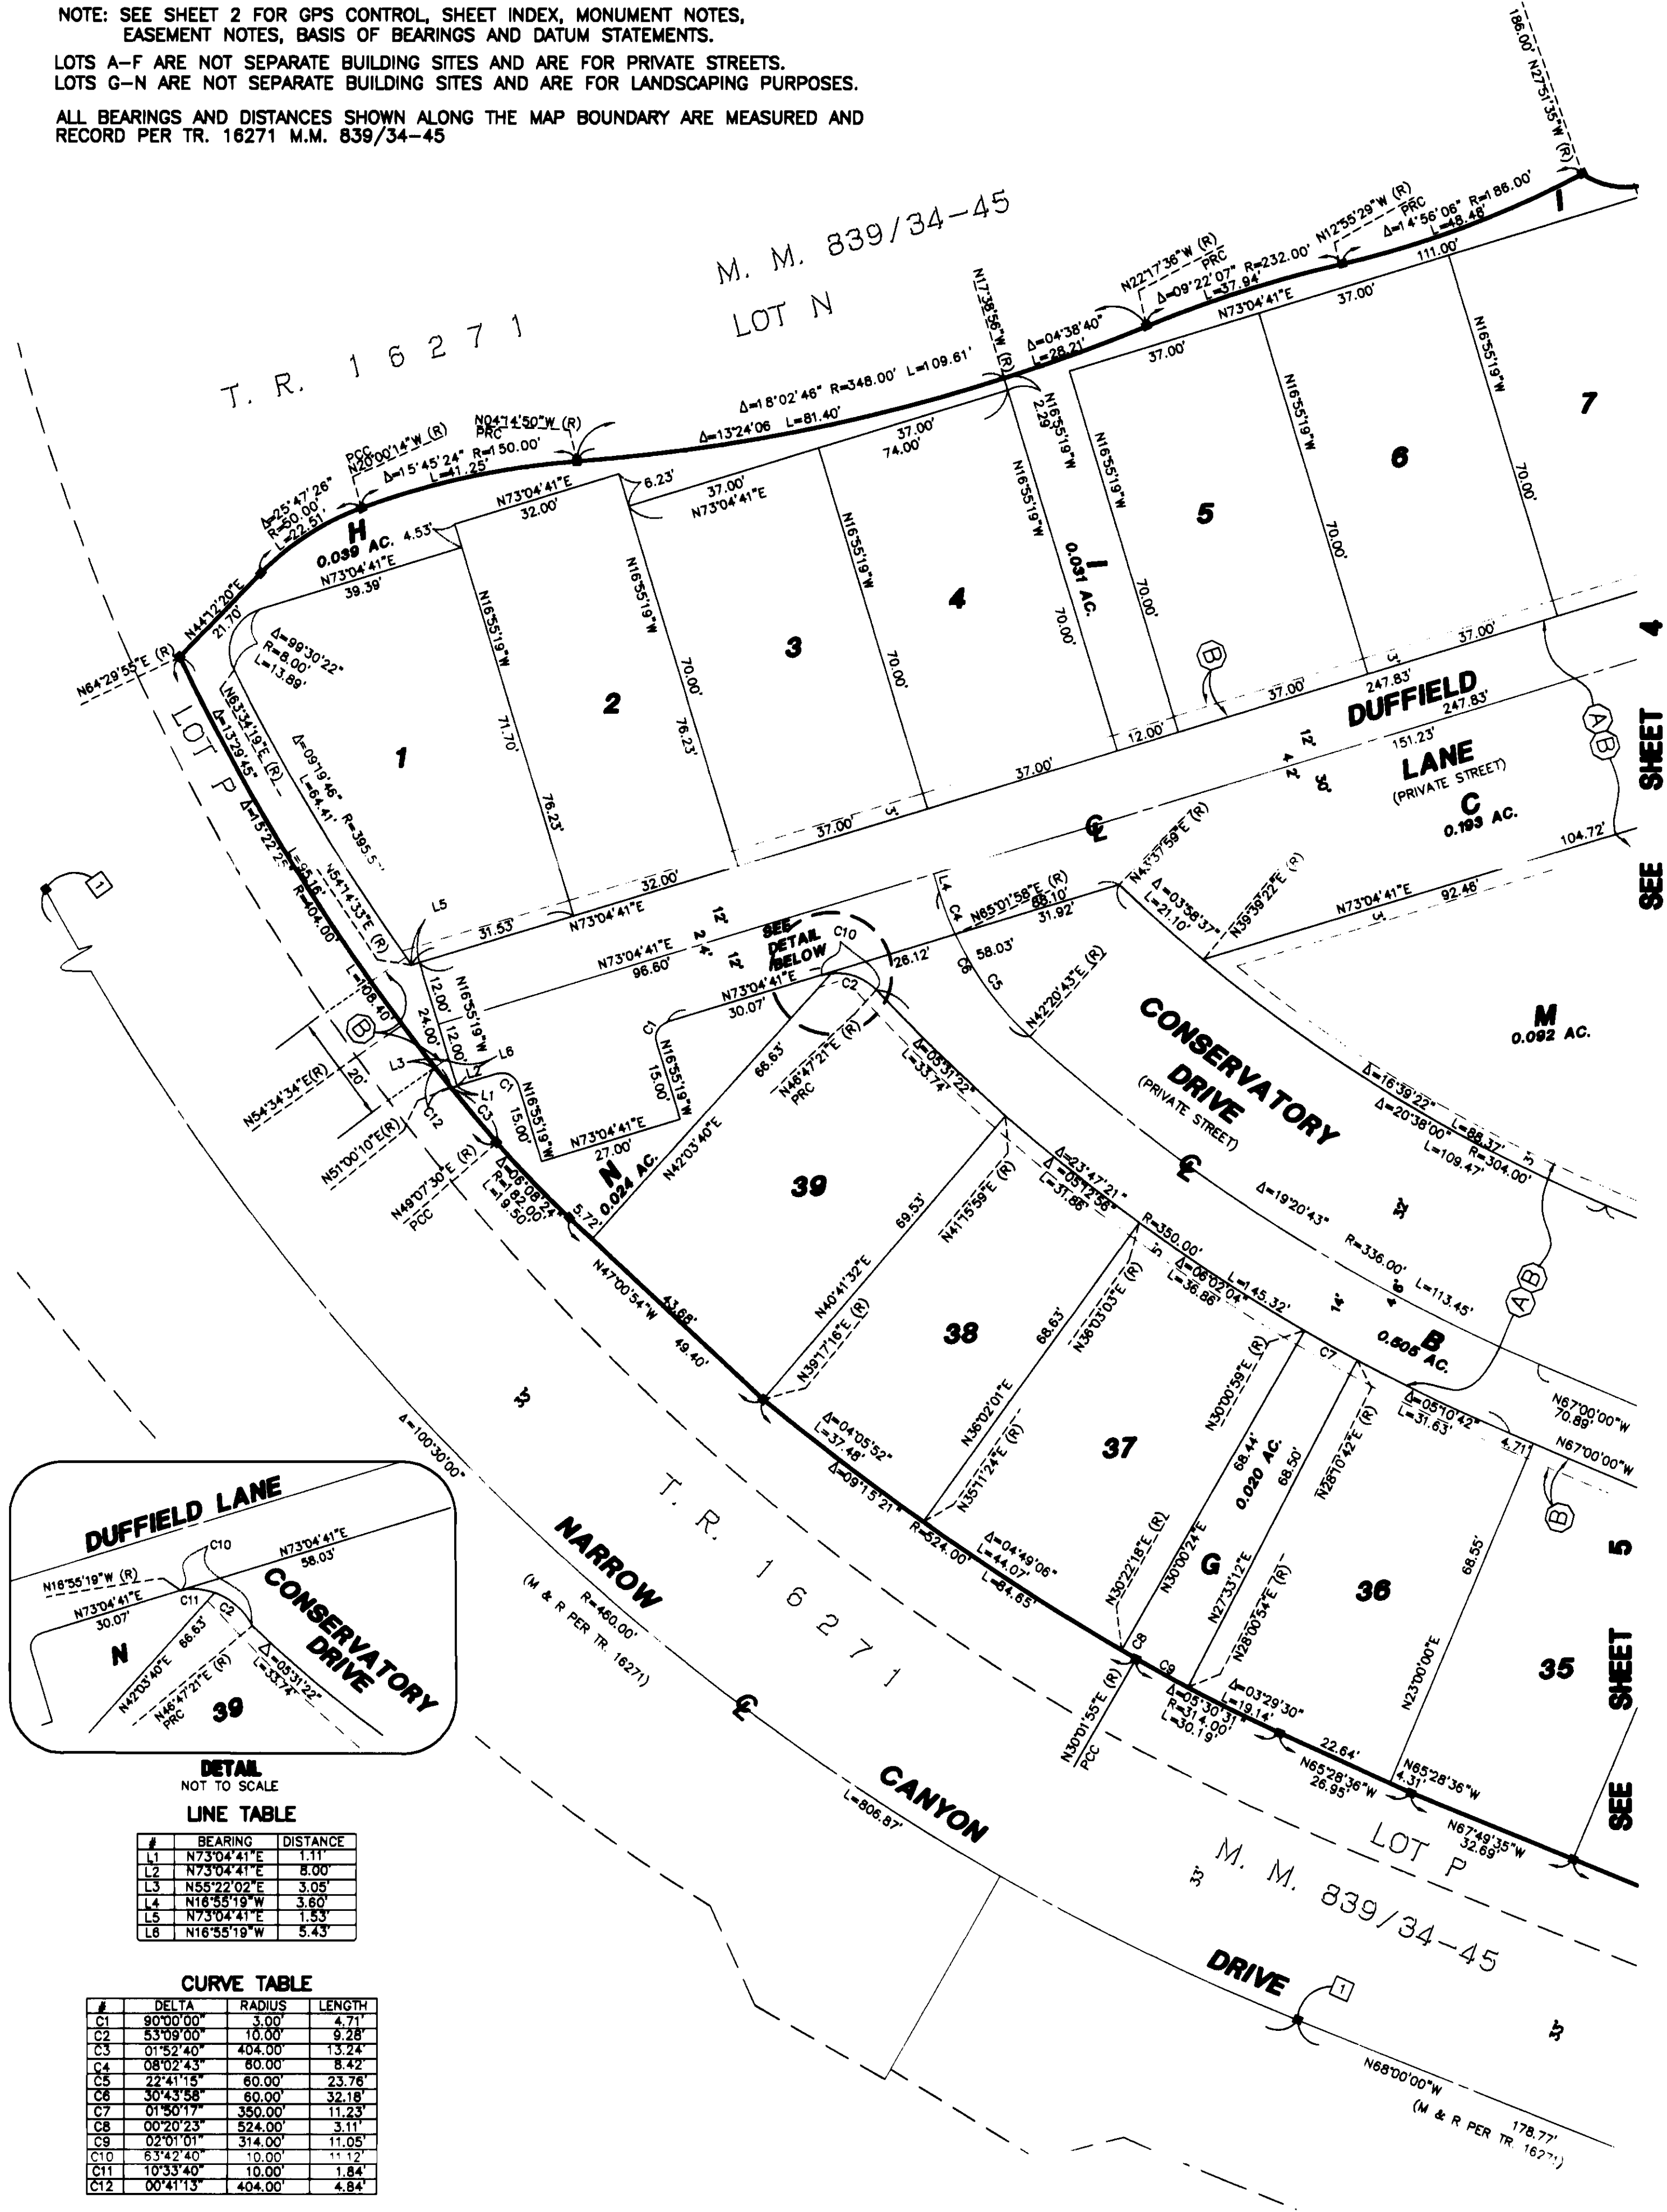

SEE SHEET

SEE SHEET

850 35

SHEET 4 OF 5

SCALE: 1" = 20'
39 NUMBERED LOTS AND
LOTS A THROUGH N, INCLUSIVE
ACREAGE = 4.255 ACRES
A PORTION OF TENTATIVE
TRACT NO. 16271

DATE OF SURVEY: DEC. 2002

ADAMS-STREETER CIVIL ENGINEERS, INC. JAN A. ADAMS R.C.E. 21687

TRACT NO. 16352

IN THE UNINCORPORATED TERRITORY OF ORANGE COUNTY,
STATE OF CALIFORNIA


NOTE: SEE SHEET 2 FOR GPS CONTROL, SHEET INDEX, MONUMENT NOTES,
EASEMENT NOTES, BASIS OF BEARINGS AND DATUM STATEMENTS.
ALL BEARINGS AND DISTANCES SHOWN ALONG THE MAP BOUNDARY
ARE MEASURED AND RECORDED PER TR. 16271 M.M. 839/34-45
SEE SHEET 2 FOR EASEMENT "B" NOTCH-OUT DETAILS FOR LOTS
J, I, 13, 14 & 21.

CURVE TABLE

#	DELTA	RADIUS	LENGTH
C1	90.00°	3.00'	4.71'
C2	63.36°	10.00'	11.10'
C3	116.23°	10.00'	20.32'
C4	19.54°	45.00'	15.63'
C5	49.49°	18.00'	12.62'
C6	40.10°	18.00'	21.48'
C7	24.36°	50.00'	1.56'
C8	0°-47'15"	50.00'	12.02'
C9	13°46'27"	14.00'	10.30'
C10	42°10'18"	14.00'	16.40'
C11	67°06'02"	50.00'	23.04'
C12	26°23'52"	50.00'	23.04'

LINE TABLE

#	BEARING	DISTANCE
1	N66°45'00"W	2.00'
2	N66°45'00"W	13.00'
3	N23°15'00"E	8.00'
4	N23°15'00"E	2.00'
5	N23°15'00"E	9.00'
6	N23°15'00"E	1.50'
7	N23°15'00"E	10.94'
8	N16°55'19"W	8.41'
9	N16°55'19"W	6.00'
10	N16°55'19"W	11.08'
11	N16°55'19"W	2.08'
12	N7°04'41"E	6.17'
13	N15°28'27"E	8.16'
14	N86°51'08"E	12.42'

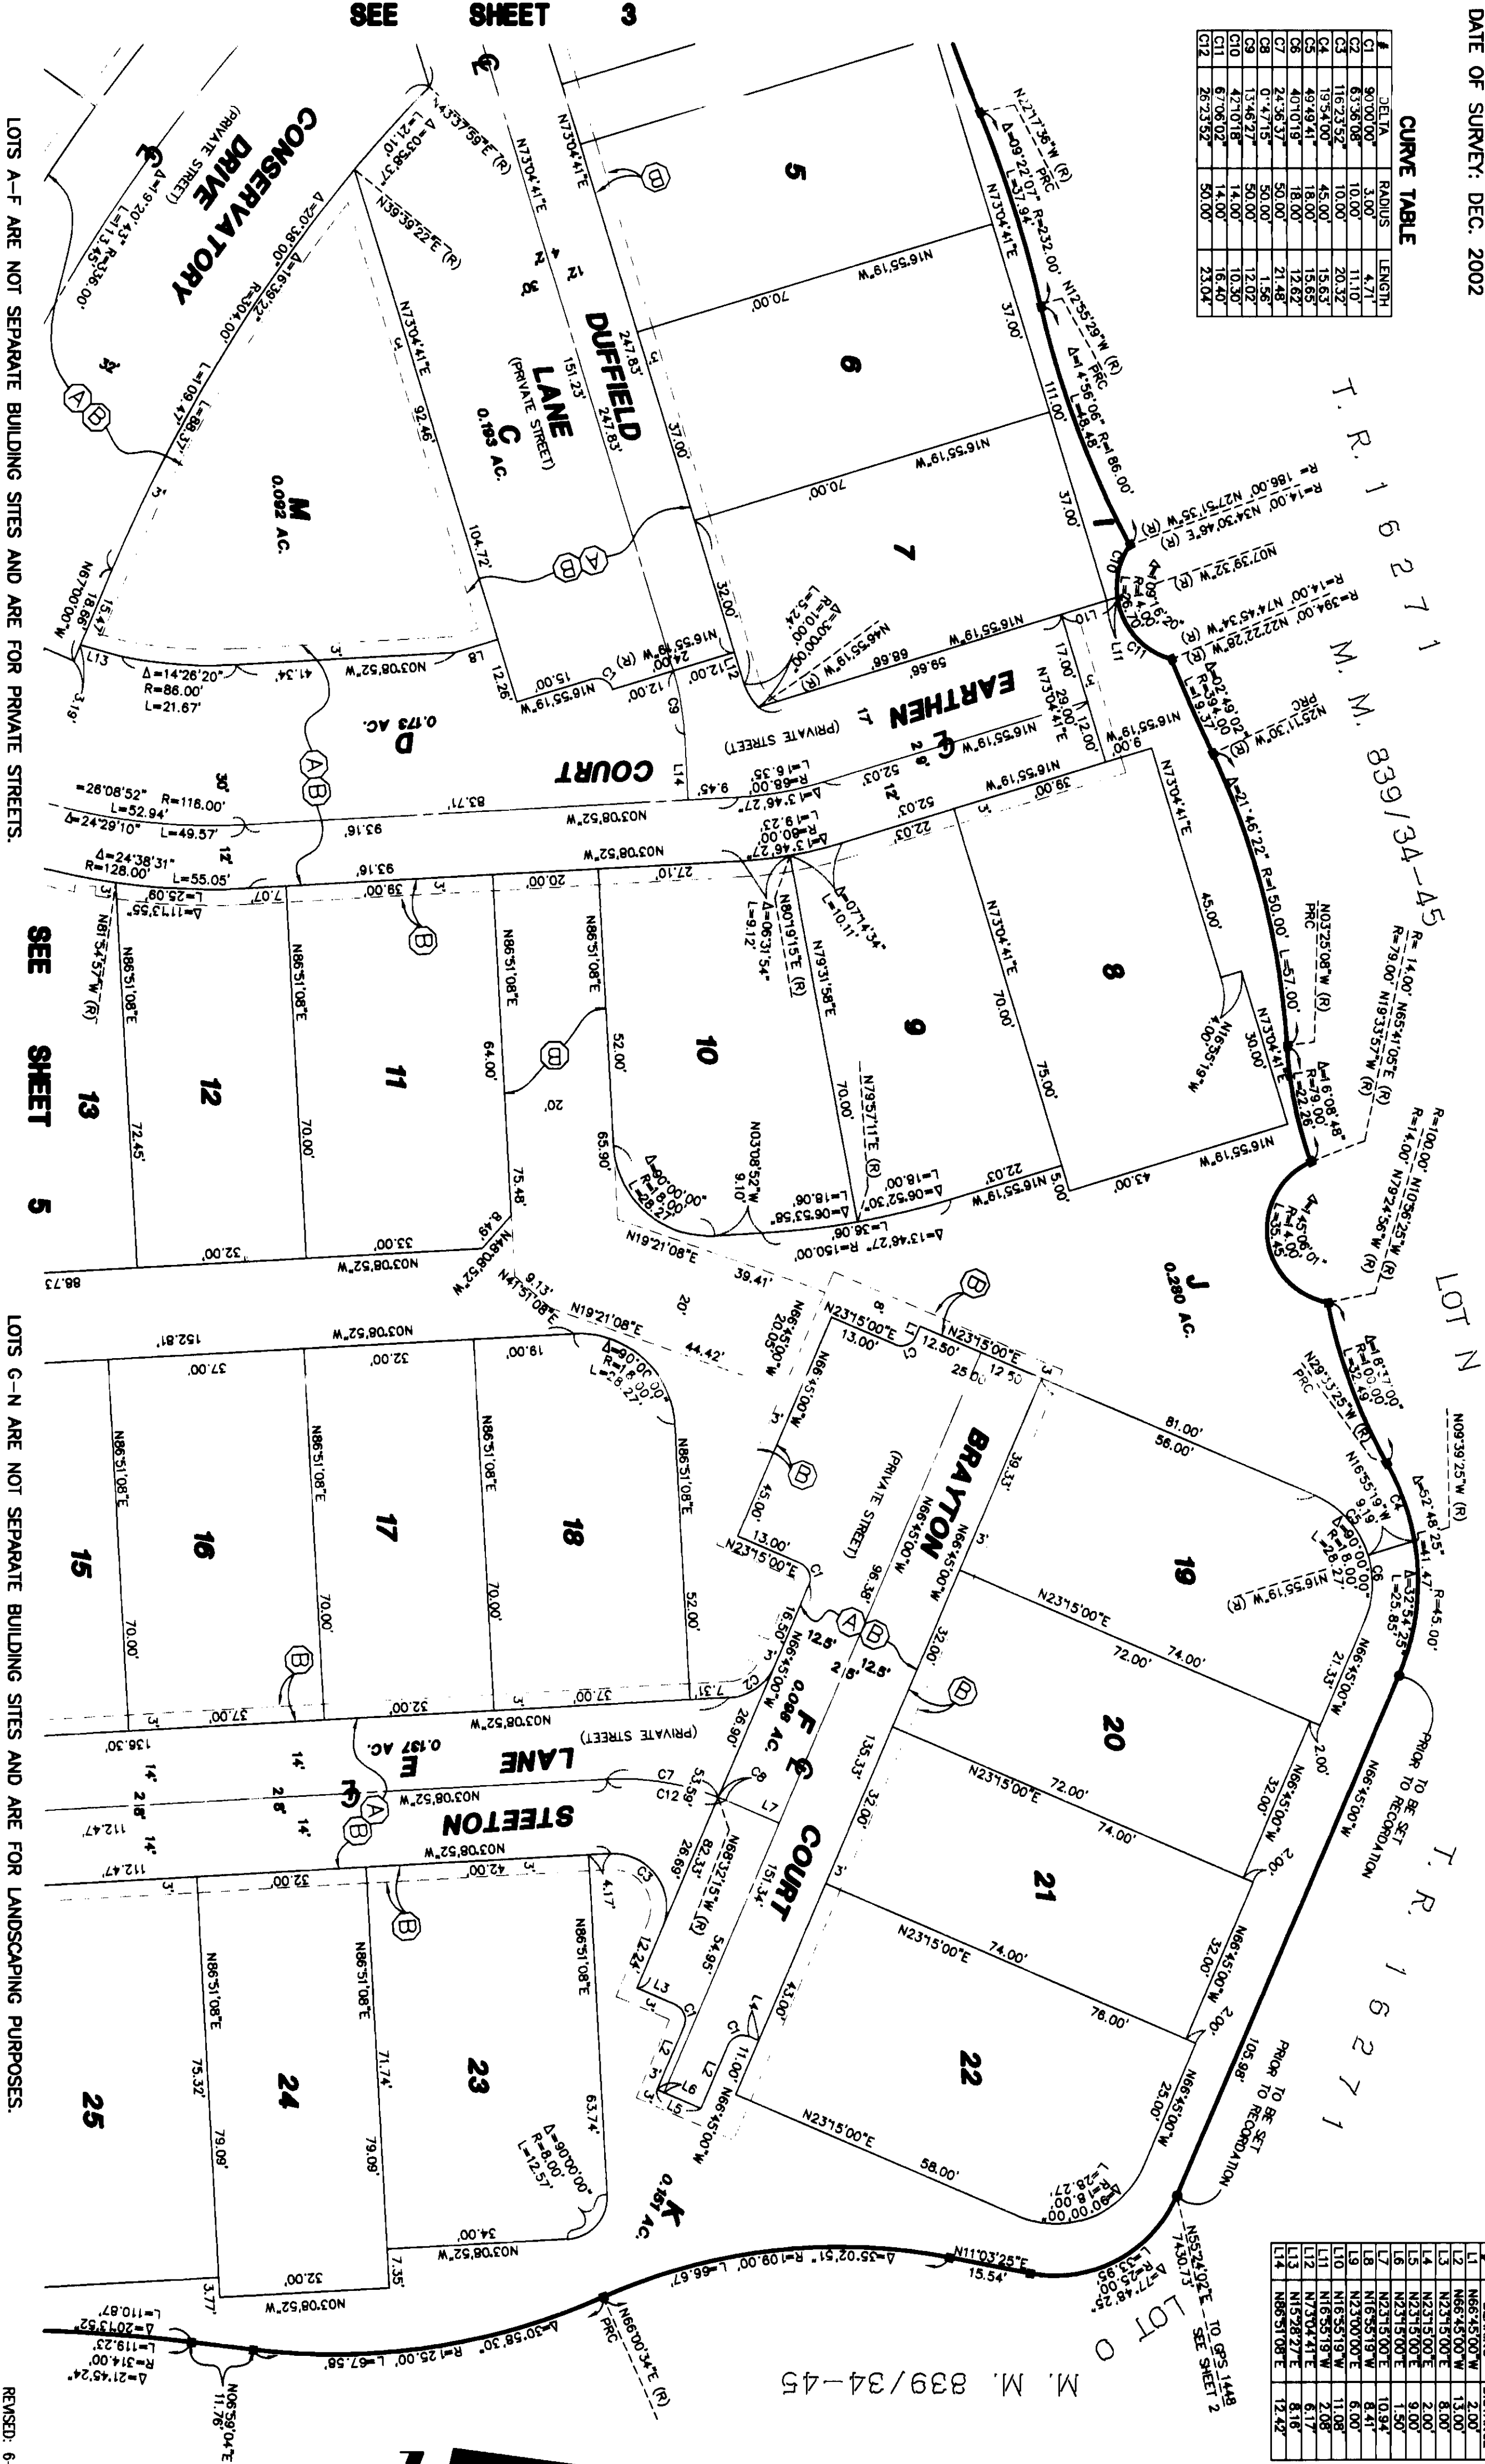

LOTS A-F ARE NOT SEPARATE BUILDING SITES AND ARE FOR PRIVATE STREETS.

SEE SHEET 5


LOTS G-N ARE NOT SEPARATE BUILDING SITES AND ARE FOR LANDSCAPING PURPOSES.

SHEET 5 OF 5
SCALE: 1" = 20'
39 NUMBERED LOTS AND
LOTS A THROUGH N, INCLUSIVE
ACREAGE = 4.255 ACRES
A PORTION OF TENTATIVE
TRACT NO. 16271
DATE OF SURVEY: DEC. 2002

TRACT NO. 16352
IN THE UNINCORPORATED TERRITORY OF ORANGE COUNTY,
STATE OF CALIFORNIA
ADAMS-STREETER CIVIL ENGINEERS, INC. JAN A. ADAMS R.C.E. 21687

NOTE: SEE SHEET 2 FOR GPS CONTROL, SHEET INDEX, MONUMENT NOTES,
EASEMENT NOTES, BASIS OF BEARINGS AND DATUM STATEMENTS.
ALL BEARINGS AND DISTANCES SHOWN ALONG THE MAP BOUNDARY
ARE MEASURED AND RECORDED PER TR. 16271 M.M. 839/34-45
SEE SHEET 2 FOR EASEMENT "B" NOTCH-OUT DETAILS FOR LOTS
25, 13, 14 & 27.

SEE SHEET 4

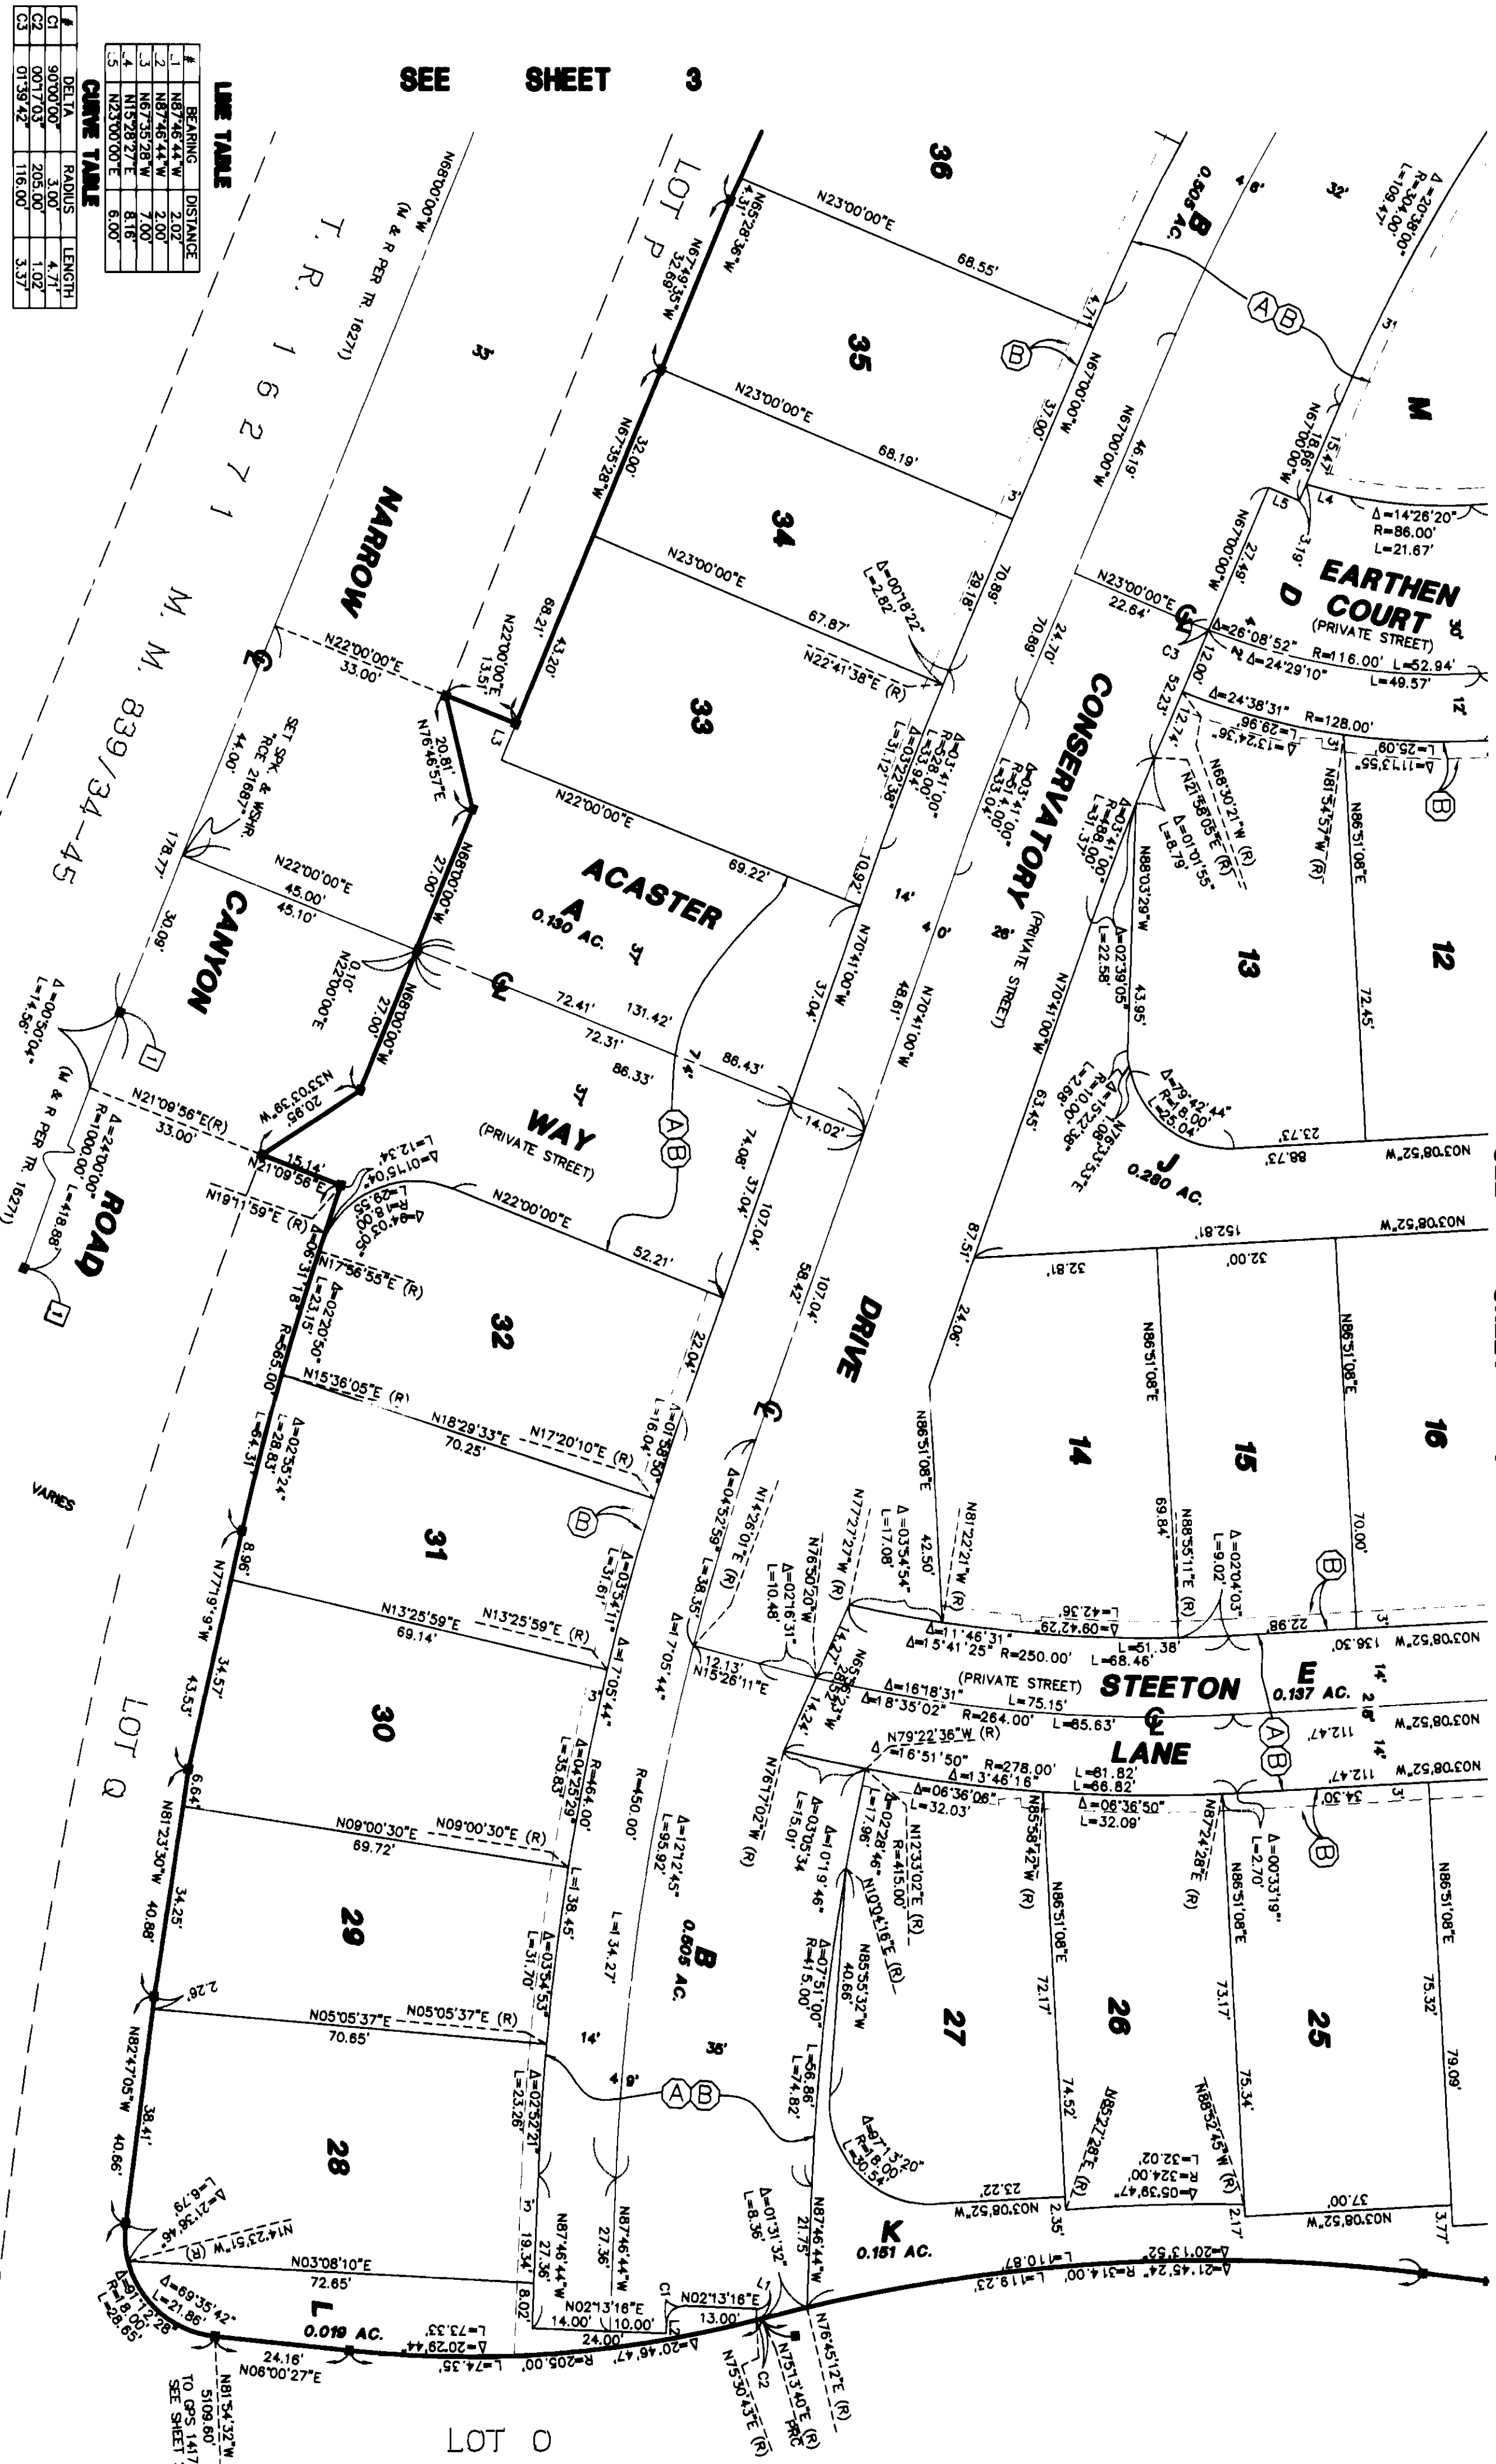

CURVE TABLE

#	BEARING	DISTANCE
1	N87°46'44"W	2.02
2	N87°46'44"W	2.00
3	N67°35'28"W	7.00
4	N15°28'27"E	8.18
5	N23°00'00"E	6.00

CURVE TABLE

#	DELTA	RADIUS	LENGTH
C1	90°00'00"	3.00	4.71
C2	90°17'03"	205.00	1.02
C3	01°39'42"	116.00	3.37

LOTS A-F ARE NOT SEPARATE BUILDING SITES AND ARE FOR PRIVATE STREETS.

LOTS G-N ARE NOT SEPARATE BUILDING SITES AND ARE FOR LANDSCAPING PURPOSES.

M. M. 839/34-45

T. R. 16271