

SHEET 1 OF 5 SHEETS

TRACT NO. 16353

ALL OF VESTING TENTATIVE TRACT
MAP NO. 16353
TOTAL LOTS: NUMBERED LOTS 1 THROUGH 44
AND LETTERED LOTS A THROUGH N
TOTAL ACREAGE: 6.367 ACRES

IN THE UNINCORPORATED TERRITORY OF THE COUNTY OF ORANGE,
STATE OF CALIFORNIA
BEING A SUBDIVISION OF LOT 7, AS SHOWN ON TRACT NO. 16271
FILED IN BOOK 839, PAGES 34 THROUGH 45 OF MISCELLANEOUS MAPS,
IN THE OFFICE OF THE COUNTY RECORDER OF SAID COUNTY, STATE OF CALIFORNIA
ADAMS - STREETER CIVIL ENGINEERS, INC. JAN A. ADAMS, R.C.E. 21687
DATE OF SURVEY: APRIL, 2003

ACCEPTED AND FILED AT THE
REQUEST OF
FIDELITY NATIONAL TITLE COMPANY

DATE DECEMBER 19, 2003
TIME 02:59 PM FEE \$ 15.00
INSTRUMENT # 2003001502989
BOOK 853 PAGE 16-20 m/n
TOM DALY
COUNTY CLERK-RECORDER
BY [Signature] DEPUTY

OWNERSHIP CERTIFICATE

WE, THE UNDERSIGNED, BEING ALL PARTIES HAVING ANY RECORD TITLE INTEREST IN THE LAND COVERED BY THIS MAP, DO HEREBY CONSENT TO THE PREPARATION AND RECORDATION OF SAID MAP, AS SHOWN WITHIN THE DISTINCTIVE BORDER LINE.

WE HEREBY DEDICATE TO THE COUNTY OF ORANGE:

1. AN EASEMENT FOR EMERGENCY AND PUBLIC SERVICE VEHICULAR INGRESS-EGRESS PURPOSES AS SHOWN ON THIS MAP.

WE ALSO DEDICATE TO THE SANTA MARGARITA WATER DISTRICT, THE EASEMENTS FOR SEWER, WATER PIPELINE AND ACCESS PURPOSES AS SHOWN ON THIS MAP, WHICH EASEMENTS SHALL BE SUBJECT TO THE SAME TERMS AND CONDITIONS AS ARE SHOWN IN THAT CERTAIN EASEMENT RECORDED OCTOBER 6, 1980, IN BOOK 13776, PAGE 341, OF OFFICIAL RECORDS, COUNTY OF ORANGE.

WILLIAM LYON HOMES, INC., A CALIFORNIA CORPORATION

BY: [Signature]
PRINT NAME: THOMAS J. MITCHELL
PRINT TITLE: SENIOR VICE PRESIDENT

BY: [Signature]
PRINT NAME: Thomas G. Grable
PRINT TITLE: Assistant Secretary

RESIDENTIAL FUNDING CORPORATION, A DELAWARE CORPORATION, BENEFICIARY UNDER A DEED OF TRUST RECORDED APRIL 4, 2003 AS INSTRUMENT NO. 2003000372400 OF OFFICIAL RECORDS.

BY: [Signature]
PRINT NAME: DONALD V. PIERCE
PRINT TITLE: MANAGING DIRECTOR

BY: [Signature]
PRINT NAME: Michael Frank
PRINT TITLE: Managing Director

DMB LADERA, LLC, A DELAWARE LIMITED LIABILITY COMPANY, BENEFICIARY UNDER A DEED OF TRUST RECORDED APRIL 4, 2003 AS INSTRUMENT NO. 2003000372402 OF OFFICIAL RECORDS.

BY: [Signature]
PRINT NAME: RANCHO MISSION VIEJO, LLC, A DELAWARE LIMITED LIABILITY COMPANY, ITS AUTHORIZED AGENT AND MANAGER.

BY: [Signature]
PRINT NAME: DONALD T. STANLON
PRINT TITLE: VICE PRESIDENT

BY: [Signature]
PRINT NAME: Gregory S. Edwards
PRINT TITLE: Chief Financial Officer

STATE OF CALIFORNIA)
COUNTY OF ORANGE) SS

ON THIS 26th DAY OF August, 2003, BEFORE ME, Sheryl L. Alworth, A NOTARY PUBLIC IN AND FOR SAID STATE, PERSONALLY APPEARED Thomas J. Mitchell AND Thomas G. Grable PERSONALLY KNOWN TO ME (OR PROVED TO ME ON THE BASIS OF SATISFACTORY EVIDENCE) TO BE THE PERSONS WHOSE NAMES ARE SUBSCRIBED TO THE WITHIN INSTRUMENT AND ACKNOWLEDGED TO ME THAT THEY EXECUTED THE SAME IN THEIR AUTHORIZED CAPACITIES, AND THAT BY THEIR SIGNATURES ON THE INSTRUMENT THE PERSONS, OR THE ENTITY UPON BEHALF OF WHICH THE PERSONS ACTED, EXECUTED THE INSTRUMENT.

WITNESS MY HAND:

[Signature]
NOTARY PUBLIC IN AND FOR SAID STATE
Sheryl L. Alworth
PRINT NAME

MY PRINCIPAL PLACE OF BUSINESS
IS IN Orange COUNTY
MY COMMISSION EXPIRES January 13, 2006

STATE OF Minnesota)
COUNTY OF Hennepin) SS

ON THIS 4th DAY OF September, 2003, BEFORE ME, Rodney C. Achenbach, A NOTARY PUBLIC IN AND FOR SAID STATE, PERSONALLY APPEARED Donald V. Pierce AND Michael Frank PERSONALLY KNOWN TO ME (OR PROVED TO ME ON THE BASIS OF SATISFACTORY EVIDENCE) TO BE THE PERSONS WHOSE NAMES ARE SUBSCRIBED TO THE WITHIN INSTRUMENT AND ACKNOWLEDGED TO ME THAT THEY EXECUTED THE SAME IN THEIR AUTHORIZED CAPACITIES, AND THAT BY THEIR SIGNATURES ON THE INSTRUMENT THE PERSONS, OR THE ENTITY UPON BEHALF OF WHICH THE PERSONS ACTED, EXECUTED THE INSTRUMENT.

WITNESS MY HAND:

[Signature]
NOTARY PUBLIC IN AND FOR SAID STATE
Rodney C. Achenbach
PRINT NAME

MY PRINCIPAL PLACE OF BUSINESS
IS IN Hennepin COUNTY
MY COMMISSION EXPIRES 1/31/05

STATE OF CALIFORNIA)
COUNTY OF ORANGE) SS

ON THIS 9th DAY OF September, 2003, BEFORE ME, Diana L. Binks, A NOTARY PUBLIC IN AND FOR SAID STATE, PERSONALLY APPEARED Donald T. Stanlon AND Gregory S. Edwards PERSONALLY KNOWN TO ME (OR PROVED TO ME ON THE BASIS OF SATISFACTORY EVIDENCE) TO BE THE PERSONS WHOSE NAMES ARE SUBSCRIBED TO THE WITHIN INSTRUMENT AND ACKNOWLEDGED TO ME THAT THEY EXECUTED THE SAME IN THEIR AUTHORIZED CAPACITIES, AND THAT BY THEIR SIGNATURES ON THE INSTRUMENT THE PERSONS, OR THE ENTITY UPON BEHALF OF WHICH THE PERSONS ACTED, EXECUTED THE INSTRUMENT.

WITNESS MY HAND:


[Signature]
NOTARY PUBLIC IN AND FOR SAID STATE
Diana L. Binks
PRINT NAME

MY PRINCIPAL PLACE OF BUSINESS
IS IN Orange COUNTY
MY COMMISSION EXPIRES December 12, 2006

ENGINEER'S STATEMENT

THIS MAP WAS PREPARED BY ME OR UNDER MY DIRECTION AND IS BASED UPON A FIELD SURVEY IN CONFORMANCE WITH THE REQUIREMENTS OF THE SUBDIVISION MAP ACT AND LOCAL ORDINANCE AT THE REQUEST OF WILLIAM LYON HOMES, INC. IN APRIL, 2003. I HEREBY STATE THAT ALL MONUMENTS ARE OF THE CHARACTER AND OCCUPY THE POSITIONS INDICATED, OR THAT THEY WILL BE SET IN SUCH POSITIONS; AND THAT SAID MONUMENTS ARE SUFFICIENT TO ENABLE THE SURVEY TO BE RETRACED. I HEREBY STATE THAT THIS FINAL MAP SUBSTANTIALLY CONFORMS TO THE CONDITIONALLY APPROVED TENTATIVE MAP.

[Signature]
JAN A. ADAMS, R.C.E. 21687
EXPIRES: 9/30/05

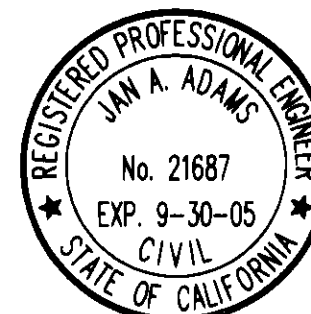

COUNTY SURVEYOR'S STATEMENT

I HEREBY STATE THAT I HAVE EXAMINED THIS MAP AND HAVE FOUND IT TO BE SUBSTANTIALLY IN CONFORMANCE WITH THE TENTATIVE MAP AS FILED WITH, AMENDED AND APPROVED BY THE ORANGE COUNTY SUBDIVISION COMMITTEE; THAT ALL PROVISIONS OF THE SUBDIVISION MAP ACT AND COUNTY SUBDIVISION REGULATIONS HAVE BEEN COMPLIED WITH AND I AM SATISFIED SAID MAP IS TECHNICALLY CORRECT.

DATED THIS 4TH DAY OF DECEMBER, 2003

[Signature]
JOHN CANAS, COUNTY SURVEYOR
LS 4408 EXPIRATION DATE: 9-30-05
BY: Michael K. Sullivan DEPUTY
LS 6884 EXPIRES 6/30/06



COUNTY TREASURER - TAX COLLECTOR'S CERTIFICATE

STATE OF CALIFORNIA)
COUNTY OF ORANGE) SS

I HEREBY CERTIFY THAT ACCORDING TO THE RECORDS OF MY OFFICE, THERE ARE NO LIENS AGAINST THE LAND COVERED BY THIS MAP OR ANY PART THEREOF FOR UNPAID STATE, COUNTY, MUNICIPAL OR LOCAL TAXES OR SPECIAL ASSESSMENTS COLLECTED AS TAXES, EXCEPT TAXES OR SPECIAL ASSESSMENTS COLLECTED AS TAXES NOT YET PAYABLE.

~~AND DO ALSO CERTIFY TO THE RECORDER OF ORANGE COUNTY THAT THE PROVISIONS OF THE SUBDIVISION MAP ACT HAVE BEEN COMPLIED WITH REGARDING DEPOSITS TO SECURE PAYMENT OF TAXES OR SPECIAL ASSESSMENTS COLLECTED AS TAXES ON THE LAND COVERED BY THIS MAP.~~

DATED THIS 1st DAY OF December, 2003

JOHN M. W. MOORLACH
COUNTY TREASURER - TAX COLLECTOR

BY: [Signature]
DEPUTY TREASURER - TAX COLLECTOR

CLERK OF THE BOARD OF SUPERVISORS CERTIFICATE

STATE OF CALIFORNIA)
COUNTY OF ORANGE) SS

I HEREBY CERTIFY THAT THIS MAP WAS PRESENTED FOR APPROVAL TO THE BOARD OF SUPERVISORS OF ORANGE COUNTY AT A REGULAR MEETING THEREOF HELD ON THE 16th DAY OF December, 2003, AND THAT THEREUPON SAID BOARD DID, BY AN ORDER DULY PASSED AND ENTERED, APPROVE SAID MAP.

AND DID ACCEPT ON BEHALF OF THE COUNTY OF ORANGE:

1. THE EASEMENT FOR EMERGENCY AND PUBLIC SERVICE VEHICULAR INGRESS-EGRESS, AS DEDICATED.

DATED THIS 16th DAY OF December, 2003.

[Signature]
DARLENE J. BLOOM, CLERK OF THE BOARD OF SUPERVISORS



CERTIFICATE OF ACCEPTANCE

THE UNDERSIGNED, BEING THE DULY APPOINTED AGENT OF THE SANTA MARGARITA WATER DISTRICT, A PUBLIC CORPORATION OF ORANGE COUNTY, CALIFORNIA, PURSUANT TO ITS RESOLUTION NO. 88-10-2, DOES HEREBY ACCEPT ON BEHALF OF SAID DISTRICT THE EASEMENTS FOR SEWER, WATER AND ACCESS PURPOSES, AS DEDICATED AND AS SHOWN ON THIS TRACT MAP, BY AND BETWEEN THE SANTA MARGARITA WATER DISTRICT AND DMB LADERA, LLC, AND DOES HEREBY CERTIFY THAT THE GRANTEE CONSENTS TO THE RECORDATION OF SAID TRACT.

BY: [Signature]
DANIEL R. FERONS, CHIEF ENGINEER
SANTA MARGARITA WATER DISTRICT

STATE OF CALIFORNIA)
COUNTY OF ORANGE) SS

ON THIS 18th DAY OF SEPTEMBER, 2003, BEFORE ME, CINDY R. LANE, A NOTARY PUBLIC IN AND FOR SAID STATE, PERSONALLY APPEARED Daniel R. Ferons, PERSONALLY KNOWN TO ME (OR PROVED TO ME ON THE BASIS OF SATISFACTORY EVIDENCE) TO BE THE PERSON WHOSE NAME IS SUBSCRIBED TO THE WITHIN INSTRUMENT AND ACKNOWLEDGED TO ME THAT HE EXECUTED THE SAME IN HIS AUTHORIZED CAPACITY AND THAT BY HIS SIGNATURE ON THE INSTRUMENT THE PERSON, OR THE ENTITY UPON BEHALF OF WHICH THE PERSON ACTED, EXECUTED THE INSTRUMENT.

WITNESS MY HAND:

[Signature]
NOTARY PUBLIC IN AND FOR SAID STATE
CINDY R. LANE
PRINT NAME

MY PRINCIPAL PLACE OF BUSINESS
IS IN ORANGE COUNTY
MY COMMISSION EXPIRES 8-20-05

TRACT NO. 16353

ALL OF VESTING TENTATIVE TRACT
MAP NO. 16353
TOTAL LOTS: NUMBERED LOTS 1 THROUGH 44
AND LETTERED LOTS A THROUGH N
TOTAL ACREAGE: 6.367 ACRES

IN THE UNINCORPORATED TERRITORY OF THE COUNTY OF ORANGE,
STATE OF CALIFORNIA

ADAMS - STREETER CIVIL ENGINEERS, INC. JAN A. ADAMS, R.C.E. 21687
DATE OF SURVEY: APRIL, 2003

BASIS OF BEARINGS

THE BEARINGS SHOWN HEREON ARE BASED ON THE BEARING BETWEEN ORANGE COUNTY SURVEYOR'S HORIZONTAL CONTROL STATION GPS NO. 1417 AND STATION GPS NO. 1448 BEING N10°48'13"E PER TRACT NO. 16271, MM 839/34-45, RECORDS OF ORANGE COUNTY, CALIFORNIA.

DATUM STATEMENT

COORDINATES SHOWN ARE BASED ON THE CALIFORNIA COORDINATE SYSTEM (CCS83), ZONE VI, 1983 NAD (1991.35 EPOCH O.C.S. GPS ADJUSTMENT).

ALL DISTANCES SHOWN ARE GROUND, UNLESS OTHERWISE NOTED. TO OBTAIN GRID DISTANCES MULTIPLY THE GROUND DISTANCE BY THE COMBINATION FACTOR 0.999948295 SPECIFIC TO THIS PROJECT.

MONUMENT NOTES

- ① INDICATES FOUND O.C.S. HORIZONTAL CONTROL STATION AS NOTED.
- INDICATES LOCATION OF 2" IRON PIPE TAGGED "P.L.S. 5557", OR SPIKE AND WASHER STAMPED "P.L.S. 5557", OR LEAD, TACK AND TAG "P.L.S. 5557" TO BE SET PER TRACT NO. 16341, MM 840/1-20.
- INDICATES LOCATION OF 2" IRON PIPE TAGGED "P.L.S. 5557", OR SPIKE AND WASHER STAMPED "P.L.S. 5557", OR LEAD, TACK AND TAG "P.L.S. 5557" TO BE SET PER TRACT NO. 16271, MM 839/34-45.
- INDICATES SET 2" IRON PIPE TAGGED "RCE 21687" PRIOR TO RECORDATION OF THIS MAP.
- 2" IRON PIPE TAGGED "RCE 21687", OR SPIKE AND WASHER STAMPED "RCE 21687", OR LEAD, TACK AND TAG STAMPED "RCE 21687", OR NAIL AND TAG STAMPED "RCE 21687", OR A TAG STAMPED "RCE 21687" SECURED WITH EPOXY TO BE SET AT ALL TRACT BOUNDARY CORNERS, UNLESS OTHERWISE NOTED.
- 1" IRON PIPE TAGGED "RCE 21687", OR SPIKE AND WASHER STAMPED "RCE 21687", OR LEAD, TACK AND TAG STAMPED "RCE 21687", OR NAIL AND TAG STAMPED "RCE 21687", OR A TAG STAMPED "RCE 21687" SECURED WITH EPOXY TO BE SET AT ALL CORNERS, EXCEPT AT THOSE LOT CORNERS:
 - THAT ABOUT A SIDEWALK, IN WHICH CASE, LEAD, TACK AND TAG STAMPED "RCE 21687" WILL BE SET ON THE PROLONGATION OF THE SIDE LOT LINE, 0.50 FEET FROM THE TRUE LOT CORNER, IN THE ADJACENT CONCRETE SIDEWALK;
 - THAT ARE LOCATED IN THE FACE OF THE CONCRETE CURB, IN WHICH CASE, LEAD, TACK AND TAG STAMPED "RCE 21687" WILL BE SET ON THE SIDE LOT LINE, 0.25 FEET FROM THE TRUE LOT CORNER, IN THE TOP OF THE CONCRETE CURB, AND;
 - THAT ARE OBSTRUCTED BY ANY PHYSICAL IMPROVEMENT THAT PREVENTS THE SETTING OF THE ABOVE MENTIONED MONUMENTS, IN WHICH CASE, ONE OF THOSE MONUMENTS WILL BE SET ON THE PROLONGATION OF THE SIDE LOT LINE, 1.0 FOOT FROM THE TRUE LOT CORNER.
- 8" SPIKE AND WASHER STAMPED "RCE 21687" TO BE SET AT ALL STREET CENTERLINE POINTS OF CONTROL, UNLESS OTHERWISE NOTED.
- ALL MONUMENTS WILL BE SET WITHIN 90 DAYS AFTER THE ACCEPTANCE OF IMPROVEMENTS.
- ALL TRACT BOUNDARY DATA IS MEASURED AND RECORD PER TRACT NO. 16271, MM 839/34-45, UNLESS OTHERWISE NOTED.

SIGNATURE OMISSIONS

PURSUANT TO THE PROVISIONS OF SECTION 66436 (a) (3) (A) (C) OF THE SUBDIVISION MAP ACT, THE FOLLOWING SIGNATURES HAVE BEEN OMITTED:

LADERA DEVELOPMENT COMPANY, LLC, HOLDER OF OIL, GAS AND MINERAL RIGHTS RECORDED DECEMBER 10, 1996 AS INSTRUMENT NO. 19960624029 OF OFFICIAL RECORDS.

DMB LADERA, LLC, A DELAWARE LIMITED LIABILITY COMPANY, HOLDER OF EASEMENTS RESERVED IN THE DEED RECORDED APRIL 4, 2003 AS INSTRUMENT NO. 2003000372399 OF OFFICIAL RECORDS.

EASEMENT NOTES

- AN EASEMENT FOR EMERGENCY AND PUBLIC SERVICE VEHICULAR INGRESS-EGRESS DEDICATED TO THE COUNTY OF ORANGE.
- AN EASEMENT FOR SEWER, WATER PIPELINE AND ACCESS PURPOSES DEDICATED TO THE SANTA MARGARITA WATER DISTRICT.

LOT TABULATION

LOT A	PRIVATE STREET	0.627 ACRES	LOT L	OPEN SPACE	0.101 ACRES
LOT B	PRIVATE DRIVE	0.301 ACRES	LOT M	OPEN SPACE	0.272 ACRES
LOT C	PRIVATE STREET	0.105 ACRES	LOT N	OPEN SPACE	0.016 ACRES
LOT D	PRIVATE DRIVE	0.344 ACRES			
LOT E	PRIVATE DRIVE	0.260 ACRES			
LOT F	PRIVATE DRIVE	0.175 ACRES			
LOT G	PRIVATE DRIVE	0.142 ACRES			
LOT H	PRIVATE DRIVE	0.152 ACRES			
LOT I	OPEN SPACE	0.021 ACRES			
LOT J	OPEN SPACE	0.283 ACRES			
LOT K	OPEN SPACE	0.154 ACRES			

NOTES


- LETTERED LOTS ARE NOT SEPARATE BUILDING SITES.
- LOTS SHOWN AS "OPEN SPACE" ARE FOR LANDSCAPE PURPOSES AND WILL BE MAINTAINED BY THE HOMEOWNER'S ASSOCIATION.

ⓧ SHEET NUMBER

ADDITIONAL INFORMATION

PURSUANT TO THE PROVISIONS OF SECTION 66434.2 OF THE SUBDIVISION MAP ACT, THE FOLLOWING IS PROVIDED FOR INFORMATIONAL PURPOSES ONLY, AND IS NOT INTENDED TO AFFECT RECORD TITLE INTEREST:

- THIS MAP IS NOT WITHIN OR ADJOINING A SPECIAL FIRE PROTECTION AREA.
- THE PRIVATE STREETS CONSTRUCTED WITHIN THIS MAP SHALL BE OWNED, OPERATED AND MAINTAINED BY THE DEVELOPER, SUCCESSORS OR ASSIGNS. THE COUNTY OF ORANGE SHALL HAVE NO RESPONSIBILITY THEREFORE UNLESS PURSUANT TO APPROPRIATE SECTIONS OF THE STREETS AND HIGHWAYS CODE OF THE STATE OF CALIFORNIA, THE SAID PRIVATE STREETS HAVE BEEN ACCEPTED INTO THE COUNTY ROAD SYSTEM BY APPROPRIATE RESOLUTION OF THE ORANGE COUNTY BOARD OF SUPERVISORS.

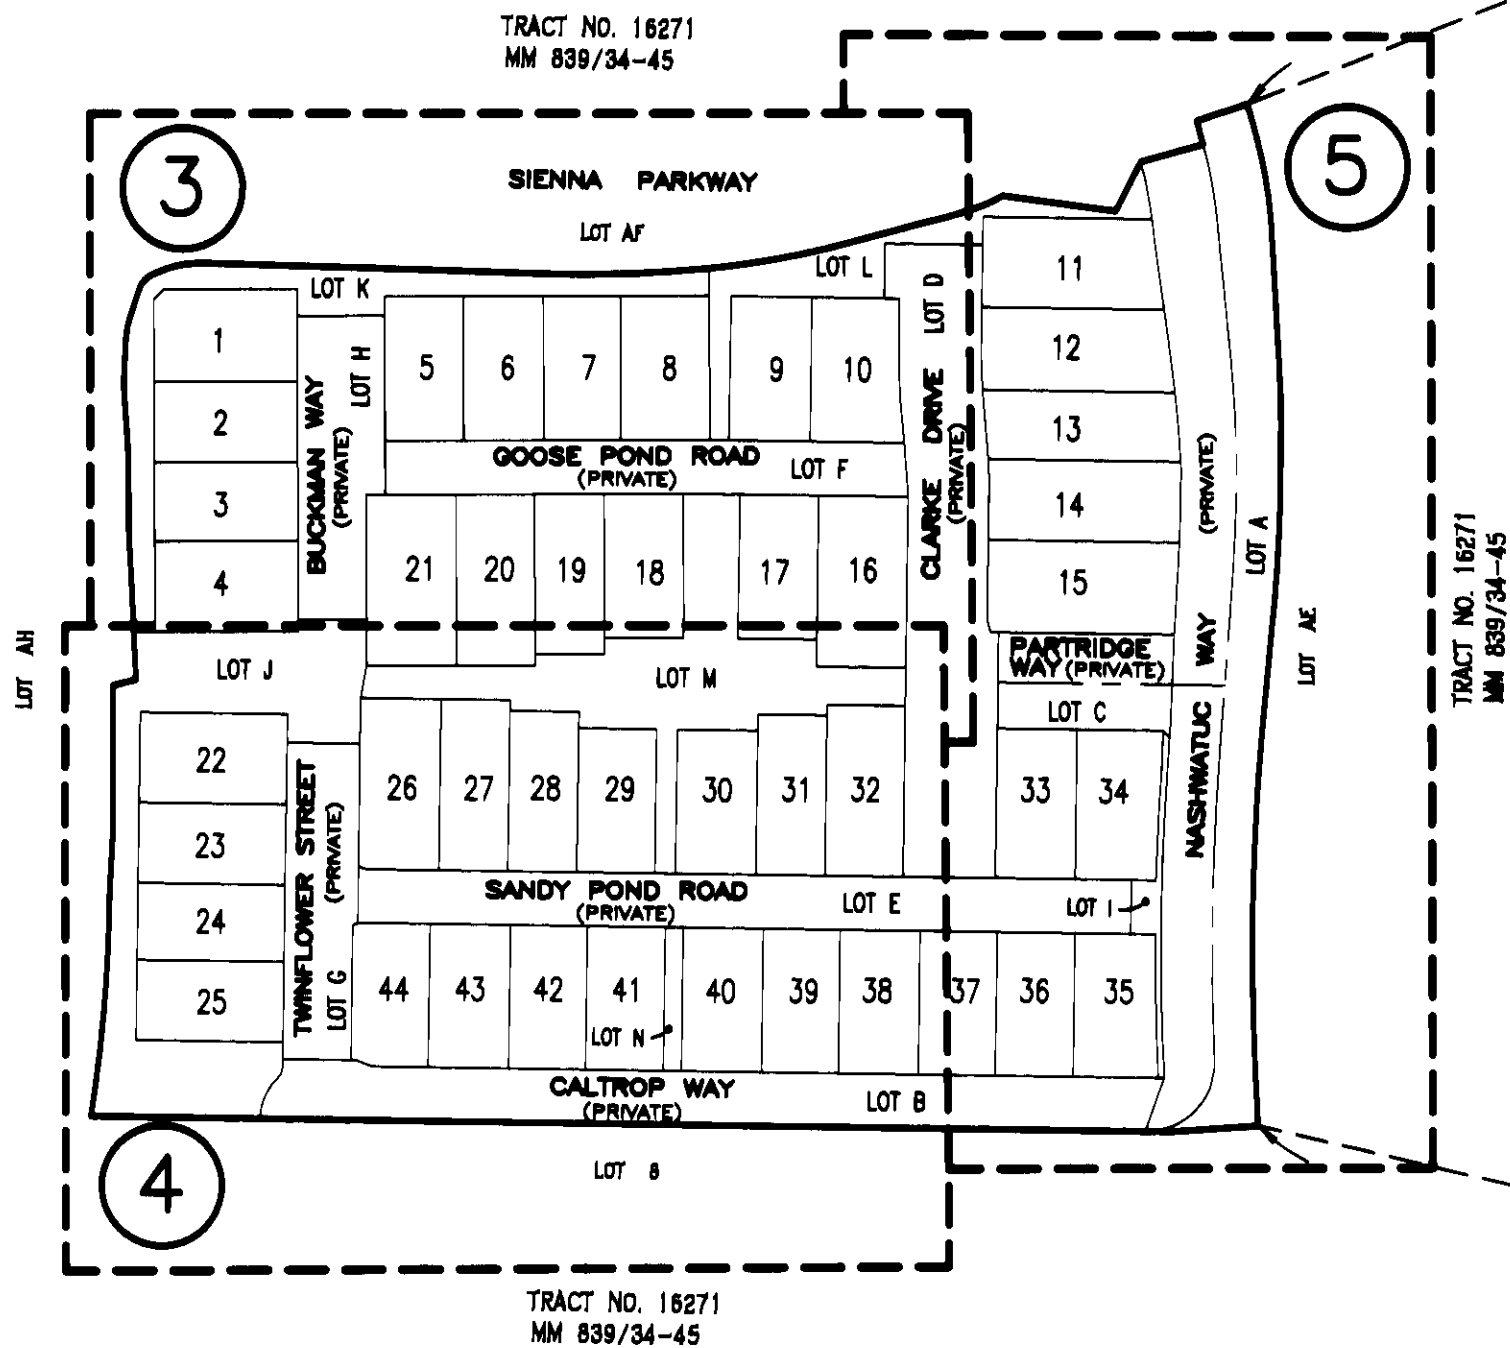

N51°25'13"E 6272.09' (TIE)

GPS NO. 1448
N 2146790.819
E 6142602.585
FD. 2" IRON PIPE
W/1 3/4" OCS BRASS CAP
STAMPED "1448 9-95"
PER RECORDS ON FILE
IN THE ORANGE COUNTY
SURVEYORS OFFICE

BASIS OF BEARINGS

N10°48'13"E 5436.90' (5436.62' GRID)


SCALE: 1" = 100'

N76°44'50"W 3929.22' (TIE)


GPS NO. 1417
N 2141450.558
E 6141583.535
FD. 2 1/2" IRON PIPE
W/2" OCS BRASS CAP
STAMPED "GPS 1417 9-95"
PER TRACT NO. 16271,
MM 839/34-45

SHEET 3 OF 5 SHEETS
ALL OF VESTING TENTATIVE TRACT
MAP NO. 16353
TOTAL LOTS: NUMBERED LOTS 1 THROUGH 44
AND LETTERED LOTS A THROUGH N
TOTAL ACRES: 6.367 ACRES

TRACT NO. 16353
IN THE UNINCORPORATED TERRITORY OF THE COUNTY OF ORANGE,
STATE OF CALIFORNIA
ADAMS - STREETER CIVIL ENGINEERS, INC. JAN A ADAMS, R.C.E. 21667
DATE OF SURVEY: APRIL, 2003

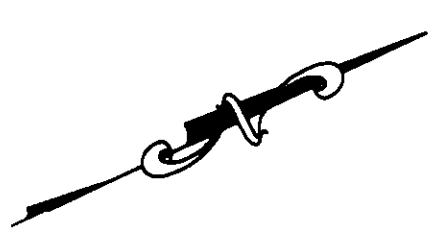

SCALE: 1" = 30'

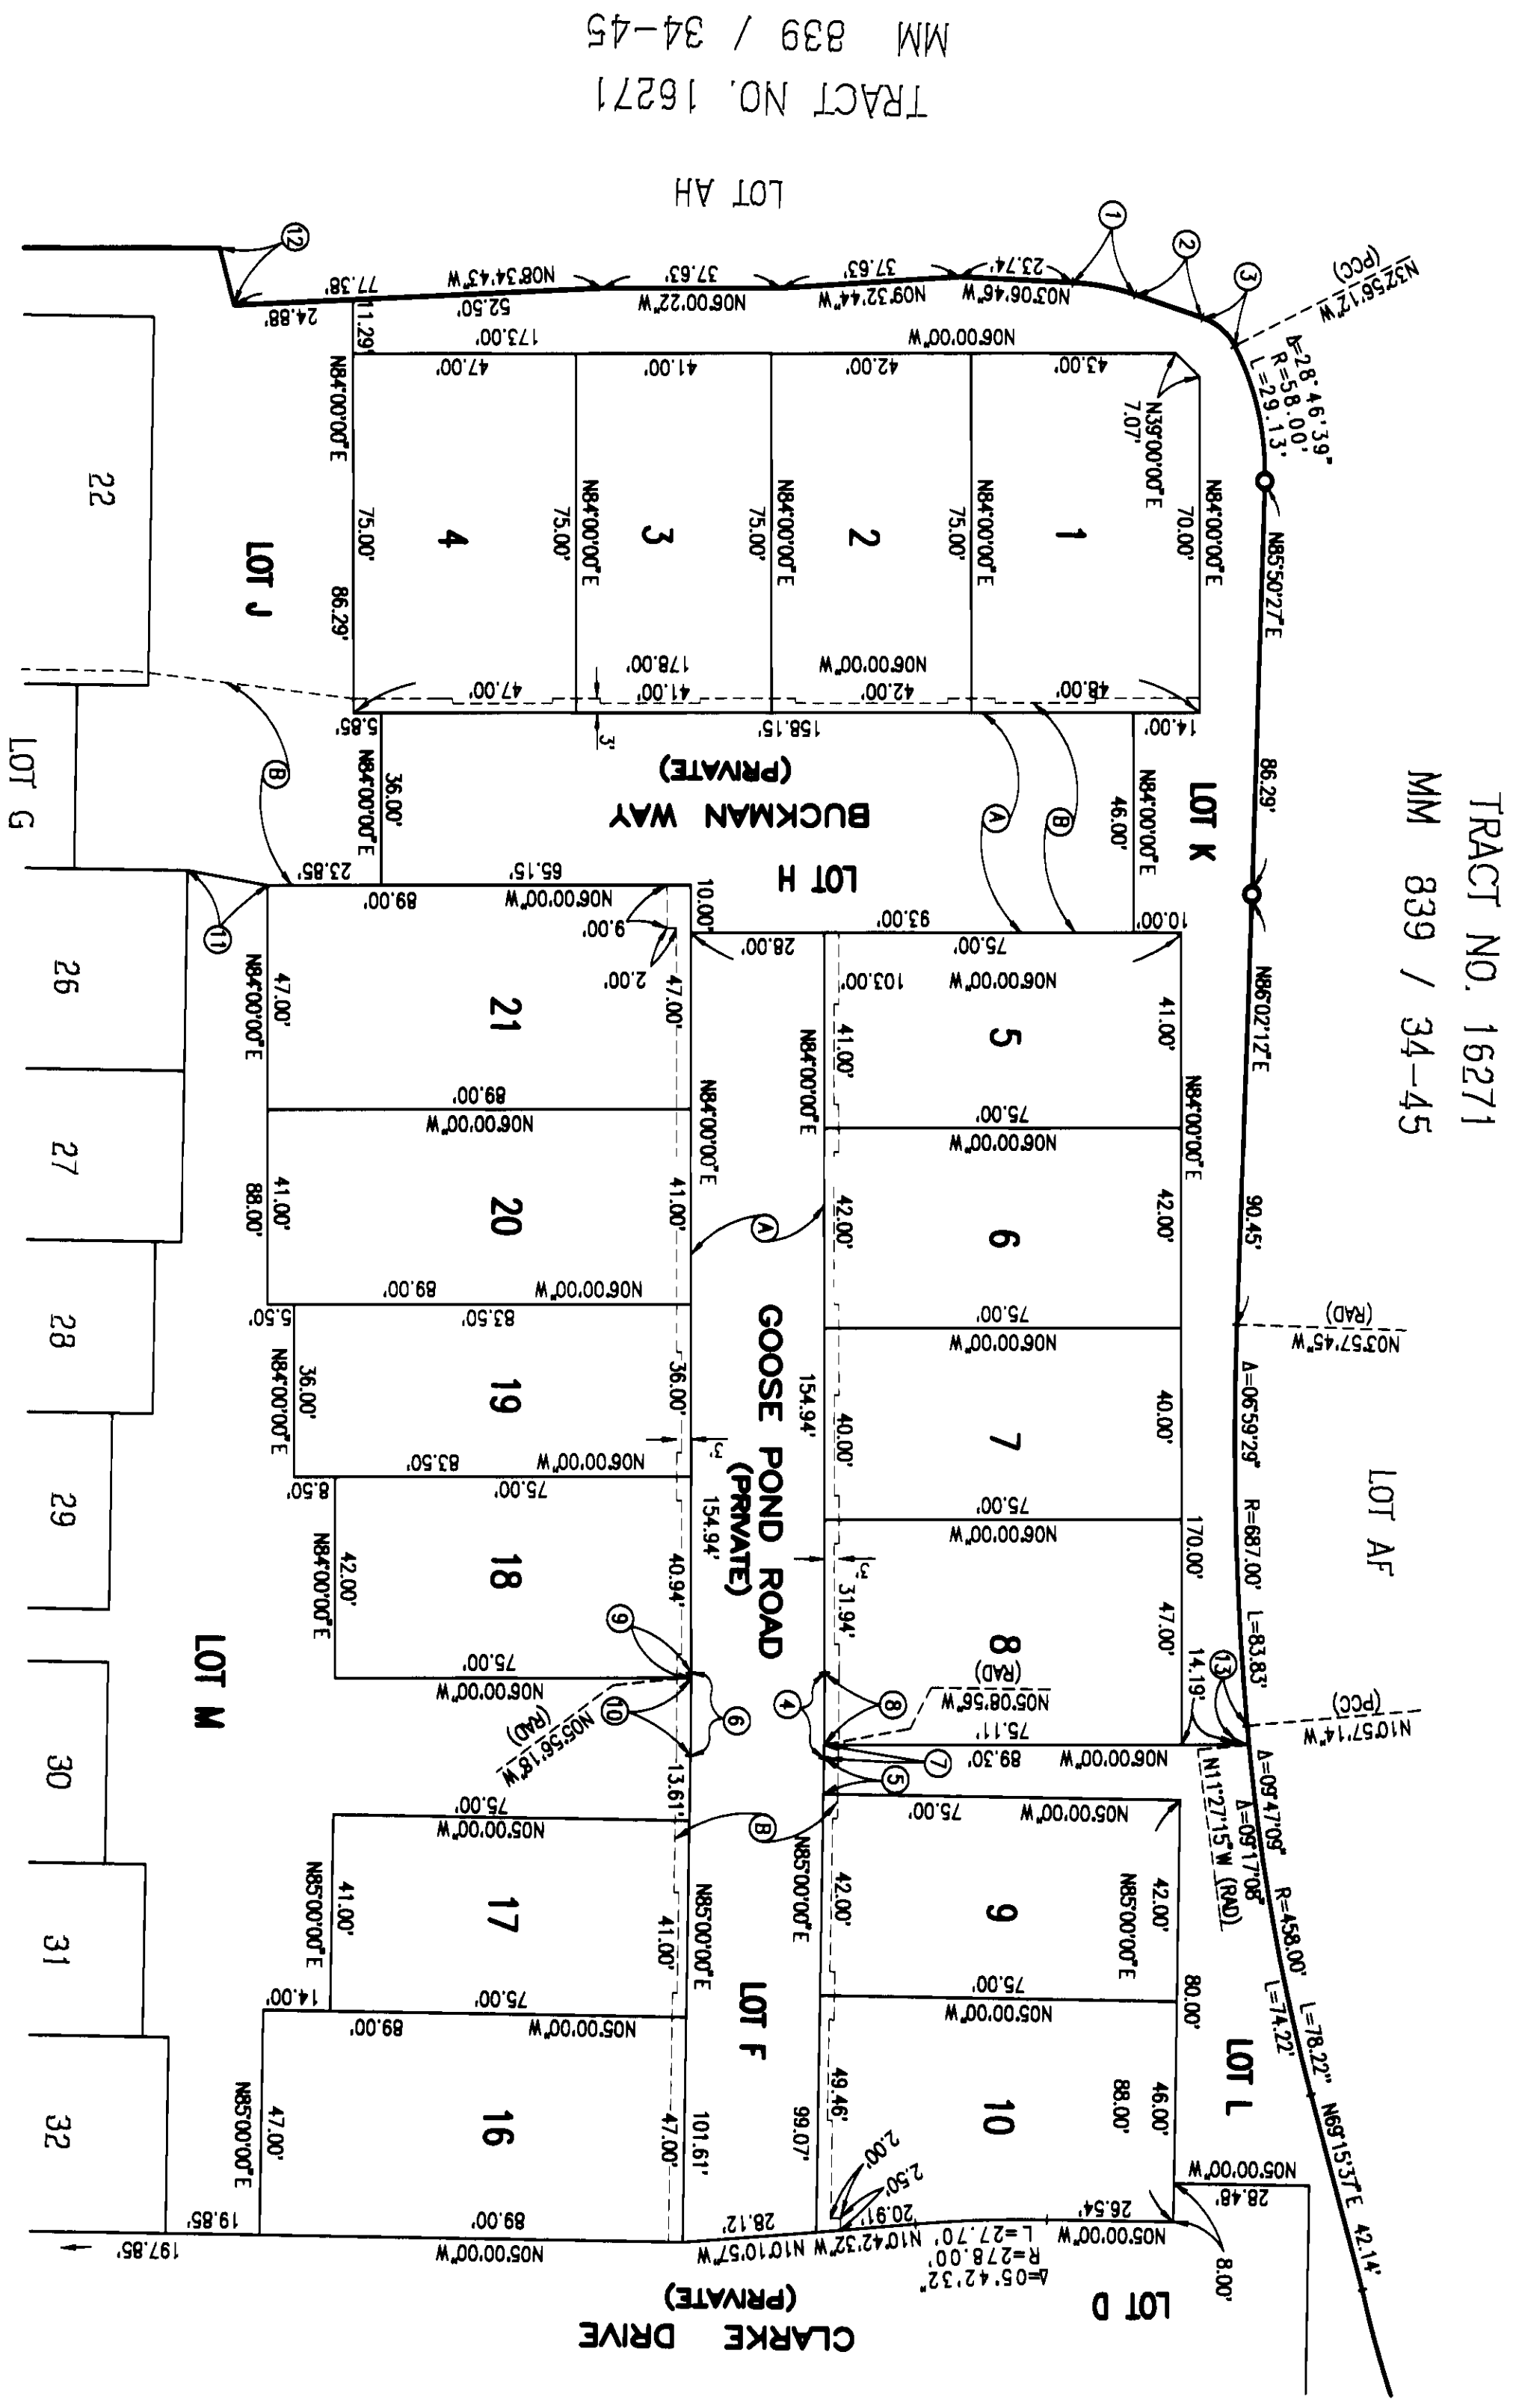

TRACT NO. 16271
MM 839 / 34-45

CURVE AND LINE DATA

- ① A=1539.26' R=48.00' L=13.40'
- ② N1252.40'E 14.95'
- ③ A=4411.08' R=12.00' L=9.25'
- ④ A=0100.00' R=1014.00' L=17.70'
- ⑤ N8500.00'E 7.61'
- ⑥ A=0100.00' R=986.00' L=17.21'
- ⑦ A=0008.56' R=1014.00' L=2.63'
- ⑧ A=0051.04' R=1014.00' L=15.06'
- ⑨ A=0003.42' R=986.00' L=1.06'
- ⑩ A=0056.18' R=986.00' L=16.15'
- ⑪ N0431.18'E 17.07'
- ⑫ N6954.41'E 12.32'
- ⑬ A=0013.01' R=458.00' L=4.00'


NOTE:

SEE SHEET 2 FOR BOUNDARY CONTROL, SHEET INDEX, BASIS OF BEARINGS,
DATUM STATEMENT, MONUMENT NOTES, EASEMENT NOTES AND LOT TABULATION.


SEE SHEET 4

SHEET 4 OF 5 SHEETS
ALL OF VESTING TENTATIVE TRACT
MAP NO. 16353
TOTAL LOTS: NUMBERED LOTS 1 THROUGH 44
AND LETTERED LOTS A THROUGH N
TOTAL ACREAGE: 6.367 ACRES

TRACT NO. 16353
IN THE UNINCORPORATED TERRITORY OF THE COUNTY OF ORANGE,
STATE OF CALIFORNIA
ADAMS - STREETER CIVIL ENGINEERS, INC. JAN A ADAMS, R.C.E. 21687
DATE OF SURVEY: APRIL, 2003

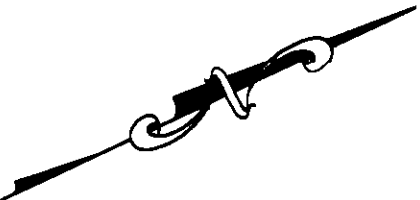

SCALE: 1" = 30'

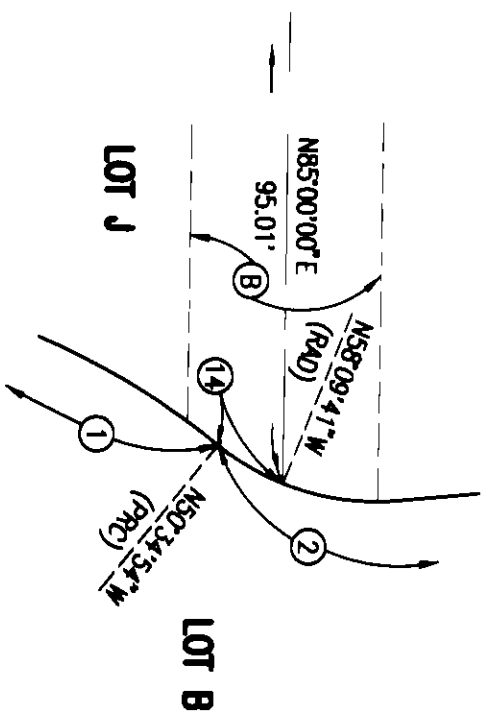


DETAIL
NOT TO SCALE

CURVE AND LINE DATA

- ① A=4°4'25.06" R=30.00' L=23.26"
- ② A=4°4'25.06" R=10.00' L=7.75'
- ③ N05°00'00"W 3.27'
- ④ N04°21'30"W 15.00'
- ⑤ N69°54'41"E 12.32'
- ⑥ N04°31'16"E 17.07'
- ⑦ A=3°07'00"00" R=10.00' L=5.24"
- ⑧ A=1°4'28.39" R=10.00' L=2.53"
- ⑨ A=1°5'31.21" R=10.00' L=2.71"
- ⑩ A=3°07'00"00" R=10.00' L=5.24"
- ⑪ N85°00'00"E 2.50'
- ⑫ N7°14'52"W 9.23'
- ⑬ A=0°1'38.55" R=771.00' L=22.18"
- ⑭ A=0°34'47" R=10.00' L=1.32'

NOTE:

SEE SHEET 2 FOR BOUNDARY CONTROL, SHEET INDEX, BASIS OF BEARINGS,
DATUM STATEMENT, MONUMENT NOTES, EASEMENT NOTES AND LOT TABULATION.

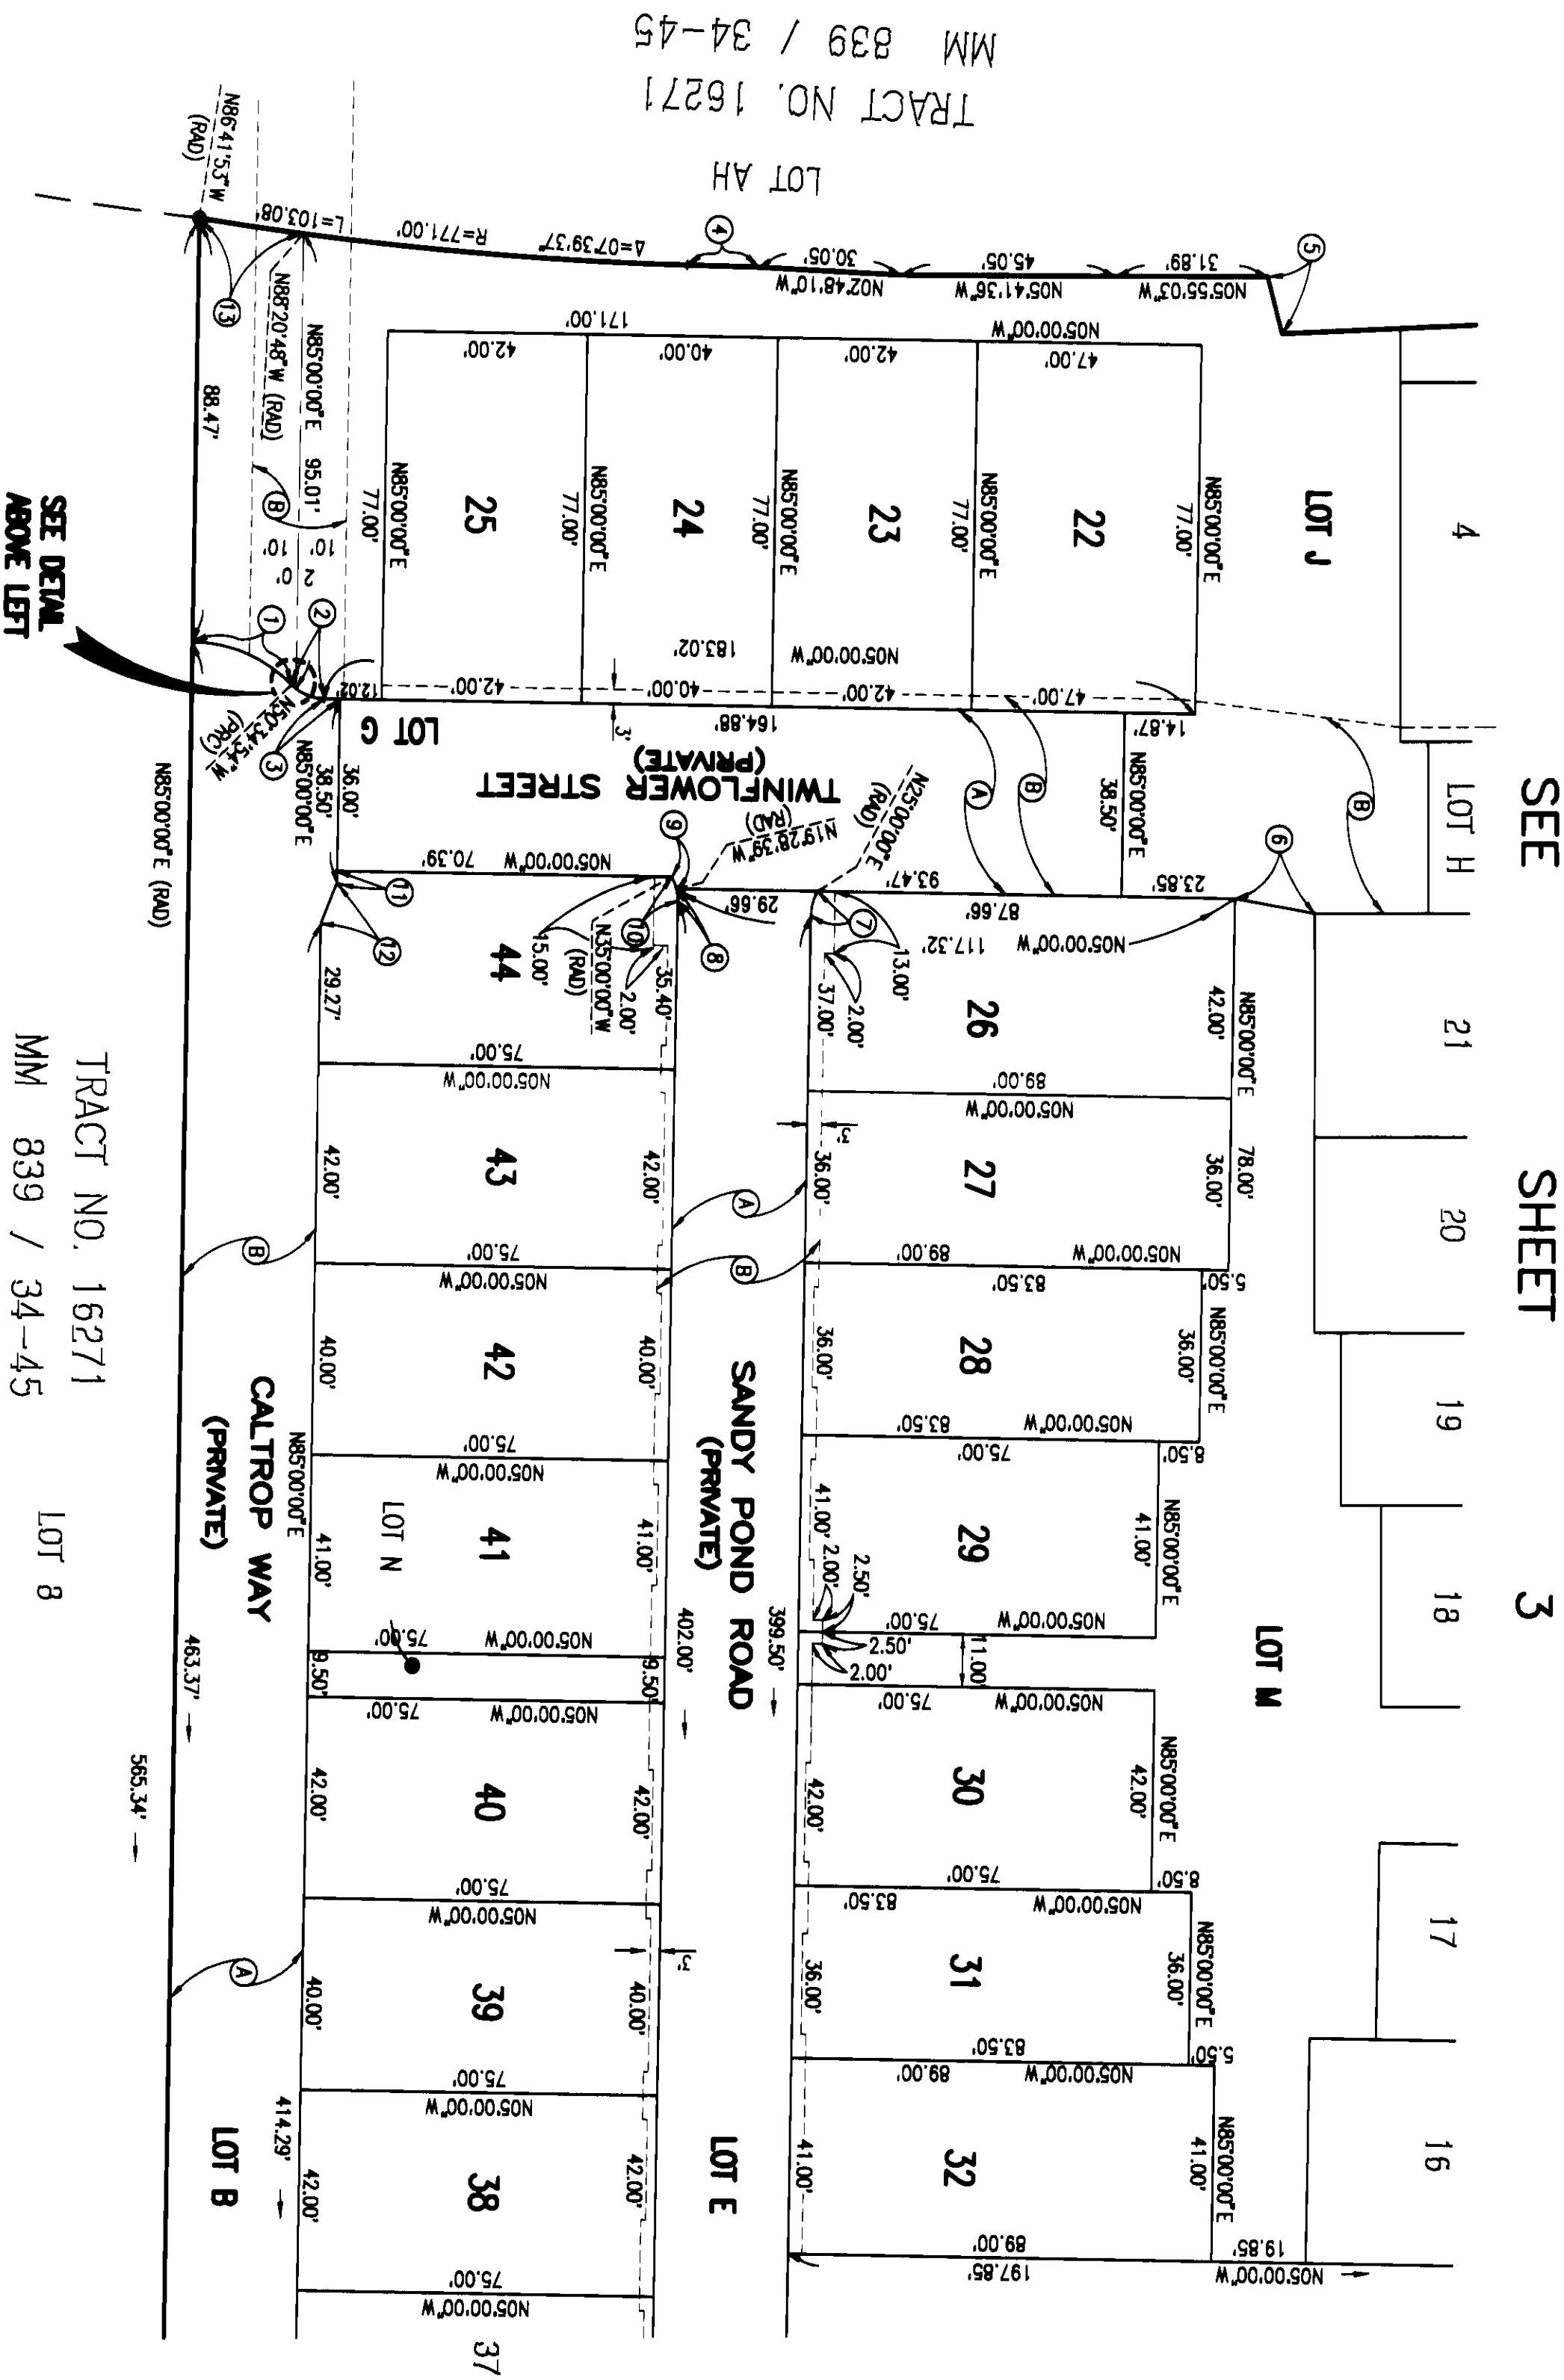

TRACT NO. 16271
MM 839 / 34-45
LOT 8

SEE SHEET

ALL OF VESTING TENTATIVE TRACT
MAP NO. 16353
TOTAL LOTS: NUMBERED LOTS 1 THROUGH 44
AND LETTERED LOTS A THROUGH N
TOTAL ACREAGE: 6.367 ACRES

TRACT NO. 16353


IN THE UNINCORPORATED TERRITORY OF THE COUNTY OF ORANGE,
STATE OF CALIFORNIA
ADAMS - STREETER CIVIL ENGINEERS, INC. JAN A. ADAMS, R.C.E. 21687
DATE OF SURVEY: APRIL, 2003

SCALE: 1" = 30'



TRACT NO. 16271
MM 839 / 34-45

DETAIL A
NOT TO SCALE

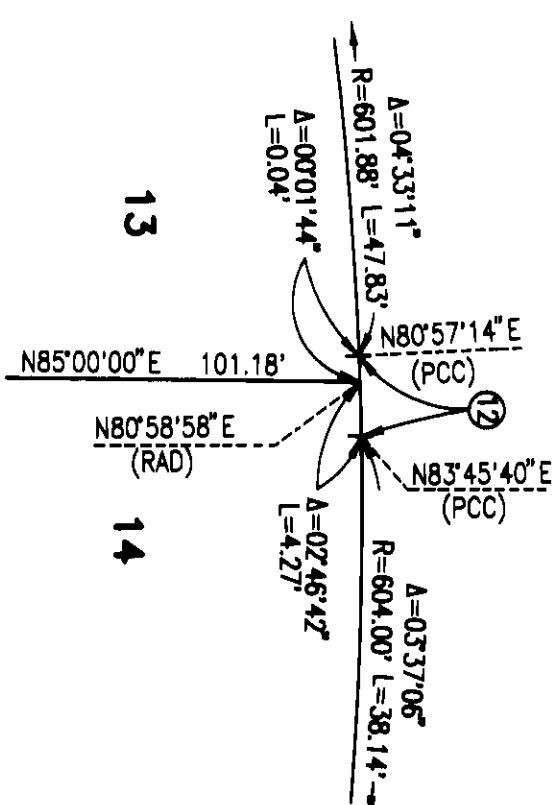

CURVE AND LINE DATA

- ① - N57°44'12"E 10.75'
- ② - A=05°42'32" R=235.00' L=23.42'
- ③ - A=04°57'30" R=235.00' L=20.34'
- ④ - A=07°45'02" R=235.00' L=3.08'
- ⑤ - A=01°40'47" R=265.00' L=7.77'
- ⑥ - A=04°01'45" R=265.00' L=18.63'
- ⑦ - A=05°42'32" R=265.00' L=26.40'
- ⑧ - A=23°34'41" R=20.00' L=8.23'
- ⑨ - N85°00'00"E 4.33'
- ⑩ - A=23°34'41" R=10.00' L=4.12'
- ⑪ - A=07°02'16" R=604.00' L=0.40'
- ⑫ - A=07°48'26" R=88.00' L=4.31'
- ⑬ - A=07°02'28" R=112.00' L=3.99'
- ⑭ - A=07°55'46" R=250.00' L=12.78'
- ⑮ - A=07°48'38" R=106.00' L=5.20'
- ⑯ - A=01°55'40" R=94.00' L=3.16'
- ⑰ - A=01°21'51" R=216.00' L=5.14'
- ⑱ - A=08°04'53" R=216.00' L=30.47'
- ⑲ - A=01°06'44" R=601.88' L=11.68'

SEE

SHEET

3

SEE

SHEET

4

