

SHEET 1 OF 4 SHEETS
43 NUMBERED LOTS AND
LOTS A THROUGH F, INCLUSIVE
ACREAGE: 10.286 ACRES
(ALL OF TENTATIVE
TRACT NO. 16354)

TRACT NO. 16354

IN UNINCORPORATED TERRITORY OF THE COUNTY OF ORANGE,
STATE OF CALIFORNIA

BEING A SUBDIVISION OF LOT 10 OF TRACT NO. 16271, AS PER MAP FILED IN
BOOK 839, PAGES 34 THROUGH 45, INCLUSIVE, OF MISCELLANEOUS MAPS,
IN THE OFFICE OF THE COUNTY RECORDER OF SAID COUNTY.

HUNSAKER AND ASSOCIATES IRVINE, INC.
RORY S. WILLIAMS, L.S. 6654

DATE OF SURVEY: JANUARY, 2003

ACCEPTED AND FILED AT THE
REQUEST OF

FIRST AMERICAN TITLE INS

DATE: AUGUST 18, 2003

TIME: 09:28 AM FEE: \$ 13.00

INSTRUMENT NO. 2003000993830

BOOK 848 PAGE 19-22 N/A

TOM DALY
COUNTY CLERK - RECORDER

BY  DEPUTY

OWNERSHIP CERTIFICATE:


WE, THE UNDERSIGNED, BEING ALL PARTIES HAVING ANY RECORD TITLE INTEREST IN THE LAND COVERED BY THIS MAP, DO HEREBY CONSENT TO THE PREPARATION AND RECORDATION OF SAID MAP, AS SHOWN WITHIN THE DISTINCTIVE BORDER LINE.

WE HEREBY DEDICATE TO THE PUBLIC FOR STREET PURPOSES: COPIOUS LANE, EPONA WAY, GALORA LANE AND ILLUMINATA LANE.

WE ALSO HEREBY DEDICATE TO THE COUNTY OF ORANGE: THE EASEMENTS FOR STORM DRAIN PURPOSES, AS SHOWN ON THIS MAP.

WE ALSO HEREBY DEDICATE TO THE SANTA MARGARITA WATER DISTRICT THE EASEMENTS FOR SEWER, WATER AND ACCESS PURPOSES, AS SHOWN ON THIS TRACT MAP, WHICH EASEMENTS SHALL BE SUBJECT TO THE SAME TERMS AND CONDITIONS AS SHOWN IN THAT CERTAIN EASEMENT RECORDED OCTOBER 6, 1980, IN BOOK 13776, PAGE 341 OF OFFICIAL RECORDS.

SHEA HOMES LIMITED PARTNERSHIP, A CALIFORNIA LIMITED PARTNERSHIP, OWNER.

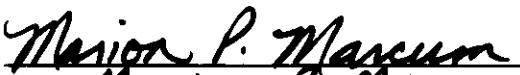BY:  NAME: MARION P. MARCUM
TITLE: ASSISTANT SECRETARY
BY:  NAME: LINDA C. TONG
TITLE: ASSISTANT SECRETARY

DMB LADERA, LLC, A DELAWARE LIMITED LIABILITY COMPANY, BENEFICIARY UNDER DEED OF TRUST RECORDED MARCH 28, 2003, AS INSTRUMENT NO. 2003000344006 OF OFFICIAL RECORDS, AND HOLDER OF EASEMENTS RESERVED IN THE DEED RECORDED MARCH 28, 2003, AS INSTRUMENT NO. 2003000344005 OF OFFICIAL RECORDS.

BY: RANCHO MISSION VIEJO, L.L.C., A DELAWARE LIMITED LIABILITY COMPANY, ITS AUTHORIZED AGENT AND MANAGER.

BY:  NAME: DONALD T. STEHLE
TITLE: DIRECTOR
BY:  NAME: PAUL JOHNSON
TITLE: V.P.-COMMUNITY DEVELOPMENT

NOTARY ACKNOWLEDGMENT:

STATE OF CALIFORNIA }
COUNTY OF ORANGE } SS

ON May 21, 2003, BEFORE ME, Beth A. Hutchinson, PERSONALLY APPEARED Marion P. Marcum AND Linda C. Tong PERSONALLY KNOWN TO ME (OR PROVED TO ME ON THE BASIS OF SATISFACTORY EVIDENCE) TO BE THE PERSON(S) WHOSE NAME(S) ARE SUBSCRIBED TO THE WITHIN INSTRUMENT AND ACKNOWLEDGED TO ME THAT ~~HE/SHE~~/THEY EXECUTED THE SAME IN ~~THEIR~~/THEIR AUTHORIZED CAPACITY(IES), AND THAT BY ~~THEIR~~/THEIR SIGNATURE(S) ON THE INSTRUMENT THE PERSON(S), OR ENTITY UPON BEHALF OF WHICH THE PERSON(S) ACTED, EXECUTED THE INSTRUMENT.

WITNESS MY HAND:

SIGNATURE  MY PRINCIPAL PLACE OF BUSINESS IS
NOTARY PUBLIC IN AND FOR SAID STATE IN Orange COUNTY.
Beth A. Hutchinson MY COMMISSION EXPIRES: 5-8-05
(NAME PRINTED)

STATE OF CALIFORNIA }
COUNTY OF ORANGE } SS

ON May 23, 2003 BEFORE ME, Tina T. Baker, Notary Public, PERSONALLY APPEARED Donald T. Stehle AND Paul Johnson PERSONALLY KNOWN TO ME (OR PROVED TO ME ON THE BASIS OF SATISFACTORY EVIDENCE) TO BE THE PERSON(S) WHOSE NAME(S) ARE SUBSCRIBED TO THE WITHIN INSTRUMENT AND ACKNOWLEDGED TO ME THAT ~~HE/SHE~~/THEY EXECUTED THE SAME IN ~~THEIR~~/THEIR AUTHORIZED CAPACITY(IES), AND THAT BY ~~THEIR~~/THEIR SIGNATURE(S) ON THE INSTRUMENT THE PERSON(S), OR ENTITY UPON BEHALF OF WHICH THE PERSON(S) ACTED, EXECUTED THE INSTRUMENT.

WITNESS MY HAND:

SIGNATURE  MY PRINCIPAL PLACE OF BUSINESS IS
NOTARY PUBLIC IN AND FOR SAID STATE IN Orange COUNTY.
TINA T. BAKER MY COMMISSION EXPIRES: 8-29-04
(NAME PRINTED)

AUTOMATIC FIRE SPRINKLER NOTE:

ALL COMMERCIAL STRUCTURES GREATER THAN 6,000 SQUARE FEET, ALL MULTIFAMILY RESIDENTIAL STRUCTURES, ALL SINGLE-FAMILY STRUCTURES EXCEEDING 5,500 SQUARE FEET, AND ALL STRUCTURES EXCEEDING FIRE DEPARTMENT ACCESS REQUIREMENTS SHALL BE PROTECTED BY AN AUTOMATIC FIRE SPRINKLER SYSTEM.

SPECIAL FIRE PROTECTION NOTE:

SUBJECT PROPERTY IS IN A SPECIAL FIRE PROTECTION AREA AND MUST MEET ALL REQUIREMENTS FOR DEVELOPMENT WITHIN THE AREA.

HIGH FIRE HAZARD AREA NOTE:

THE LOTS SHOWN ON THIS MAP ARE IN A HIGH FIRE HAZARD AREA DUE TO WILDLAND EXPOSURE.

SURVEYOR'S STATEMENT:

THIS MAP WAS PREPARED BY ME OR UNDER MY DIRECTION AND IS BASED UPON A FIELD SURVEY IN CONFORMANCE WITH THE REQUIREMENTS OF THE SUBDIVISION MAP ACT AND LOCAL ORDINANCE AT THE REQUEST OF DMB LADERA, L.L.C., IN JANUARY, 2003. I HEREBY STATE THAT ALL MONUMENTS ARE OF THE CHARACTER AND OCCUPY THE POSITIONS INDICATED, OR THAT THEY WILL BE SET IN SUCH POSITIONS; AND THAT SAID MONUMENTS ARE SUFFICIENT TO ENABLE THE SURVEY TO BE RETRACED. I HEREBY STATE THAT THIS FINAL MAP SUBSTANTIALLY CONFORMS TO THE CONDITIONALLY APPROVED TENTATIVE MAP.

 5/16/03
RORY S. WILLIAMS, L.S. 6654 DATE
LICENSE EXPIRES: 12/31/03




COUNTY SURVEYOR'S STATEMENT

I HEREBY STATE THAT I HAVE EXAMINED THIS MAP AND HAVE FOUND IT TO BE SUBSTANTIALLY IN CONFORMANCE WITH THE TENTATIVE MAP AS FILED WITH, AMENDED AND APPROVED BY THE ORANGE COUNTY SUBDIVISION COMMITTEE; THAT ALL PROVISIONS OF THE SUBDIVISION MAP ACT AND COUNTY SUBDIVISION REGULATIONS HAVE BEEN COMPLIED WITH AND I AM SATISFIED SAID MAP IS TECHNICALLY CORRECT.

DATED THIS 24TH DAY OF JULY, 2003.


JOHN CANAS, COUNTY SURVEYOR
LS 4408, EXPIRATION DATE: 9-30-05

BY: MICHAEL K. SULLIVAN, DEPUTY
LS 8254 EXPIRES 6/30/06

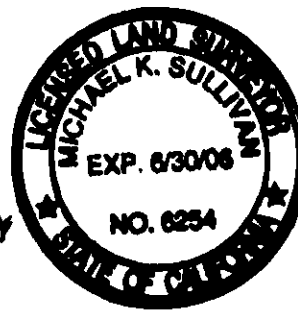


COUNTY TREASURER-TAX COLLECTOR'S CERTIFICATE:

STATE OF CALIFORNIA }
COUNTY OF ORANGE } SS

I HEREBY CERTIFY THAT ACCORDING TO THE RECORDS OF MY OFFICE THERE ARE NO LIENS AGAINST THE LAND COVERED BY THIS MAP OR ANY PART THEREOF FOR UNPAID STATE, COUNTY, MUNICIPAL OR LOCAL TAXES OR SPECIAL ASSESSMENTS COLLECTED AS TAXES, EXCEPT TAXES OR SPECIAL ASSESSMENTS COLLECTED AS TAXES NOT YET PAYABLE.

AND DO CERTIFY TO THE RECORDER OF ORANGE COUNTY THAT THE PROVISIONS OF THE SUBDIVISION MAP ACT HAVE BEEN COMPLIED WITH REGARDING DEPOSITS TO SECURE PAYMENT OF TAXES OR SPECIAL ASSESSMENTS COLLECTED AS TAXES ON THE LAND COVERED BY THIS MAP.

DATED THIS 26th DAY OF June, 2003.

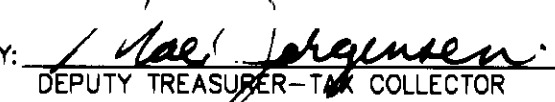JOHN M.W. MOORLACH COUNTY TREASURER-TAX COLLECTOR BY:  DEPUTY TREASURER-TAX COLLECTOR

CLERK OF THE BOARD OF SUPERVISORS' CERTIFICATE:

STATE OF CALIFORNIA }
COUNTY OF ORANGE } SS

I HEREBY CERTIFY THAT THIS MAP WAS PRESENTED FOR APPROVAL TO THE BOARD OF SUPERVISORS OF THE COUNTY OF ORANGE AT REGULAR MEETING THEREOF HELD ON THE 12th DAY OF August, 2003, AND THAT THEREUPON SAID BOARD DID, BY AN ORDER DULY PASSED AND ENTERED, APPROVE SAID MAP.

AND DID ACCEPT ON BEHALF OF THE PUBLIC, SUBJECT TO IMPROVEMENTS, THE DEDICATION FOR STREET PURPOSES OF: COPIOUS LANE, EPONA WAY, GALORA LANE AND ILLUMINATA LANE.

AND DID ALSO ACCEPT, ON BEHALF OF THE COUNTY OF ORANGE: THE EASEMENTS FOR STORM DRAIN PURPOSES, AS DEDICATED.

DATED THIS 12th DAY OF August, 2003.


CLERK OF THE BOARD OF SUPERVISORS
DARLENE J. BLOOM



CERTIFICATE OF ACCEPTANCE - SANTA MARGARITA WATER DISTRICT

THE UNDERSIGNED, BEING THE DULY APPOINTED AGENT OF THE SANTA MARGARITA WATER DISTRICT, A PUBLIC CORPORATION IN ORANGE COUNTY, CALIFORNIA, PURSUANT TO ITS RESOLUTION NO. 88-10-2, DOES HEREBY ACCEPT ON BEHALF OF SAID DISTRICT, THE EASEMENTS FOR SEWER, WATER AND ACCESS PURPOSES AS DEDICATED AND SHOWN ON THIS TRACT MAP, BY AND BETWEEN THE SANTA MARGARITA WATER DISTRICT AND DMB LADERA, L.L.C., A DELAWARE LIMITED LIABILITY COMPANY, AND DOES HEREBY CERTIFY THAT THE GRANTEE CONSENTS TO THE RECORDATION OF SAID TRACT MAP.


DANIEL R. FERONS, CHIEF ENGINEER
SANTA MARGARITA WATER DISTRICT

NOTARY ACKNOWLEDGMENT - SANTA MARGARITA WATER DISTRICT

STATE OF CALIFORNIA }
COUNTY OF ORANGE } SS

ON June 20, 2003, BEFORE ME, ANDREA M. EVANS, Notary Public, PERSONALLY APPEARED DANIEL R. FERONS, PERSONALLY KNOWN TO ME (OR PROVED TO ME ON THE BASIS OF SATISFACTORY EVIDENCE) TO BE THE PERSON WHOSE NAME IS SUBSCRIBED TO THE WITHIN INSTRUMENT AND ACKNOWLEDGED TO ME THAT HE EXECUTED THE SAME IN HIS AUTHORIZED CAPACITY, AND THAT BY HIS SIGNATURE ON THE INSTRUMENT THE PERSON, OR ENTITY UPON BEHALF OF WHICH THE PERSON ACTED, EXECUTED THE INSTRUMENT.

WITNESS MY HAND:

SIGNATURE  MY PRINCIPAL PLACE OF BUSINESS IS
NOTARY PUBLIC IN AND FOR SAID STATE IN Orange COUNTY.
ANDREA M. EVANS MY COMMISSION EXPIRES: April 8, 2004
(NAME PRINTED)

SIGNATURE OMISSION:

PURSUANT TO THE PROVISIONS OF SECTION 66436 (a)(3)(C) OF THE SUBDIVISION MAP ACT, THE FOLLOWING SIGNATURE HAS BEEN OMITTED:

LADERA DEVELOPMENT COMPANY, L.L.C., HOLDER OF OIL, GAS AND MINERAL RIGHTS RECORDED DECEMBER 10, 1996, AS INSTRUMENT NO. 19960624029 OF OFFICIAL RECORDS.

DMB LADERA, LLC, A DELAWARE LIMITED LIABILITY COMPANY, HOLDER OF EASEMENTS RESERVED IN THE DEED RECORDED MARCH 28, 2003, AS INSTRUMENT NO. 2003000344005 OF OFFICIAL RECORDS.

848

19

SHEET 2 OF 4 SHEETS
SCALE: 1" = 80'
43 NUMBERED LOTS AND
LOTS A THROUGH F, INCLUSIVE
ACREAGE: 10.285 ACRES
(ALL OF TENTATIVE
TRACT NO. 16354)

TRACT NO. 16354

IN UNINCORPORATED TERRITORY OF THE COUNTY OF ORANGE,
STATE OF CALIFORNIA

HUNSAKER AND ASSOCIATES IRVINE, INC.
RORY S. WILLIAMS, L.S. 6654
DATE OF SURVEY: JANUARY, 2003

BASIS OF BEARINGS:

THE BEARINGS SHOWN HEREON ARE BASED ON THE BEARING BETWEEN
O.C.S. HORIZONTAL CONTROL STATION GPS NO. 1417 AND STATION
GPS NO. 1448 BEING N10°48'13"E PER RECORDS ON FILE IN THE
OFFICE OF THE ORANGE COUNTY SURVEYOR.

DATUM STATEMENT:

COORDINATES SHOWN ARE BASED ON THE CALIFORNIA COORDINATE SYSTEM
(CCS83), ZONE VI, 1983 NAD, (1991.35 EPOCH OCS GPS ADJUSTMENT). ALL
DISTANCES SHOWN ARE GROUND, UNLESS OTHERWISE NOTED. TO OBTAIN GRID
DISTANCE MULTIPLY GROUND DISTANCE BY 0.999848285. THIS COMBINATION
FACTOR IS PROJECT SPECIFIC.

NOTE:

LOTS A THROUGH F, INCLUSIVE, ARE FOR OPEN SPACE/LANDSCAPE PURPOSES,
AND ARE NOT SEPARATE BUILDING SITES.

EASEMENT NOTES:

- (A) INDICATES AN EASEMENT FOR STORM DRAIN PURPOSES DEDICATED HEREON
TO THE COUNTY OF ORANGE.
- (B) INDICATES AN EASEMENT FOR SEWER, WATER AND ACCESS PURPOSES
DEDICATED HEREON TO THE SANTA MARGARITA WATER DISTRICT.

MONUMENT NOTES:

2" I.P. TAGGED L.S. 6654 OR LEAD, TACK & TAG L.S. 6654 OR NAIL & TAG L.S. 6654 OR 8" S&W STAMPED
L.S. 6654 TO BE SET AT ALL TRACT BOUNDARY CORNERS WITHIN 90 DAYS AFTER ACCEPTANCE OF
IMPROVEMENTS, UNLESS OTHERWISE NOTED.

1" I.P. TAGGED L.S. 6654 OR LEAD, TACK & TAG L.S. 6654 OR NAIL & TAG L.S. 6654 OR 8" S&W STAMPED
L.S. 6654 TO BE SET AT ALL LOT CORNERS, EXCEPT LOT CORNERS THAT ARE THE INTERSECTION OF SIDE LOT
LINES WITH STREET RIGHT OF WAY, WITHIN 90 DAYS AFTER ACCEPTANCE OF IMPROVEMENTS, UNLESS OTHERWISE
NOTED.

8" S&W STAMPED L.S. 6654 OR LEAD, TACK & TAG L.S. 6654 OR 1" I.P. TAGGED L.S. 6654 TO BE SET AT ALL
STREET CENTERLINE POINTS OF CONTROL, WITHIN 90 DAYS AFTER ACCEPTANCE OF IMPROVEMENTS, UNLESS
OTHERWISE NOTED.

LEAD, TACK & TAG L.S. 6654 TO BE SET IN TOP OF CURB AT AN OFFSET OF 0.25' ALONG FRONT SIDE LOT
LINES PRODUCED, IN LIEU OF AT FRONT LOT CORNERS, WITHIN 90 DAYS AFTER ACCEPTANCE OF IMPROVEMENTS,
UNLESS OTHERWISE NOTED. FOR ALL SIDE LOT LINES NON-RADIAL OR NON-PERPENDICULAR TO STREET RIGHT
OF WAY, OR NOT AT AN OFFSET OF 0.25' BEARING AND DISTANCE OF PRODUCTION IS AS NOTED HEREON.

● INDICATES LOCATION OF MONUMENT SET, AS NOTED.

■ INDICATES NOTHING TO BE SET.

▲ INDICATES FOUND ORANGE COUNTY SURVEYOR GPS CONTROL MONUMENT AS NOTED.

P# INDICATES BEARING AND DISTANCE OF LOT LINE PRODUCTION FROM LOT CORNER TO MONUMENT.

[1] INDICATES LOCATION OF 1" I.P. TAGGED "P.L.S. 5557" OR SPIKE & WASHER STAMPED "P.L.S. 5557" OR LEAD,
TACK & TAG "P.L.S. 5557" TO BE SET PER TRACT NO. 16271, M.M. 839/34-45.



[2] INDICATES LOCATION OF O.C.S. WELL MONUMENT WITH A 2" BRASS DISK STAMPED "P.L.S. 5557 OR LEAD, TACK
& TAG "P.L.S. 5557" TO BE SET PER TRACT NO. 16271, M.M. 839/34-45.

[3] INDICATES LOCATION OF 2" I.P. TAGGED "P.L.S. 5557" OR SPIKE & WASHER STAMPED "P.L.S. 5557" OR LEAD,
TACK & TAG "P.L.S. 5557" TO BE SET PER TRACT NO. 16271, M.M. 839/34-45.

[4] INDICATES SET 2" I.P. TAGGED L.S. 6654 PRIOR TO MAP RECORDATION.

SHEET INDEX AND GPS CONTROL MAP

3 INDICATES SHEET NUMBER

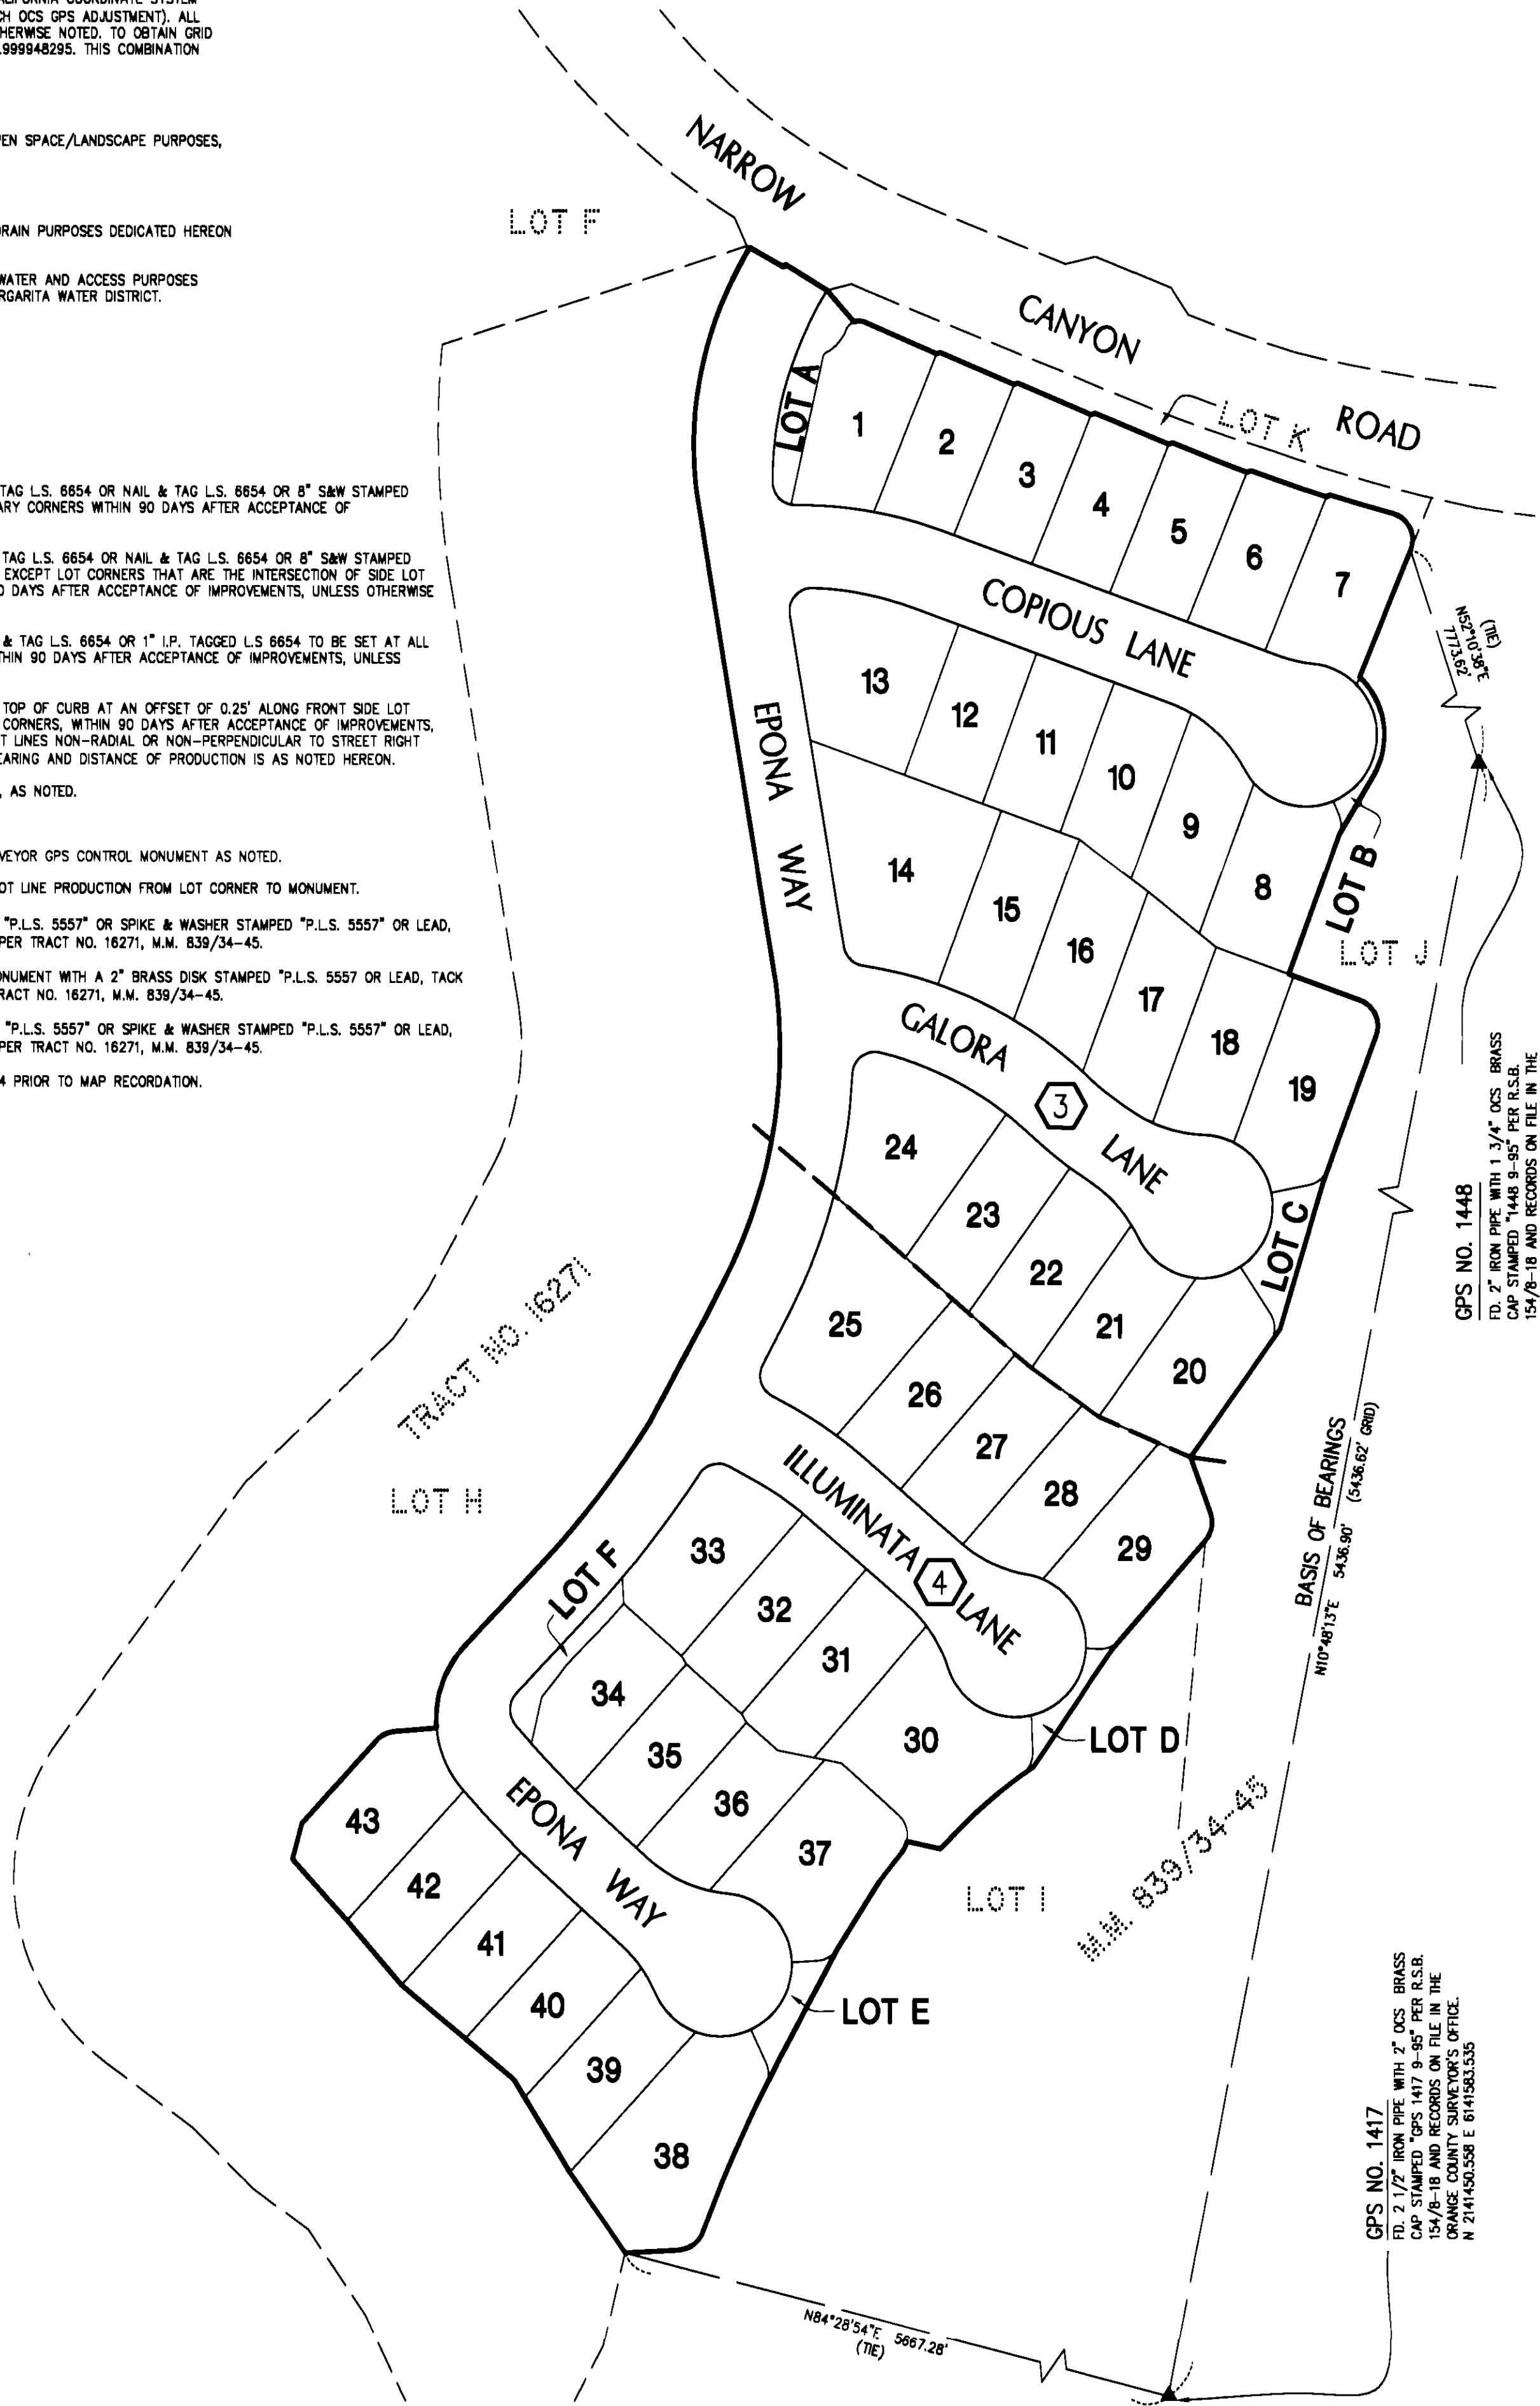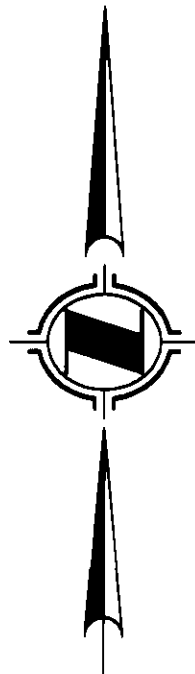

GPS NO. 1448
FD. 2" IRON PIPE WITH 1 3/4" OCS BRASS
CAP STAMPED "1448 9-95" PER R.S.B.
154/8-18 AND RECORDS ON FILE IN THE
ORANGE COUNTY SURVEYOR'S OFFICE
N 2146790.819 E 6142602.585

GPS NO. 1417
FD. 2 1/2" IRON PIPE WITH 2" OCS BRASS
CAP STAMPED "GPS 1417 9-95" PER R.S.B.
154/8-18 AND RECORDS ON FILE IN THE
ORANGE COUNTY SURVEYOR'S OFFICE
N 2141450.558 E 6141583.535

SHEET 3 OF 4 SHEETS
SCALE: 1" = 40'
43 NUMBERED LOTS AND
LOTS A THROUGH F, INCLUSIVE
ACREAGE: 10.285 ACRES
(ALL OF TENTATIVE
TRACT NO. 16354)

TRACT NO. 16354

IN UNINCORPORATED TERRITORY OF THE COUNTY OF ORANGE,
STATE OF CALIFORNIA

HUNSAKER AND ASSOCIATES IRVINE, INC.
RORY S. WILLIAMS, L.S. 6654

DATE OF SURVEY: JANUARY, 2003

SEE SHEET 2 FOR BASIS OF BEARINGS, DATUM STATEMENT,
MONUMENT NOTES, SHEET INDEX AND GPS CONTROL MAP,
EASEMENT NOTES AND NOTES.

MONUMENT OFFSET TABLE		
LINE	BEARING	LENGTH
P1	S12°18'14"W	8.11'
P2	S22°00'00"W	8.94'
P3	S22°00'00"W	8.76'
P4	S22°00'00"W	8.76'
P5	S22°00'00"W	8.76'
P6	S22°00'00"W	8.76'
P7	S22°00'00"W	8.76'
P8	N22°00'00"E	9.78'
P9	N20°00'00"E	10.20'
P10	N20°00'00"E	8.87'
P11	S20°00'00"W	8.75'
P12	S20°00'00"W	9.51'
P13	S20°00'00"W	9.51'
P14	S20°00'00"W	8.77'
P15	S20°00'00"W	8.82'
P16	S20°00'00"W	10.63'
P17	N35°18'46"E	9.43'
P18	N35°18'46"E	8.75'
P19	N35°18'46"E	8.76'
P20	N35°18'46"E	8.76'
P21	N35°18'46"E	8.76'

LOT F


NARROW CANYON

COPIOUS LANE

EPONA WAY

LOT B
0.015 AC.

LOT C
0.055 AC.

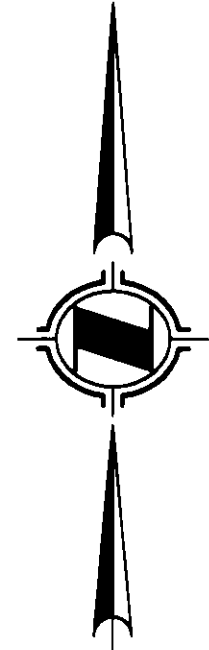


LINE TABLE		
LINE	BEARING	LENGTH
L3	N78°35'11"W	26.49'

CURVE TABLE			
CURVE	DELTA	RADIUS	LENGTH
C1	47°47'25"	9.00'	7.51'
C3	34°46'35"	47.00'	28.53'
C4	31°33'03"	47.00'	25.88'

SEE SHEET 4

TRACT NO. 16354
IN UNINCORPORATED TERRITORY OF THE COUNTY OF ORANGE,
STATE OF CALIFORNIA

SEE SHEET 4

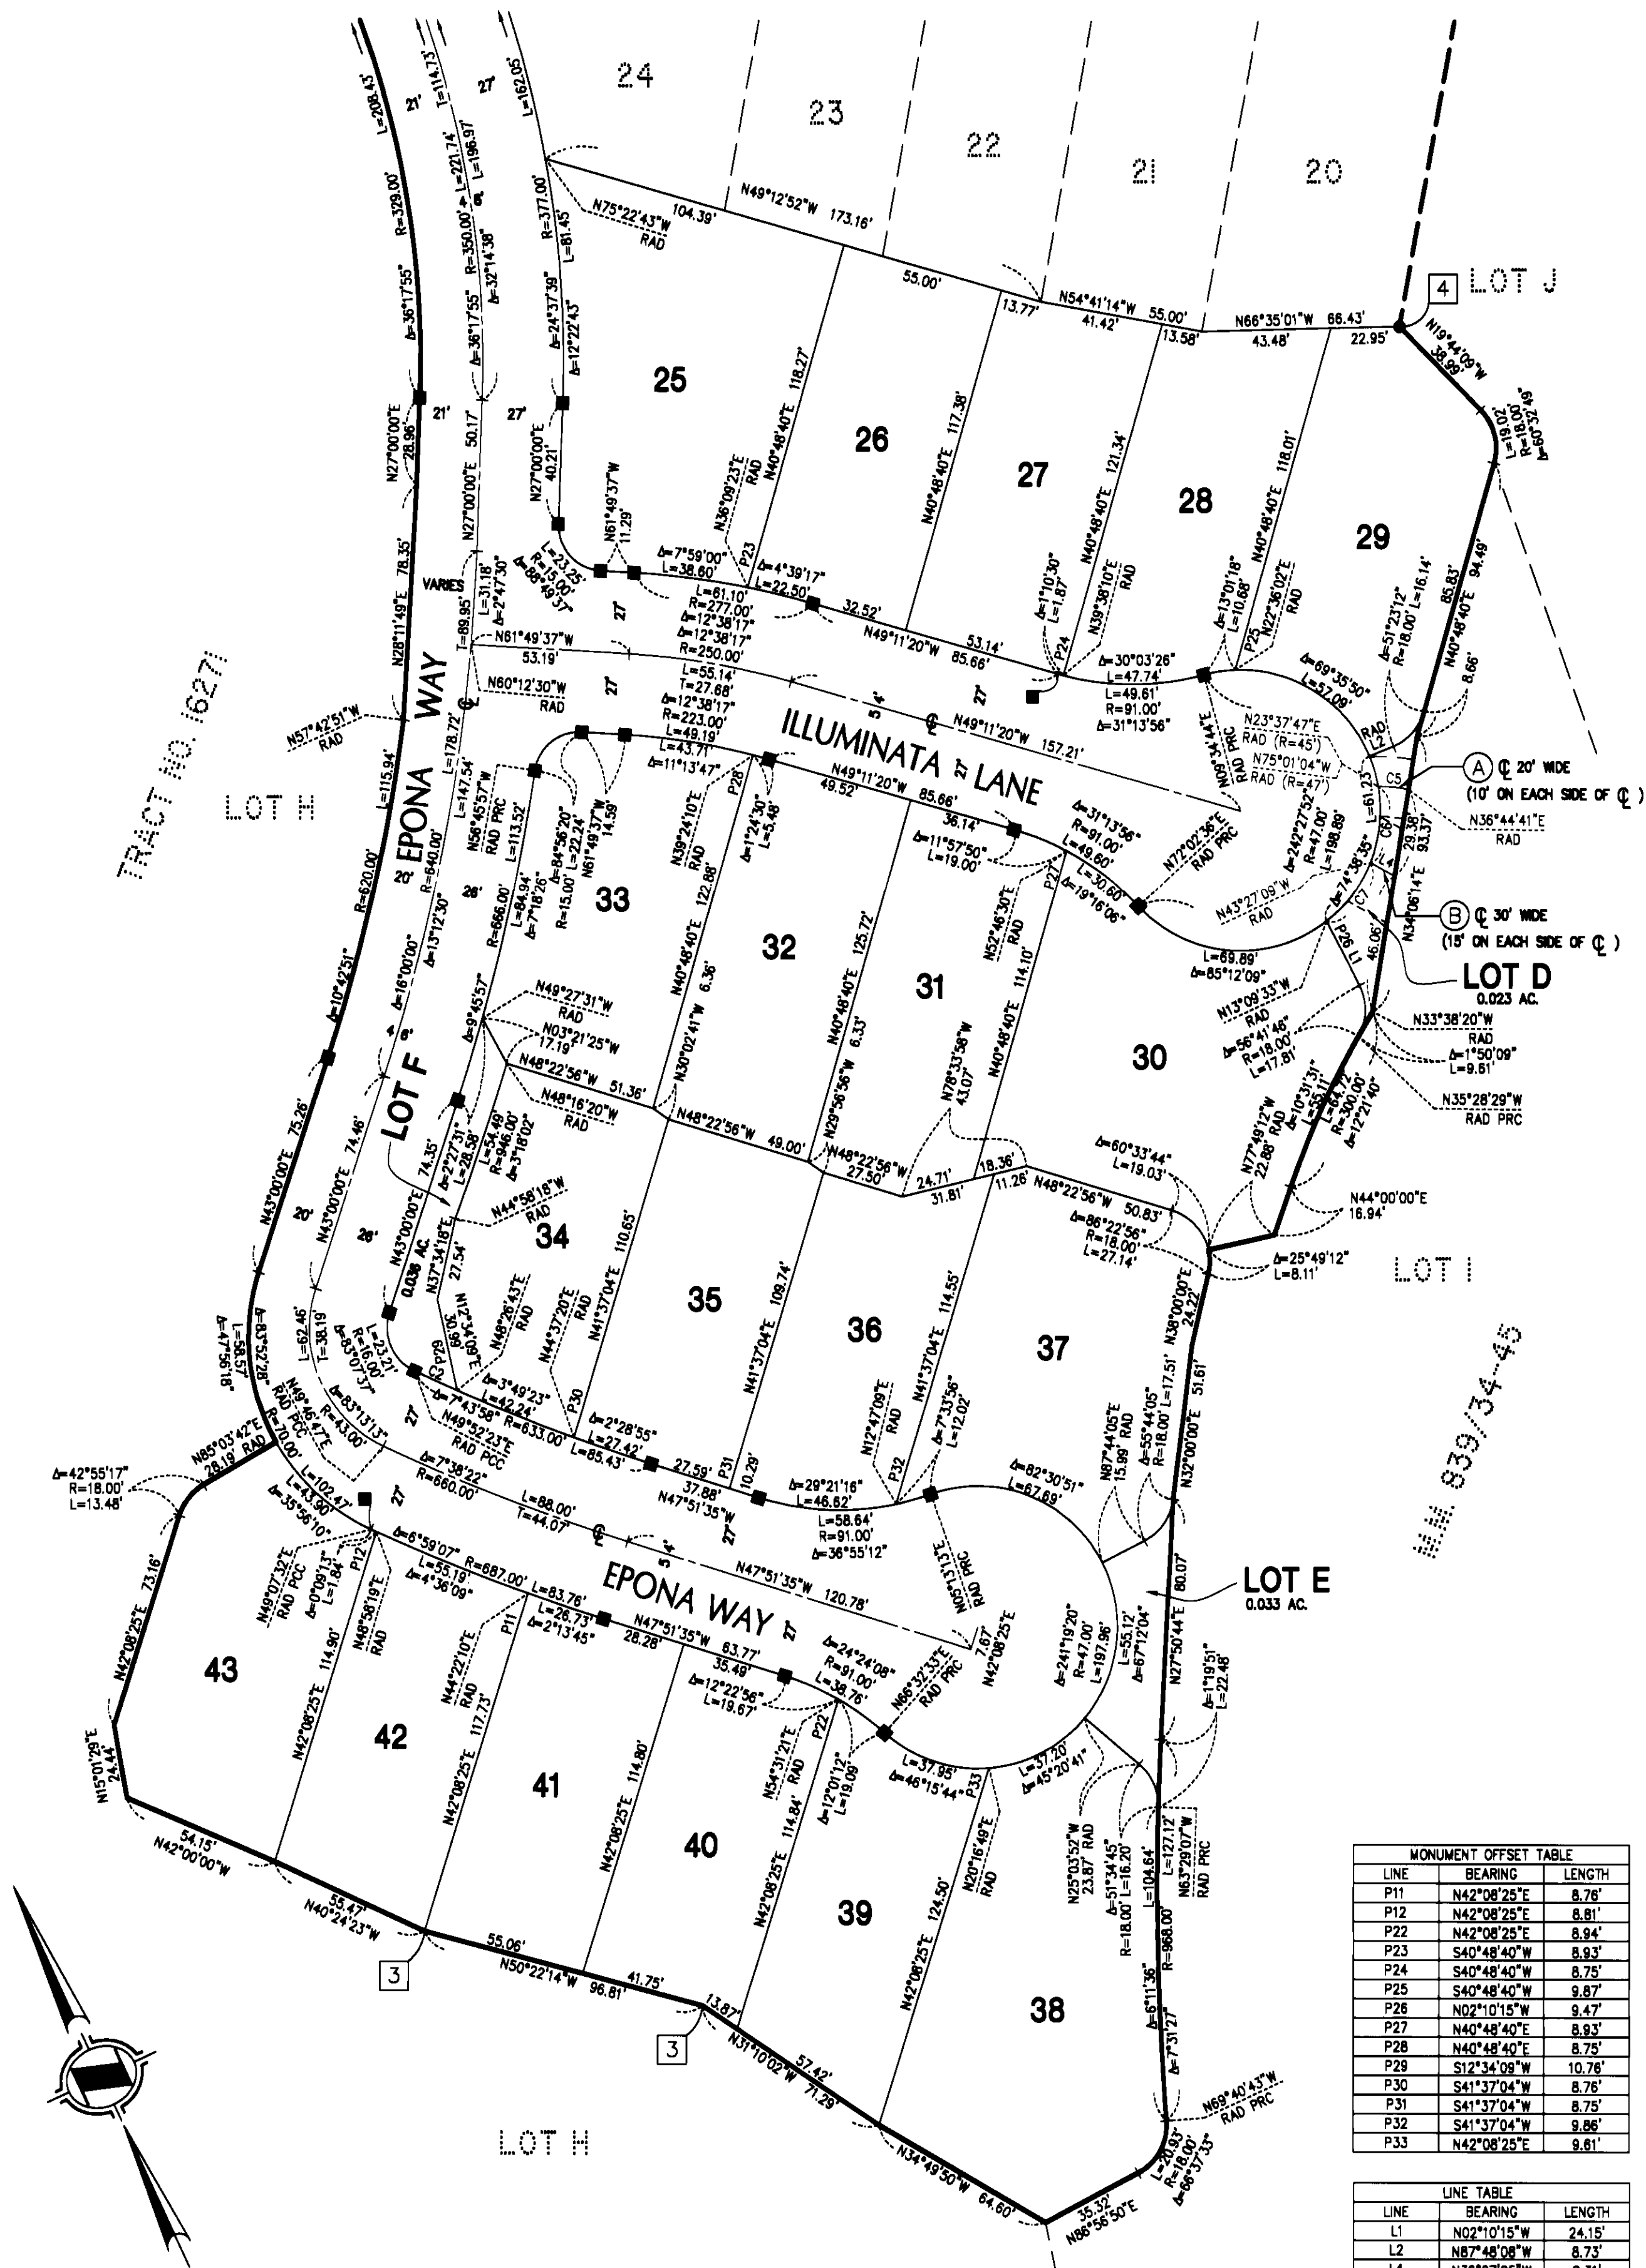

**SEE SHEET 2 FOR BASIS OF BEARINGS, DATUM STATEMENT,
MONUMENT NOTES, SHEET INDEX AND GPS CONTROL MAP,
EASEMENT NOTES AND NOTES.**

MONUMENT OFFSET TABLE		
LINE	BEARING	LENGTH
P11	N42°08'25"E	8.76'
P12	N42°08'25"E	8.81'
P22	N42°08'25"E	8.94'
P23	S40°48'40"W	8.93'
P24	S40°48'40"W	8.75'
P25	S40°48'40"W	9.87'
P26	N02°10'15"E	9.47'
P27	N40°48'40"E	8.93'
P28	N40°48'40"E	8.75'
P29	S12°34'09"W	10.76'
P30	S41°37'04"W	8.76'
P31	S41°37'04"W	8.75'
P32	S41°37'04"W	9.86'
P33	N42°08'25"E	9.61'

LINE TABLE		
LINE	BEARING	LENGTH
L1	N02°10'15"W	24.15'
L2	N87°48'08"W	8.73'
L4	N36°07'05"W	9.31'

CURVE TABLE			
CURVE	DELTA	RADIUS	LENGTH
C2	01°25'40"	633.00'	15.7
C5	13°06'54"	45.00'	10.3
C6	31°33'55"	47.00'	25.8
C7	30°17'38"	47.00'	24.8