

TRACT NO. 16355

ALL OF VESTING TENTATIVE TRACT
MAP NO. 16355
TOTAL LOTS: 1-48 AND
LOTS A, B, C, D, E, F AND G
TOTAL ACREAGE: 9.196 ACRES
DATE OF SURVEY: FEBRUARY, 2003

IN THE UNINCORPORATED TERRITORY OF THE COUNTY OF ORANGE,
STATE OF CALIFORNIA
BEING A SUBDIVISION OF LOT 9, AS SHOWN ON TRACT NO. 16271
FILED IN BOOK 839, PAGES 34 THROUGH 45 OF MISCELLANEOUS MAPS,
IN THE OFFICE OF THE COUNTY RECORDER OF SAID COUNTY, STATE OF CALIFORNIA
ADAMS - STREETER CIVIL ENGINEERS, INC. JAN A. ADAMS, R.C.E. 21687
DATE OF SURVEY: FEBRUARY, 2003

ACCEPTED AND FILED AT THE
REQUEST OF

FIRST AMERICAN TITLE COMPANY

DATE DECEMBER 18, 2003
TIME 10:57 AM FEE \$ 17.00
INSTRUMENT # 2003001496649
BOOK 852 PAGE 16m

TOM DALY
COUNTY CLERK-RECORDERBY [Signature]
DEPUTY

OWNERSHIP CERTIFICATE

WE, THE UNDERSIGNED, BEING ALL PARTIES HAVING ANY RECORD TITLE INTEREST IN THE LAND COVERED BY THIS MAP, DO HEREBY CONSENT TO THE PREPARATION AND RECORDATION OF SAID MAP, AS SHOWN WITHIN THE DISTINCTIVE BORDER LINE.

WE HEREBY DEDICATE TO THE PUBLIC FOR STREET PURPOSES: ETHEREAL STREET, CITRUS LANE, TANGO LANE, MELODY LANE AND LULLABY CIRCLE.

WE ALSO HEREBY DEDICATE TO THE COUNTY OF ORANGE:

1. THE EASEMENTS FOR STORM DRAIN PURPOSES AS SHOWN ON THIS MAP.
2. THE EASEMENTS FOR STORM DRAIN MAINTENANCE ACCESS ROAD PURPOSES AS SHOWN ON THIS MAP.

DMB LADERA, LLC, A DELAWARE LIMITED LIABILITY COMPANY.

BY: RANCHO MISSION VIEJO, LLC, A DELAWARE LIMITED LIABILITY COMPANY,
ITS AUTHORIZED AGENT AND MANAGER.

BY: [Signature]
PRINT NAME: DONALD T. STARKIN
PRINT TITLE: VICER PRESIDENT

BY: [Signature]
PRINT NAME: GREGORY S. EDWARDS
PRINT TITLE: Jr. V.P. CFO

STATE OF CALIFORNIA)
COUNTY OF ORANGE) SS

ON THIS 13th DAY OF October, 2003, BEFORE ME, Diana L. Binks, A NOTARY PUBLIC IN AND FOR SAID STATE, PERSONALLY APPEARED Donald T. Starkin AND Gregory S. Edwards PERSONALLY KNOWN TO ME (OR PROVED TO ME ON THE BASIS OF SATISFACTORY EVIDENCE) TO BE THE PERSONS WHOSE NAMES ARE SUBSCRIBED TO THE WITHIN INSTRUMENT AND ACKNOWLEDGED TO ME THAT THEY EXECUTED THE SAME IN THEIR AUTHORIZED CAPACITIES, AND THAT BY THEIR SIGNATURES ON THE INSTRUMENT THE PERSONS, OR THE ENTITY UPON BEHALF OF WHICH THE PERSONS ACTED, EXECUTED THE INSTRUMENT.

WITNESS MY HAND:

Diana L. Binks
NOTARY PUBLIC IN AND FOR SAID STATE
Diana L. Binks
PRINT NAME

MY PRINCIPAL PLACE OF BUSINESS
IS IN Orange COUNTY

MY COMMISSION EXPIRES Dec. 12, 2006

SIGNATURE OMISSIONS


PURSUANT TO THE PROVISIONS OF SECTION 66436(a)(3)(C) OF THE SUBDIVISION MAP ACT, THE FOLLOWING SIGNATURES HAVE BEEN OMITTED:

LADERA DEVELOPMENT COMPANY, LLC, HOLDER OF OIL, GAS AND MINERAL RIGHTS RECORDED
DECEMBER 10, 1996 AS INSTRUMENT NO. 19960624029 OF OFFICIAL RECORDS.

ENGINEER'S STATEMENT

THIS MAP WAS PREPARED BY ME OR UNDER MY DIRECTION AND IS BASED UPON A FIELD SURVEY IN CONFORMANCE WITH THE REQUIREMENTS OF THE SUBDIVISION MAP ACT AND LOCAL ORDINANCE AT THE REQUEST OF DMB LADERA, LLC, IN FEBRUARY 2003. I HEREBY STATE THAT ALL MONUMENTS ARE OF THE CHARACTER AND OCCUPY THE POSITIONS INDICATED, OR THAT THEY WILL BE SET IN SUCH POSITIONS; AND THAT SAID MONUMENTS ARE SUFFICIENT TO ENABLE THE SURVEY TO BE RETRACED. I HEREBY STATE THAT THIS FINAL MAP SUBSTANTIALLY CONFORMS TO THE CONDITIONALLY APPROVED TENTATIVE MAP.

JAN A. ADAMS, R.C.E. 21687
EXPIRES: 9/30/05

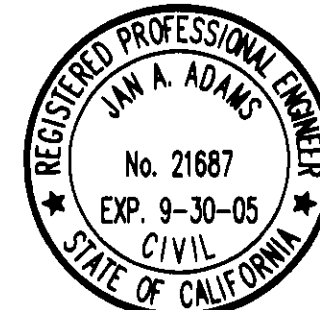


COUNTY SURVEYOR'S STATEMENT

I HEREBY STATE THAT I HAVE EXAMINED THIS MAP AND HAVE FOUND IT TO BE SUBSTANTIALLY IN CONFORMANCE WITH THE TENTATIVE MAP AS FILED WITH, AMENDED AND APPROVED BY THE ORANGE COUNTY SUBDIVISION COMMITTEE; THAT ALL PROVISIONS OF THE SUBDIVISION MAP ACT AND COUNTY SUBDIVISION REGULATIONS HAVE BEEN COMPLIED WITH AND I AM SATISFIED SAID MAP IS TECHNICALLY CORRECT.

DATED THIS 26th DAY OF November, 2003

[Signature]
JOHN CANAS, COUNTY SURVEYOR
LS 4408, EXPIRATION DATE: 9-30-05
ROBERT JELINEK, DEPUTY COUNTY SURVEYOR
LS 6803, EXPIRATION DATE: 9-30-04

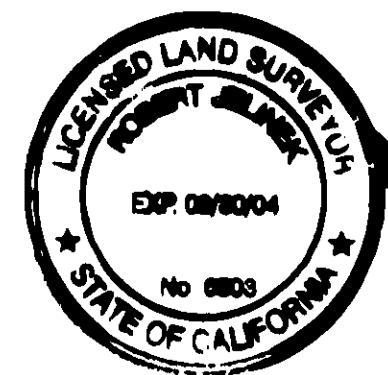

COUNTY TREASURER - TAX COLLECTOR'S CERTIFICATE

STATE OF CALIFORNIA)
COUNTY OF ORANGE) SS

I HEREBY CERTIFY THAT ACCORDING TO THE RECORDS OF MY OFFICE, THERE ARE NO LIENS AGAINST THE LAND COVERED BY THIS MAP OR ANY PART THEREOF FOR UNPAID STATE, COUNTY, MUNICIPAL OR LOCAL TAXES OR SPECIAL ASSESSMENTS COLLECTED AS TAXES, EXCEPT TAXES OR SPECIAL ASSESSMENTS COLLECTED AS TAXES NOT YET PAYABLE.

~~AND DO ALSO CERTIFY TO THE RECORDER OF ORANGE COUNTY THAT THE PROVISIONS OF THE SUBDIVISION MAP ACT HAVE BEEN COMPLIED WITH REGARDING DEPOSITS TO SECURE PAYMENT OF TAXES OR SPECIAL ASSESSMENTS COLLECTED AS TAXES ON THE LAND COVERED BY THIS MAP.~~

DATED THIS 10th DAY OF November, 2003

JOHN M. W. MOORLACH
COUNTY TREASURER - TAX COLLECTOR

BY: [Signature]
DEPUTY TREASURER TAX COLLECTOR

CLERK OF THE BOARD OF SUPERVISORS CERTIFICATE

STATE OF CALIFORNIA)
COUNTY OF ORANGE) SS

I HEREBY CERTIFY THAT THIS MAP WAS PRESENTED FOR APPROVAL TO THE BOARD OF SUPERVISORS OF ORANGE COUNTY AT A REGULAR MEETING THEREOF HELD ON THE 16th DAY OF December, 2003, AND THAT THEREUPON SAID BOARD DID, BY AN ORDER DULY PASSED AND ENTERED, APPROVE SAID MAP AND DID ACCEPT ON BEHALF OF THE PUBLIC, SUBJECT TO IMPROVEMENTS, THE DEDICATION FOR STREET PURPOSES OF: ETHEREAL STREET, CITRUS LANE, TANGO LANE, MELODY LANE AND LULLABY CIRCLE.

AND DID ALSO ACCEPT ON BEHALF OF THE COUNTY OF ORANGE:

1. THE EASEMENTS FOR STORM DRAIN PURPOSES AS DEDICATED.
2. THE EASEMENTS FOR STORM DRAIN MAINTENANCE ACCESS ROAD PURPOSES AS DEDICATED.

DATED THIS 16th DAY OF December, 2003.

[Signature]
DARLENE J. BLOOM, CLERK OF THE BOARD OF SUPERVISORS



852 2

SHEET 2 OF 6 SHEETS

ALL OF VESTING TENTATIVE TRACT
MAP NO. 16355
TOTAL LOTS: 1-48 AND
LOTS A, B, C, D, E, F AND G
TOTAL ACREAGE: 9.196 ACRES
DATE OF SURVEY: FEBRUARY, 2003

TRACT NO. 16355

IN THE UNINCORPORATED TERRITORY OF THE COUNTY OF ORANGE,
STATE OF CALIFORNIA

ADAMS - STREETER CIVIL ENGINEERS, INC. JAN A. ADAMS, R.C.E. 21687

DATE OF SURVEY: FEBRUARY, 2003

BASIS OF BEARINGS

THE BEARINGS SHOWN HEREON ARE BASED ON THE BEARING BETWEEN ORANGE COUNTY SURVEYOR'S HORIZONTAL CONTROL STATION GPS NO. 1417 AND STATION GPS NO. 1448 BEING N10°48'13"E PER TRACT NO. 16271, MM 839/34-45, RECORDS OF ORANGE COUNTY, CALIFORNIA.

DATUM STATEMENT

COORDINATES SHOWN ARE BASED ON THE CALIFORNIA COORDINATE SYSTEM (CCS83), ZONE VI, 1983 NAD (1991.35 EPOCH O.C.S. GPS ADJUSTMENT).

ALL DISTANCES SHOWN ARE GROUND, UNLESS OTHERWISE NOTED. TO OBTAIN GRID DISTANCES MULTIPLY THE GROUND DISTANCE BY THE COMBINATION FACTOR 0.999948295 SPECIFIC TO THIS PROJECT.

MONUMENT NOTES

- ① INDICATES FOUND O.C.S. HORIZONTAL CONTROL STATION AS NOTED.
 - INDICATES LOCATION OF 2" IRON PIPE TAGGED "P.L.S. 5557", OR SPIKE AND WASHER STAMPED "P.L.S. 5557", OR LEAD, TACK AND TAG "P.L.S. 5557" TO BE SET PER TRACT NO. 16271, MM 839/34-45.
 - INDICATES SET 2" IRON PIPE TAGGED "RCE 21687" PRIOR TO RECORDATION OF THIS MAP.
 - 2" IRON PIPE TAGGED "RCE 21687", OR SPIKE AND WASHER STAMPED "RCE 21687", OR LEAD, TACK AND TAG STAMPED "RCE 21687", OR NAIL AND TAG STAMPED "RCE 21687", OR A TAG STAMPED "RCE 21687" SECURED WITH EPOXY TO BE SET AT ALL TRACT BOUNDARY CORNERS, UNLESS OTHERWISE NOTED.
 - 1" IRON PIPE TAGGED "RCE 21687", OR SPIKE AND WASHER STAMPED "RCE 21687", OR LEAD, TACK AND TAG STAMPED "RCE 21687", OR A TAG STAMPED "RCE 21687" SECURED WITH EPOXY TO BE SET AT ALL LOT CORNERS, EXCEPT AT THOSE LOT CORNERS:
(a) THAT ABOUT A STREET, IN WHICH CASE, LEAD, TACK AND TAG STAMPED "RCE 21687" WILL BE SET ON THE PROLONGATION OF THE SIDE LOT LINE, 1.00 FOOT FROM THE TRUE LOT CORNER, IN THE ADJACENT CONCRETE SIDEWALK, UNLESS OTHERWISE NOTED.
- NO MONUMENTS WILL BE SET FOR B.C.'s, E.C.'s OR P.C.C.'s ALONG THE STREET RIGHT OF WAY WHERE THE STREET CENTERLINE IS MONUMENTED AND TIED OUT AT THESE LOCATIONS.
- 8" SPIKE AND WASHER STAMPED "RCE 21687" TO BE SET AT ALL STREET CENTERLINE POINTS OF CONTROL, UNLESS OTHERWISE NOTED.
 - ALL MONUMENTS WILL BE SET WITHIN 90 DAYS AFTER THE ACCEPTANCE OF IMPROVEMENTS.
 - ALL TRACT BOUNDARY DATA IS MEASURED AND RECORD PER TRACT NO. 16271, MM 839/34-45, UNLESS OTHERWISE NOTED.

NOTES

LETTERED LOTS ARE FOR LANDSCAPING/OPEN SPACE AND NOT SEPARATE BUILDING SITES.




SHEET NUMBER

ADDITIONAL INFORMATION

PURSUANT TO THE PROVISIONS OF SECTION 66434.2 OF THE SUBDIVISION MAP ACT, THE FOLLOWING IS PROVIDED FOR INFORMATIONAL PURPOSES ONLY, AND IS NOT INTENDED TO AFFECT RECORD TITLE INTEREST:

- THIS MAP IS NOT WITHIN OR ADJOINING A SPECIAL FIRE PROTECTION AREA.

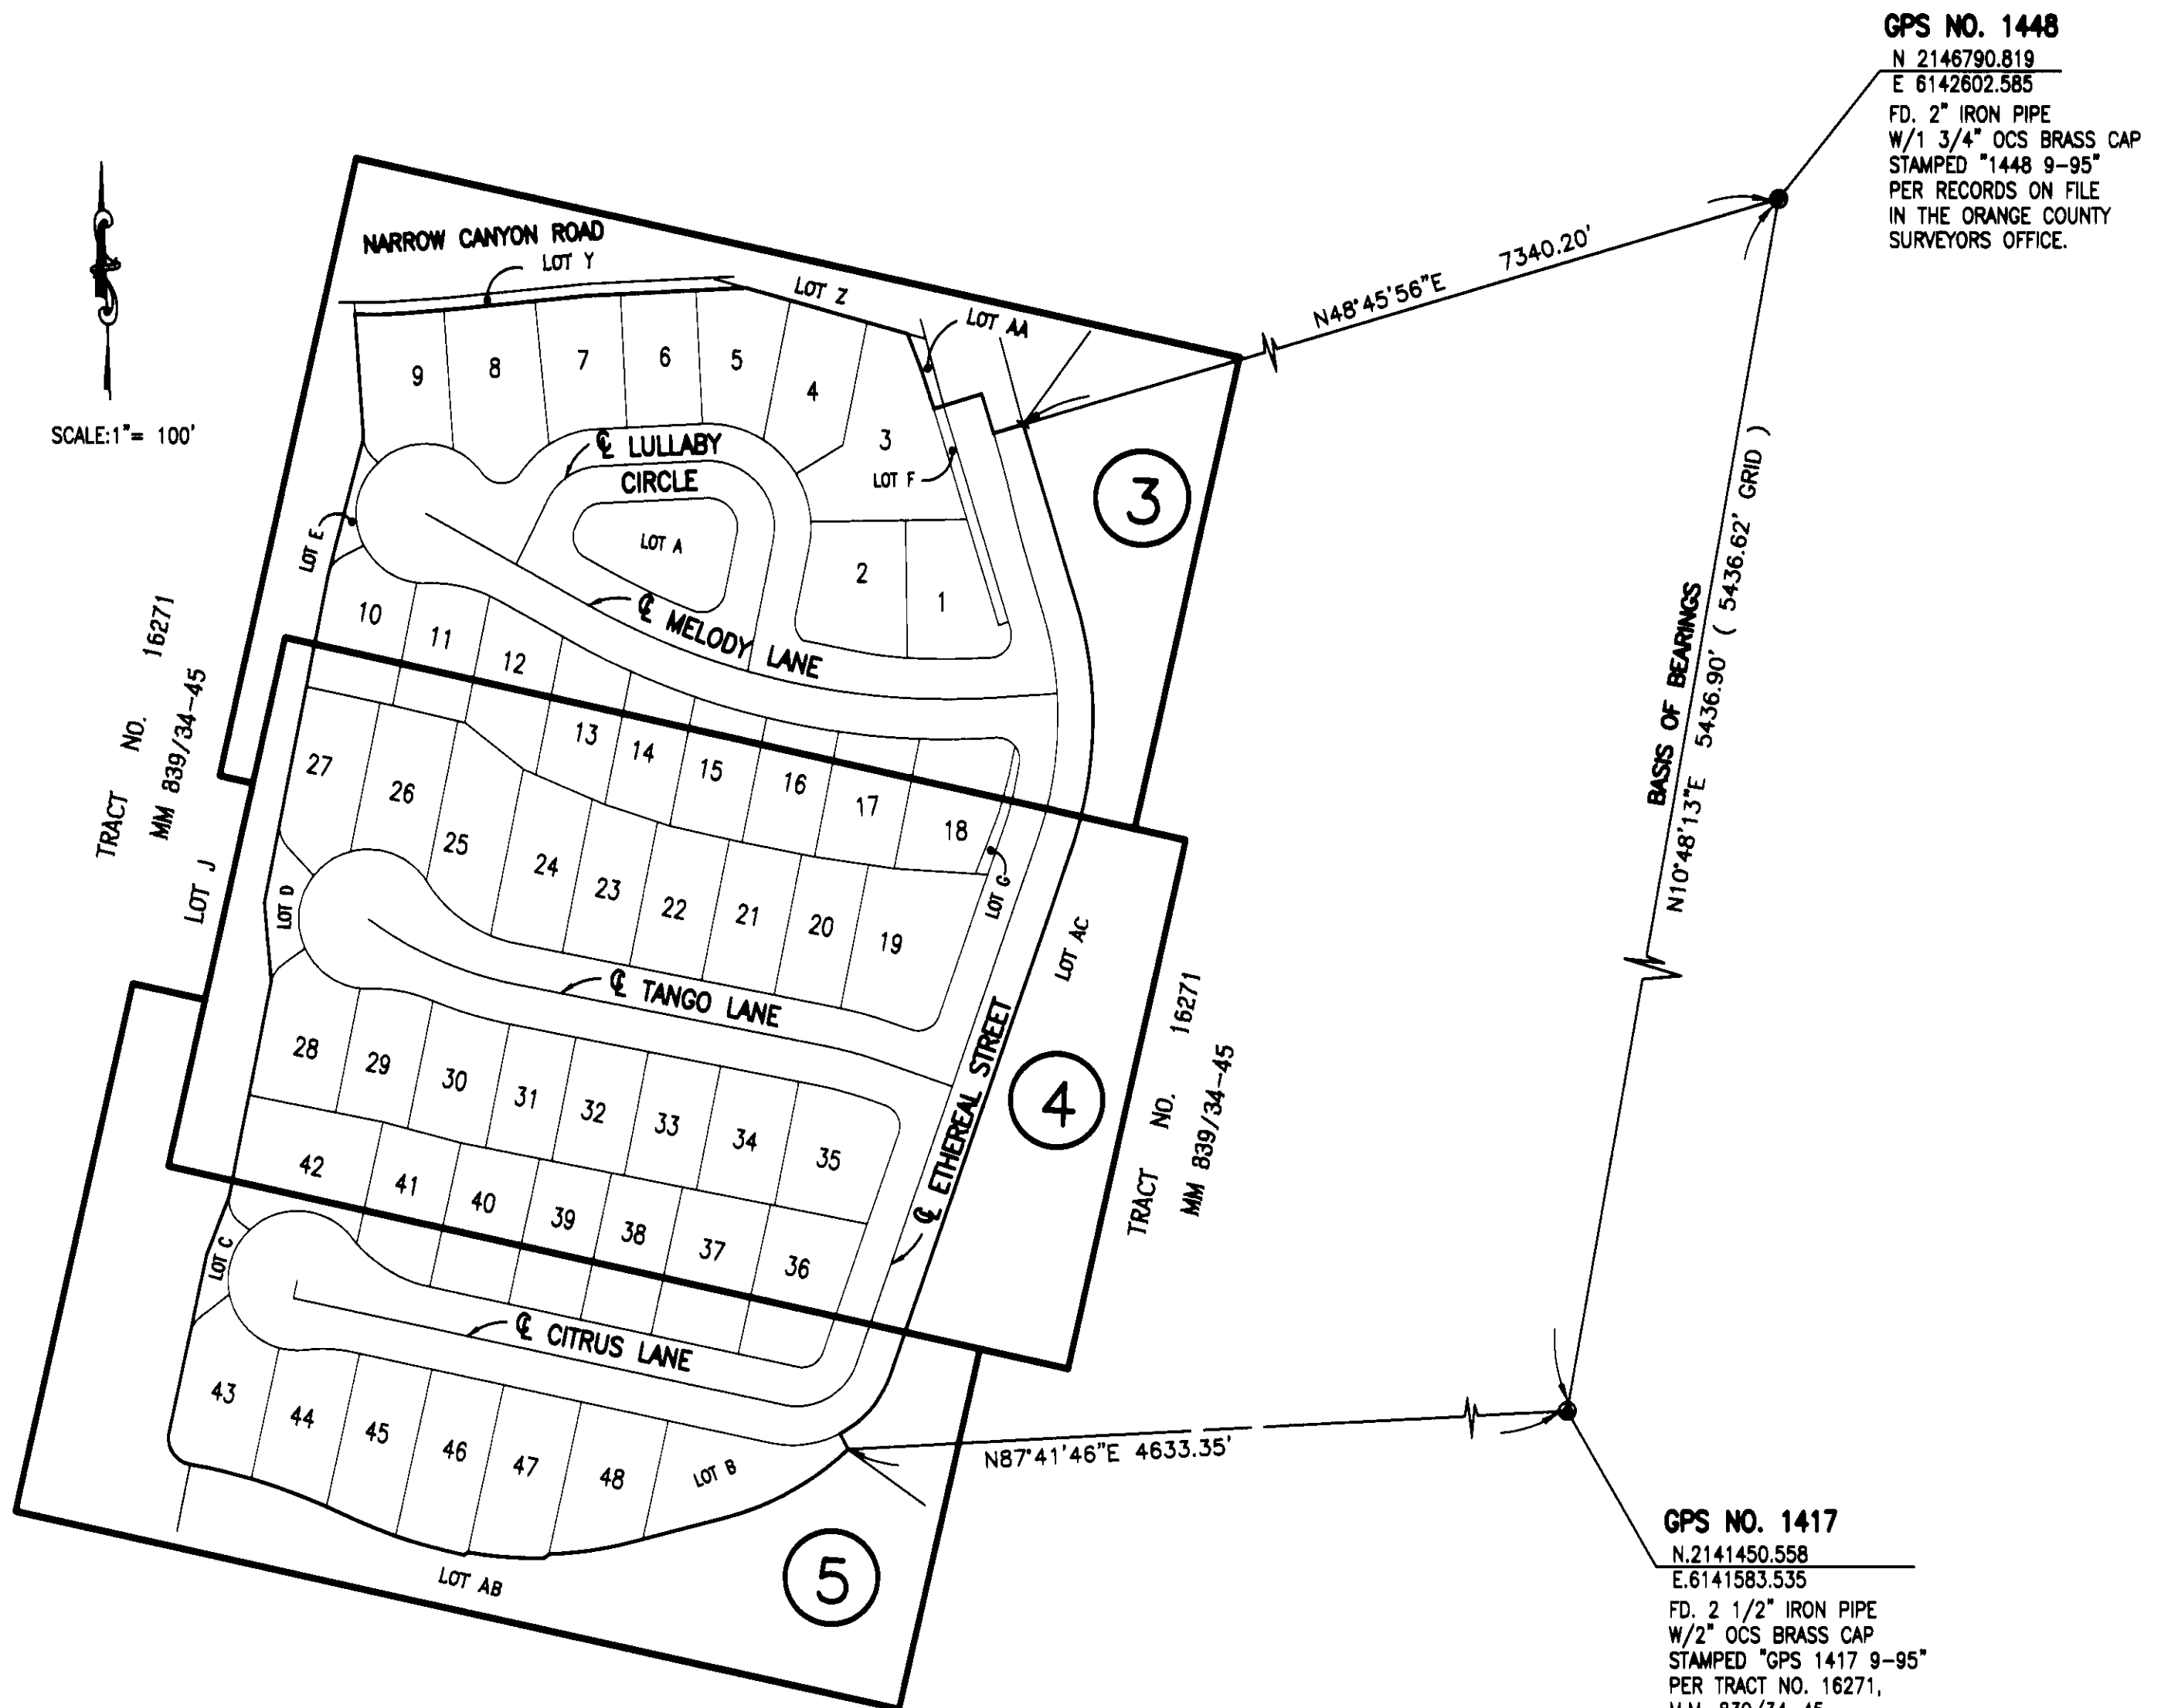


BOUNDARY CONTROL AND SHEET INDEX

852 2

ALL OF VESTING TENTATIVE TRACT
MAP NO. 16355
TOTAL LOTS: 1-48 AND
LOTS A, B, C, D, E, F AND G
TOTAL ACRES: 9.196 ACRES
DATE OF SURVEY: FEBRUARY, 2003

TRACT NO. 16355
IN THE UNINCORPORATED TERRITORY OF THE COUNTY OF ORANGE,
STATE OF CALIFORNIA
ADAMS - STREETER CIVIL ENGINEERS, INC. JAN A. ADAMS, R.C.E. 21687
DATE OF SURVEY: FEBRUARY, 2003

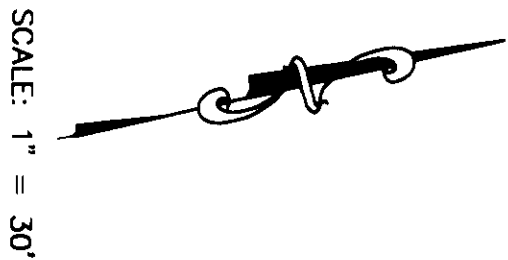

SCALE: 1" = 30'


TRACT NO. 16271
M.M. 839/34-45

CURVE AND LINE DATA

- ① A=101°52'44" R=15.00' L=26.67'
- ② A=01°21'03" R=223.00' L=5.26'
- ③ A=7°40'00"E (RAD) 7.00'
- ④ A=03°29'30" R=90.00' L=5.48'
- ⑤ A=02°52'13" R=80.00' L=4.01'
- ⑥ A=00°34'59" R=104.00' L=10.66'
- ⑦ A=02°57'52" R=70.00' L=3.62'
- ⑧ A=00°45'24" R=104.00' L=13.83'
- ⑨ A=7°37'22"W (RAD) 7.20'
- ⑩ A=6°28'58"E (RAD) 16.72'
- ⑪ A=27°09'34"E 7.43'
- ⑫ A=60°50'26" R=16.00' L=16.99'
- ⑬ A=87°08'34" R=16.00' L=24.34'
- ⑭ A=60°00'00"W 16.71'
- ⑮ A=73°53'40" R=47.00' L=60.62'
- ⑯ A=08°02'31" R=47.00' L=7.42'
- ⑰ A=04°06'23" R=91.00' L=6.52'
- ⑱ A=101°27'20" R=15.00' L=26.56'

NOTE:

- 1. SEE SHEET 2 FOR BOUNDARY CONTROL, SHEET INDEX, BASIS OF BEARINGS, DATUM STATEMENT AND MONUMENT NOTES.
- 2. SEE SHEET 6 FOR EASEMENT NOTES AND DETAILS.

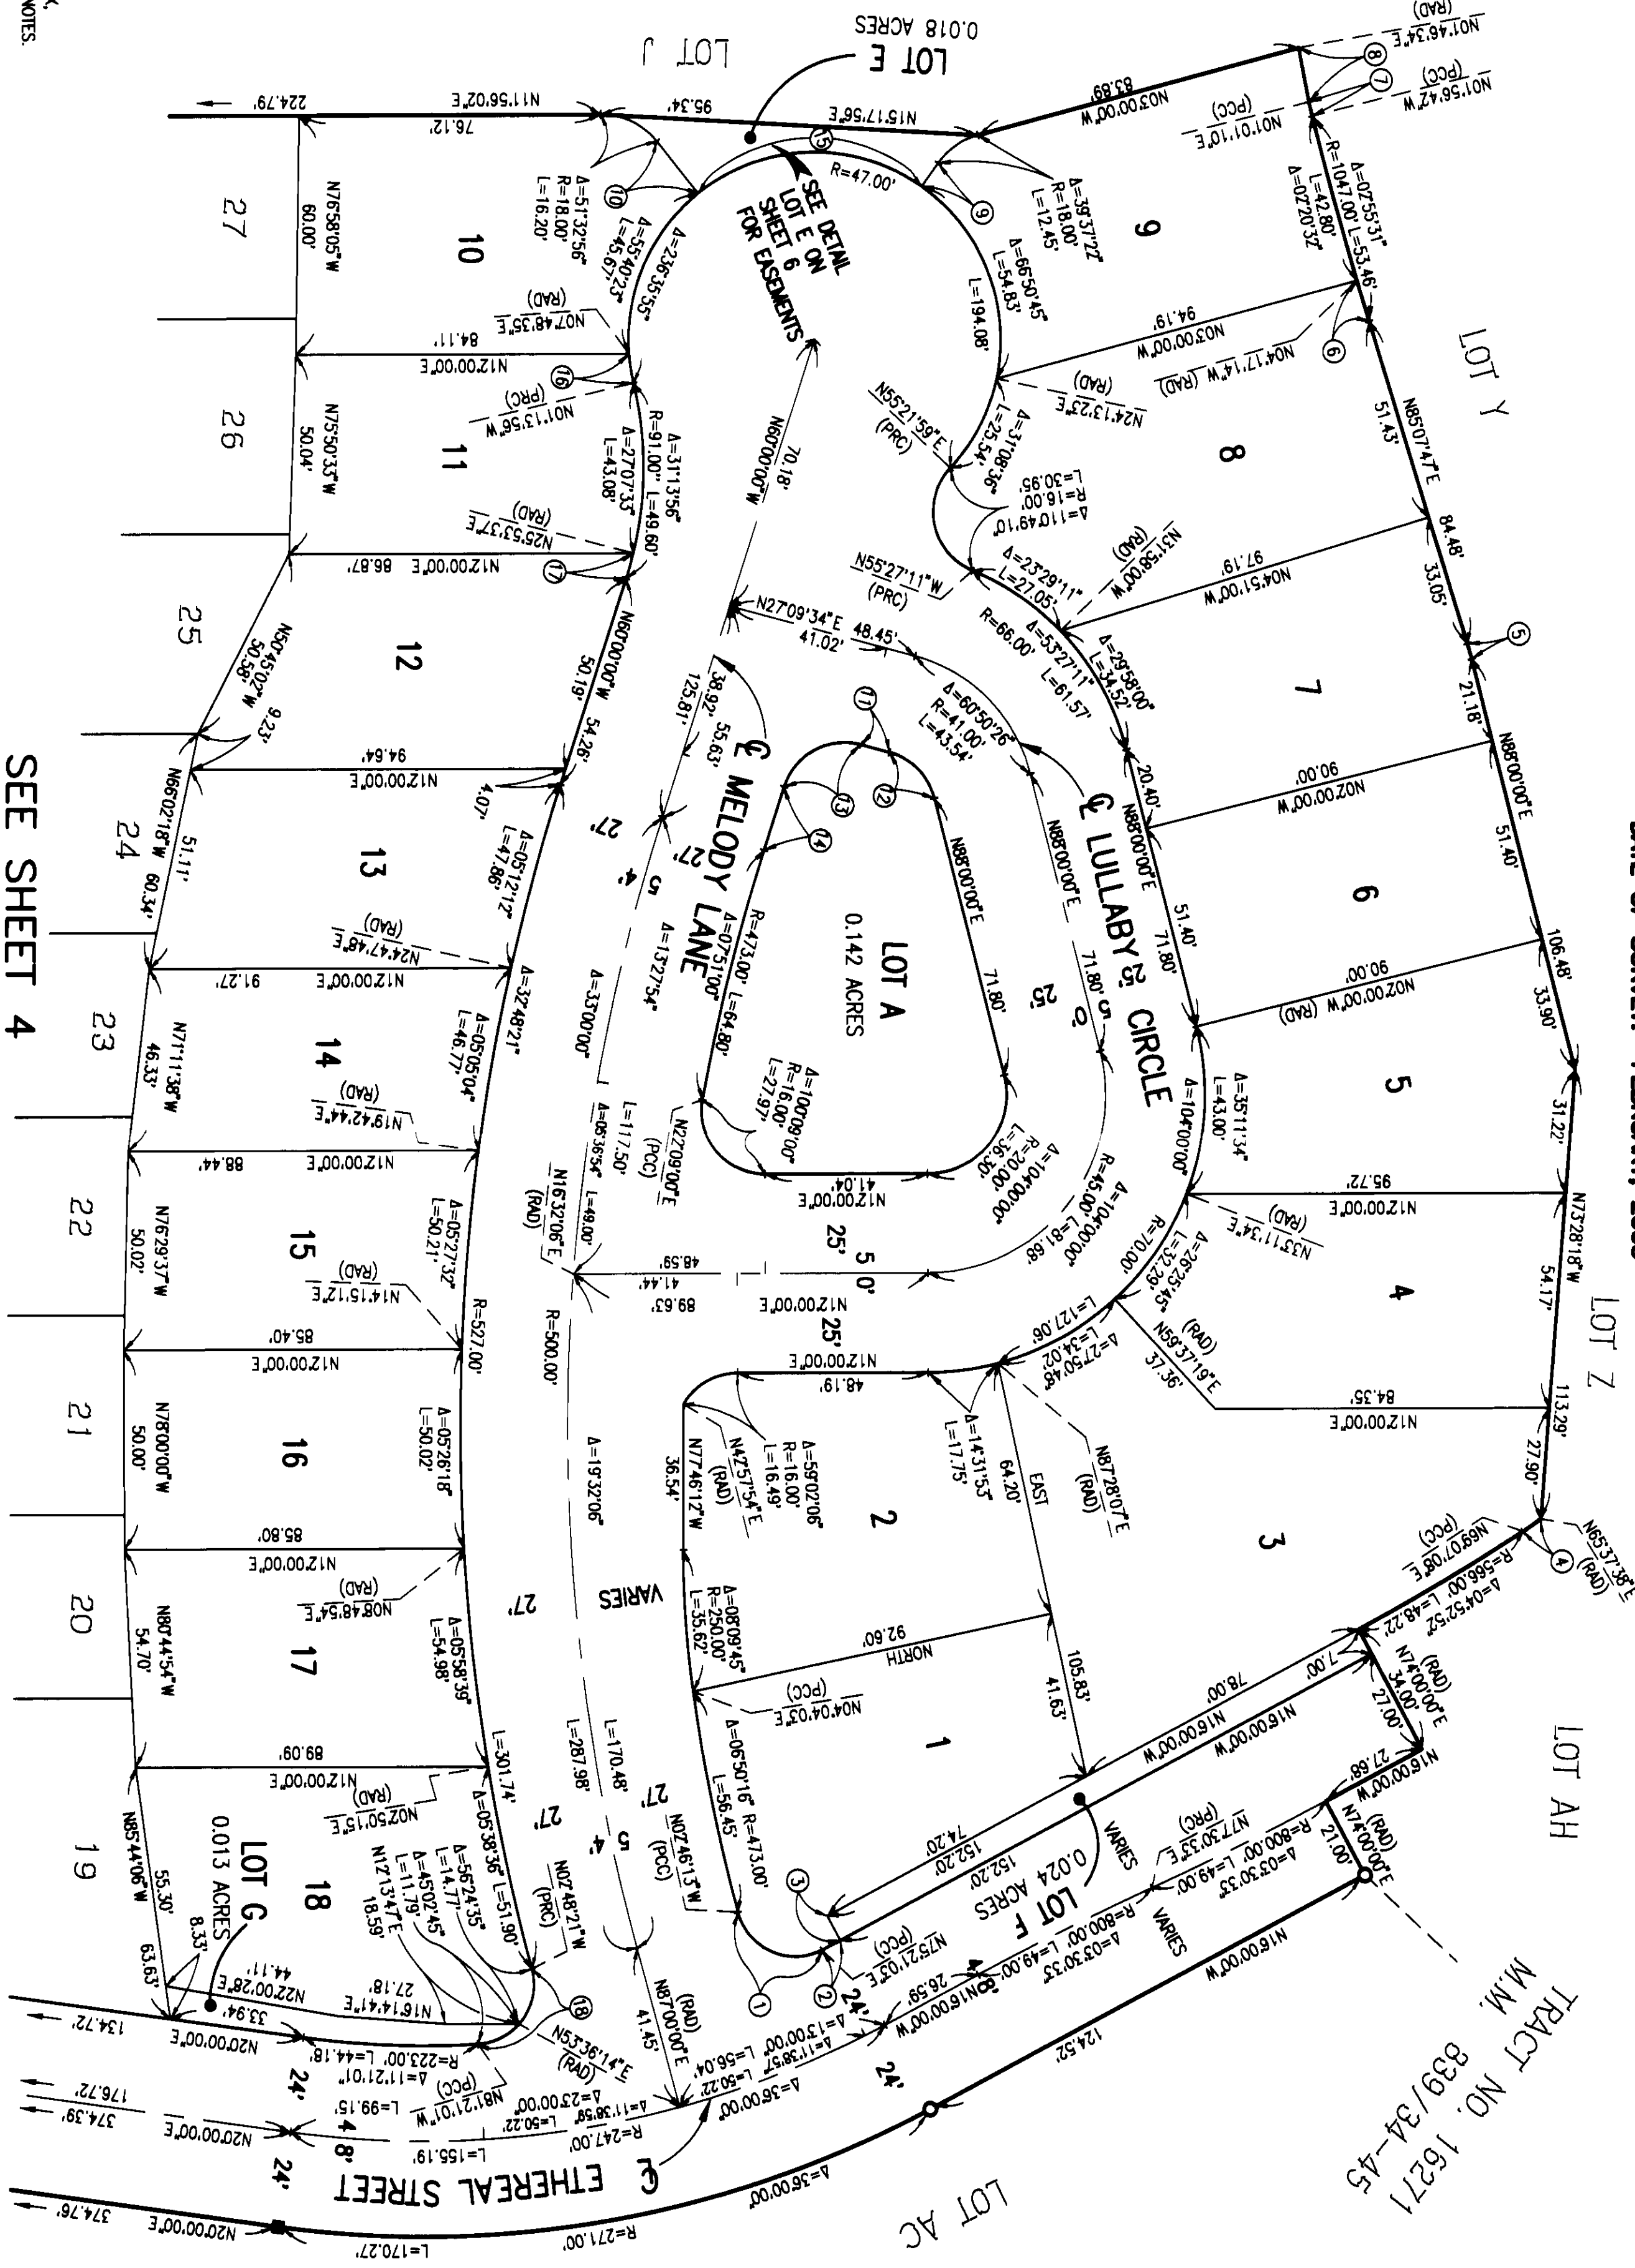

SEE SHEET 4

852 4

SHEET 4 OF 6 SHEETS

ALL OF VESTING TENTATIVE TRACT
MAP NO. 16355
TOTAL LOTS: 1-48 AND
LOTS A, B, C, D, E, F AND G
TOTAL ACRES: 9.196 ACRES
DATE OF SURVEY: FEBRUARY, 2003


TRACT NO. 16355

IN THE UNINCORPORATED TERRITORY OF THE COUNTY OF ORANGE,
STATE OF CALIFORNIA

ADAMS - STREETER CIVIL ENGINEERS, INC. JAN A ADAMS, R.C.E. 21667

DATE OF SURVEY: FEBRUARY, 2003

852 5

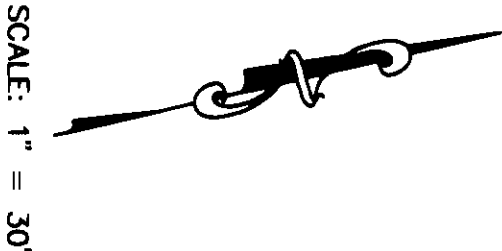

SCALE: 1" = 30'

SEE SHEET 3

TRACT NO. 16271
M.M. 839/34-45

SEE DETAIL
LOT D ON
SHEET 6
FOR EASEMENTS


CURVE AND LINE DATA

- ① - N7°00'00"W 15.05'
- ② - Δ=0°50'15" R=277.00' L=4.05'

NOTE:

- 1. SEE SHEET 2 FOR BOUNDARY CONTROL, SHEET INDEX,
BASIS OF BEARINGS, DATUM STATEMENT AND MONUMENT NOTES.
- 2. SEE SHEET 6 FOR EASEMENT NOTES AND DETAILS.

SEE SHEET 5

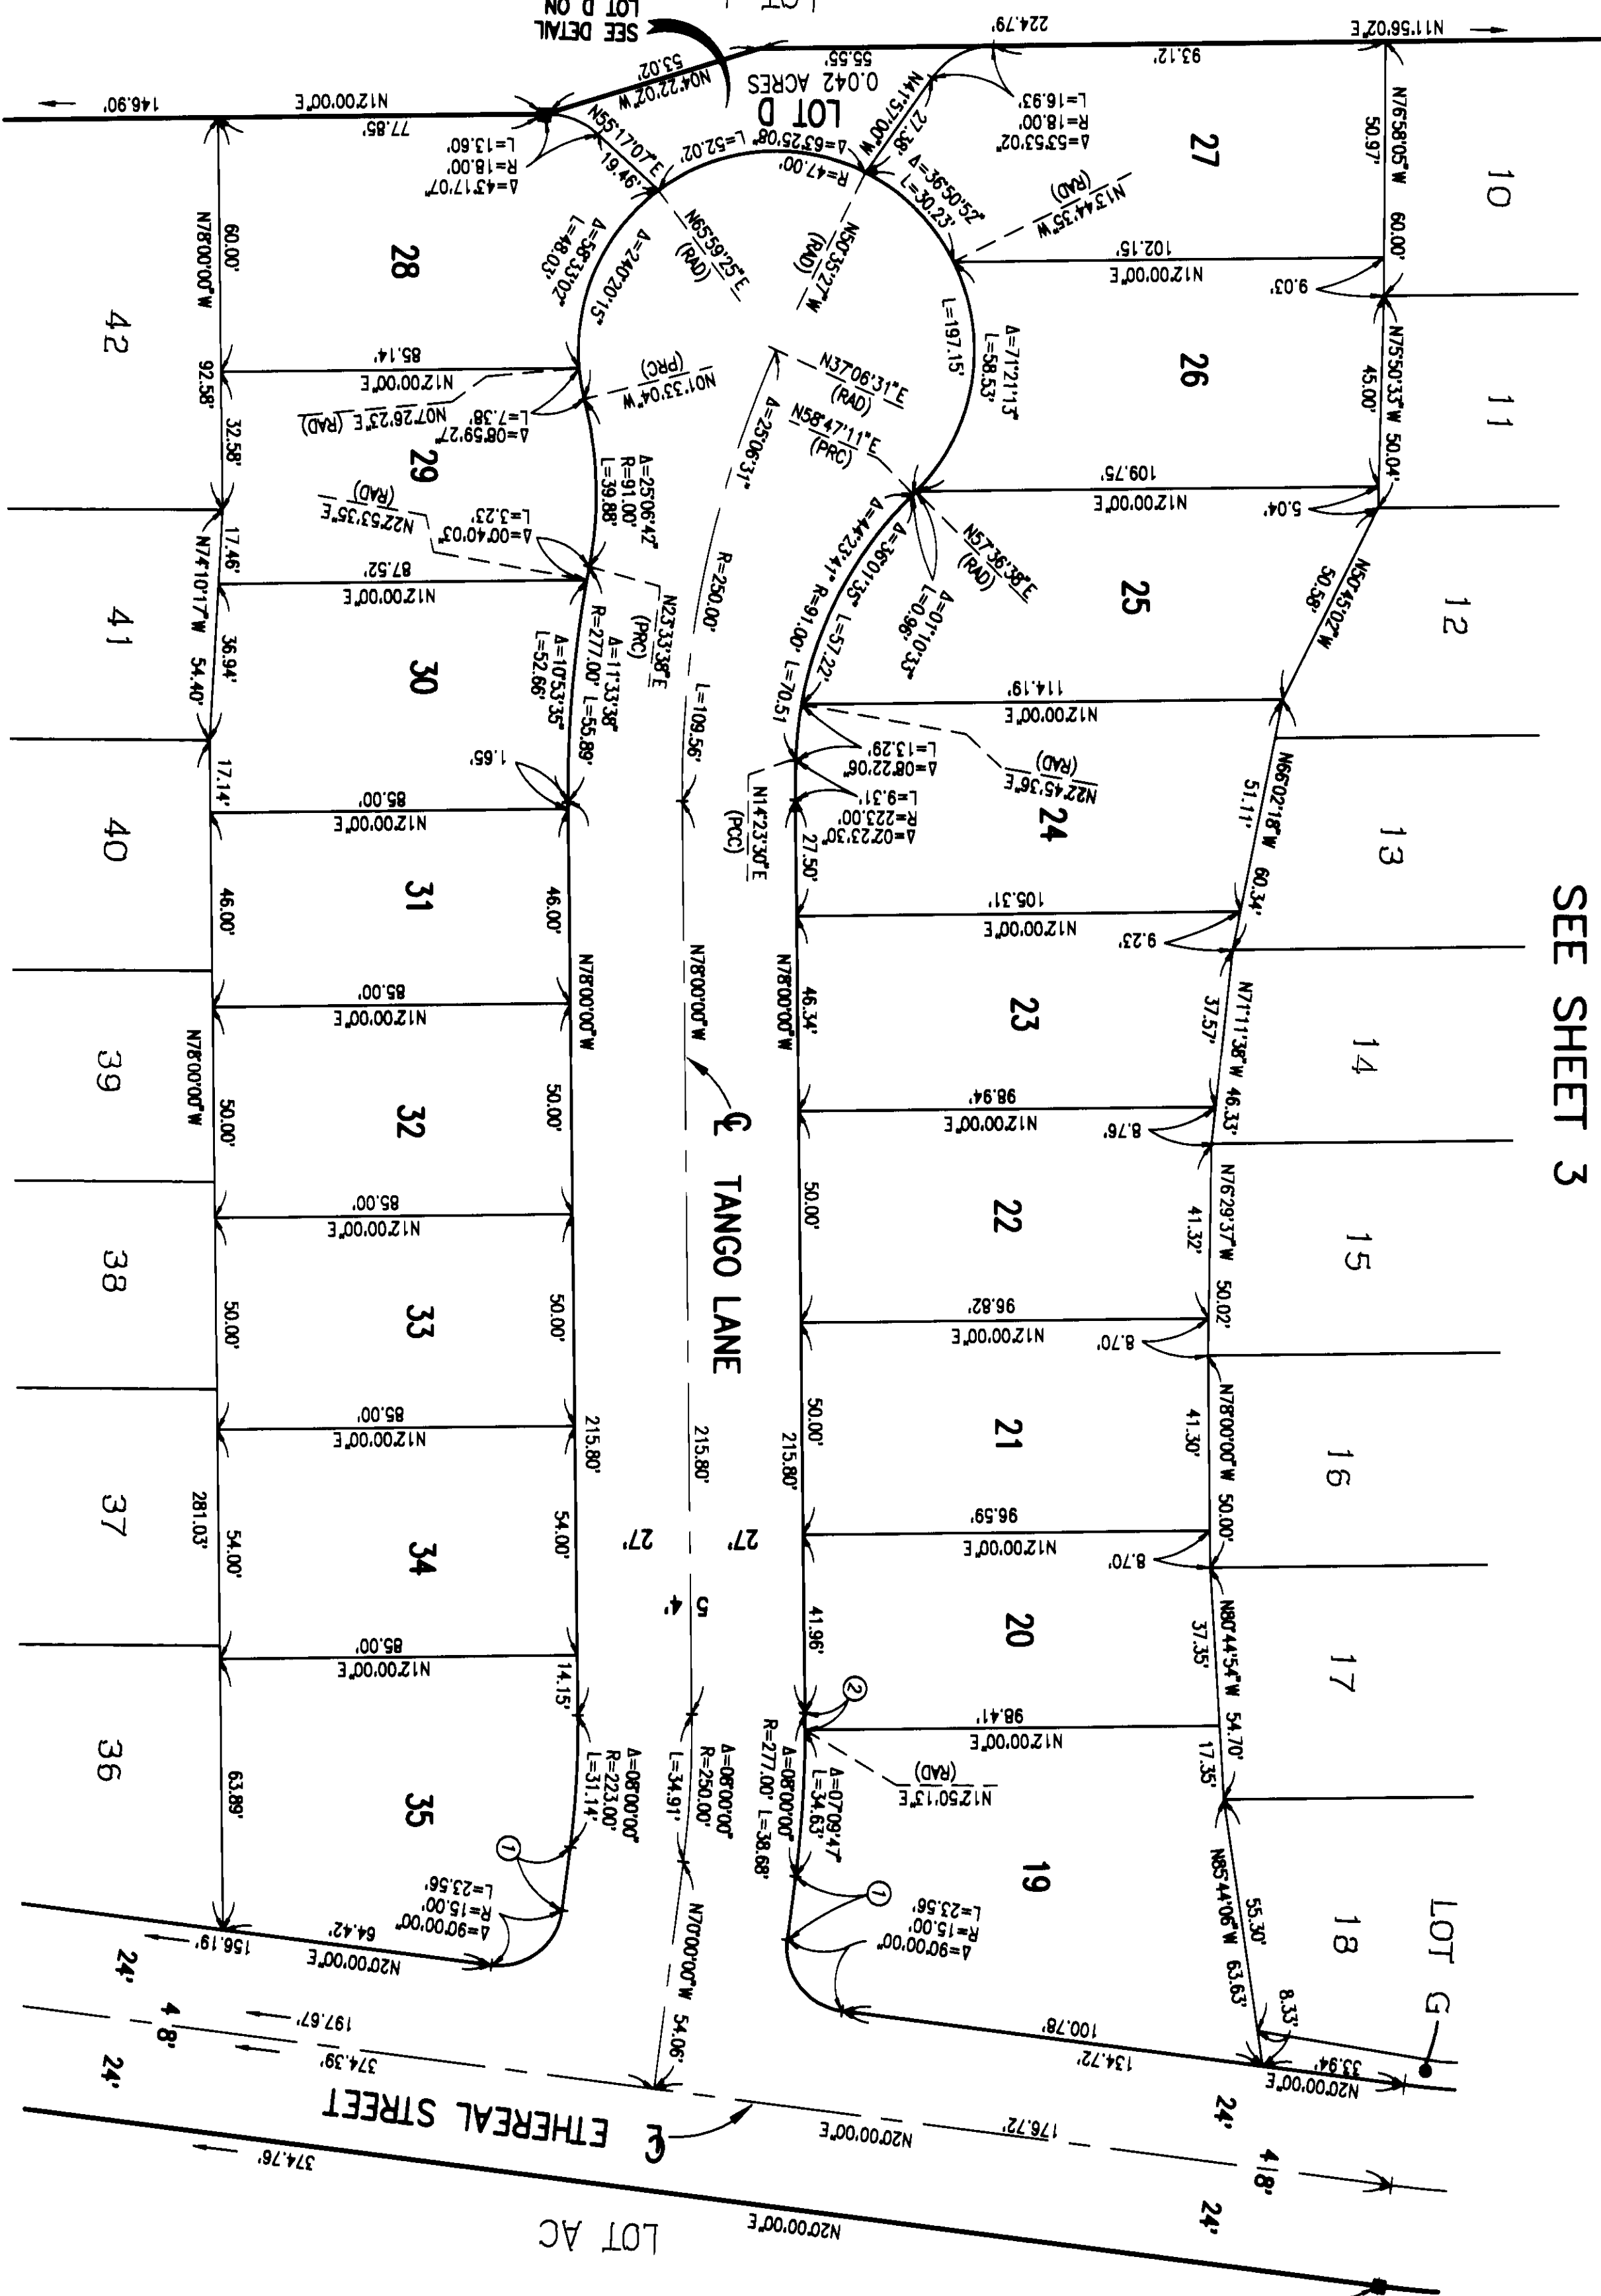


IN THE UNINCORPORATED TERRITORY OF THE COUNTY OF ORANGE,
STATE OF CALIFORNIA
ADAMS - STREETER CIVIL ENGINEERS, INC. JAN A. ADAMS, R.C.E. 21687
DATE OF SURVEY: FEBRUARY, 2003

5515

SCALE: 1" = 30'

TRACT NO. 16271
M.M. 839/34-45

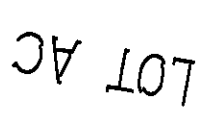


1. SEE SHEET 2 FOR BOUNDARY CONTROL, SHEET INDEX, BASIS OF BEARINGS, DATUM STATEMENT AND MONUMENT NOTES.
2. SEE SHEET 6 FOR EASEMENT NOTES AND DETAILS.

SHEET 6 OF 6 SHEETS
ALL OF VESTING TENTATIVE TRACT
MAP NO. 16355
TOTAL LOTS: 1-48 AND
LOTS A, B, C, D, E, F AND G
TOTAL ACREAGE: 9.196 ACRES
DATE OF SURVEY: FEBRUARY, 2003

TRACT NO. 16355

IN THE UNINCORPORATED TERRITORY OF THE COUNTY OF ORANGE,
STATE OF CALIFORNIA
ADAMS - STREETER CIVIL ENGINEERS, INC. JAN A ADAMS, R.C.E. 21667
DATE OF SURVEY: FEBRUARY, 2003


NOTE:
SEE SHEET 2 FOR BOUNDARY CONTROL, SHEET INDEX,
BASIS OF BEARINGS, DATUM STATEMENT AND MONUMENT NOTES.

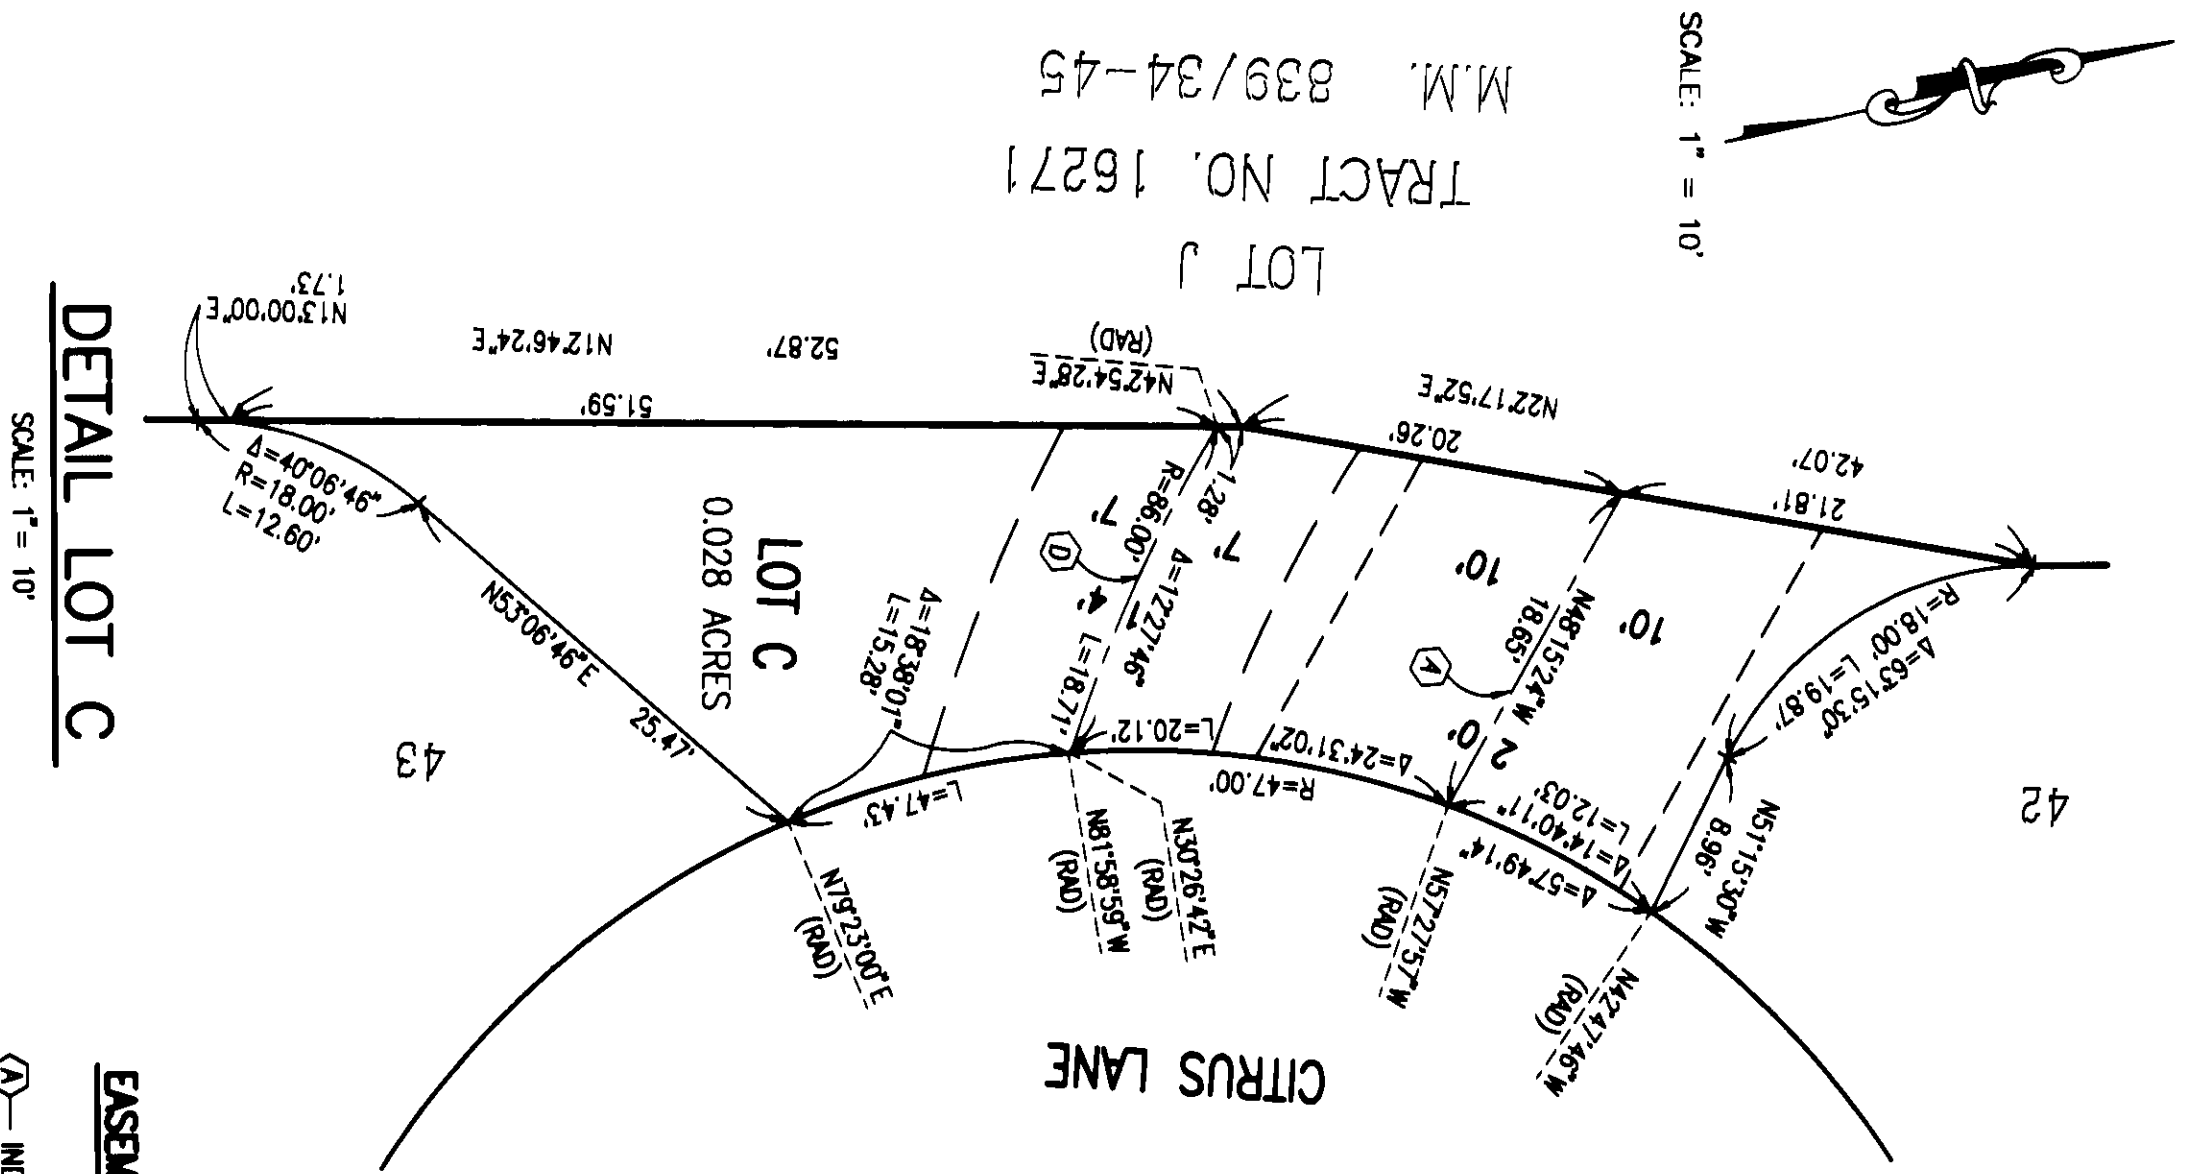

DETAIL LOT C

EASEMENT NOTES:

- (A) INDICATES CENTERLINE OF 20.00' WIDE STORM DRAIN EASEMENT DEDICATED TO THE COUNTY OF ORANGE.
- (B) INDICATES CENTERLINE OF 15.00' WIDE STORM DRAIN EASEMENT DEDICATED TO THE COUNTY OF ORANGE.
- (C) INDICATES CENTERLINE OF 22.00' WIDE STORM DRAIN MAINTENANCE ACCESS ROAD EASEMENT DEDICATED TO THE COUNTY OF ORANGE.
- (D) INDICATES CENTERLINE OF 14.00' WIDE STORM DRAIN MAINTENANCE ACCESS ROAD EASEMENT DEDICATED TO THE COUNTY OF ORANGE.

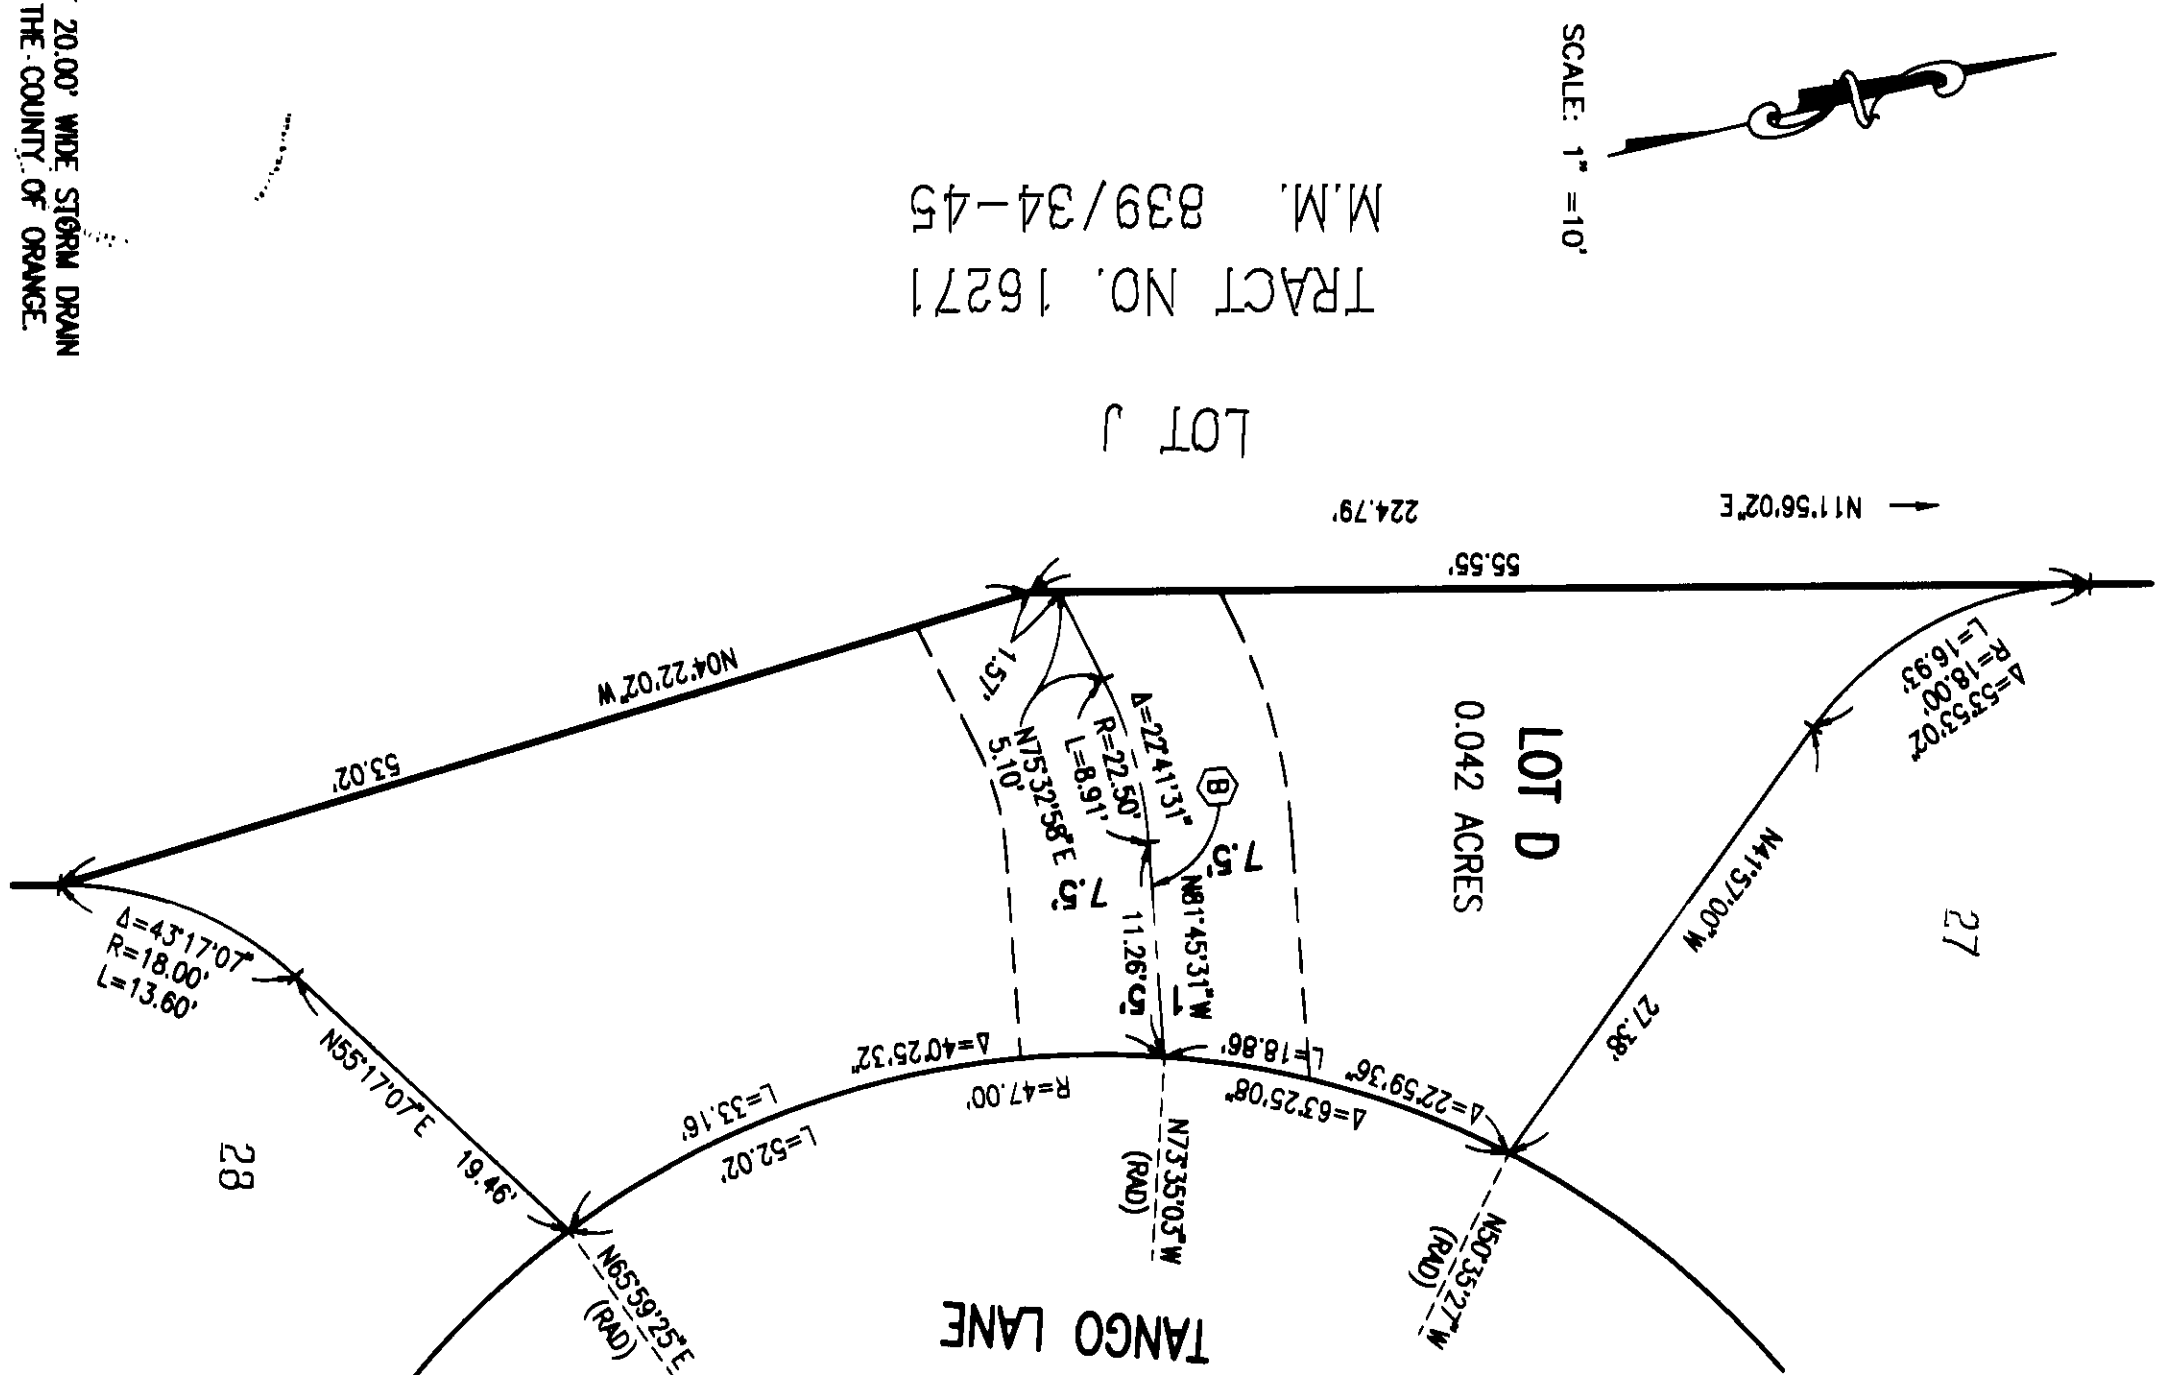

DETAIL LOT D

CURVE AND LINE DATA

①	N51°17'48"E	11.19'
②	Δ=08°05'12" R=57.14'	L=8.06'
③	Δ=08°17'42" R=47.00'	L=6.81'

DETAIL LOT E

