

SHEET 1 OF 4 SHEETS
20 NUMBERED LOTS AND
LOTS A, B & C
ACREAGE = 5.675 ACRES
A FINAL UNIT OF VESTING
TENTATIVE TRACT NO. 16384
DATE OF SURVEY: MAY 2003

TRACT NO. 16384

IN THE UNINCORPORATED TERRITORY OF THE COUNTY OF ORANGE,
STATE OF CALIFORNIA

BEING A SUBDIVISION OF PARCEL 1 OF LOT LINE ADJUSTMENT LL 2003-021, RECORDED AS INSTRUMENT NO.
2003001091079, OFFICIAL RECORDS OF SAID COUNTY, STATE OF CALIFORNIA

ADAMS - STREETER CIVIL ENGINEERS, INC. JAN A. ADAMS, R.C.E. 21687

ACCEPTED AND FILED AT THE
REQUEST OF

FIRST AMERICAN TITLE INSURANCE COMPANY

DATE February 13, 2004
TIME 11:24am FEE \$ 1600
INSTRUMENT # 20040000112627
BOOK 853 PAGE 39-42 m

TOM DALY
COUNTY - CLERK RECORDER
BY Paula Yocanville
DEPUTY

OWNER'S CERTIFICATE:

WE, THE UNDERSIGNED, BEING ALL PARTIES HAVING ANY RECORD TITLE INTEREST IN THE LAND COVERED BY THIS MAP, DO HEREBY CONSENT TO THE PREPARATION AND RECORDATION OF SAID MAP, AS SHOWN WITHIN THE DISTINCTIVE BORDER LINE.

WE ALSO HEREBY DEDICATE TO THE COUNTY OF ORANGE:

1. AN EASEMENT FOR EMERGENCY AND PUBLIC SERVICE VEHICULAR INGRESS-EGRESS PURPOSES AS SHOWN HEREIN.

WE ALSO DEDICATE TO THE SANTA MARGARITA WATER DISTRICT, THE EASEMENTS FOR SEWER, WATER AND ACCESS PURPOSES AS SHOWN ON SAID MAP, WHICH EASEMENTS SHALL BE SUBJECT TO THE SAME TERMS AND CONDITIONS AS ARE SHOWN IN THAT CERTAIN EASEMENT RECORDED SEPT. 18, 2002, AS INST. NO. 20020799401, OF OFFICIAL RECORDS, COUNTY OF ORANGE.

STANDARD PACIFIC CORP. A DELAWARE CORPORATION

William C. Fischel
NAME: WILLIAM C. FISCHEL
TITLE: AUTHORIZED REPRESENTATIVE

Todd Palmer
NAME: TODD PALMER
TITLE: AUTHORIZED REPRESENTATIVE

ENGINEER'S STATEMENT

THIS MAP WAS PREPARED BY ME OR UNDER MY DIRECTION AND IS BASED UPON A FIELD SURVEY IN CONFORMANCE WITH THE REQUIREMENTS OF THE SUBDIVISION MAP ACT AND LOCAL ORDINANCE AT THE REQUEST OF STANDARD PACIFIC CORP. IN MAY 2003. I HEREBY STATE THAT ALL MONUMENTS ARE OF THE CHARACTER AND OCCUPY THE POSITIONS INDICATED, OR THAT THEY WILL BE SET IN SUCH POSITIONS; AND THAT SAID MONUMENTS ARE SUFFICIENT TO ENABLE THE SURVEY TO BE RETRACED. I HEREBY STATE THAT THIS MAP SUBSTANTIALLY CONFORMS TO THE CONDITIONALLY APPROVED TENTATIVE MAP.

JAN A. ADAMS
JAN A. ADAMS, R.C.E. 21687
EXPIRES: 9/30/05




COUNTY SURVEYOR'S STATEMENT

I HEREBY STATE THAT I HAVE EXAMINED THIS MAP AND HAVE FOUND IT TO BE SUBSTANTIALLY IN CONFORMANCE WITH THE TENTATIVE MAP AS FILED WITH, AMENDED AND APPROVED BY THE ORANGE COUNTY SUBDIVISION COMMITTEE; THAT ALL PROVISIONS OF THE SUBDIVISION MAP ACT AND COUNTY SUBDIVISION REGULATIONS HAVE BEEN COMPLIED WITH AND I AM SATISFIED SAID MAP IS TECHNICALLY CORRECT.

DATED THIS 26th DAY OF January, 2004

Robert Jelimek
ROBERT JELIMEK, DEPUTY COUNTY SURVEYOR
LS 6803 EXPIRATION DATE: 09/30/04
JOHN CANAS, COUNTY SURVEYOR
LS 4408 EXPIRATION DATE: 09-30-05

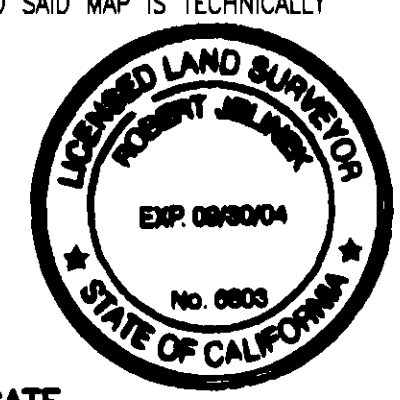

COUNTY TREASURER - TAX COLLECTOR'S CERTIFICATE

STATE OF CALIFORNIA }
COUNTY OF ORANGE } ss

I HEREBY CERTIFY THAT ACCORDING TO THE RECORDS OF MY OFFICE THERE ARE NO LIENS AGAINST THE LAND COVERED BY THIS MAP OR ANY PART THEREOF FOR UNPAID STATE, COUNTY, MUNICIPAL OR LOCAL TAXES OR SPECIAL ASSESSMENTS COLLECTED AS TAXES, EXCEPT TAXES OR SPECIAL ASSESSMENTS COLLECTED AS TAXES NOT YET PAYABLE.

AND DO ALSO CERTIFY TO THE RECORDER OF ORANGE COUNTY, THAT THE PROVISIONS OF THE SUBDIVISION MAP ACT HAVE BEEN COMPLIED WITH REGARDING DEPOSITS TO SECURE THE PAYMENT OF TAXES OR SPECIAL ASSESSMENTS COLLECTED AS TAXES ON THE LAND COVERED BY THIS MAP.

DATED THIS 13th DAY OF January, 2004

JOHN M. W. MOORLACH
COUNTY TREASURER - TAX COLLECTOR
BY Jain T...
DEPUTY TREASURER - TAX COLLECTOR

CLERK OF THE BOARD OF SUPERVISOR'S CERTIFICATE

STATE OF CALIFORNIA }
COUNTY OF ORANGE } ss

I HEREBY CERTIFY THAT THIS MAP WAS PRESENTED FOR APPROVAL TO THE BOARD OF SUPERVISORS OF ORANGE COUNTY AT A REGULAR MEETING THEREOF HELD ON THE 10th DAY OF February, 2004, AND THAT THEREUPON SAID BOARD DID, BY AN ORDER DULY PASSED AND ENTERED, APPROVE SAID MAP.

AND DID ACCEPT ON BEHALF OF THE COUNTY OF ORANGE:

1. AN EASEMENT FOR EMERGENCY AND PUBLIC SERVICE VEHICULAR INGRESS-EGRESS PURPOSES, AS DEDICATED.

AND DID ALSO APPROVE SUBJECT MAP PURSUANT TO THE PROVISIONS OF SECTION 66436 (a)(3)(A) OF THE SUBDIVISION MAP ACT.

DATED THIS 10th DAY OF February, 2004

Darlene J. Bloom
DARLENE J. BLOOM, CLERK OF THE BOARD OF SUPERVISORS



CERTIFICATE OF ACCEPTANCE

THE UNDERSIGNED, BEING THE DULY APPOINTED AGENT OF THE SANTA MARGARITA WATER DISTRICT, A PUBLIC CORPORATION OF ORANGE COUNTY, CALIFORNIA, PURSUANT TO ITS RESOLUTION NO. 88-10-2, DOES HEREBY ACCEPT ON BEHALF OF SAID DISTRICT THE EASEMENTS FOR SEWER, WATER AND ACCESS PURPOSES, AS DEDICATED AND AS SHOWN ON THIS TRACT MAP, BY AND BETWEEN THE SANTA MARGARITA WATER DISTRICT AND STANDARD PACIFIC CORP. DOES HEREBY CERTIFY THAT THE GRANTEE CONSENTS TO THE RECORDATION OF SAID TRACT.

BY: Daniel R. Feron
DANIEL R. FERONS, CHIEF ENGINEER
SANTA MARGARITA WATER DISTRICT

STATE OF CALIFORNIA }
COUNTY OF ORANGE } ss

ON THIS 26th DAY OF November, 2003, BEFORE ME, Cindy R. Lane, A NOTARY PUBLIC IN AND FOR SAID STATE, PERSONALLY APPEARED Daniel R. Feron PERSONALLY KNOWN TO ME (OR PROVED TO ME ON THE BASIS OF SATISFACTORY EVIDENCE) TO BE THE PERSON WHOSE NAME IS SUBSCRIBED TO THE WITHIN INSTRUMENT AND ACKNOWLEDGED TO ME THAT HE EXECUTED THE SAME IN HIS AUTHORIZED CAPACITY AND THAT BY HIS SIGNATURE ON THE INSTRUMENT THE PERSON, OR THE ENTITY UPON BEHALF OF WHICH THE PERSON ACTED, EXECUTED THE INSTRUMENT.

WITNESS MY HAND:
Cindy R. Lane
NOTARY PUBLIC IN AND FOR SAID STATE
CINDY R. LANE
PRINT NAME

MY PRINCIPAL PLACE OF BUSINESS
IS IN ORANGE COUNTY
MY COMMISSION EXPIRES 2/20/2005

NOTARY ACKNOWLEDGMENTS

STATE OF CALIFORNIA }
COUNTY OF ORANGE } ss

ON THIS 21st DAY OF OCTOBER, 2003, BEFORE ME, Kathleen M. Villari, A NOTARY PUBLIC IN AND FOR SAID STATE, PERSONALLY APPEARED WILLIAM C. FISCHEL & TODD PALMER PERSONALLY KNOWN TO ME (OR PROVED TO ME ON THE BASIS OF SATISFACTORY EVIDENCE) TO BE THE PERSONS WHOSE NAMES ARE SUBSCRIBED TO THE WITHIN INSTRUMENT AND ACKNOWLEDGED TO ME THAT THEY EXECUTED THE SAME IN THEIR AUTHORIZED CAPACITIES AND THAT BY THEIR SIGNATURES ON THE INSTRUMENT THE PERSON OR THE ENTITY UPON BEHALF OF WHICH THE PERSONS ACTED, EXECUTED THE INSTRUMENT.

WITNESS MY HAND:
Kathleen M. Villari
NOTARY PUBLIC IN AND FOR SAID STATE
KATHLEEN M. VILLARI
PRINT NAME

MY PRINCIPAL PLACE OF BUSINESS
IS IN ORANGE COUNTY
MY COMMISSION EXPIRES 2/15/2007

STATE OF CALIFORNIA }
COUNTY OF } ss

ON THIS _____ DAY OF _____, 2003, BEFORE ME, _____, A NOTARY PUBLIC IN AND FOR SAID STATE, PERSONALLY APPEARED _____ PERSONALLY KNOWN TO ME (OR PROVED TO ME ON THE BASIS OF SATISFACTORY EVIDENCE) TO BE THE PERSONS WHOSE NAMES ARE SUBSCRIBED TO THE WITHIN INSTRUMENT AND ACKNOWLEDGED TO ME THAT THEY EXECUTED THE SAME IN THEIR AUTHORIZED CAPACITIES AND THAT BY THEIR SIGNATURES ON THE INSTRUMENT THE PERSON OR THE ENTITY UPON BEHALF OF WHICH THE PERSONS ACTED, EXECUTED THE INSTRUMENT.

WITNESS MY HAND:

NOTARY PUBLIC IN AND FOR SAID STATE

PRINT NAME

MY PRINCIPAL PLACE OF BUSINESS
IS IN _____ COUNTY

MY COMMISSION EXPIRES _____

PRIVATE STREETS NOTE

THE PRIVATE STREETS CONTRACTED WITHIN THIS MAP SHALL BE OWNED, OPERATED AND MAINTAINED BY THE DEVELOPER, SUCCESSORS OR ASSIGNS. THE COUNTY OF ORANGE SHALL HAVE NO RESPONSIBILITY THEREFORE UNLESS PURSUANT TO APPROPRIATE SECTIONS OF THE STREETS AND HIGHWAYS CODE OF THE STATE OF CALIFORNIA, THE SAID PRIVATE STREETS HAVE BEEN ACCEPTED INTO THE COUNTY ROAD SYSTEM BY APPROPRIATE RESOLUTION OF THE ORANGE COUNTY BOARD OF SUPERVISORS.

SIGNATURE OMISSIONS

PURSUANT TO THE PROVISIONS OF SECTION 66436 (a)(3)(A)(C) OF THE SUBDIVISION MAP ACT, THE FOLLOWING SIGNATURES HAVE BEEN OMITTED:

LADERA DEVELOPMENT COMPANY, LLC, HOLDER OF OIL, GAS AND MINERAL RIGHTS RECORDED AS INSTRUMENT NO. 19960624029 OF OFFICIAL RECORDS.

DMB LADERA, LLC, HOLDER OF EASEMENTS RECORDED AS INSTRUMENT NO. 2003001135586 OF OFFICIAL RECORDS.

SOUTHERN CALIFORNIA GAS COMPANY, A CALIFORNIA CORPORATION, HOLDER OF AN EASEMENT FOR FACILITIES AND INCIDENTAL PURPOSES RECORDED NOVEMBER 25, 2003 AS INSTRUMENT NO. 2003001423369 OF OFFICIAL RECORDS.

SHEET 2 OF 4 SHEETS

20 NUMBERED LOTS AND
LOTS A, B & C

ACREAGE = 5.675 ACRES

A FINAL UNIT OF VESTING
TENTATIVE TRACT NO. 16384

DATE OF SURVEY: MAY 2003

TRACT NO. 16384

IN THE UNINCORPORATED TERRITORY OF THE COUNTY OF ORANGE,
STATE OF CALIFORNIABEING A SUBDIVISION OF PARCEL 1 OF LOT LINE ADJUSTMENT LL 2003-021, RECORDED AS INSTRUMENT NO.
2003001091079, OFFICIAL RECORDS OF SAID COUNTY, STATE OF CALIFORNIA

ADAMS - STREETER CIVIL ENGINEERS, INC. JAN A. ADAMS, R.C.E. 21687

OWNER'S CERTIFICATE (CONT.):

DMB LADERA, LLC. A DELAWARE LIMITED LIABILITY COMPANY

BENEFICIARY UNDER A DEED OF TRUST RECORDED ON SEPTEMBER 16, 2003 AS INSTRUMENT NO.
2003001135588 OF OFFICIAL RECORDS.BY: RANCHO MISSION VIEJO, LLC, A DELAWARE LIMITED LIABILITY COMPANY,
ITS AUTHORIZED AGENT AND MANAGER.BY: John V. Markel
PRINT NAME: John V. Markel PRINT NAME: John V. Markel
PRINT TITLE: V.P. PRINT TITLE: V.P.

NOTARY ACKNOWLEDGMENTS

STATE OF CALIFORNIA }
COUNTY OF } ssON THIS 28th DAY OF December, 2003, BEFORE ME, Diana L. Binks, A NOTARY
PUBLIC IN AND FOR SAID STATE, PERSONALLY APPEARED Donald T. Stahler & John V. Markel
PERSONALLY KNOWN TO ME (OR PROVED TO ME ON THE BASIS OF SATISFACTORY EVIDENCE) TO BE
THE PERSONS WHOSE NAMES ARE SUBSCRIBED TO THE WITHIN INSTRUMENT AND ACKNOWLEDGED TO ME
THAT THEY EXECUTED THE SAME IN THEIR AUTHORIZED CAPACITIES AND THAT BY THEIR SIGNATURES ON
THE INSTRUMENT THE PERSON OR THE ENTITY UPON BEHALF OF WHICH THE PERSONS ACTED, EXECUTED
THE INSTRUMENT.

WITNESS MY HAND:

Diana L. Binks
NOTARY PUBLIC IN AND FOR SAID STATEDiana L. Binks
PRINT NAMEMY PRINCIPAL PLACE OF BUSINESS
IS IN orange COUNTYMY COMMISSION EXPIRES 12/12/06

SHEET 3 OF 4 SHEETS
20 NUMBERED LOTS AND
LOTS A, B & C
ACREAGE = 5.675 ACRES
A FINAL UNIT OF VESTING
TENTATIVE TRACT NO. 16384

TRACT NO. 16384

IN THE UNINCORPORATED TERRITORY OF THE COUNTY OF ORANGE,
 STATE OF CALIFORNIA

ADAMS - STREETER CIVIL ENGINEERS, INC. JAN A. ADAMS, R.C.E. 21687
 DATE OF SURVEY: DEC. 2002

SCALE: 1"=100'

MONUMENT NOTES:

1. ● 2" IRON PIPE, TAGGED "R.C.E. 21687" TO BE SET PRIOR TO RECORDATION.
2. ■ 8" SPIKE AND WASHER STAMPED "L.S. 5557" IN ASPHALT PAVING OR LEAD, TACK AND TAG "L.S. 5557" IN CONCRETE OR 1" IRON PIPE, TAGGED "L.S. 5557" TO BE SET PER TRACT 15987, MM 839/1-18.
3. 1" IRON PIPE, TAGGED "R.C.E. 21687", OR SPIKE AND WASHER, STAMPED "R.C.E. 21687", OR LEAD, TACK AND TAG "R.C.E. 21687" TO BE SET AT ALL LOT CORNERS, EXCEPT AT LOT CORNERS THAT ABUT A STREET, WHICH WILL BE SET ON A 9.75' OFFSET OUTSIDE THE TRUE LOT CORNER ON A PROLONGATION OF THE SIDE LOT LINE BY A LEAD, TACK AND TAG "R.C.E. 21687" IN THE TOP OF ADJACENT CONCRETE CURB, UNLESS OTHERWISE NOTED.
4. 8" SPIKE AND WASHER STAMPED "RCE 21687" IN ASPHALT PAVING OR LEAD, TACK AND TAG "R.C.E. 21687" IN CONCRETE OR 1" IRON PIPE, TAGGED "RCE 21687" TO BE SET AT ALL CENTERLINE INTERSECTIONS, B.C.'S, E.C.'S AND ALL OTHER CENTERLINE POINTS OF CONTROL, UNLESS OTHERWISE NOTED.
5. ALL MONUMENTS SHOWN AS "TO BE SET" WILL BE SET 90 DAYS AFTER THE ACCEPTANCE OF THE FINAL IMPROVEMENTS.
6. NO MONUMENTS TO BE SET AT BC'S AND EC'S OF STREET RIGHT OF WAY LINES.
7. ▲ FOUND GPS HORIZONTAL CONTROL POINT PER RECORDS ON FILE IN THE ORANGE COUNTY SURVEYOR'S OFFICE.
8. 2" IRON PIPE TAGGED "RCE 21687", OR SPIKE AND WASHER STAMPED "RCE 21687", OR LEAD, TACK AND TAG STAMPED "RCE 21687", OR NAIL AND TAG STAMPED "RCE 21687", OR A TAG STAMPED "RCE 21687" SECURED WITH EPOXY TO BE SET AT ALL TRACT BOUNDARY CORNERS, UNLESS OTHERWISE NOTED.

BASIS OF BEARINGS

THE BEARINGS SHOWN HEREON ARE BASED ON THE BEARING BETWEEN ORANGE COUNTY SURVEYOR'S HORIZONTAL CONTROL STATION "GPS NO. 7751" AND "GPS NO. 9009", BEING N. 25°35'15" E., PER RECORDS ON FILE IN THE OFFICE OF THE ORANGE COUNTY SURVEYOR.

DATUM STATEMENT

COORDINATES SHOWN HEREON ARE BASED ON THE CALIFORNIA COORDINATE SYSTEM (CCS83) ZONE VI, 1983 NAD (1991.35 EPOCH, O.C.S. GPS ADJUSTMENT). ALL DISTANCES SHOWN HEREON ARE GROUND, UNLESS OTHERWISE NOTED. TO OBTAIN GRID DISTANCE MULTIPLY GROUND DISTANCE BY 0.99994794.

AUTOMATIC FIRE SPRINKLER NOTE:

ALL RESIDENTIAL STRUCTURES EXCEEDING 5,500 SQUARE FEET AND ALL STRUCTURES EXCEEDING FIRE DEPARTMENT ACCESS REQUIREMENTS SHALL BE PROTECTED BY AN AUTOMATIC FIRE SPRINKLER SYSTEM, IN A MANNER MEETING THE APPROVAL OF THE FIRE CHIEF.

SPECIAL FIRE PROTECTION NOTE:

PROPERTY IS CONDITIONALLY EXCLUDED FROM A SPECIAL FIRE PROTECTION AREA. ALL REQUIREMENTS FOR DEVELOPMENT AND CONSTRUCTION WITHIN A "SPECIAL FIRE PROTECTION AREA" INCLUDING INCREASED STREET WIDTHS AND CLASS A ROOF ASSEMBLIES WILL BE MET.

EASEMENT NOTES:


- (A) AN EASEMENT FOR SEWER AND WATER PIPELINE AND ACCESS PURPOSES DEDICATED TO THE SANTA MARGARITA WATER DISTRICT HEREON.
- (B) AN EASEMENT FOR SEWER AND WATER PIPELINE AND ACCESS PURPOSES DEDICATED TO THE SANTA MARGARITA WATER DISTRICT PER TRACT 15987 M.M. 839/1-18.
- (C) AN EASEMENT FOR EMERGENCY AND PUBLIC SERVICE VEHICULAR INGRESS-EGRESS DEDICATED TO THE COUNTY OF ORANGE HEREON.

GPS NO. 9009

FOUND 2 1/2" IRON PIPE W/2" BRASS CAP
 STAMPED "LEMONHEAD OCS 9009" PER R.S.
 92-1034, RSB 150/36-50 AND RECORDS
 ON FILE IN THE ORANGE COUNTY SURVEYOR'S
 OFFICE.
 N 2151259.152
 E 6133621.604

GPS NO. 7751

FOUND PUN. SPK & TIN.
 NOT STAMPED PER RECORD OF SURVEY
 92-1034, RSB 150/36-50 AND RECORDS
 ON FILE IN THE ORANGE COUNTY SURVEYOR'S
 OFFICE.
 N 2144604.077
 E 6130434.809

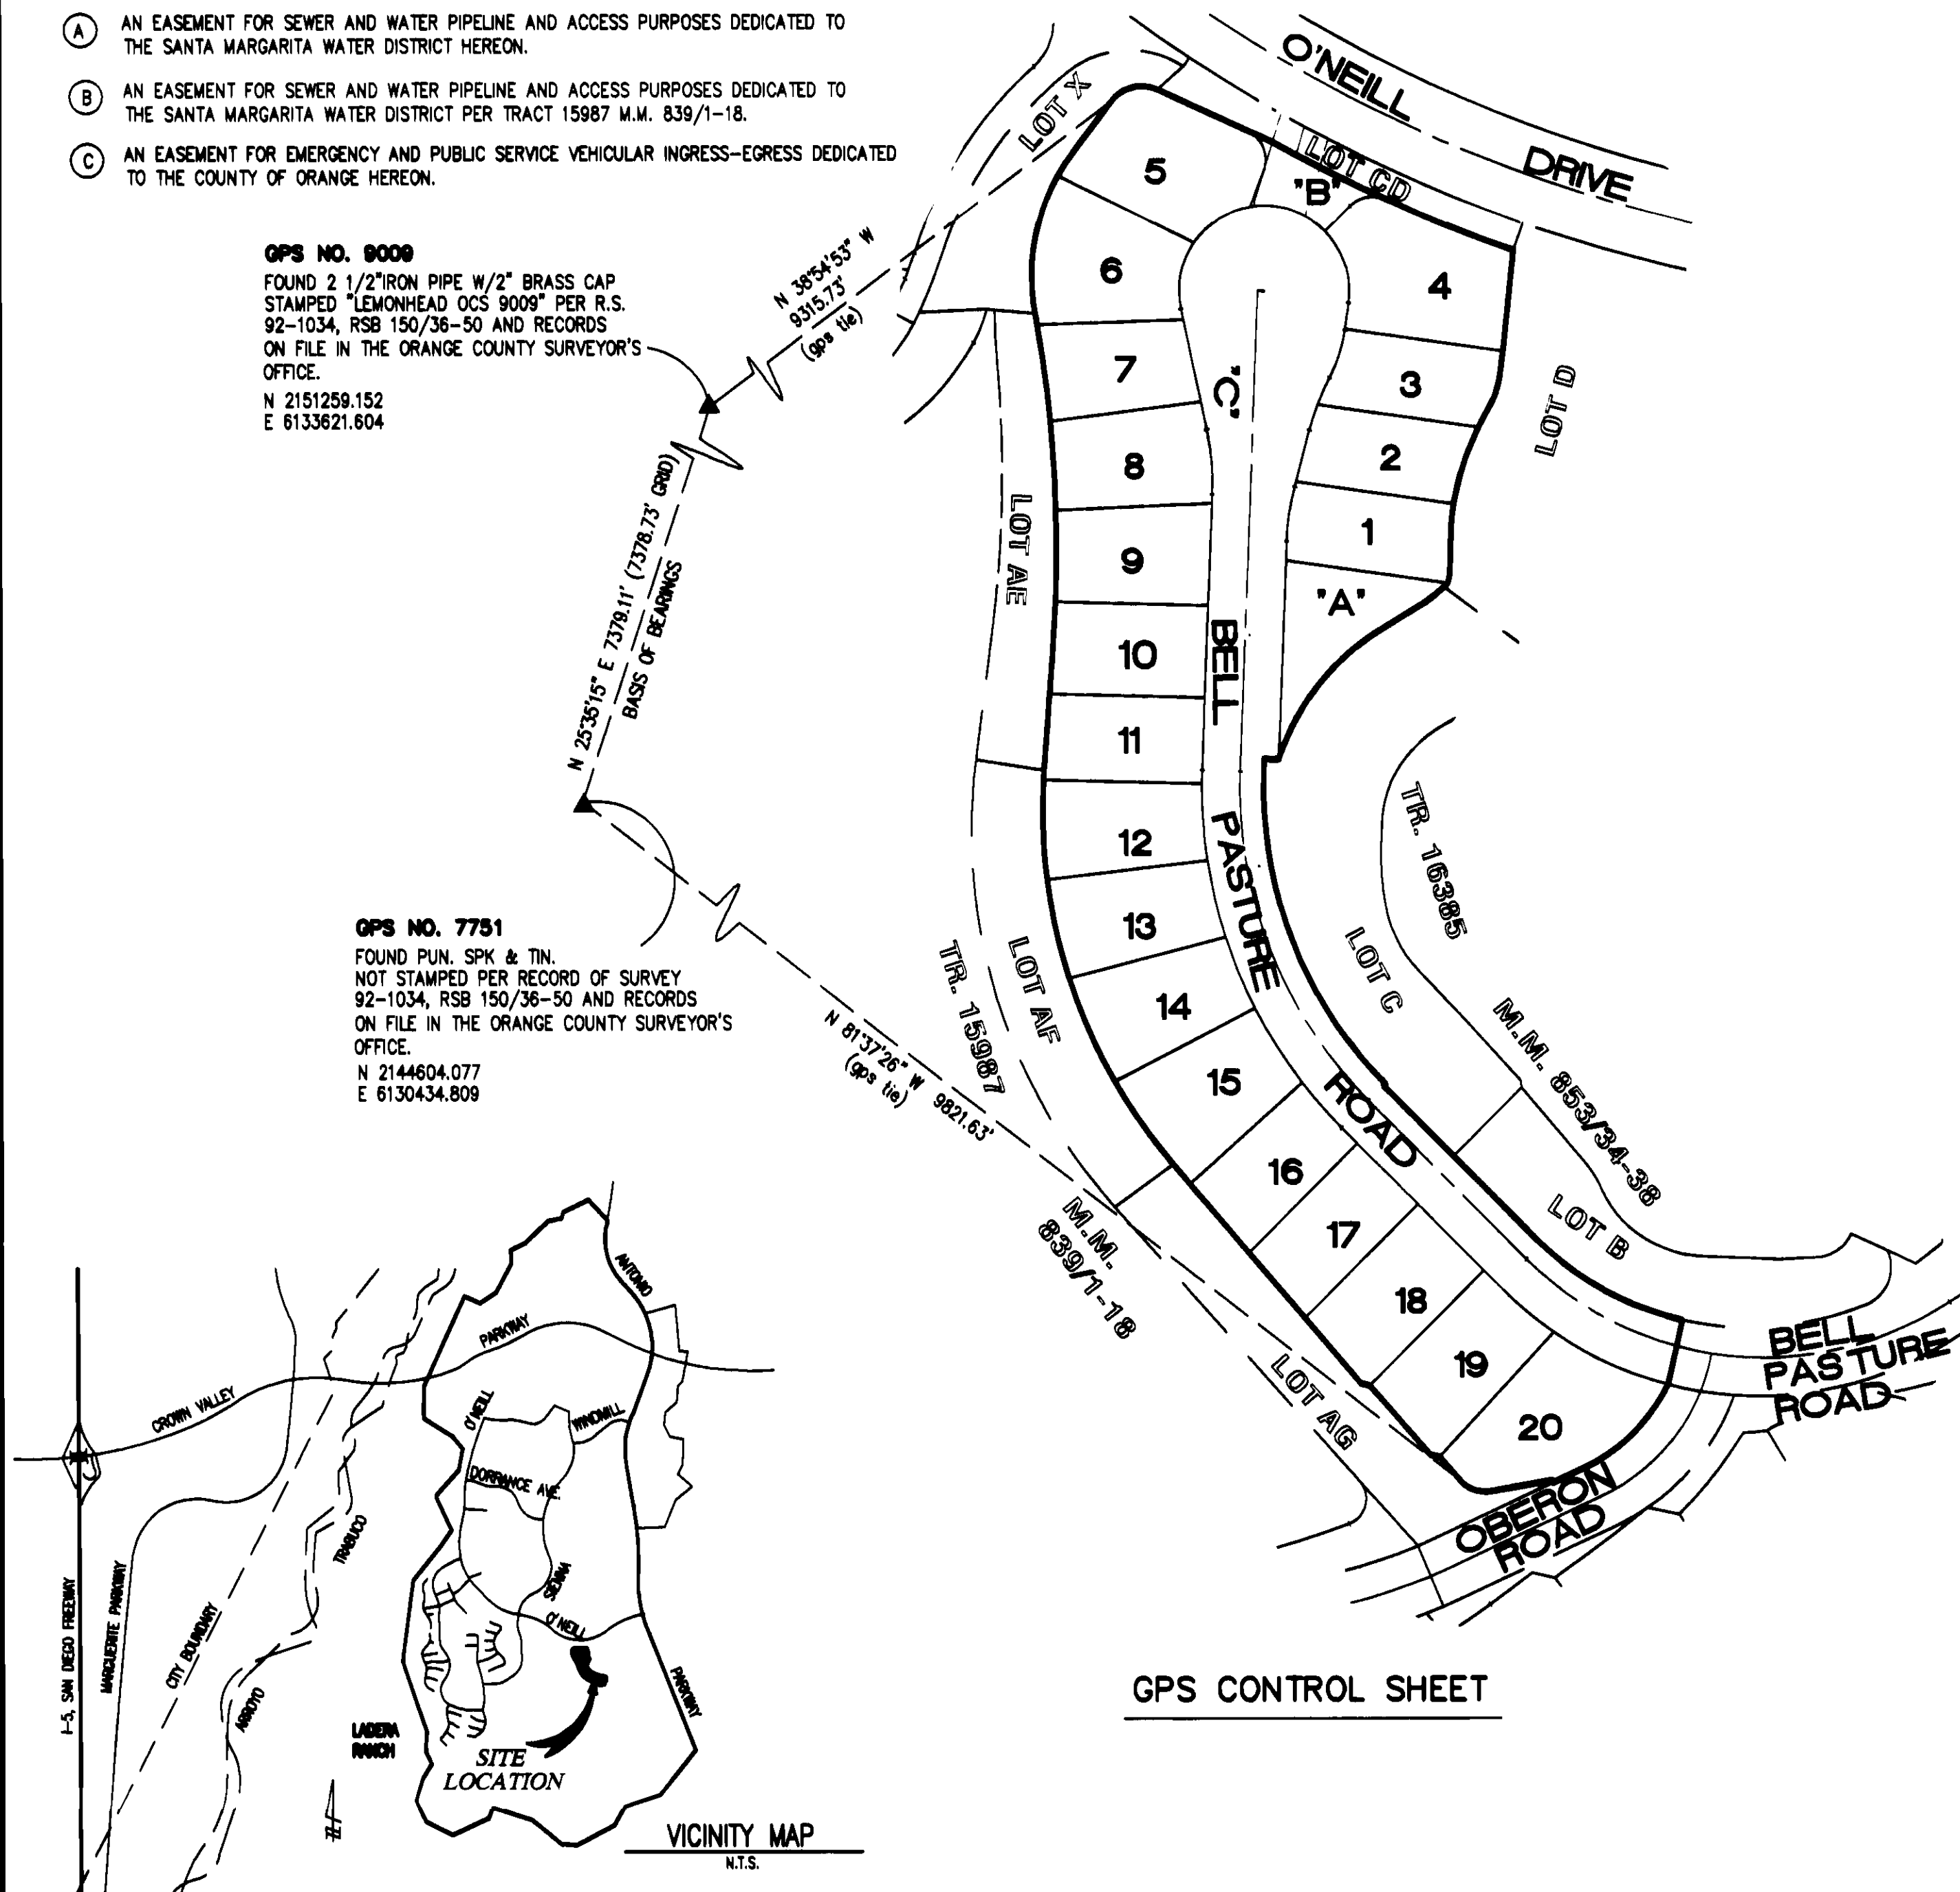

GPS CONTROL SHEET

SHEET 4 OF 4 SHEETS
20 NUMBERED LOTS AND
LOTS A, B & C
ACREAGE = 5.675 ACRES
A FINAL UNIT OF VESTING
TENTATIVE TRACT NO. 16384

TRACT NO. 16384

IN THE UNINCORPORATED TERRITORY OF THE COUNTY OF ORANGE,
STATE OF CALIFORNIA


ADAMS - STREETER CIVIL ENGINEERS, INC. JAN A. ADAMS, R.C.E. 21687
DATE OF SURVEY: DEC. 2002

SCALE: 1"=60'

LOT "A" IS NOT A SEPARATE BUILDING SITE AND IS FOR PARK PURPOSES.
LOT "B" IS NOT A SEPARATE BUILDING SITE AND IS FOR LANDSCAPE/OPEN SPACE PURPOSES.
LOT "C" IS NOT A SEPARATE BUILDING SITE AND IS FOR PRIVATE STREET.

SEE SHEET 3 FOR GPS CONTROL, BASIS OF BEARINGS,
MONUMENT AND EASEMENT NOTES.

ALL BEARINGS SHOWN ALONG THE TRACT BOUNDARY ARE
MEASURED AND RECORD PER TRACT NO. 15987 M.M.
839/1-18.

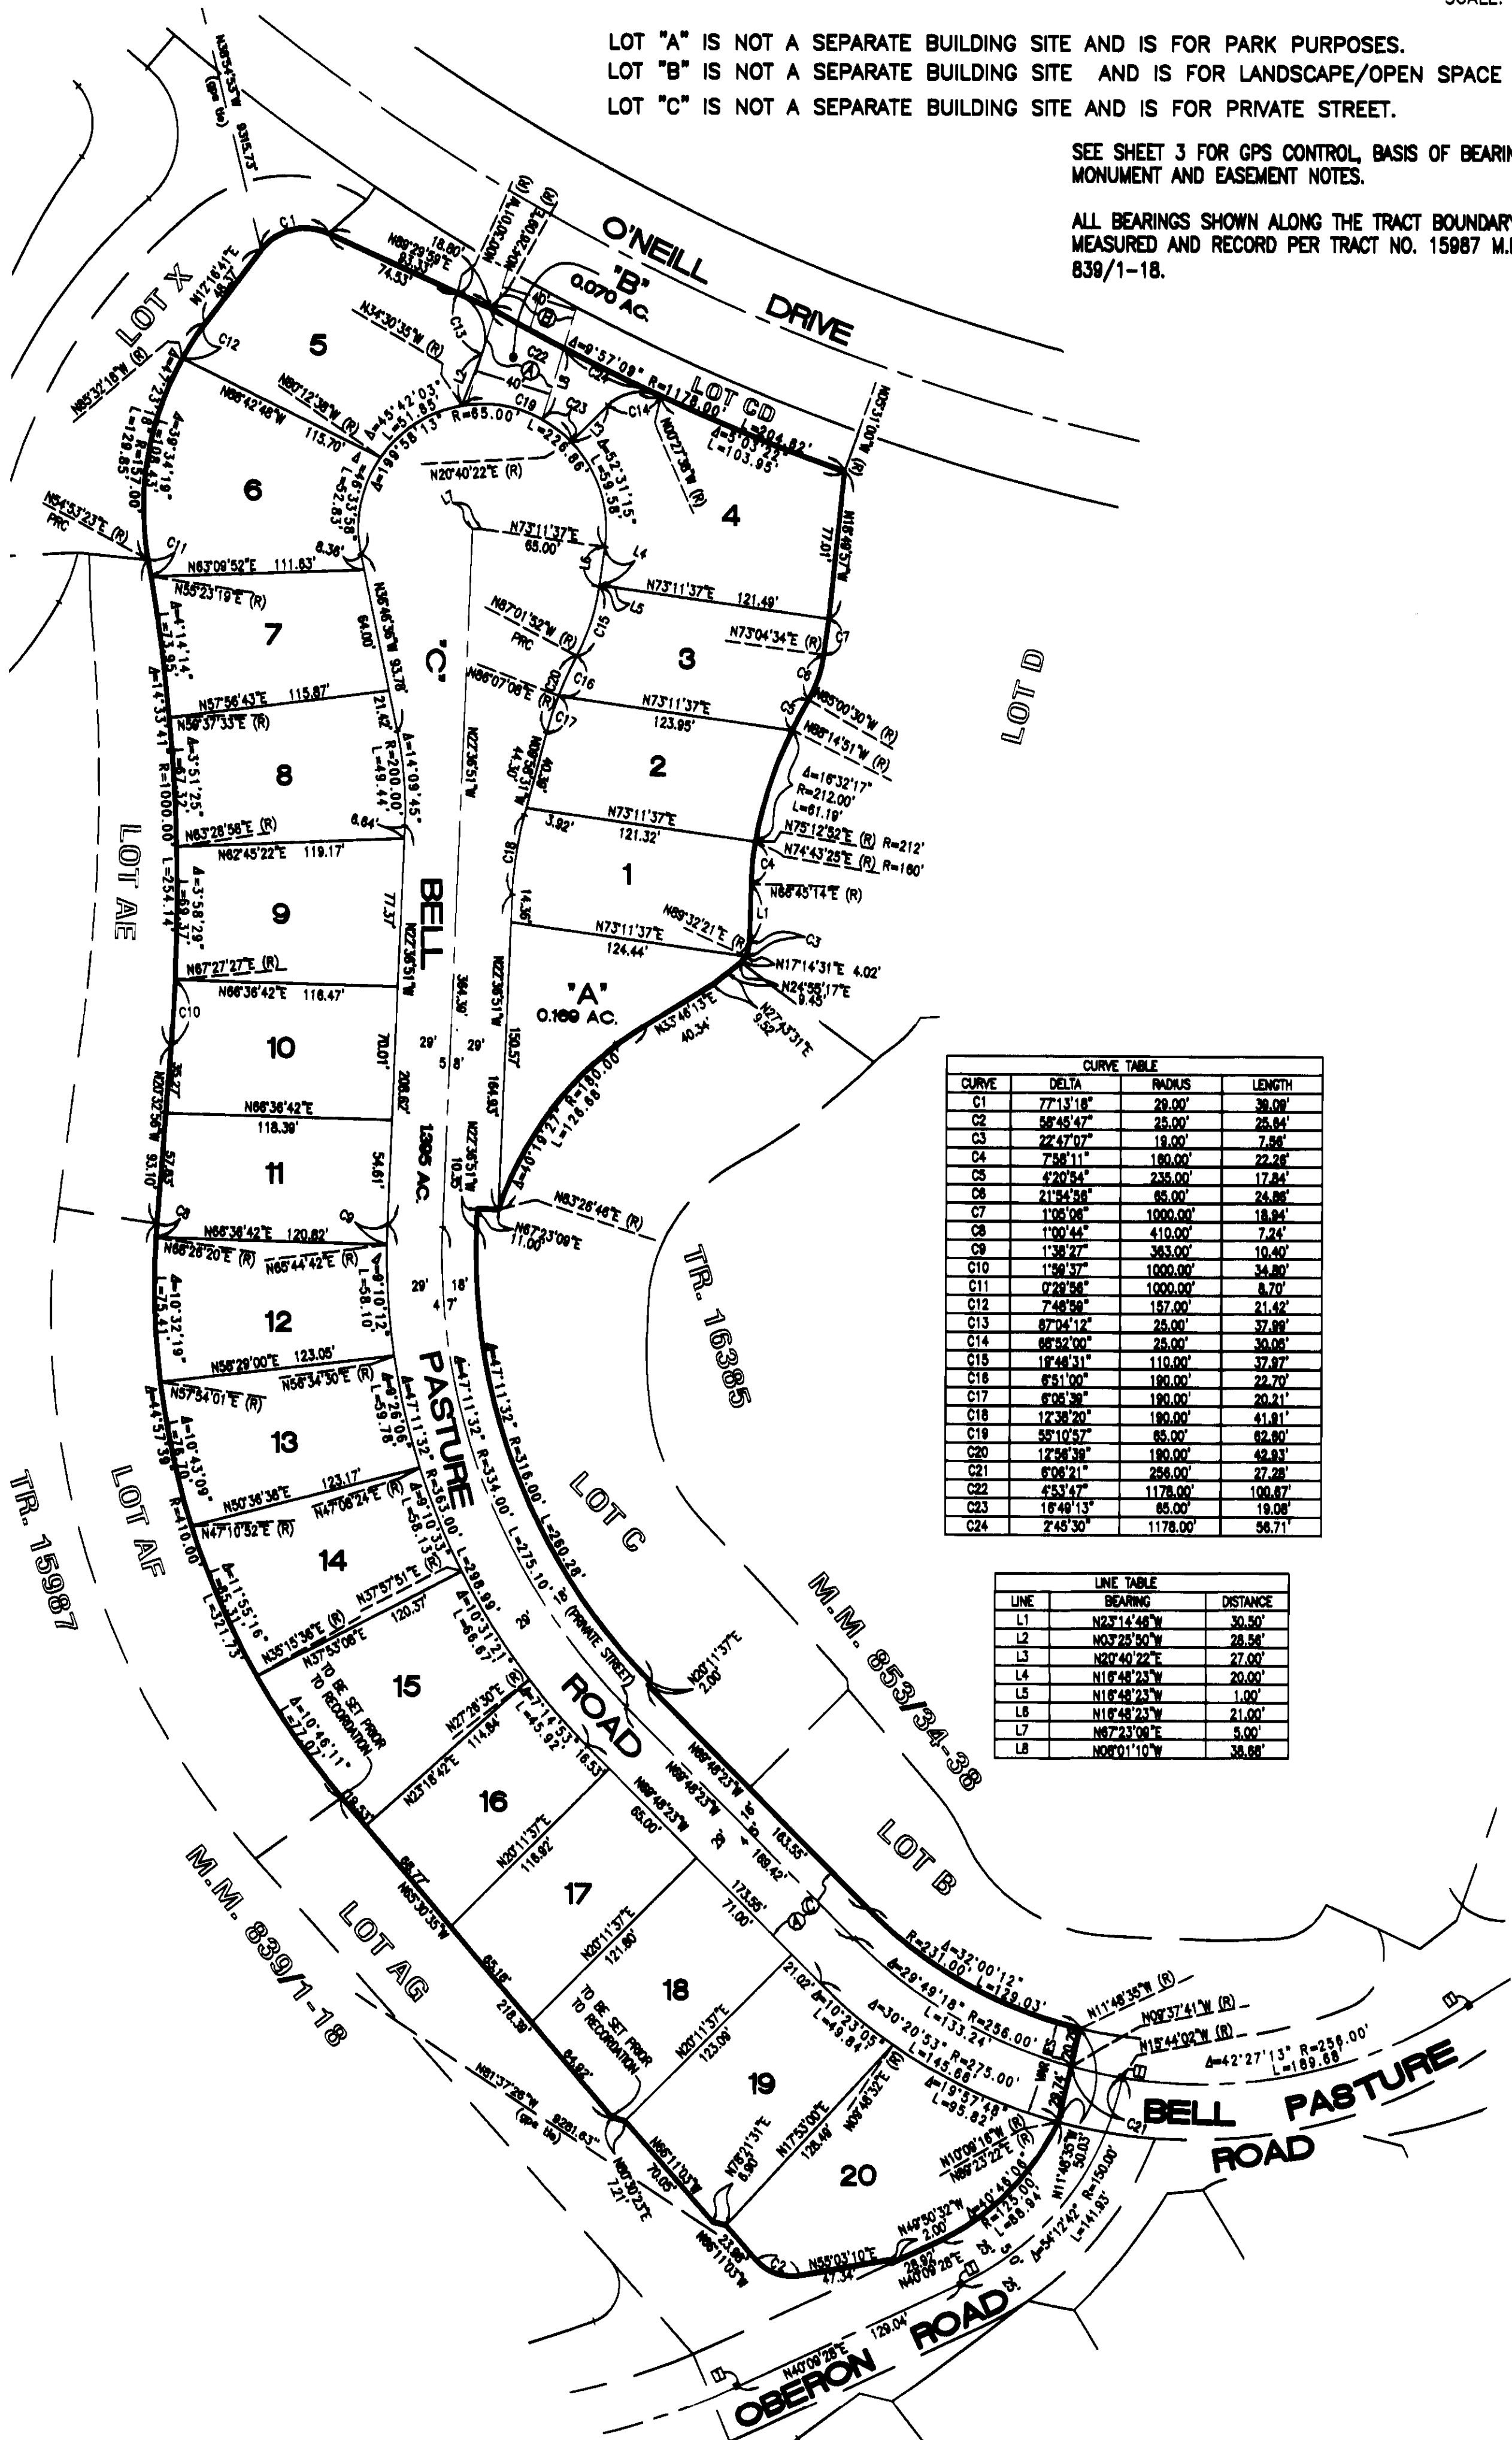

CURVE TABLE			
CURVE	DELTA	RADIUS	LENGTH
C1	77°13'18"	28.00'	36.08'
C2	58°45'47"	25.00'	25.84'
C3	22°47'07"	18.00'	7.68'
C4	7°58'11"	180.00'	22.28'
C5	4°20'54"	235.00'	17.84'
C6	21°54'58"	65.00'	24.88'
C7	1°05'08"	1000.00'	18.84'
C8	1°00'44"	410.00'	7.24'
C9	1°38'27"	363.00'	10.40'
C10	1°58'37"	1000.00'	34.80'
C11	0°28'58"	1000.00'	8.70'
C12	7°48'56"	157.00'	21.42'
C13	87°04'12"	25.00'	37.88'
C14	88°52'00"	25.00'	30.08'
C15	18°48'31"	110.00'	37.87'
C16	6°51'00"	180.00'	22.70'
C17	6°08'58"	180.00'	20.21'
C18	12°38'20"	180.00'	41.81'
C19	58°10'57"	65.00'	82.80'
C20	12°56'38"	180.00'	42.83'
C21	6°08'21"	258.00'	27.28'
C22	4°53'47"	1178.00'	100.87'
C23	18°48'13"	65.00'	19.08'
C24	2°45'30"	1178.00'	56.71'

LINE TABLE		
LINE	BEARING	DISTANCE
L1	N23°14'48"W	30.50'
L2	N02°25'50"W	28.56'
L3	N20°40'22"E	27.00'
L4	N18°48'23"W	20.00'
L5	N18°48'23"W	1.00'
L6	N18°48'23"W	21.00'
L7	N67°23'08"E	5.00'
L8	N08°01'10"W	38.88'