

SHEET 1 OF 5

7 NUMBERED LOTS AND LOTS "A-F"
ACREAGE = 5.578 ACRES
A PORTION OF TENTATIVE
TRACT NO. 16384
DATE OF SURVEY: MAY. 2003

TRACT NO. 16385

IN THE UNINCORPORATED TERRITORY OF THE COUNTY OF ORANGE,
STATE OF CALIFORNIA

BEING A SUBDIVISION OF LOTS 6, AH, AJ, AK, AND AL AS SHOWN ON TRACT NO. 15987 FILED IN BOOK 839,
PAGES 1 THROUGH 18, INCLUSIVE OF MISCELLANEOUS MAPS, TOGETHER WITH PARCEL 'A' OF LOT LINE
ADJUSTMENT LL 2003-021 RECORDED AS INSTRUMENT NO. 2003001091079, OFFICIAL RECORDS IN THE OFFICE
OF THE COUNTY RECORDER OF SAID COUNTY, STATE OF CALIFORNIA

ADAMS - STREETER CIVIL ENGINEERS, INC. JAN A. ADAMS, R.C.E. 21687

ACCEPTED AND FILED AT THE
REQUEST OF

FIRST AMERICAN TITLE INSURANCE COMPANY

DATE February 13, 2004
TIME 11:24am FEE \$ 19.00
INSTRUMENT # 20040000112626
BOOK 853 PAGE 34-38 m

TOM DALY
COUNTY - CLERK RECORDER

BY Julia Y. Gonzalez
DEPUTY

OWNER'S CERTIFICATE:

WE, THE UNDERSIGNED, BEING ALL PARTIES HAVING ANY RECORD TITLE INTEREST IN THE LAND COVERED
BY THIS MAP, DO HEREBY CONSENT TO THE PREPARATION AND RECORDATION OF SAID MAP, AS SHOWN
WITHIN THE DISTINCTIVE BORDER LINE.

WE ALSO HEREBY DEDICATE TO THE COUNTY OF ORANGE:

AN EASEMENT FOR EMERGENCY AND PUBLIC SERVICE VEHICULAR INGRESS-EGRESS PURPOSES
AS SHOWN HEREON.

WE ALSO DEDICATE TO THE SANTA MARGARITA WATER DISTRICT, THE EASEMENTS FOR SEWER, WATER
AND ACCESS PURPOSES AS SHOWN ON SAID MAP, WHICH EASEMENTS SHALL BE SUBJECT TO THE
SAME TERMS AND CONDITIONS AS ARE SHOWN IN THAT CERTAIN EASEMENT RECORDED SEPT. 18, 2002,
AS INST. NO. 20020799401, OF OFFICIAL RECORDS, COUNTY OF ORANGE.

STANDARD PACIFIC CORP. A DELAWARE CORPORATION

William C. Fischel
NAME: William C. Fischel
TITLE: Authorized Representative

Michael C. Battaglia
NAME: MICHAEL C. BATTAGLIA
TITLE: Authorized Representative

DMB LADERA, LLC., A DELAWARE LIMITED LIABILITY COMPANY
BY: RANCHO MISSION VIEJO, LLC, A DELAWARE LIMITED LIABILITY COMPANY
ITS AUTHORIZED AGENT AND MANAGER

Donald T. Stahlin
NAME: DONALD T. STAHLIN
TITLE: VICE PRESIDENT

Gregory S. Edwards
NAME: Gregory S. Edwards
TITLE: S.A.V.P. & CEO

NOTARY ACKNOWLEDGMENTS

STATE OF CALIFORNIA }
COUNTY OF Orange } ss

ON THIS 16th DAY OF OCTOBER, 2003, BEFORE ME, Kathleen M. Villari, A NOTARY
PUBLIC IN AND FOR SAID STATE, PERSONALLY APPEARED William C. Fischel, Michael C. Battaglia
PERSONALLY KNOWN TO ME (OR PROVED TO ME ON THE BASIS OF SATISFACTORY EVIDENCE) TO BE
THE PERSONS WHOSE NAMES ARE SUBSCRIBED TO THE WITHIN INSTRUMENT AND ACKNOWLEDGED TO ME
THAT THEY EXECUTED THE SAME IN THEIR AUTHORIZED CAPACITIES AND THAT BY THEIR SIGNATURES ON
THE INSTRUMENT THE PERSON OR THE ENTITY UPON BEHALF OF WHICH THE PERSONS ACTED, EXECUTED
THE INSTRUMENT.

WITNESS MY HAND:

Kathleen M. Villari
NOTARY PUBLIC IN AND FOR SAID STATE
KATHLEEN M. VILLARI
PRINT NAME

MY PRINCIPAL PLACE OF BUSINESS
IS IN Orange COUNTY

MY COMMISSION EXPIRES 8-15-2007

STATE OF CALIFORNIA }
COUNTY OF Orange } ss

ON THIS 16th DAY OF October, 2003, BEFORE ME, Diana L. Binks, A NOTARY
PUBLIC IN AND FOR SAID STATE, PERSONALLY APPEARED Donald T. Stahlin and Gregory S. Edwards
PERSONALLY KNOWN TO ME (OR PROVED TO ME ON THE BASIS OF SATISFACTORY EVIDENCE) TO BE
THE PERSONS WHOSE NAMES ARE SUBSCRIBED TO THE WITHIN INSTRUMENT AND ACKNOWLEDGED TO ME
THAT THEY EXECUTED THE SAME IN THEIR AUTHORIZED CAPACITIES AND THAT BY THEIR SIGNATURES ON
THE INSTRUMENT THE PERSON OR THE ENTITY UPON BEHALF OF WHICH THE PERSONS ACTED, EXECUTED
THE INSTRUMENT.

WITNESS MY HAND:

Diana L. Binks
NOTARY PUBLIC IN AND FOR SAID STATE
Diana L. BINKS
PRINT NAME

MY PRINCIPAL PLACE OF BUSINESS
IS IN Orange COUNTY

MY COMMISSION EXPIRES 12/12/06

PRIVATE STREETS NOTE

THE PRIVATE STREETS CONSTRUCTED WITHIN THIS MAP SHALL BE OWNED, OPERATED AND
MAINTAINED BY THE DEVELOPER, SUCCESSORS OR ASSIGNS. THE COUNTY OF ORANGE SHALL
HAVE NO RESPONSIBILITY THEREFORE UNLESS PURSUANT TO APPROPRIATE SECTIONS OF THE
STREETS AND HIGHWAYS CODE OF THE STATE OF CALIFORNIA, THE SAID PRIVATE STREETS
HAVE BEEN ACCEPTED INTO THE COUNTY ROAD SYSTEM BY APPROPRIATE RESOLUTION OF
THE ORANGE COUNTY BOARD OF SUPERVISORS.

SIGNATURE OMISSIONS

PURSUANT TO THE PROVISIONS OF SECTION 66436 (a)(3)(A)(C) OF THE SUBDIVISION MAP ACT,
THE FOLLOWING SIGNATURES HAVE BEEN OMITTED:

LADERA DEVELOPMENT COMPANY, LLC, HOLDER OF OIL, GAS AND MINERAL RIGHTS RECORDED
ON DECEMBER 10, 1996 AS INSTRUMENT NO. 19960624029 OF OFFICIAL RECORDS.

COUNTY OF ORANGE HOLDER OF AN EASEMENT FOR SIDEWALK AND INCIDENTAL PURPOSES
AS DEDICATED ON TRACT NO. 15987, FILED IN BOOK 839, PAGE 1 THROUGH 18 OF
MISCELLANEOUS MAPS.


DMB LADERA, L.L.C., HOLDER OF EASEMENTS RESERVED IN A DEED RECORDED
ON SEPTEMBER 16, 2003 AS INST. NO. 2003001135586 OF OFFICIAL RECORDS.

SOUTHERN CALIFORNIA GAS COMPANY, A CALIFORNIA CORPORATION,
HOLDER OF AN EASEMENT FOR FACILITIES AND INCIDENTAL PURPOSES
RECORDED NOVEMBER 25, 2003 AS INSTRUMENT NO. 2003001423369 OF OFFICIAL RECORDS.

ENGINEER'S STATEMENT

THIS MAP WAS PREPARED BY ME OR UNDER MY DIRECTION AND IS BASED UPON A FIELD SURVEY IN
CONFORMANCE WITH THE REQUIREMENTS OF THE SUBDIVISION MAP ACT AND LOCAL ORDINANCE AT THE
REQUEST OF STANDARD PACIFIC CORP. AND DMB LADERA, LLC, IN MAY 2003. I HEREBY STATE THAT ALL
MONUMENTS ARE OF THE CHARACTER AND OCCUPY THE POSITIONS INDICATED, OR THAT THEY WILL BE SET IN
SUCH POSITIONS; AND THAT SAID MONUMENTS ARE SUFFICIENT TO ENABLE THE SURVEY TO BE RETRACED. I
HEREBY STATE THAT THIS MAP SUBSTANTIALLY CONFORMS TO THE CONDITIONALLY APPROVED TENTATIVE MAP.

JAN A. ADAMS, R.C.E. 21687
EXPIRES: 9/30/05

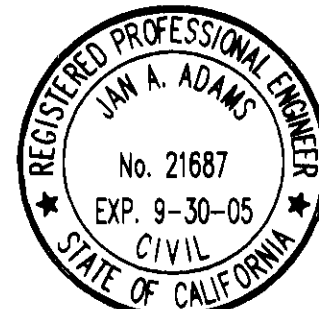


COUNTY SURVEYOR'S STATEMENT

I HEREBY STATE THAT I HAVE EXAMINED THIS MAP AND HAVE FOUND IT TO BE SUBSTANTIALLY IN
CONFORMANCE WITH THE TENTATIVE MAP AS FILED WITH, AMENDED AND APPROVED BY THE ORANGE
COUNTY SUBDIVISION COMMITTEE; THAT ALL PROVISIONS OF THE SUBDIVISION MAP ACT AND COUNTY
SUBDIVISION REGULATIONS HAVE BEEN COMPLIED WITH AND I AM SATISFIED SAID MAP IS TECHNICALLY
CORRECT.

DATED THIS 2ND DAY OF FEBRUARY, 2004

Michael K. Sullivan
JOHN CANAS, COUNTY SURVEYOR
LS 4408 EXPIRATION DATE: 9-30-05 BY: MICHAEL K. SULLIVAN, DEPUTY
LS 6254 EXPIRES 6/30/06

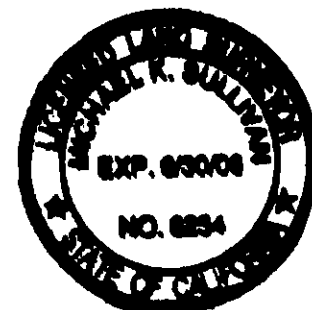

COUNTY TREASURER - TAX COLLECTOR'S CERTIFICATE

STATE OF CALIFORNIA }
COUNTY OF ORANGE } ss

I HEREBY CERTIFY THAT ACCORDING TO THE RECORDS OF MY OFFICE THERE ARE NO LIENS AGAINST THE
LAND COVERED BY THIS MAP OR ANY PART THEREOF FOR UNPAID STATE, COUNTY, MUNICIPAL OR LOCAL
TAXES OR SPECIAL ASSESSMENTS COLLECTED AS TAXES, EXCEPT TAXES OR SPECIAL ASSESSMENTS
COLLECTED AS TAXES NOT YET PAYABLE.

AND DO ALSO CERTIFY TO THE RECORDER OF ORANGE COUNTY THAT THE PROVISIONS OF THE
SUBDIVISION MAP ACT HAVE BEEN COMPLIED WITH REGARDING DEPOSITS TO SECURE THE PAYMENT OF
TAXES OR SPECIAL ASSESSMENTS COLLECTED AS TAXES ON THE LAND COVERED BY THIS MAP.

DATED THIS 28th DAY OF January, 2004

John M. W. Moorlach BY Maar Jorgensen
COUNTY TREASURER - TAX COLLECTOR DEPUTY TREASURER - TAX COLLECTOR

CLERK OF THE BOARD OF SUPERVISOR'S CERTIFICATE

STATE OF CALIFORNIA }
COUNTY OF ORANGE } ss

I HEREBY CERTIFY THAT THIS MAP WAS PRESENTED FOR APPROVAL TO THE BOARD OF SUPERVISORS OF
ORANGE COUNTY AT A REGULAR MEETING THEREOF HELD ON THE 10th DAY OF FEBRUARY,
2004, AND THAT THEREUPON SAID BOARD DID, BY AN ORDER DULY PASSED AND ENTERED, APPROVE
SAID MAP.

AND DID ACCEPT ON BEHALF OF THE COUNTY OF ORANGE:

AN EASEMENT FOR EMERGENCY AND PUBLIC SERVICE VEHICULAR INGRESS-EGRESS PURPOSES,
AS DEDICATED.

AND DID ALSO APPROVE SUBJECT MAP PURSUANT TO THE PROVISIONS OF SECTION 66436 (a)(3)(A) OF
THE SUBDIVISION MAP ACT.

DATED THIS 10th DAY OF FEBRUARY, 2004

Darlene J. Bloom
DARLENE J. BLOOM, CLERK OF THE BOARD OF SUPERVISORS



CERTIFICATE OF ACCEPTANCE

THE UNDERSIGNED, BEING THE DULY APPOINTED AGENT OF THE SANTA MARGARITA WATER DISTRICT,
A PUBLIC CORPORATION OF ORANGE COUNTY, CALIFORNIA, PURSUANT TO ITS RESOLUTION NO. 88-10-2,
DOES HEREBY ACCEPT ON BEHALF OF SAID DISTRICT THE EASEMENTS FOR SEWER, WATER AND ACCESS
PURPOSES, AS DEDICATED AND AS SHOWN ON THIS TRACT MAP, BY AND BETWEEN THE SANTA MARGARITA
WATER DISTRICT AND STANDARD PACIFIC CORP. AND DMB LADERA, LLC. DOES HEREBY CERTIFY THAT THE
GRANTEE CONSENTS TO THE RECORDATION OF SAID TRACT.

BY: Daniel R. Ferons
DANIEL R. FERONS, CHIEF ENGINEER
SANTA MARGARITA WATER DISTRICT

STATE OF CALIFORNIA }
COUNTY OF ORANGE } ss

ON THIS 20th DAY OF OCTOBER, 2003, BEFORE ME, Cindy R. Lane, A NOTARY
PUBLIC IN AND FOR SAID STATE, PERSONALLY APPEARED Daniel R. Ferons, PERSONALLY KNOWN TO ME
(OR PROVED TO ME ON THE BASIS OF SATISFACTORY EVIDENCE) TO BE THE PERSON WHOSE NAME IS
SUBSCRIBED TO THE WITHIN INSTRUMENT AND ACKNOWLEDGED TO ME THAT HE EXECUTED THE SAME IN
HIS AUTHORIZED CAPACITY AND THAT BY HIS SIGNATURE ON THE INSTRUMENT THE PERSON, OR THE
ENTITY UPON BEHALF OF WHICH THE PERSON ACTED, EXECUTED THE INSTRUMENT.

WITNESS MY HAND:

Cindy R. Lane
NOTARY PUBLIC IN AND FOR SAID STATE
CINDY R. LANE
PRINT NAME

MY PRINCIPAL PLACE OF BUSINESS
IS IN ORANGE COUNTY

MY COMMISSION EXPIRES 2/20/05

SHEET 2 OF 5

7 NUMBERED LOTS AND LOTS "A-F"
ACREAGE = 5.578 ACRES

A PORTION OF TENTATIVE
TRACT NO. 16384

DATE OF SURVEY: MAY. 2003

TRACT NO. 16385

IN THE UNINCORPORATED TERRITORY OF THE COUNTY OF ORANGE,
STATE OF CALIFORNIA

ADAMS - STREETER CIVIL ENGINEERS, INC. JAN A. ADAMS, R.C.E. 21687

OWNER'S CERTIFICATE (CONT.):

DMB LADERA, LLC. A DELAWARE LIMITED LIABILITY COMPANY

BENEFICIARY UNDER A DEED OF TRUST RECORDED ON SEPTEMBER 16, 2003 AS INSTRUMENT NO.
2003001135588 OF OFFICIAL RECORDS.

BY: RANCHO MISSION VIEJO, LLC, A DELAWARE LIMITED LIABILITY COMPANY,
ITS AUTHORIZED AGENT AND MANAGER.

BY: [Signature]
PRINT NAME: Donald T. Starkin
PRINT TITLE: V.P.

BY: [Signature]
PRINT NAME: John V. Markel
PRINT TITLE: V.P.

NOTARY ACKNOWLEDGMENTS

STATE OF CALIFORNIA }
COUNTY OF ORANGE }ss

ON THIS 29th DAY OF December, 2003, BEFORE ME, Diana L. Binks, A NOTARY
PUBLIC IN AND FOR SAID STATE, PERSONALLY APPEARED Donald T. Starkin & John V. Markel
PERSONALLY KNOWN TO ME (OR ~~PROVED TO ME ON THE BASIS OF SATISFACTORY EVIDENCE~~) TO BE
THE PERSONS WHOSE NAMES ARE SUBSCRIBED TO THE WITHIN INSTRUMENT AND ACKNOWLEDGED TO ME
THAT THEY EXECUTED THE SAME IN THEIR AUTHORIZED CAPACITIES AND THAT BY THEIR SIGNATURES ON
THE INSTRUMENT THE PERSON OR THE ENTITY UPON BEHALF OF WHICH THE PERSONS ACTED, EXECUTED
THE INSTRUMENT.

WITNESS MY HAND:

Diana L. Binks
NOTARY PUBLIC IN AND FOR SAID STATE

Diana L. Binks
PRINT NAME

MY PRINCIPAL PLACE OF BUSINESS
IS IN orange COUNTY

MY COMMISSION EXPIRES 12/12/06

853

36

SHEET 3 OF 5

7 NUMBERED LOTS AND LOTS "A-F"
ACREAGE = 5.578 ACRES
A PORTION OF TENTATIVE
TRACT NO. 16384

TRACT NO. 16385

IN THE UNINCORPORATED TERRITORY OF THE COUNTY OF ORANGE,
STATE OF CALIFORNIA

ADAMS - STREETER CIVIL ENGINEERS, INC. JAN A. ADAMS, R.C.E. 21687
DATE OF SURVEY: MAY 2003



SCALE: 1"=60'

MONUMENT NOTES:

1. ● 2" IRON PIPE, TAGGED "R.C.E. 21687" TO BE SET PRIOR TO RECORDATION.
2. ■ 8" SPIKE AND WASHER STAMPED "L.S. 5557" IN ASPHALT PAVING OR LEAD, TACK AND TAG "L.S. 5557" IN CONCRETE OR 1" IRON PIPE, TAGGED "L.S. 5557" TO BE SET PER TRACT 15987, MM 839/1-18.
3. ■ 1" IRON PIPE, TAGGED "P.L.S. 5557", OR SPIKE AND WASHER, STAMPED "P.L.S. 5557", OR LEAD, TACK AND TAG "P.L.S. 5557" TO BE SET PER TR. 16025 M.M. 812/40-48.
4. 1" IRON PIPE, TAGGED "R.C.E. 21687", OR SPIKE AND WASHER, STAMPED "R.C.E. 21687", OR LEAD, TACK AND TAG "R.C.E. 21687" TO BE SET AT ALL LOT CORNERS, EXCEPT AT LOT CORNERS THAT ABUT A STREET, WHICH WILL BE SET ON A 9.75' OFFSET OUTSIDE THE TRUE LOT CORNER ON A PROLONGATION OF THE SIDE LOT LINE BY A LEAD, TACK AND TAG "R.C.E. 21687" IN THE TOP OF ADJACENT CONCRETE CURB, UNLESS OTHERWISE NOTED.
5. 8" SPIKE AND WASHER STAMPED "RCE 21687" IN ASPHALT PAVING OR LEAD, TACK AND TAG "R.C.E. 21687" IN CONCRETE OR 1" IRON PIPE, TAGGED "RCE 21687" TO BE SET AT ALL CENTERLINE INTERSECTIONS, B.C.'S, E.C.'S AND ALL OTHER CENTERLINE POINTS OF CONTROL, UNLESS OTHERWISE NOTED.
6. ALL MONUMENTS SHOWN AS "TO BE SET" WILL BE SET 90 DAYS AFTER THE ACCEPTANCE OF THE FINAL IMPROVEMENTS.
7. NO MONUMENTS TO BE SET AT BC'S AND EC'S OF STREET RIGHT OF WAY LINES.
8. ▲ FOUND GPS HORIZONTAL CONTROL POINT PER RECORDS ON FILE IN THE ORANGE COUNTY SURVEYOR'S OFFICE.
9. 2" IRON PIPE TAGGED "RCE 21687", OR SPIKE AND WASHER STAMPED "RCE 21687", OR LEAD, TACK AND TAG STAMPED "RCE 21687", OR NAIL AND TAG STAMPED "RCE 21687", OR A TAG STAMPED "RCE 21687" SECURED WITH EPOXY TO BE SET AT ALL TRACT BOUNDARY CORNERS, UNLESS OTHERWISE NOTED.

BASIS OF BEARINGS

THE BEARINGS SHOWN HEREON ARE BASED ON THE BEARING BETWEEN ORANGE COUNTY SURVEYOR'S HORIZONTAL CONTROL STATION "GPS NO. 7751" AND "GPS NO. 9009", BEING N. 25°35'15" E., PER RECORDS ON FILE IN THE OFFICE OF THE ORANGE COUNTY SURVEYOR.

DATUM STATEMENT

COORDINATES SHOWN HEREON ARE BASED ON THE CALIFORNIA COORDINATE SYSTEM (CCS83) ZONE VI, 1983 NAD (1991.35 EPOCH, O.C.S. GPS ADJUSTMENT). ALL DISTANCES SHOWN HEREON ARE GROUND, UNLESS OTHERWISE NOTED. TO OBTAIN GRID DISTANCE MULTIPLY GROUND DISTANCE BY 0.99994794.

AUTOMATIC FIRE SPRINKLER NOTE:

ALL RESIDENTIAL STRUCTURES EXCEEDING 5,500 SQUARE FEET AND ALL STRUCTURES EXCEEDING FIRE DEPARTMENT ACCESS REQUIREMENTS SHALL BE PROTECTED BY AN AUTOMATIC FIRE SPRINKLER SYSTEM, IN A MANNER MEETING THE APPROVAL OF THE FIRE CHIEF.

SPECIAL FIRE PROTECTION NOTE:

PROPERTY IS CONDITIONALLY EXCLUDED FROM A SPECIAL FIRE PROTECTION AREA. ALL REQUIREMENTS FOR DEVELOPMENT AND CONSTRUCTION WITHIN A "SPECIAL FIRE PROTECTION AREA" INCLUDING INCREASED STREET WIDTHS AND CLASS A ROOF ASSEMBLIES WILL BE MET.

EASEMENT NOTES:


- AN EASEMENT FOR EMERGENCY AND PUBLIC SERVICE VEHICULAR INGRESS-EGRESS PURPOSES DEDICATED TO THE COUNTY OF ORANGE HEREON.
- AN EASEMENT FOR WATER, RECYCLED WATER, SEWER AND ACCESS DEDICATED TO THE SANTA MARGARITA WATER DISTRICT HEREON.
- AN EASEMENT FOR SIDEWALK PURPOSES DEDICATED TO THE COUNTY OF ORANGE PER TR. 15987 M.M. 839/1-18.
- AN EASEMENT FOR WATER PURPOSES DEDICATED TO THE SANTA MARGARITA WATER DISTRICT HEREON.

GPS NO. 9009

FOUND 2 1/2" IRON PIPE W/2" BRASS CAP
STAMPED "LEMONHEAD OCS 9009" PER R.S.
92-1034, RSB 150/36-50 AND RECORDS
ON FILE IN THE ORANGE COUNTY SURVEYOR'S
OFFICE.
N 2151259.152
E 6133621.604

GPS NO. 7751

FOUND PUN. SPK & TIN.
NOT STAMPED PER RECORD OF SURVEY
92-1034, RSB 150/36-50 AND RECORDS
ON FILE IN THE ORANGE COUNTY SURVEYOR'S
OFFICE.
N 2144604.077
E 6130434.809

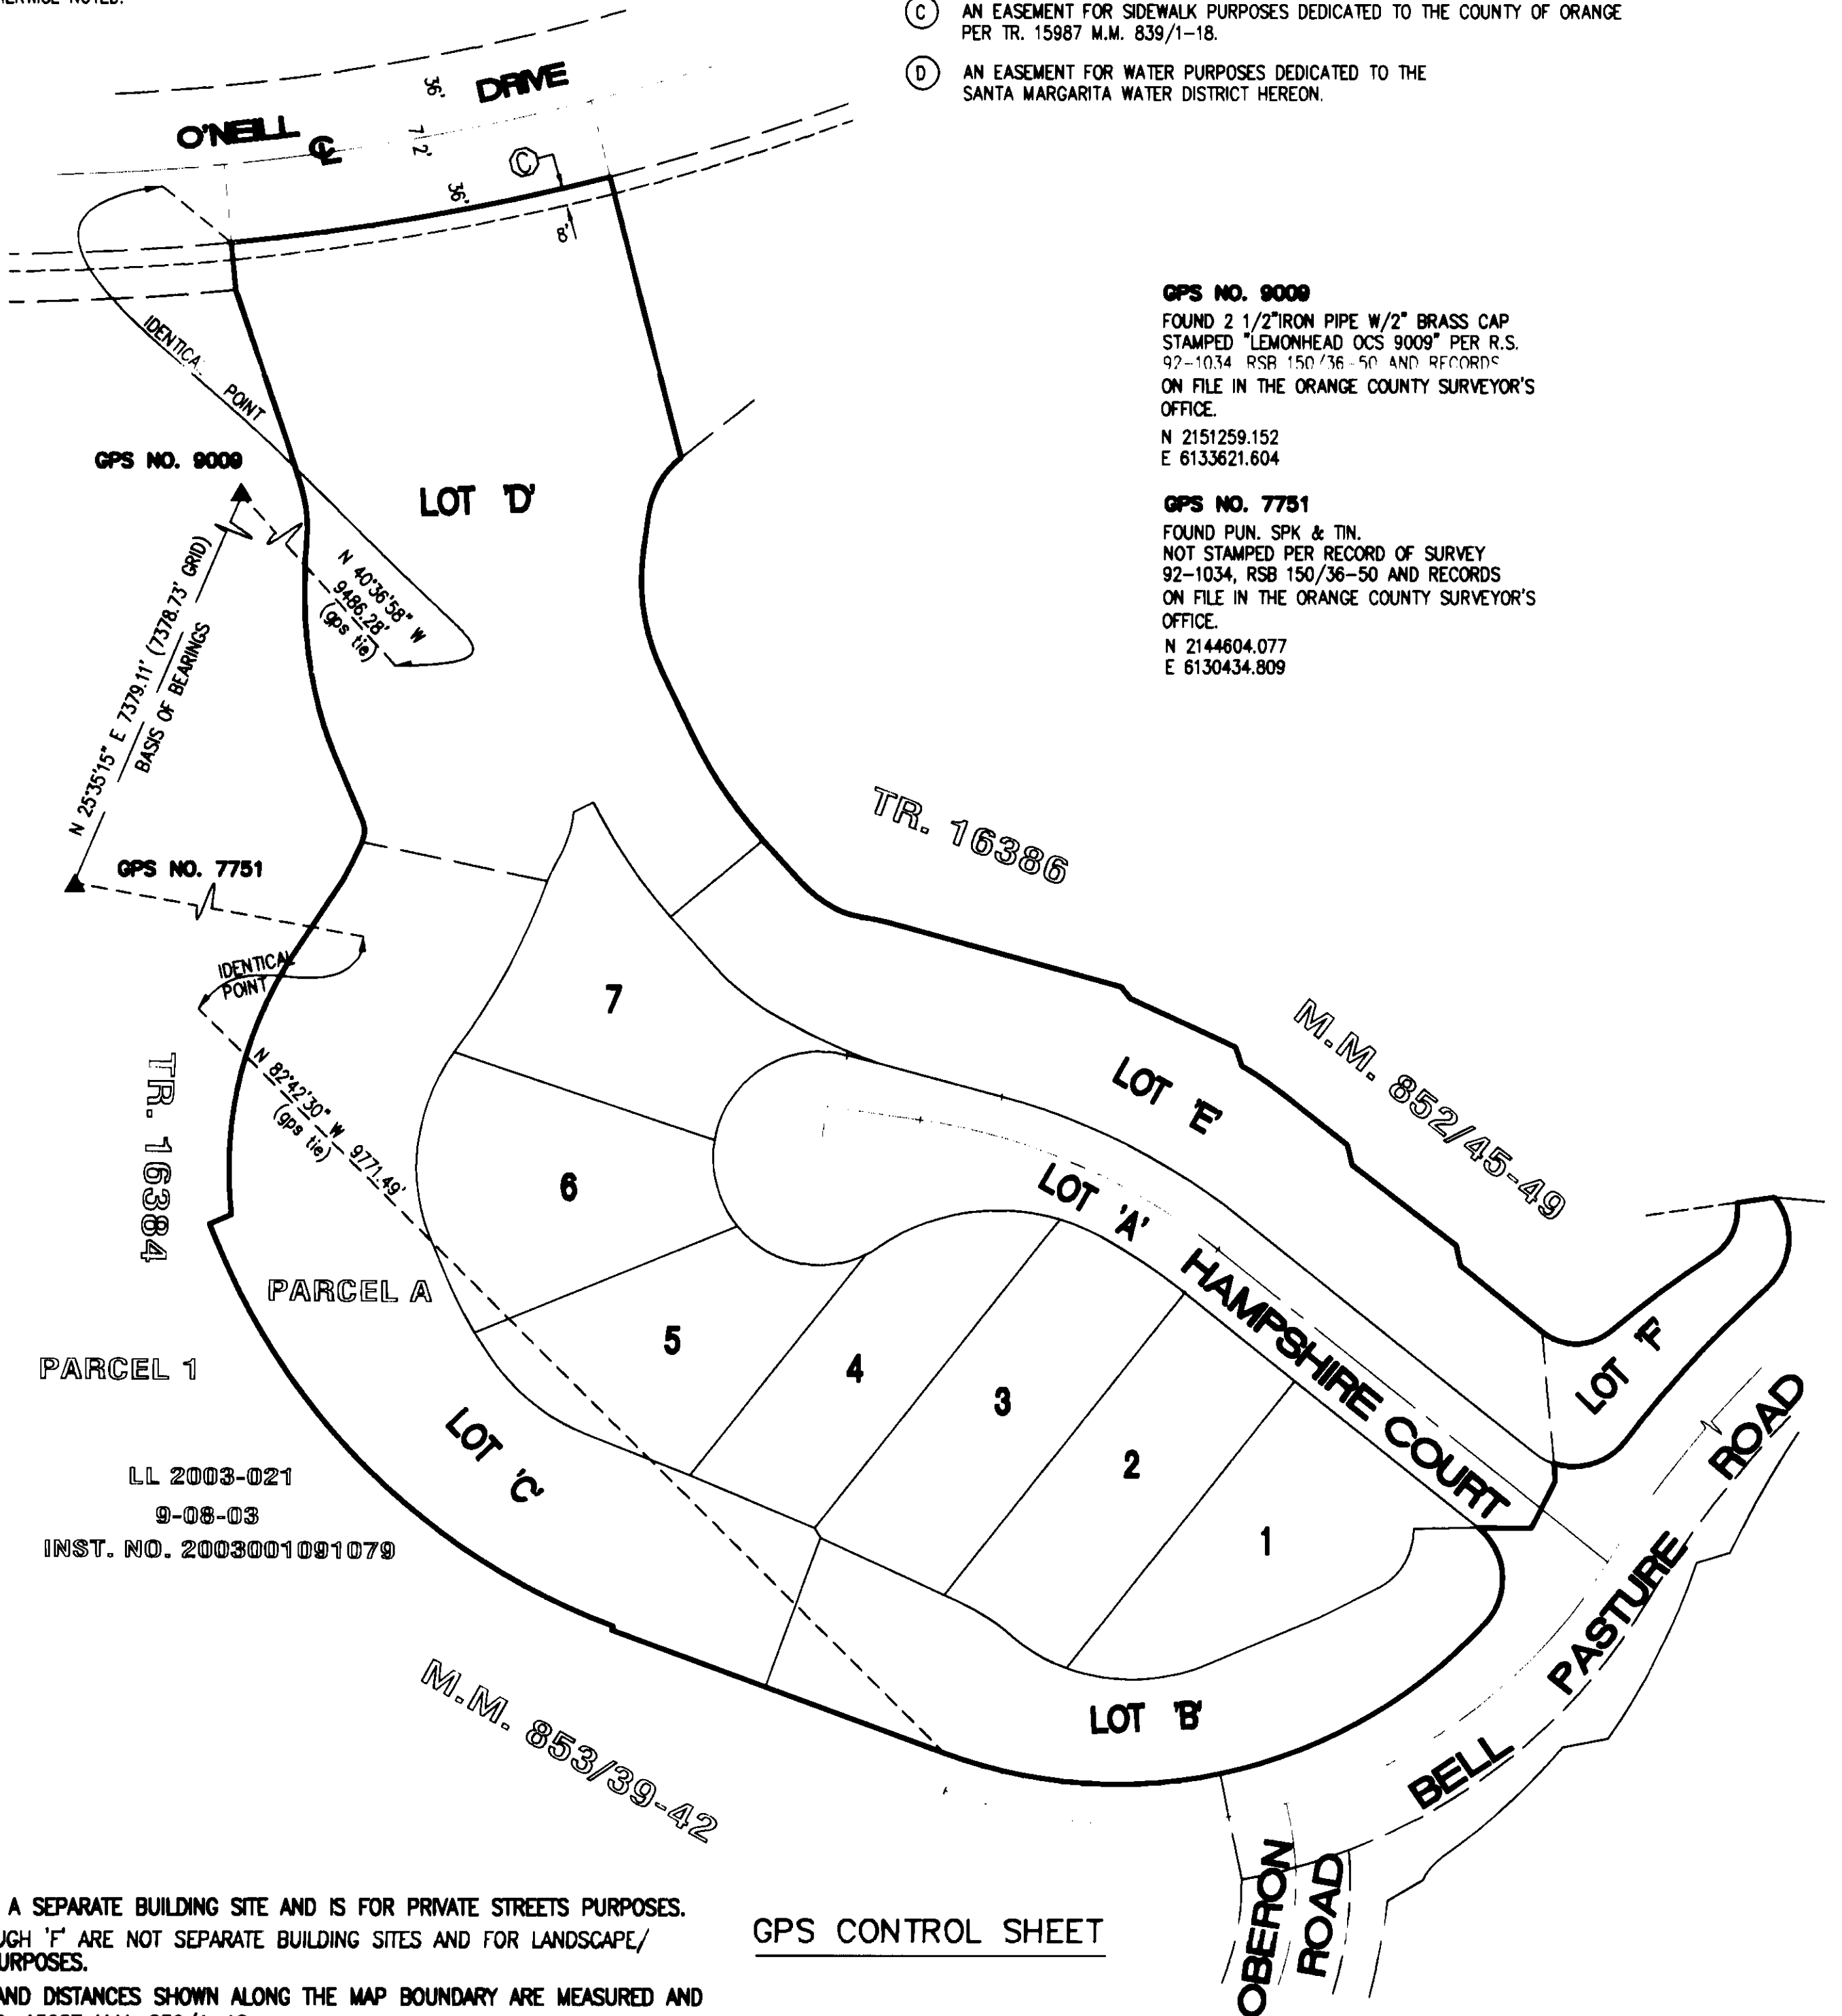

LOT 'A' IS NOT A SEPARATE BUILDING SITE AND IS FOR PRIVATE STREETS PURPOSES.
LOTS 'B' THROUGH 'F' ARE NOT SEPARATE BUILDING SITES AND FOR LANDSCAPE/
OPEN SPACE PURPOSES.
ALL BEARINGS AND DISTANCES SHOWN ALONG THE MAP BOUNDARY ARE MEASURED AND
RECORD PER TR. 15987 M.M. 839/1-18.

GPS CONTROL SHEET


SHEET 4 OF 5

7 NUMBERED LOTS AND LOTS "A-F"
ACREAGE = 5.578 ACRES
A PORTION OF TENTATIVE
TRACT NO. 16384
SCALE: 1" = 50'

TRACT NO. 16385

IN THE UNINCORPORATED TERRITORY OF THE COUNTY OF ORANGE,
STATE OF CALIFORNIA

ADAMS - STREETER CIVIL ENGINEERS, INC. JAN A. ADAMS, R.C.E. 21687
DATE OF SURVEY: MAY 2003

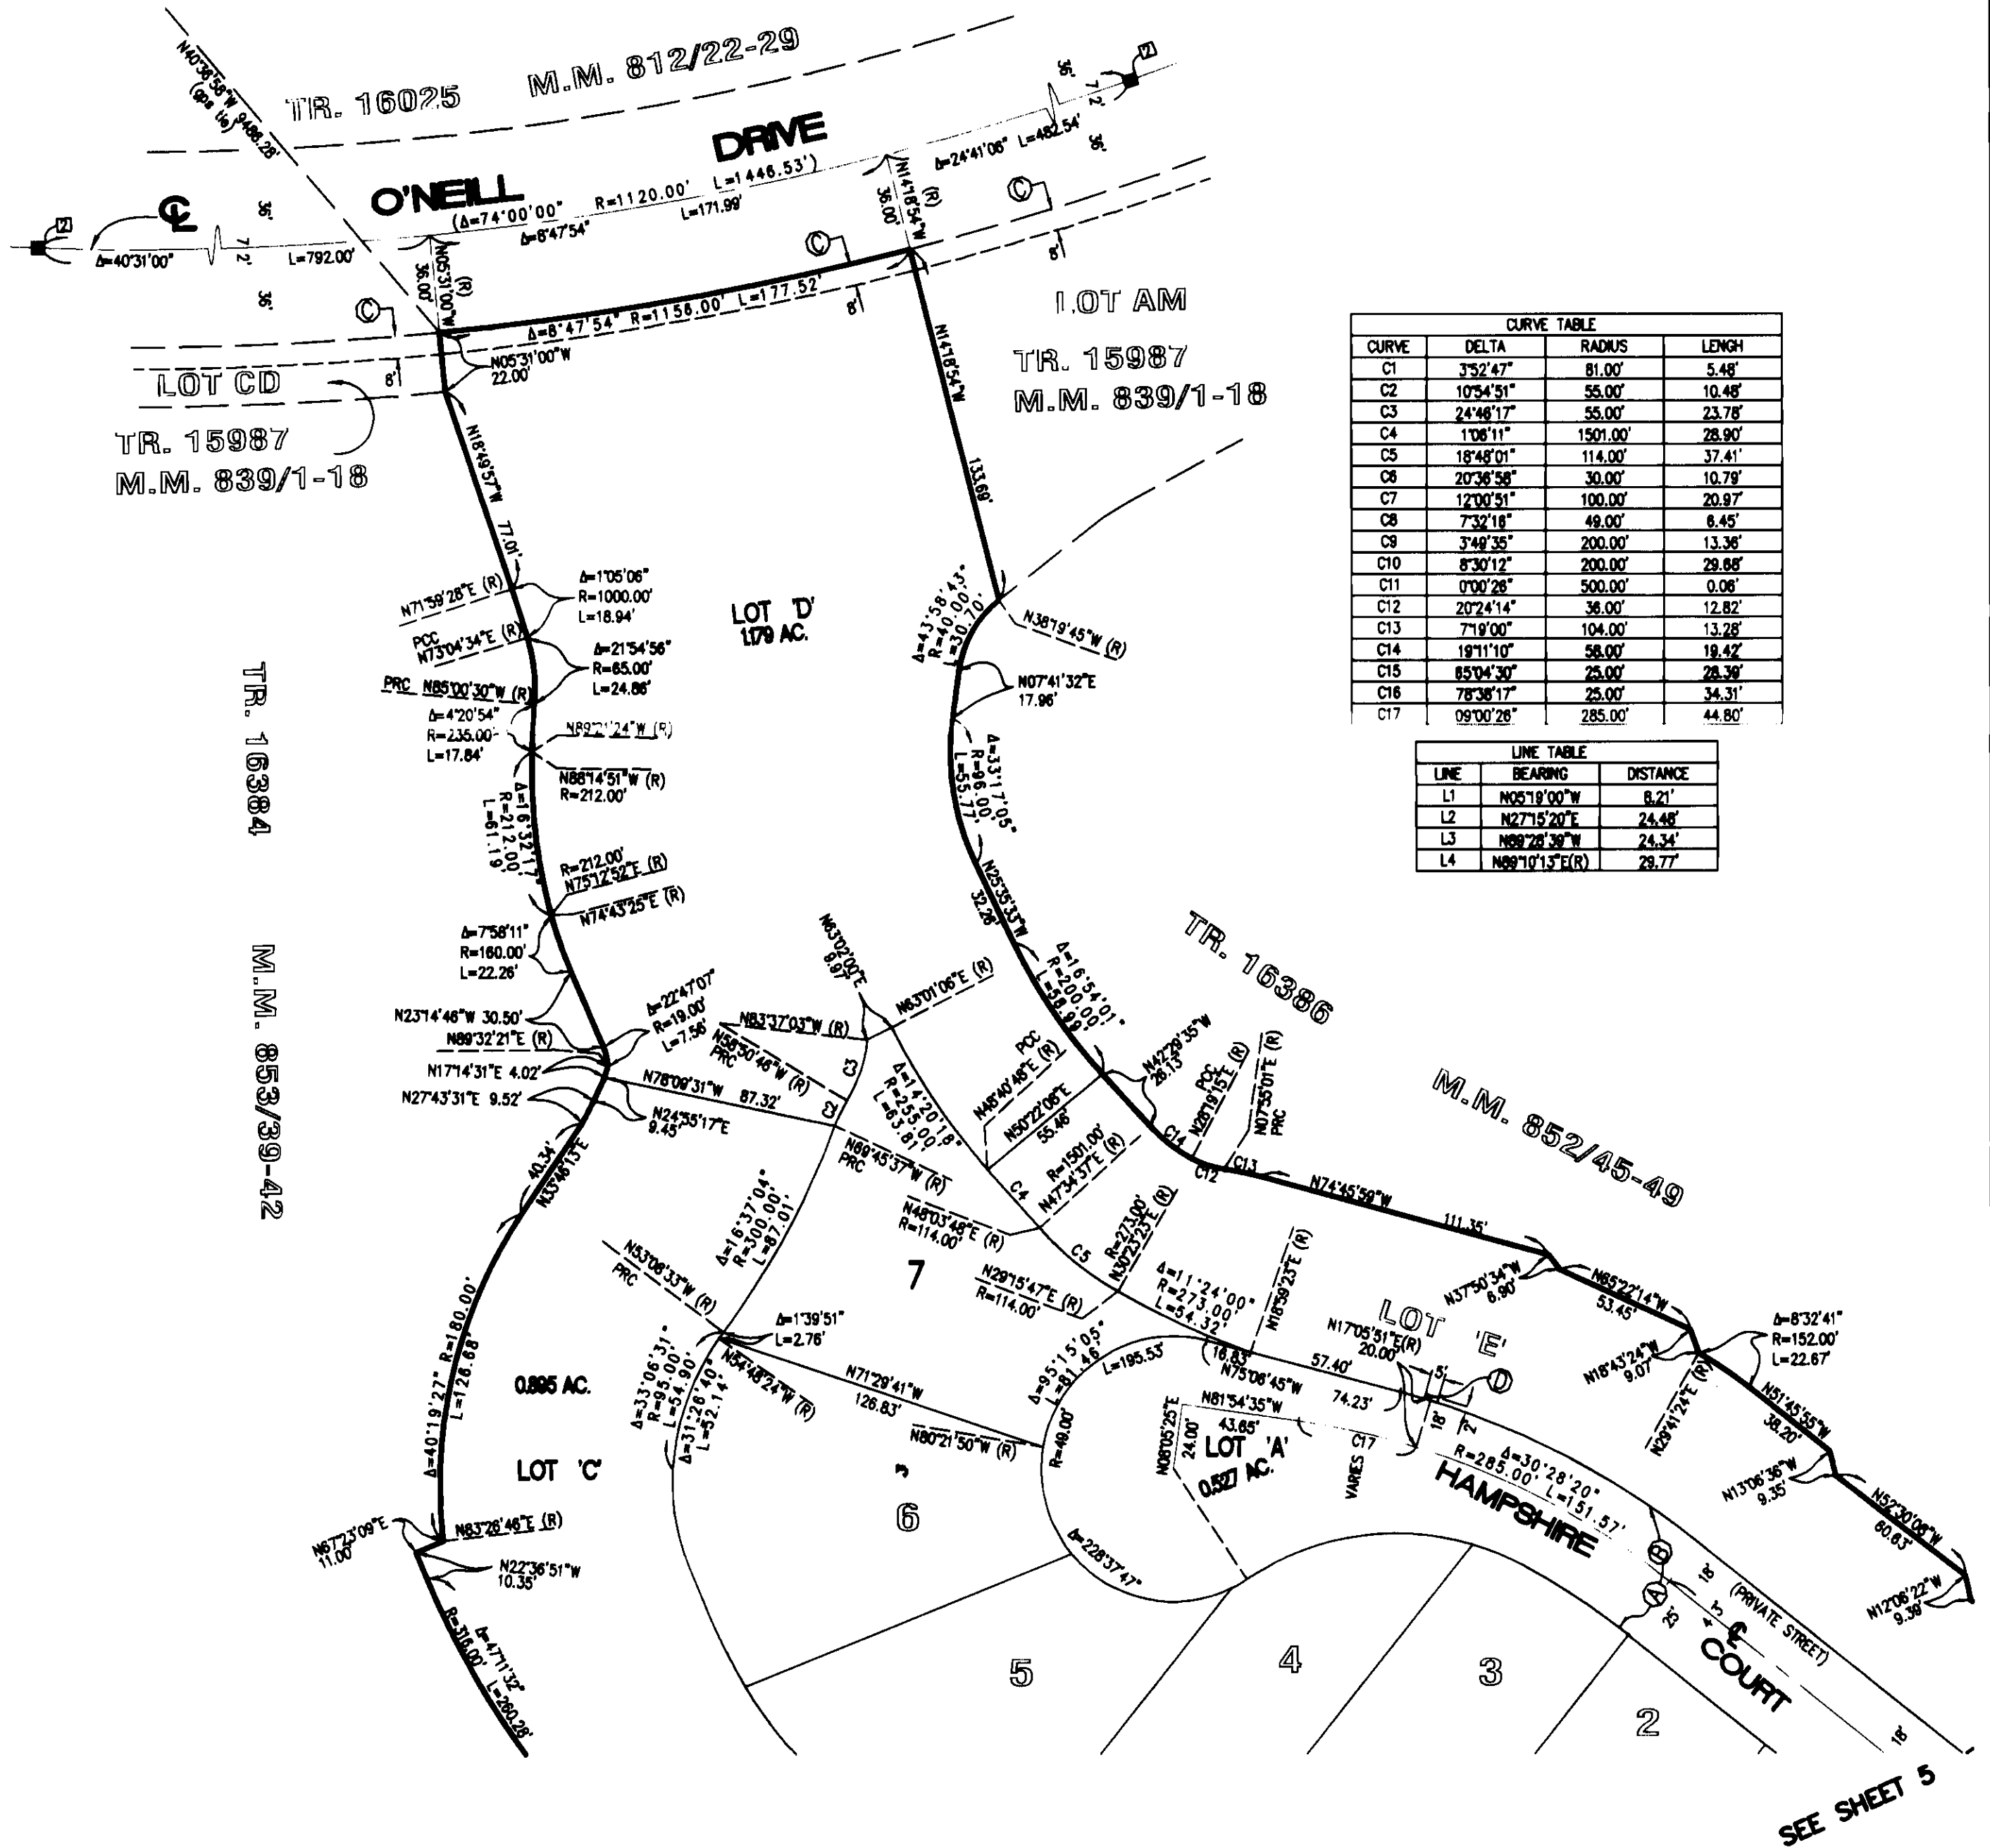

SEE SHEET 3 FOR GPS CONTROL, MONUMENT NOTES,
EASEMENT NOTES, BASIS OF BEARINGS AND DATUM STATEMENTS.

LOT 'A' IS NOT A SEPARATE BUILDING SITE AND IS FOR PRIVATE STREET PURPOSES.
LOTS 'B' THROUGH 'F' ARE NOT SEPARATE BUILDING SITES AND FOR LANDSCAPE/
OPEN SPACE PURPOSES.

ALL BEARINGS AND DISTANCES SHOWN ALONG THE MAP BOUNDARY ARE MEASURED AND
RECORD PER TR. 15987 M.M. 839/1-18.

SHEET 5 OF 5

SCALE: 1" = 50'
7 NUMBERED LOTS AND LOTS "A-F"
ACREAGE = 5.578 ACRES
A PORTION OF TENTATIVE
TRACT NO. 16384

TRACT NO. 16385



IN THE UNINCORPORATED TERRITORY OF ORANGE COUNTY,
STATE OF CALIFORNIA

ADAMS-STREETER CIVIL ENGINEERS, INC. JAN A ADAMS R.C.E. 21687
MAY 2003

SEE SHEET 4

CURVE	DELTA	RADIUS	LENGTH
C1	3°52'47"	81.00'	5.48'
C2	10°54'30"	55.00'	10.48'
C3	24°48'17"	55.00'	23.78'
C4	1°08'11"	1500.00'	28.90'
C5	18°48'01"	114.00'	37.41'
C6	20°36'36"	30.00'	10.79'
C7	17°00'51"	100.00'	20.97'
C8	7°32'15"	49.00'	8.45'
C9	3°49'35"	200.00'	13.36'
C10	8°30'12"	200.00'	28.68'
C11	0°07'28"	500.00'	0.08'
C12	20°24'14"	38.00'	12.82'
C13	7°19'10"	104.00'	13.28'
C14	19°11'10"	58.00'	18.42'
C15	6°04'30"	25.00'	28.39'
C16	78°28'17"	25.00'	34.31'

LINE	BEARING	DISTANCE
L1	N85°19'00"W	8.21'
L2	N27°13'20"E	24.46'
L3	N88°28'39"W	24.54'
L4	N88°10'13"E(R)	25.77'

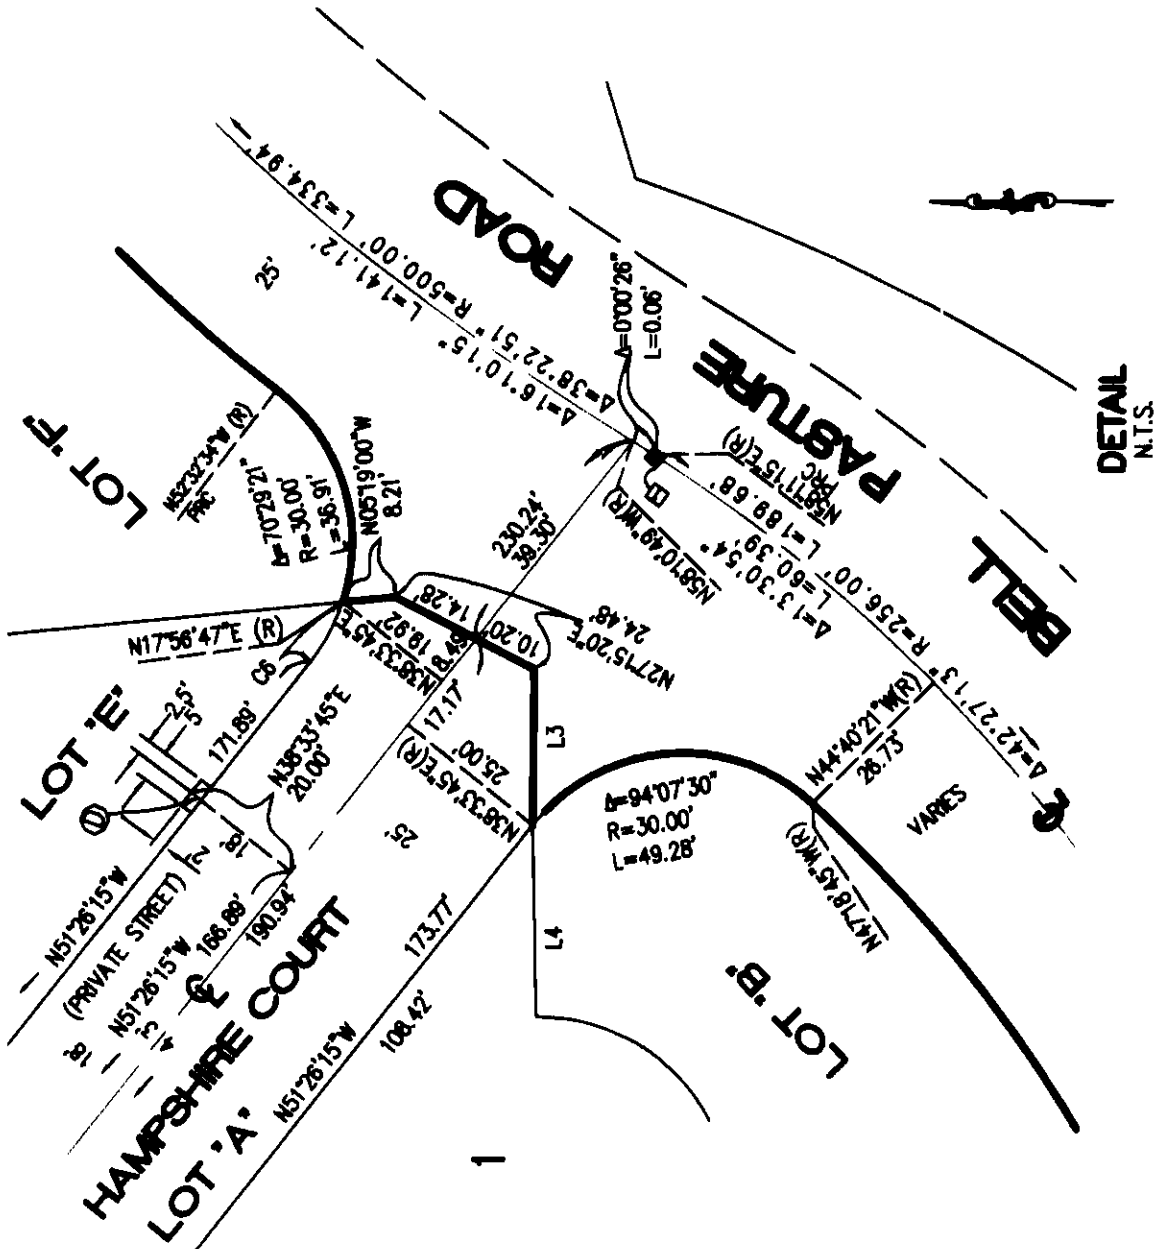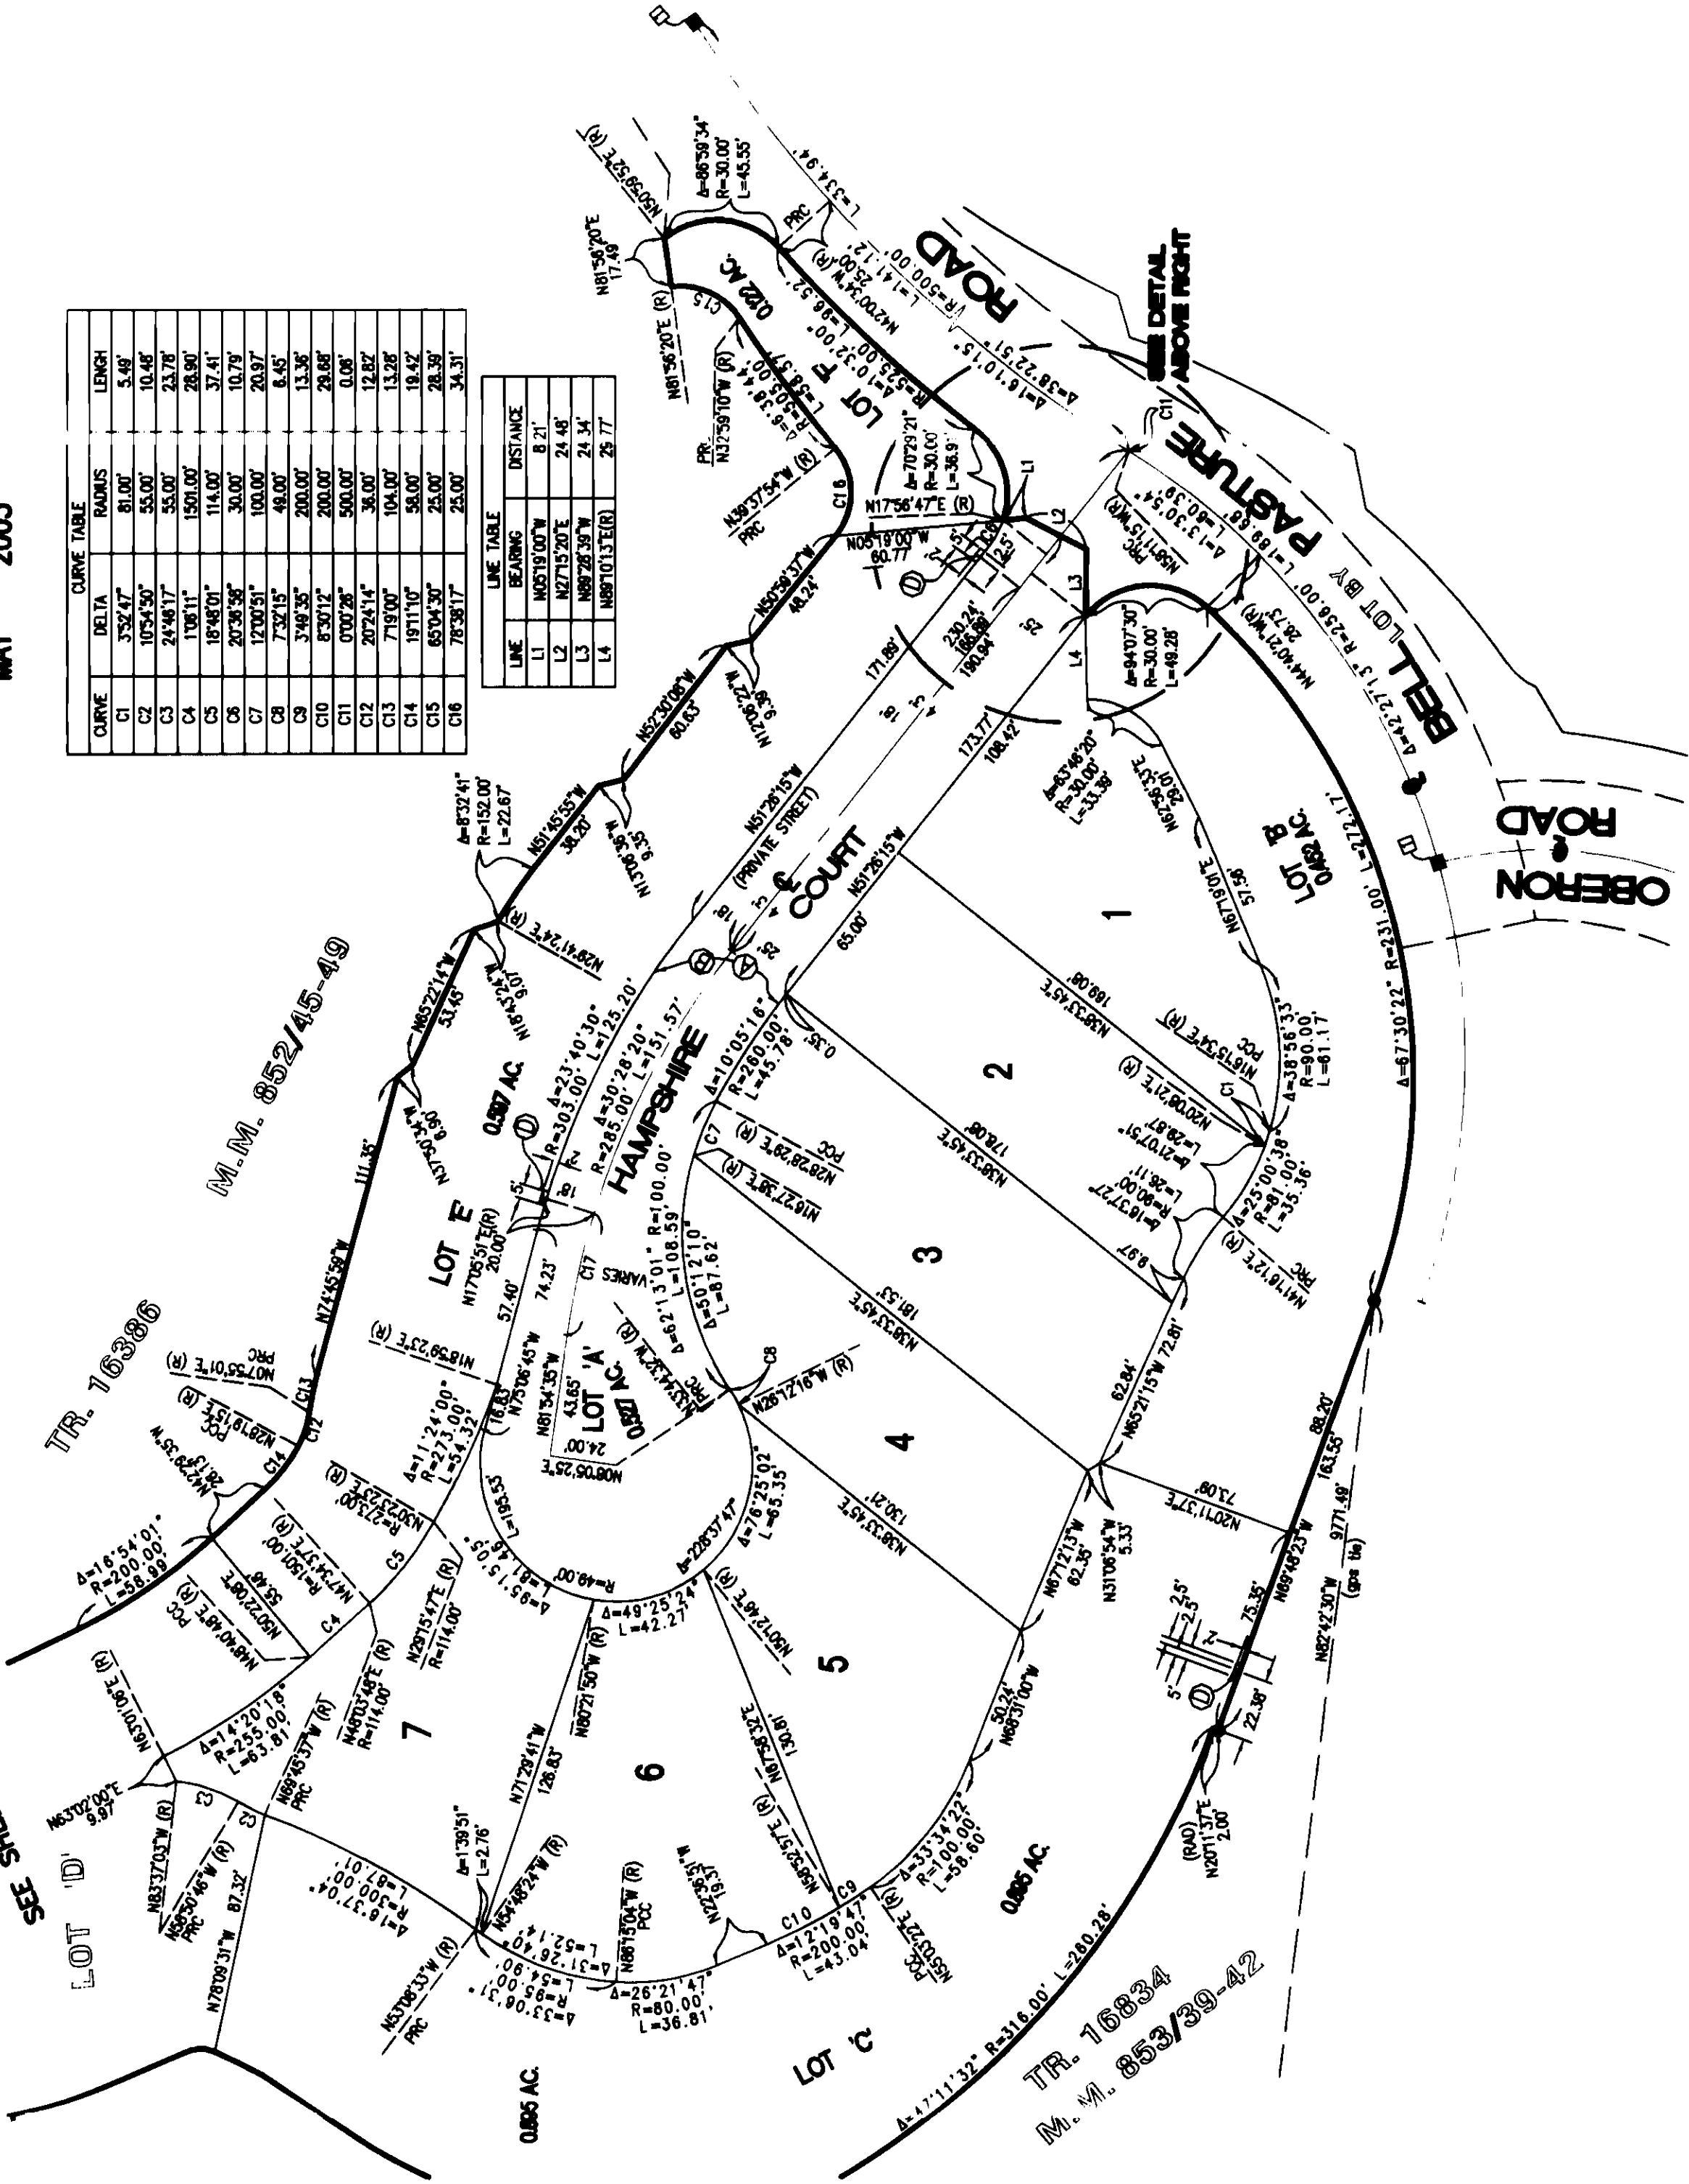

SEE SHEET 3 FOR GPS CONTROL, MONUMENT NOTES,
EASEMENT NOTES, BASIS OF BEARINGS AND DATUM STATEMENTS.

LOT 'A' IS NOT A SEPARATE BUILDING SITE AND IS FOR PRIVATE STREET PURPOSES.
LOTS 'B' THROUGH 'F' ARE NOT SEPARATE BUILDING SITES AND FOR LANDSCAPE/
OPEN SPACE PURPOSES.

ALL BEARINGS AND DISTANCES SHOWN ALONG THE MAP BOUNDARY ARE MEASURED AND
RECORD PER TR. 15987 M.M. 839/1-18.