

SHEET 1 OF 5 SHEETS

21 NUMBERED LOTS AND LOTS A, B & C

ACREAGE = 6.309 ACRES

A PORTION OF TENTATIVE
TRACT NO. 16384

DATE OF SURVEY: MAY 2003

TRACT NO. 16386

IN THE UNINCORPORATED TERRITORY OF THE COUNTY OF ORANGE,
STATE OF CALIFORNIABEING A SUBDIVISION OF LOT 7, AS SHOWN ON TRACT MAP NO. 15987
FILED IN BOOK 839, PAGES 1 THROUGH 18, INCLUSIVE OF MISCELLANEOUS MAPS,
IN THE OFFICE OF THE COUNTY RECORDER OF SAID COUNTY, STATE OF CALIFORNIA

ADAMS - STREETER CIVIL ENGINEERS, INC. JAN A. ADAMS, R.C.E. 21687

ACCEPTED AND FILED AT THE
REQUEST OF

FIRST AMERICAN TITLE INSURANCE COMPANY

DATE February 13, 2004TIME 11:24 am FEE \$ 1900INSTRUMENT # 20040000112625BOOK 852 PAGE 45-49 m/mTOM DALY
COUNTY - CLERK RECORDERBY Julia G. Adams
DEPUTY

OWNER'S CERTIFICATE:

WE, THE UNDERSIGNED, BEING ALL PARTIES HAVING ANY RECORD TITLE INTEREST IN THE LAND COVERED
BY THIS MAP, DO HEREBY CONSENT TO THE PREPARATION AND RECORDATION OF SAID MAP, AS SHOWN
WITHIN THE DISTINCTIVE BORDER LINE.

WE ALSO HEREBY DEDICATE TO THE COUNTY OF ORANGE:

1. AN EASEMENT FOR EMERGENCY AND PUBLIC SERVICE VEHICULAR INGRESS-EGRESS PURPOSES
AS SHOWN HEREIN.

WE ALSO DEDICATE TO THE SANTA MARGARITA WATER DISTRICT, THE EASEMENTS FOR SEWER, WATER
AND ACCESS PURPOSES AS SHOWN ON SAID MAP, WHICH EASEMENTS SHALL BE SUBJECT TO THE
SAME TERMS AND CONDITIONS AS ARE SHOWN IN THAT CERTAIN EASEMENT RECORDED SEPT. 18, 2002,
AS INST. NO. 20020799401 OF OFFICIAL RECORDS, COUNTY OF ORANGE.

STANDARD PACIFIC CORP. A DELAWARE CORPORATION

William C. Fischel
NAME: WILLIAM C. FISCHEL
TITLE: AUTHORIZED REPRESENTATIVE

Todd Palamaer
NAME: TODD PALAMAER
TITLE: AUTHORIZED REPRESENTATIVE

NOTARY ACKNOWLEDGMENTS

STATE OF CALIFORNIA }
COUNTY OF ORANGE } ssON THIS 21st DAY OF OCTOBER, 2003, BEFORE ME KATHIEEN H. VILLARI A NOTARY
PUBLIC IN AND FOR SAID STATE, PERSONALLY APPEARED WILLIAM C. FISCHEL & TODD PALAMAER
PERSONALLY KNOWN TO ME (OR PROVED TO ME ON THE BASIS OF SATISFACTORY EVIDENCE) TO BE
THE PERSONS WHOSE NAMES ARE SUBSCRIBED TO THE WITHIN INSTRUMENT AND ACKNOWLEDGED TO ME
THAT THEY EXECUTED THE SAME IN THEIR AUTHORIZED CAPACITIES AND THAT BY THEIR SIGNATURES ON
THE INSTRUMENT THE PERSON OR THE ENTITY UPON BEHALF OF WHICH THE PERSONS ACTED, EXECUTED
THE INSTRUMENT.

WITNESS MY HAND:

Kathleen H. Villari
NOTARY PUBLIC IN AND FOR SAID STATE

MY PRINCIPAL PLACE OF BUSINESS
IS IN ORANGE COUNTYMY COMMISSION EXPIRES 8/15/2007

KATHIEEN H. VILLARI
PRINT NAME

PRIVATE STREETS NOTE

THE PRIVATE STREETS CONSTRUCTED WITHIN THIS MAP SHALL BE OWNED, OPERATED AND
MAINTAINED BY THE DEVELOPER, SUCCESSORS OR ASSIGNS. THE COUNTY OF ORANGE SHALL
HAVE NO RESPONSIBILITY THEREFORE UNLESS PURSUANT TO APPROPRIATE SECTIONS OF THE
STREETS AND HIGHWAYS CODE OF THE STATE OF CALIFORNIA, THE SAID PRIVATE STREETS
HAVE BEEN ACCEPTED INTO THE COUNTY ROAD SYSTEM BY APPROPRIATE RESOLUTION OF
THE ORANGE COUNTY BOARD OF SUPERVISORS.

SIGNATURE OMISSIONS

PURSUANT TO THE PROVISIONS OF SECTION 66436 (a)(3)(A)(C) OF THE SUBDIVISION MAP ACT,
THE FOLLOWING SIGNATURES HAVE BEEN OMITTED:LADERA DEVELOPMENT COMPANY, LLC, HOLDER OF OIL, GAS AND MINERAL RIGHTS RECORDED AS
INSTRUMENT NO. 19980624029 OF OFFICIAL RECORDS.


DMB LADERA, LLC. HOLDER OF EASEMENTS RESERVED IN A DEED RECORDED
AS INSTRUMENT NO. 2003001135586 OF OFFICIAL RECORDS.

SOUTHERN CALIFORNIA GAS COMPANY, A CALIFORNIA CORPORATION, HOLDER
OF AN EASEMENT FOR FACILITIES AND INCIDENTAL PURPOSES RECORDED
NOVEMBER 25, 2003 AS INSTRUMENT NO. 2003001423369 OF
OFFICIAL RECORDS.

ENGINEER'S STATEMENT

THIS MAP WAS PREPARED BY ME OR UNDER MY DIRECTION AND IS BASED UPON A FIELD SURVEY IN
CONFORMANCE WITH THE REQUIREMENTS OF THE SUBDIVISION MAP ACT AND LOCAL ORDINANCE AT THE
REQUEST OF STANDARD PACIFIC CORP., IN DECEMBER 2002. I HEREBY STATE THAT ALL MONUMENTS ARE OF
THE CHARACTER AND OCCUPY THE POSITIONS INDICATED, OR THAT THEY WILL BE SET IN SUCH POSITIONS;
AND THAT SAID MONUMENTS ARE SUFFICIENT TO ENABLE THE SURVEY TO BE RETRACED. I HEREBY STATE
THAT THIS MAP SUBSTANTIALLY CONFORMS TO THE CONDITIONALLY APPROVED TENTATIVE MAP.


Jan A. Adams
JAN A. ADAMS, R.C.E. 21687
EXPIRES: 9/30/05

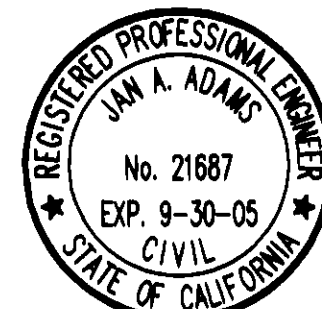

COUNTY SURVEYOR'S STATEMENT

I HEREBY STATE THAT I HAVE EXAMINED THIS MAP AND HAVE FOUND IT TO BE SUBSTANTIALLY IN
CONFORMANCE WITH THE TENTATIVE MAP AS FILED WITH, AMENDED AND APPROVED BY THE ORANGE
COUNTY SUBDIVISION COMMITTEE; THAT ALL PROVISIONS OF THE SUBDIVISION MAP ACT AND COUNTY
SUBDIVISION REGULATIONS HAVE BEEN COMPLIED WITH AND I AM SATISFIED SAID MAP IS TECHNICALLY
CORRECT.DATED THIS 26th DAY OF January, 2004

Robert Jelinek
JOHN CANAS, COUNTY SURVEYOR
LS 4408 EXPIRATION DATE: 9-30-05
ROBERT JELINEK, DEPUTY COUNTY SURVEYOR
LS 6803, EXPIRATION DATE: 09-30-04

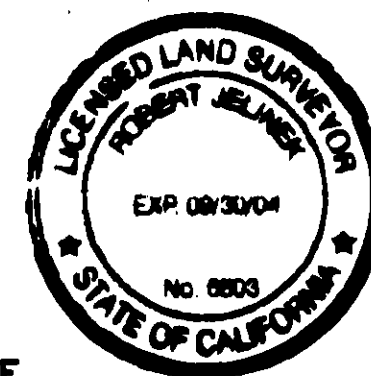

COUNTY TREASURER - TAX COLLECTOR'S CERTIFICATE

STATE OF CALIFORNIA }
COUNTY OF ORANGE } ssI HEREBY CERTIFY THAT ACCORDING TO THE RECORDS OF MY OFFICE THERE ARE NO LIENS AGAINST THE
LAND COVERED BY THIS MAP OR ANY PART THEREOF FOR UNPAID STATE, COUNTY, MUNICIPAL OR LOCAL
TAXES OR SPECIAL ASSESSMENTS COLLECTED AS TAXES, EXCEPT THOSE ORIGINALLY PRESENTED AS
COLLECTED AS TAXES NOT YET PAYABLE.AND DO ALSO CERTIFY TO THE RECORDER OF ORANGE COUNTY THAT THE PROVISIONS OF THE
SUBDIVISION MAP ACT HAVE BEEN COMPLIED WITH REGARDING DEPOSITS TO SECURE THE PAYMENT OF
TAXES OR SPECIAL ASSESSMENTS COLLECTED AS TAXES ON THE LAND COVERED BY THIS MAP.DATED THIS 13th DAY OF January, 2004

John M. W. Moorlach
JOHN M. W. MOORLACH
COUNTY TREASURER - TAX COLLECTOR

Jan T. J.
BY Jan T. J.
DEPUTY TREASURER - TAX COLLECTOR

CLERK OF THE BOARD OF SUPERVISOR'S CERTIFICATE

STATE OF CALIFORNIA }
COUNTY OF ORANGE } ssI HEREBY CERTIFY THAT THIS MAP WAS PRESENTED FOR APPROVAL TO THE BOARD OF SUPERVISORS OF
ORANGE COUNTY AT A REGULAR MEETING THEREOF HELD ON THE 3rd DAY OF February,
2004 AND THAT THEREUPON SAID BOARD DID, BY AN ORDER DULY PASSED AND ENTERED, APPROVE
SAID MAP.

AND DID ACCEPT ON BEHALF OF THE COUNTY OF ORANGE:

1. AN EASEMENT FOR EMERGENCY AND PUBLIC SERVICE VEHICULAR INGRESS-EGRESS PURPOSES, AS DEDICATED.

AND DID ALSO APPROVE SUBJECT MAP PURSUANT TO THE PROVISIONS OF SECTION 66436 (a)(3)(A) OF
THE SUBDIVISION MAP ACT.DATED THIS 3rd DAY OF February, 2004

Darlene J. Bloom
DARLENE J. BLOOM, CLERK OF THE BOARD OF SUPERVISORS



CERTIFICATE OF ACCEPTANCE

THE UNDERSIGNED, BEING THE DULY APPOINTED AGENT OF THE SANTA MARGARITA WATER DISTRICT,
A PUBLIC CORPORATION OF ORANGE COUNTY, CALIFORNIA, PURSUANT TO ITS RESOLUTION NO. 88-10-2,
DOES HEREBY ACCEPT ON BEHALF OF SAID DISTRICT THE EASEMENTS FOR SEWER, WATER AND ACCESS
PURPOSES, AS DEDICATED AND AS SHOWN ON THIS TRACT MAP, BY AND BETWEEN THE SANTA MARGARITA
WATER DISTRICT AND STANDARD PACIFIC CORP., DOES HEREBY CERTIFY THAT THE
GRANTEE CONSENTS TO THE RECORDATION OF SAID TRACT.

Daniel R. Ferons
BY Daniel R. Ferons
DANIEL R. FERONS, CHIEF ENGINEER
SANTA MARGARITA WATER DISTRICT

STATE OF CALIFORNIA }
COUNTY OF ORANGE } ssON THIS 26th DAY OF November, 2003, BEFORE ME Cindy R. Lane A NOTARY
PUBLIC IN AND FOR SAID STATE, PERSONALLY APPEARED Daniel R. Ferons PERSONALLY KNOWN TO ME
(OR PROVED TO ME ON THE BASIS OF SATISFACTORY EVIDENCE) TO BE THE PERSON WHOSE NAME IS
SUBSCRIBED TO THE WITHIN INSTRUMENT AND ACKNOWLEDGED TO ME THAT HE EXECUTED THE SAME IN
HIS AUTHORIZED CAPACITY AND THAT BY HIS SIGNATURE ON THE INSTRUMENT THE PERSON, OR THE
ENTITY UPON BEHALF OF WHICH THE PERSON ACTED, EXECUTED THE INSTRUMENT.

WITNESS MY HAND:

Cindy R. Lane
NOTARY PUBLIC IN AND FOR SAID STATE
Cindy R. Lane
PRINT NAME

MY PRINCIPAL PLACE OF BUSINESS
IS IN ORANGE COUNTYMY COMMISSION EXPIRES 2/20/2005

SHEET 2 OF 5 SHEETS
21 NUMBERED LOTS AND LOTS A, B & C
ACREAGE = 6.309 ACRES
A PORTION OF TENTATIVE
TRACT NO. 16384
DATE OF SURVEY: MAY 2003

TRACT NO. 16386

IN THE UNINCORPORATED TERRITORY OF THE COUNTY OF ORANGE,
STATE OF CALIFORNIA

BEING A SUBDIVISION OF LOT 7, AS SHOWN ON TRACT MAP NO. 15987
FILED IN BOOK 839, PAGES 1 THROUGH 18, INCLUSIVE OF MISCELLANEOUS MAPS,
IN THE OFFICE OF THE COUNTY RECORDER OF SAID COUNTY, STATE OF CALIFORNIA
ADAMS - STREETER CIVIL ENGINEERS, INC. JAN A. ADAMS, R.C.E. 21687

OWNER'S CERTIFICATE (CONT.)

DMB LADERA, LLC, A DELAWARE LIMITED LIABILITY COMPANY
BENEFICIARY UNDER A DEED OF TRUST RECORDED ON SEPTEMBER 16, 2003 AS INSTRUMENT NO.
2003001135588, O.R.

BY: RANCHO MISSION VIEJO, LLC, A DELAWARE LIMITED LIABILITY COMPANY,
ITS AUTHORIZED AGENT AND MANAGER.
BY: [Signature] BY: [Signature]
PRINT NAME: JOHN V. MARKEI PRINT NAME: JOHN V. MARKEI
PRINT TITLE: V.P. PRINT TITLE: V.P.

NOTARY ACKNOWLEDGMENTS

STATE OF CALIFORNIA }
COUNTY OF } ss
ON THIS 29th DAY OF December, 2003, BEFORE ME, Diana L. Binks, A NOTARY
PUBLIC IN AND FOR SAID STATE, PERSONALLY APPEARED Donald T. Stahlke + John V. Markei
PERSONALLY KNOWN TO ME (OR ~~PROVED TO ME ON THE BASIS OF SATISFACTORY EVIDENCE~~) TO BE
THE PERSONS WHOSE NAMES ARE SUBSCRIBED TO THE WITHIN INSTRUMENT AND ACKNOWLEDGED TO ME
THAT THEY EXECUTED THE SAME IN THEIR AUTHORIZED CAPACITIES AND THAT BY THEIR SIGNATURES ON
THE INSTRUMENT THE PERSON OR THE ENTITY UPON BEHALF OF WHICH THE PERSONS ACTED, EXECUTED
THE INSTRUMENT.
WITNESS MY HAND:
Diana L. Binks MY PRINCIPAL PLACE OF BUSINESS
NOTARY PUBLIC IN AND FOR SAID STATE IS IN Orange COUNTY
Diana L. Binks MY COMMISSION EXPIRES 12/12/06
PRINT NAME

SHEET 3 OF 5 SHEETS

21 NUMBERED LOTS AND LOTS A, B & C

ACREAGE = 6.309 ACRES

A PORTION OF TENTATIVE
TRACT NO. 16384

TRACT NO. 16386

IN THE UNINCORPORATED TERRITORY OF THE COUNTY OF ORANGE,
STATE OF CALIFORNIAADAMS - STREETER CIVIL ENGINEERS, INC. JAN A. ADAMS, R.C.E. 21687
DATE OF SURVEY: MAY 2003

SCALE: 1"=100'

MONUMENT NOTES:

1. ● 2" IRON PIPE, TAGGED "R.C.E. 21687" TO BE SET PRIOR TO RECORDATION.
2. ■ 8" SPIKE AND WASHER STAMPED "L.S. 5557" IN ASPHALT PAVING OR LEAD, TACK AND TAG "L.S. 5557" IN CONCRETE OR 1" IRON PIPE, TAGGED "L.S. 5557" TO BE SET PER TRACT 15987, MM 839/1-18.
3. 1" IRON PIPE, TAGGED "R.C.E. 21687", OR SPIKE AND WASHER, STAMPED "R.C.E. 21687", OR LEAD, TACK AND TAG "R.C.E. 21687" TO BE SET AT ALL LOT CORNERS, EXCEPT AT LOT CORNERS THAT ABUT A STREET, WHICH WILL BE SET ON A 9.75' OFFSET OUTSIDE THE TRUE LOT CORNER ON A PROLONGATION OF THE SIDE LOT LINE BY A LEAD, TACK AND TAG "R.C.E. 21687" IN THE TOP OF ADJACENT CONCRETE CURB, UNLESS OTHERWISE NOTED.
4. 8" SPIKE AND WASHER STAMPED "RCE 21687" IN ASPHALT PAVING OR LEAD, TACK AND TAG "R.C.E. 21687" IN CONCRETE OR 1" IRON PIPE, TAGGED "RCE 21687" TO BE SET AT ALL CENTERLINE INTERSECTIONS, B.C.'S, E.C.'S AND ALL OTHER CENTERLINE POINTS OF CONTROL, UNLESS OTHERWISE NOTED.
5. ALL MONUMENTS SHOWN AS "TO BE SET" WILL BE SET 90 DAYS AFTER THE ACCEPTANCE OF THE FINAL IMPROVEMENTS.
6. NO MONUMENTS TO BE SET AT BC'S AND EC'S OF STREET RIGHT OF WAY LINES.
7. ▲ FOUND GPS HORIZONTAL CONTROL POINT PER RECORDS ON FILE IN THE ORANGE COUNTY SURVEYOR'S OFFICE.
8. 2" IRON PIPE TAGGED "RCE 21687", OR SPIKE AND WASHER STAMPED "RCE 21687", OR LEAD, TACK AND TAG STAMPED "RCE 21687", OR NAIL AND TAG STAMPED "RCE 21687", OR A TAG STAMPED "RCE 21687" SECURED WITH EPOXY TO BE SET AT ALL TRACT BOUNDARY CORNERS, UNLESS OTHERWISE NOTED.

EASEMENT NOTES:

- A AN EASEMENT FOR SEWER AND WATER PIPELINE AND ACCESS PURPOSES DEDICATED TO THE SANTA MARGARITA WATER DISTRICT HEREON
- B AN EASEMENT FOR EMERGENCY AND PUBLIC SERVICE VEHICULAR INGRESS-EGRESS DEDICATED TO THE COUNTY OF ORANGE HEREON.
- C AN EASEMENT FOR SEWER AND WATER PIPELINE AND ACCESS PURPOSES DEDICATED TO THE SANTA MARGARITA WATER DISTRICT PER TRACT 15987 M.M. 839/1-18.

BASIS OF BEARINGS

THE BEARINGS SHOWN HEREON ARE BASED ON THE BEARING BETWEEN ORANGE COUNTY SURVEYOR'S HORIZONTAL CONTROL STATION "GPS NO. 7751" AND "GPS NO. 9009", BEING N. 25°35'15" E., PER RECORDS ON FILE IN THE OFFICE OF THE ORANGE COUNTY SURVEYOR.

DATUM STATEMENT

COORDINATES SHOWN HEREON ARE BASED ON THE CALIFORNIA COORDINATE SYSTEM (CCS83) ZONE VI, 1983 NAD (1991.35 EPOCH, O.C.S. GPS ADJUSTMENT). ALL DISTANCES SHOWN HEREON ARE GROUND, UNLESS OTHERWISE NOTED. TO OBTAIN GRID DISTANCE MULTIPLY GROUND DISTANCE BY 0.99994794.


AUTOMATIC FIRE SPRINKLER NOTE:

ALL RESIDENTIAL STRUCTURES EXCEEDING 5,500 SQUARE FEET AND ALL STRUCTURES EXCEEDING FIRE DEPARTMENT ACCESS REQUIREMENTS SHALL BE PROTECTED BY AN AUTOMATIC FIRE SPRINKLER SYSTEM, IN A MANNER MEETING THE APPROVAL OF THE FIRE CHIEF.

SPECIAL FIRE PROTECTION NOTE:

PROPERTY IS CONDITIONALLY EXCLUDED FROM A SPECIAL FIRE PROTECTION AREA. ALL REQUIREMENTS FOR DEVELOPMENT AND CONSTRUCTION WITHIN A "SPECIAL FIRE PROTECTION AREA" INCLUDING INCREASED STREET WIDTHS AND CLASS A ROOF ASSEMBLIES WILL BE MET.

GPS CONTROL SHEET

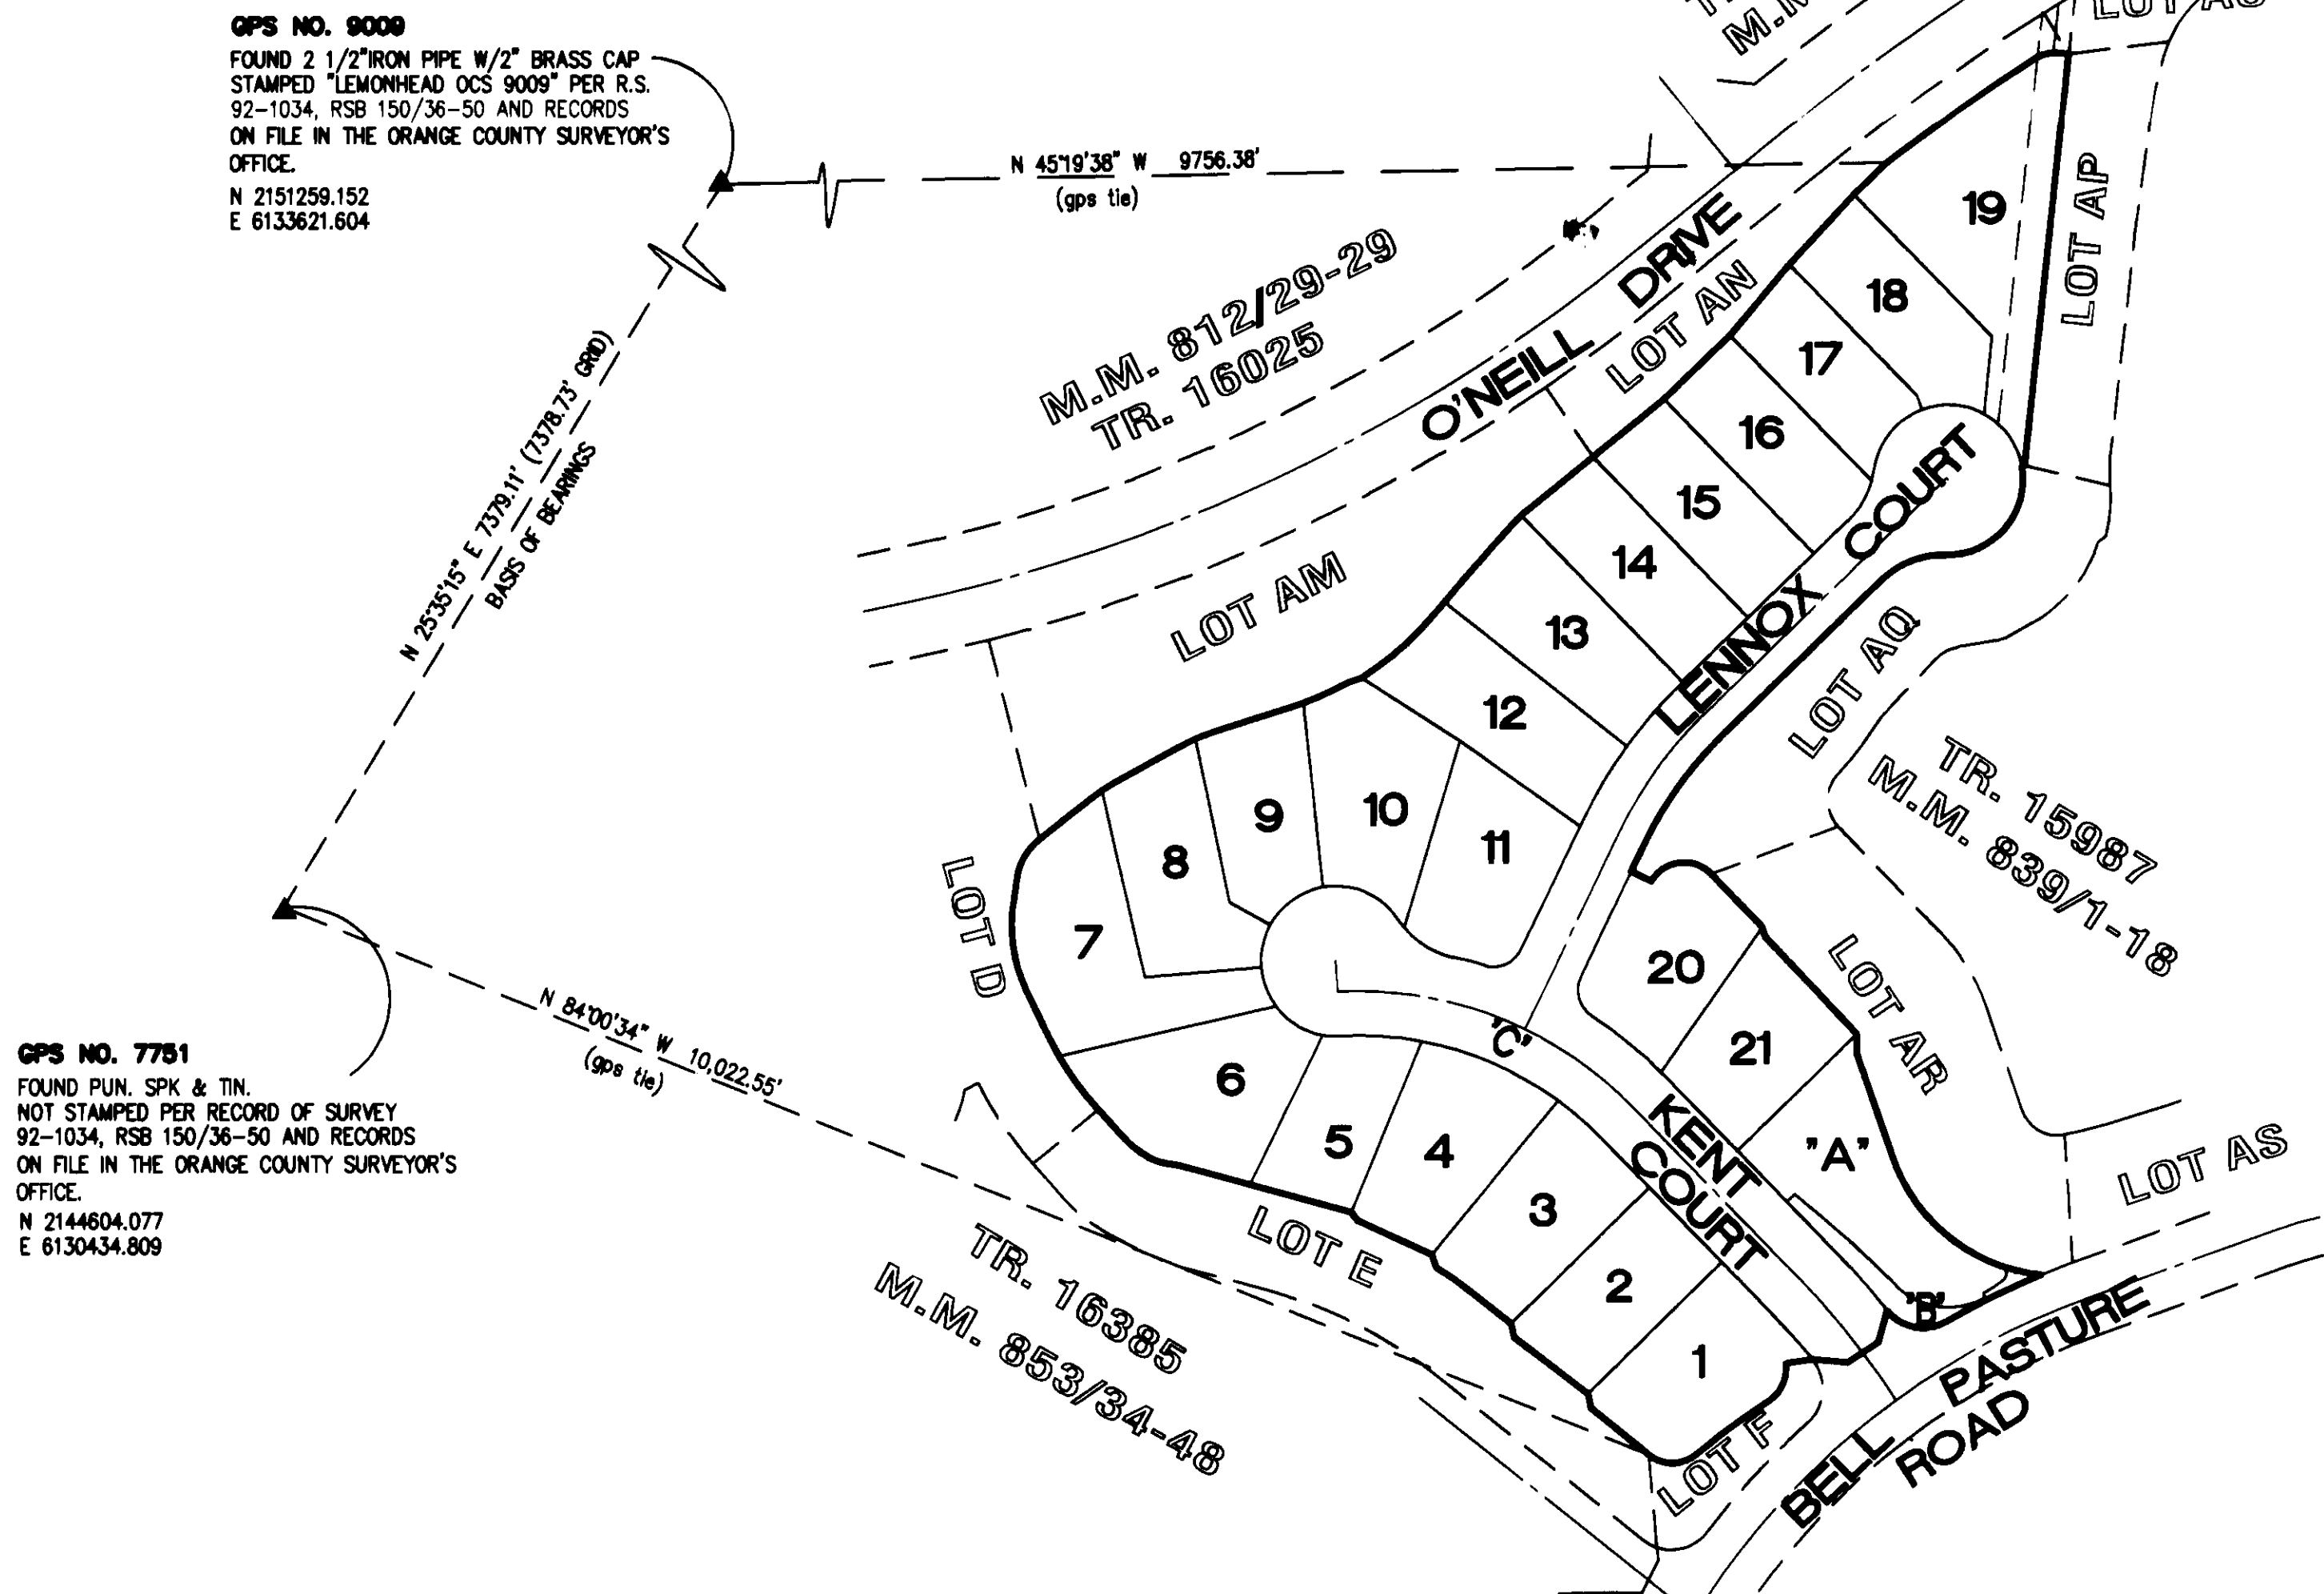

LOTS A & B ARE NOT SEPARATE BUILDING SITES AND ARE FOR PARK PURPOSES.
LOT C IS NOT A SEPARATE BUILDING SITE AND IS FOR PRIVATE STREET PURPOSES.

revised: 1-14-04

SHEET 4 OF 5 SHEETS
21 NUMBERED LOTS AND LOTS A, B & C
ACREAGE = 6.309 ACRES
A PORTION OF TENTATIVE
TRACT NO. 16384

TRACT NO. 16386


IN THE UNINCORPORATED TERRITORY OF THE COUNTY OF ORANGE,
STATE OF CALIFORNIA

ADAMS - STREETER CIVIL ENGINEERS, INC. JAN A. ADAMS, R.C.E. 21687
DATE OF SURVEY: MAY 2003

SCALE: 1"=60'

CURVE TABLE			
CURVE	DELTA	RADIUS	LENGTH
C1	78°38'17"	25.00'	34.31'
C2	65°04'30"	25.00'	28.39'
C3	51°41'7"	471.00'	43.06'
C4	83°2'41"	152.00'	22.87'
C5	131°0'49"	49.00'	11.27'
C6	43°01'25"	49.00'	36.79'
C7	122°0'50"	200.00'	43.10'
C8	32°11'39"	49.00'	27.53'
C9	33°38'12"	49.00'	28.74'
C10	44°2'54"	100.00'	8.23'
C11	45°1'59"	100.00'	8.49'
C12	51°2'01"	140.00'	12.71'
C13	53°58'50"	140.00'	14.81'
C14	22°31'11"	198.00'	8.25'
C15	9°06'39"	198.00'	31.46'
C16	4°22'01"	279.00'	21.26'
C17	6°45'08"	58.00'	6.95'
C18	36°41'27"	58.00'	37.78'
C19	81°20'38"	20.00'	28.36'
C20	9°40'48"	300.00'	50.68'
C21	30°02'10"	58.00'	30.93'
C22	7°37'20"	58.00'	7.85'
C23	49°25'58"	49.00'	42.28'
C24	38°36'59"	25.00'	17.00'
C25	51°13'04"	49.00'	43.80'
C26	82°41'55"	20.00'	28.87'
C27	123°44'28"	5.00'	10.80'
C28	72°32'42"	49.00'	61.86'
C29	7°38'04"	120.00'	16.02'
C30	13°23'37"	115.00'	28.88'
C31	81°28'37"	30.00'	42.84'
C32	04°33'12"	200.00'	15.89'
C33	12°38'51"	279.00'	61.59'
C34	00°37'43"	279.00'	3.06'
C35	08°47'15"	767.15'	90.88'
C36	43°28'35"	58.00'	44.74'
C37	37°39'30"	58.00'	38.78'
C38	88°59'34"	30.00'	45.55'

LINE TABLE		
LINE	BEARING	DISTANCE
L1	N81°36'20"E (R)	17.49'
L2	N80°35'55"W	30.86'
L3	N20°36'43"W	10.00'
L4	N83°51'45"W	6.42'
L5	N45°45'35"E	7.00'
L6	N26°29'02"W	3.00'
L7	N15°20'58"E	21.29'
L8	N58°35'38"E	12.02'
L9	N58°35'38"E	24.05'
L10	N85°05'17"W	23.23'

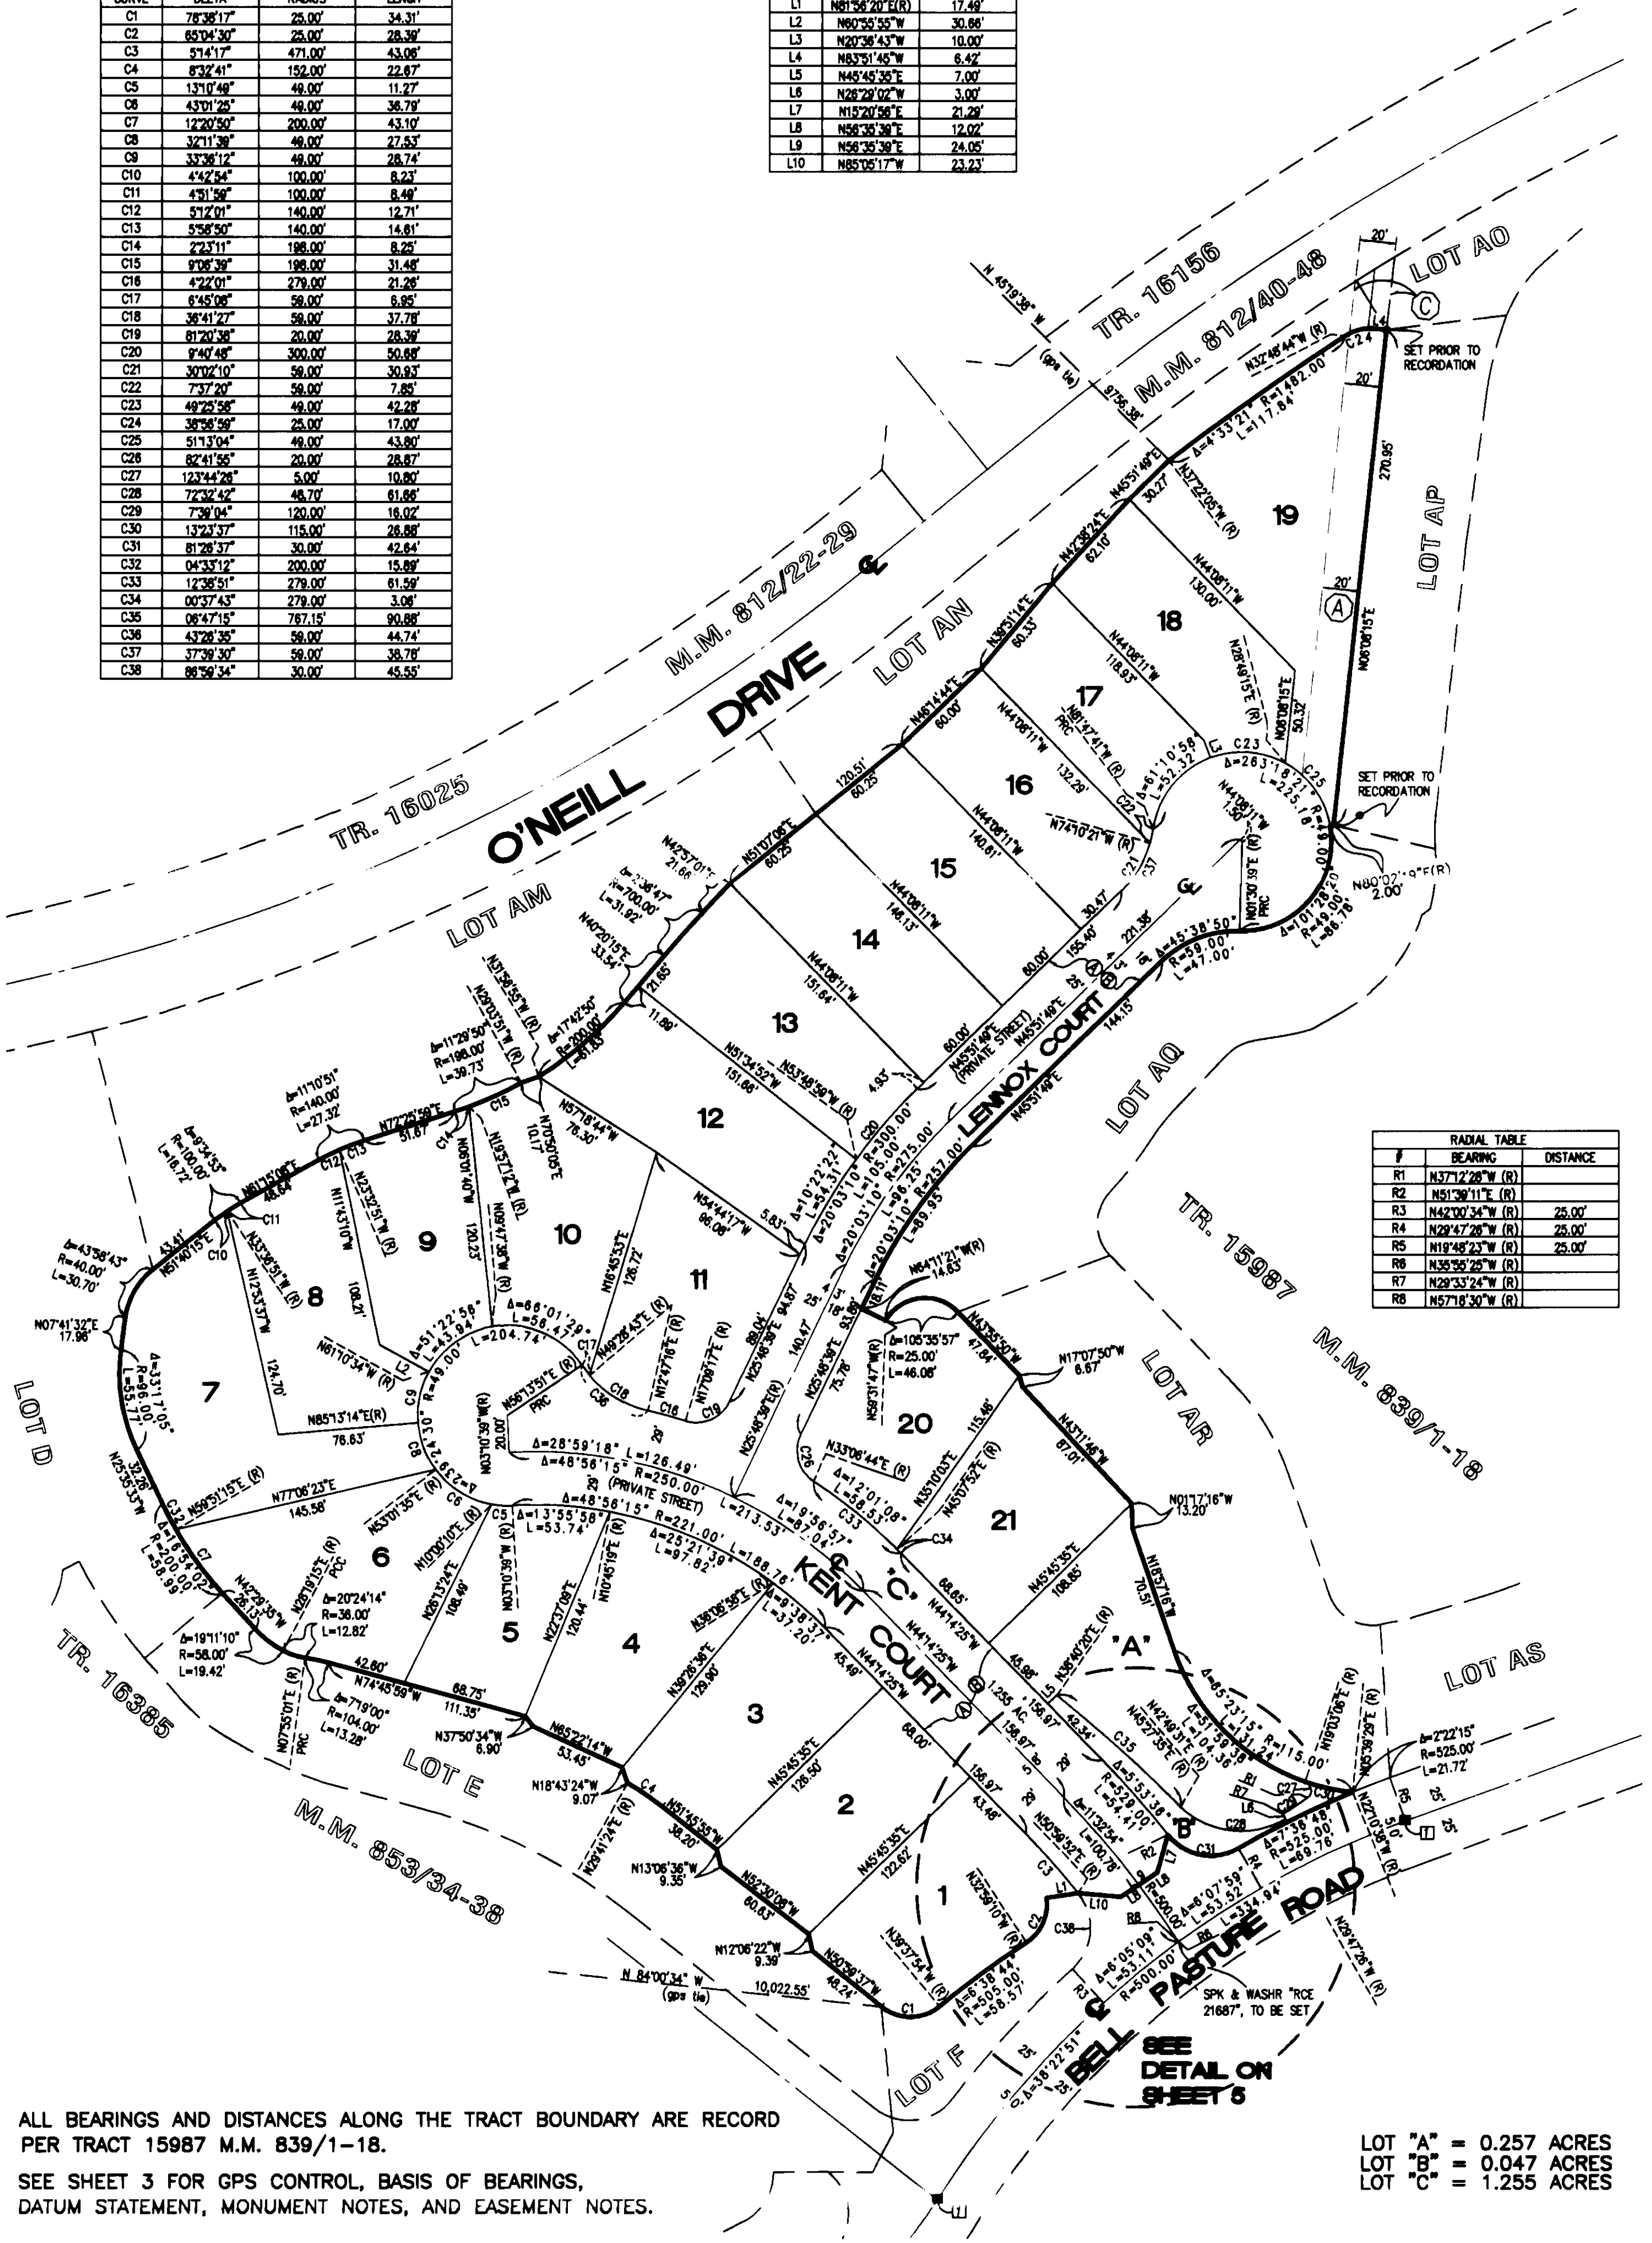

RADIAL TABLE		
#	BEARING	DISTANCE
R1	N37°12'28"W (R)	
R2	N51°30'11"E (R)	
R3	N42°00'34"W (R)	25.00'
R4	N29°47'28"W (R)	25.00'
R5	N19°48'23"W (R)	25.00'
R6	N35°55'25"W (R)	
R7	N29°33'24"W (R)	
R8	N57°18'30"W (R)	

ALL BEARINGS AND DISTANCES ALONG THE TRACT BOUNDARY ARE RECORD
PER TRACT 15987 M.M. 839/1-18.

SEE SHEET 3 FOR GPS CONTROL, BASIS OF BEARINGS,
DATUM STATEMENT, MONUMENT NOTES, AND EASEMENT NOTES.

LOTS A & B ARE NOT SEPARATE BUILDING SITES AND ARE FOR PARK PURPOSES.
LOT C IS NOT A SEPARATE BUILDING SITE AND IS FOR PRIVATE STREET PURPOSES.


LOT "A" = 0.257 ACRES
LOT "B" = 0.047 ACRES
LOT "C" = 1.255 ACRES

SHEET 5 OF 5 SHEETS
21 NUMBERED LOTS AND LOTS A, B & C
ACREAGE = 6.309 ACRES
A PORTION OF TENTATIVE
TRACT NO. 16384

TRACT NO. 16386
IN THE UNINCORPORATED TERRITORY OF THE COUNTY OF ORANGE,
STATE OF CALIFORNIA
ADAMS - STREETER CIVL ENGINEERS, INC. JAN A. ADAMS, R.C.E. 21687
DATE OF SURVEY: MAY 2003

INTERSECTION DETAIL SHEET

LOT "A" = 0.257 ACRES
LOT "B" = 0.047 ACRES
LOT "C" = 1.255 ACRES

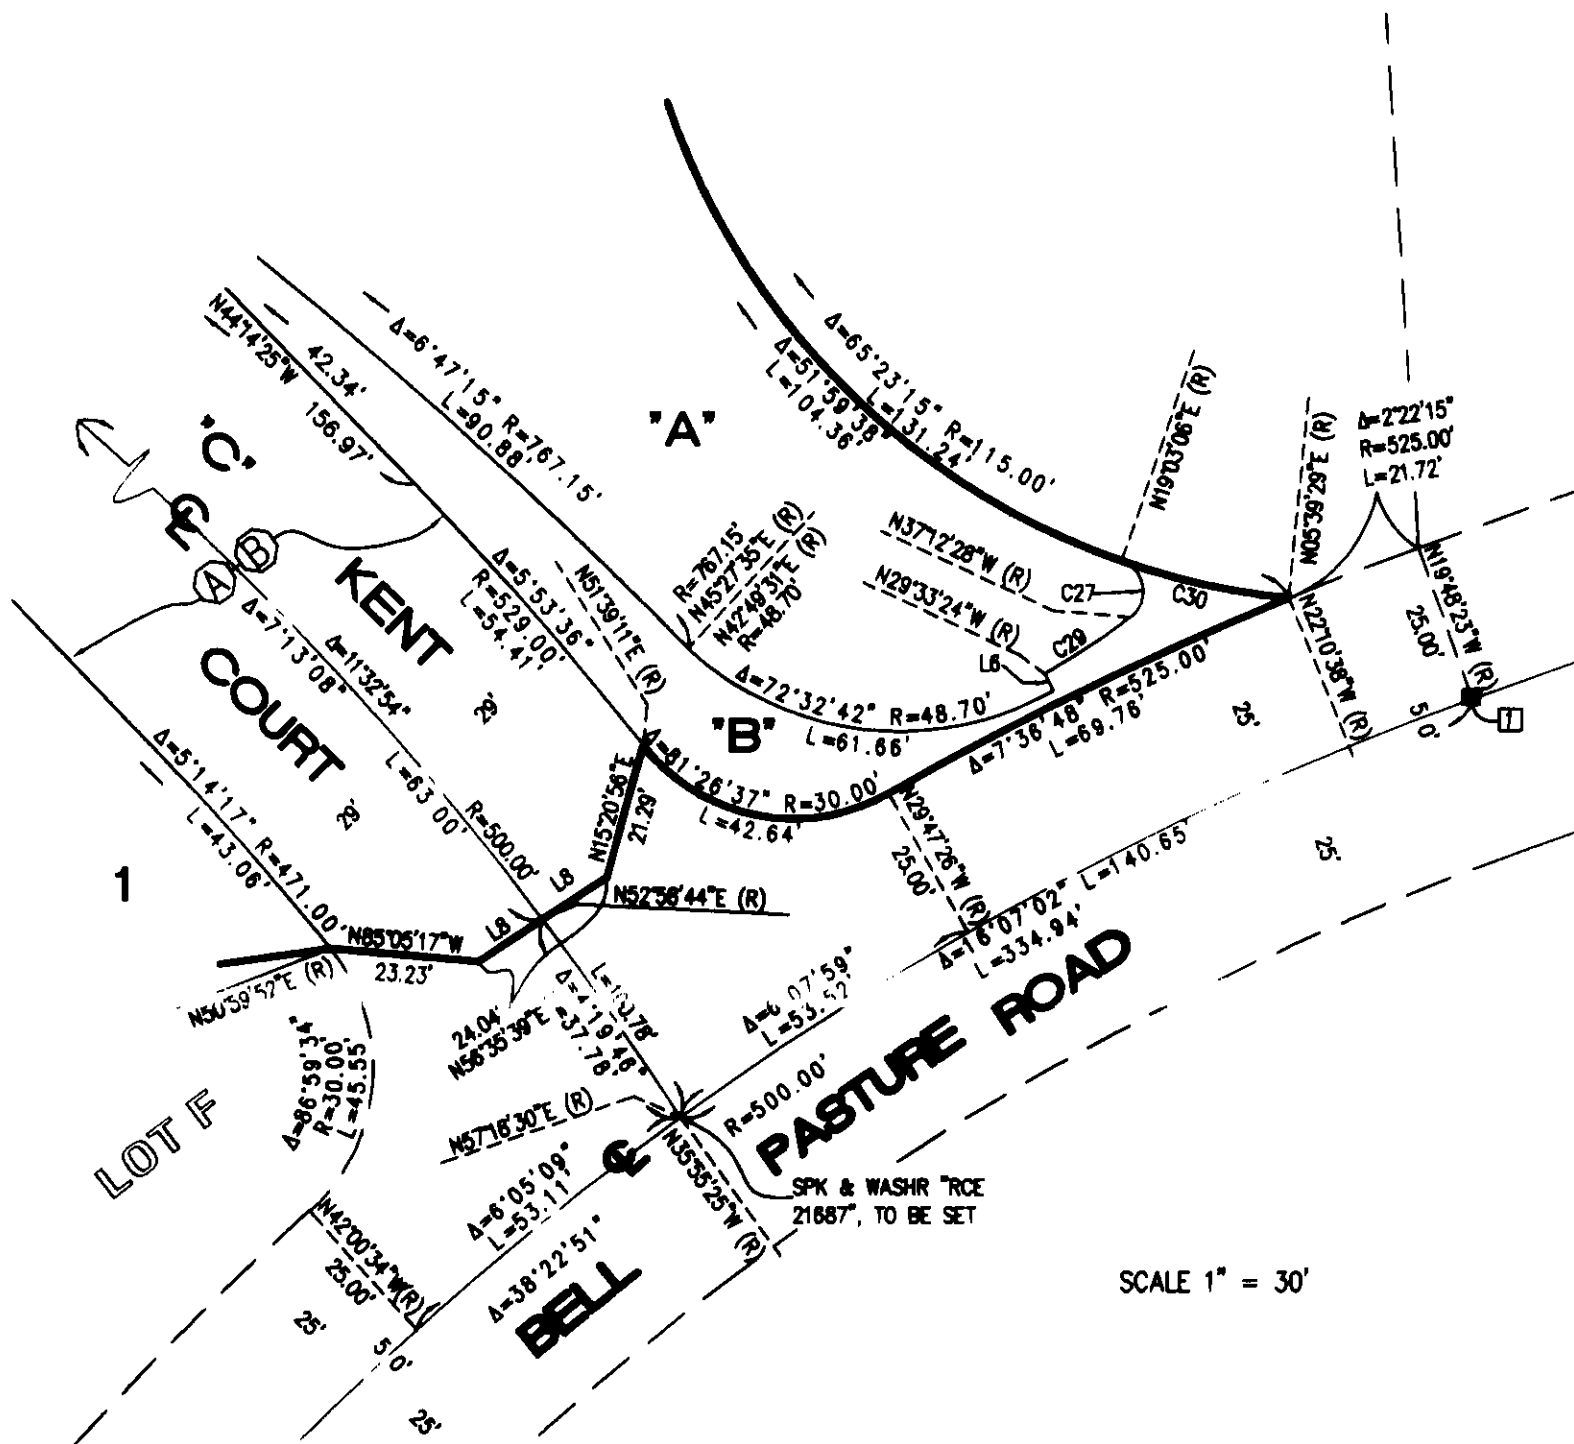

SCALE 1" = 30'

LINE TABLE		
LINE	BEARING	DISTANCE
L8	N28°29'02"W	3.00'
L8	N56°35'39"E	12.02'

CURVE TABLE			
CURVE	DELTA	RADIUS	LENGTH
C26	82°41'55"	20.00'	28.87'
C27	123°44'28"	5.00'	10.80'
C29	7°39'04"	120.00'	16.02'
C30	13°23'37"	115.00'	28.88'

SEE SHEET 3 FOR GPS CONTROL, BASIS OF BEARINGS,
DATUM STATEMENT, MONUMENT NOTES, AND EASEMENT NOTES.
LOTS A & B ARE NOT SEPARATE BUILDING SITES AND ARE FOR PARK PURPOSES.
LOT C IS NOT SEPARATE BUILDING SITES AND IS FOR PRIVATE STREET PURPOSES.
ALL BEARINGS AND DISTANCES ALONG THE TRACT BOUNDARY ARE RECORD
PER TRACT 15987 M.M. 839/1-18.