

SHEET 1 OF 4 SHEETS
26 NUMBERED LOTS AND
LOTS A THROUGH J, INCLUSIVE
ACREAGE: 8.286 ACRES
(FINAL UNIT OF TENTATIVE
TRACT NO. 16387)

TRACT NO. 16387

IN UNINCORPORATED TERRITORY OF THE COUNTY OF ORANGE,
STATE OF CALIFORNIA

BEING A SUBDIVISION OF LOTS 8, AU, AV AND AW OF TRACT NO. 15987, AS PER
MAP FILED IN BOOK 839, PAGES 1 THROUGH 18, INCLUSIVE, OF MISCELLANEOUS
MAPS, IN THE OFFICE OF THE COUNTY RECORDER OF SAID COUNTY.

HUNSAKER AND ASSOCIATES IRVINE, INC.
RORY S. WILLIAMS, L.S. 6654 DATE OF SURVEY: JULY, 2003

ACCEPTED AND FILED AT THE
REQUEST OF

First American Title Insurance

DATE: February 04, 2004

TIME: 10:38am FEE: \$16.00

INSTRUMENT NO. 200400086051 \$m

BOOK 853 PAGE 47-50

TOM DALY
COUNTY CLERK - RECORDER

BY Julia Escaneda
DEPUTY

OWNERSHIP CERTIFICATE:

WE, THE UNDERSIGNED, BEING ALL PARTIES HAVING ANY RECORD TITLE INTEREST IN THE LAND COVERED BY THIS MAP, DO HEREBY CONSENT TO THE PREPARATION AND RECORDATION OF SAID MAP, AS SHOWN WITHIN THE DISTINCTIVE BORDER LINE.

WE HEREBY DEDICATE TO COUNTY OF ORANGE EASEMENTS FOR EMERGENCY ACCESS PURPOSES OVER ALL OF LOTS A AND B, AND THAT PORTION OF LOT E, AS SHOWN ON SAID MAP.

WE ALSO HEREBY DEDICATE TO THE SANTA MARGARITA WATER DISTRICT THE EASEMENTS FOR WATER, RECYCLED WATER, SEWER, DRAINAGE AND ACCESS PURPOSES OVER THOSE EASEMENT AREAS AS SHOWN ON SAID MAP, WHICH EASEMENTS SHALL BE SUBJECT TO THE SAME CONDITIONS AS SHOWN IN THAT CERTAIN GRANT OF EASEMENT TO SANTA MARGARITA WATER DISTRICT RECORDED SEPTEMBER 18, 2002, AS INSTRUMENT NO. 20020799401 OF OFFICIAL RECORDS, COUNTY OF ORANGE.

SHEA HOMES LIMITED PARTNERSHIP, A CALIFORNIA LIMITED PARTNERSHIP, OWNER.

BY: J.F. SHEA LLC, A DELAWARE LIMITED LIABILITY COMPANY,
ITS GENERAL PARTNER.

BY: Marion P. Marcum BY: John C. Danvers
NAME: MARION P. MARCUM NAME: JOHN C. DANVERS
TITLE: ASSISTANT SECRETARY TITLE: ASSISTANT SECRETARY

DMB LADERA, L.L.C., A DELAWARE LIMITED LIABILITY COMPANY, OWNER AND BENEFICIARY UNDER DEED OF TRUST RECORDED SEPTEMBER 16, 2003, AS INSTRUMENT NO. 2003-001135592 OF OFFICIAL RECORDS.

BY: RANCHO MISSION VIEJO, L.L.C., A DELAWARE LIMITED LIABILITY COMPANY, ITS
AUTHORIZED AGENT AND MANAGER.

BY: Donald T. Stahlin BY: Gregory B. Edwards
NAME: DONALD T. STAHLIN NAME: GREGORY B. EDWARDS
TITLE: VICE PRESIDENT TITLE: Sr. V.P. / CFO

NOTARY ACKNOWLEDGMENT:

STATE OF CALIFORNIA } SS
COUNTY OF ORANGE }

ON Nov. 17, 2003 BEFORE ME, Beth A. Hutchinson, PERSONALLY
APPEARED Marion P. Marcum AND John C. Danvers PERSONALLY
KNOWN TO ME (OR PROVED TO ME ON THE BASIS OF SATISFACTORY EVIDENCE) TO BE THE PERSON(S)
WHOSE NAME(S) IS/ARE SUBSCRIBED TO THE WITHIN INSTRUMENT AND ACKNOWLEDGED TO ME THAT
HE/SHE/IT EXECUTED THE SAME IN AS/PER THEIR AUTHORIZED CAPACITY(IES), AND THAT BY
THEIR SIGNATURE(S) ON THE INSTRUMENT THE PERSON(S), OR ENTITY UPON BEHALF OF
WHICH THE PERSON(S) ACTED, EXECUTED THE INSTRUMENT.

WITNESS MY HAND:

SIGNATURE Beth A. Hutchinson MY PRINCIPAL PLACE OF BUSINESS IS
NOTARY PUBLIC IN AND FOR SAID STATE IN Orange COUNTY.
Beth A. Hutchinson MY COMMISSION EXPIRES: May 8, 2005
(NAME PRINTED)

NOTARY ACKNOWLEDGMENT:

STATE OF CALIFORNIA } SS
COUNTY OF ORANGE }

ON Dec. 1, 2003 BEFORE ME, Diana L. Binks, Notary Public, PERSONALLY
APPEARED Donald T. Stahlin AND Gregory B. Edwards PERSONALLY
KNOWN TO ME (OR PROVED TO ME ON THE BASIS OF SATISFACTORY EVIDENCE) TO BE THE PERSON(S)
WHOSE NAME(S) IS/ARE SUBSCRIBED TO THE WITHIN INSTRUMENT AND ACKNOWLEDGED TO ME THAT
HE/SHE/IT EXECUTED THE SAME IN AS/PER THEIR AUTHORIZED CAPACITY(IES), AND THAT BY
HIS/HER/THEIR SIGNATURE(S) ON THE INSTRUMENT THE PERSON(S), OR ENTITY UPON BEHALF OF
WHICH THE PERSON(S) ACTED, EXECUTED THE INSTRUMENT.

WITNESS MY HAND:

SIGNATURE Diana L. Binks MY PRINCIPAL PLACE OF BUSINESS IS
NOTARY PUBLIC IN AND FOR SAID STATE IN Orange COUNTY.
Diana L. Binks MY COMMISSION EXPIRES: 12-12-06
(NAME PRINTED)

AUTOMATIC FIRE SPRINKLER NOTE:

ALL COMMERCIAL STRUCTURES GREATER THAN 6,000 SQUARE FEET, ALL MULTIFAMILY RESIDENTIAL STRUCTURES, ALL SINGLE-FAMILY STRUCTURES EXCEEDING 5,500 SQUARE FEET, AND ALL STRUCTURES EXCEEDING FIRE DEPARTMENT ACCESS REQUIREMENTS SHALL BE PROTECTED BY AN AUTOMATIC FIRE SPRINKLER SYSTEM.

SPECIAL FIRE PROTECTION NOTE:

SUBJECT PROPERTY IS IN A SPECIAL FIRE PROTECTION AREA AND MUST MEET ALL REQUIREMENTS FOR DEVELOPMENT WITHIN THE AREA.

HIGH FIRE HAZARD AREA NOTE:

THE LOTS SHOWN ON THIS MAP ARE IN A HIGH FIRE HAZARD AREA DUE TO WILDLAND EXPOSURE.


NOTE:

"THE PRIVATE STREETS CONSTRUCTED WITHIN THIS MAP SHALL BE OWNED, OPERATED AND MAINTAINED BY THE DEVELOPER, SUCCESSORS OR ASSIGNS. THE COUNTY OF ORANGE SHALL HAVE NO RESPONSIBILITY THEREFOR, UNLESS PURSUANT TO APPROPRIATE SECTIONS OF THE STREETS AND HIGHWAYS CODE OF THE STATE OF CALIFORNIA, THE SAID PRIVATE STREETS HAVE BEEN ACCEPTED INTO THE COUNTY ROAD SYSTEM BY APPROPRIATE RESOLUTION OF THE ORANGE COUNTY BOARD OF SUPERVISORS."

SURVEYOR'S STATEMENT:

THIS MAP WAS PREPARED BY ME OR UNDER MY DIRECTION AND IS BASED UPON A FIELD SURVEY IN CONFORMANCE WITH THE REQUIREMENTS OF THE SUBDIVISION MAP ACT AND LOCAL ORDINANCE AT THE REQUEST OF DMB LADERA, L.L.C., IN JULY, 2003. I HEREBY STATE THAT ALL MONUMENTS ARE OF THE CHARACTER AND OCCUPY THE POSITIONS INDICATED, OR THAT THEY WILL BE SET IN SUCH POSITIONS; AND THAT SAID MONUMENTS ARE SUFFICIENT TO ENABLE THE SURVEY TO BE RETRACED. I HEREBY STATE THAT THIS FINAL MAP SUBSTANTIALLY CONFORMS TO THE CONDITIONALLY APPROVED TENTATIVE MAP.

Rory S. Williams 12/5/03
RORY S. WILLIAMS, L.S. 6654 DATE
LICENSE EXPIRES: 12/31/03

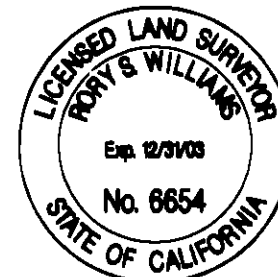

COUNTY SURVEYOR'S STATEMENT

I HEREBY STATE THAT I HAVE EXAMINED THIS MAP AND HAVE FOUND IT TO BE SUBSTANTIALLY IN CONFORMANCE WITH THE TENTATIVE MAP AS FILED WITH, AMENDED AND APPROVED BY THE ORANGE COUNTY SUBDIVISION COMMITTEE; THAT ALL PROVISIONS OF THE SUBDIVISION MAP ACT AND COUNTY SUBDIVISION REGULATIONS HAVE BEEN COMPLIED WITH AND I AM SATISFIED SAID MAP IS TECHNICALLY CORRECT.

DATED THIS 8TH DAY OF JANUARY, 2004.

Michael K. Sullivan
JOHN CANAS, COUNTY SURVEYOR BY: MICHAEL K. SULLIVAN, DEPUTY
L.S. 4408 EXPIRATION DATE: 9/30/05 L.S. 6654 EXPIRES 8/30/08



COUNTY TREASURER-TAX COLLECTOR'S CERTIFICATE:

STATE OF CALIFORNIA } SS
COUNTY OF ORANGE }

I HEREBY CERTIFY THAT ACCORDING TO THE RECORDS OF MY OFFICE THERE ARE NO LIENS AGAINST THE LAND COVERED BY THIS MAP OR ANY PART THEREOF FOR UNPAID STATE, COUNTY, MUNICIPAL OR LOCAL TAXES OR SPECIAL ASSESSMENTS COLLECTED AS TAXES, EXCEPT TAXES OR SPECIAL ASSESSMENTS COLLECTED AS TAXES NOT YET PAYABLE:

AND DO CERTIFY TO THE RECORDER OF ORANGE COUNTY THAT THE PROVISIONS OF THE SUBDIVISION MAP ACT HAVE BEEN COMPLIED WITH REGARDING DEPOSITS TO SECURE PAYMENT OF TAXES OR SPECIAL ASSESSMENTS COLLECTED AS TAXES ON THE LAND COVERED BY THIS MAP.

DATED THIS 2nd DAY OF January, 2004.

John M.W. Moorlach BY: Michael K. Sullivan
COUNTY TREASURER-TAX COLLECTOR DEPUTY TREASURER-TAX COLLECTOR

CLERK OF THE BOARD OF SUPERVISORS' CERTIFICATE:

STATE OF CALIFORNIA } SS
COUNTY OF ORANGE }


I HEREBY CERTIFY THAT THIS MAP WAS PRESENTED FOR APPROVAL TO THE BOARD OF SUPERVISORS OF THE COUNTY OF ORANGE AT REGULAR MEETING THEREOF HELD ON THE 27th DAY OF January, 2004, AND THAT THEREUPON SAID BOARD DID, BY AN ORDER DULY PASSED AND ENTERED, APPROVE SAID MAP.

AND DID ACCEPT ON BEHALF OF THE COUNTY OF ORANGE THE EASEMENTS FOR EMERGENCY ACCESS PURPOSES OVER ALL OF LOTS A AND B, AND THAT PORTION OF LOT E, AS DEDICATED.

AND DID ALSO APPROVE SUBJECT MAP PURSUANT TO THE PROVISIONS OF SECTION 66436 (a)(3)(A) OF THE SUBDIVISION MAP ACT.

DATED THIS 27th DAY OF January, 2004.

Darlene J. Bloom
CLERK OF THE BOARD OF SUPERVISORS
DARLENE J. BLOOM

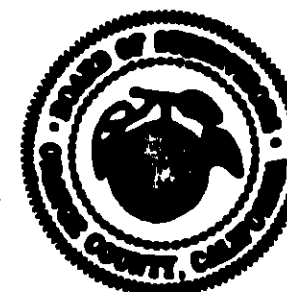

CERTIFICATE OF ACCEPTANCE - SANTA MARGARITA WATER DISTRICT

THE UNDERSIGNED, BEING THE DULY APPOINTED AGENT OF THE SANTA MARGARITA WATER DISTRICT, A PUBLIC CORPORATION IN ORANGE COUNTY, CALIFORNIA, PURSUANT TO ITS RESOLUTION NO. 88-10-2, DOES HEREBY ACCEPT ON BEHALF OF SAID DISTRICT, THE EASEMENTS FOR WATER, RECYCLED WATER, SEWER, DRAINAGE AND ACCESS PURPOSES AS DEDICATED AND SHOWN ON THIS TRACT MAP, BY AND BETWEEN THE SANTA MARGARITA WATER DISTRICT AND DMB LADERA, L.L.C., A DELAWARE LIMITED LIABILITY COMPANY, AND SHEA HOMES PARTNERSHIP, A CALIFORNIA LIMITED PARTNERSHIP, AND DOES HEREBY CERTIFY THAT THE GRANTEE CONSENTS TO THE RECORDATION OF SAID TRACT MAP.

Daniel R. Feron
DANIEL R. FERONS, CHIEF ENGINEER
SANTA MARGARITA WATER DISTRICT

NOTARY ACKNOWLEDGMENT - SANTA MARGARITA WATER DISTRICT

STATE OF CALIFORNIA } SS
COUNTY OF ORANGE }

ON DEC 4, 2003 BEFORE ME, Cindy R. Lane, Notary Public, PERSONALLY
APPEARED DANIEL R. FERONS, PERSONALLY KNOWN TO ME (OR PROVED TO ME ON THE BASIS OF SATISFACTORY EVIDENCE) TO BE THE PERSON WHOSE NAME IS SUBSCRIBED TO THE WITHIN INSTRUMENT AND ACKNOWLEDGED TO ME THAT HE EXECUTED THE SAME IN HIS AUTHORIZED CAPACITY, AND THAT BY HIS SIGNATURE ON THE INSTRUMENT THE PERSON, OR ENTITY UPON BEHALF OF WHICH THE PERSON ACTED, EXECUTED THE INSTRUMENT.

WITNESS MY HAND:

SIGNATURE Cindy R. Lane MY PRINCIPAL PLACE OF BUSINESS IS
NOTARY PUBLIC IN AND FOR SAID STATE IN Orange COUNTY.
CINDY R. LANE MY COMMISSION EXPIRES: 2-20-05
(NAME PRINTED)

SIGNATURE OMISSIONS:

PURSUANT TO THE PROVISIONS OF SECTION 66436(a)(3)(A)&(C) OF THE SUBDIVISION MAP ACT, THE FOLLOWING SIGNATURES HAVE BEEN OMITTED:

THE COUNTY OF ORANGE, HOLDER OF A SIDEWALK EASEMENT AS DEDICATED PER TRACT NO. 15987, M.M. 839/1-18.

DMB LADERA, L.L.C., A DELAWARE LIMITED LIABILITY COMPANY, HOLDER OF EASEMENTS AS RESERVED IN THE DEED RECORDED SEPTEMBER 16, 2003, AS INSTRUMENT NO. 2003001135590 OF OFFICIAL RECORDS. (EASEMENTS ARE BLANKET IN NATURE).

LADERA DEVELOPMENT COMPANY, L.L.C., HOLDER OF OIL, GAS AND MINERAL RIGHTS RECORDED DECEMBER 10, 1996, AS INSTRUMENT NO. 19960624029 OF OFFICIAL RECORDS.

853 pg 47

SHEET 2 OF 4 SHEETS
SCALE: 1" = 100'
26 NUMBERED LOTS AND
LOTS A THROUGH J, INCLUSIVE
ACREAGE 8.206 ACRES
(FINAL UNIT OF TENTATIVE
TRACT NO. 16387)

TRACT NO. 16387

IN THE UNINCORPORATED TERRITORY OF THE COUNTY OF ORANGE,
STATE OF CALIFORNIA

HUNSAKER AND ASSOCIATES IRVINE, INC.
RORY S. WILLIAMS, L.S. 6654
DATE OF SURVEY: JULY, 2003

SHEET INDEX AND GPS CONTROL MAP

3 INDICATES SHEET NUMBER

BASIS OF BEARINGS:
THE BEARINGS SHOWN ARE BASED ON THE BEARING BETWEEN O.C.S. HORIZONTAL CONTROL STATION GPS NO. 1417 AND STATION GPS NO. 1448 BEING 107°46'13"E PER RECORDS ON FILE IN THE OFFICE OF THE ORANGE COUNTY SURVEYOR.

DATUM STATEMENT:
COORDINATES SHOWN ARE BASED ON THE CALIFORNIA COORDINATE SYSTEM (CCS3), ZONE VI, 1983 NAD, (1997.35 EPOCH OCS GPS ADJUSTMENT). ALL DISTANCES SHOWN ARE GROUND, UNLESS OTHERWISE NOTED. TO OBTAIN GRID DISTANCE, MULTIPLY GROUND DISTANCE BY 0.999948295. THIS COMBINATION FACTOR IS PROJECT SPECIFIC.

NOTES:


- LOTS A AND B ARE PRIVATE STREETS.
- LOTS C THROUGH F, INCLUSIVE, AND LOTS H THROUGH J, INCLUSIVE, ARE FOR LANDSCAPE/OPEN SPACE PURPOSES.
- LOT G IS FOR POCKET PARK PURPOSES.

EASEMENT NOTES:

- (A) INDICATES AN EASEMENT FOR SEWER, WATER, RECYCLED WATER, DRAINAGE AND ACCESS PURPOSES DEDICATED HEREON TO THE SANTA MARGARITA WATER DISTRICT.
- (B) INDICATES AN EASEMENT FOR INGRESS AND EGRESS OF EMERGENCY AND PUBLIC SERVICE VEHICLES DEDICATED HEREON TO THE COUNTY OF ORANGE.
- (C) INDICATES AN EASEMENT FOR SEWER, WATER, RECYCLED WATER AND ACCESS PURPOSES DEDICATED TO THE SANTA MARGARITA WATER DISTRICT PER TRACT NO. 15987, M.M. 839/1-18.
- (D) INDICATES A SIDEWALK EASEMENT DEDICATED TO THE COUNTY OF ORANGE PER TRACT NO. 15987, M.M. 839/1-18.

MONUMENT NOTES:

- 2" I.P. TAGGED L.S. 6654 OR LEAD, TACK & TAG L.S. 6654 OR NAIL & TAG L.S. 6654 OR 8" SAW STAMPED L.S. 6654 TO BE SET AT ALL TRACT BOUNDARY CORNERS WITHIN 90 DAYS AFTER ACCEPTANCE OF IMPROVEMENTS, UNLESS OTHERWISE NOTED.
- 1" I.P. TAGGED L.S. 6654 OR LEAD, TACK & TAG L.S. 6654 OR NAIL & TAG L.S. 6654 OR 8" SAW STAMPED L.S. 6654 TO BE SET AT ALL LOT CORNERS, EXCEPT LOT CORNERS THAT ARE THE INTERSECTION OF SIDE LOT LINES WITH STREET RIGHT OF WAY, WITHIN 90 DAYS AFTER ACCEPTANCE OF IMPROVEMENTS, UNLESS OTHERWISE NOTED.
- 8" SAW STAMPED L.S. 6654 OR LEAD, TACK & TAG L.S. 6654 OR 1" I.P. TAGGED L.S. 6654 TO BE SET AT ALL STREET CENTERLINE POINTS OF CONTROL, WITHIN 90 DAYS AFTER ACCEPTANCE OF IMPROVEMENTS, UNLESS OTHERWISE NOTED.
- LEAD, TACK & TAG L.S. 6654 TO BE SET IN CONCRETE SIDEWALK AT AN OFFSET ALONG FRONT SIDE LOT LINES PRODUCED, IN LIEU OF AT FRONT LOT CORNERS, WITHIN 90 DAYS AFTER ACCEPTANCE OF IMPROVEMENTS, UNLESS OTHERWISE NOTED. BEARING AND DISTANCE OF OFFSET IS AS NOTED HEREON.
- INDICATES FOUND MONUMENT AS NOTED.
- INDICATES NOTHING TO BE SET PER SUBJECT MAP OR ADJACENT MAP.
- ▲ INDICATES FOUND ORANGE COUNTY GPS CONTROL MONUMENT, AS NOTED.
- P# INDICATES BEARING AND DISTANCE OF LOT LINE PRODUCTION FROM LOT CORNER TO MONUMENT.
- 1 INDICATES LOCATION OF 1" I.P. TAGGED "P.L.S. 5557" OR SAW STAMPED "P.L.S. 5557" OR LEAD, TACK & TAG "P.L.S. 5557" TO BE SET PER TRACT NO. 16156, M.M. 812/40-48.
- 2 INDICATES LOCATION OF 1" I.P. TAGGED "P.L.S. 5557" OR SAW STAMPED "P.L.S. 5557" OR LEAD, TACK & TAG "P.L.S. 5557" TO BE SET PER TRACT NO. 15987, M.M. 839/1-18.
- 3 INDICATES FOUND O.C.S. WELL MONUMENT W/2 1/2" BRASS DISK STAMPED "ORANGE COUNTY SURVEYOR" PER TRACT NO. 16156, M.M. 812/40-48.
- 4 INDICATES LOCATION OF 2" I.P. TAGGED L.S. 6654 OR LEAD, TACK & TAG L.S. 6654 OR 8" SAW STAMPED L.S. 6654 TO BE SET PER TRACT NO. 16388, M.M. 854/1-5.
- 5 INDICATES LOCATION OF 8" SAW STAMPED L.S. 6654 OR LEAD, TACK & TAG L.S. 6654 OR 1" I.P. TAGGED L.S. 6654 TO BE SET PER TRACT NO. 16388, M.M. 854/1-5.

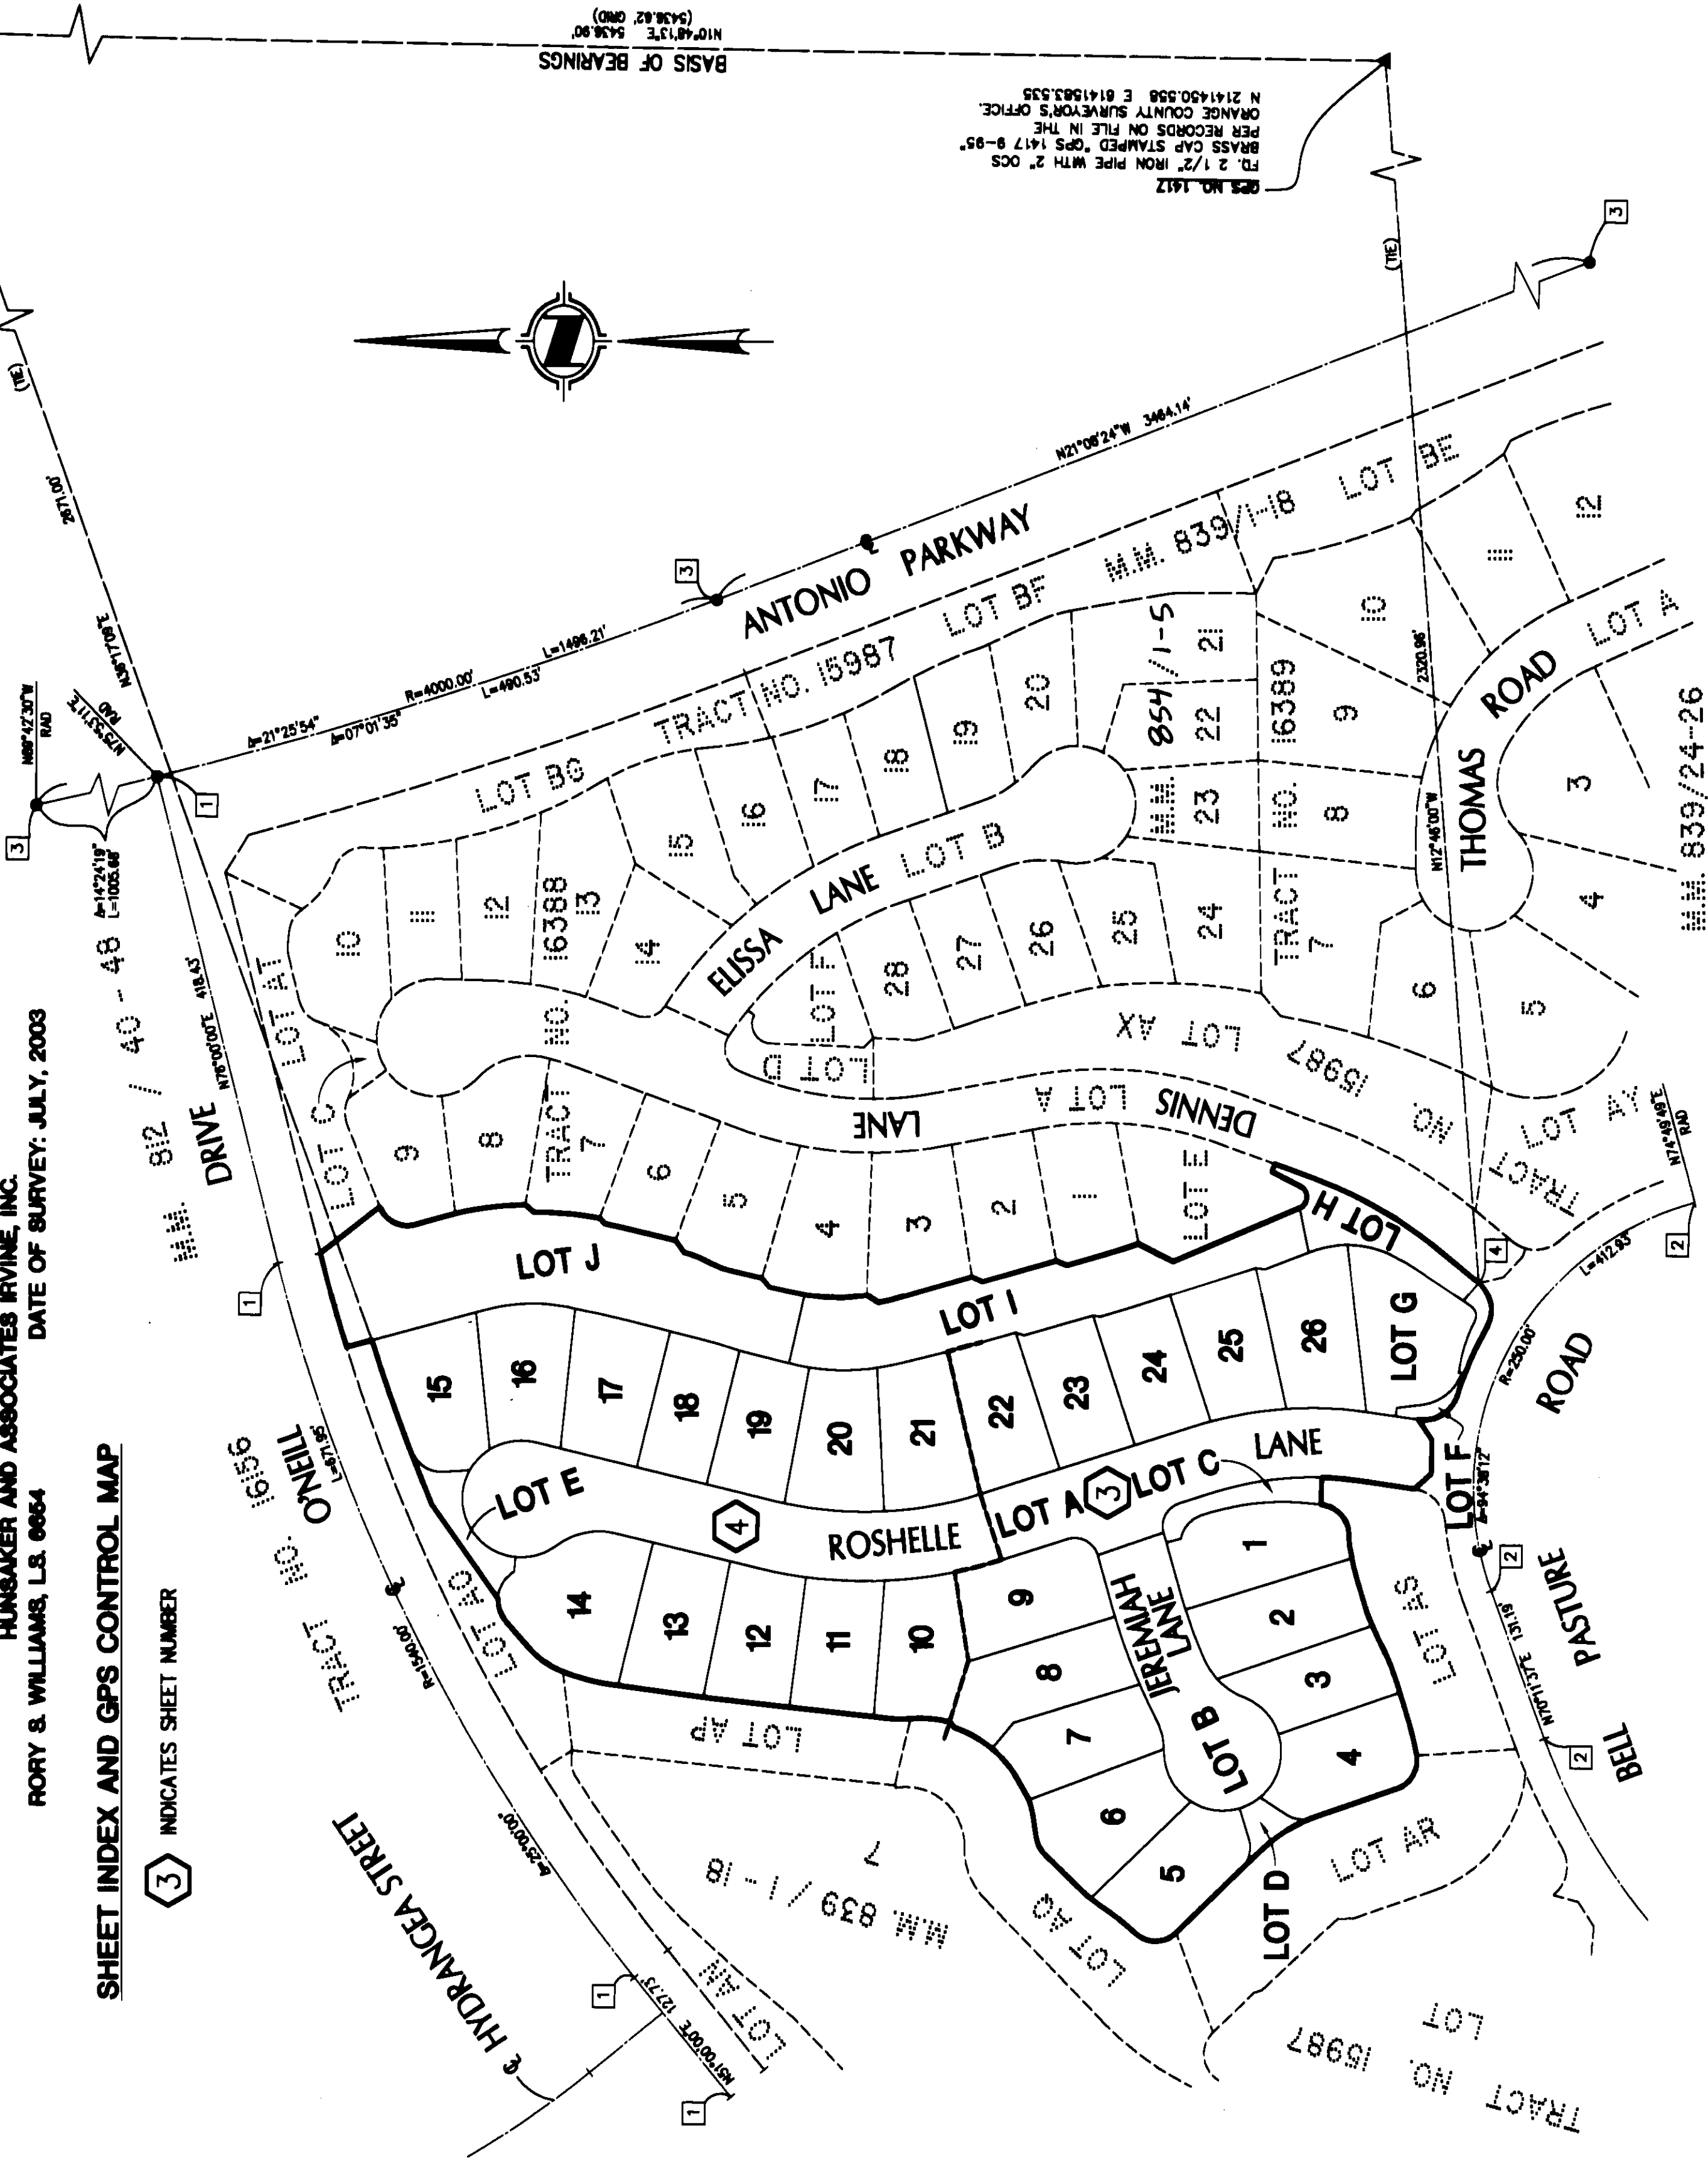

GPS NO. 1448
FD. 2" IRON PIPE WITH 1-3/4" OCS
BRASS CAP STAMPED "1448 9-95"
PER RECORDS ON FILE IN THE
ORANGE COUNTY SURVEYOR'S OFFICE
N 2146790.819 E 6142602.595

GPS NO. 1417
FD. 2 1/2" IRON PIPE WITH 2" OCS
BRASS CAP STAMPED GPS 1417 8-95
PER RECORDS ON FILE IN THE
ORANGE COUNTY SURVEYOR'S OFFICE
N 2141450.558 E 6141583.535

N 10°48'13"E
S 43°06'00"E
(5438.82' ONS)

**SHEET 3 OF 4 SHEETS
SCALE: 1" = 40'
26 NUMBERED LOTS AND
LOTS A THROUGH J, INCLUSIVE
ACREAGE: 8.285 ACRES
(FINAL UNIT OF TENTATIVE
TRACT NO. 10387)**


HUNSAKER AND ASSOCIATES IRVINE, INC.
RORY S. WILLIAMS, L.S. 9854 DATE OF SURV

DATE OF SURVEY: JULY, 2003
SHEET 4

SEE SHEET

MONUMENT OFFSET TABLE		
LINE	BEARING	LENGTH
P1	N15°30'05"W	16.75'
P2	N17°08'57"W	10.75'
P3	N18°57'16"W	11.50'
P4	N18°57'16"W	10.75'
P5	N35°28'11"E	11.39'
P6	N17°32'15"E	10.75'
P7	S43°45'50"E	11.13'
P8	S40°29'23"E	11.23'
P9	S16°32'43"E	10.62'
P10	S16°32'43"E	10.75'
P11	N81°24'20"E	10.76'
P24	S72°11'26"W	10.79'
P25	S72°11'26"W	14.75'
P26	S72°17'58"W	14.75'
P27	S72°17'58"W	10.76'
P28	S71°50'10"W	10.87'
P29	S85°32'51"W	11.11'

**SEE SHEET 2 FOR BASIS OF BEARINGS,
DATUM STATEMENT, MONUMENT NOTES,
SHEET INDEX AND GPS CONTROL MAP,
EASEMENT NOTES AND NOTES.**

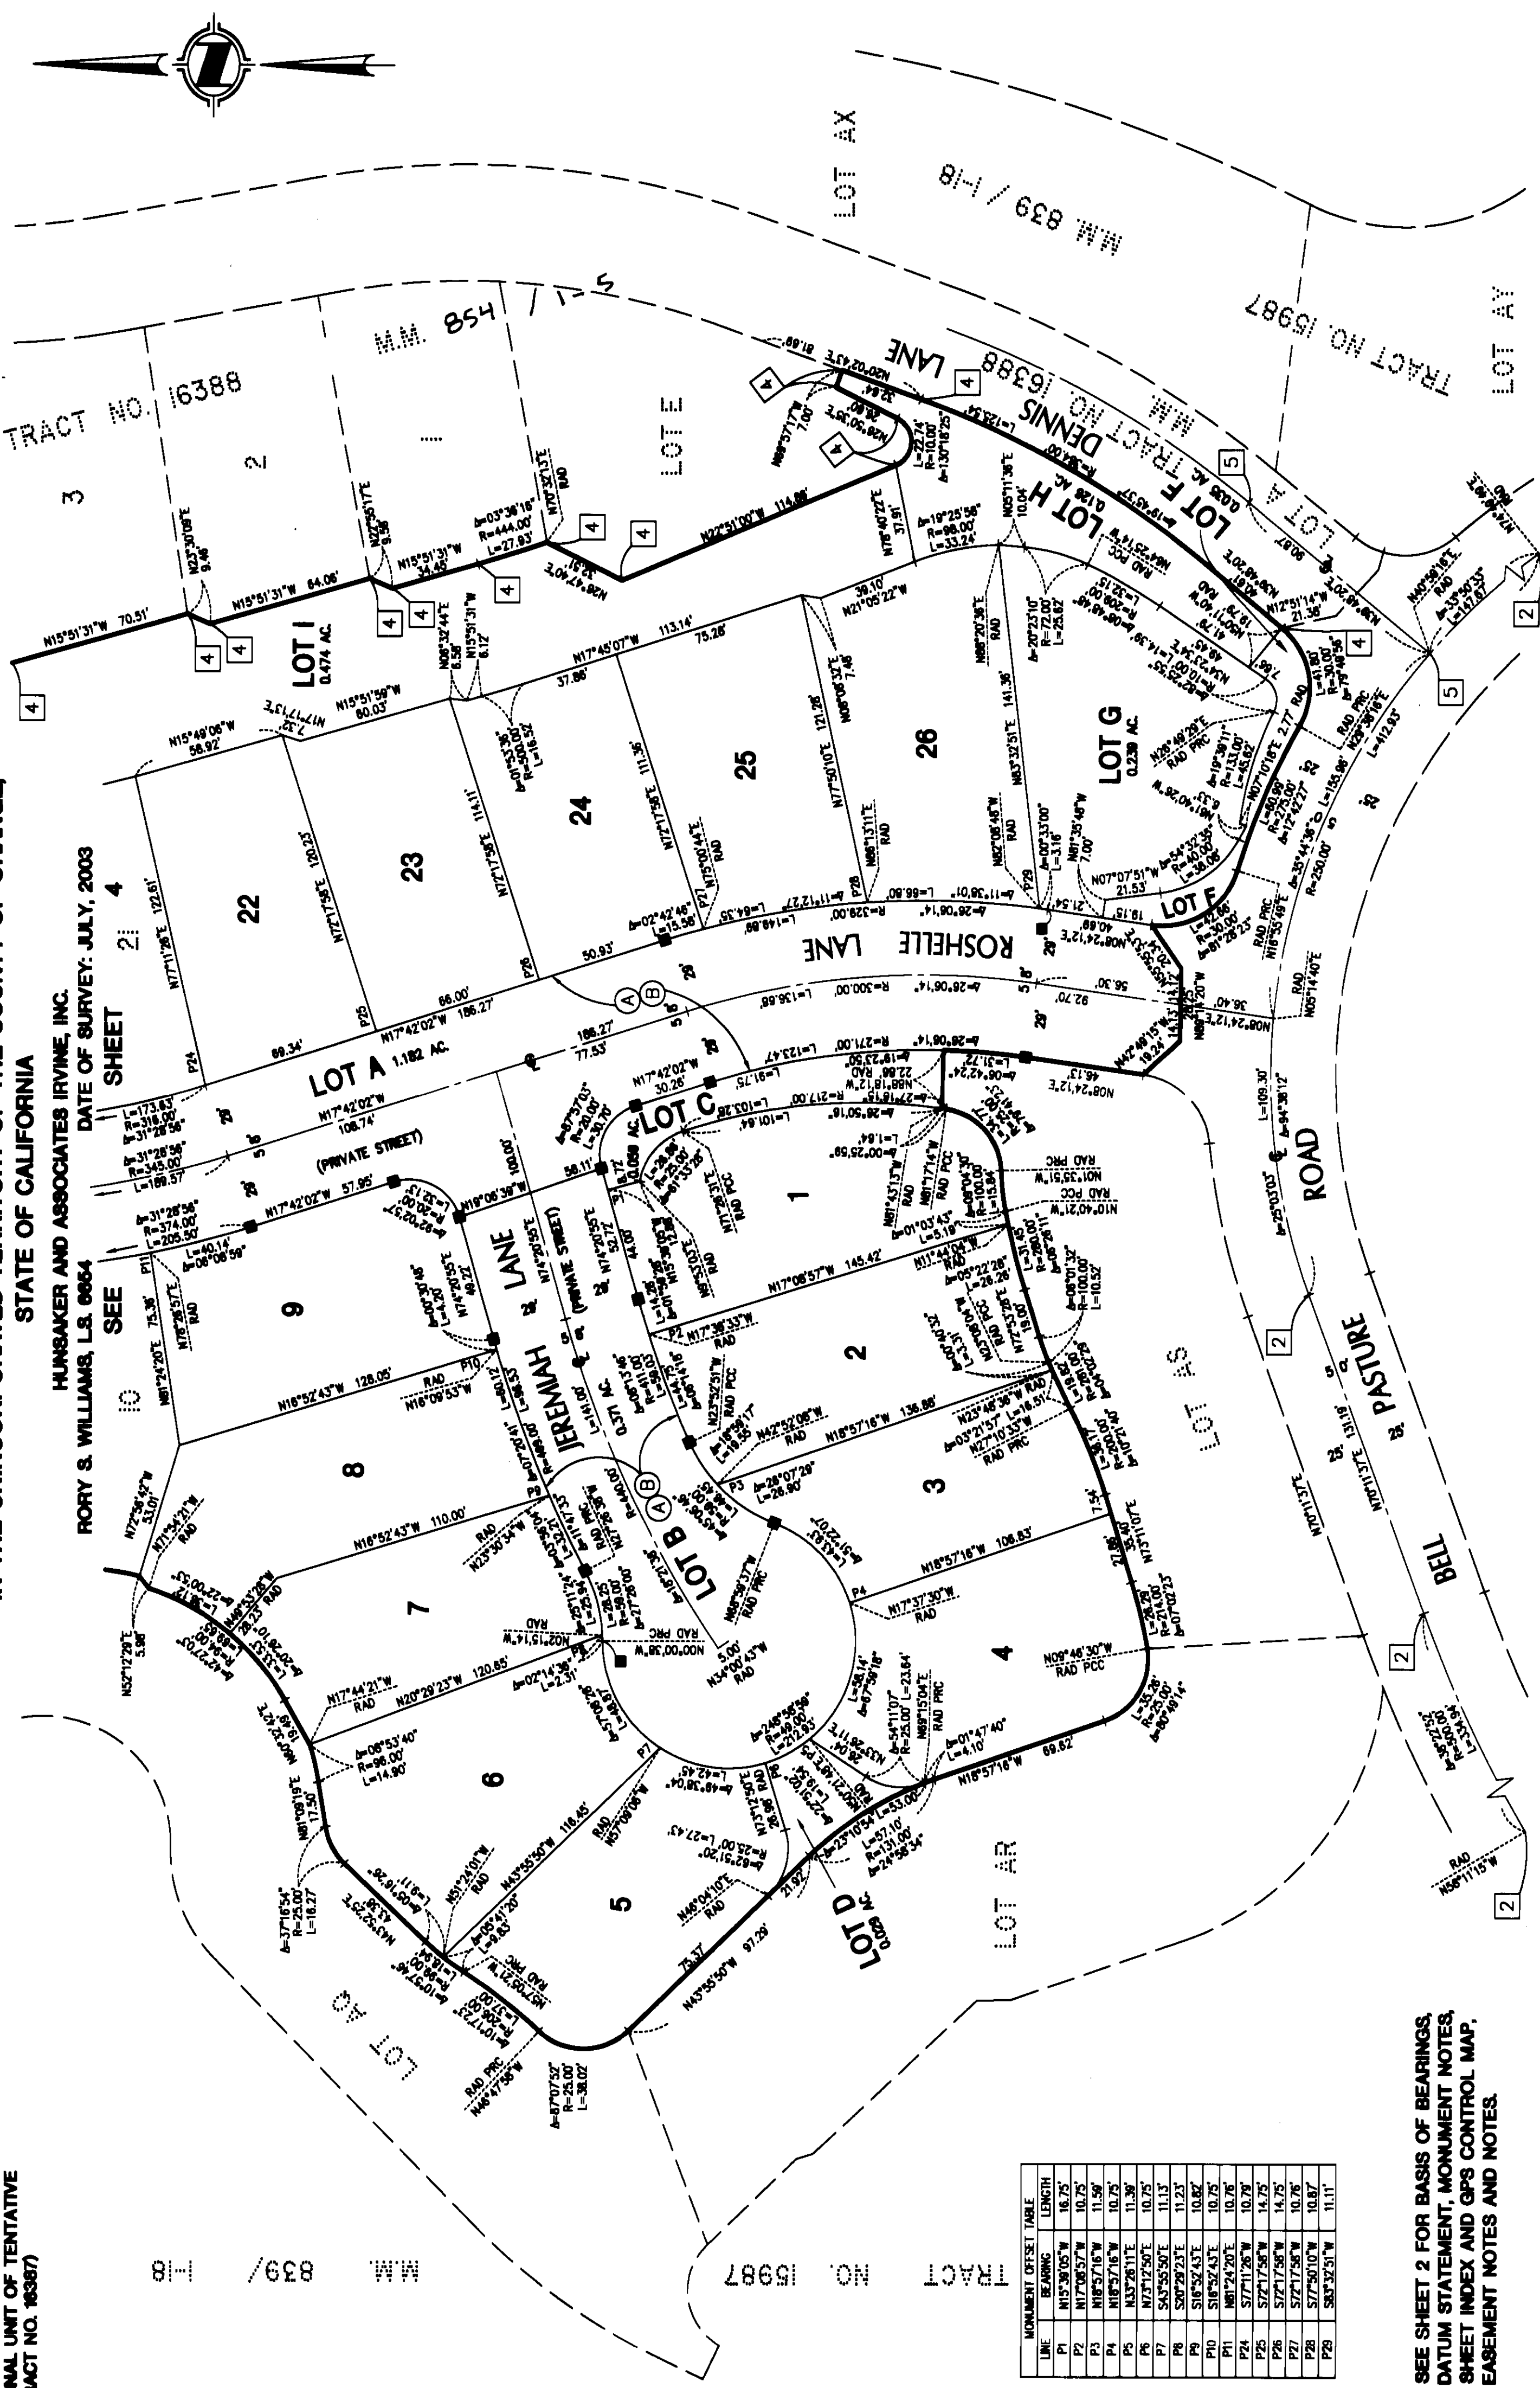


SHEET 4 OF 4 SHEETS
SCALE: 1" = 40'
20 NUMBERED LOTS AND
LOTS A THROUGH J, INCLUSIVE
ACREAGE: 8.286 ACRES
(FINAL UNIT OF TENTATIVE
TRACT NO. 16387)

TRACT NO. 16387

IN THE UNINCORPORATED TERRITORY OF THE COUNTY OF ORANGE,
STATE OF CALIFORNIA

HUNSAKER AND ASSOCIATES IRVINE, INC.
RORY S. WILLIAMS, L.S. 6654

DATE OF SURVEY: JULY, 2003

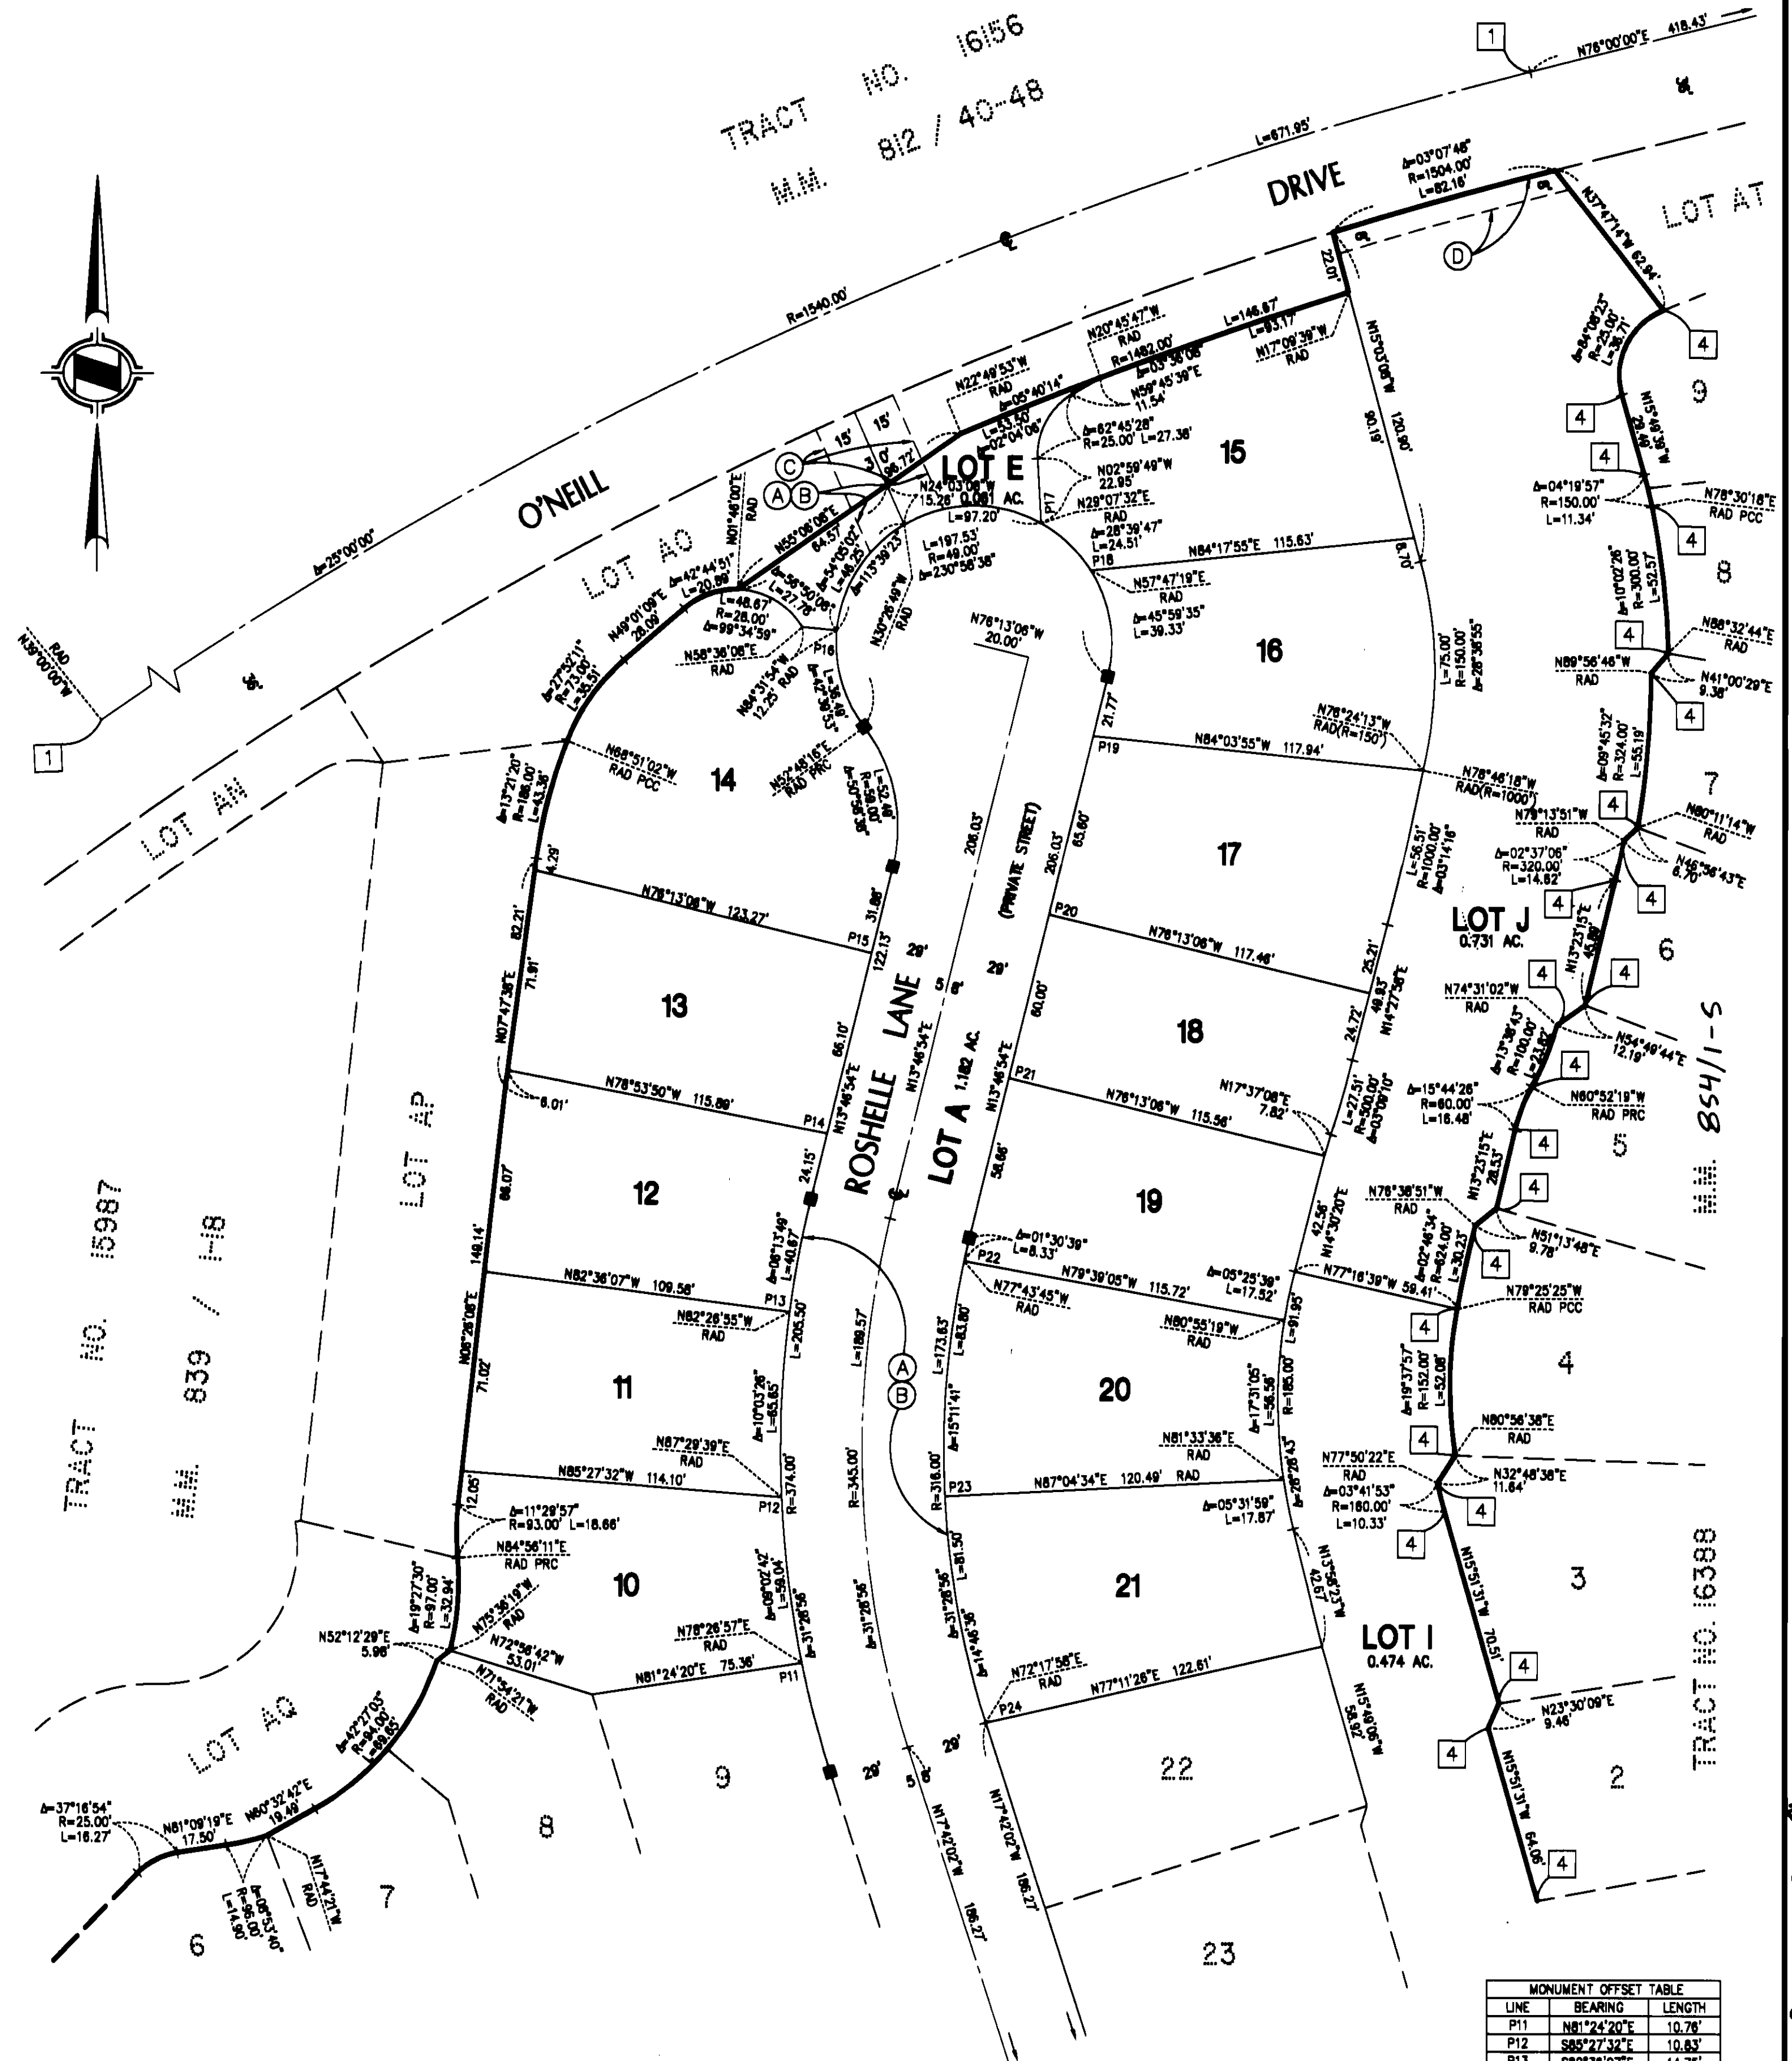

SEE SHEET 3

SEE SHEET 2 FOR BASIS OF BEARINGS,
DATUM STATEMENT, MONUMENT NOTES,
SHEET INDEX AND GPS CONTROL MAP,
EASEMENT NOTES AND NOTES.