

SHEET 1 OF 6 SHEETS
28 NUMBERED LOTS AND
LOTS A THROUGH F, INCLUSIVE
ACREAGE: 7.696 ACRES
(PORTION OF TENTATIVE
TRACT NO. 16387)

TRACT NO. 16388

IN UNINCORPORATED TERRITORY OF THE COUNTY OF ORANGE,
STATE OF CALIFORNIA.

BEING A SUBDIVISION OF LOT 9 OF TRACT NO. 16987, AS PER MAP FILED
IN BOOK 839, PAGES 1 THROUGH 18, INCLUSIVE, OF MISCELLANEOUS
MAPS, IN THE OFFICE OF THE COUNTY RECORDER OF SAID COUNTY.

HUNSAKER AND ASSOCIATES IRVINE, INC.
RORY S. WILLIAMS, L.S. 6654 DATE OF SURVEY: JULY, 2003

ACCEPTED AND FILED AT THE
REQUEST OF
First American Title Company
DATE: January 30, 2004
TIME: 9:39 a.m. FEE: \$1900
INSTRUMENT NO. 2004000071844
BOOK 854 PAGE 1-5
TOM DALY
COUNTY CLERK - RECORDER
BY Julia Escanuela
DEPUTY

OWNERSHIP CERTIFICATE:

WE, THE UNDERSIGNED, BEING ALL PARTIES HAVING ANY RECORD TITLE INTEREST IN THE LAND COVERED BY THIS MAP, DO HEREBY CONSENT TO THE PREPARATION AND RECORDATION OF SAID MAP, AS SHOWN WITHIN THE DISTINCTIVE BORDER LINE.

WE HEREBY DEDICATE TO COUNTY OF ORANGE AN EASEMENT FOR EMERGENCY ACCESS PURPOSES OVER ALL OF LOTS A AND B, AS SHOWN ON SAID MAP.

WE ALSO HEREBY DEDICATE TO THE SANTA MARGARITA WATER DISTRICT THE EASEMENTS FOR WATER, RECYCLED WATER, SEWER AND ACCESS PURPOSES OVER THOSE EASEMENT AREAS AS SHOWN ON SAID MAP, WHICH EASEMENTS SHALL BE SUBJECT TO THE SAME CONDITIONS AS SHOWN IN THAT CERTAIN GRANT OF EASEMENT TO SANTA MARGARITA WATER DISTRICT RECORDED SEPTEMBER 18, 2002, AS INSTRUMENT NO. 20020799401 OF OFFICIAL RECORDS, COUNTY OF ORANGE.

SHEA HOMES LIMITED PARTNERSHIP, A CALIFORNIA LIMITED PARTNERSHIP, OWNER.

BY: J.F. SHEA LLC, A DELAWARE LIMITED LIABILITY COMPANY,
ITS GENERAL PARTNER.

BY: Marion P. Marcum BY: John C. Danvers
NAME: MARION P. MARCUM NAME: JOHN C. DANVERS
TITLE: ASSISTANT SECRETARY TITLE: Assistant Secretary

DMB LADERA L.L.C., A DELAWARE LIMITED LIABILITY COMPANY, BENEFICIARY UNDER
DEED OF TRUST RECORDED SEPTEMBER 16, 2003, AS INSTRUMENT NO.
2003001135592 OF OFFICIAL RECORDS.

BY: RANCHO MISSION VIEJO, L.L.C., A DELAWARE LIMITED LIABILITY COMPANY, ITS
AUTHORIZED AGENT AND MANAGER.

BY: Donald T. Stahl BY: Gregory S. Edwards
NAME: Donald T. Stahl NAME: Gregory S. Edwards
TITLE: Vice President TITLE: S.A. R/CFO

NOTARY ACKNOWLEDGMENT:

STATE OF CALIFORNIA }
COUNTY OF ORANGE } SS

ON Nov 17, 2003, BEFORE ME, Beth A. Hutchinson, PERSONALLY
APPEARED Marion P. Marcum AND John C. Danvers PERSONALLY
KNOWN TO ME (OR PROVED TO ME ON THE BASIS OF SATISFACTORY EVIDENCE) TO BE THE PERSON(S)
WHOSE NAME(S) is/are SUBSCRIBED TO THE WITHIN INSTRUMENT AND ACKNOWLEDGED TO ME THAT
he/she/they EXECUTED THE SAME IN his/her/their AUTHORIZED CAPACITY(IES), AND THAT BY
his/her/their SIGNATURE(S) ON THE INSTRUMENT THE PERSON(S), OR ENTITY UPON BEHALF OF
WHICH THE PERSON(S) ACTED, EXECUTED THE INSTRUMENT.

WITNESS MY HAND:

SIGNATURE Beth A. Hutchinson MY PRINCIPAL PLACE OF BUSINESS IS
NOTARY PUBLIC IN AND FOR SAID STATE IN Orange COUNTY.
Beth A. Hutchinson MY COMMISSION EXPIRES May 8, 2005
(NAME PRINTED)

STATE OF CALIFORNIA }
COUNTY OF ORANGE } SS

ON Dec 1, 2003, BEFORE ME, Diana L. Binks, Notary Public PERSONALLY
APPEARED Donald T. Stahl AND Gregory S. Edwards PERSONALLY
KNOWN TO ME (OR PROVED TO ME ON THE BASIS OF SATISFACTORY EVIDENCE) TO BE THE PERSON(S)
WHOSE NAME(S) is/are SUBSCRIBED TO THE WITHIN INSTRUMENT AND ACKNOWLEDGED TO ME THAT
he/she/they EXECUTED THE SAME IN his/her/their AUTHORIZED CAPACITY(IES), AND THAT BY
his/her/their SIGNATURE(S) ON THE INSTRUMENT THE PERSON(S), OR ENTITY UPON BEHALF OF
WHICH THE PERSON(S) ACTED, EXECUTED THE INSTRUMENT.

WITNESS MY HAND:

SIGNATURE Diana L. Binks MY PRINCIPAL PLACE OF BUSINESS IS
NOTARY PUBLIC IN AND FOR SAID STATE IN Orange COUNTY.
Diana L. Binks MY COMMISSION EXPIRES: 12-12-06
(NAME PRINTED)

AUTOMATIC FIRE SPRINKLER NOTE:

ALL COMMERCIAL STRUCTURES GREATER THAN 6,000 SQUARE FEET, ALL MULTIFAMILY
RESIDENTIAL STRUCTURES, ALL SINGLE-FAMILY STRUCTURES EXCEEDING 5,500 SQUARE FEET,
AND ALL STRUCTURES EXCEEDING FIRE DEPARTMENT ACCESS REQUIREMENTS SHALL BE
PROTECTED BY AN AUTOMATIC FIRE SPRINKLER SYSTEM.

SPECIAL FIRE PROTECTION NOTE:

SUBJECT PROPERTY IS IN A SPECIAL FIRE PROTECTION AREA AND MUST MEET ALL
REQUIREMENTS FOR DEVELOPMENT WITHIN THE AREA.

HIGH FIRE HAZARD AREA NOTE:

THE LOTS SHOWN ON THIS MAP ARE IN A HIGH FIRE HAZARD AREA DUE TO WILDLAND
EXPOSURE.

NOTE:

"THE PRIVATE STREETS CONSTRUCTED WITHIN THIS MAP SHALL BE OWNED, OPERATED AND
MAINTAINED BY THE DEVELOPER, SUCCESSORS OR ASSIGNS. THE COUNTY OF ORANGE SHALL
HAVE NO RESPONSIBILITY THEREFOR, UNLESS PURSUANT TO APPROPRIATE SECTIONS OF THE
STREETS AND HIGHWAYS CODE OF THE STATE OF CALIFORNIA, THE SAID PRIVATE STREETS HAVE
BEEN ACCEPTED INTO THE COUNTY ROAD SYSTEM BY APPROPRIATE RESOLUTION OF THE
ORANGE COUNTY BOARD OF SUPERVISORS."

SURVEYOR'S STATEMENT:

THIS MAP WAS PREPARED BY ME OR UNDER MY DIRECTION AND IS BASED UPON A FIELD SURVEY
IN CONFORMANCE WITH THE REQUIREMENTS OF THE SUBDIVISION MAP ACT AND LOCAL ORDINANCE
AT THE REQUEST OF DMB LADERA, L.L.C., IN JULY, 2003. I HEREBY STATE THAT ALL MONUMENTS
ARE OF THE CHARACTER AND OCCUPY THE POSITIONS INDICATED, OR THAT THEY WILL BE SET IN
SUCH POSITIONS; AND THAT SAID MONUMENTS ARE SUFFICIENT TO ENABLE THE SURVEY TO BE
RETRACED. I HEREBY STATE THAT THIS FINAL MAP SUBSTANTIALLY CONFORMS TO THE
CONDITIONALLY APPROVED TENTATIVE MAP.

Rory S. Williams 12/02/03
RORY S. WILLIAMS, L.S. 6654 DATE
LICENSE EXPIRES: 12/31/03




COUNTY SURVEYOR'S STATEMENT

I HEREBY STATE THAT I HAVE EXAMINED THIS MAP AND HAVE FOUND IT TO BE SUBSTANTIALLY
IN CONFORMANCE WITH THE TENTATIVE MAP AS FILED WITH, AMENDED AND APPROVED BY THE
ORANGE COUNTY SUBDIVISION COMMITTEE; THAT ALL PROVISIONS OF THE SUBDIVISION MAP ACT
AND COUNTY SUBDIVISION REGULATIONS HAVE BEEN COMPLIED WITH AND I AM SATISFIED SAID
MAP IS TECHNICALLY CORRECT.

DATED THIS 8th DAY OF JANUARY, 2004.

Michael K. Sullivan
JOHN CANAS COUNTY SURVEYOR
L.S. 4408 EXPIRATION DATE: 9/30/05 BY: Michael K. Sullivan DEPUTY
L.S. 6834 EXPIRES 8/30/05

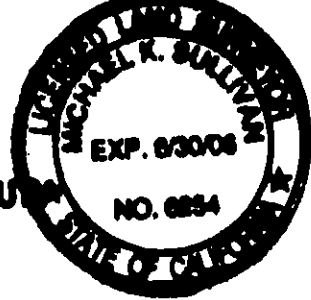

COUNTY TREASURER-TAX COLLECTOR'S CERTIFICATE:

STATE OF CALIFORNIA }
COUNTY OF ORANGE } SS

I HEREBY CERTIFY THAT ACCORDING TO THE RECORDS OF MY OFFICE THERE ARE NO LIENS
AGAINST THE LAND COVERED BY THIS MAP OR ANY PART THEREOF FOR UNPAID STATE,
COUNTY, MUNICIPAL OR LOCAL TAXES OR SPECIAL ASSESSMENTS COLLECTED AS TAXES,
EXCEPT TAXES OR SPECIAL ASSESSMENTS COLLECTED AS TAXES NOT YET PAYABLE.

AND DO CERTIFY TO THE RECORDER OF ORANGE COUNTY THAT THE PROVISIONS OF
THE SUBDIVISION MAP ACT HAVE BEEN COMPLIED WITH REGARDING DEPOSITS TO SECURE
PAYMENT OF TAXES OR SPECIAL ASSESSMENTS COLLECTED AS TAXES ON THE LAND
GOVERNED BY THIS MAP.

DATED THIS 2nd DAY OF January, 2004.

John M.W. Moorlach BY: John M.W. Moorlach
COUNTY TREASURER-TAX COLLECTOR DEPUTY TREASURER-TAX COLLECTOR

CLERK OF THE BOARD OF SUPERVISORS' CERTIFICATE:

STATE OF CALIFORNIA }
COUNTY OF ORANGE } SS

I HEREBY CERTIFY THAT THIS MAP WAS PRESENTED FOR APPROVAL TO THE BOARD OF
SUPERVISORS OF THE COUNTY OF ORANGE AT REGULAR MEETING THEREOF HELD ON
THE 27th DAY OF January, 2004, AND THAT THEREUPON SAID
BOARD DID, BY AN ORDER DULY PASSED AND ENTERED, APPROVE SAID MAP.

AND DID ACCEPT ON BEHALF OF THE COUNTY OF ORANGE THE EASEMENTS FOR EMERGENCY
ACCESS PURPOSES OVER ALL OF LOTS A AND B, AS DEDICATED.

DATED THIS 27th DAY OF January, 2004.

Darlene J. Bloom
CLERK OF THE BOARD OF SUPERVISORS
DARLENE J. BLOOM



CERTIFICATE OF ACCEPTANCE - SANTA MARGARITA WATER DISTRICT

THE UNDERSIGNED, BEING THE DULY APPOINTED AGENT OF THE SANTA MARGARITA WATER
DISTRICT, A PUBLIC CORPORATION IN ORANGE COUNTY, CALIFORNIA, PURSUANT TO ITS
RESOLUTION NO. 88-10-2, DOES HEREBY ACCEPT ON BEHALF OF SAID DISTRICT, THE EASEMENTS
FOR WATER, RECYCLED WATER, SEWER AND ACCESS PURPOSES AS DEDICATED AND
SHOWN ON THIS TRACT MAP, BY AND BETWEEN THE SANTA MARGARITA WATER DISTRICT AND SHEA
HOMES LIMITED PARTNERSHIP, A CALIFORNIA LIMITED PARTNERSHIP AND DOES HEREBY CERTIFY THAT THE
GRANTEE CONSENTS TO THE RECORDATION OF SAID TRACT MAP.

Daniel R. Feron
DANIEL R. FERONS, CHIEF ENGINEER
SANTA MARGARITA WATER DISTRICT

NOTARY ACKNOWLEDGMENT - SANTA MARGARITA WATER DISTRICT

STATE OF CALIFORNIA }
COUNTY OF ORANGE } SS

ON Dec 17, 2003, BEFORE ME, Cindy R. Lane, Notary Public PERSONALLY
APPEARED Daniel R. Feron, PERSONALLY KNOWN TO ME (OR PROVED TO ME ON THE BASIS
OF SATISFACTORY EVIDENCE) TO BE THE PERSON WHOSE NAME IS SUBSCRIBED TO THE WITHIN
INSTRUMENT AND ACKNOWLEDGED TO ME THAT HE EXECUTED THE SAME IN HIS AUTHORIZED
CAPACITY, AND THAT BY HIS SIGNATURE ON THE INSTRUMENT THE PERSON, OR ENTITY UPON
BEHALF OF WHICH THE PERSON ACTED, EXECUTED THE INSTRUMENT.

WITNESS MY HAND:

SIGNATURE Cindy R. Lane MY PRINCIPAL PLACE OF BUSINESS IS
NOTARY PUBLIC IN AND FOR SAID STATE IN Orange COUNTY.
CINDY R. LANE MY COMMISSION EXPIRES: 2-20-2005
(NAME PRINTED)

SIGNATURE OMISSIONS:

PURSUANT TO THE PROVISIONS OF SECTION 66436(o)(3)(A)(C) OF THE SUBDIVISION MAP ACT,
THE FOLLOWING SIGNATURES HAVE BEEN OMITTED:

DMB LADERA, L.L.C., A DELAWARE LIMITED LIABILITY COMPANY, HOLDER OF EASEMENTS RESERVED
IN THE DEED RECORDED SEPTEMBER 16, 2003, AS INSTRUMENT NO. 2003001135592 OF OFFICIAL
RECORDS. (EASEMENTS ARE BLANKET IN NATURE).

LADERA DEVELOPMENT COMPANY, L.L.C., HOLDER OF OIL, GAS AND MINERAL RIGHTS RECORDED
DECEMBER 10, 1996, AS INSTRUMENT NO. 19960624029 OF OFFICIAL RECORDS.

SHEET 2 OF 3 SHEETS
SCALE: 1" = 100'
28 NUMBERED LOTS AND
LOTS A THROUGH F, INCLUSIVE
ACREAGE: 7.696 ACRES
(PORTION OF TENTATIVE
TRACT NO. 16387)

BASIS OF BEARINGS:
THE BEARINGS SHOWN HEREON ARE BASED ON THE BEARING BETWEEN O.C.S. HORIZONTAL CONTROL STATION GPS NO. 1417 AND STATION GPS NO. 1448 BEING NOTED IN THE PER RECORDS ON FILE IN THE OFFICE OF THE ORANGE COUNTY SURVEYOR.

DATUM STATEMENT:
COORDINATES SHOWN ARE BASED ON THE CALIFORNIA COORDINATE SYSTEM (CCS83), ZONE VI, 1983 NAD, (1981.35 EPOCH OCS GPS ADJUSTMENT). ALL DISTANCES SHOWN ARE GROUND, UNLESS OTHERWISE NOTED. TO OBTAIN GRID DISTANCE, MULTIPLY GROUND DISTANCE BY 0.999948295. THIS COMBINATION FACTOR IS PROJECT SPECIFIC.

NOTES:
LOTS A AND B ARE PRIVATE STREETS.
LOTS C AND D ARE FOR LANDSCAPING/OPEN SPACE PURPOSES.
LOT E IS FOR POCKET PARK PURPOSES.

- EASEMENT NOTES:**
- (A) INDICATES AN EASEMENT FOR SEWER, WATER, RECYCLED WATER AND ACCESS PURPOSES DEDICATED HEREON TO THE SANTA MARGARITA WATER DISTRICT.
 - (B) INDICATES AN EASEMENT FOR EMERGENCY ACCESS PURPOSES OVER ALL OF LOTS A AND B DEDICATED HEREON TO THE COUNTY OF ORANGE.
 - (C) INDICATES AN EASEMENT FOR WATER LINE PURPOSES DEDICATED HEREON TO THE SANTA MARGARITA WATER DISTRICT.

MONUMENT NOTES:

- 2" IP TAGGED L.S. 6654 OR LEAD, TACK & TAG L.S. 6654 OR NAIL & TAG L.S. 6654 OR 8" SAW STAMPED L.S. 6654 TO BE SET AT ALL TRACT BOUNDARY CORNERS WITHIN 90 DAYS AFTER ACCEPTANCE OF IMPROVEMENTS, UNLESS OTHERWISE NOTED.
- 1" IP, TAGGED L.S. 6654 OR LEAD, TACK & TAG L.S. 6654 OR NAIL & TAG L.S. 6654 OR 8" SAW STAMPED L.S. 6654 TO BE SET AT ALL LOT CORNERS, EXCEPT LOT CORNERS THAT ARE THE INTERSECTION OF SIDE LOT LINES WITH STREET RIGHT OF WAY, WITHIN 90 DAYS AFTER ACCEPTANCE OF IMPROVEMENTS, UNLESS OTHERWISE NOTED.
- 8" SAW STAMPED L.S. 6654 OR LEAD, TACK & TAG L.S. 6654 OR 1" IP, TAGGED L.S. 6654 TO BE SET AT ALL STREET CENTERLINE POINTS OF CONTROL, WITHIN 90 DAYS AFTER ACCEPTANCE OF IMPROVEMENTS, UNLESS OTHERWISE NOTED.
- LEAD, TACK & TAG L.S. 6654 TO BE SET IN CONCRETE SIDEWALK AT AN OFFSET ALONG FRONT SIDE LOT LINES PRODUCED IN LIEU OF AT FRONT LOT CORNERS, WITHIN 90 DAYS AFTER ACCEPTANCE OF IMPROVEMENTS, UNLESS OTHERWISE NOTED. BEARING AND DISTANCE OF OFFSET IS AS NOTED HEREON.
- INDICATES FOUND MONUMENT, AS NOTED.
- INDICATES NOTHING TO BE SET PER SUBJECT MAP OR ADJACENT MAP.
- ▲ INDICATES FOUND ORANGE COUNTY GPS CONTROL MONUMENT, AS NOTED.
- P# INDICATES BEARING AND DISTANCE OF LOT LINE PRODUCTION FROM LOT CORNER TO MONUMENT.
- 1 INDICATES LOCATION OF 2" IP, TAGGED "P.L.S. 5557" OR SAW STAMPED "P.L.S. 5557" OR LEAD, TACK & TAG "P.L.S. 5557" TO BE SET PER TRACT NO. 15987, M.M. 839/1-18.
- 2 INDICATES LOCATION OF 1" IP, TAGGED "P.L.S. 5557" OR SAW STAMPED "P.L.S. 5557" OR LEAD, TACK & TAG "P.L.S. 5557" TO BE SET PER TRACT NO. 15987, M.M. 839/1-18.
- 3 INDICATES FOUND O.C.S. WELL MONUMENT W/2 1/2" BRASS DISK STAMPED "ORANGE COUNTY SURVEYOR" PER TRACT NO. 16156, M.M. 812/40-48.
- 4 INDICATES LOCATION OF 1" IP, TAGGED "P.L.S. 5557" OR SAW STAMPED "P.L.S. 5557" OR LEAD, TACK & TAG "P.L.S. 5557" TO BE SET PER TRACT NO. 16156, M.M. 812/40-48.


TRACT NO. 16388

IN THE UNINCORPORATED TERRITORY OF THE COUNTY OF ORANGE,
STATE OF CALIFORNIA

HUNSAKER AND ASSOCIATES IRVINE, INC.
RORY S. WILLIAMS, L.S. 6664
DATE OF SURVEY: JULY, 2003


SHEET INDEX AND GPS CONTROL MAP

3 INDICATES SHEET NUMBER

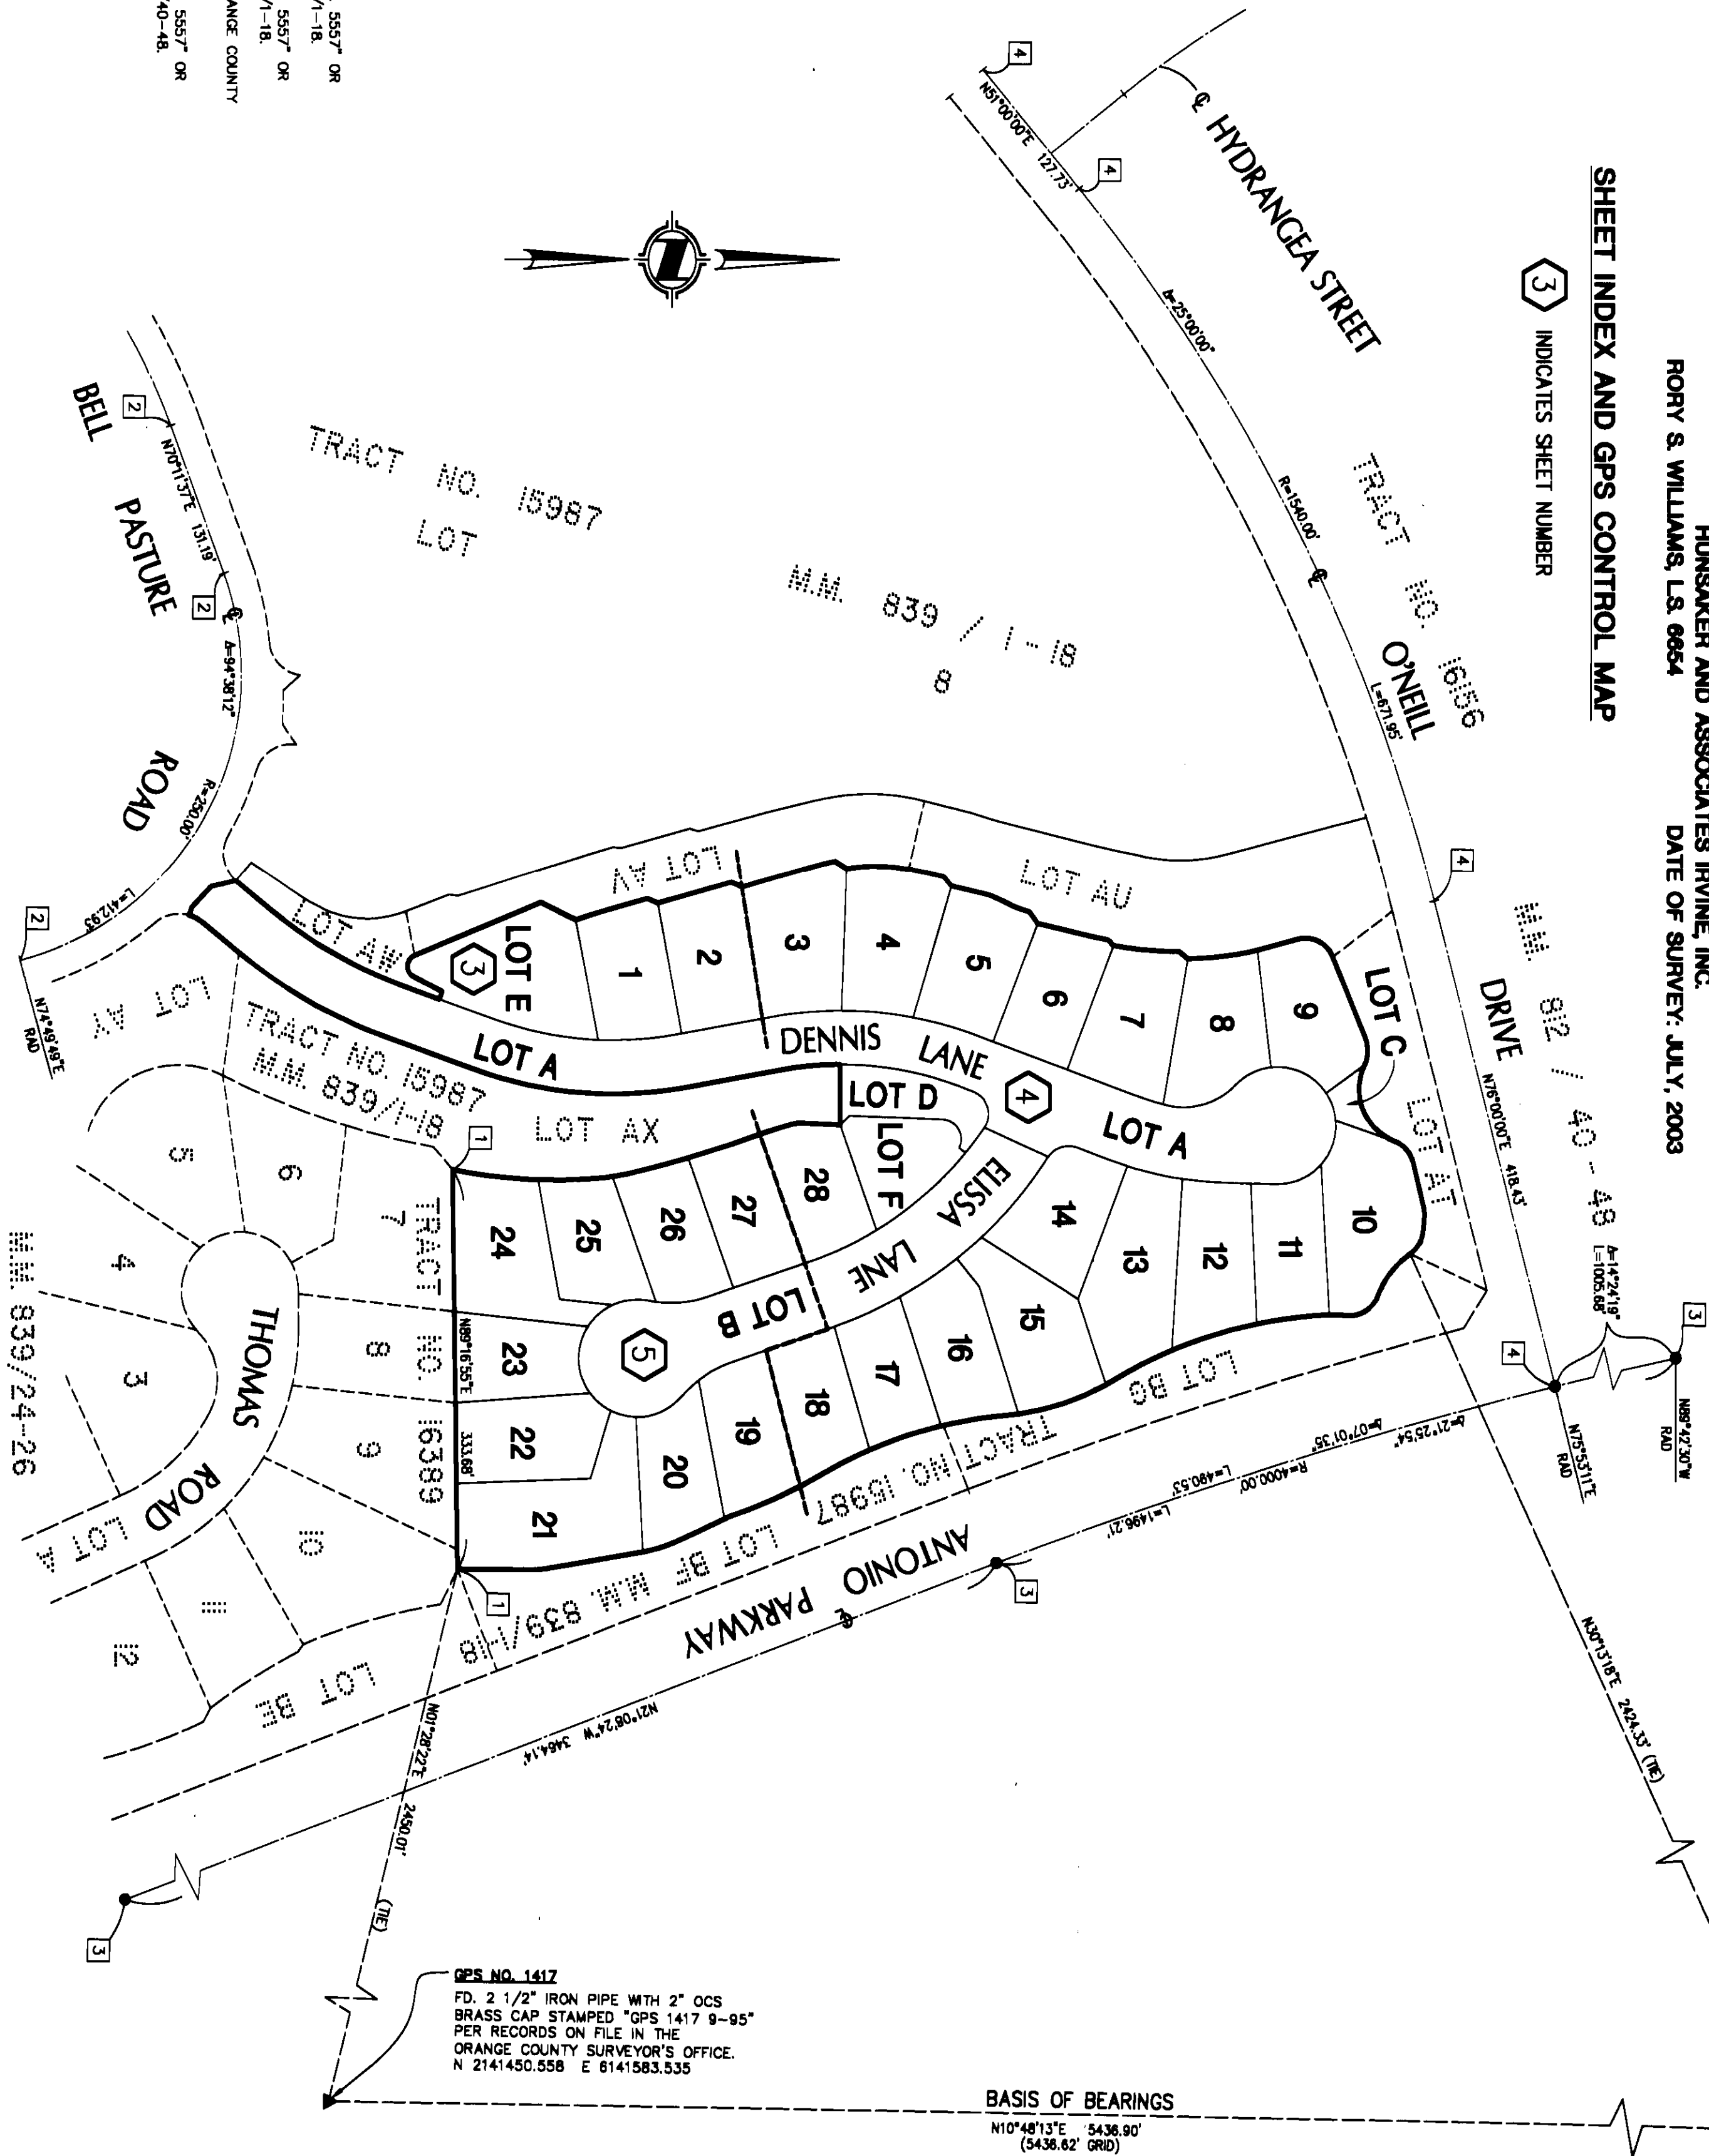


SHEET 3 OF 5 SHEETS
SCALE: 1" = 40'
28 NUMBERED LOTS AND
LOTS A THROUGH F, INCLUSIVE
ACREAGE: 7.696 ACRES
(PORTION OF TENTATIVE
TRACT NO. 16387)

TRACT NO. 16388
IN THE UNINCORPORATED TERRITORY OF THE COUNTY OF ORANGE,
STATE OF CALIFORNIA
HUNSAKER AND ASSOCIATES IRVINE, INC.
RORY S. WILLIAMS, L.S. 6654 DATE OF SURVEY: JULY, 2003

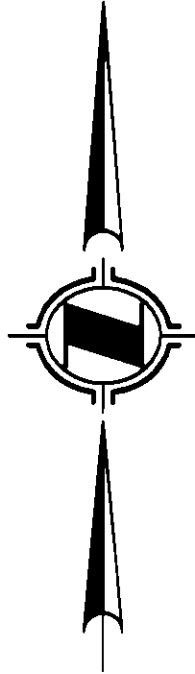

SEE SHEET 4

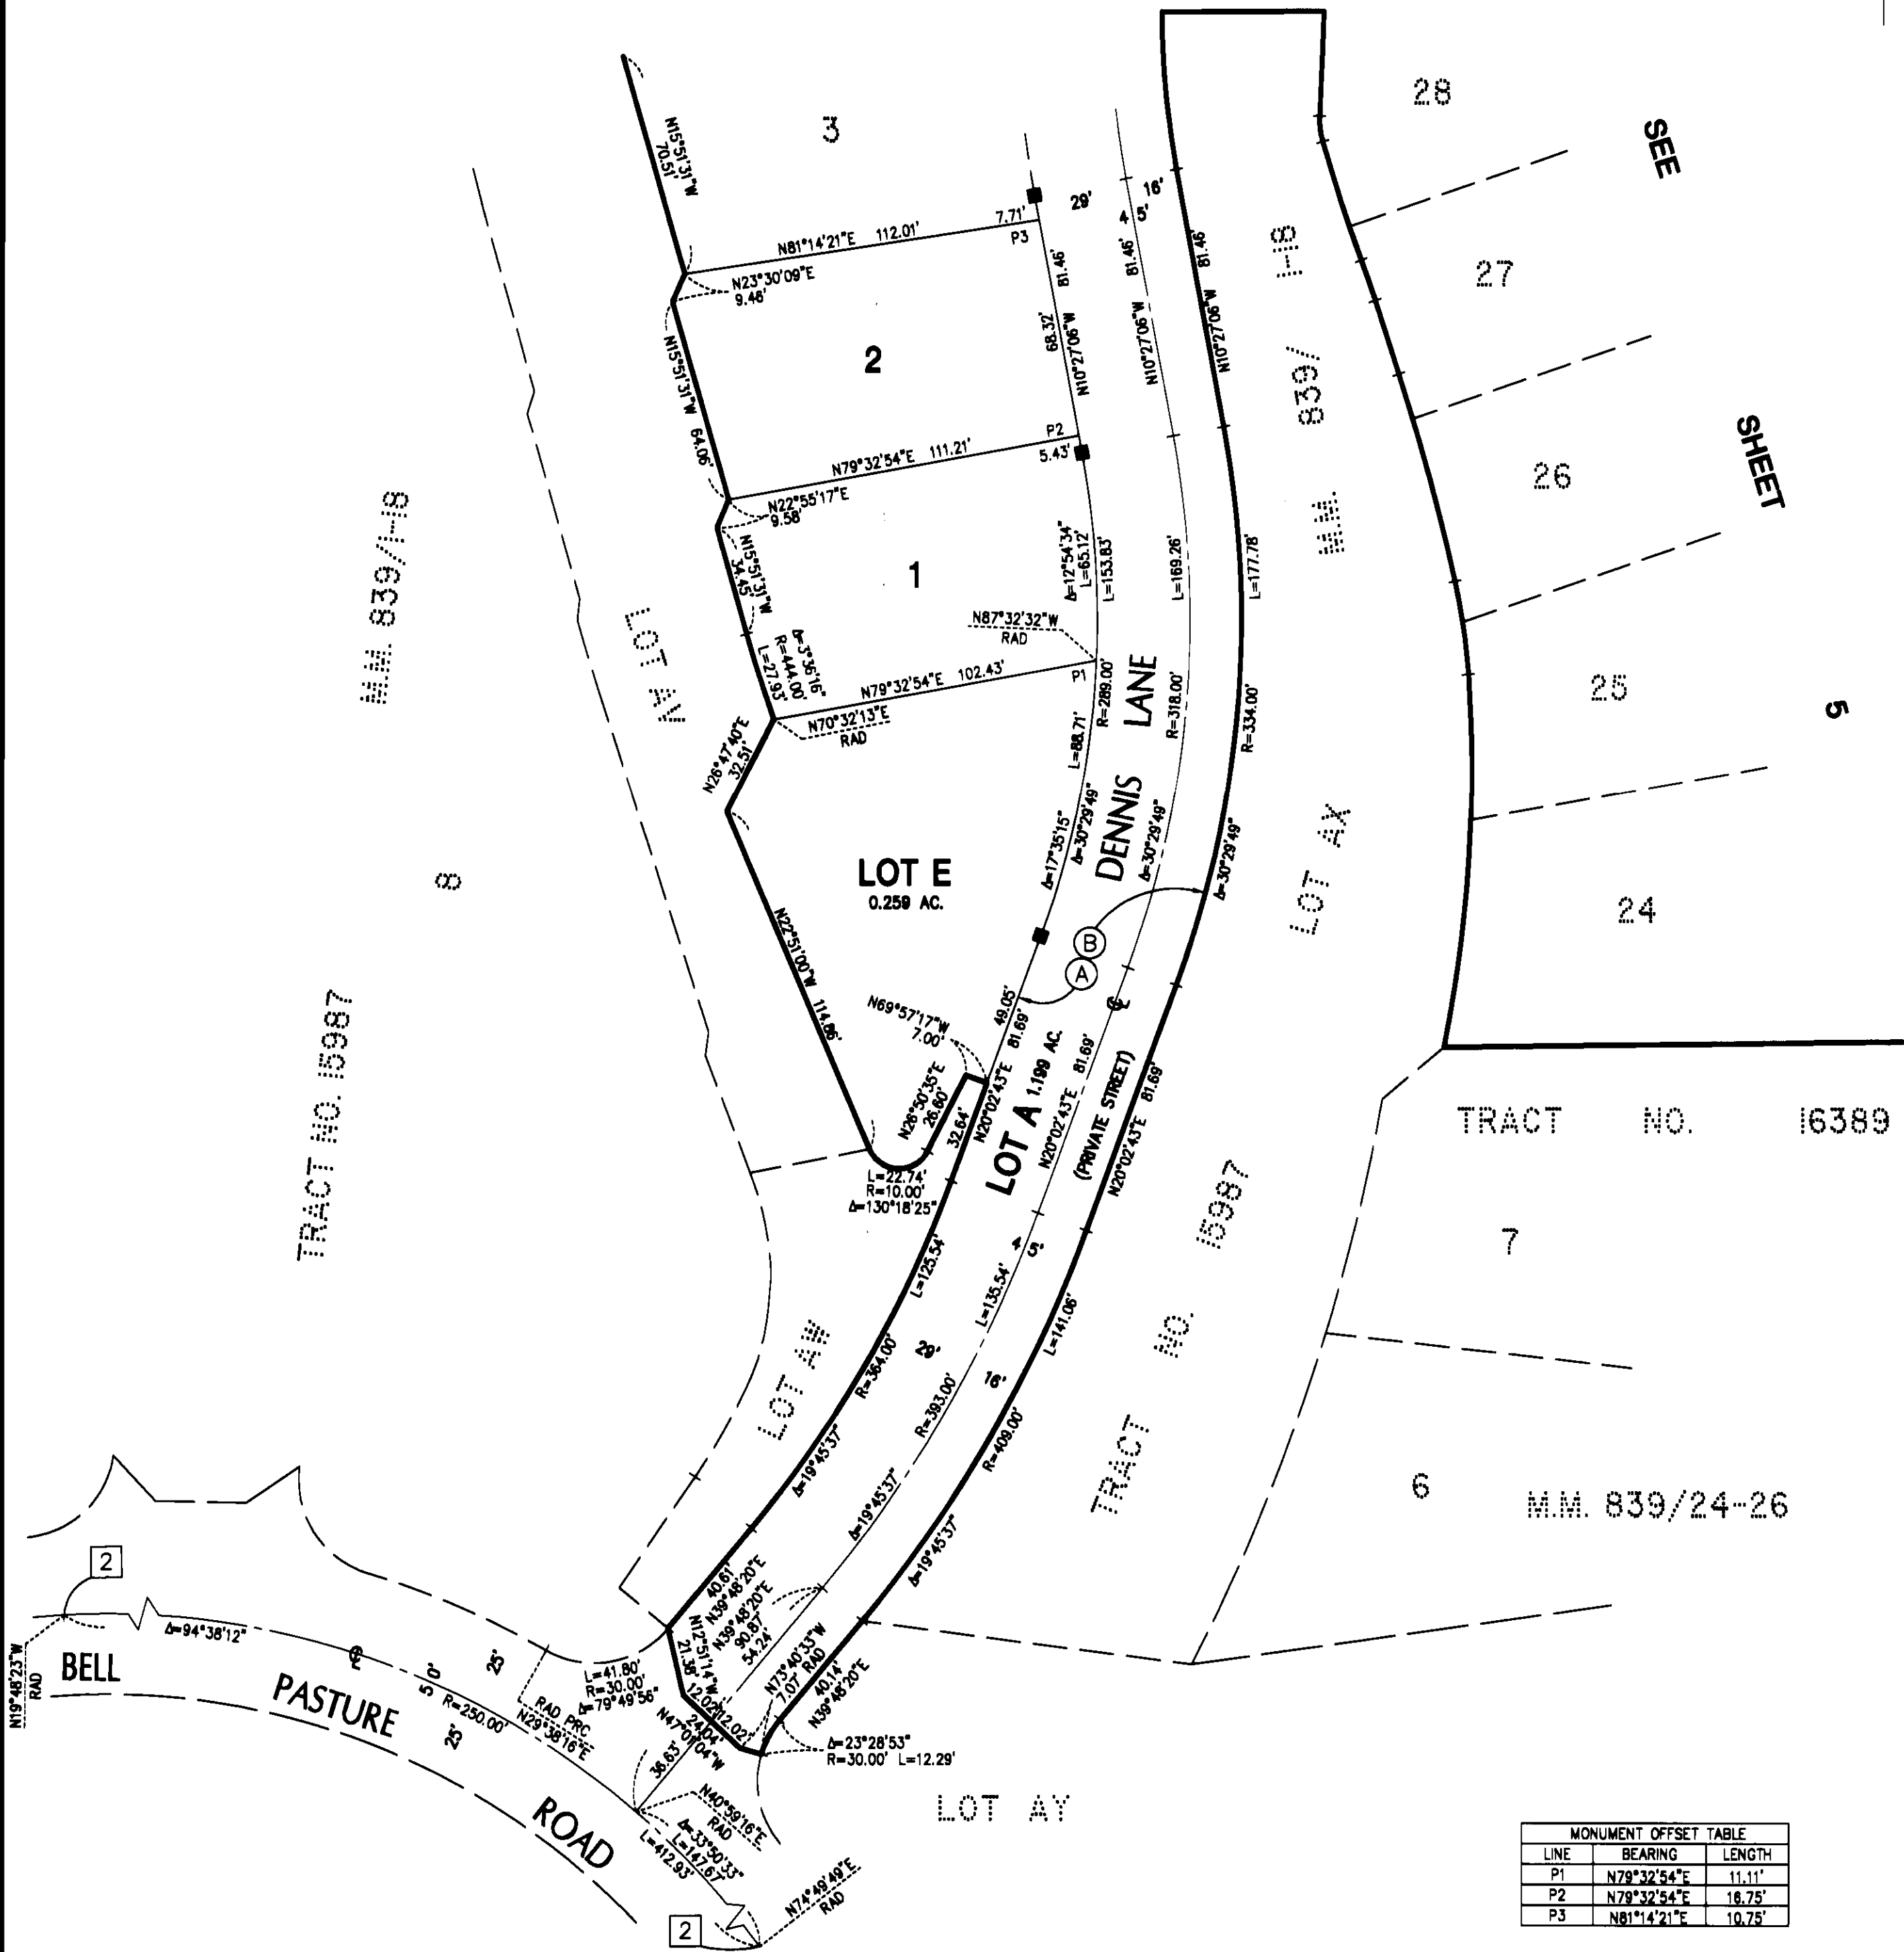

MONUMENT OFFSET TABLE		
LINE	BEARING	LENGTH
P1	N78°32'54"E	11.11'
P2	N79°32'54"E	18.75'
P3	N81°14'21"E	10.75'

SEE SHEET 2 FOR BASIS OF BEARINGS,
DATUM STATEMENT, MONUMENT NOTES,
SHEET INDEX AND GPS CONTROL MAP,
EASEMENT NOTES AND NOTES.

5



SHEET 5 OF 5 SHEETS
SCALE: 1" = 40'
28 NUMBERED LOTS AND
LOTS A THROUGH F, INCLUSIVE
ACREAGE: 7.698 AC.
(PORTION OF TENTATIVE
TRACT NO. 16387)

TRACT NO. 16388

IN THE UNINCORPORATED TERRITORY OF THE COUNTY OF ORANGE,
STATE OF CALIFORNIA

HUNSAKER AND ASSOCIATES IRVINE, INC.
RORY S. WILLIAMS, L.S. 6664
DATE OF SURVEY: JULY, 2003

MONUMENT OFFSET TABLE		
LINE	BEARING	LENGTH
P20	S76°01'52"W	10.78'
P21	S76°16'32"W	11.92'
P22	S87°06'32"W	10.76'
P23	N73°15'05"W	10.86'
P24	N04°09'28"W	13.49'
P25	N06°22'16"E	12.46'
P26	N70°50'47"E	11.85'
P27	N70°50'47"E	10.75'
P28	N70°50'57"E	10.75'

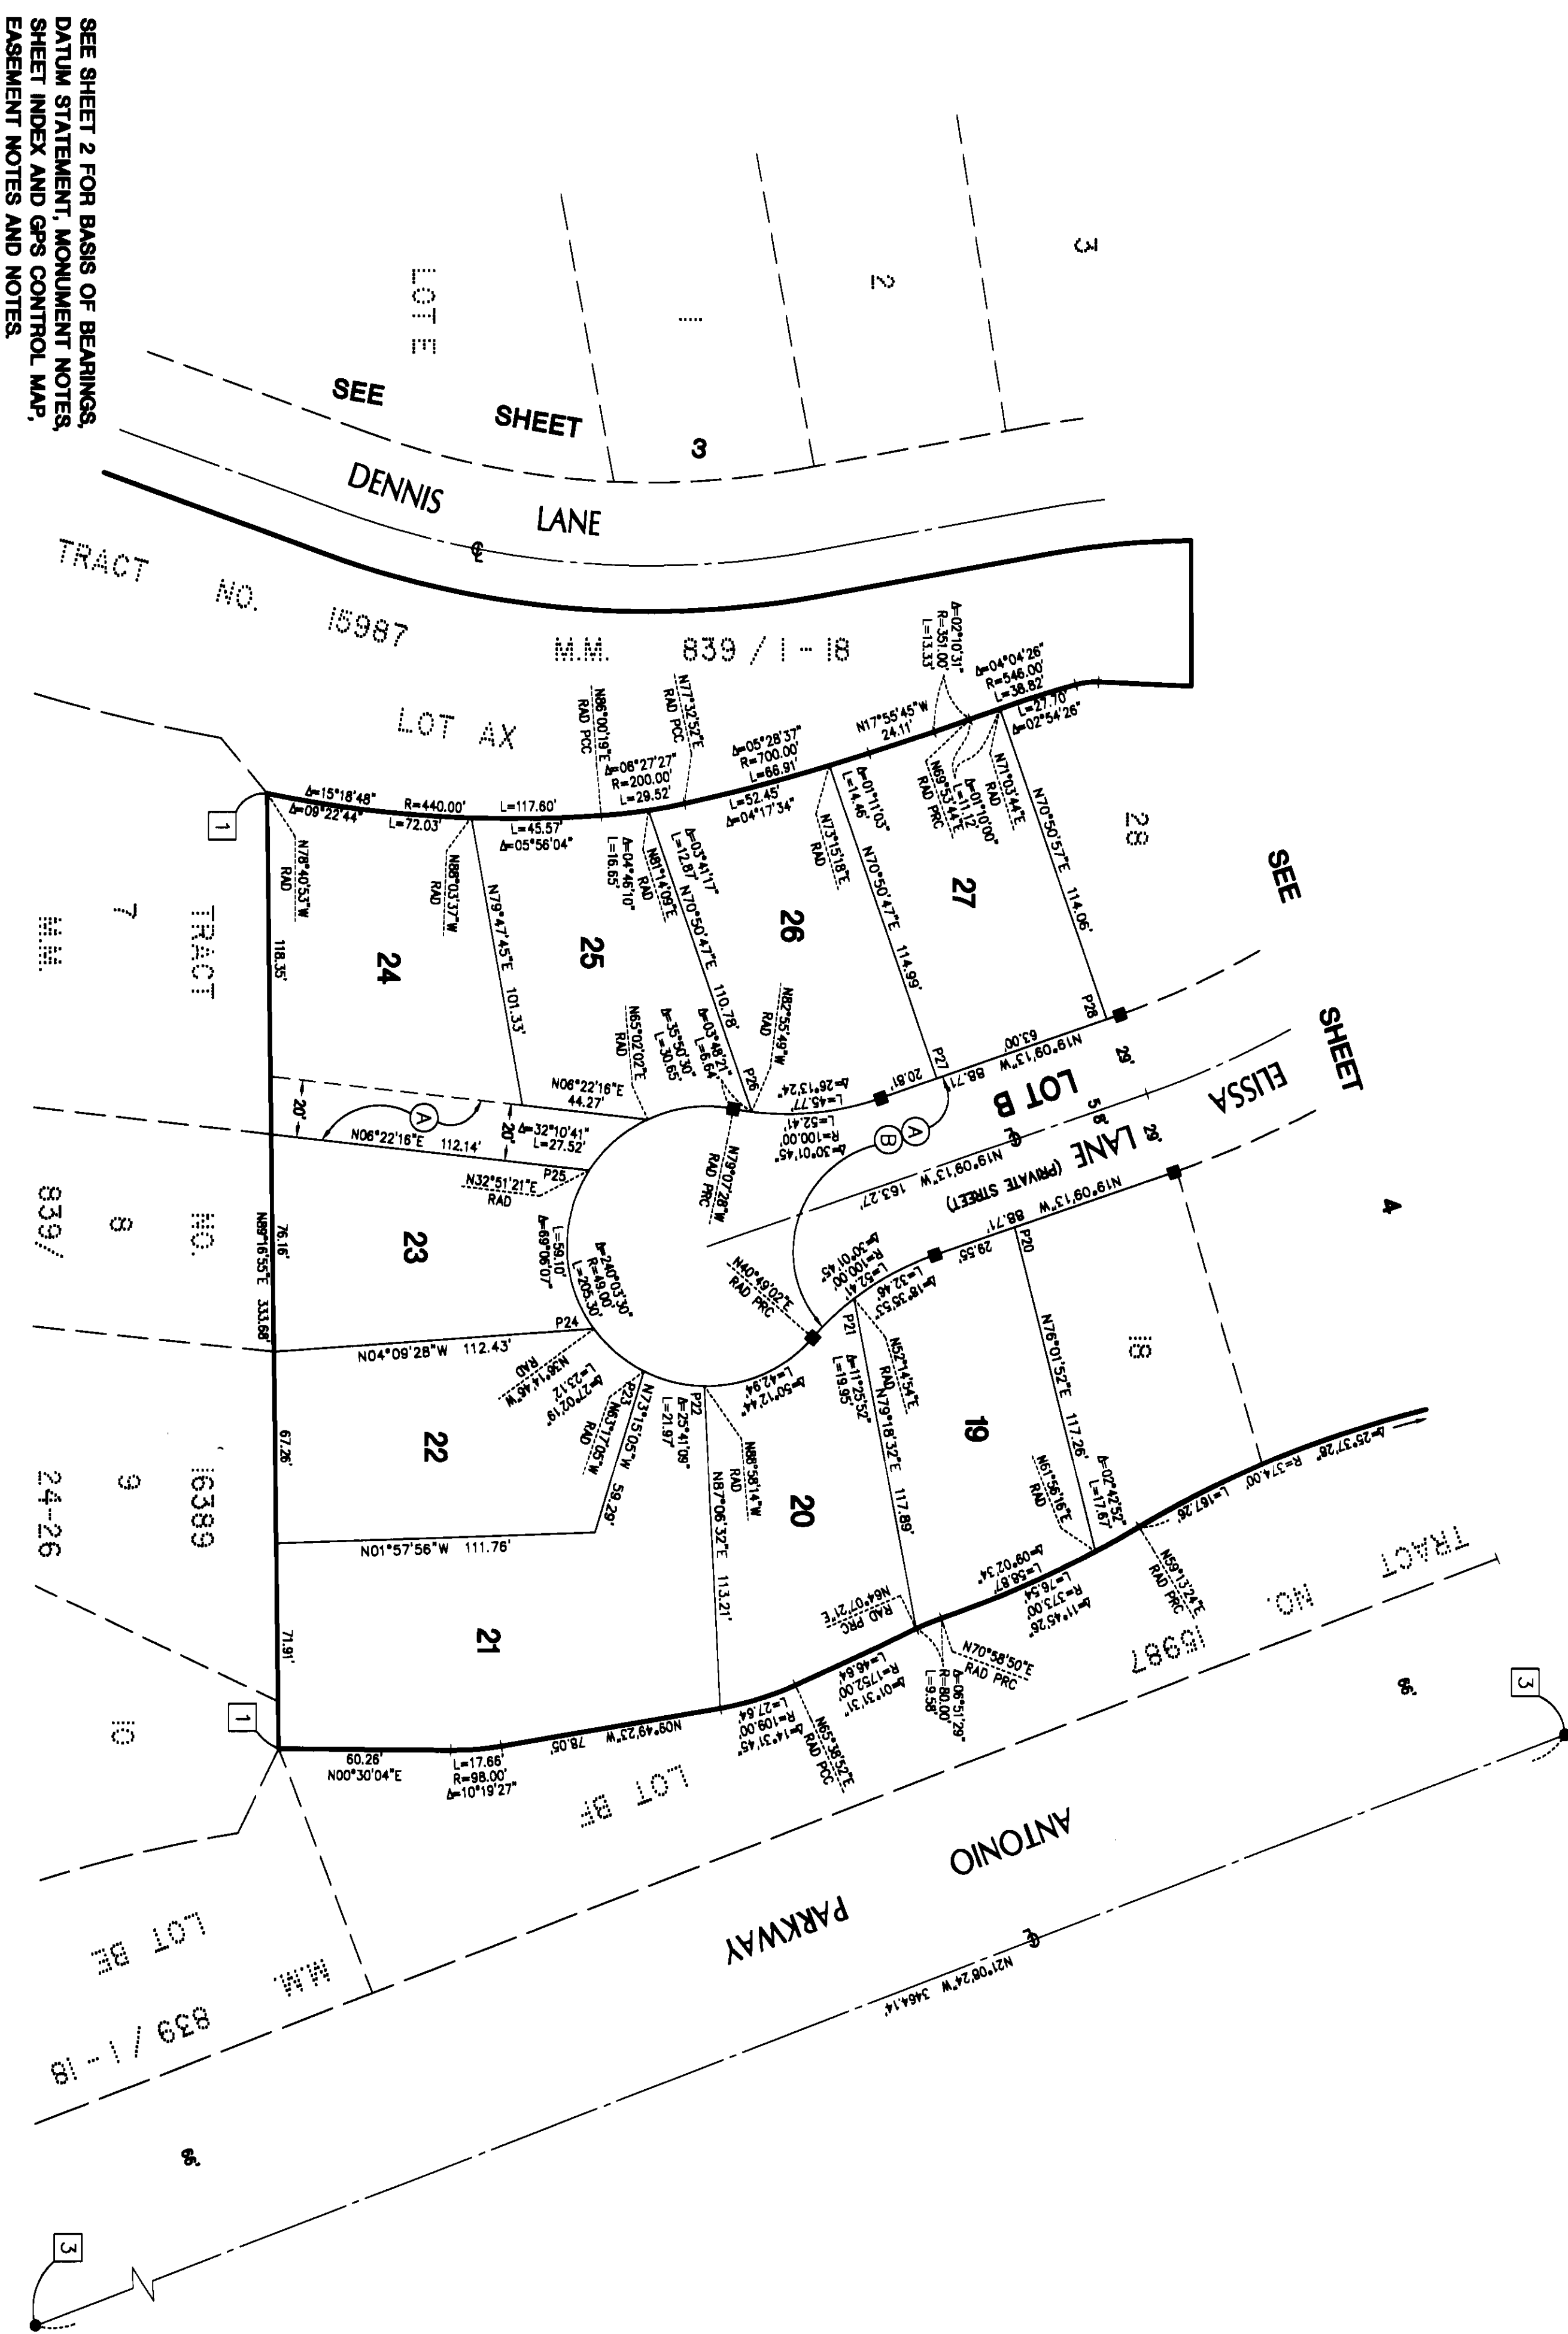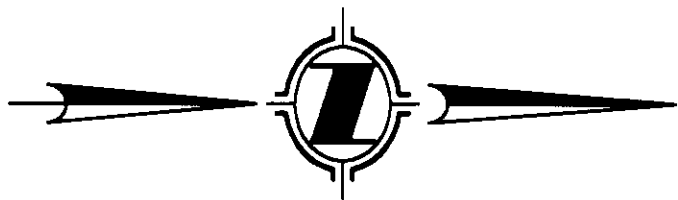

SEE SHEET 2 FOR BASIS OF BEARINGS,
DATUM STATEMENT, MONUMENT NOTES,
SHEET INDEX AND GPS CONTROL MAP,
EASEMENT NOTES AND NOTES.