

SHEET 1 OF 5 SHEETS
31 NUMBERED LOTS AND
LOTS A THROUGH I, INCLUSIVE
ACREAGE: 12.180 ACRES
(ALL OF TENTATIVE
TRACT NO. 16390)

TRACT NO. 16390

IN UNINCORPORATED TERRITORY OF THE COUNTY OF ORANGE,
STATE OF CALIFORNIA

BEING A SUBDIVISION OF LOT 13 OF TRACT NO. 15986, AS PER MAP FILED IN BOOK 849,
PAGES 1 THROUGH 15, INCLUSIVE, AND LOTS 11 AND CB OF TRACT NO. 15987, AS PER
MAP FILED IN BOOK 839, PAGES 1 THROUGH 18, INCLUSIVE, BOTH OF MISCELLANEOUS
MAPS, IN THE OFFICE OF THE COUNTY RECORDER OF SAID COUNTY.

HUNSAKER AND ASSOCIATES IRVINE, INC.
RORY S. WILLIAMS, L.S. 6654 DATE OF SURVEY: NOVEMBER, 2002

ACCEPTED AND FILED AT THE
REQUEST OF

First American Title

DATE: April 23, 2004

TIME: 9:02am FEE: \$19.00

INSTRUMENT NO. 2004100845438

BOOK 856 PAGE 30-34

TOM DALY
COUNTY CLERK - RECORDER

BY Julia Y. Canul
DEPUTY

OWNERSHIP CERTIFICATE:

WE, THE UNDERSIGNED, BEING ALL PARTIES HAVING ANY RECORD TITLE INTEREST IN THE LAND COVERED BY THIS MAP, DO HEREBY CONSENT TO THE PREPARATION AND RECORDATION OF SAID MAP, AS SHOWN WITHIN THE DISTINCTIVE BORDER LINE.

WE HEREBY DEDICATE TO THE COUNTY OF ORANGE THE EASEMENTS FOR INGRESS AND EGRESS OF EMERGENCY AND PUBLIC SERVICE VEHICLES AS SHOWN ON SAID MAP.

WE ALSO HEREBY DEDICATE TO THE SANTA MARGARITA WATER DISTRICT THE EASEMENTS FOR WATER, RECYCLED WATER, SEWER, DRAINAGE AND ACCESS PURPOSES OVER THOSE EASEMENT AREAS AS SHOWN ON SAID MAP, WHICH EASEMENTS SHALL BE SUBJECT TO THE SAME CONDITIONS AS SHOWN IN THAT CERTAIN GRANT OF EASEMENT TO SANTA MARGARITA WATER DISTRICT RECORDED SEPTEMBER 18, 2002, AS INSTRUMENT NO. 20020799401 OF OFFICIAL RECORDS, COUNTY OF ORANGE.

DMB LADERA, LLC, A DELAWARE LIMITED LIABILITY COMPANY, OWNER.

BY: RANCHO MISSION VIEJO, L.L.C., A DELAWARE LIMITED LIABILITY COMPANY, ITS
AUTHORIZED AGENT AND MANAGER.

BY: [Signature]
NAME: DONALD T. STAHLEN
TITLE: VICE PRESIDENT

BY: [Signature]
NAME: Greg Edwards
TITLE: Chief Financial Officer

NOTARY ACKNOWLEDGMENT:

STATE OF CALIFORNIA } SS
COUNTY OF ORANGE }

ON August 11, 2003 BEFORE ME, Diana L. BINKS, Notary Public PERSONALLY
APPEARED Donald T. Stahlin AND Greg Edwards PERSONALLY
KNOWN TO ME (OR PROVED TO ME ON THE BASIS OF SATISFACTORY EVIDENCE) TO BE THE PERSON(S)
WHOSE NAME(S) IS/ARE SUBSCRIBED TO THE WITHIN INSTRUMENT AND ACKNOWLEDGED TO ME THAT
HE/SHE/ THEY EXECUTED THE SAME IN HIS/HER/ THEIR AUTHORIZED CAPACITY(IES) AND THAT BY
HIS/HER/ THEIR SIGNATURE(S) ON THE INSTRUMENT THE PERSON(S) OR ENTITY UPON BEHALF OF
WHICH THE PERSON(S) ACTED, EXECUTED THE INSTRUMENT.

WITNESS MY HAND:

SIGNATURE Diana L. BINKS
NOTARY PUBLIC IN AND FOR SAID STATE
Diana L. BINKS
(NAME PRINTED)

MY PRINCIPAL PLACE OF BUSINESS IS
IN ORANGE COUNTY.

MY COMMISSION EXPIRES: 12/12/06

AUTOMATIC FIRE SPRINKLER NOTE:

ALL COMMERCIAL STRUCTURES GREATER THAN 6,000 SQUARE FEET, ALL MULTIFAMILY RESIDENTIAL STRUCTURES, ALL SINGLE-FAMILY STRUCTURES EXCEEDING 5,500 SQUARE FEET, AND ALL STRUCTURES EXCEEDING FIRE DEPARTMENT ACCESS REQUIREMENTS SHALL BE PROTECTED BY AN AUTOMATIC FIRE SPRINKLER SYSTEM.

SPECIAL FIRE PROTECTION NOTE:

SUBJECT PROPERTY IS IN A SPECIAL FIRE PROTECTION AREA AND MUST MEET ALL REQUIREMENTS FOR DEVELOPMENT WITHIN THE AREA.

HIGH FIRE HAZARD AREA NOTE:

THE LOTS SHOWN ON THIS MAP ARE IN A HIGH FIRE HAZARD AREA DUE TO WILDLAND EXPOSURE.


NOTE:

THE PRIVATE STREETS CONSTRUCTED WITHIN THIS MAP SHALL BE OWNED, OPERATED AND MAINTAINED BY THE DEVELOPER, SUCCESSORS OR ASSIGNS. THE COUNTY OF ORANGE SHALL HAVE NO RESPONSIBILITY THEREFOR, UNLESS PURSUANT TO APPROPRIATE SECTIONS OF THE STREETS AND HIGHWAYS CODE OF THE STATE OF CALIFORNIA, THE SAID PRIVATE STREETS HAVE BEEN ACCEPTED INTO THE COUNTY ROAD SYSTEM BY APPROPRIATE RESOLUTION OF THE ORANGE COUNTY BOARD OF SUPERVISORS.

SURVEYOR'S STATEMENT:

THIS MAP WAS PREPARED BY ME OR UNDER MY DIRECTION AND IS BASED UPON A FIELD SURVEY IN CONFORMANCE WITH THE REQUIREMENTS OF THE SUBDIVISION MAP ACT AND LOCAL ORDINANCE AT THE REQUEST OF DMB LADERA, L.L.C., IN NOVEMBER, 2002. I HEREBY STATE THAT ALL MONUMENTS ARE OF THE CHARACTER AND OCCUPY THE POSITIONS INDICATED, OR THAT THEY WILL BE SET IN SUCH POSITIONS; AND THAT SAID MONUMENTS ARE SUFFICIENT TO ENABLE THE SURVEY TO BE RETRACED. I HEREBY STATE THAT THIS FINAL MAP SUBSTANTIALLY CONFORMS TO THE CONDITIONALLY APPROVED TENTATIVE MAP.

Rory S. Williams 7/23/03
RORY S. WILLIAMS, L.S. 6654 DATE
LICENSE EXPIRES: 12/31/03

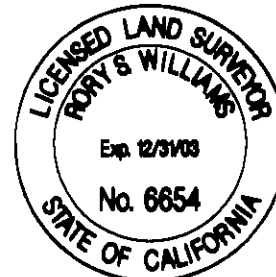


COUNTY SURVEYOR'S STATEMENT

I HEREBY STATE THAT I HAVE EXAMINED THIS MAP AND HAVE FOUND IT TO BE SUBSTANTIALLY IN CONFORMANCE WITH THE TENTATIVE MAP AS FILED WITH, AMENDED AND APPROVED BY THE ORANGE COUNTY SUBDIVISION COMMITTEE; THAT ALL PROVISIONS OF THE SUBDIVISION MAP ACT AND COUNTY SUBDIVISION REGULATIONS HAVE BEEN COMPLIED WITH AND I AM SATISFIED SAID MAP IS TECHNICALLY CORRECT.

DATED THIS 24TH DAY OF MARCH, 2004.

Michael K. Sullivan
COUNTY SURVEYOR

BY Michael K. Sullivan, DEPUTY
2254 EXPIRES 6/30/05

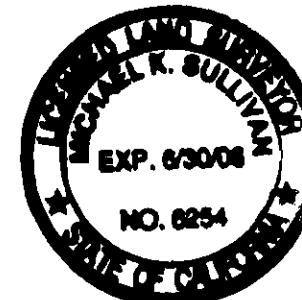

COUNTY TREASURER-TAX COLLECTOR'S CERTIFICATE:

STATE OF CALIFORNIA } SS
COUNTY OF ORANGE }

I HEREBY CERTIFY THAT ACCORDING TO THE RECORDS OF MY OFFICE THERE ARE NO LIENS AGAINST THE LAND COVERED BY THIS MAP OR ANY PART THEREOF FOR UNPAID STATE, COUNTY, MUNICIPAL OR LOCAL TAXES OR SPECIAL ASSESSMENTS COLLECTED AS TAXES, EXCEPT TAXES OR SPECIAL ASSESSMENTS COLLECTED AS TAXES NOT YET PAYABLE.

AND DO CERTIFY TO THE RECORDER OF ORANGE COUNTY THAT THE PROVISIONS OF THE SUBDIVISION MAP ACT HAVE BEEN COMPLIED WITH REGARDING DEPOSITS TO SECURE PAYMENT OF TAXES OR SPECIAL ASSESSMENTS COLLECTED AS TAXES ON THE LAND COVERED BY THIS MAP.

DATED THIS 17th DAY OF March, 2004.

John M.W. Moorlach
COUNTY TREASURER-TAX COLLECTOR

BY: [Signature]
DEPUTY TREASURER-TAX COLLECTOR

CLERK OF THE BOARD OF SUPERVISORS' CERTIFICATE:

STATE OF CALIFORNIA } SS
COUNTY OF ORANGE }

I HEREBY CERTIFY THAT THIS MAP WAS PRESENTED FOR APPROVAL TO THE BOARD OF SUPERVISORS OF THE COUNTY OF ORANGE AT REGULAR MEETING THEREOF HELD ON THE 20th DAY OF April, 2004, AND THAT THEREUPON SAID BOARD DID, BY AN ORDER DULY PASSED AND ENTERED, APPROVE SAID MAP.

AND DID ACCEPT ON BEHALF OF THE COUNTY OF ORANGE THE EASEMENTS FOR INGRESS AND EGRESS OF EMERGENCY AND PUBLIC SERVICE VEHICLES AS DEDICATED.

AND DID ALSO APPROVE SUBJECT MAP PURSUANT TO THE PROVISIONS OF SECTION 66436(a)(3)(A) OF THE SUBDIVISION MAP ACT.

DATED THIS 20th DAY OF April, 2004.

[Signature]
CLERK OF THE BOARD OF SUPERVISORS
DARLENE J. BLOOM



CERTIFICATE OF ACCEPTANCE - SANTA MARGARITA WATER DISTRICT

THE UNDERSIGNED, BEING THE DULY APPOINTED AGENT OF THE SANTA MARGARITA WATER DISTRICT, A PUBLIC CORPORATION IN ORANGE COUNTY, CALIFORNIA, PURSUANT TO ITS RESOLUTION NO. 88-10-2, DOES HEREBY ACCEPT ON BEHALF OF SAID DISTRICT, THE EASEMENTS FOR WATER, RECYCLED WATER, SEWER, DRAINAGE AND ACCESS PURPOSES, AS DEDICATED AND SHOWN ON THIS TRACT MAP, BY AND BETWEEN THE SANTA MARGARITA WATER DISTRICT AND DMB LADERA, L.L.C., A DELAWARE LIMITED LIABILITY COMPANY, AND DOES HEREBY CERTIFY THAT THE GRANTEE CONSENTS TO THE RECORDATION OF SAID TRACT MAP.

[Signature]
DANIEL R. FERONS, CHIEF ENGINEER
SANTA MARGARITA WATER DISTRICT

NOTARY ACKNOWLEDGMENT - SANTA MARGARITA WATER DISTRICT

STATE OF CALIFORNIA } SS
COUNTY OF ORANGE }

ON SEPT. 23, 2002 BEFORE ME, Cindy R. Lane, Notary Public PERSONALLY
APPEARED DANIEL R. FERONS, PERSONALLY KNOWN TO ME (OR PROVED TO ME ON THE BASIS OF SATISFACTORY EVIDENCE) TO BE THE PERSON WHOSE NAME IS SUBSCRIBED TO THE WITHIN INSTRUMENT AND ACKNOWLEDGED TO ME THAT HE EXECUTED THE SAME IN HIS AUTHORIZED CAPACITY, AND THAT BY HIS SIGNATURE ON THE INSTRUMENT THE PERSON, OR ENTITY UPON BEHALF OF WHICH THE PERSON ACTED, EXECUTED THE INSTRUMENT.

WITNESS MY HAND:

SIGNATURE Cindy R. Lane
NOTARY PUBLIC IN AND FOR SAID STATE
CINDY R. LANE
(NAME PRINTED)

MY PRINCIPAL PLACE OF BUSINESS IS
IN Orange COUNTY.

MY COMMISSION EXPIRES: Feb 20, 2005

SIGNATURE OMISSIONS:

PURSUANT TO THE PROVISIONS OF SECTION 66436 (a)(3) OF THE SUBDIVISION MAP ACT, THE FOLLOWING SIGNATURES HAVE BEEN OMITTED:

LADERA DEVELOPMENT COMPANY, L.L.C., HOLDER OF OIL, GAS AND MINERAL RIGHTS RECORDED DECEMBER 10, 1996, AS INSTRUMENT NO. 19960624029 OF OFFICIAL RECORDS.

THE COUNTY OF ORANGE, HOLDER OF AN EASEMENT FOR EMERGENCY ACCESS PURPOSES AS DEDICATED ON THE MAP OF TRACT NO. 15987, M.M. 839/1-18.

SANTA MARGARITA WATER DISTRICT, HOLDER OF SEWER, WATER, RECYCLED WATER, ACCESS AND DRAINAGE EASEMENTS AS DEDICATED ON THE MAP OF TRACT NO. 15987, M.M. 839/1-18.

TRACT NO. 16390
IN UNINCORPORATED TERRITORY OF THE COUNTY OF ORANGE,
STATE OF CALIFORNIA

RORY S. WILLIAMS, L.S. 6854 **DATE OF SURVEY: NOVEMBER, 2002**

SHEET INDEX AND GPS CONTROL MAP

DATUM STATEMENT:

MONUMENT NOTES:


● INDICATES FOUND MONUMENT OR LOCATION OF MONUMENT SET, AS NOTED.

▲ INDICATES FOUND ORANGE COUNTY SURVEYOR GPS CONTROL MONUMENT AS NOTED.

6 INDICATES SET 2ND I.P. TAGGED L.S. 6654 PRIOR TO MAP RECORDATION.

INDICATES A DRAINAGE EASEMENT DEDICATED TO THE SANTA MARGARITA WATER DISTRICT
PER TRACT NO. 15987, M.M. 839/1-8.

LOTS E, F, G, AND H ARE FOR PRIVATE STREET PURPOSES.

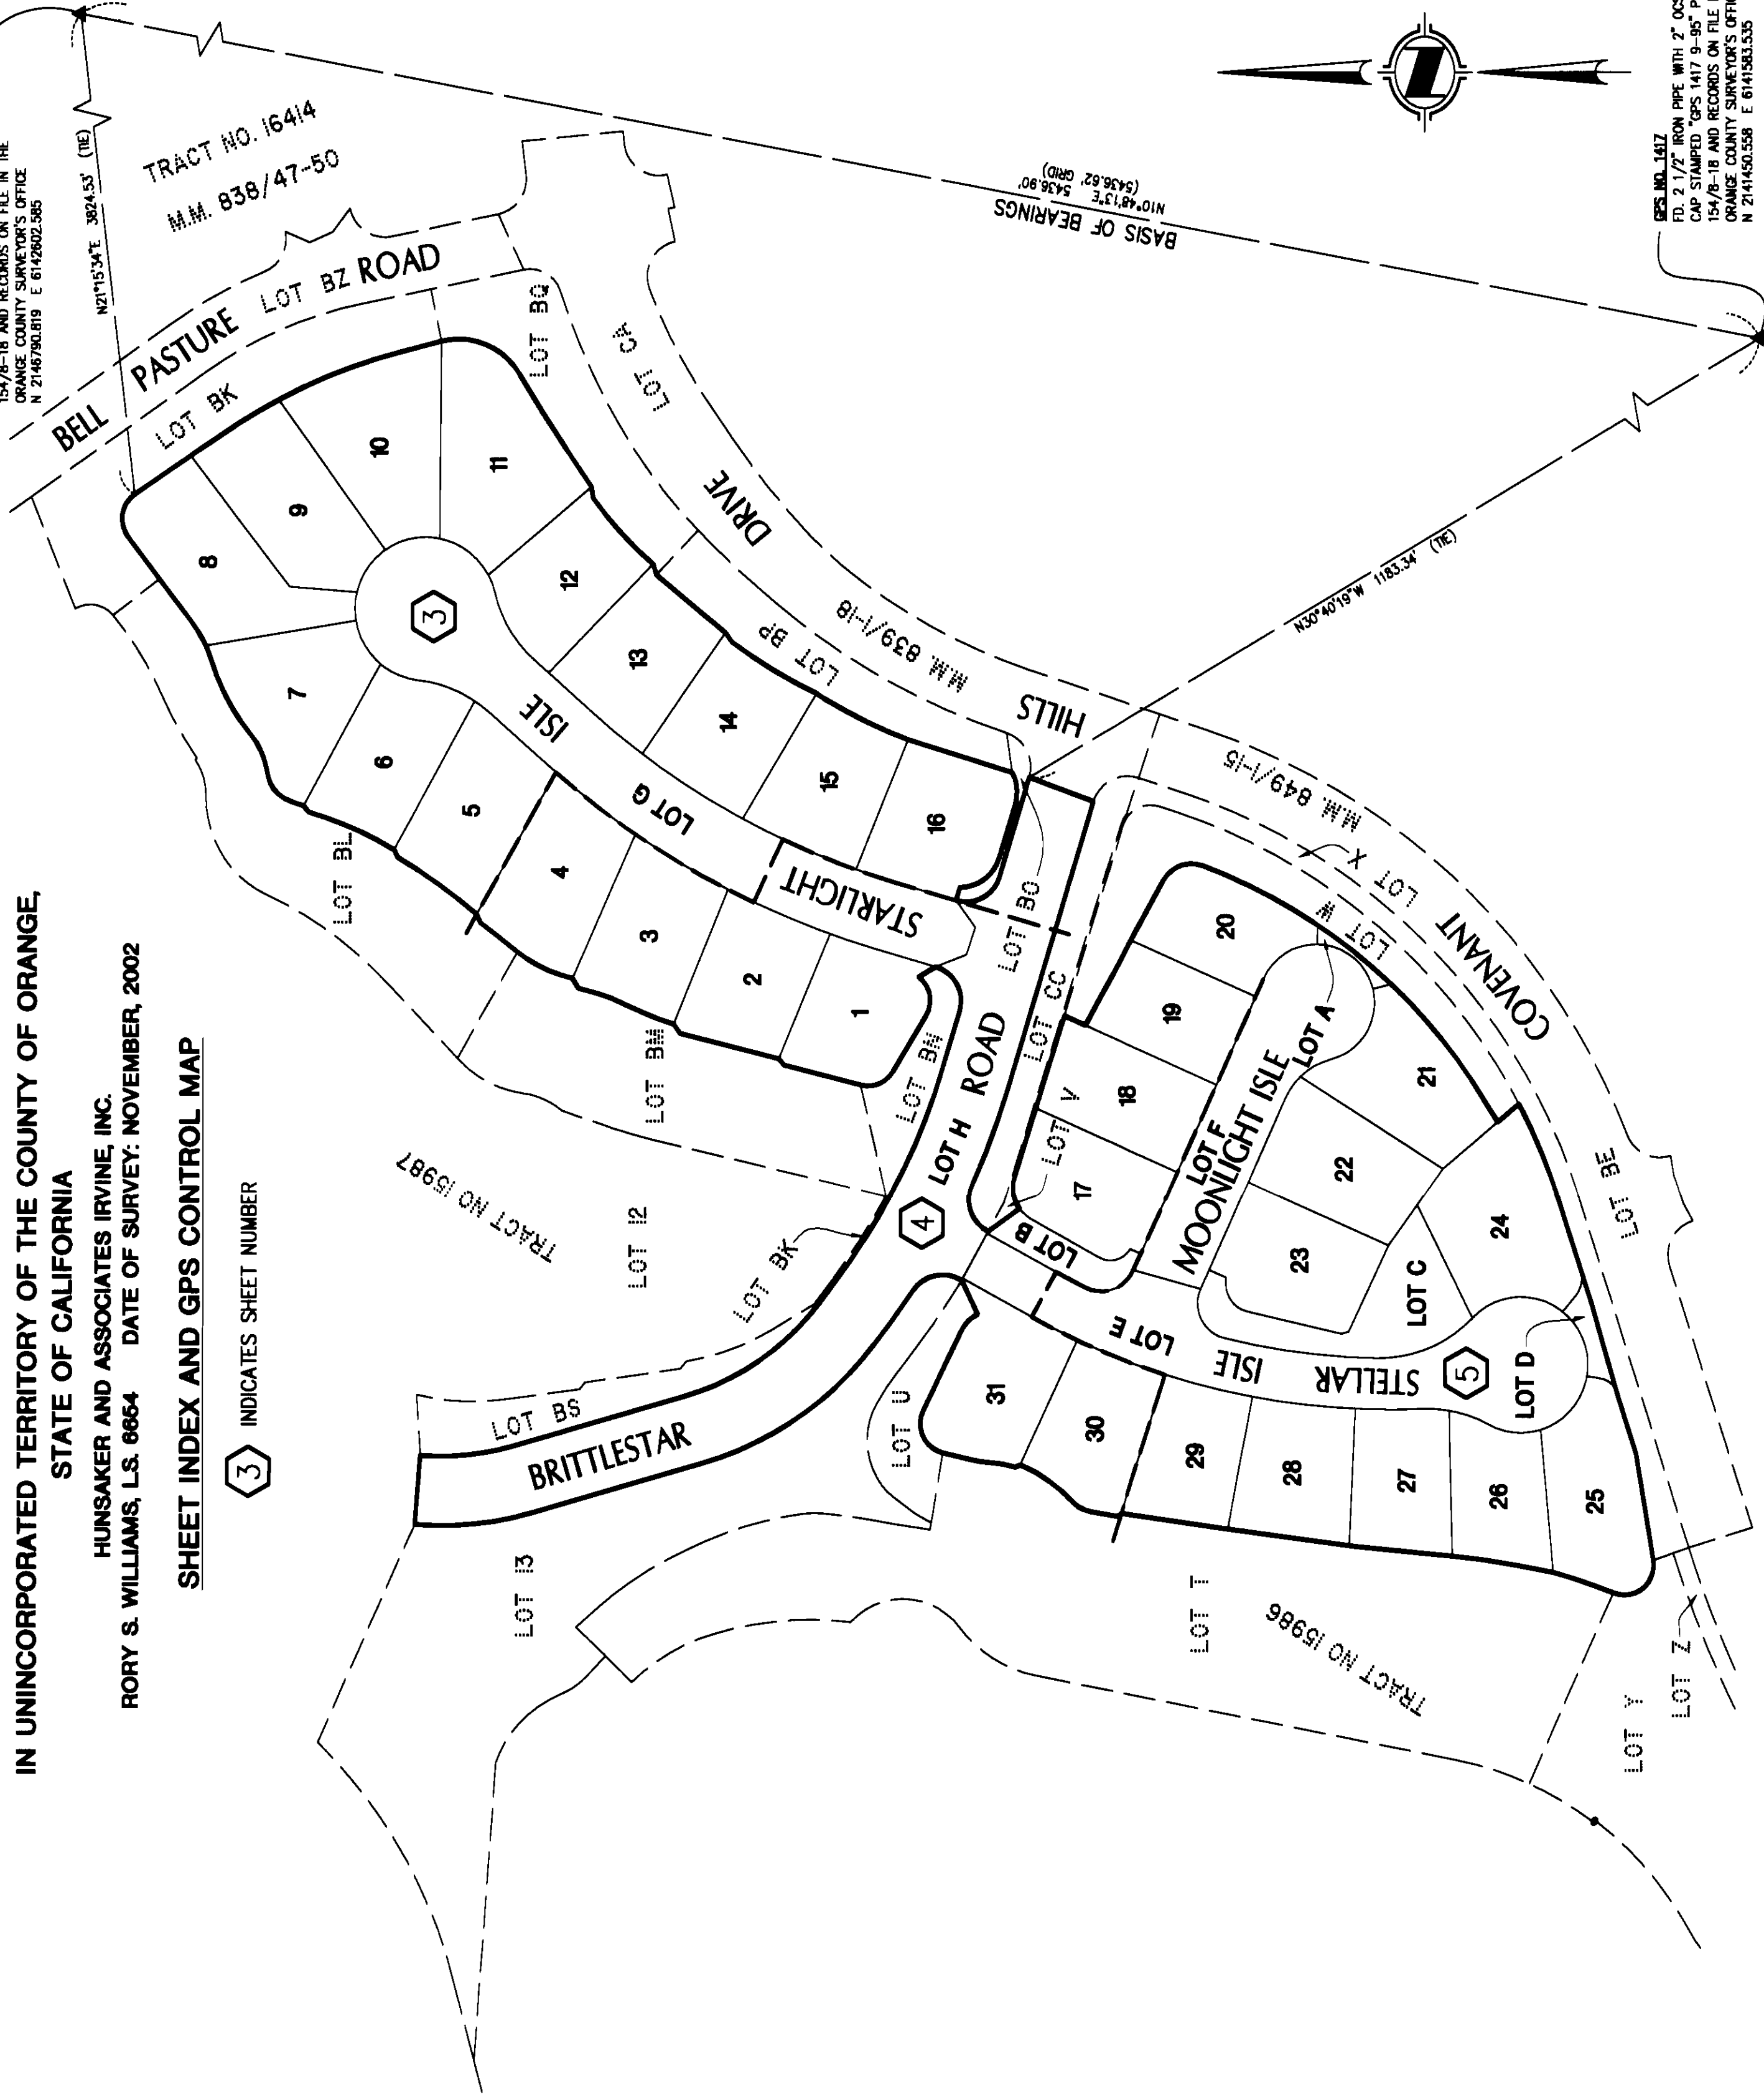

TRACT NO. 16414
M.M. 838/47-50

GPS NO. 141Z
FD. 2 1/2" IRON PIPE WITH 2" OCS BRASS
CAP STAMPED "GPS 1417 9-95" PER R.S.B.
154/8-18 AND RECORDS ON FILE IN THE
ORANGE COUNTY SURVEYOR'S OFFICE. 
N 2141450.558 E 6141583.535


856 32

SHEET 3 OF 5 SHEETS
SCALE: 1" = 40'
31 NUMBERED LOTS AND LOTS
A THROUGH H, INCLUSIVE
ACREAGE: 12.180 ACRES
(ALL OF TENTATIVE
TRACT NO. 16390)

TRACT NO. 16390

IN UNINCORPORATED TERRITORY OF THE COUNTY OF ORANGE,
STATE OF CALIFORNIA

HUNSAKER AND ASSOCIATES IRVINE, INC.
RORY S. WILLIAMS, L.S. 6654 DATE OF SURVEY: NOVEMBER, 2002

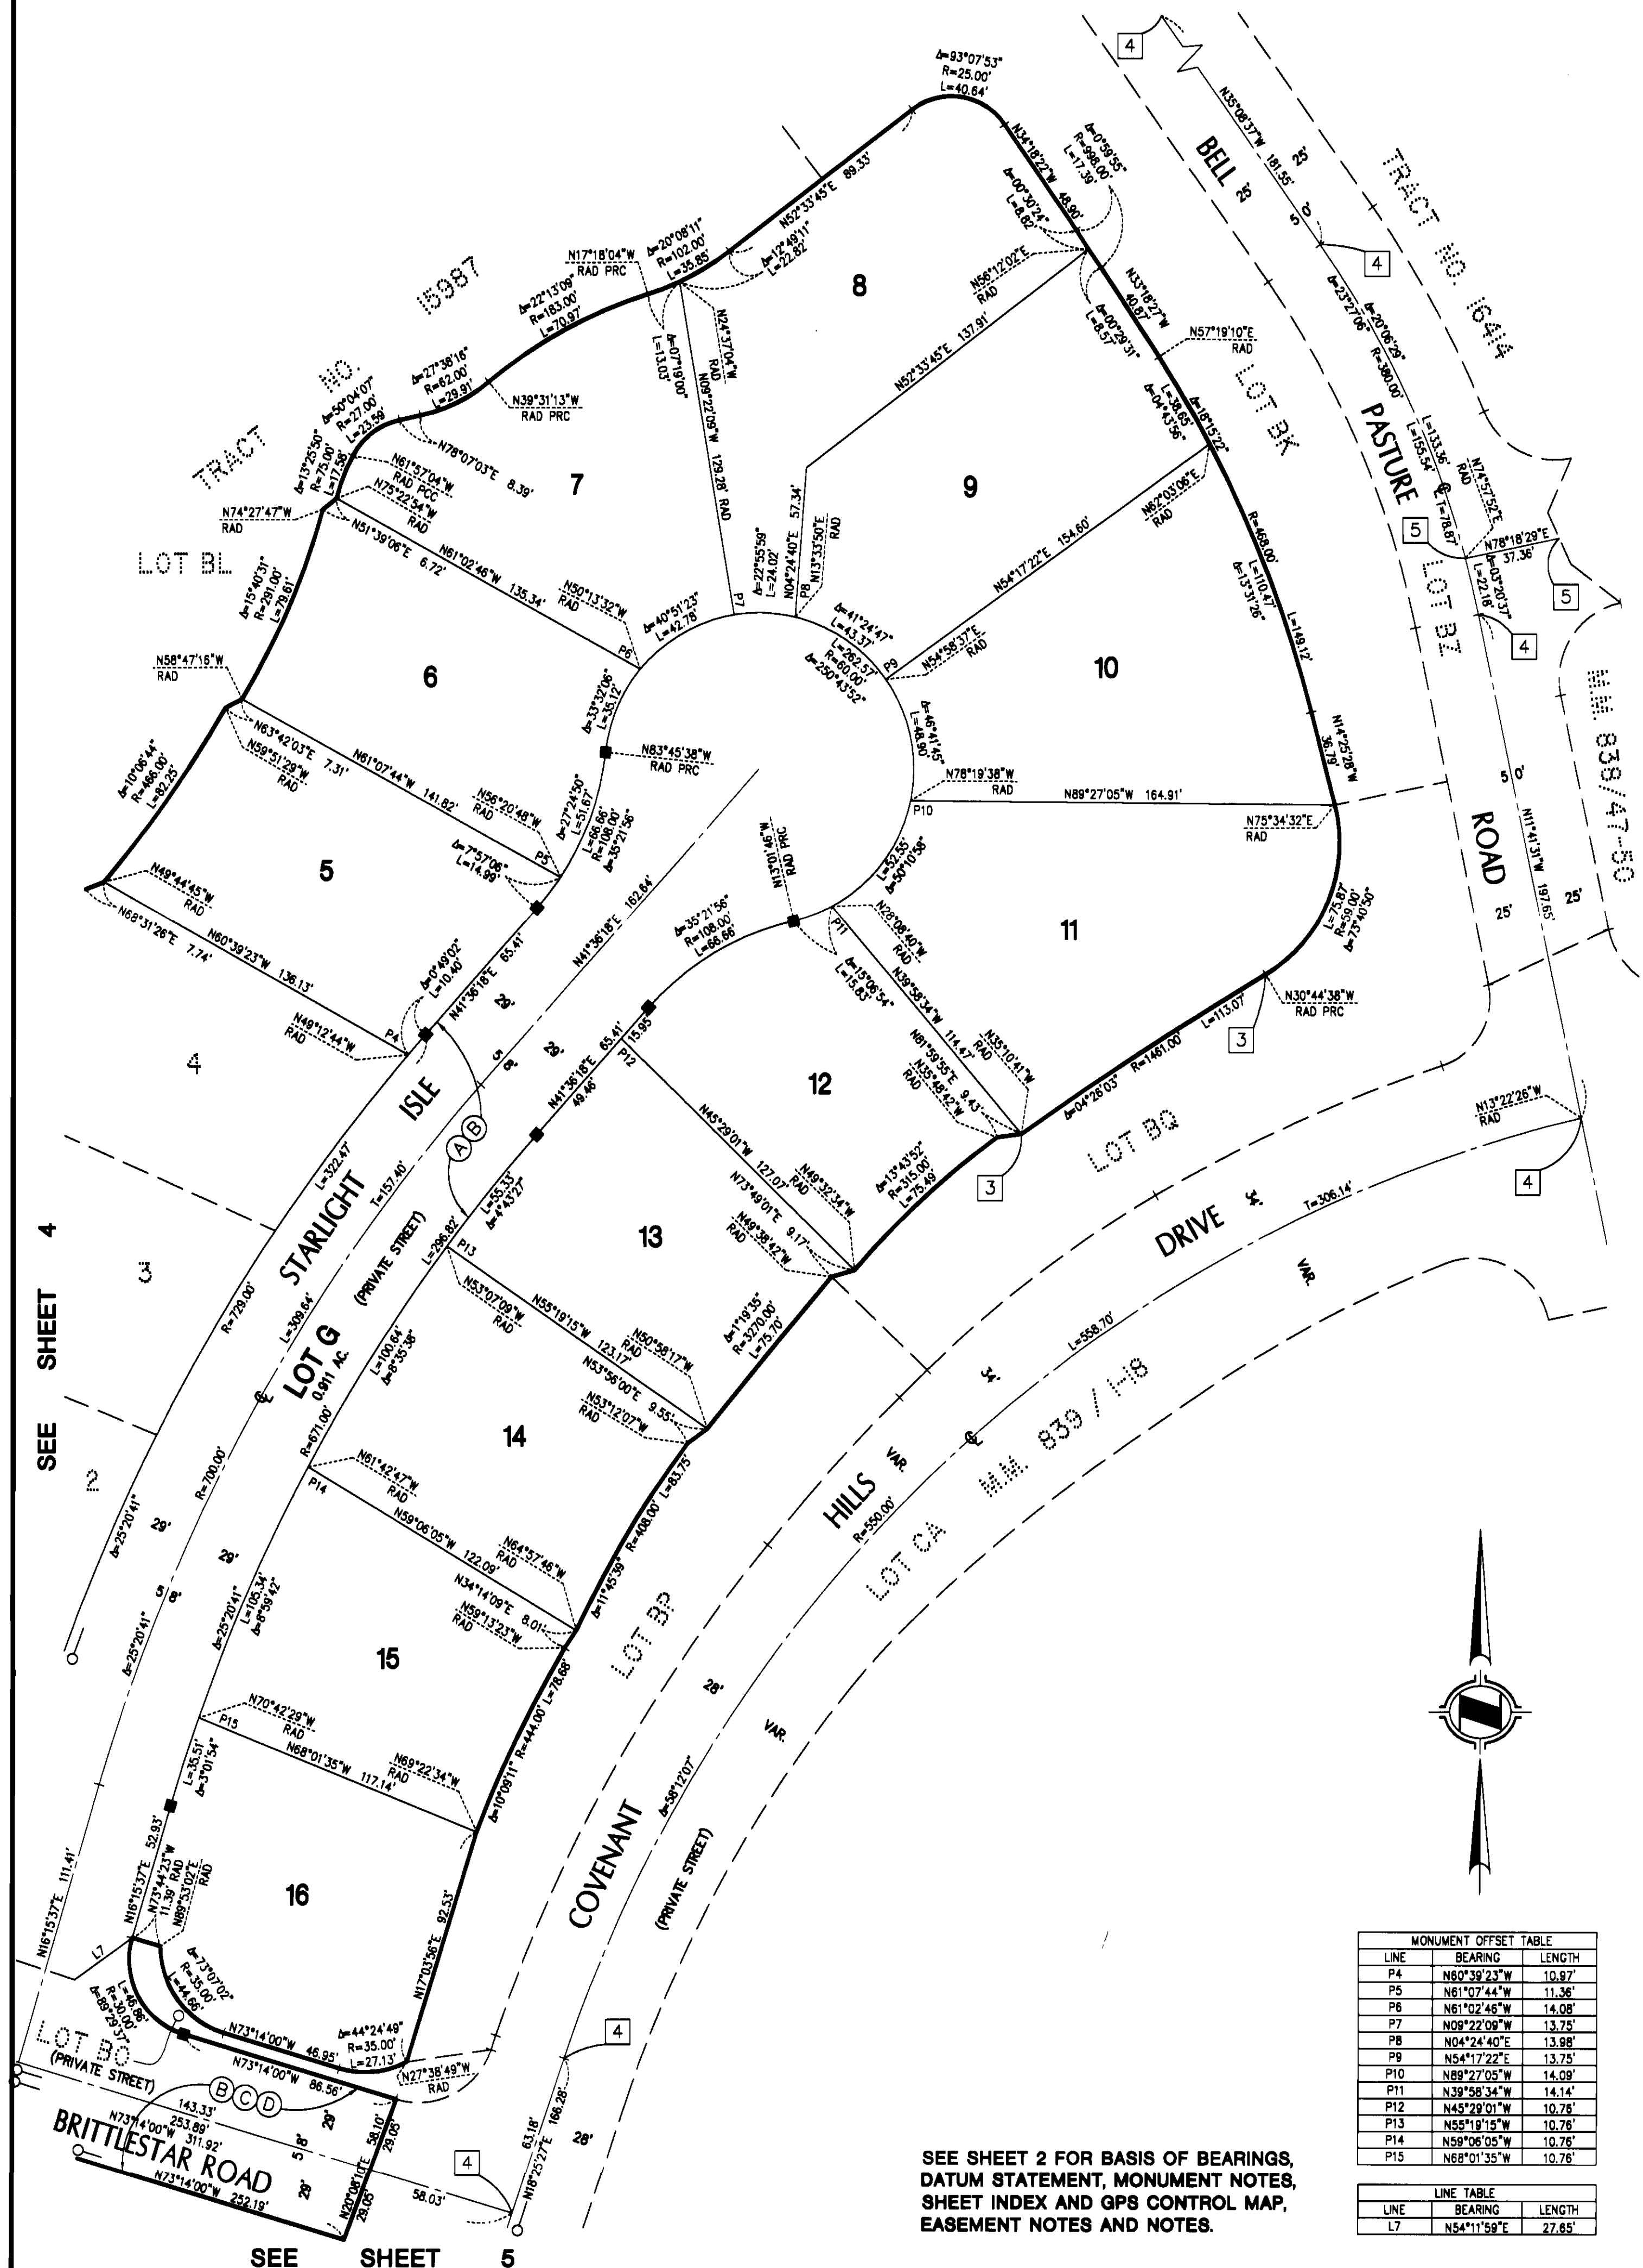

856 32

856 33

SHEET 4 OF 5 SHEETS
SCALE: 1" = 40'
31 NUMBERED LOTS AND
LOTS A THROUGH H, INCLUSIVE
ACREAGE: 12.180 ACRES
(ALL OF TENTATIVE
TRACT NO. 16390)

TRACT NO. 16390

IN UNINCORPORATED TERRITORY OF THE COUNTY OF ORANGE,
STATE OF CALIFORNIA


HUNSAKER AND ASSOCIATES IRVINE, INC.
RORY S. WILLIAMS, L.S. 6664 DATE OF SURVEY: NOVEMBER, 2002

SEE SHEET 2 FOR BASIS OF BEARINGS,
DATUM STATEMENT, MONUMENT NOTES,
SHEET INDEX AND GPS CONTROL MAP,
EASEMENT NOTES AND NOTES.

LINE TABLE		
LINE	BEARING	LENGTH
L1	N36°05'14"W	32.90'
L2	N64°27'18"E	31.66'
L5	N21°11'21"W	27.96'
L6	N72°10'43"W	24.01'
L7	N54°11'59"E	27.65'

CURVE TABLE			
CURVE	DELTA	RADIUS	LENGTH
C1	24°30'43"	30.00'	12.84'

MONUMENT OFFSET TABLE		
LINE	BEARING	LENGTH
P1	N67°27'34"W	10.77'
P2	N67°51'59"W	10.79'
P3	N66°08'02"W	17.03'
P4	N60°39'23"W	10.97'
P16	N24°06'45"E	16.75'
P17	N24°06'45"E	10.75'
P18	N24°06'45"E	10.75'
P19	N24°06'45"E	10.75'
P20	N24°06'45"E	10.75'
P32	N72°29'42"W	16.75'
P33	N65°12'52"W	16.75'

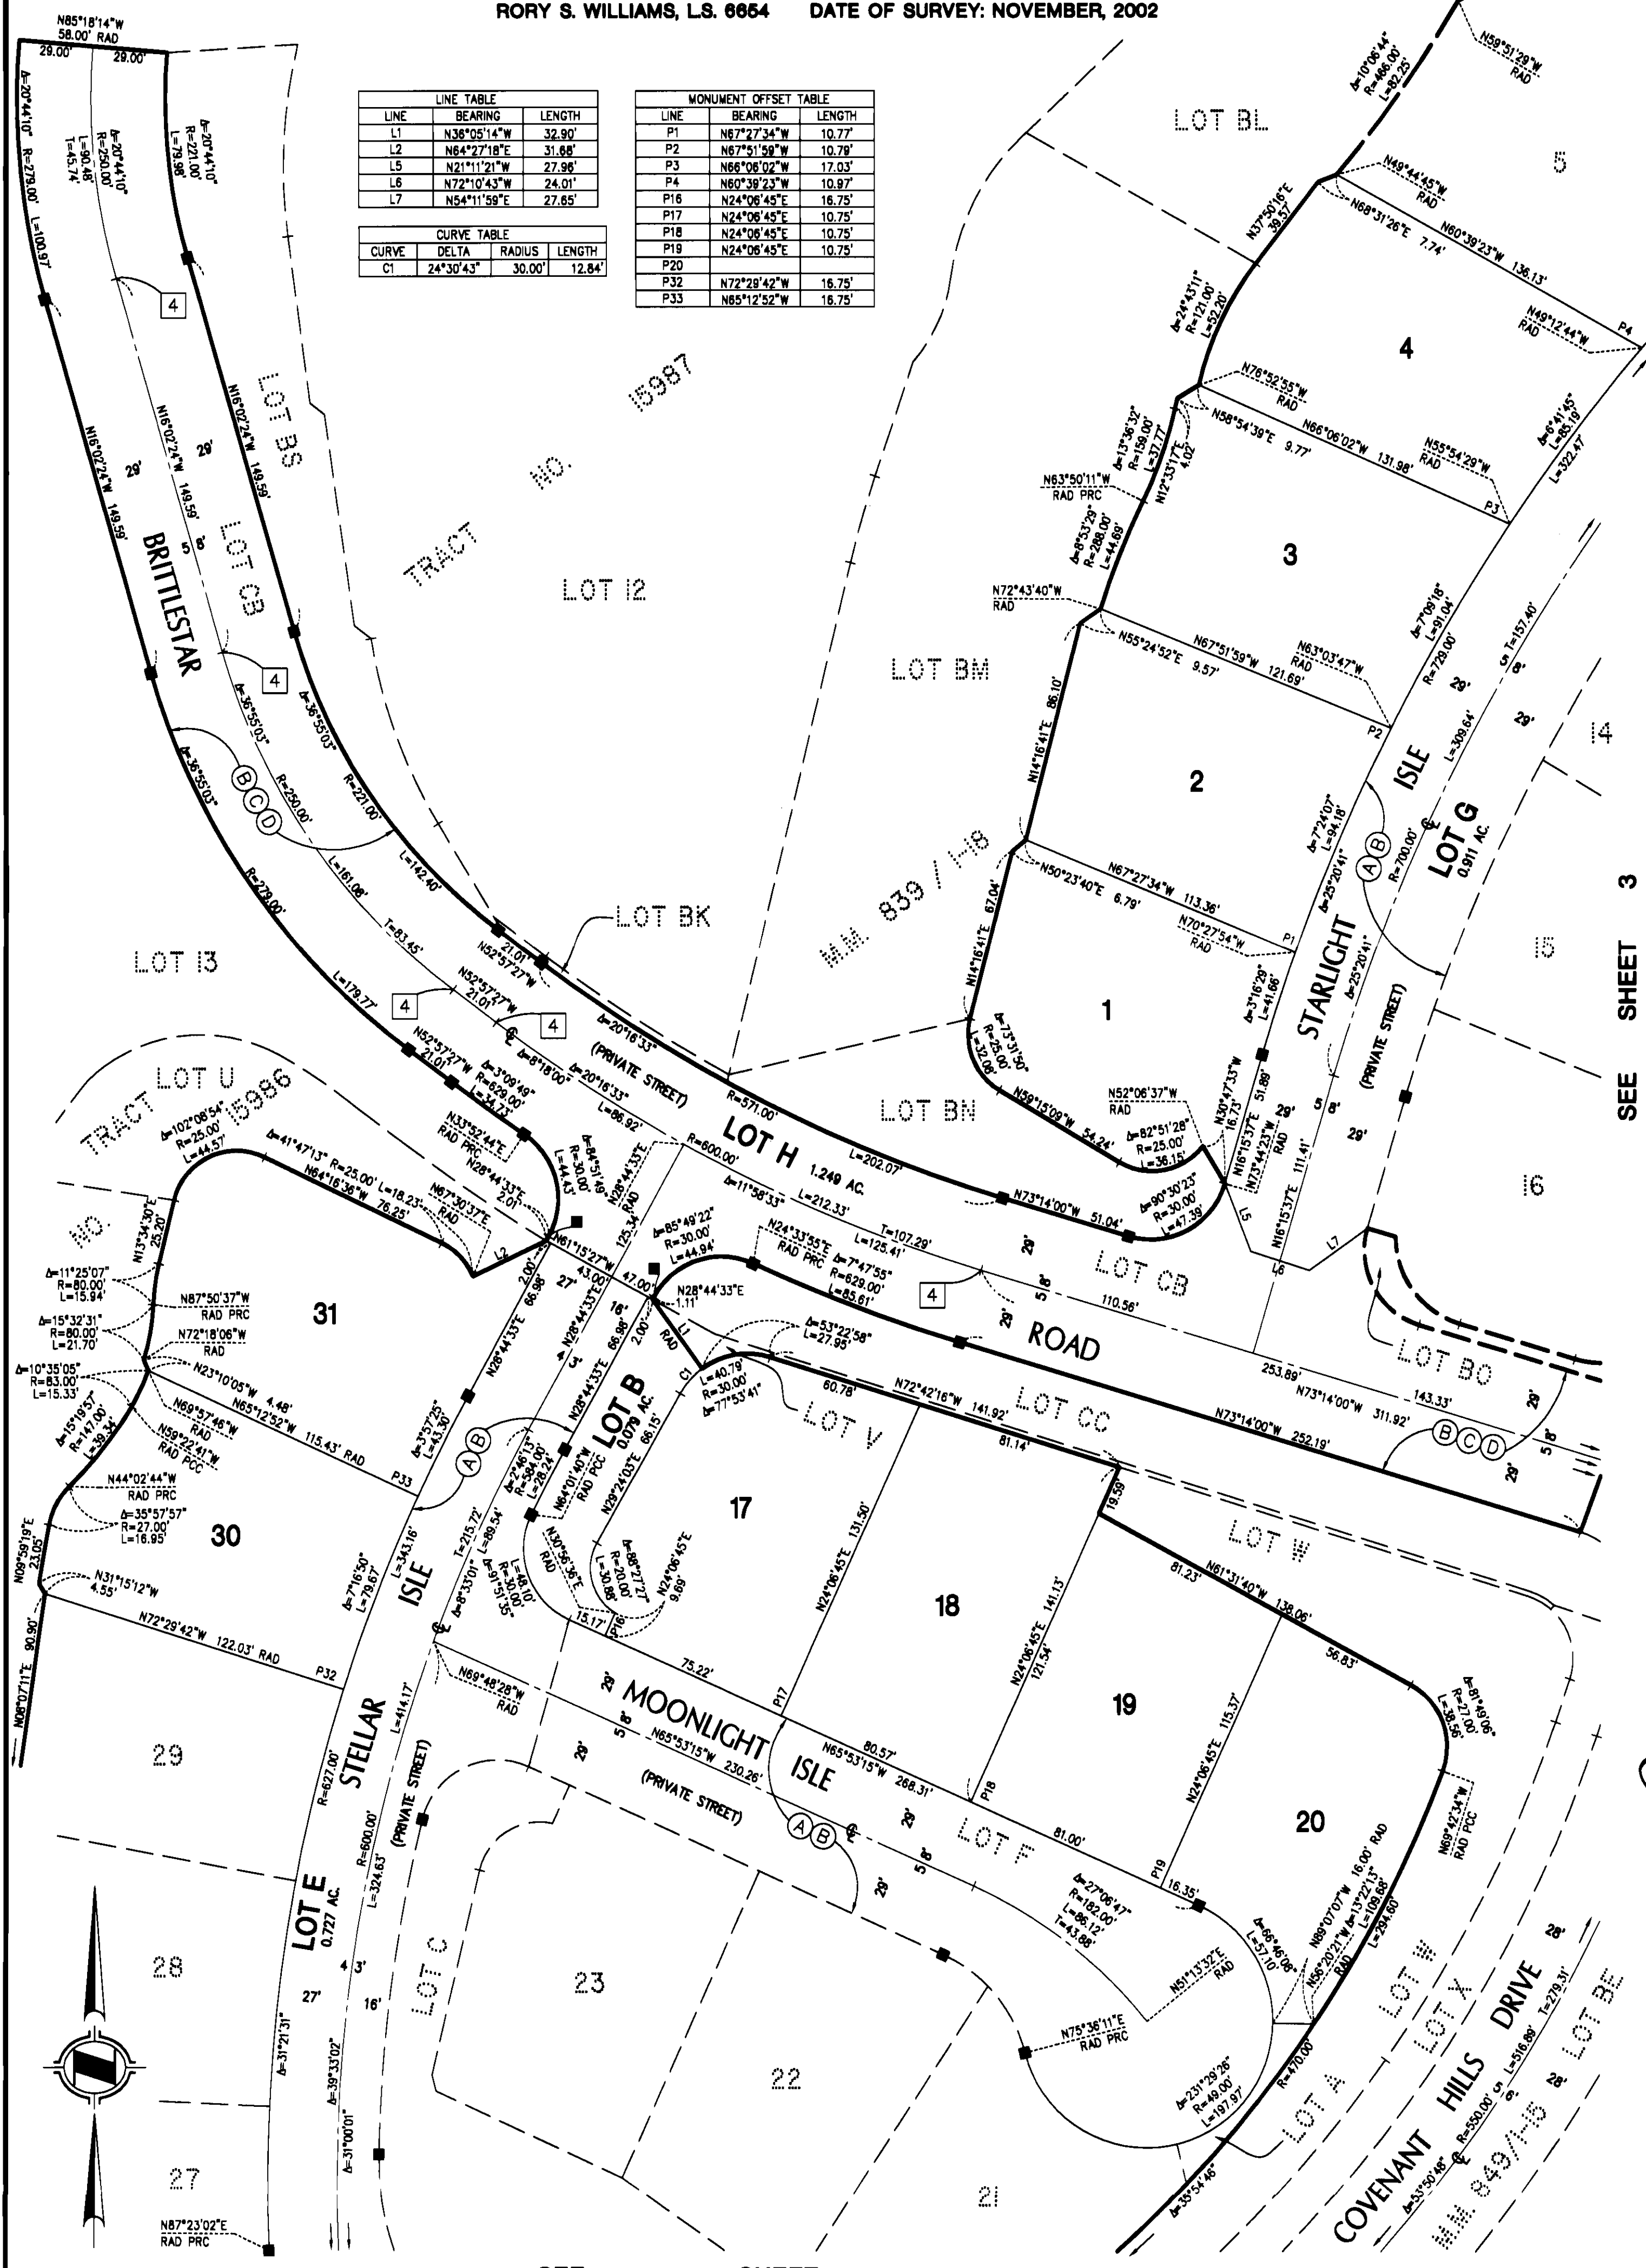

856 33


856 34

SHEET 5 OF 5 SHEETS
SCALE: 1" = 40'
31 NUMBERED LOTS AND
LOTS A THROUGH H, INCLUSIVE
ACREAGE: 12.180 ACRES
(ALL OF TENTATIVE
TRACT NO. 16390)

TRACT NO. 16390

IN UNINCORPORATED TERRITORY OF THE COUNTY OF ORANGE,
STATE OF CALIFORNIA

HUNSAKER AND ASSOCIATES IRVINE, INC.
RORY S. WILLIAMS, L.S. 6864 DATE OF SURVEY: NOVEMBER, 2002

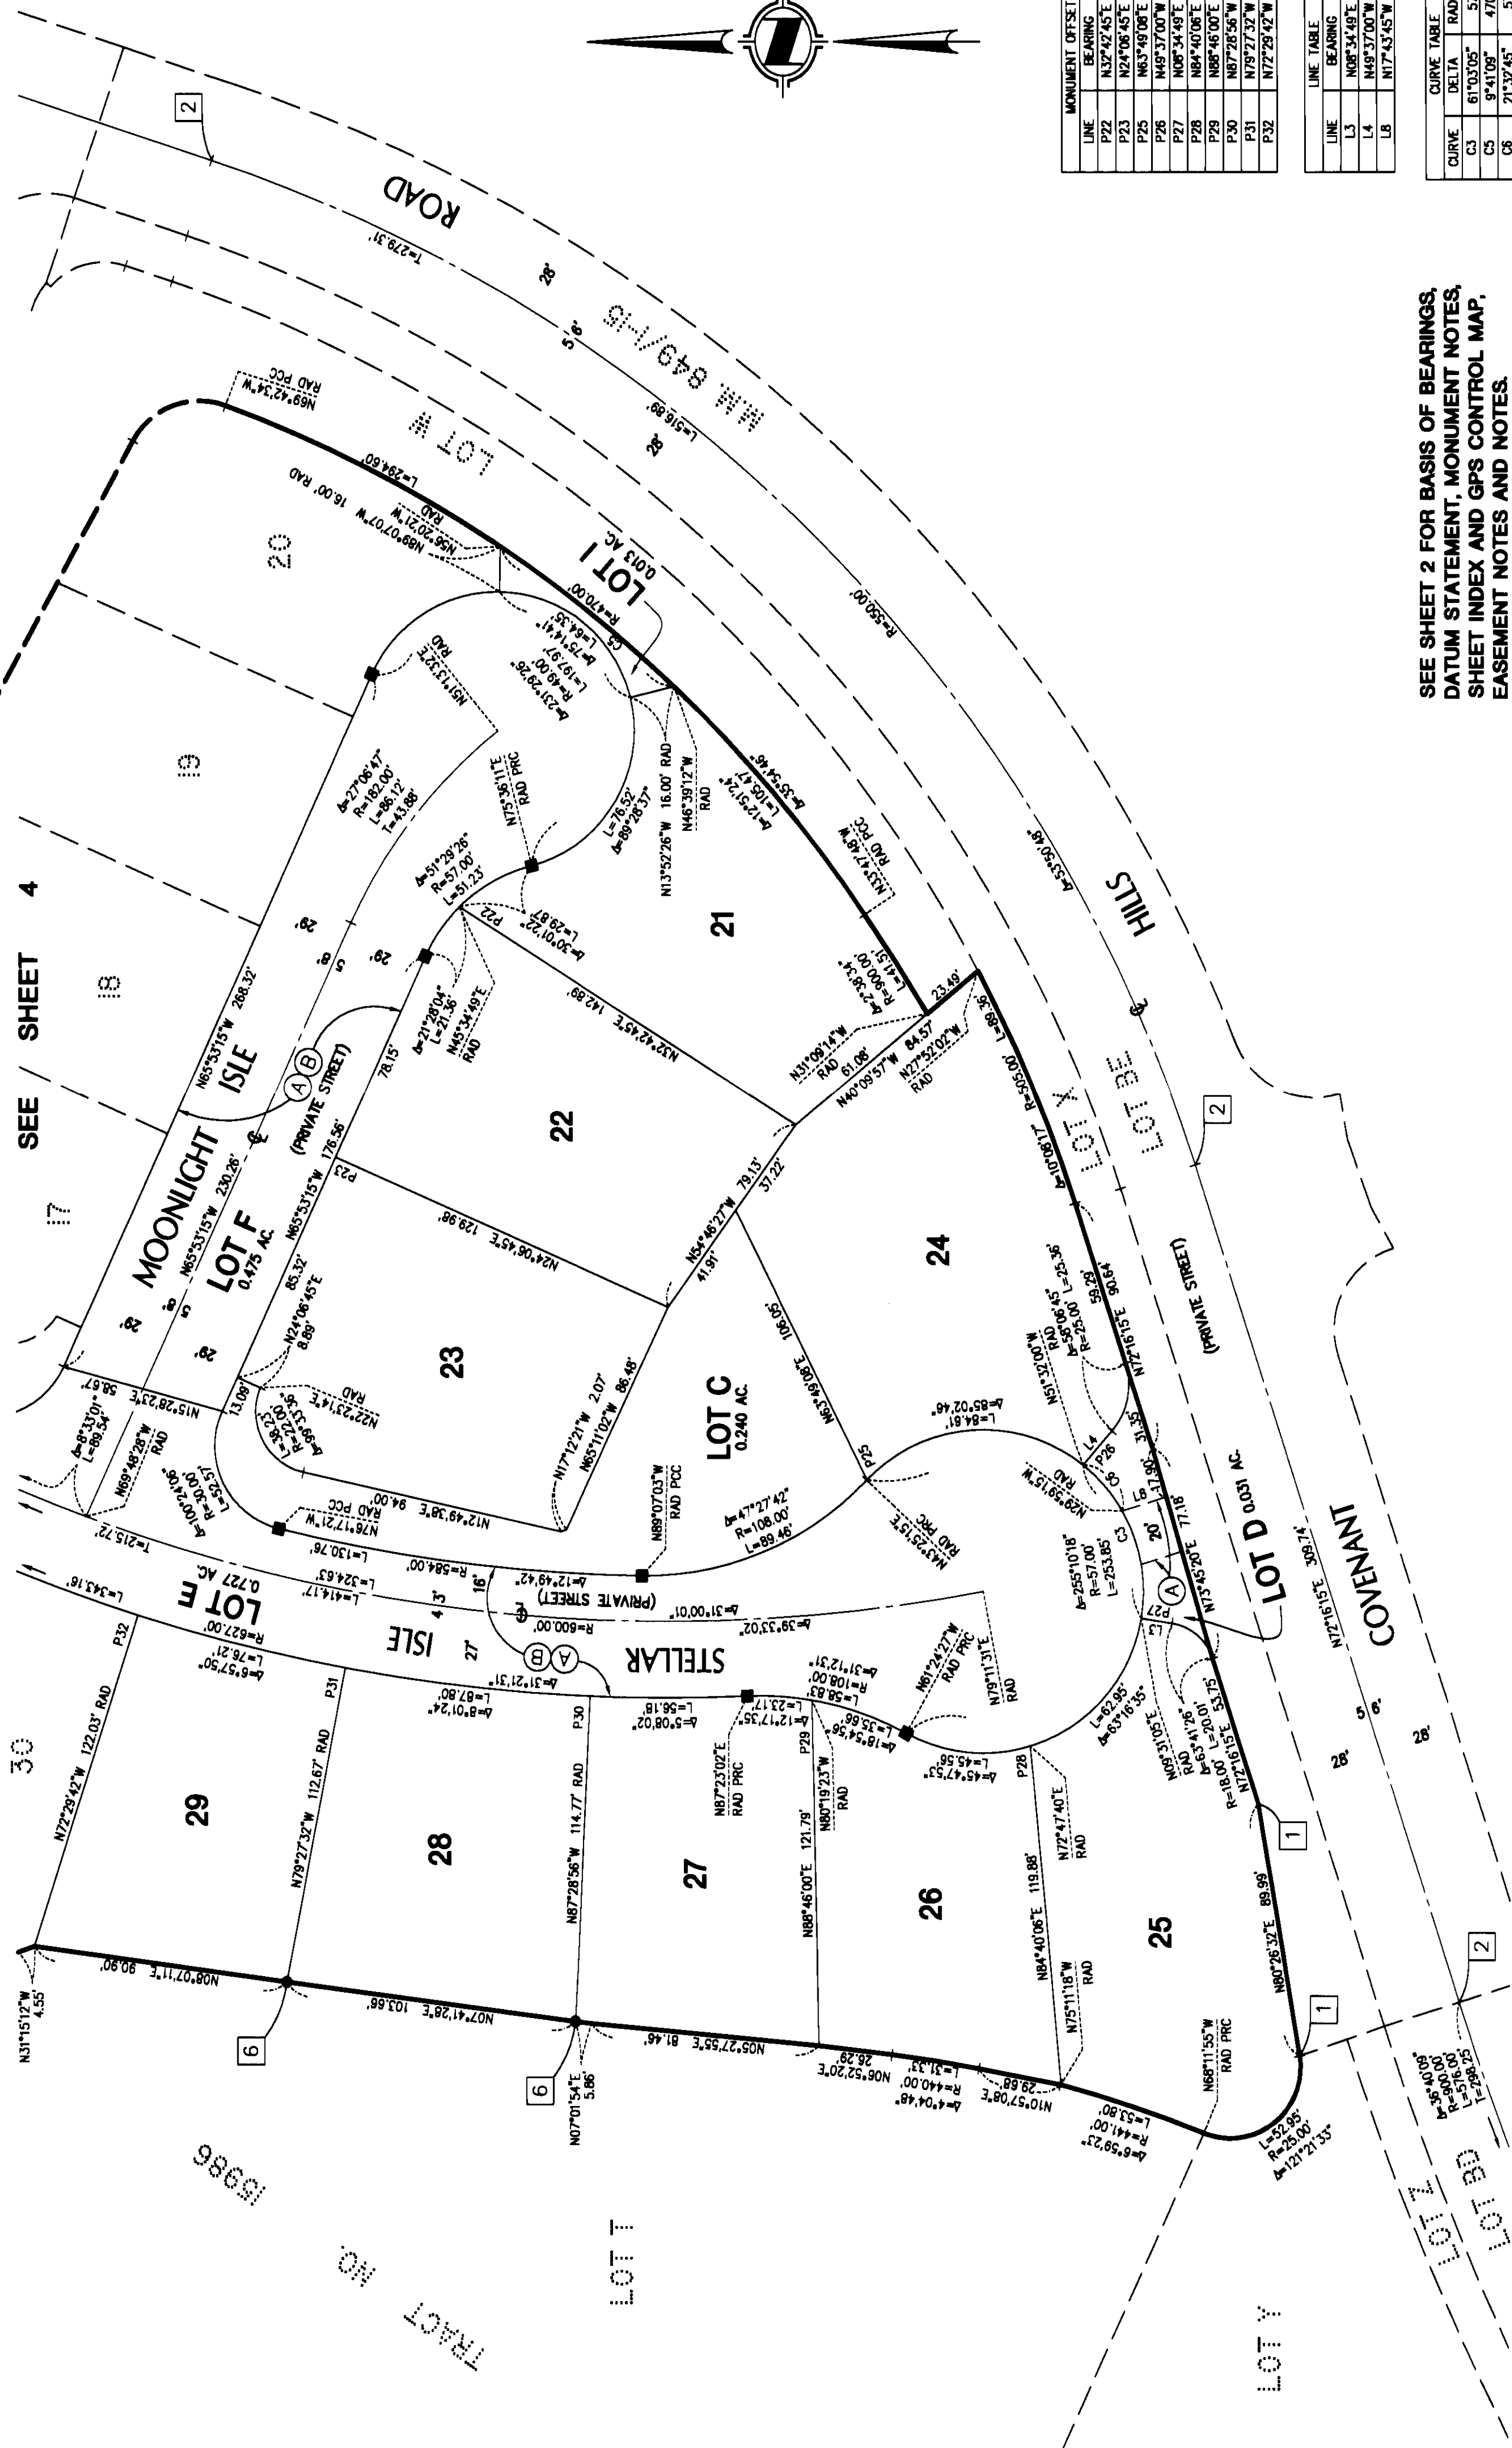

MONUMENT OFFSET TABLE		
LINE	BEARING	LENGTH
P22	N37°42'45"E	10.98'
P23	N24°06'45"E	10.75'
P25	N63°49'06"E	10.88'
P26	N49°37'00"W	10.76'
P27	N08°34'49"E	11.04'
P28	N84°40'06"E	10.75'
P29	N88°45'00"E	12.24'
P30	N87°26'56"W	12.75'
P31	N79°27'32"W	12.75'
P32	N72°29'42"W	16.75'

LINE TABLE		
LINE	BEARING	LENGTH
L3	N08°34'49"E	11.12'
L4	N49°37'00"W	15.91'
L8	N17°43'45"W	16.50'

CURVE TABLE		
CURVE	DELTA	RADIUS
C3	61°03'05"	57.00'
C5	9°41'08"	470.00'
C8	21°32'45"	57.00'

SEE SHEET 2 FOR BASIS OF BEARINGS,
DATUM STATEMENT, MONUMENT NOTES,
SHEET INDEX AND GPS CONTROL MAP,
EASEMENT NOTES AND NOTES.