

SHEET 1 OF 6 SHEETS
37 NUMBERED LOTS AND
LOTS A THROUGH N INCLUSIVE
ACREAGE: 17.499 ACRES
(FINAL UNIT OF VESTING
TENTATIVE TRACT NO. 16395)

TRACT NO. 16395

IN UNINCORPORATED TERRITORY OF THE COUNTY OF ORANGE,
STATE OF CALIFORNIA

BEING A SUBDIVISION OF LOTS 4, 6, AF AND AR OF TRACT NO. 15986, AS PER MAP
FILED IN BOOK 849, PAGES 1 THROUGH 16, INCLUSIVE, OF MISCELLANEOUS MAPS,
IN THE OFFICE OF THE COUNTY RECORDER OF SAID COUNTY.

HUNSAKER AND ASSOCIATES IRVINE, INC.
RORY S. WILLIAMS, L.S. 6654 DATE OF SURVEY: JULY, 2002

ACCEPTED AND FILED AT THE
REQUEST OF
First American Title Ins.
DATE: October 28, 2004
TIME: 11:19 AM FEE: \$ 22.00
INSTRUMENT NO. 2004000973024
BOOK 861 PAGE 36-41mm
TOM DALY
COUNTY CLERK RECORDER
BY Sammy J. Demettry DEPUTY

OWNERSHIP CERTIFICATE:

WE, THE UNDERSIGNED, BEING ALL PARTIES HAVING ANY RECORD TITLE INTEREST IN THE LAND COVERED BY THIS MAP, DO HEREBY CONSENT TO THE PREPARATION AND RECORDATION OF SAID MAP, AS SHOWN WITHIN THE DISTINCTIVE BORDER LINE.

WE HEREBY DEDICATE TO COUNTY OF ORANGE THE EASEMENTS FOR INGRESS AND EGRESS OF EMERGENCY AND PUBLIC SERVICE VEHICLES AS SHOWN ON SAID MAP.

WE ALSO HEREBY DEDICATE TO THE SANTA MARGARITA WATER DISTRICT THE EASEMENTS FOR WATER, RECYCLED WATER, SEWER AND ACCESS PURPOSES OVER THOSE EASEMENT AREAS AS SHOWN ON SAID MAP, WHICH EASEMENTS SHALL BE SUBJECT TO THE SAME CONDITIONS AS SHOWN IN THAT CERTAIN GRANT OF EASEMENT TO SANTA MARGARITA WATER DISTRICT RECORDED SEPTEMBER 18, 2002, AS INSTRUMENT NO. 20020799401 OF OFFICIAL RECORDS, COUNTY OF ORANGE.

DMB LADERA, LLC, A DELAWARE LIMITED LIABILITY COMPANY, OWNER.

BY: RANCHO MISSION VIEJO, L.L.C., A DELAWARE LIMITED LIABILITY COMPANY, ITS
AUTHORIZED AGENT AND MANAGER.

BY: Paul Johnson BY: Gregory S. Edwards
NAME: PAUL JOHNSON NAME: Gregory S. Edwards
TITLE: SVP - COMMUNITY DEVELOPMENT TITLE: CFO

NOTARY ACKNOWLEDGMENT:

STATE OF CALIFORNIA } SS
COUNTY OF ORANGE }

ON July 22, 2004 BEFORE ME, LINDA K. LEDGER, Notary Public PERSONALLY
APPEARED PAUL JOHNSON AND GREGORY S. EDWARDS PERSONALLY
KNOWN TO ME (OR PROVED TO ME ON THE BASIS OF SATISFACTORY EVIDENCE) TO BE THE PERSON(S)
WHOSE NAME(S) IS/ARE SUBSCRIBED TO THE WITHIN INSTRUMENT AND ACKNOWLEDGED TO ME THAT
HE/SHE/HEY EXECUTED THE SAME IN HIS/HER/THEIR AUTHORIZED CAPACITY(IES), AND THAT BY
HIS/HER/THEIR SIGNATURE(S) ON THE INSTRUMENT THE PERSON(S), OR ENTITY UPON BEHALF OF
WHICH THE PERSON(S) ACTED, EXECUTED THE INSTRUMENT.

WITNESS MY HAND:

SIGNATURE Linda K. Ledger
NOTARY PUBLIC IN AND FOR SAID STATE
LINDA K. LEDGER
(NAME PRINTED)

MY PRINCIPAL PLACE OF BUSINESS IS
IN ORANGE COUNTY.
MY COMMISSION EXPIRES: 03/07/07

AUTOMATIC FIRE SPRINKLER NOTE:

ALL COMMERCIAL STRUCTURES GREATER THAN 6,000 SQUARE FEET, ALL MULTIFAMILY RESIDENTIAL STRUCTURES, ALL SINGLE-FAMILY STRUCTURES EXCEEDING 5,500 SQUARE FEET, AND ALL STRUCTURES EXCEEDING FIRE DEPARTMENT ACCESS REQUIREMENTS SHALL BE PROTECTED BY AN AUTOMATIC FIRE SPRINKLER SYSTEM.

SPECIAL FIRE PROTECTION NOTE:

SUBJECT PROPERTY IS IN A SPECIAL FIRE PROTECTION AREA AND MUST MEET ALL REQUIREMENTS FOR DEVELOPMENT WITHIN THE AREA.

HIGH FIRE HAZARD AREA NOTE:

THE LOTS SHOWN ON THIS MAP ARE IN A HIGH FIRE HAZARD AREA DUE TO WILDLAND EXPOSURE.

NOTE:

THE PRIVATE STREETS CONSTRUCTED WITHIN THIS MAP SHALL BE OWNED, OPERATED AND MAINTAINED BY THE DEVELOPER, SUCCESSORS OR ASSIGNS. THE COUNTY OF ORANGE SHALL HAVE NO RESPONSIBILITY THEREFOR, UNLESS PURSUANT TO APPROPRIATE SECTIONS OF THE STREETS AND HIGHWAYS CODE OF THE STATE OF CALIFORNIA, THE SAID PRIVATE STREETS HAVE BEEN ACCEPTED INTO THE COUNTY ROAD SYSTEM BY APPROPRIATE RESOLUTION OF THE ORANGE COUNTY BOARD OF SUPERVISORS.

SURVEYOR'S STATEMENT:

THIS MAP WAS PREPARED BY ME OR UNDER MY DIRECTION AND IS BASED UPON A FIELD SURVEY IN CONFORMANCE WITH THE REQUIREMENTS OF THE SUBDIVISION MAP ACT AND LOCAL ORDINANCE AT THE REQUEST OF DMB LADERA, L.L.C., IN JULY, 2002. I HEREBY STATE THAT ALL MONUMENTS ARE OF THE CHARACTER AND OCCUPY THE POSITIONS INDICATED, OR THAT THEY WILL BE SET IN SUCH POSITIONS; AND THAT SAID MONUMENTS ARE SUFFICIENT TO ENABLE THE SURVEY TO BE RETRACED. I HEREBY STATE THAT THIS FINAL MAP SUBSTANTIALLY CONFORMS TO THE CONDITIONALLY APPROVED TENTATIVE MAP.

Rory S. Williams 6/29/04
RORY S. WILLIAMS, L.S. 6654 DATE
LICENSE EXPIRES: 12/31/05




COUNTY SURVEYOR'S STATEMENT

I HEREBY STATE THAT I HAVE EXAMINED THIS MAP AND HAVE FOUND IT TO BE SUBSTANTIALLY IN CONFORMANCE WITH THE TENTATIVE MAP AS FILED WITH, AMENDED AND APPROVED BY THE ORANGE COUNTY SUBDIVISION COMMITTEE; THAT ALL PROVISIONS OF THE SUBDIVISION MAP ACT AND COUNTY SUBDIVISION REGULATIONS HAVE BEEN COMPLIED WITH AND I AM SATISFIED SAID MAP IS TECHNICALLY CORRECT.

DATED THIS 22nd DAY OF September, 2004.

Raymond L. Mathe
RAYMOND L. MATHE, COUNTY SURVEYOR
P.L.S. 6185, EXPIRATION DATE: 03-31-06

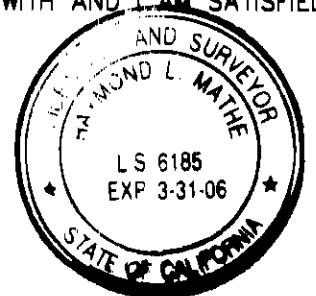

COUNTY TREASURER-TAX COLLECTOR'S CERTIFICATE:

STATE OF CALIFORNIA } SS
COUNTY OF ORANGE }

I HEREBY CERTIFY THAT ACCORDING TO THE RECORDS OF MY OFFICE THERE ARE NO LIENS AGAINST THE LAND COVERED BY THIS MAP OR ANY PART THEREOF FOR UNPAID STATE, COUNTY, MUNICIPAL OR LOCAL TAXES OR SPECIAL ASSESSMENTS COLLECTED AS TAXES, EXCEPT TAXES OR SPECIAL ASSESSMENTS COLLECTED AS TAXES NOT YET PAYABLE.

AND DO CERTIFY TO THE RECORDER OF ORANGE COUNTY THAT THE PROVISIONS OF THE SUBDIVISION MAP ACT HAVE BEEN COMPLIED WITH REGARDING DEPOSITS TO SECURE PAYMENT OF TAXES OR SPECIAL ASSESSMENTS COLLECTED AS TAXES ON THE LAND COVERED BY THIS MAP.

DATED THIS 11th DAY OF August, 2004.

John M.W. Moorlach
JOHN M.W. MOORLACH
COUNTY TREASURER-TAX COLLECTOR

BY: John M.W. Moorlach
DEPUTY TREASURER-TAX COLLECTOR

CLERK OF THE BOARD OF SUPERVISORS' CERTIFICATE:

STATE OF CALIFORNIA } SS
COUNTY OF ORANGE }

I HEREBY CERTIFY THAT THIS MAP WAS PRESENTED FOR APPROVAL TO THE BOARD OF SUPERVISORS OF THE COUNTY OF ORANGE AT REGULAR MEETING THEREOF HELD ON THE 19th DAY OF October, 2004, AND THAT THEREUPON SAID BOARD DID, BY AN ORDER DULY PASSED AND ENTERED, APPROVE SAID MAP.

AND DID ACCEPT ON BEHALF OF THE COUNTY OF ORANGE THE EASEMENTS FOR INGRESS AND EGRESS OF EMERGENCY AND PUBLIC SERVICE VEHICLES AS DEDICATED.

DATED THIS 19th DAY OF October, 2004.

Darlene J. Bloom
CLERK OF THE BOARD OF SUPERVISORS
DARLENE J. BLOOM



CERTIFICATE OF ACCEPTANCE - SANTA MARGARITA WATER DISTRICT

THE UNDERSIGNED, BEING THE DULY APPOINTED AGENT OF THE SANTA MARGARITA WATER DISTRICT, A PUBLIC CORPORATION IN ORANGE COUNTY, CALIFORNIA, PURSUANT TO ITS RESOLUTION NO. 88-10-2, DOES HEREBY ACCEPT ON BEHALF OF SAID DISTRICT, THE EASEMENTS FOR WATER, RECYCLED WATER, SEWER AND ACCESS PURPOSES AS DEDICATED AND SHOWN ON THIS TRACT MAP, BY AND BETWEEN THE SANTA MARGARITA WATER DISTRICT AND DMB LADERA, L.L.C., A DELAWARE LIMITED LIABILITY COMPANY, AND DOES HEREBY CERTIFY THAT THE GRANTEE CONSENTS TO THE RECORDATION OF SAID TRACT MAP.

Daniel R. Ferons
DANIEL R. FERONS, CHIEF ENGINEER
SANTA MARGARITA WATER DISTRICT

NOTARY ACKNOWLEDGMENT - SANTA MARGARITA WATER DISTRICT

STATE OF CALIFORNIA } SS
COUNTY OF ORANGE }

ON August 20, 2004 BEFORE ME, Kristen J. Collins PERSONALLY
APPEARED DANIEL R. FERONS, PERSONALLY KNOWN TO ME (OR PROVED TO ME ON THE BASIS OF SATISFACTORY EVIDENCE) TO BE THE PERSON WHOSE NAME IS SUBSCRIBED TO THE WITHIN INSTRUMENT AND ACKNOWLEDGED TO ME THAT HE EXECUTED THE SAME IN HIS AUTHORIZED CAPACITY, AND THAT BY HIS SIGNATURE ON THE INSTRUMENT THE PERSON, OR ENTITY UPON BEHALF OF WHICH THE PERSON ACTED, EXECUTED THE INSTRUMENT.

WITNESS MY HAND:

SIGNATURE Kristen J. Collins
NOTARY PUBLIC IN AND FOR SAID STATE
Kristen J. Collins
(NAME PRINTED)

MY PRINCIPAL PLACE OF BUSINESS IS
IN Orange COUNTY.
MY COMMISSION EXPIRES: Jan. 20, 2008


SIGNATURE OMISSIONS:

PURSUANT TO THE PROVISIONS OF SECTION 86436(a)(3)(C) OF THE SUBDIVISION MAP ACT, THE FOLLOWING SIGNATURES HAVE BEEN OMITTED:

LADERA DEVELOPMENT COMPANY, L.L.C., HOLDER OF OIL, GAS AND MINERAL RIGHTS RECORDED DECEMBER 10, 1996, AS INSTRUMENT NO. 19960624029 OF OFFICIAL RECORDS.

861-36

861-37

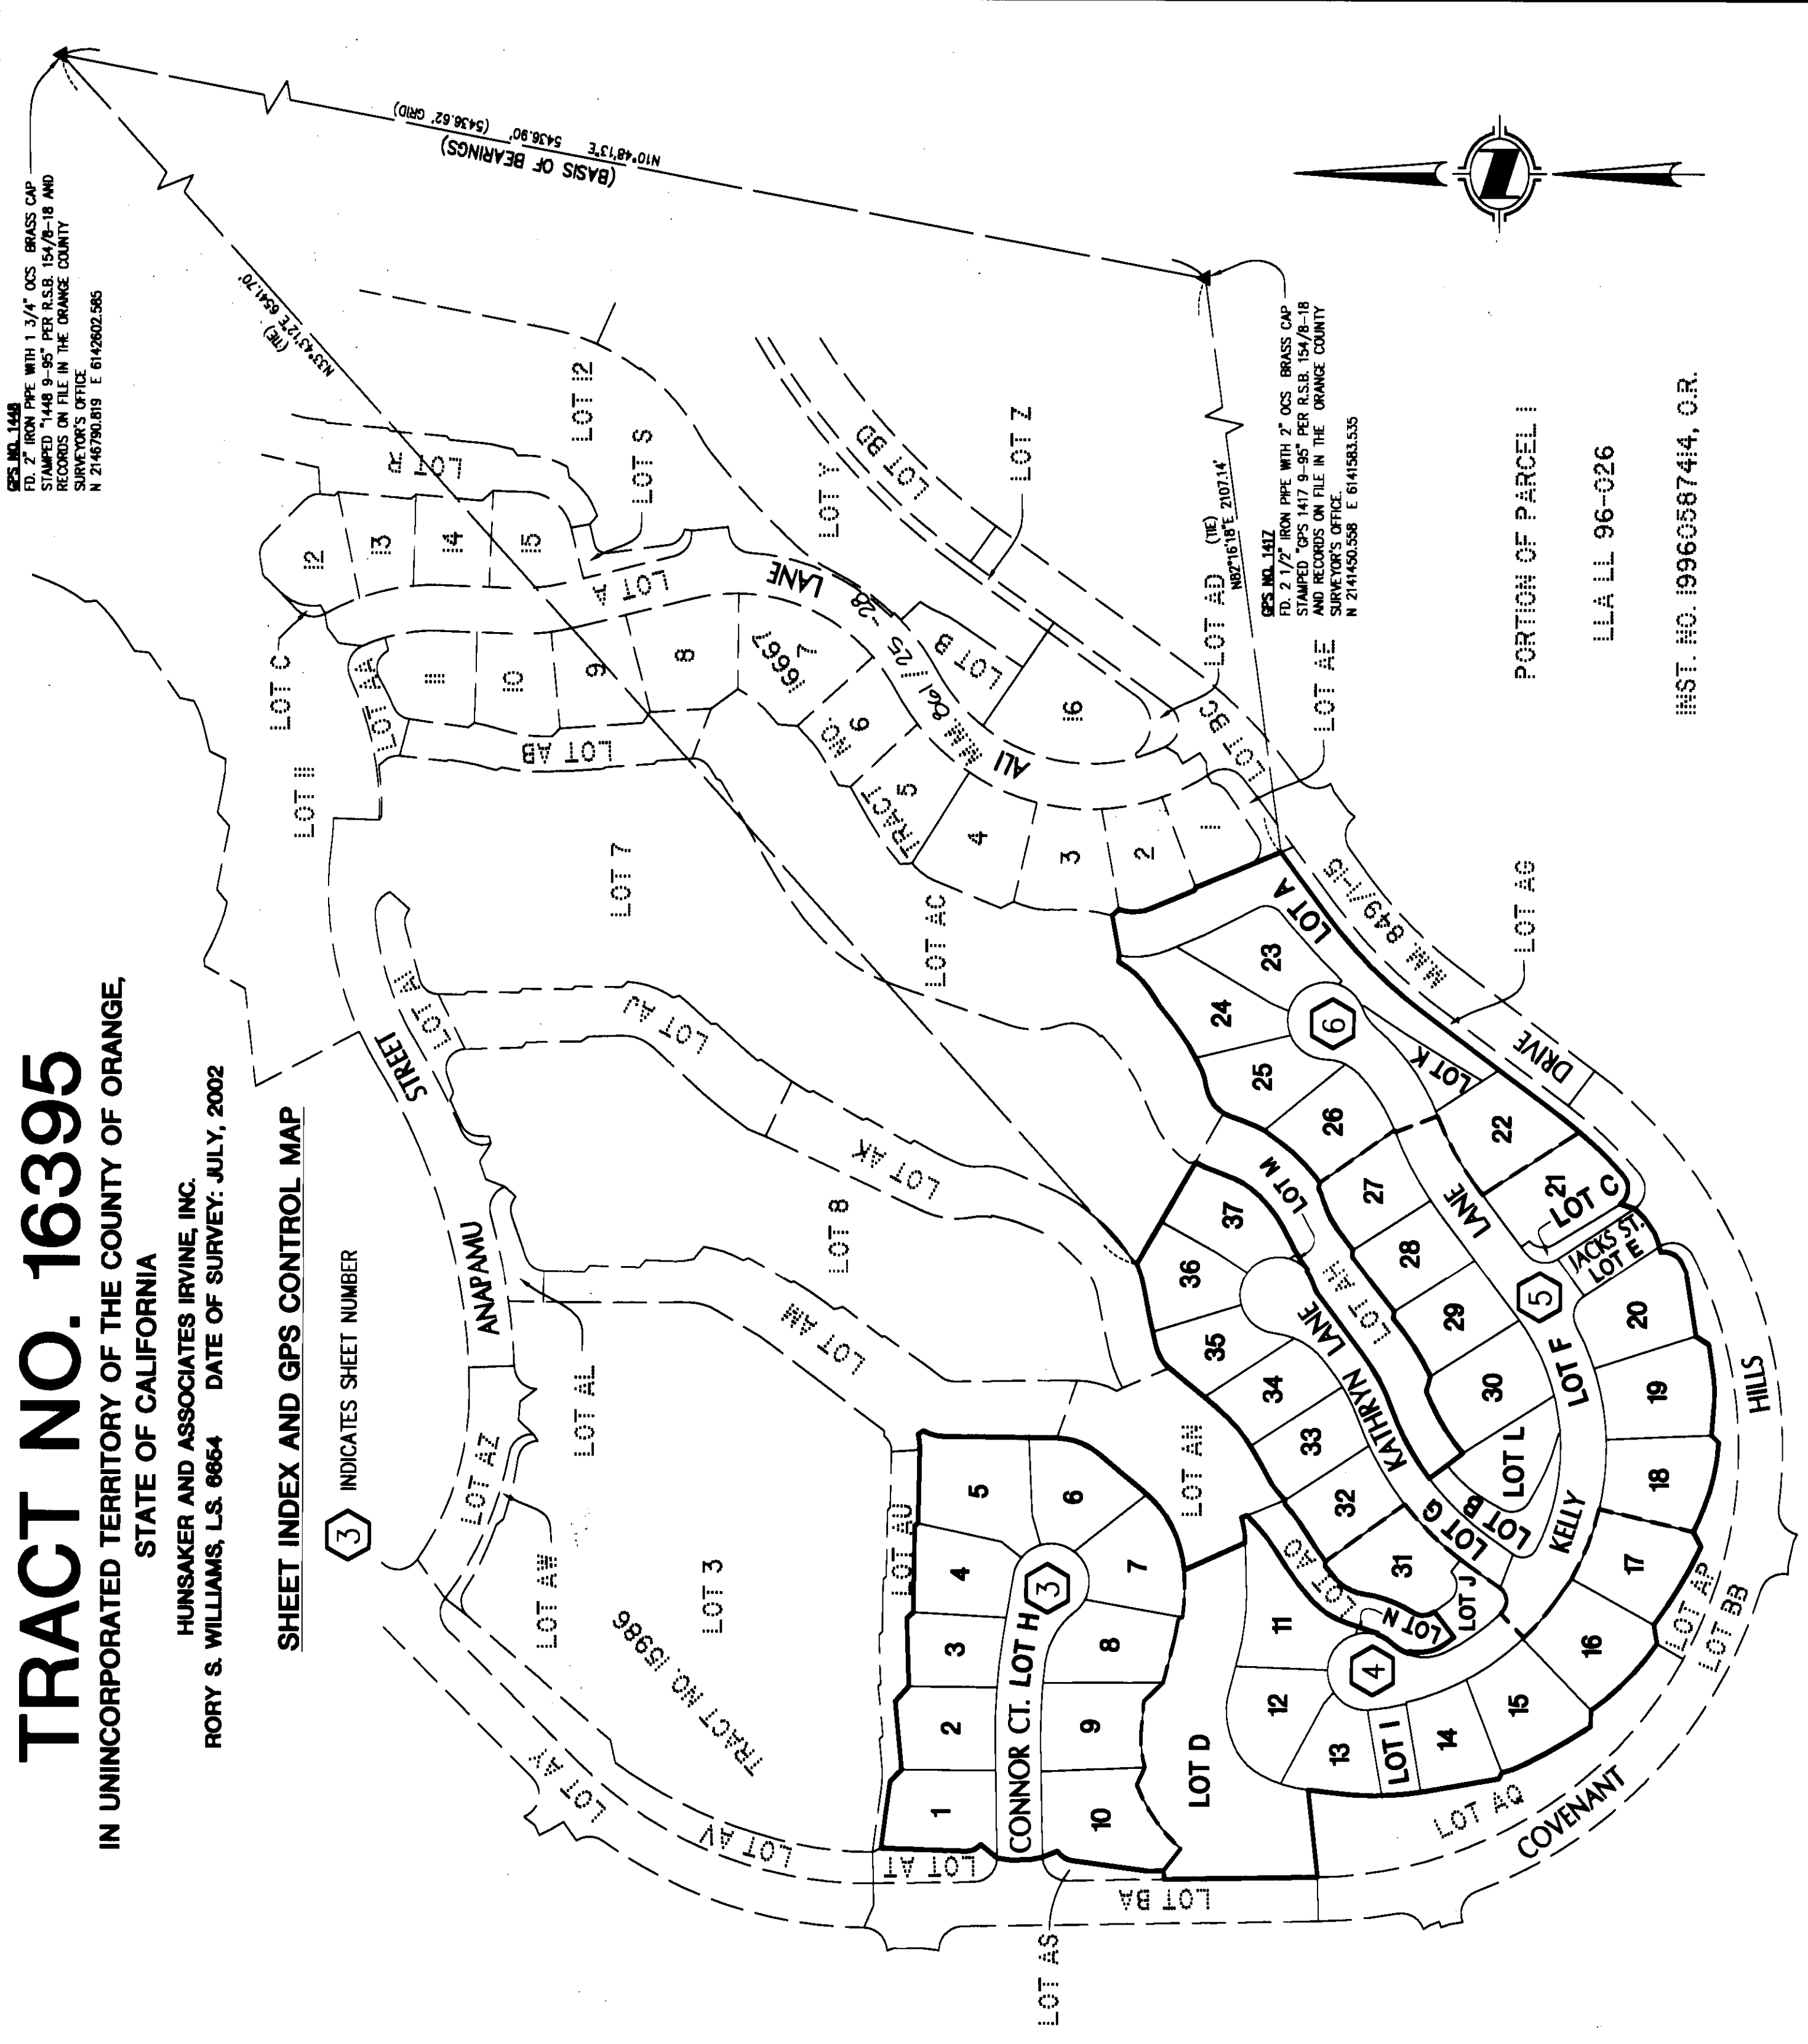

TRACT NO. 16395

IN UNINCORPORATED TERRITORY OF THE COUNTY OF ORANGE,
STATE OF CALIFORNIA

HUNSAKER AND ASSOCIATES IRVINE, INC.
RORY S. WILLIAMS, L.S. 6654 DATE OF SURVEY: JULY, 2002

SHEET INDEX AND GPS CONTROL MAP

3 INDICATES SHEET NUMBER

SHEET 2 OF 6 SHEETS
SCALE: 1" = 150'
37 NUMBERED LOTS AND
LOTS A THROUGH N INCLUSIVE
ACREAGE: 17.499 ACRES
(FINAL UNIT OF VESTING
TENTATIVE TRACT NO. 16395)

BASIS OF BEARINGS:

THE BEARINGS SHOWN HEREON ARE BASED ON THE BEARING BETWEEN O.C.S. HORIZONTAL CONTROL STATION GPS NO. 1417 AND STATION GPS NO. 1448 BEING N10°48'13"E PER RECORDS ON FILE IN THE OFFICE OF THE ORANGE COUNTY SURVEYOR.

DATUM STATEMENT:

COORDINATES SHOWN ARE BASED ON THE CALIFORNIA COORDINATE SYSTEM (CCS83). ZONE VI, 1983 NAD, (1991.35 EPOCH OCS GPS ADJUSTMENT). ALL DISTANCES SHOWN ARE GROUND, UNLESS OTHERWISE NOTED. TO OBTAIN GRID DISTANCE, MULTIPLY GROUND DISTANCE BY 0.999948293. THIS COMBINATION FACTOR IS PROJECT SPECIFIC.

MONUMENT NOTES:

- 2" IP, TAGGED L.S. 6654 OR LEAD, TACK & TAG L.S. 6654 OR NAIL & TAG L.S. 6654 OR 8" SAW STAMPED L.S. 6654, TO BE SET AT ALL TRACT BOUNDARY CORNERS WITHIN 90 DAYS AFTER ACCEPTANCE OF IMPROVEMENTS, UNLESS OTHERWISE NOTED.
- 1" IP, TAGGED L.S. 6654 OR LEAD, TACK & TAG L.S. 6654 OR NAIL & TAG L.S. 6654 OR 8" SAW STAMPED L.S. 6654, TO BE SET AT ALL LOT CORNERS, EXCEPT LOT CORNERS THAT ARE THE INTERSECTION OF SIDE LOT LINES WITH STREET RIGHT OF WAY, WITHIN 90 DAYS AFTER ACCEPTANCE OF IMPROVEMENTS, UNLESS OTHERWISE NOTED.
- 8" SAW STAMPED L.S. 6654 OR LEAD, TACK & TAG L.S. 6654 OR 1" IP, TAGGED L.S. 6654, TO BE SET AT ALL STREET CORNER POINTS OF CONTROL, WITHIN 90 DAYS AFTER ACCEPTANCE OF IMPROVEMENTS, UNLESS OTHERWISE NOTED.
- LEAD, TACK & TAG L.S. 6654, TO BE SET IN TOP OF CURB AT AN OFFSET ALONG FRONT SIDE LOT LINES PRODUCED, IN LIEU OF AT FRONT LOT CORNERS, WITHIN 90 DAYS AFTER ACCEPTANCE OF IMPROVEMENTS, UNLESS OTHERWISE NOTED. BEARING AND DISTANCE OF PRODUCTION IS AS NOTED IN MONUMENT OFF-SET TABLES HEREON.

● INDICATES FOUND MONUMENT OR LOCATION OF MONUMENT SET, AS NOTED.

■ INDICATES NOTHING TO BE SET.

▲ INDICATES FOUND ORANGE COUNTY SURVEYOR GPS CONTROL MONUMENT AS NOTED.

P/E INDICATES BEARING AND DISTANCE OF LOT LINE PRODUCTION FROM LOT CORNER TO MONUMENT.

1 INDICATES LOCATION OF 2" IP, TAGGED "P.L.S. 5557" OR SPIKE & WASHER STAMPED "P.L.S. 5557" OR LEAD, TACK & TAG "P.L.S. 5557" TO BE SET PER TRACT NO. 15986, M.M. 849/1-15.

2 INDICATES LOCATION OF 1" IP, TAGGED "P.L.S. 5557" OR SPIKE & WASHER STAMPED "P.L.S. 5557" OR LEAD, TACK & TAG "P.L.S. 5557" TO BE SET PER TRACT NO. 15986, M.M. 849/1-15.

3 INDICATES LOCATION OF 2" IP, TAGGED L.S. 6654 OR LEAD & TAG L.S. 6654 OR AN 8" S. & W. STAMPED L.S. 6654 OR NAIL & TAG L.S. 6654, TO BE SET PER TRACT NO. 16667, M.M. 864/15-20.

4 ○ INDICATES SET 2" IP, TAGGED L.S. 6654 PRIOR TO MAP RECORDATION.

EASEMENT NOTES:

- (A) INDICATES AN EASEMENT FOR WATER, RECYCLED WATER, SEWER AND ACCESS PURPOSES DEDICATED HEREON TO THE SANTA MARGARITA WATER DISTRICT
- (B) INDICATES AN EASEMENT FOR INGRESS AND EGRESS OF EMERGENCY AND PUBLIC SERVICE VEHICLES DEDICATED HEREON TO THE COUNTY OF ORANGE.

NOTES:

LOTS A, B, C, D, L, M AND N ARE FOR OPEN SPACE/LANDSCAPE PURPOSES AND ARE NOT SEPARATE BUILDING SITES.
LOTS K AND L ARE FOR POCKET PARK PURPOSES.
LOTS E, F, G AND H ARE FOR PRIVATE STREET PURPOSES.

GPS NO. 1448
FD. 2" IRON PIPE WITH 1 3/4" OCS BRASS CAP
STAMPED "1448 9-95" PER R.S.B. 154/8-18 AND
RECORDS ON FILE IN THE ORANGE COUNTY
SURVEYOR'S OFFICE
N 2146790.819 E 6142802.565

GPS NO. 1417
FD. 2 1/2" IRON PIPE WITH 2" OCS BRASS CAP
STAMPED "GPS 1417 9-95" PER R.S.B. 154/8-18
AND RECORDS ON FILE IN THE ORANGE COUNTY
SURVEYOR'S OFFICE
N 2141450.558 E 6141583.535

PORTION OF PARCEL I

LLA LL 96-026

INST. NO. 1996058744, O.R.

861-37

861-38

SHEET 3 OF 6 SHEETS
SCALE: 1" = 40'
37 NUMBERED LOTS AND
LOTS A THROUGH N, INCLUSIVE
ACREAGE: 17.499 ACRES
(FINAL UNIT OF VESTING
TENTATIVE TRACT NO. 16395)

TRACT NO. 16395


IN UNINCORPORATED TERRITORY OF THE COUNTY OF ORANGE,
STATE OF CALIFORNIA

HUNSAKER AND ASSOCIATES IRVINE, INC.
RORY S. WILLIAMS, L.S. 8654 DATE OF SURVEY: JULY, 2002

SEE SHEET 2 FOR BASIS OF BEARINGS, DATUM STATEMENT,
MONUMENT NOTES, SHEET INDEX AND GPS CONTROL MAP,
EASEMENT NOTES AND NOTES.


TRACT NO. 16395

PORTION OF PCL. 1
L.L.A. LL 96-026
INST. NO. 10960587414, O.R.

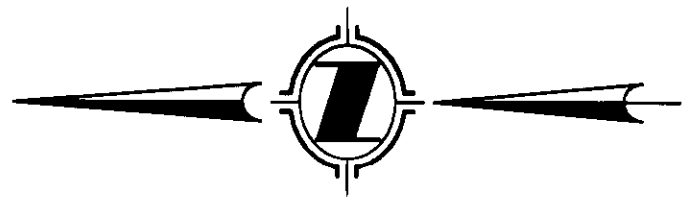

MONUMENT OFFSET TABLE		
LINE	BEARING	LENGTH
P1	S00°19'20"W	10.75'
P2	S00°19'20"W	16.79'
P3	S03°10'51"W	10.81'
P4	S38°45'40"W	10.75'
P5	S72°58'03"W	10.75'
P6	N38°09'47"W	11.23'
P7	N10°07'35"E	11.38'
P8	N00°16'26"W	14.01'
P9	N02°30'13"W	10.75'

LINE TABLE		
LINE	BEARING	LENGTH
L1	N09°09'56"E	17.26'
L2	N00°59'32"W	24.00'
L3	N11°00'01"W	17.26'

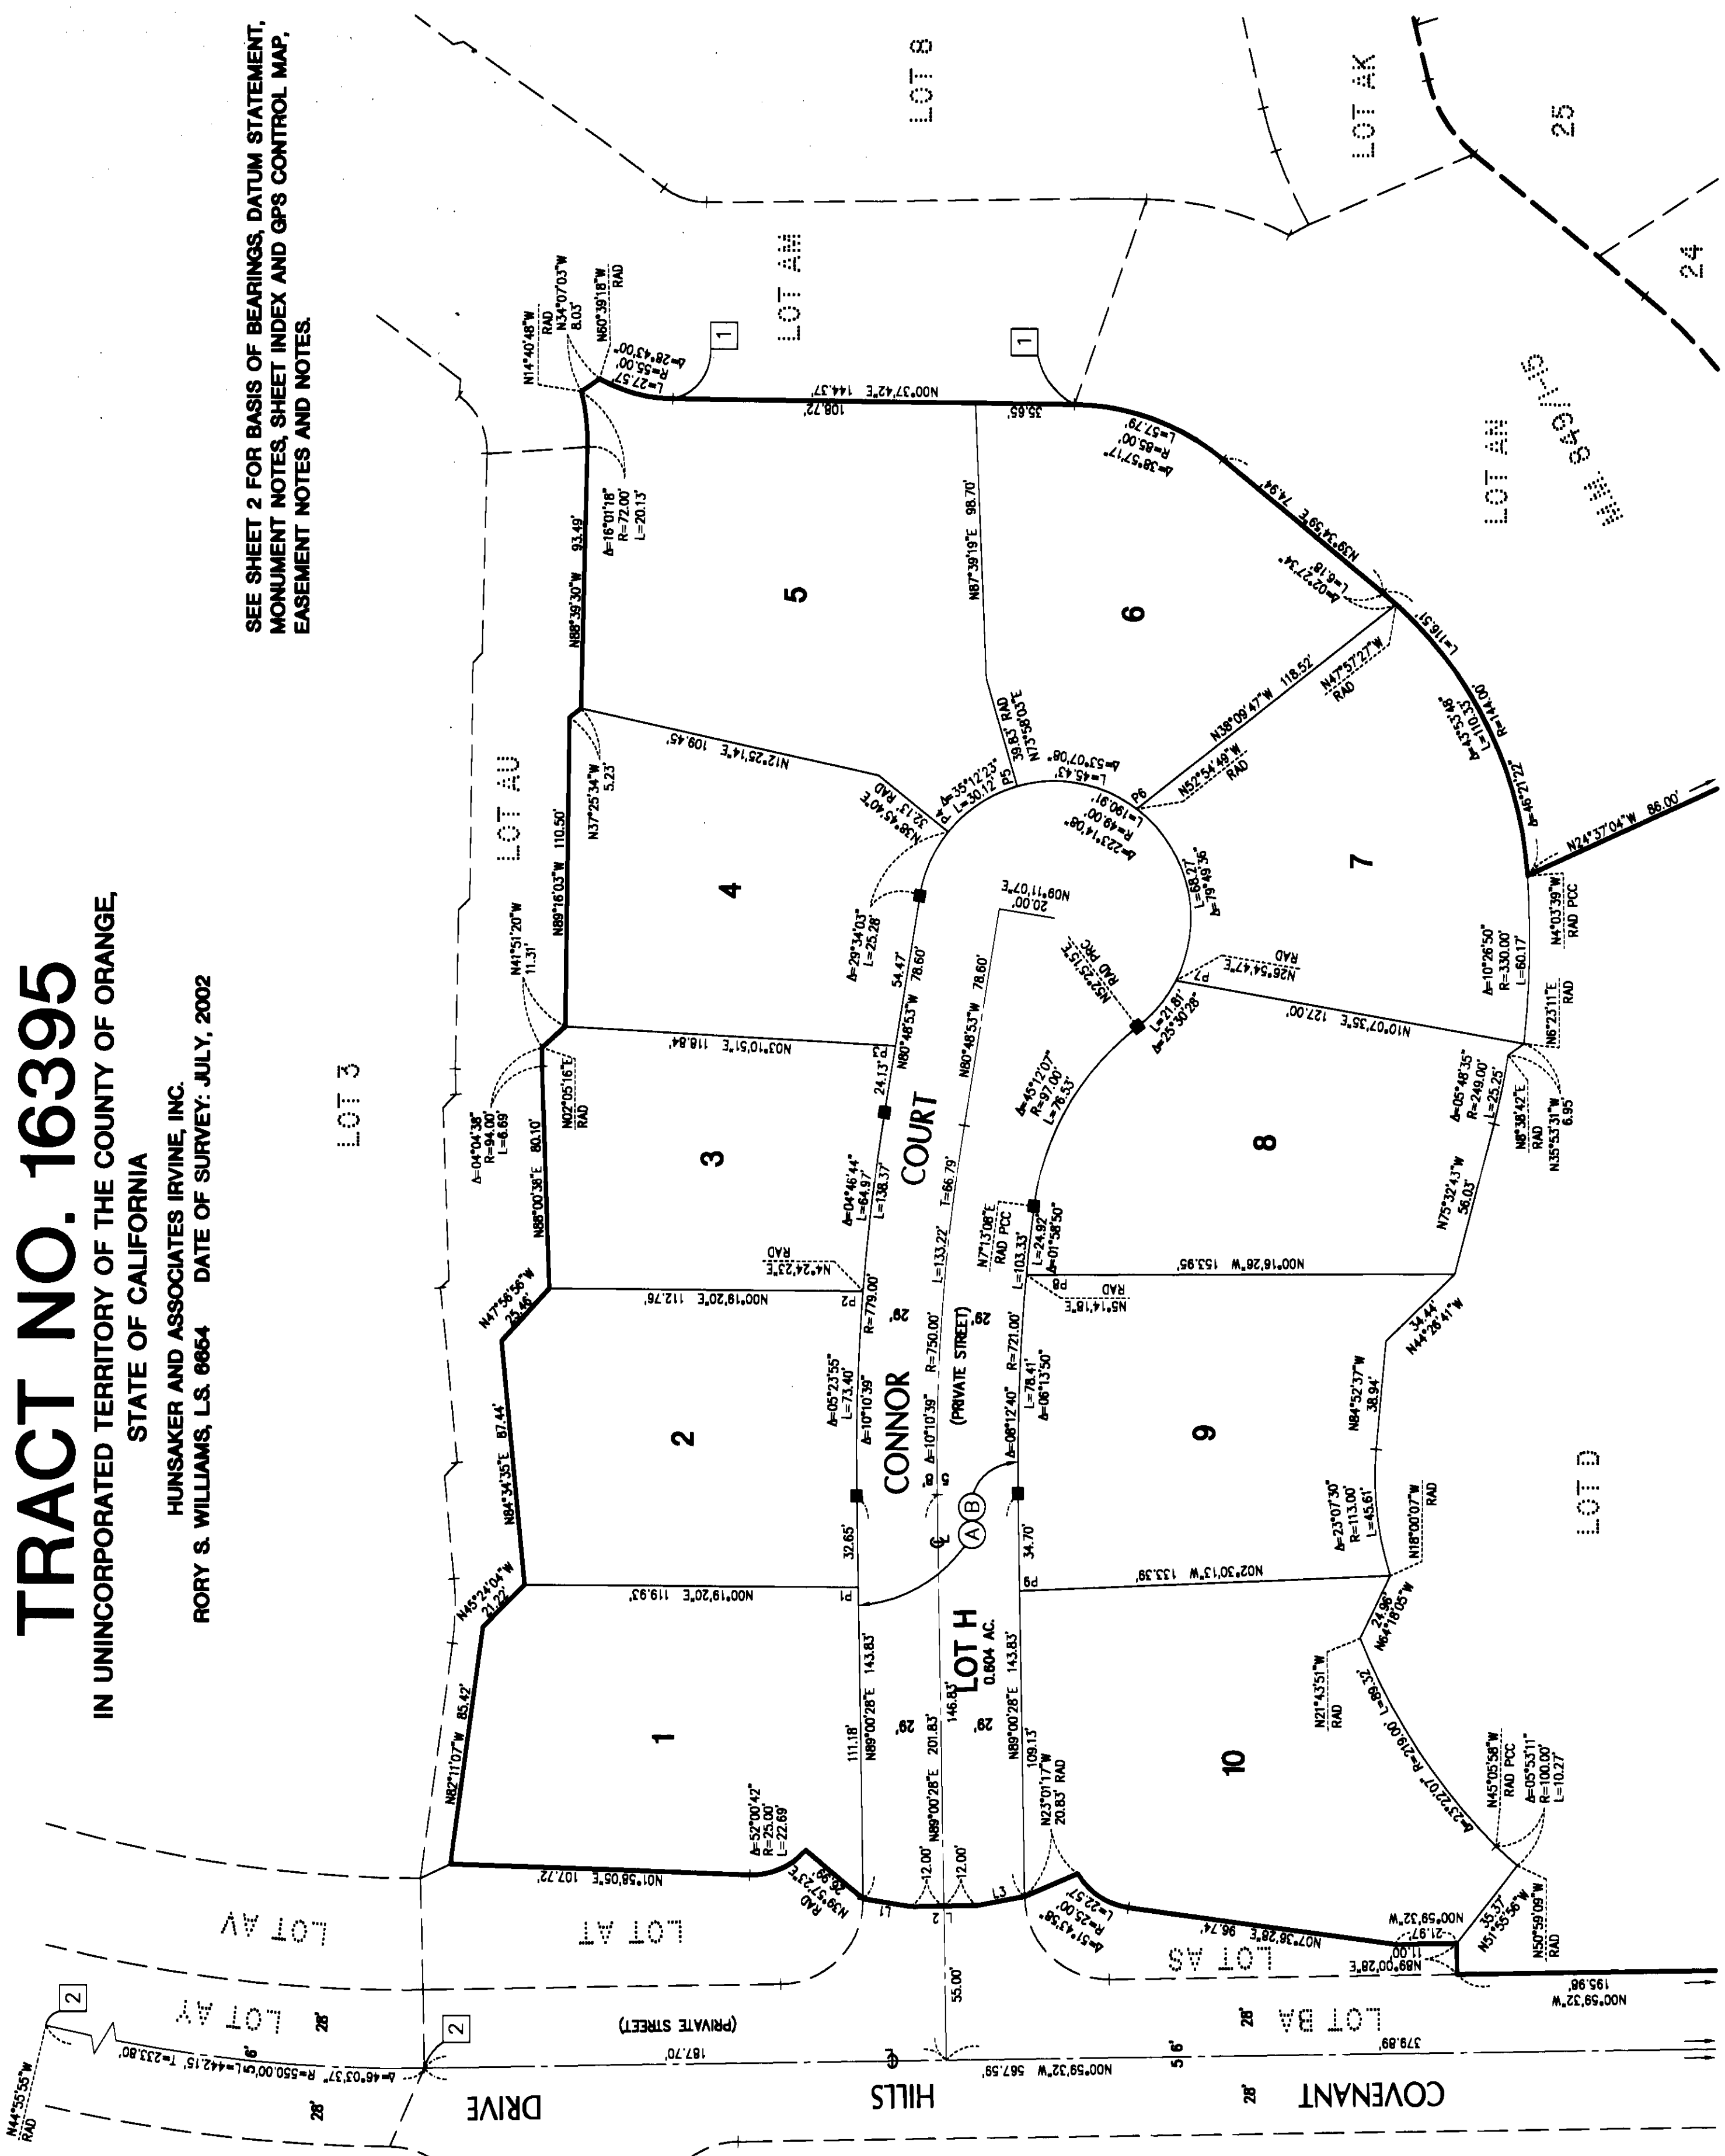


861-38

SHEET 4 OF 6 SHEETS
SCALE: T = 40'
37 NUMBERED LOTS AND
LOTS A THROUGH N, INCLUSIVE
ACREAGE: 17.499 ACRES
(FINAL UNIT OF VESTING
TENTATIVE TRACT NO. 16395)

TRACT NO. 16395

IN UNINCORPORATED TERRITORY OF THE COUNTY OF ORANGE,
STATE OF CALIFORNIA

HUNSAKER AND ASSOCIATES IRVINE, INC.
RORY S. WILLIAMS, L.S. 0654 DATE OF SURVEY: JULY, 2002

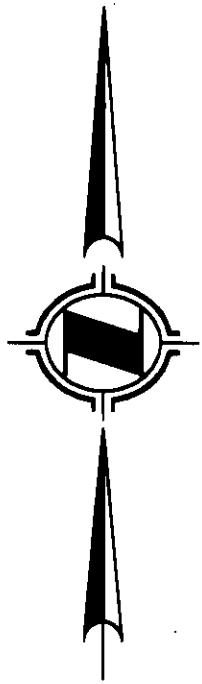

SEE SHEET 3

TRACT NO. 15986

LOT AN
M.M. 849/1-15

KELLY LANE
(PRIVATE STREET)

LOT F

LOT Z

LOT J
DETAIL 'A'
N.T.S.

MONUMENT OFFSET TABLE		
LINE	BEARING	LENGTH
P10	S01°58'43"W	10.56'
P11	S48°37'28"E	12.16'
P12	N80°28'18"E	12.06'
P13	N80°28'18"E	10.78'
P14	N88°43'30"E	10.82'
P15	N45°47'28"E	10.75'
P16	N28°16'48"E	11.01'
P17	N13°25'07"E	10.75'
P31	S52°58'18"E	10.75'
P32	S35°41'05"E	10.78'

CURVE TABLE			
CURVE	DELTA	RADIUS	LENGTH
C3	100°15'18"	20.00'	35.00'
C4	24°28'32"	59.00'	25.17'
C5	25°21'50"	49.00'	21.89'
C8	25°23'55"	72.00'	31.92'
C7	18°27'12"	40.00'	12.88'
C8	33°12'11"	49.00'	28.40'

LINE TABLE		
LINE	BEARING	LENGTH
L8	N35°36'45"W	17.44'
L9	N69°04'25"W	46.46'
L10	N68°21'07"W	2.57'

SEE SHEET 2 FOR BASIS OF BEARINGS, DATUM STATEMENT,
MONUMENT NOTES, SHEET INDEX AND GPS CONTROL MAP,
EASEMENT NOTES AND NOTES.

PORTION OF PCL. 1

L.L.A. LL 96-026

INST. NO. 19960587414, O.R.

SEE SHEET 5

861-38

861 40

SHEET 5 OF 6 SHEETS
SCALE: 1" = 40'
37 NUMBERED LOTS AND
LOTS A THROUGH N, INCLUSIVE
ACREAGE: 17,499 ACRES
(FINAL UNIT OF VESTING
TENTATIVE TRACT NO. 16395)

TRACT NO. 16395

IN UNINCORPORATED TERRITORY OF THE COUNTY OF ORANGE,
STATE OF CALIFORNIA


HUNSAKER AND ASSOCIATES IRVINE, INC.
RORY S. WILLIAMS, L.S. 6854 DATE OF SURVEY: JULY, 2002

SEE SHEET 2 FOR BASIS OF BEARINGS,
DATUM STATEMENT, MONUMENT NOTES,
SHEET INDEX AND GPS CONTROL MAP,
EASEMENT NOTES AND NOTES.

MONUMENT OFFSET TABLE		
LINE	BEARING	LENGTH
P17	N13°25'07"E	10.75'
P18	N02°24'35"W	10.75'
P19	N17°40'17"W	10.75'
P20	N36°55'10"W	16.75'
P21	N33°06'47"W	10.77'
P26	S35°06'55"E	17.18'
P27	S32°39'45"E	10.75'
P28	S32°39'45"E	10.78'
P29	S32°39'45"E	16.77'
P30	S32°39'45"E	11.32'
P31	S52°59'18"E	10.75'
P32	S35°41'05"E	10.78'
P33	S33°15'22"E	10.86'
P34	S33°15'22"E	16.75'
P35	S33°15'22"E	12.72'
P36	S17°15'25"E	10.78'
P37	S33°10'34"W	10.78'

LINE TABLE		
LINE	BEARING	LENGTH
L4	N70°34'19"E	17.52'
L5	N58°32'18"E	24.00'
L6	N42°30'17"E	17.52'
L7	N17°41'58"E	19.28'
L9	N69°04'25"W	46.48'

CURVE TABLE			
CURVE	DELTA	RADIUS	LENGTH
C1	94°55'48"	25.00'	41.42'
C2	4°50'42"	25.00'	2.11'
C3	31°44'02"	49.00'	27.14'
C4	7°14'28"	190.00'	24.01'

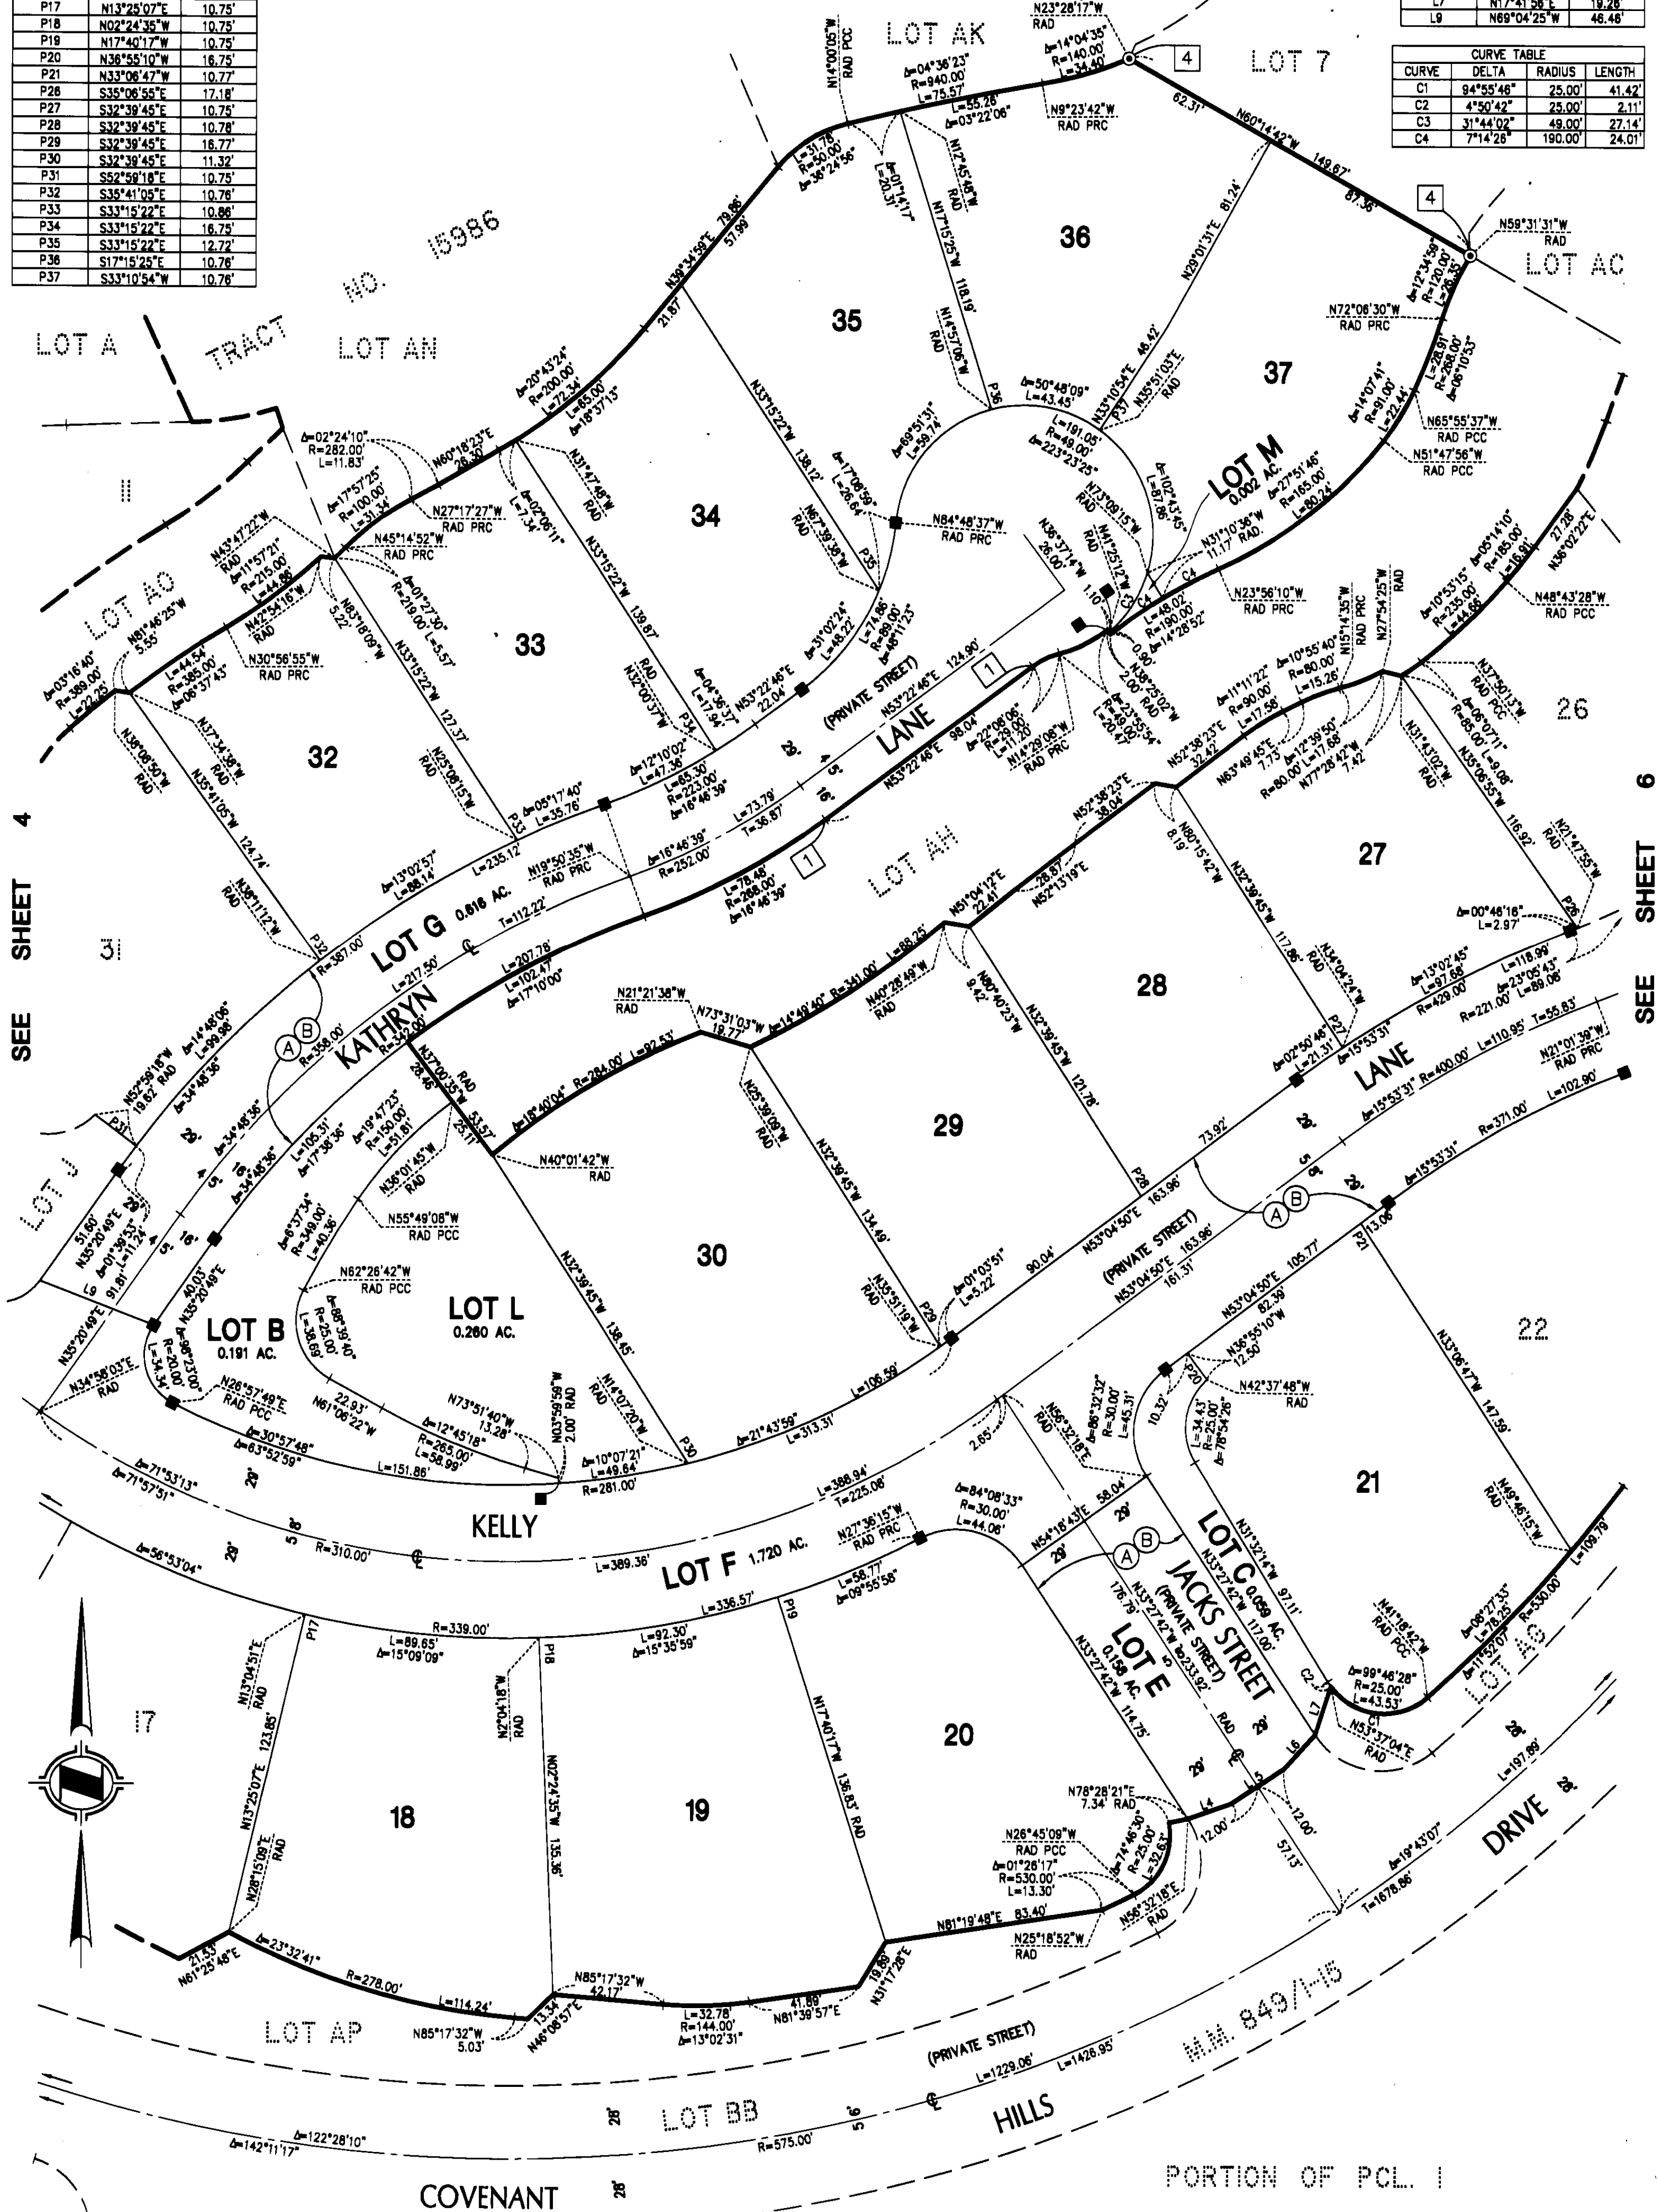

PORTION OF PCL. I
LLA LL 96-026
INST. NO. 19960587414, O.R.

861 40


861-41

SHEET 6 OF 6 SHEETS
SCALE: 1" = 40'
37 NUMBERED LOTS AND
LOTS A THROUGH N, INCLUSIVE
ACREAGE: 17.499 ACRES
(FINAL UNIT OF VESTING
TENTATIVE TRACT NO. 16395)

TRACT NO. 16395

IN UNINCORPORATED TERRITORY OF THE COUNTY OF ORANGE,
STATE OF CALIFORNIA

HUNSAKER AND ASSOCIATES IRVINE, INC.
RORY S. WILLIAMS, L.S. 6654 DATE OF SURVEY: JULY, 2002

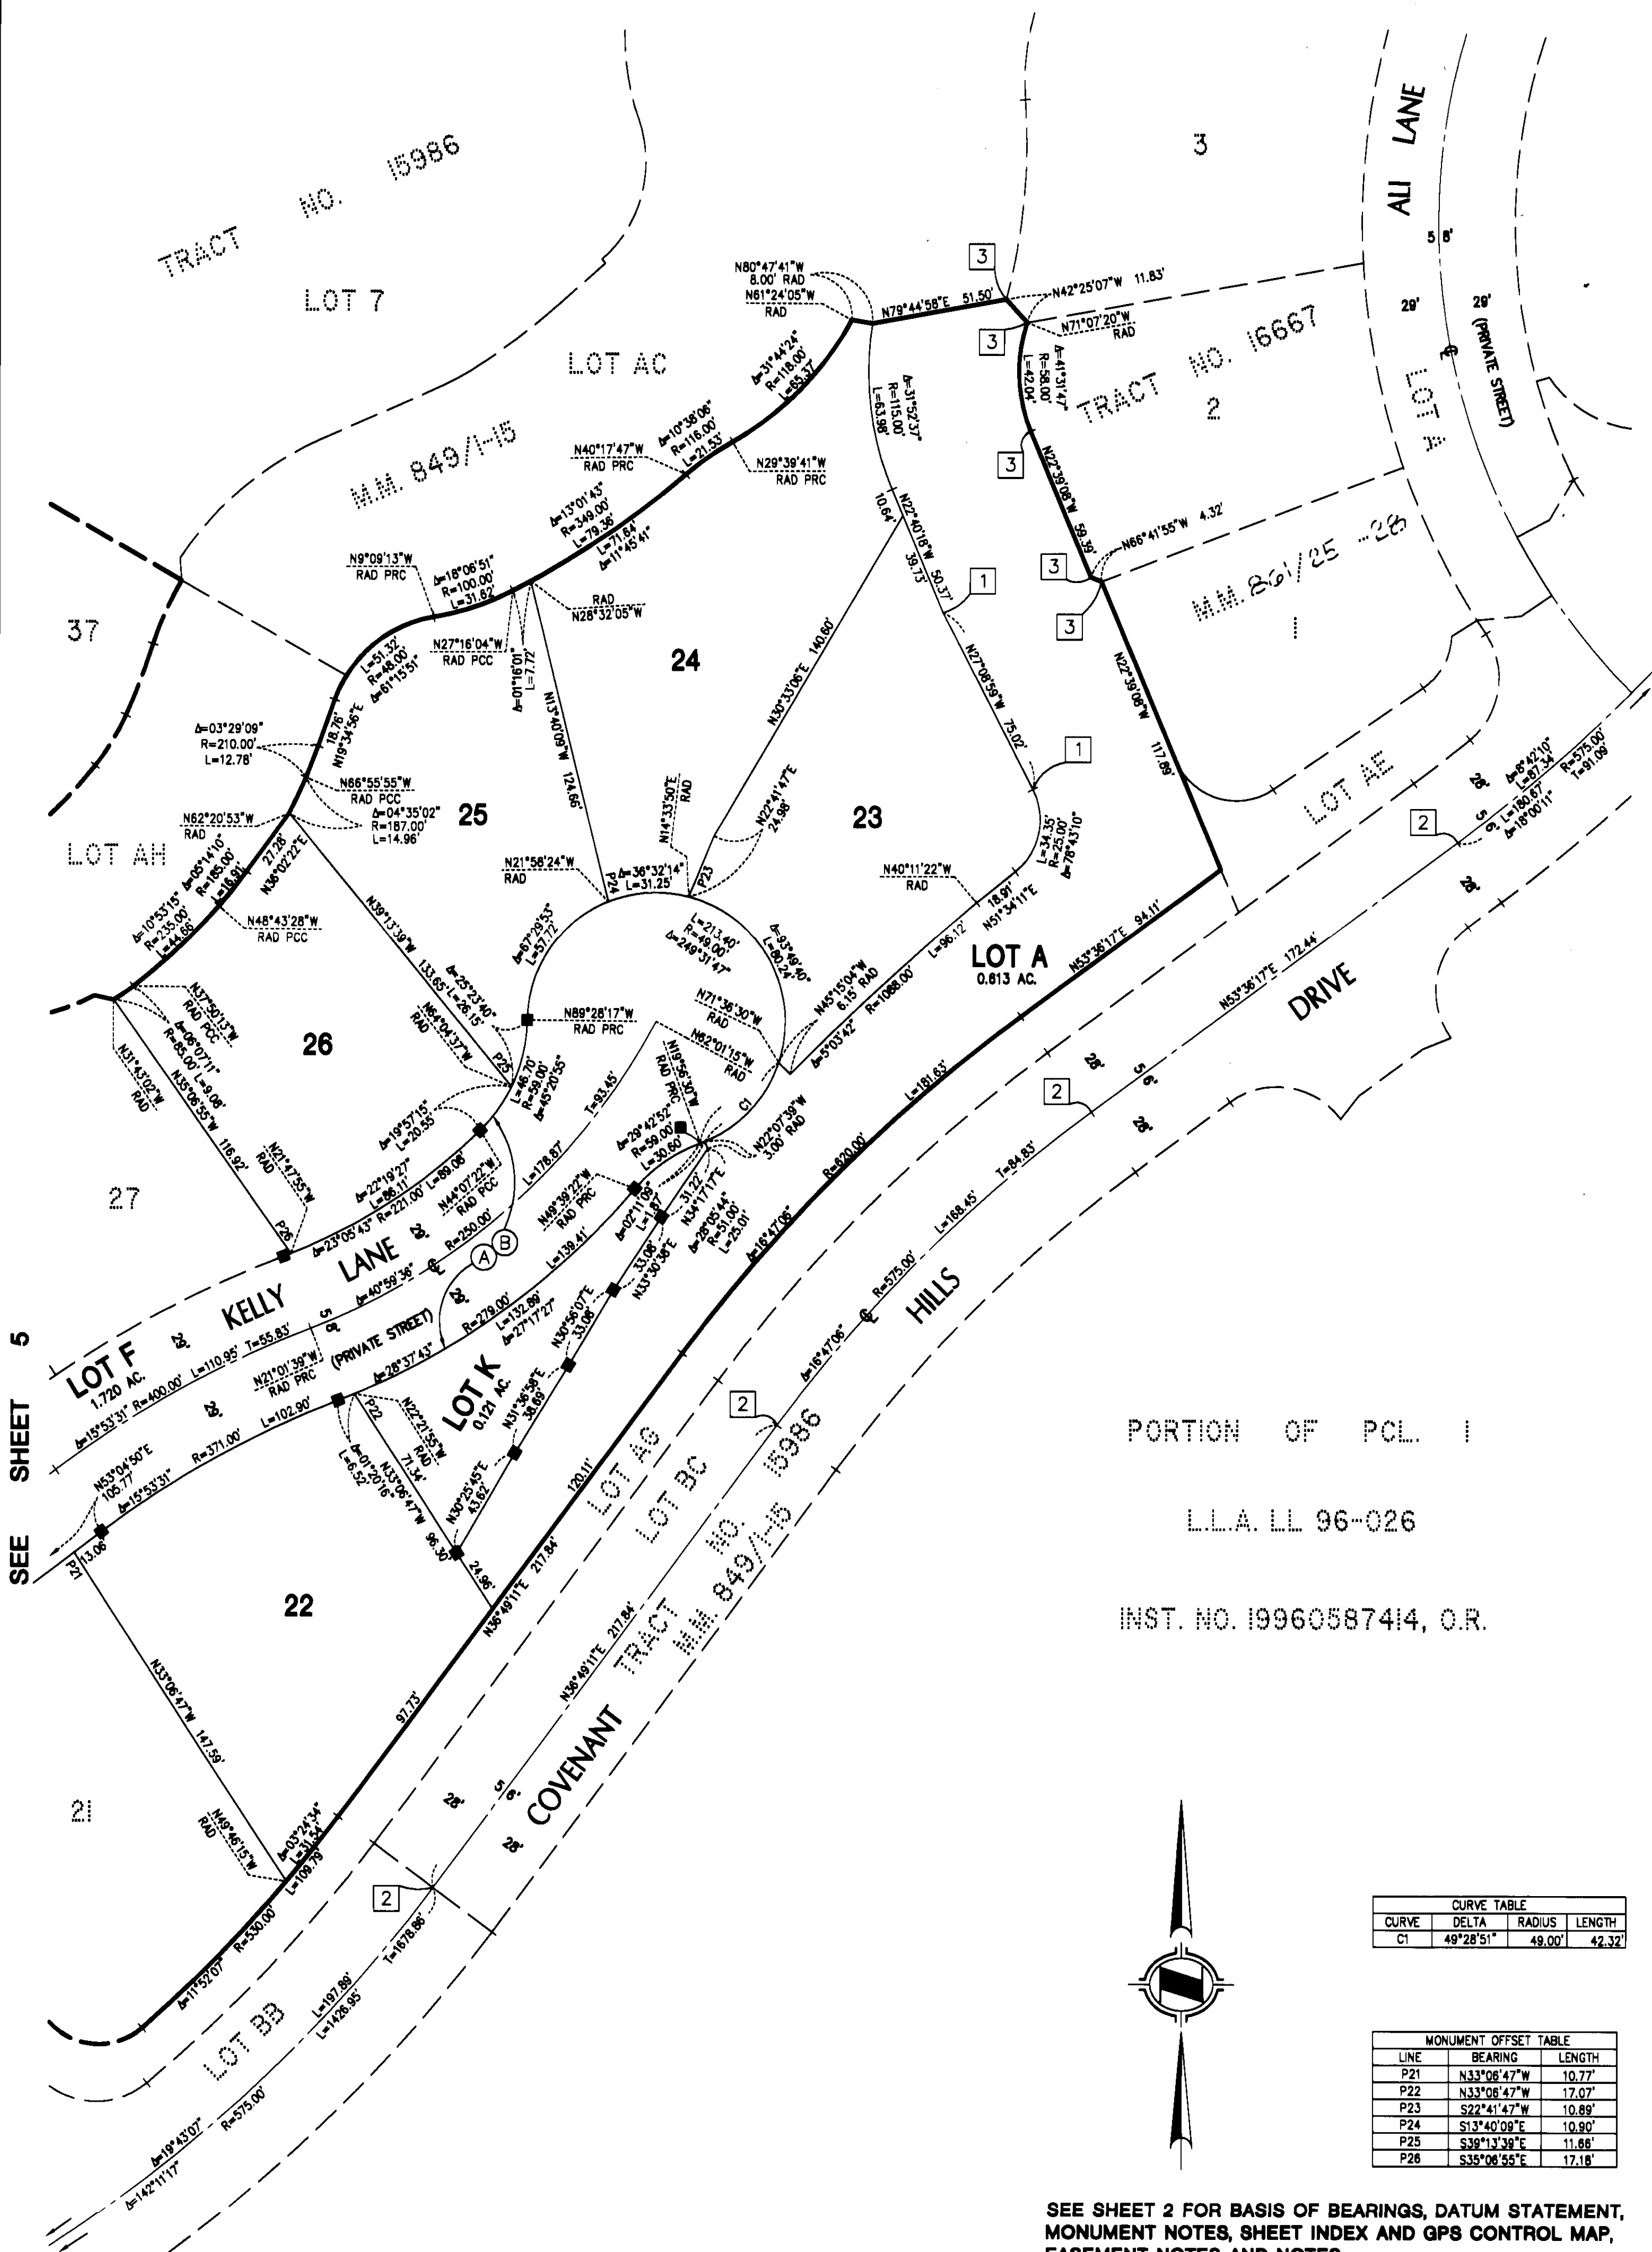

PORTION OF PCL. 1

L.L.A. LL 96-026

INST. NO. 19960587414, O.R.

CURVE TABLE			
CURVE	DELTA	RADIUS	LENGTH
C1	49°28'51"	49.00'	42.32'

MONUMENT OFFSET TABLE		
LINE	BEARING	LENGTH
P21	N33°06'47"W	10.77'
P22	N33°06'47"W	17.07'
P23	S22°41'47"W	10.89'
P24	S13°40'08"E	10.80'
P25	S39°13'38"E	11.68'
P26	S35°06'55"E	17.18'

SEE SHEET 2 FOR BASIS OF BEARINGS, DATUM STATEMENT,
MONUMENT NOTES, SHEET INDEX AND GPS CONTROL MAP,
EASEMENT NOTES AND NOTES.

861-41