

SHEET 1 OF 5 SHEETS
24 NUMBERED LOTS
5 LETTERED LOTS
6.474 ACRES
FINAL UNIT OF VESTING
T.T.M. 16400
DATE OF SURVEY:
JANUARY, 1999

TRACT MAP NO. 16400

IN THE UNINCORPORATED TERRITORY OF THE COUNTY OF ORANGE,
STATE OF CALIFORNIA

BEING A SUBDIVISION OF LOT 3 OF TRACT NO. 15986, IN THE UNINCORPORATED
TERRITORY OF THE COUNTY OF ORANGE, CALIFORNIA AS SHOWN IN BOOK 849,
PAGES 1 THROUGH 15, INCLUSIVE, OF MISCELLANEOUS MAPS IN THE OFFICE OF
THE COUNTY RECORDER OF SAID COUNTY.

HALL & FOREMAN, INC.

STEVEN C. SHAMBECK, P.L.S. 6217
OCTOBER, 2003

ACCEPTED AND FILED AT THE
REQUEST OF

FIDELITY NATIONAL TITLE COMPANY
DATE July 6, 2004
TIME 9:45 AM FEES 19.00

INSTRUMENT # 2004000609148
BOOK 859 PAGE 28-32/111

TOM DALY
COUNTY CLERK-RECORDER

Samuel J. Demetri
DEPUTY

OWNERSHIP CERTIFICATE

WE, THE UNDERSIGNED, BEING ALL PARTIES HAVING ANY RECORD TITLE INTEREST
IN THE LAND COVERED BY THIS MAP, DO HEREBY CONSENT TO THE PREPARATION
AND RECORDATION OF SAID MAP, AS SHOWN WITHIN THE DISTINCTIVE BORDER
LINE.

WE HEREBY DEDICATE TO THE COUNTY OF ORANGE:

1. THE EASEMENT FOR EMERGENCY ACCESS PURPOSES OVER ALL OF LOTS BA AND
BB AS SHOWN ON SAID MAP.

WE ALSO HEREBY DEDICATE TO THE SANTA MARGARITA WATER DISTRICT THE EASEMENTS FOR
WATER, SEWER, AND ACCESS PURPOSES OVER THOSE EASEMENT AREAS AS SHOWN ON SAID
MAP WHICH EASEMENTS SHALL BE SUBJECT TO THE SAME CONDITIONS AS ARE SHOWN IN THAT
CERTAIN GRANT OF EASEMENT TO SANTA MARGARITA WATER DISTRICT RECORDED SEPTEMBER
18, 2002 AS INSTRUMENT NO. 20020799401, OF OFFICIAL RECORDS, COUNTY OF ORANGE.

COVENANT HILLS P30B, LLC, A DELAWARE LIMITED LIABILITY COMPANY

BY: WILLIAM LYON HOMES, INC. A CALIFORNIA CORPORATION,
ITS MANAGING MEMBER

BY: Thomas J. Mitchell BY: Thomas G. Grable
PRINT NAME: THOMAS J. MITCHELL PRINT NAME: THOMAS G. GRABLE
PRINT TITLE: SENIOR VICE PRESIDENT PRINT TITLE: ASSISTANT SECRETARY

NOTARY ACKNOWLEDGEMENT

STATE OF CALIFORNIA)
COUNTY OF ORANGE)SS

ON January 14, 2007 BEFORE ME, SUSAN E MENARD

PERSONALLY APPEARED THOMAS J. MITCHELL and THOMAS G. GRABLE
PERSONALLY KNOWN TO ME (OR PROVED TO ME ON THE BASIS OF SATISFACTORY
EVIDENCE) TO BE THE PERSON(S) WHOSE NAME(S) IS/ARE SUBSCRIBED TO THE
WITHIN INSTRUMENT AND ACKNOWLEDGED TO ME THAT HE/SHE/ THEY EXECUTED
THE SAME IN HIS/HER/ THEIR AUTHORIZED CAPACITY(IES), AND THAT BY HIS/
HER/ THEIR SIGNATURE(S) ON THE INSTRUMENT THE PERSON(S), OR THE ENTITY UPON
BEHALF OF WHICH THE PERSON(S) ACTED, EXECUTED THE INSTRUMENT.

WITNESS MY HAND:

Susan E Menard
NOTARY PUBLIC IN AND FOR SAID STATE

Susan E Menard
PRINT NAME

MY PRINCIPAL PLACE OF BUSINESS IS IN ORANGE COUNTY
MY COMMISSION EXPIRES October 26, 2007

DMB LADERA, LLC, A DELAWARE LIMITED LIABILITY COMPANY BENEFICIARY UNDER DEED
OF TRUST RECORDED OCTOBER 8, 2003 AS INSTRUMENT NO. 2003001238184 OF
OFFICIAL RECORDS. OPTIONEER DOCUMENT RECORDED OCTOBER
31, 2003 AS INSTRUMENT NO. 2003001238185 OF OFFICIAL
RECORDS.

BY: RANCHO MISSION VIEJO, L.L.C. A DELAWARE LIMITED LIABILITY COMPANY,
AS ITS AUTHORIZED AGENT AND MANAGER

BY: Donald T. Stahlin BY: Gregory S. Edwards
PRINT NAME: DONALD T. STAHLIN PRINT NAME: GREGORY S. EDWARDS
PRINT TITLE: V.P. PRINT TITLE: C.F.O.

NOTARY ACKNOWLEDGEMENT

STATE OF California)
COUNTY OF Orange)SS

ON January 30, 2004 BEFORE ME, Diana L. Binks

PERSONALLY APPEARED Donald T. Stahlin and Gregory S. Edwards
PERSONALLY KNOWN TO ME (OR PROVED TO ME ON THE BASIS OF SATISFACTORY
EVIDENCE) TO BE THE PERSON(S) WHOSE NAME(S) IS/ARE SUBSCRIBED TO THE
WITHIN INSTRUMENT AND ACKNOWLEDGED TO ME THAT HE/SHE/ THEY EXECUTED
THE SAME IN HIS/HER/ THEIR AUTHORIZED CAPACITY(IES), AND THAT BY HIS/
HER/ THEIR SIGNATURE(S) ON THE INSTRUMENT THE PERSON(S), OR THE ENTITY UPON
BEHALF OF WHICH THE PERSON(S) ACTED, EXECUTED THE INSTRUMENT.

WITNESS MY HAND:

Diana L. Binks
NOTARY PUBLIC IN AND FOR SAID STATE

Diana L. Binks
PRINT NAME

MY PRINCIPAL PLACE OF BUSINESS IS IN Orange COUNTY
MY COMMISSION EXPIRES 12/12/06

SEE SHEET 2 FOR WATER DISTRICT ACCEPTANCE AND SIGNATURE OMISSIONS

SURVEYOR'S STATEMENT

THIS MAP WAS PREPARED BY ME OR UNDER MY DIRECTION AND IS BASED UPON A
FIELD SURVEY IN CONFORMANCE WITH THE REQUIREMENTS OF THE SUBDIVISION MAP
ACT AND LOCAL ORDINANCE AT THE REQUEST OF DMB LADERA, LLC IN JANUARY,
1999. I HEREBY STATE THAT ALL MONUMENTS ARE OF THE CHARACTER AND
OCCUPY THE POSITIONS INDICATED, OR THAT THEY WILL BE SET IN SUCH
POSITIONS; AND THAT SAID MONUMENTS ARE SUFFICIENT TO ENABLE THE SURVEY
TO BE RETRACED. I HEREBY STATE THAT THIS FINAL MAP SUBSTANTIALLY
CONFORMS TO THE CONDITIONALLY APPROVED TENTATIVE MAP.

St C. Shambeck
STEVEN C. SHAMBECK, P.L.S. 6217
LICENSE EXPIRES: 3/31/06

1-12-04
DATE



COUNTY SURVEYOR'S STATEMENT

I HEREBY STATE THAT I HAVE EXAMINED THIS MAP AND HAVE FOUND IT TO BE
SUBSTANTIALLY IN CONFORMANCE WITH THE TENTATIVE MAP AS FILED WITH,
AMENDED AND APPROVED BY THE ORANGE COUNTY SUBDIVISION COMMITTEE; THAT
ALL PROVISIONS OF THE SUBDIVISION MAP ACT AND COUNTY SUBDIVISION
REGULATIONS HAVE BEEN COMPLIED WITH AND I AM SATISFIED SAID MAP IS
TECHNICALLY CORRECT.

DATED THIS 17th DAY OF JUNE, 2004.

Michael K. Sullivan
RAYMOND L. MATHE, COUNTY SURVEYOR
L.S. 6185 EXPIRATION DATE: 3/31/06

BY: MICHAEL K. SULLIVAN, DEPUTY
LS 6254 EXPIRES 6/30/06



CLERK OF THE BOARD OF SUPERVISOR'S CERTIFICATE

STATE OF CALIFORNIA)
COUNTY OF ORANGE)SS


I HEREBY CERTIFY THAT THIS MAP WAS PRESENTED FOR APPROVAL TO THE
BOARD OF SUPERVISORS OF ORANGE COUNTY AT A REGULAR MEETING THEREOF
HELD ON THE 29th DAY OF June, 2004 AND THAT
THEREUPON SAID BOARD DID, BY AN ORDER DULY PASSED AND ENTERED,
APPROVE SAID MAP.

AND DID ACCEPT ON BEHALF OF THE COUNTY OF ORANGE:

1. THE EASEMENT FOR EMERGENCY ACCESS PURPOSES OVER ALL OF LOTS BA
AND BB AS DEDICATED.

DATED THIS 29th DAY OF June, 2004.

Darlene J. Bloom
DARLENE J. BLOOM
CLERK OF THE BOARD OF SUPERVISORS

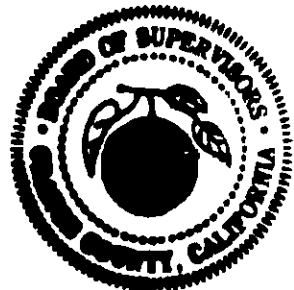

COUNTY TREASURER-TAX COLLECTOR'S CERTIFICATE

STATE OF CALIFORNIA)
COUNTY OF ORANGE)SS

I HEREBY CERTIFY THAT ACCORDING TO THE RECORDS OF MY OFFICE
THERE ARE NO LIENS AGAINST THE LAND COVERED BY THIS MAP OR
ANY PART THEREOF FOR UNPAID STATE, COUNTY, MUNICIPAL OR LOCAL
TAXES OR SPECIAL ASSESSMENTS COLLECTED AS TAXES, EXCEPT TAXES
OR SPECIAL ASSESSMENTS COLLECTED AS TAXES NOT YET PAYABLE.

AND DO ALSO CERTIFY TO THE RECORDER OF THE COUNTY OF ORANGE
THAT THE PROVISIONS OF THE SUBDIVISION MAP ACT HAVE BEEN COMPLIED
WITH REGARDING DEPOSITS TO SECURE PAYMENT OF TAXES OR SPECIAL
ASSESSMENTS COLLECTED AS TAXES ON THE LAND COVERED BY THIS MAP.

DATED THIS 6th DAY OF May, 2004.

JOHN M.W. MOORLACH
COUNTY TREASURER-TAX COLLECTOR

BY: Maes prinsen
DEPUTY TREASURER -
TAX COLLECTOR

SHEET 2 OF 5 SHEETS
24 NUMBERED LOTS
5 LETTERED LOTS
6.474 ACRES
FINAL UNIT OF VESTING
T.T.M. 16400
DATE OF SURVEY:
JANUARY, 1999

TRACT MAP NO. 16400

IN THE UNINCORPORATED TERRITORY OF THE COUNTY OF ORANGE,
STATE OF CALIFORNIA

HALL & FOREMAN, INC.

STEVEN C. SHAMBECK, P.L.S. 6217
OCTOBER, 2003

CERTIFICATE OF ACCEPTANCE

THE UNDERSIGNED, BEING THE DULY APPOINTED AGENT OF THE SANTA MARGARITA WATER DISTRICT, A PUBLIC CORPORATION OF ORANGE COUNTY, CALIFORNIA, PURSUANT TO ITS RESOLUTION NO. 88-10-02, DOES HEREBY ACCEPT ON BEHALF OF SAID DISTRICT THE EASEMENTS FOR, WATER, SEWER, AND ACCESS PURPOSES, AS DEDICATED AND AS SHOWN ON THIS TRACT MAP, BY AND BETWEEN THE SANTA MARGARITA WATER DISTRICT AND COVENANT HILLS P30B, LLC, AND DOES HEREBY CERTIFY THAT THE GRANTEE CONSENTS TO THE RECORDATION OF SAID TRACT.



DANIEL R. FERONS, CHIEF ENGINEER
SANTA MARGARITA WATER DISTRICT

SANTA MARGARITA WATER DISTRICT

STATE OF CALIFORNIA)
COUNTY OF ORANGE) SS

ON THIS 5th DAY OF FEB 2004, BEFORE ME, CINDY R. LANE
A NOTARY PUBLIC IN AND FOR SAID STATE, PERSONALLY APPEARED DANIEL R. FERONS PERSONALLY KNOWN TO ME OR ~~PROVED TO ME ON THE BASIS OF SATISFACTORY EVIDENCE~~ TO BE THE PERSON WHOSE NAME IS SUBSCRIBED TO THE WITHIN INSTRUMENT AND ACKNOWLEDGED TO ME THAT HE EXECUTED THE SAME IN HIS AUTHORIZED CAPACITY, AND THAT BY HIS SIGNATURE ON THE INSTRUMENT THE PERSON OR THE ENTITY UPON BEHALF OF WHICH THE PERSON ACTED, EXECUTED THE INSTRUMENT.

WITNESS MY HAND:

MY COMMISSION EXPIRES 2-20-05



NOTARY PUBLIC IN AND FOR SAID STATE IS IN ORANGE COUNTY

CINDY R. LANE
PRINT NAME

AUTOMATIC FIRE SPRINKLER NOTE:
ALL SINGLE FAMILY STRUCTURES EXCEEDING 5,500 SQUARE FEET, AND ALL STRUCTURES EXCEEDING FIRE DEPARTMENT ACCESS REQUIREMENTS SHALL BE PROTECTED BY AN AUTOMATIC SPRINKLER SYSTEM.

SPECIAL FIRE PROTECTION NOTE:
PROPERTY IS IN A SPECIAL FIRE PROTECTION AREA AND MUST MEET ALL REQUIREMENTS FOR DEVELOPMENT WITHIN THE AREA.

HIGH FIRE HAZARD AREA NOTE:
THE LOTS SHOWN ON THIS MAP ARE IN A HIGH FIRE HAZARD AREA DUE TO WILD LAND EXPOSURE.

NOTE:

THE PRIVATE STREETS CONSTRUCTED WITHIN THIS MAP SHALL BE OWNED, OPERATED AND MAINTAINED BY THE DEVELOPER, SUCCESSORS OR ASSIGNS. THE COUNTY OF ORANGE SHALL HAVE NO RESPONSIBILITY THEREFORE UNLESS PURSUANT TO APPROPRIATE SECTIONS OF THE STREETS AND HIGHWAYS CODE OF THE STATE OF CALIFORNIA, THE SAID PRIVATE STREETS HAVE BEEN ACCEPTED INTO THE COUNTY ROAD SYSTEM BY APPROPRIATE RESOLUTION OF THE ORANGE COUNTY BOARD OF SUPERVISORS.

SIGNATURE OMISSIONS

PURSUANT TO THE PROVISIONS OF SECTION 66436 (d)(3)(C) OF THE SUBDIVISION MAP ACT, THE FOLLOWING SIGNATURES HAVE BEEN OMITTED:

DMB LADERA, L.L.C., A DELAWARE LIMITED LIABILITY COMPANY, HOLDER OF OIL, GAS, AND MINERAL RIGHTS PER DEED RECORDED DECEMBER 10, 1996 AS INSTRUMENT NO. 19960624029 OF OFFICIAL RECORDS.

DMB LADERA, L.L.C., A DELAWARE LIMITED LIABILITY COMPANY, HOLDER OF EASEMENTS FOR CONSTRUCTION FACILITIES, TELECOMMUNICATION FACILITIES, PUBLIC UTILITIES, SURFACE RUNOFF, PRIVATE AND PUBLIC STREETS, ROADS, TRAILS, WALKWAYS, AND IRRIGATION PURPOSES PER DOCUMENT RECORDED OCTOBER 8, 2003 AS INSTRUMENT NO. 2003001238183 OF OFFICIAL RECORDS. (UNPLOTTABLE)

EASEMENT NOTES

 INDICATES WATER, SEWER AND ACCESS EASEMENT DEDICATED TO SANTA MARGARITA WATER DISTRICT.

BASIS OF BEARINGS

THE BEARINGS SHOWN HEREON ARE BASED ON THE BEARING BETWEEN O.C.S. HORIZONTAL CONTROL STATION GPS NO. 1417 AND STATION GPS NO. 1448, BEING NORTH 10°48'13" EAST PER RECORDS ON FILE IN THE OFFICE OF THE ORANGE COUNTY SURVEYOR.

DATUM STATEMENT

COORDINATES SHOWN ARE BASED ON THE CALIFORNIA COORDINATE SYSTEM (CCS 83), ZONE VI, 1983 NAD (1991.35 EPOCH OCS GPS ADJUSTMENT). ALL DISTANCES ARE GROUND DISTANCES UNLESS OTHERWISE NOTED. TO OBTAIN GRID DISTANCE MULTIPLY GROUND DISTANCE BY 0.999948295. THIS FACTOR IS PROJECT-SPECIFIC.

MONUMENT NOTES

● INDICATES FOUND MONUMENT AS NOTED.

 INDICATES FOUND 2 1/2" IRON PIPE W/2" OCS BRASS CAP STAMPED "GPS 1448 9-95" PER TRACT NO. 16203, M.M. 826/B-20 AND RECORD ON FILE IN THE ORANGE COUNTY SURVEYORS OFFICE. N2146790.819, E6142602.585

 INDICATES FOUND 2 1/2" IRON PIPE W/2" OCS BRASS CAP STAMPED "GPS 1417 9-95" PER TRACT NO. 16203, M.M. 826/B-20 AND RECORD ON FILE IN THE ORANGE COUNTY SURVEYORS OFFICE. N2141450.558, E6141583.535

 INDICATES 2" I.P. TAGGED P.L.S. 5557 OR SPIKE & WASHER STAMPED P.L.S. 5557 OR LEAD, TACK & TAG P.L.S. 5557 TO BE SET PER TRACT NO. 15986 M.M. 849/1-15, UNLESS OTHERWISE NOTED.

 INDICATES 1" I.P. TAGGED P.L.S. 5557 OR SPIKE & WASHER STAMPED P.L.S. 5557 OR LEAD, TACK & TAG P.L.S. 5557 TO BE SET PER TRACT NO. 15986 M.M. 849/1-15, UNLESS OTHERWISE NOTED.

2" I.P. TAGGED L.S. 6217 OR SPIKE & WASHER STAMPED L.S. 6217 OR LEAD, TACK & TAG L.S. 6217 TO BE SET AT ALL TRACT BOUNDARY CORNERS WITHIN 90 DAYS AFTER ACCEPTANCE OF IMPROVEMENTS.

1" I.P. TAGGED L.S. 6217 OR SPIKE & WASHER STAMPED L.S. 6217 OR LEAD, TACK & TAG L.S. 6217 TO BE SET AT LOT CORNERS WITHIN 90 DAYS AFTER ACCEPTANCE OF IMPROVEMENTS.

1" I.P. TAGGED L.S. 6217 OR SPIKE & WASHER STAMPED L.S. 6217 OR LEAD, TACK & TAG L.S. 6217 TO BE SET AT ALL CENTERLINE INTERSECTIONS, E.C.'S AND B.C.'S WITHIN 90 DAYS AFTER ACCEPTANCE OF IMPROVEMENTS.

NOTES

LOTS BA AND BB ARE FOR PRIVATE STREET PURPOSES AND ARE NOT SEPARATE BUILDING SITES.

LOTS A THROUGH C ARE FOR LANDSCAPE/OPEN SPACE PURPOSES AND ARE NOT SEPARATE RESIDENTIAL BUILDING SITES.

() INDICATES MEASURED AND RECORD PER TRACT NO. 15986 M.M. 849/1-15

 INDICATES 2" I.P. TAGGED L.S. 6217 OR SPIKE & WASHER STAMPED L.S. 6217 OR LEAD, TACK & TAG L.S. 6217 TO BE SET PRIOR TO MAP RECORDATION.

SHEET 3 OF 5 SHEETS
24 NUMBERED LOTS
5 LETTERED LOTS
6.474 ACRES
FINAL UNIT OF VESTING
T.T.M. 16400
DATE OF SURVEY:
JANUARY, 1999

TRACT MAP NO. 16400


IN THE UNINCORPORATED TERRITORY OF THE COUNTY OF ORANGE,
STATE OF CALIFORNIA

HALL & FOREMAN, INC.

STEVEN C. SHAMBECK, P.L.S. 6217
OCTOBER, 2003

BOUNDARY AND INDEX SHEET

SEE SHEET 2 FOR BASIS OF
BEARINGS, DATUM STATEMENT,
MONUMENT NOTES, EASEMENT
NOTES AND NOTES

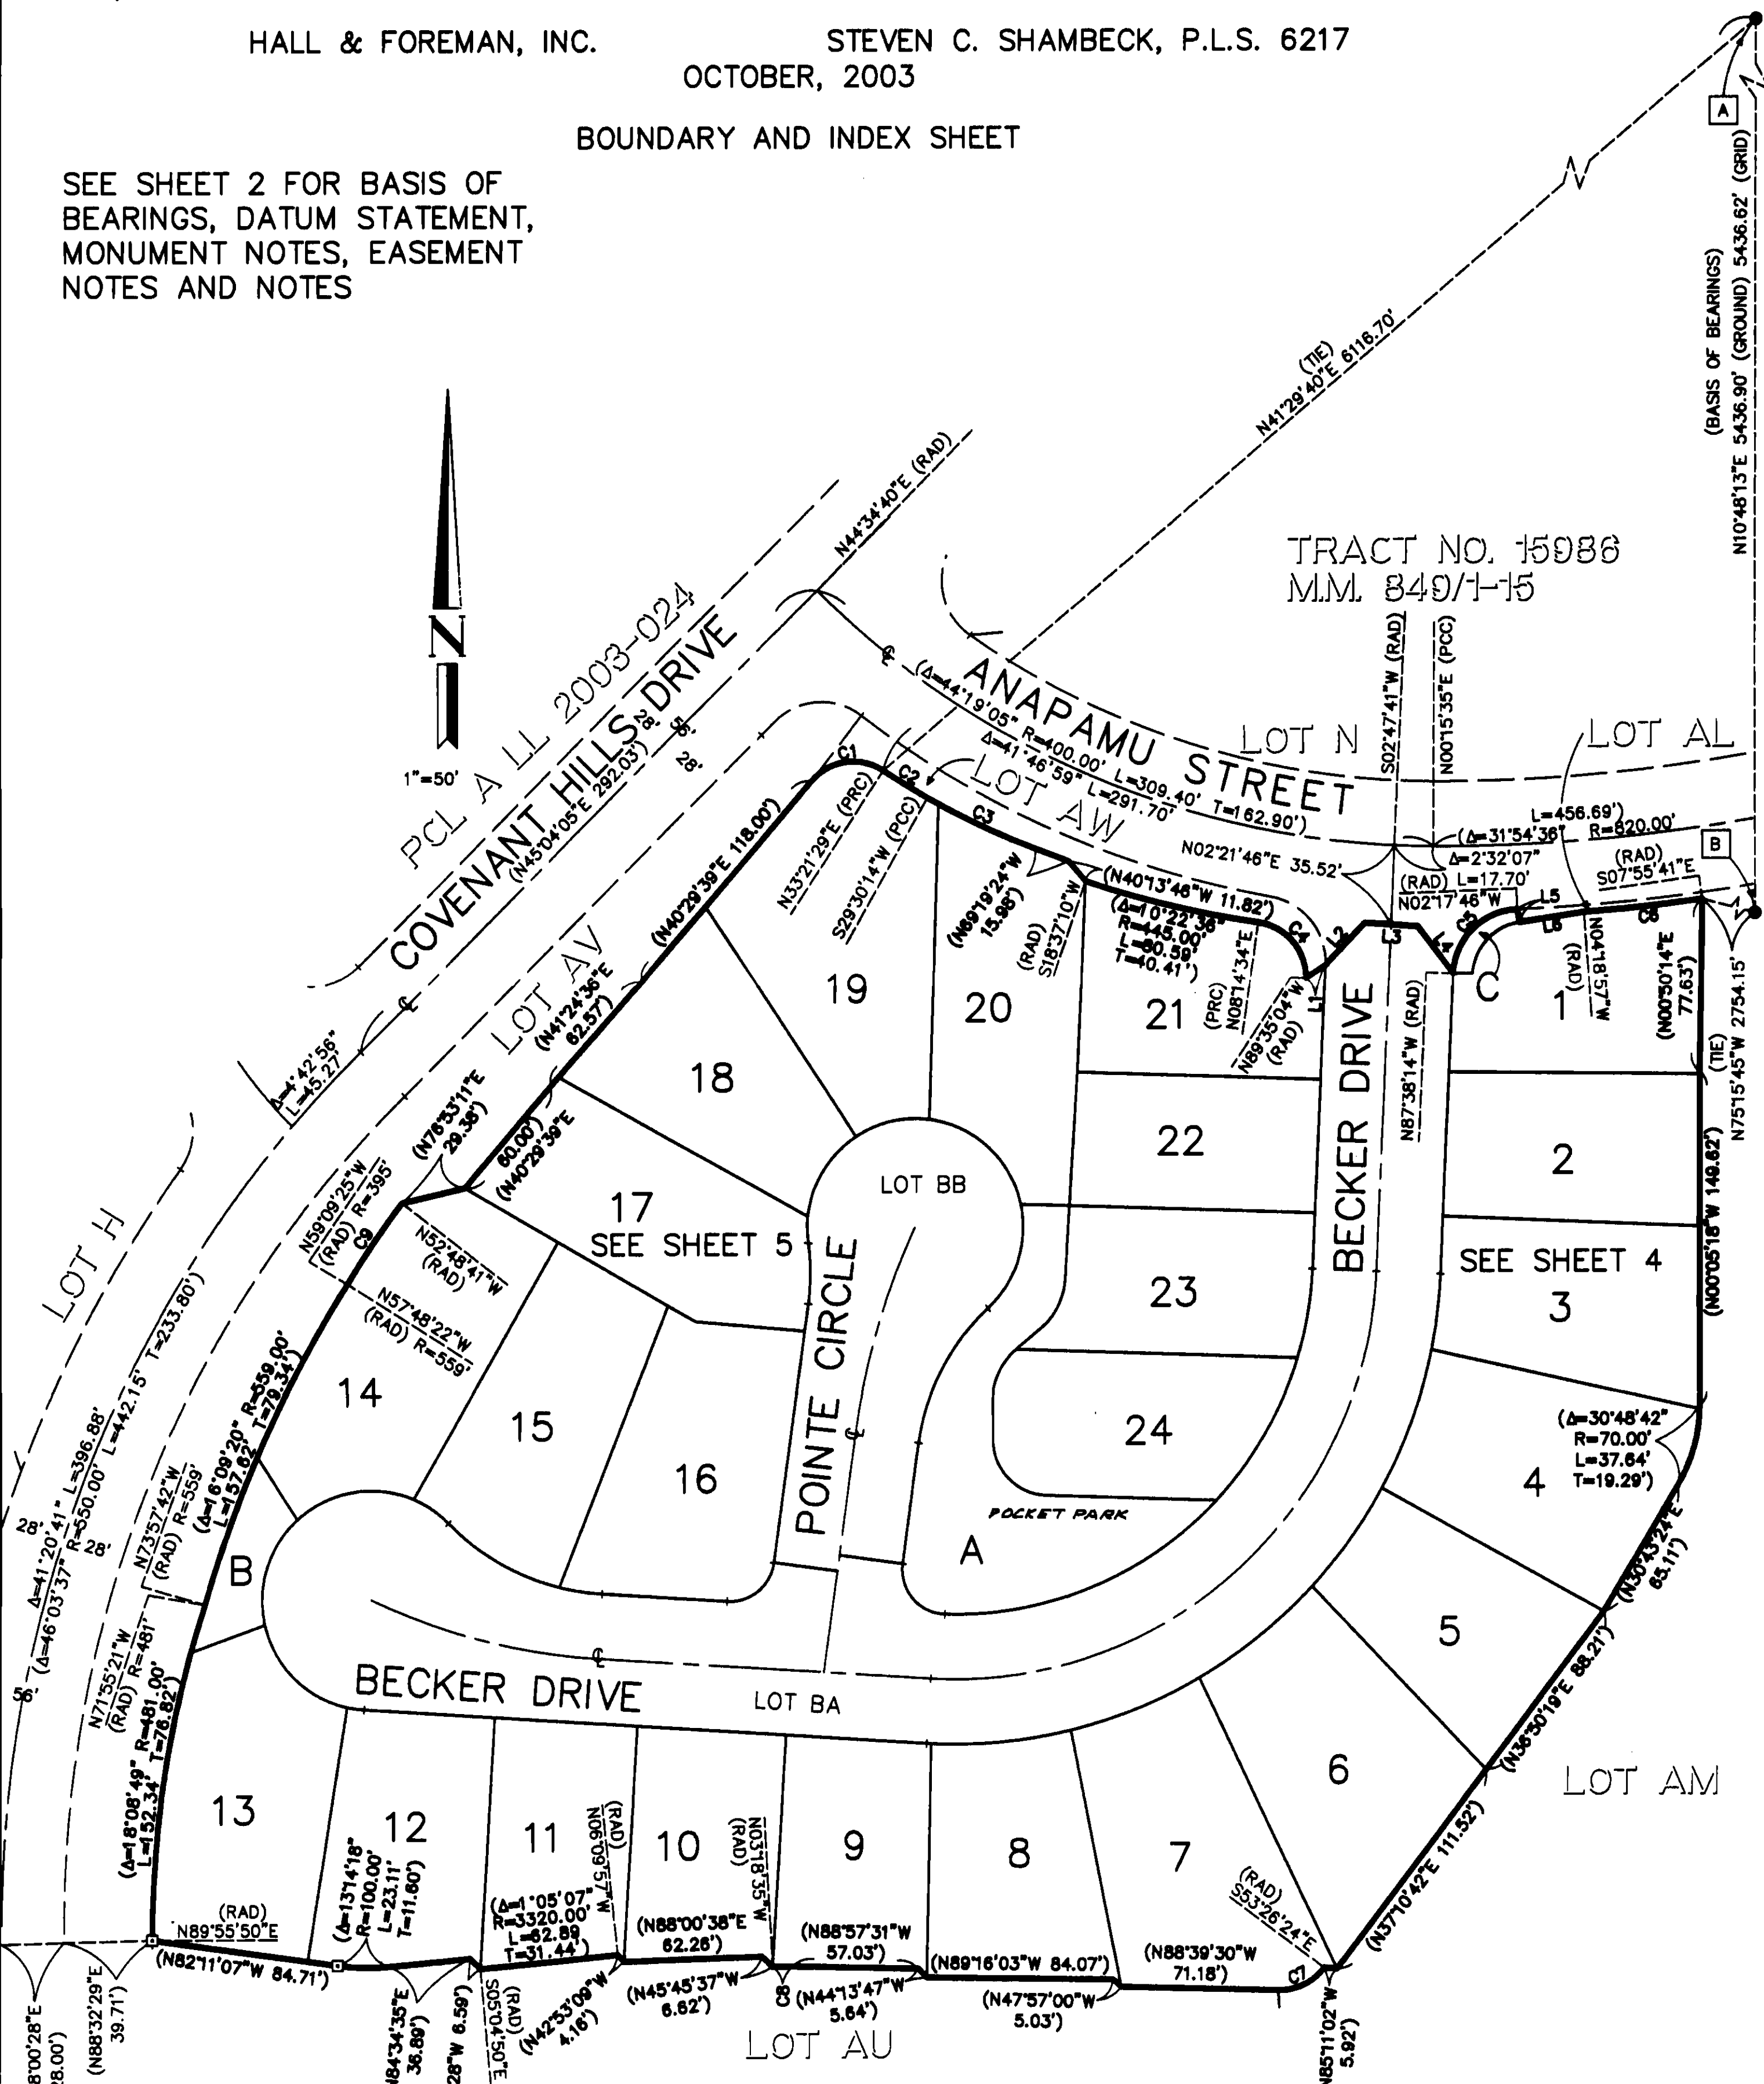

CURVE DATA				
CURVE	DELTA	RADIUS	LENGTH	TANGENT
C1	(82°51'50")	25.00	36.16	22.07
C2	(3°51'15")	349.00	23.48	11.74
C3	(8°49'38")	349.00	53.77	26.94
C4	(82°10'22")	25.00	35.85	21.80
C5	(85°20'28")	30.00	44.68	27.65
C6	(3°36'44")	852.00	53.71	26.87
C7	(54°46'54")	25.00	23.90	12.95
C8	(4°21'04")	120.00	9.11	4.56
C9	(6°20'44")	395.00	43.75	21.90

LINE DATA		
LINE	BEARING	LENGTH
L1	(N57°05'19"E)	10.52
L2	(N43°15'37"E)	25.97
L3	(N85°58'51"W)	24.01
L4	(N37°16'37"W)	26.65
L5	(N10°57'14"W)	5.85
L6	(N81°12'44"E)	29.33

TRACT NO. 15986
M.M. 849/1-15

(BASIS OF BEARINGS)
N10°48'13"E 5436.90' (GROUND) 5436.62' (GRID)

859

30

SHEET 4 OF 5 SHEETS
24 NUMBERED LOTS
5 LETTERED LOTS
6.474 ACRES
FINAL UNIT OF VESTING
T.T.M. 16400
DATE OF SURVEY:
JANUARY, 1999

TRACT MAP NO. 16400

IN THE UNINCORPORATED TERRITORY OF THE COUNTY OF ORANGE,
STATE OF CALIFORNIA


HALL & FOREMAN, INC.

STEVEN C. SHAMBECK, P.L.S. 6217

OCTOBER, 2003

SEE SHEET 2 FOR BASIS OF
BEARINGS, DATUM STATEMENT,
MONUMENT NOTES, EASEMENT
NOTES AND NOTES

TRACT NO. 15086
M.M. 840/1-15

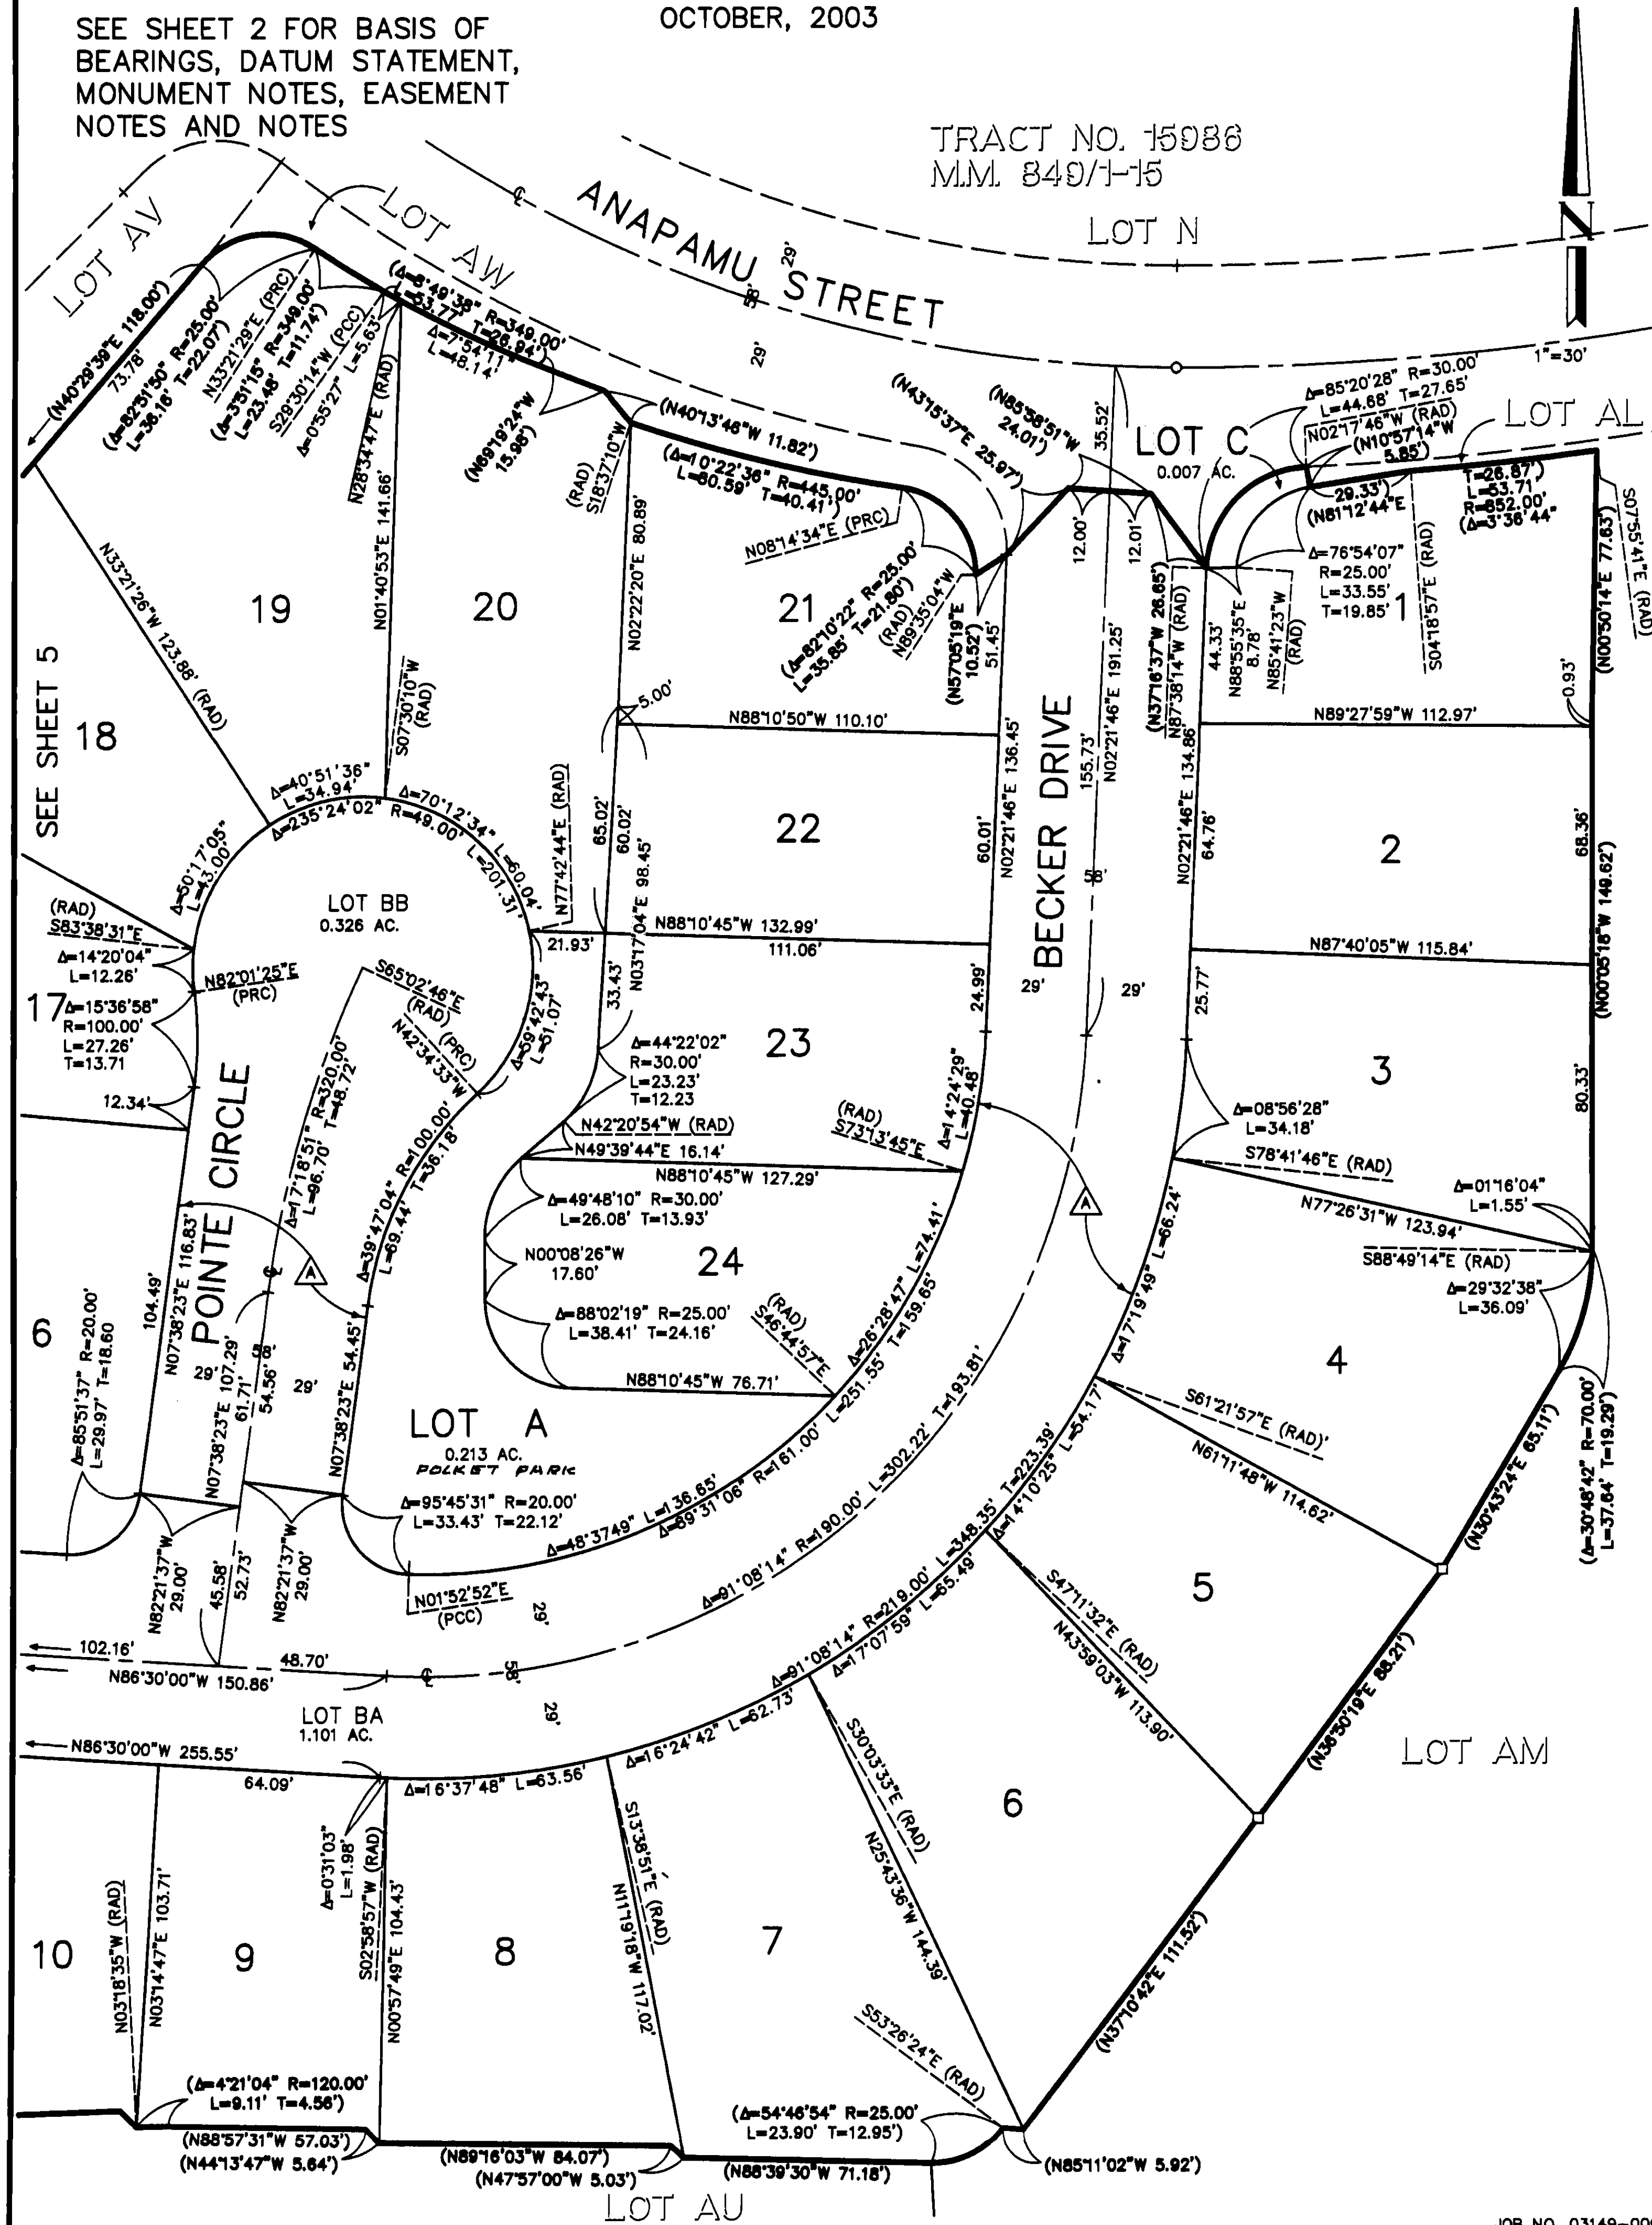

SHEET 5 OF 5 SHEETS
24 NUMBERED LOTS
5 LETTERED LOTS
6.474 ACRES
FINAL UNIT OF VESTING
T.T.M. 16400
DATE OF SURVEY:
JANUARY, 1999


TRACT MAP NO. 16400

IN THE UNINCORPORATED TERRITORY OF THE COUNTY OF ORANGE,
STATE OF CALIFORNIA

HALL & FOREMAN, INC.

STEVEN C. SHAMBECK, P.L.S. 6217
OCTOBER, 2003

SEE SHEET 2 FOR BASIS OF
BEARINGS, DATUM STATEMENT,
MONUMENT NOTES, EASEMENT
NOTES AND NOTES

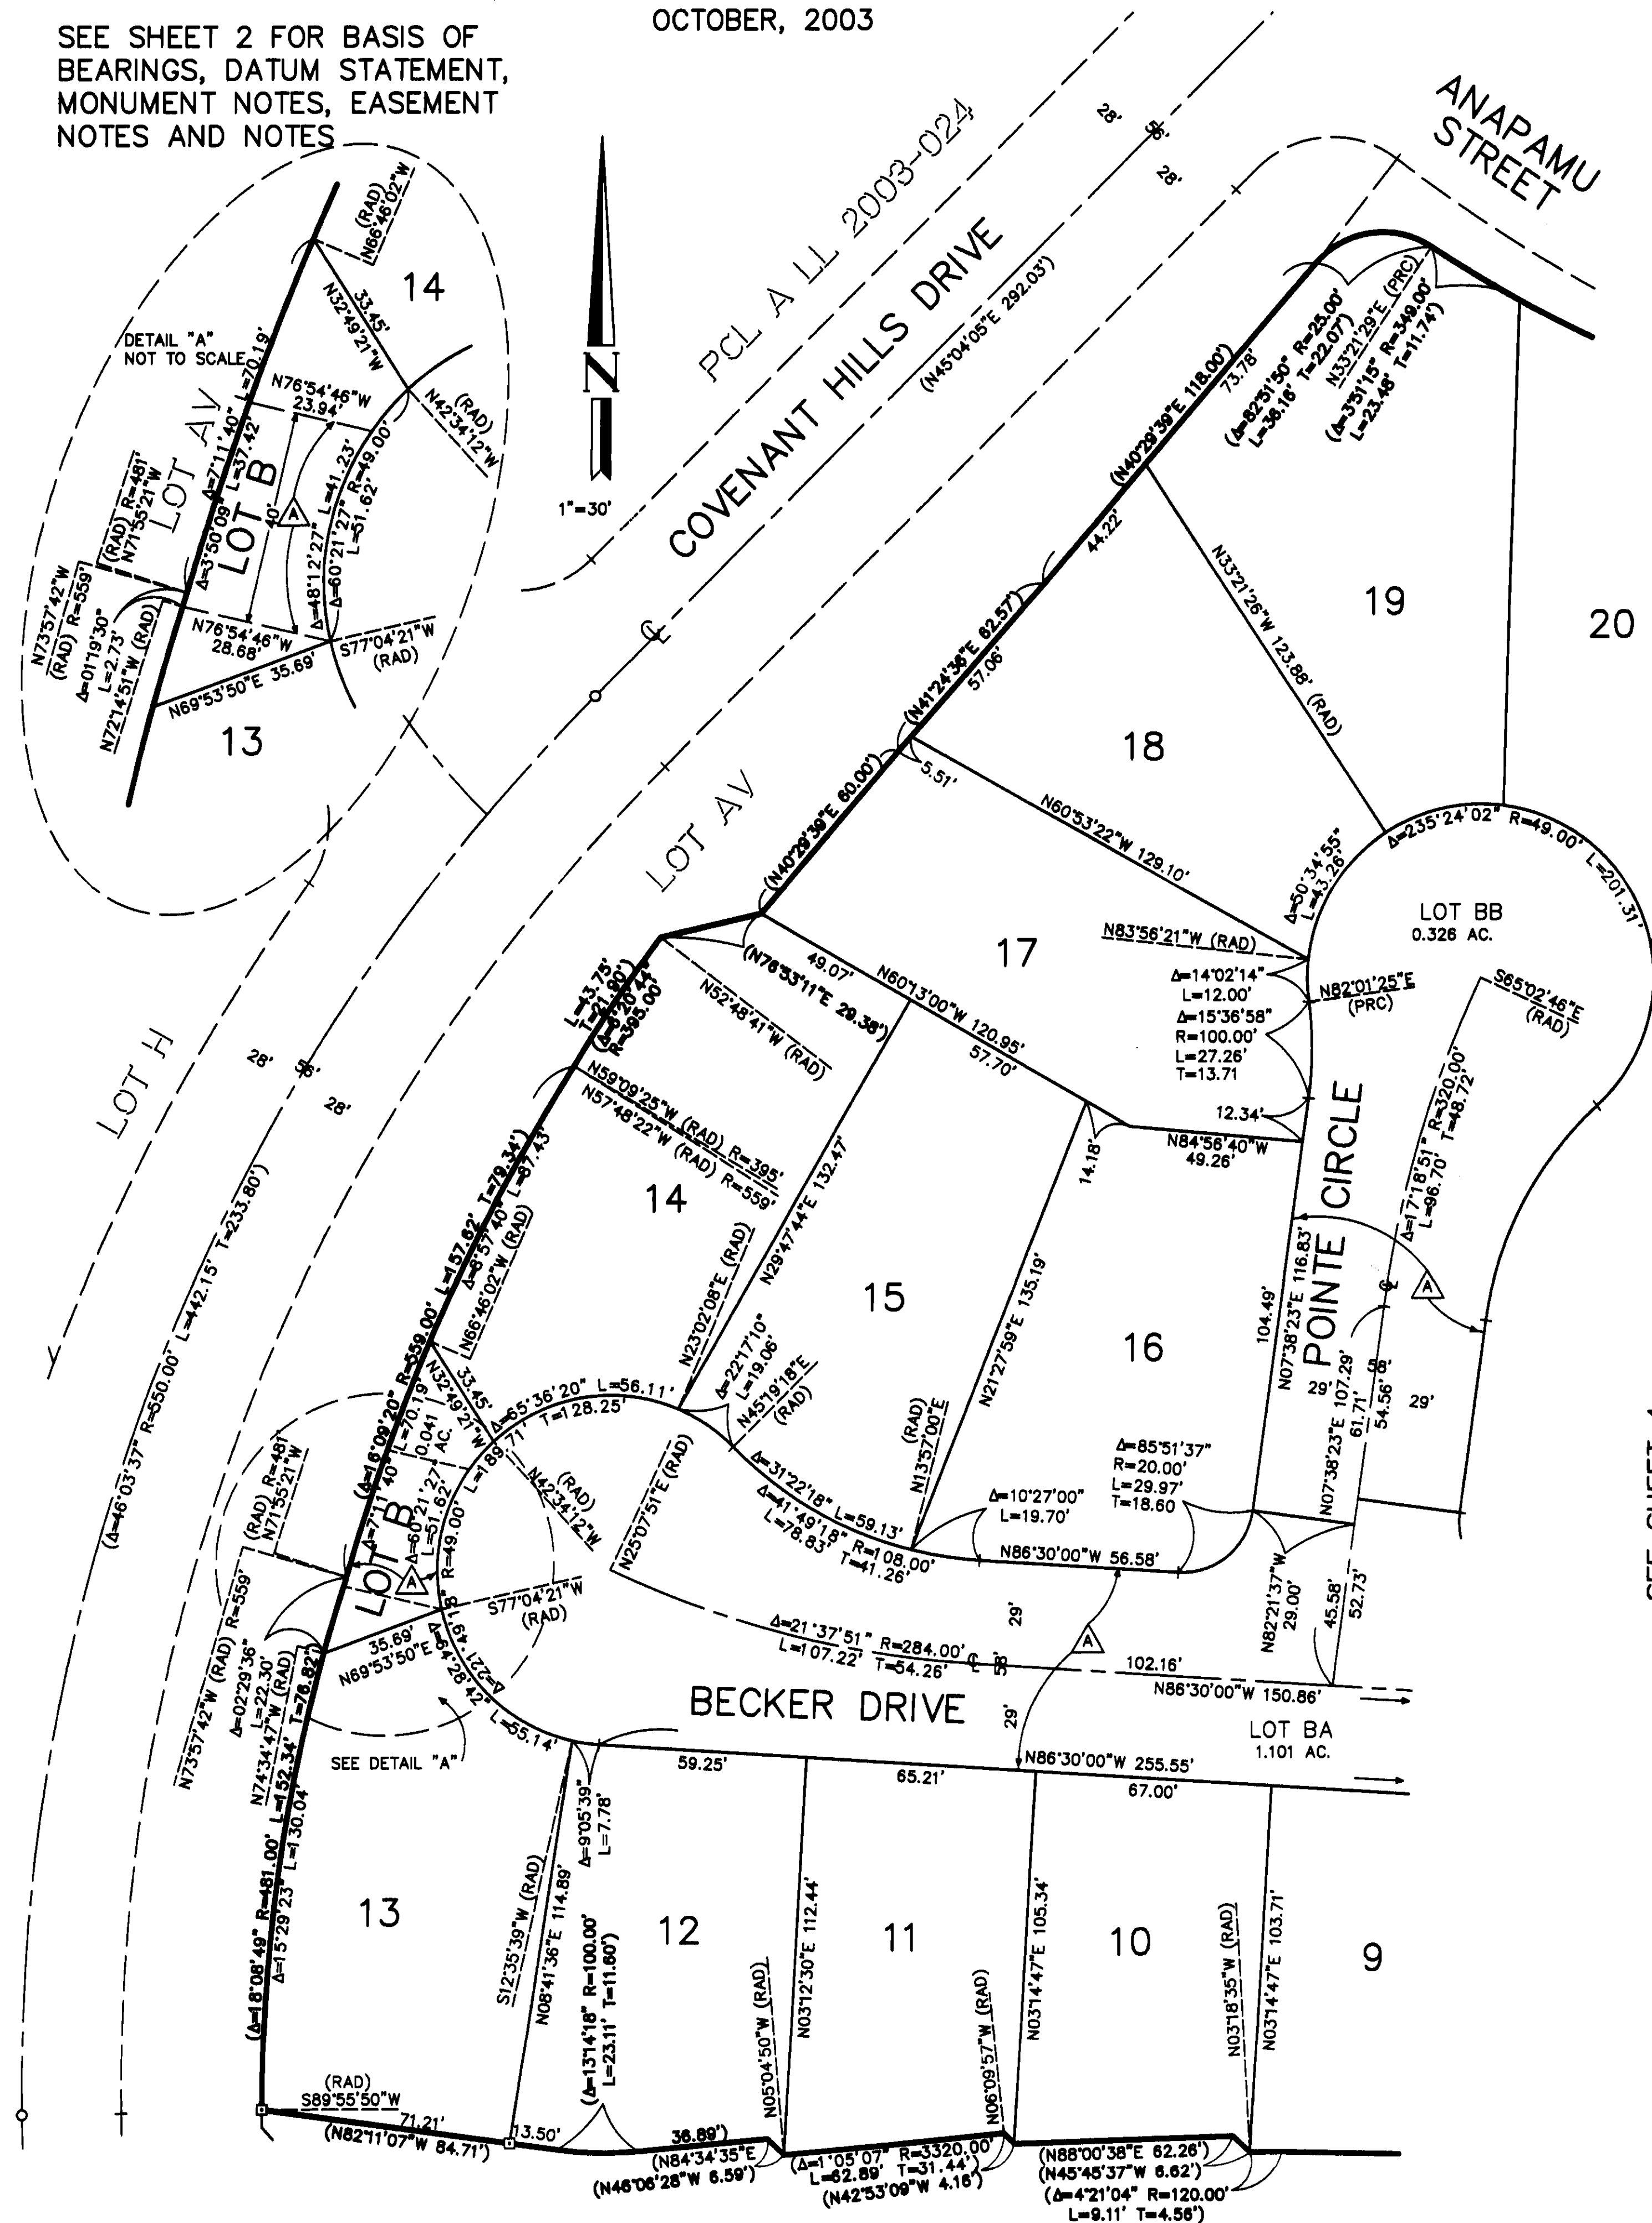

SEE SHEET 4