

SHEET 1 OF 4 SHEETS
16 NUMBERED LOTS AND
LOTS A THROUGH D, INCLUSIVE
ACREAGE: 5.364 ACRES
(A PORTION OF TENTATIVE
TRACT NO. 16389)

TRACT NO. 16414

IN UNINCORPORATED TERRITORY OF THE COUNTY OF ORANGE,
STATE OF CALIFORNIA

BEING A SUBDIVISION OF A PORTION OF LOT 10 OF TRACT NO. 15987,
AS SHOWN ON A MAP FILED IN BOOK 839, PAGES 1 THROUGH 18,
INCLUSIVE, OF MISCELLANEOUS MAPS, IN THE OFFICE OF THE
COUNTY RECORDER OF SAID COUNTY.

HUNSAKER AND ASSOCIATES IRVINE, INC.
RORY S. WILLIAMS, L.S. 6654 DATE OF SURVEY: JULY, 2002

ACCEPTED AND FILED AT THE
REQUEST OF

FIRST AMERICAN TITLE INS. CO.

DATE: FEBRUARY 6, 2003

TIME: 02:04PM FEE: \$ 13.00

INSTRUMENT NO. 2003000143050

BOOK 838 PAGE 47-50 m/m

TOM DALY
COUNTY CLERK - RECORDER

BY Rory S. Williams
DEPUTY

OWNERSHIP CERTIFICATE:

WE, THE UNDERSIGNED, BEING ALL PARTIES HAVING ANY RECORD TITLE INTEREST IN THE LAND COVERED BY THIS MAP, DO HEREBY CONSENT TO THE PREPARATION AND RECORDATION OF SAID MAP, AS SHOWN WITHIN THE DISTINCTIVE BORDER LINE.

WE HEREBY DEDICATE TO COUNTY OF ORANGE THE EASEMENTS FOR INGRESS AND EGRESS OF EMERGENCY AND PUBLIC SERVICE VEHICLES AS SHOWN ON SAID MAP.

WE ALSO DO HEREBY DECLARE THAT THE LAND COVERED BY THIS MAP IS LOCATED IN A VERY HIGH FIRE HAZARD AREA DUE TO WILDLAND EXPOSURE BASED ON STATE SRA MAPS.

WE ALSO HEREBY DEDICATE TO THE SANTA MARGARITA WATER DISTRICT THE EASEMENTS FOR WATER, RECYCLED WATER, SEWER, DRAINAGE AND ACCESS PURPOSES OVER THOSE EASEMENT AREAS AS SHOWN ON SAID MAP, WHICH EASEMENTS SHALL BE SUBJECT TO THE SAME CONDITIONS AS ARE SHOWN IN THAT CERTAIN GRANT OF EASEMENT TO SANTA MARGARITA WATER DISTRICT RECORDED SEPTEMBER 18, 2002, AS INSTRUMENT NO. 20020770401, OF OFFICIAL RECORDS, COUNTY OF ORANGE.

DMB LADERA, LLC, A DELAWARE LIMITED LIABILITY COMPANY, OWNER.

BY: RANCHO MISSION VIEJO, L.L.C., A DELAWARE LIMITED LIABILITY COMPANY, ITS AUTHORIZED AGENT AND MANAGER.

BY: [Signature] BY: [Signature]
NAME: DONALD T. STANLIN NAME: Ronald L. Vaden
TITLE: DIRECTOR OF COMMUNITY DEV. TITLE: COO

DMB CONSOLIDATED HOLDINGS, LLC, AN ARIZONA LIMITED LIABILITY COMPANY, BENEFICIARY UNDER DEEDS OF TRUST RECORDED AS INSTRUMENT NO. 19960624030 AND INSTRUMENT NO. 19990288616, BOTH OF OFFICIAL RECORDS.

BY: [Signature] BY: [Signature]
NAME: TERRY D. RANDALL NAME: Timothy A. Kachr
TITLE: VICE PRESIDENT TITLE: Executive Vice President

NOTARY ACKNOWLEDGMENTS:

STATE OF CALIFORNIA }
COUNTY OF ORANGE } SS

ON November 4th, 2002, BEFORE ME, Carolynn Rust, PERSONALLY APPEARED Terry D. Randall AND Timothy A. Kachr PERSONALLY KNOWN TO ME (OR PROVED TO ME ON THE BASIS OF SATISFACTORY EVIDENCE) TO BE THE PERSON(S) WHOSE NAME(S) IS/ARE SUBSCRIBED TO THE WITHIN INSTRUMENT AND ACKNOWLEDGED TO ME THAT HE/SHE/they EXECUTED THE SAME IN HIS/HER/their AUTHORIZED CAPACITY(IES), AND THAT BY HIS/HER/their SIGNATURE(S) ON THE INSTRUMENT THE PERSON(S), OR ENTITY UPON BEHALF OF WHICH THE PERSON(S) ACTED, EXECUTED THE INSTRUMENT.

WITNESS MY HAND:

SIGNATURE Carolynn Rust
NOTARY PUBLIC IN AND FOR SAID STATE
Carolynn Rust
(NAME PRINTED)

MY PRINCIPAL PLACE OF BUSINESS IS
IN Maricopa COUNTY.
MY COMMISSION EXPIRES: 03/01/04

STATE OF CALIFORNIA }
COUNTY OF ORANGE } SS

ON Nov 5, 2002, BEFORE ME, Tina T. Baker, Notary Public, PERSONALLY APPEARED Donald T. Stanlin AND Donald L. Vaden PERSONALLY KNOWN TO ME (OR PROVED TO ME ON THE BASIS OF SATISFACTORY EVIDENCE) TO BE THE PERSON(S) WHOSE NAME(S) IS/ARE SUBSCRIBED TO THE WITHIN INSTRUMENT AND ACKNOWLEDGED TO ME THAT HE/SHE/they EXECUTED THE SAME IN HIS/HER/their AUTHORIZED CAPACITY(IES), AND THAT BY HIS/HER/their SIGNATURE(S) ON THE INSTRUMENT THE PERSON(S), OR ENTITY UPON BEHALF OF WHICH THE PERSON(S) ACTED, EXECUTED THE INSTRUMENT.

WITNESS MY HAND:

SIGNATURE Tina T. Baker
NOTARY PUBLIC IN AND FOR SAID STATE
TINA T. BAKER
(NAME PRINTED)

MY PRINCIPAL PLACE OF BUSINESS IS
IN Orange COUNTY.
MY COMMISSION EXPIRES: 8-29-04

SIGNATURE OMISSIONS:

PURSUANT TO THE PROVISIONS OF SECTION 66436 (a)(3) OF THE SUBDIVISION MAP ACT, THE FOLLOWING SIGNATURES HAVE BEEN OMITTED:

LADERA DEVELOPMENT COMPANY, L.L.C., HOLDER OF OIL, GAS AND MINERAL RIGHTS RECORDED DECEMBER 10, 1996, AS INSTRUMENT NO. 19960624029 OF OFFICIAL RECORDS.

SURVEYOR'S STATEMENT:

THIS MAP WAS PREPARED BY ME OR UNDER MY DIRECTION AND IS BASED UPON A FIELD SURVEY IN CONFORMANCE WITH THE REQUIREMENTS OF THE SUBDIVISION MAP ACT AND LOCAL ORDINANCE AT THE REQUEST OF DMB LADERA, L.L.C., IN JULY, 2002. I HEREBY STATE THAT ALL MONUMENTS ARE OF THE CHARACTER AND OCCUPY THE POSITIONS INDICATED, OR THAT THEY WILL BE SET IN SUCH POSITIONS; AND THAT SAID MONUMENTS ARE SUFFICIENT TO ENABLE THE SURVEY TO BE RETRACED. I HEREBY STATE THAT THIS FINAL MAP SUBSTANTIALLY CONFORMS TO THE CONDITIONALLY APPROVED TENTATIVE MAP.

Rory S. Williams 10/16/02
RORY S. WILLIAMS, L.S. 6654 DATE
LICENSE EXPIRES: 12/31/03



COUNTY SURVEYOR'S STATEMENT

I HEREBY STATE THAT I HAVE EXAMINED THIS MAP AND HAVE FOUND IT TO BE SUBSTANTIALLY IN CONFORMANCE WITH THE TENTATIVE MAP AS FILED WITH, AMENDED AND APPROVED BY THE ORANGE COUNTY SUBDIVISION COMMITTEE; THAT ALL PROVISIONS OF THE SUBDIVISION MAP ACT AND COUNTY SUBDIVISION REGULATIONS HAVE BEEN COMPLIED WITH AND I AM SATISFIED SAID MAP IS TECHNICALLY CORRECT.

DATED THIS 5th DAY OF JANUARY, 2003

[Signature]
JOHN CANAS, COUNTY SURVEYOR
S 4408, EXPIRATION DATE: 9-30-05



COUNTY TREASURER-TAX COLLECTOR'S CERTIFICATE:

STATE OF CALIFORNIA }
COUNTY OF ORANGE } SS

I HEREBY CERTIFY THAT ACCORDING TO THE RECORDS OF MY OFFICE THERE ARE NO LIENS AGAINST THE LAND COVERED BY THIS MAP OR ANY PART THEREOF FOR UNPAID STATE, COUNTY, MUNICIPAL OR LOCAL TAXES OR SPECIAL ASSESSMENTS COLLECTED AS TAXES, EXCEPT TAXES OR SPECIAL ASSESSMENTS COLLECTED AS TAXES NOT YET PAYABLE.

AND DO CERTIFY TO THE RECORDER OF ORANGE COUNTY THAT THE PROVISIONS OF THE SUBDIVISION MAP ACT HAVE BEEN COMPLIED WITH REGARDING DEPOSITS TO SECURE PAYMENT OF TAXES OR SPECIAL ASSESSMENTS COLLECTED AS TAXES ON THE LAND COVERED BY THIS MAP.

DATED THIS 2nd DAY OF JANUARY, 2003

JOHN M.W. MOORLACH
COUNTY TREASURER-TAX COLLECTOR

BY: [Signature]
DEPUTY TREASURER-TAX COLLECTOR

CLERK OF THE BOARD OF SUPERVISORS' CERTIFICATE:

STATE OF CALIFORNIA }
COUNTY OF ORANGE } SS

I HEREBY CERTIFY THAT THIS MAP WAS PRESENTED FOR APPROVAL TO THE BOARD OF SUPERVISORS OF THE COUNTY OF ORANGE AT REGULAR MEETING THEREOF HELD ON THE 28th DAY OF JANUARY, 2003, AND THAT THEREUPON SAID BOARD DID, BY AN ORDER DULY PASSED AND ENTERED, APPROVE SAID MAP.

AND DID ACCEPT ON BEHALF OF THE COUNTY OF ORANGE THE EASEMENTS FOR INGRESS AND EGRESS OF EMERGENCY AND PUBLIC SERVICE VEHICLES AS DEDICATED.

DATED THIS 28th DAY OF JANUARY, 2003

[Signature]
CLERK OF THE BOARD OF SUPERVISORS
DARLENE J. BLOOM



CERTIFICATE OF ACCEPTANCE - SANTA MARGARITA WATER DISTRICT

THE UNDERSIGNED, BEING THE DULY APPOINTED AGENT OF THE SANTA MARGARITA WATER DISTRICT, A PUBLIC CORPORATION IN ORANGE COUNTY, CALIFORNIA, PURSUANT TO ITS RESOLUTION NO. 88-10-2, DOES HEREBY ACCEPT ON BEHALF OF SAID DISTRICT, THE EASEMENTS FOR SEWER, WATER AND ACCESS PURPOSES AS DEDICATED AND SHOWN ON THIS TRACT MAP, BY AND BETWEEN THE SANTA MARGARITA WATER DISTRICT AND DMB LADERA, L.L.C., A DELAWARE LIMITED LIABILITY COMPANY, AND DOES HEREBY CERTIFY THAT THE GRANTEE CONSENTS TO THE RECORDATION OF SAID TRACT MAP.

[Signature]
DANIEL R. FERONS, CHIEF ENGINEER
SANTA MARGARITA WATER DISTRICT

NOTARY ACKNOWLEDGMENT - SANTA MARGARITA WATER DISTRICT

STATE OF CALIFORNIA }
COUNTY OF ORANGE } SS

ON Nov 14, 2002, BEFORE ME, ANDREA M. EVANS, Notary Public, PERSONALLY APPEARED DANIEL R. FERONS, PERSONALLY KNOWN TO ME (OR PROVED TO ME ON THE BASIS OF SATISFACTORY EVIDENCE) TO BE THE PERSON WHOSE NAME IS SUBSCRIBED TO THE WITHIN INSTRUMENT AND ACKNOWLEDGED TO ME THAT HE EXECUTED THE SAME IN HIS AUTHORIZED CAPACITY, AND THAT BY HIS SIGNATURE ON THE INSTRUMENT THE PERSON, OR ENTITY UPON BEHALF OF WHICH THE PERSON ACTED, EXECUTED THE INSTRUMENT.

WITNESS MY HAND:

SIGNATURE Andrea M. Evans
NOTARY PUBLIC IN AND FOR SAID STATE
ANDREA M. EVANS
(NAME PRINTED)

MY PRINCIPAL PLACE OF BUSINESS IS
IN Orange COUNTY.
MY COMMISSION EXPIRES: 4/8/04

SHEET 2 OF 4 SHEETS
SCALE: 1" = 100'
16 NUMBERED LOTS AND
LOTS A THROUGH D, INCLUSIVE
ACREAGE: 5.384 ACRES
(A PORTION OF TENTATIVE
TRACT NO. 16389)

TRACT NO. 16414

IN UNINCORPORATED TERRITORY OF THE COUNTY OF ORANGE,
STATE OF CALIFORNIA

RORY S. WILLIAMS, L.S. 6654
HUNSAKER AND ASSOCIATES IRVINE, INC.
DATE OF SURVEY: JUNE, 2002

BASIS OF BEARINGS:

THE BEARINGS SHOWN HEREON ARE BASED ON THE BEARING BETWEEN O.C.S. HORIZONTAL CONTROL STATION GPS NO. 1417 AND STATION GPS NO. 1448 BEING N10°48'13"E PER RECORDS ON FILE IN THE OFFICE OF THE ORANGE COUNTY SURVEYOR.

DATUM STATEMENT:

COORDINATES SHOWN ARE BASED ON THE CALIFORNIA COORDINATE SYSTEM (CCS83), ZONE 11N, 1983 RAD, (1997.35 EPOCH OCS GPS ADJUSTMENT). ALL DISTANCES SHOWN ARE GROUND, UNLESS OTHERWISE NOTED. TO OBTAIN GRID DISTANCE MULTIPLY GROUND DISTANCE BY 0.999946235.

NOTES:

LOTS A, B AND C ARE PRIVATE STREETS.

LOT 10 IS A PRIVATE POCKET PARK AND IS NOT A RESIDENTIAL BUILDING SITE.

THIS PROPERTY IS "CONDITIONALLY EXCLUDED" FROM A SPECIAL FIRE PROTECTION AREA.

ALL RESIDENTIAL STRUCTURES EXCEEDING 5,500 SQUARE FEET (PER AMENDMENT) AND ALL STRUCTURES EXCEEDING FIRE DEPARTMENT ACCESS REQUIREMENTS SHALL BE PROTECTED BY AN AUTOMATIC FIRE SPRINKLER SYSTEM IN A MANNER MEETING THE APPROVAL OF THE FIRE CHIEF.

EASEMENT NOTES:

(A) INDICATES AN EASEMENT FOR SEWER, WATER AND ACCESS PURPOSES DEDICATED HEREON TO THE SANTA MARGARITA WATER DISTRICT.

(B) INDICATES AN EASEMENT FOR INGRESS AND EGRESS OF EMERGENCY AND PUBLIC SERVICE VEHICLES DEDICATED HEREON TO THE COUNTY OF ORANGE.

MONUMENT NOTES:

2" I.P. TAGGED L.S. 6654 OR LEAD, TACK & TAG L.S. 6654 OR NAIL & TAG L.S. 6654 OR 8" S.W. STAMPED L.S. 6654 TO BE SET AT ALL TRACT BOUNDARY CORNERS WITHIN 90 DAYS AFTER ACCEPTANCE OF IMPROVEMENTS, UNLESS OTHERWISE NOTED.

1" I.P. TAGGED L.S. 6654 OR LEAD, TACK & TAG L.S. 6654 OR NAIL & TAG L.S. 6654 OR 8" S.W. STAMPED L.S. 6654 TO BE SET AT ALL LOT CORNERS, EXCEPT LOT CORNERS THAT ARE THE PRESCRIPTION OF THE LOT LINES, WITHIN 90 DAYS AFTER ACCEPTANCE OF IMPROVEMENTS, UNLESS OTHERWISE NOTED.

8" S.W. STAMPED L.S. 6654 OR LEAD, TACK & TAG L.S. 6654 OR 1" I.P. TAGGED L.S. 6654 TO BE SET AT ALL STREET CENTERLINE POINTS OF CONTROL, WITHIN 90 DAYS AFTER ACCEPTANCE OF IMPROVEMENTS, UNLESS OTHERWISE NOTED.

LEAD, TACK & TAG L.S. 6654 TO BE SET IN CONCRETE SIDEWALK AT AN OFFSET ALONG FRONT SIDE LOT LINES PRODUCED, IN LIEU OF AT FRONT LOT CORNERS, WITHIN 90 DAYS AFTER ACCEPTANCE OF IMPROVEMENTS, UNLESS OTHERWISE NOTED. BEARING AND DISTANCE OF PRODUCTION IS AS NOTED HEREON.

● INDICATES FOUND MONUMENT OR LOCATION OF MONUMENT SET, AS NOTED.

■ INDICATES NOTHING TO BE SET.

▲ INDICATES FOUND ORANGE COUNTY SURVEYOR GPS CONTROL MONUMENT AS NOTED.

P/J INDICATES BEARING AND DISTANCE OF LOT LINE PRODUCTION FROM LOT CORNER TO MONUMENT.

[1] INDICATES LOCATION OF 2" I.P. TAGGED "P.L.S. 5557" OR SPIKE & WASHER STAMPED "P.L.S. 5557" OR LEAD, TACK & TAG "P.L.S. 5557" TO BE SET PER TRACT NO. 15987, M.M. 8.39/1-18.

[2] INDICATES LOCATION OF 1" I.P. TAGGED "P.L.S. 5557" OR SPIKE & WASHER STAMPED "P.L.S. 5557" OR LEAD, TACK & TAG "P.L.S. 5557" TO BE SET PER TRACT NO. 15987, M.M. 8.39/1-18.

[3] INDICATES SET 2" I.P. TAGGED L.S. 6654 PRIOR TO MAP RECORDATION.

[4] INDICATES FOUND O.C.S. WELL MONUMENT W/2 1/2" BRASS DISK STAMPED "ORANGE COUNTY SURVEYOR" PER TRACT NO. 16156, M.M. 812/40-48.

GPS NO. 1448
FD. 2 1/2" IRON PIPE WITH 2" OCS
BRASS CAP STAMPED "GPS 1448
9-95" PER R.S.B. 154/B-18 AND
RECORDS ON FILE IN THE ORANGE
COUNTY SURVEYOR'S OFFICE.
N 2146790.819 E 6142602.585

GPS NO. 1417
FD. 2 1/2" IRON PIPE WITH 2" OCS
BRASS CAP STAMPED "GPS 1417
9-95" PER R.S.B. 154/B-18 AND
RECORDS ON FILE IN THE ORANGE
COUNTY SURVEYOR'S OFFICE.
N 2141450.558 E 6141583.535

3 INDICATES SHEET NUMBER



838

48

48

838

838 49

TRACT NO. 16414
IN UNINCORPORATED TERRITORY OF THE COUNTY OF ORANGE,
STATE OF CALIFORNIA

SHEET 3 OF 4 SHEETS
SCALE: 1" = 40'
16 NUMBERED LOTS AND
LOTS A THROUGH D, INCLUSIVE
ACREAGE 5.384 ACRES
(A PORTION OF TENTATIVE
TRACT NO. 16389)

HUNSAKER AND ASSOCIATES IRVINE, INC.
RORY S. WILLIAMS, L.S. 6654
DATE OF SURVEY: JUNE, 2002
TRACT NO. 15987
M.M. 839/I-18
POR. LOT 10

SEE SHEET 2 FOR BASIS OF BEARINGS, DATUM STATEMENT,
MONUMENT NOTES, SHEET INDEX AND GPS CONTROL MAP,
EASEMENT NOTES AND NOTES.

ANTONIO PARKWAY

LOT BD

LOT C

SEE SHEET

THOMAS ROAD

LOT BA

BELL ROAD

PASTURE

LOT BZ

ROAD

LOT CA

COCKENHILL DRIVE


POR. POL. I

LL 96 - 026

INST. NO. 19960587414, O.R.

TRACT NO. 15987
M.M. 839/I-18

MONUMENT OFFSET TABLE		
LINE	BEARING	LENGTH
P1	N11°14'24"W	1.04'
P2	N11°14'24"W	1.08'
P3	N11°14'24"W	1.04'
P4	N11°14'24"W	1.01'
P5	N49°41'13"W	1.00'
P6	S71°42'39"W	1.00'
P7	S13°32'56"W	1.04'
P8	S13°32'56"W	1.24'

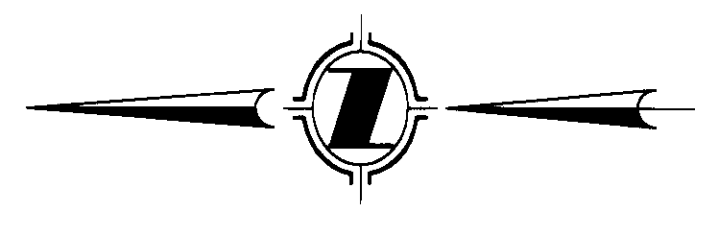

TRACT NO. 16414
IN UNINCORPORATED TERRITORY OF THE COUNTY OF ORANGE,
STATE OF CALIFORNIA

HUNSAKER AND ASSOCIATES IRVINE, INC.
RORY S. WILLIAMS, L.S. 6654
DATE OF SURVEY: JUNE, 2002


TRACT NO. 15987

PTN. LOT 10

M.M. 839/1-18

SEE SHEET 3

SHEET 4 OF 4 SHEETS
SCALE: 1" = 40'
16 NUMBERED LOTS AND
LOTS A THROUGH D, INCLUSIVE
ACREAGE: 5.384 ACRES
(A PORTION OF TENTATIVE
TRACT NO. 16389)

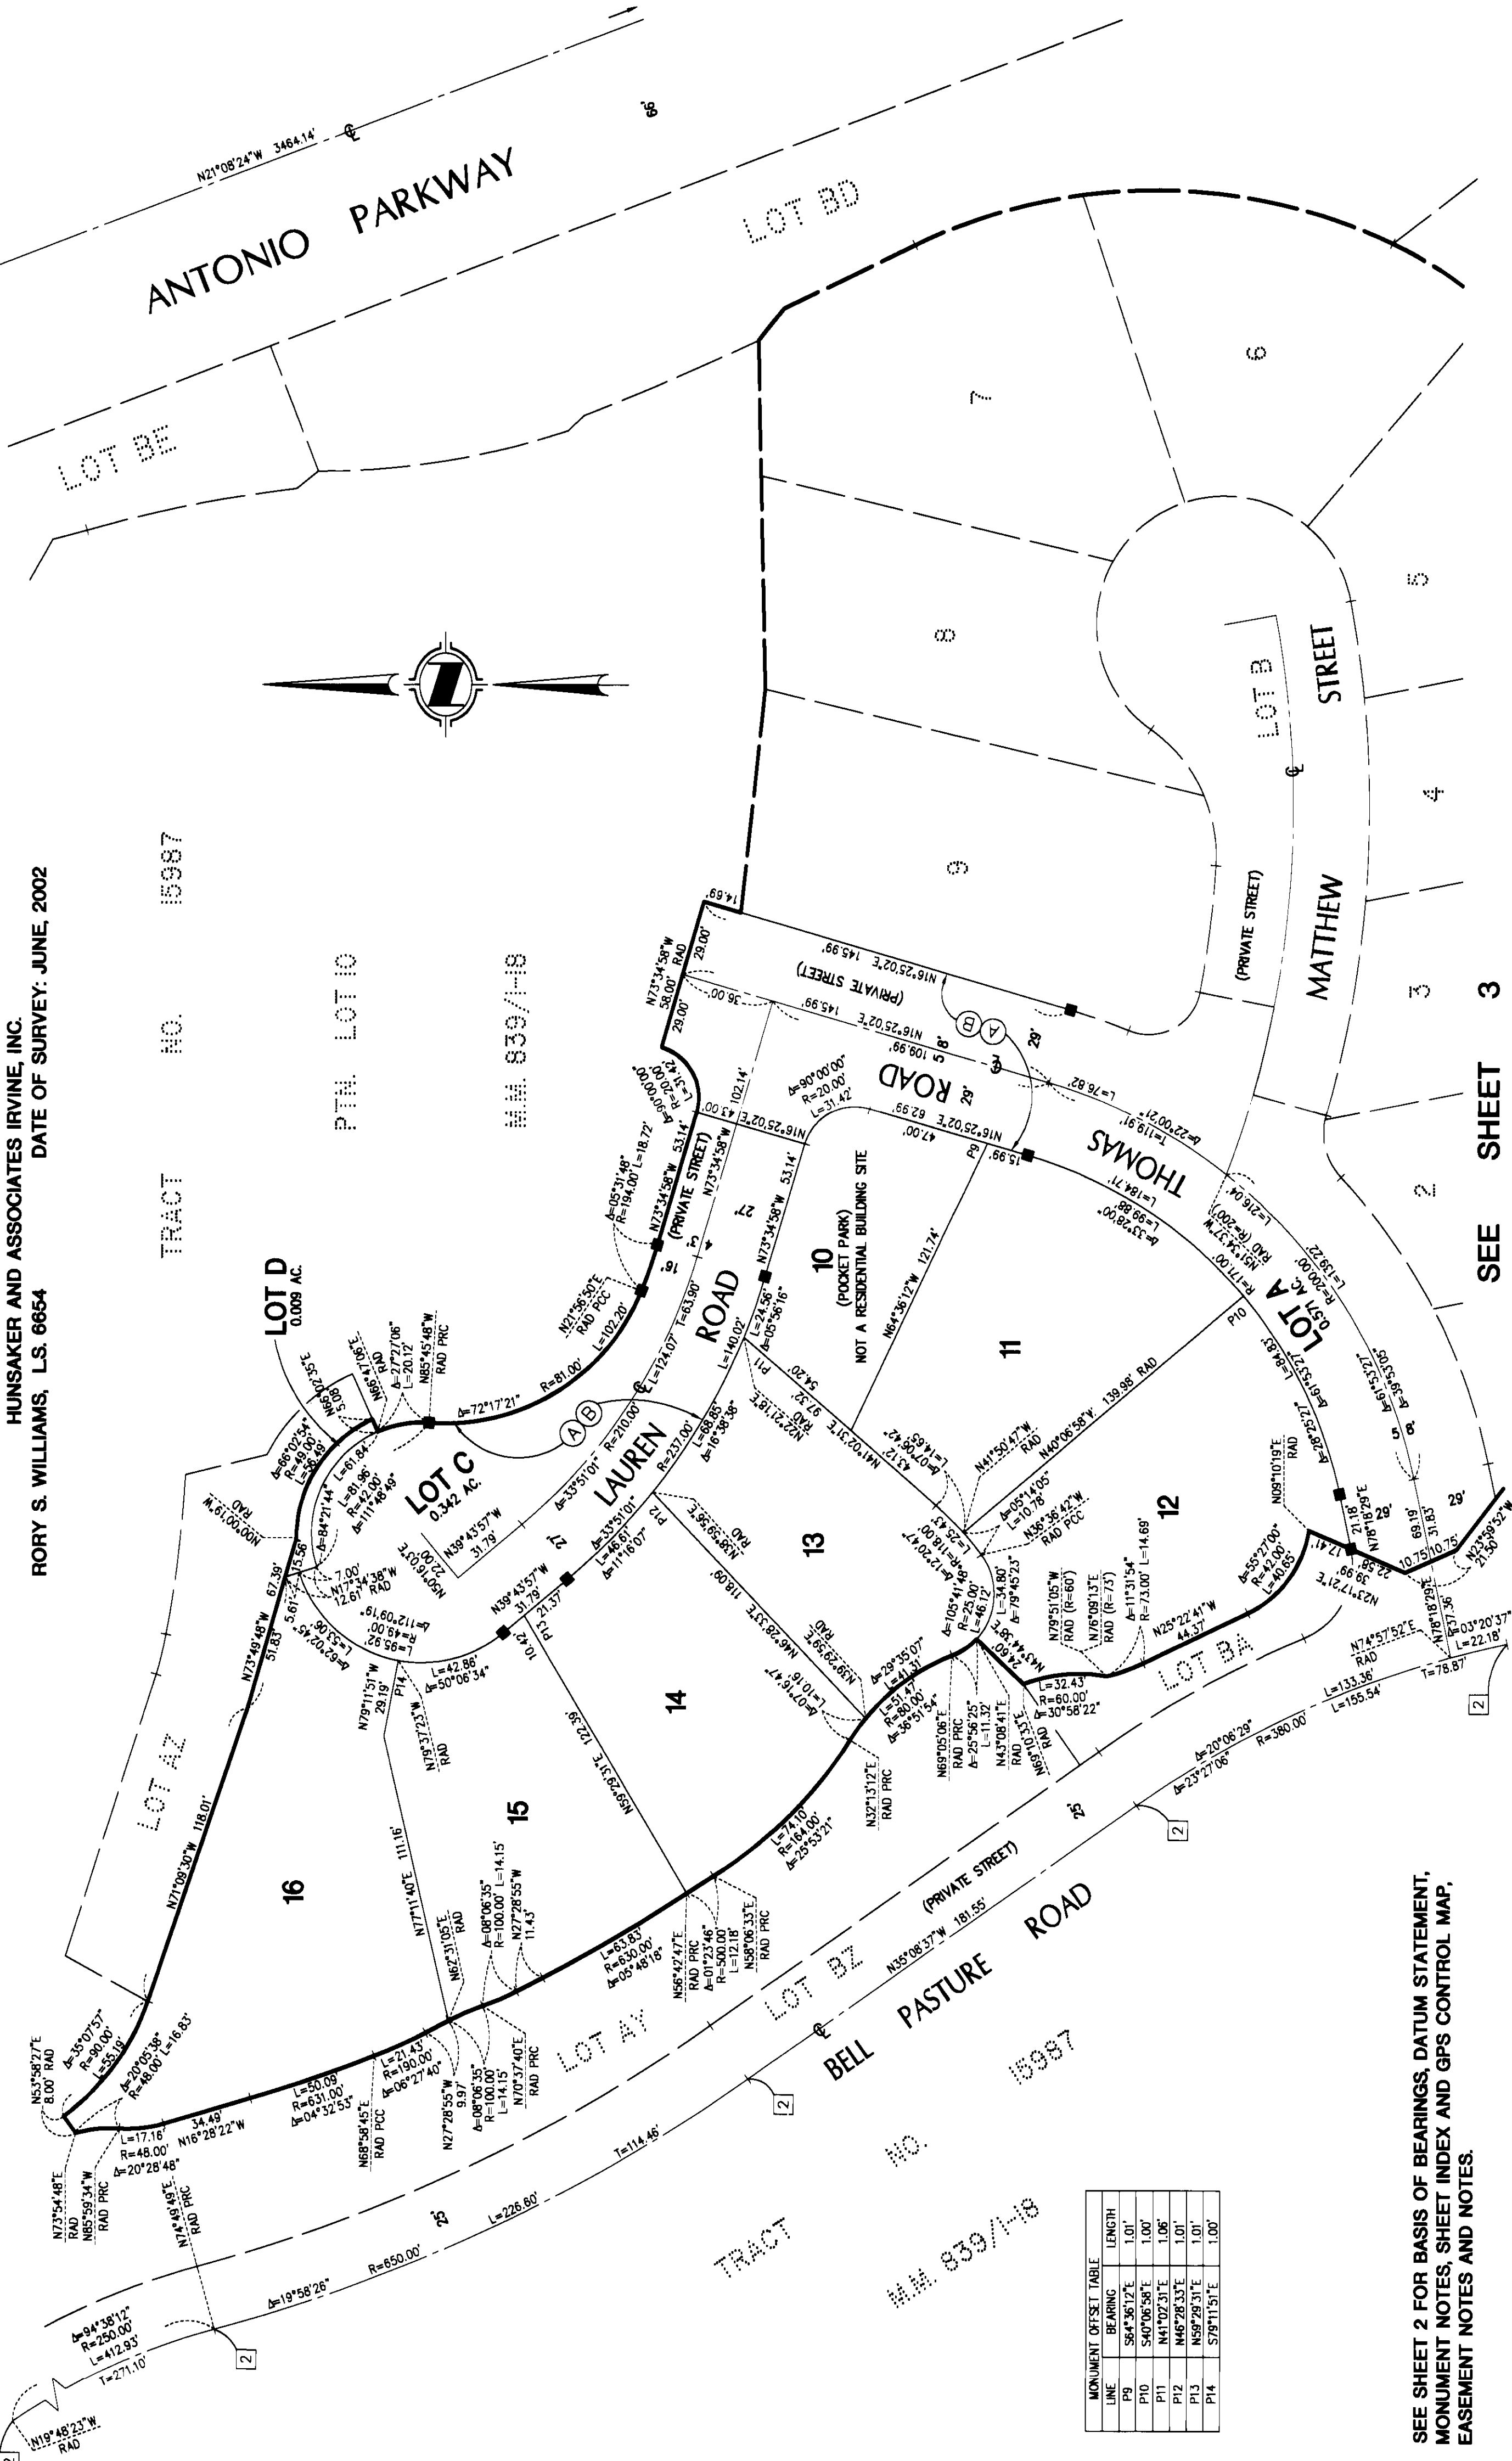

MONUMENT OFFSET TABLE		
LINE	BEARING	LENGTH
P9	S64°36'12"E	1.01'
P10	S40°06'58"E	1.00'
P11	N41°02'31"E	1.06'
P12	N46°28'33"E	1.01'
P13	N59°28'31"E	1.01'
P14	S79°11'51"E	1.00'

SEE SHEET 2 FOR BASIS OF BEARINGS, DATUM STATEMENT,
MONUMENT NOTES, SHEET INDEX AND GPS CONTROL MAP,
EASEMENT NOTES AND NOTES.