

SHEET 1 OF 8 SHEETS
2 NUMBERED LOTS
19 LETTERED LOTS
23.023 ACRES
PORTION OF VESTING
T.T.M. 15990
DATE OF SURVEY:
JANUARY, 1999

TRACT MAP NO. 16471

IN THE UNINCORPORATED TERRITORY OF THE COUNTY OF ORANGE,
STATE OF CALIFORNIA

BEING A SUBDIVISION OF A PORTION OF PARCEL 1 OF LOT LINE ADJUSTMENT NO.
LL 96-026, IN THE UNINCORPORATED TERRITORY OF THE COUNTY OF ORANGE,
STATE OF CALIFORNIA, AS SHOWN ON EXHIBIT "B" ATTACHED TO THAT CERTAIN
DOCUMENT RECORDED NOVEMBER 21, 1996 AS INSTRUMENT NO. 19960587414 OF
OFFICIAL RECORDS, IN THE OFFICE OF THE COUNTY RECORDER OF SAID COUNTY.

HALL & FOREMAN, INC.

STEVEN C. SHAMBECK, P.L.S. 6217
APRIL, 2004

ACCEPTED AND FILED AT THE
REQUEST OF

FIRST AMERICAN TITLE INSURANCE COMPANY

DATE October 28, 2004

TIME 10:54 AM FEES 28.00

INSTRUMENT # 2004000972828

BOOK 867 PAGE 42-49/111

TOM DALY
COUNTY CLERK-RECORDER

BY Jimmy A. Demaj
DEPUTY

OWNERSHIP CERTIFICATE

WE, THE UNDERSIGNED, BEING ALL PARTIES HAVING ANY RECORD TITLE INTEREST
IN THE LAND COVERED BY THIS MAP, DO HEREBY CONSENT TO THE PREPARATION
AND RECORDATION OF SAID MAP, AS SHOWN WITHIN THE DISTINCTIVE BORDER
LINE.

WE ALSO HEREBY DEDICATE TO THE COUNTY OF ORANGE:

1. THE EASEMENT FOR SCENIC PRESERVATION PURPOSES AS SHOWN ON SAID MAP
FOR THE PURPOSES AND SUBJECT TO THE SAME CONDITIONS AND LIMITATIONS
AS SHOWN IN THAT CERTAIN EASEMENT RECORDED SEPTEMBER 19, 1991 AS INSTRUMENT
NO. 91-511820, OF OFFICIAL RECORDS.
2. THE EASEMENT FOR EMERGENCY ACCESS PURPOSES OVER ALL OF LOT BA AS SHOWN
ON SAID MAP.
3. THE EASEMENT FOR FIRE PROTECTION ACCESS PURPOSES AS SHOWN ON SAID MAP.
4. THE EASEMENT FOR PUBLIC PEDESTRIAN PURPOSES AS SHOWN ON SAID MAP.
5. THE EASEMENT FOR STORM DRAIN PURPOSES AS SHOWN ON SAID MAP.

WE ALSO HEREBY GRANT TO THE ORANGE COUNTY FLOOD CONTROL DISTRICT LOT C IN
FEE SIMPLE FOR DRAINAGE PURPOSES.

WE ALSO HEREBY DEDICATE TO THE SANTA MARGARITA WATER DISTRICT THE EASEMENTS FOR
WATER, RECYCLED WATER, SEWER, DRAINAGE, AND ACCESS PURPOSES OVER THOSE EASEMENT
AREAS AS SHOWN ON SAID MAP WHICH EASEMENTS SHALL BE SUBJECT TO THE SAME
CONDITIONS AS ARE SHOWN IN THAT CERTAIN GRANT OF EASEMENT TO SANTA MARGARITA
WATER DISTRICT RECORDED SEPTEMBER 18, 2002 AS INSTRUMENT NO. 20020799401, OF
OFFICIAL RECORDS, COUNTY OF ORANGE.

THE SANTA MARGARITA WATER DISTRICT SHALL RESTORE OTHER IMPROVEMENTS OR FACILITIES
LOCATED WITHIN THE EASEMENT, IF IT HAS CONSENTED TO THE LOCATION OF SUCH
IMPROVEMENTS OR FACILITIES TO THE EXTENT THAT THE EXERCISE OF ITS RIGHTS IN
CONNECTION WITH THE EASEMENT IMPACTS OTHER IMPROVEMENTS OR FACILITIES LOCATED
WITHIN THE EASEMENT; HOWEVER, IN NO EVENT SHALL SANTA MARGARITA WATER DISTRICT
BE RESPONSIBLE FOR THE COST OF RELOCATING ITS FACILITIES IN THE EVENT OF CONFLICTS
WITH SUCH OTHER IMPROVEMENTS OR FACILITIES.

DMB LADERA, L.L.C., A DELAWARE LIMITED LIABILITY COMPANY

BY: RANCHO MISSION VIEJO, L.L.C. A DELAWARE LIMITED LIABILITY COMPANY,
IT'S AUTHORIZED AGENT AND MANAGER.

BY: Paul Johnson
PRINT NAME: Paul Johnson
PRINT TITLE: Senior V.P.

BY: Gregory S. Edwards
PRINT NAME: Gregory S. Edwards
PRINT TITLE: Sr. V.P. / CEO

NOTARY ACKNOWLEDGEMENT

STATE OF California
COUNTY OF Orange) SS

ON July 19, 2004 BEFORE ME, Diana L. Binks,

Notary Public
PERSONALLY APPEARED Paul Johnson and Gregory S. Edwards
PERSONALLY KNOWN TO ME (OR PROVED TO ME ON THE BASIS OF SATISFACTORY
EVIDENCE) TO BE THE PERSON(S) WHOSE NAME(S) IS/ARE SUBSCRIBED TO THE
WITHIN INSTRUMENT AND ACKNOWLEDGED TO ME THAT HE/SHE/they EXECUTED
THE SAME IN HIS/HER/their AUTHORIZED CAPACITY(IES), AND THAT BY HIS/
HER/their SIGNATURE(S) ON THE INSTRUMENT THE PERSON(S) OR THE ENTITY UPON
BEHALF OF WHICH THE PERSON(S) ACTED, EXECUTED THE INSTRUMENT.

WITNESS MY HAND:

Diana L. Binks
NOTARY PUBLIC IN AND FOR SAID STATE

Diana L. Binks
PRINT NAME

MY PRINCIPAL PLACE OF BUSINESS IS IN Orange COUNTY
MY COMMISSION EXPIRES 12/12/06

ORANGE COUNTY FLOOD CONTROL DISTRICT ACCEPTANCE CERTIFICATE

STATE OF CALIF.)
COUNTY OF ORANGE) SS

I HEREBY CERTIFY THAT THIS MAP WAS PRESENTED TO THE BOARD OF SUPERVISORS
OF THE ORANGE COUNTY FLOOD CONTROL DISTRICT AT A REGULAR MEETING THEREOF
HELD ON THE 19th DAY OF October, 2004 AND
THAT THEREUPON SAID BOARD DID, BY AN ORDER DULY PASSED AND ENTERED,
ACCEPT LOT C IN FEE SIMPLE FOR DRAINAGE PURPOSES AS DEDICATED.

DATED THIS 19th DAY OF October, 2004.

Darlene J. Bloom
DARLENE J. BLOOM
CLERK OF THE BOARD OF SUPERVISORS
OF THE ORANGE COUNTY FLOOD CONTROL DISTRICT


SEE SHEET 2 FOR ADDITIONAL NOTARY ACKNOWLEDGMENT AND SIGNATURE OMISSIONS

SURVEYOR'S STATEMENT

THIS MAP WAS PREPARED BY ME OR UNDER MY DIRECTION AND IS BASED UPON A
FIELD SURVEY IN CONFORMANCE WITH THE REQUIREMENTS OF THE SUBDIVISION MAP
ACT AND LOCAL ORDINANCE AT THE REQUEST OF DMB LADERA, LLC IN JANUARY,
1999. I HEREBY STATE THAT ALL MONUMENTS ARE OF THE CHARACTER AND
OCCUPY THE POSITIONS INDICATED, OR THAT THEY WILL BE SET IN SUCH
POSITIONS; AND THAT SAID MONUMENTS ARE SUFFICIENT TO ENABLE THE SURVEY
TO BE RETRACED. I HEREBY STATE THAT THIS FINAL MAP SUBSTANTIALLY
CONFORMS TO THE CONDITIONALLY APPROVED TENTATIVE MAP.

Steven C. Shambeck
STEVEN C. SHAMBECK, P.L.S. 6217
LICENSE EXPIRES: 3/31/06

7-13-2004
DATE

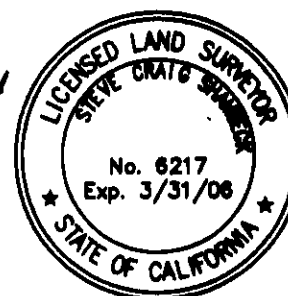


COUNTY SURVEYOR'S STATEMENT

I HEREBY STATE THAT I HAVE EXAMINED THIS MAP AND HAVE FOUND IT TO BE
SUBSTANTIALLY IN CONFORMANCE WITH THE TENTATIVE MAP AS FILED WITH,
AMENDED AND APPROVED BY THE ORANGE COUNTY SUBDIVISION COMMITTEE; THAT
ALL PROVISIONS OF THE SUBDIVISION MAP ACT AND COUNTY SUBDIVISION
REGULATIONS HAVE BEEN COMPLIED WITH AND I AM SATISFIED SAID MAP IS
TECHNICALLY CORRECT.

DATED THIS 27th DAY OF September, 2004.

Raymond L. Mathe
RAYMOND L. MATHE, COUNTY SURVEYOR
L.S. 6185 EXPIRATION DATE: 3-31-06

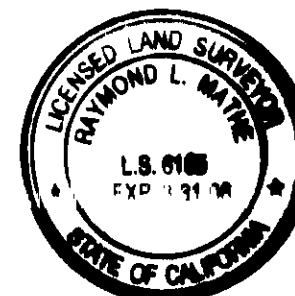

CLERK OF THE BOARD OF SUPERVISOR'S CERTIFICATE

STATE OF CALIFORNIA)
COUNTY OF ORANGE) SS

I HEREBY CERTIFY THAT THIS MAP WAS PRESENTED FOR APPROVAL TO THE
BOARD OF SUPERVISORS OF ORANGE COUNTY AT A REGULAR MEETING THEREOF
HELD ON THE 19th DAY OF October, 2004 AND THAT
THEREUPON SAID BOARD DID, BY AN ORDER DULY PASSED AND ENTERED,
APPROVE SAID MAP.


AND DID ALSO ACCEPT ON BEHALF OF THE COUNTY OF ORANGE:

1. THE EASEMENT FOR SCENIC PRESERVATION PURPOSES AS DEDICATED.
2. THE EASEMENT FOR EMERGENCY ACCESS PURPOSES OVER ALL OF LOT BA
AS DEDICATED.
3. THE EASEMENT FOR FIRE PROTECTION ACCESS PURPOSES AS DEDICATED.
4. THE EASEMENT FOR PUBLIC PEDESTRIAN PURPOSES AS DEDICATED.
5. THE EASEMENT FOR STORM DRAIN PURPOSES AS DEDICATED.

AND DID ALSO APPROVE SUBJECT MAP PURSUANT TO THE PROVISIONS OF SECTION
66438(a)(3)(A) OF THE SUBDIVISION MAP ACT.

DATED THIS 19th DAY OF October, 2004

Darlene J. Bloom
DARLENE J. BLOOM
CLERK OF THE BOARD OF SUPERVISORS

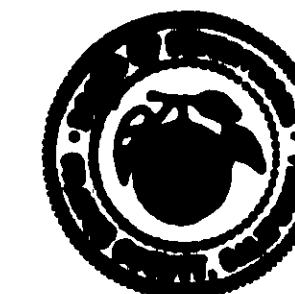

COUNTY TREASURER-TAX COLLECTOR'S CERTIFICATE

STATE OF CALIFORNIA)
COUNTY OF ORANGE) SS

I HEREBY CERTIFY THAT ACCORDING TO THE RECORDS OF MY
OFFICE THERE ARE NO LIENS AGAINST THE LAND COVERED BY THIS
MAP OR ANY PART THEREOF FOR UNPAID STATE, COUNTY, MUNICIPAL
OR LOCAL TAXES OR SPECIAL ASSESSMENTS COLLECTED AS TAXES,
EXCEPT TAXES OR SPECIAL ASSESSMENTS COLLECTED AS TAXES.

AND DO CERTIFY TO THE RECORDER OF THE COUNTY OF ORANGE
THAT THE PROVISIONS OF THE SUBDIVISION MAP ACT HAVE BEEN COMPLIED
WITH REGARDING DEPOSITS TO SECURE PAYMENT OF TAXES OR SPECIAL
ASSESSMENTS COLLECTED AS TAXES ON THE LAND COVERED BY THIS MAP.

DATED THIS 22nd DAY OF July, 2004.

John M.W. Moorlach
JOHN M.W. MOORLACH
COUNTY TREASURER-TAX COLLECTOR

BY: Mad Jorgensen
DEPUTY TREASURER -
TAX COLLECTOR

SHEET 2 OF 8 SHEETS
2 NUMBERED LOTS
19 LETTERED LOTS
23.023 ACRES
PORTION OF VESTING
T.T.M. 15990
DATE OF SURVEY:
JANUARY, 1999

TRACT MAP NO. 16471

IN THE UNINCORPORATED TERRITORY OF THE COUNTY OF ORANGE,
STATE OF CALIFORNIA

HALL & FOREMAN, INC.

STEVEN C. SHAMBECK, P.L.S. 6217
APRIL, 2004

CERTIFICATE OF ACCEPTANCE

THE UNDERSIGNED, BEING THE DULY APPOINTED AGENT OF THE SANTA MARGARITA WATER DISTRICT, A PUBLIC CORPORATION OF ORANGE COUNTY, CALIFORNIA, PURSUANT TO ITS RESOLUTION NO. 88-10-02, DOES HEREBY ACCEPT ON BEHALF OF SAID DISTRICT THE EASEMENTS FOR, WATER, RECYCLED WATER, SEWER, DRAINAGE, AND ACCESS PURPOSES, AS DEDICATED AND AS SHOWN ON THIS TRACT MAP, BY AND BETWEEN THE SANTA MARGARITA WATER DISTRICT AND DMB LADERA, L.L.C., AND DOES HEREBY CERTIFY THAT THE GRANTEE CONSENTS TO THE RECORDATION OF SAID TRACT.

DANIEL R. FERONS, CHIEF ENGINEER
SANTA MARGARITA WATER DISTRICT

SANTA MARGARITA WATER DISTRICT

STATE OF CALIFORNIA)
COUNTY OF ORANGE)

ON THIS 21st DAY OF July, 2004, BEFORE ME, Kristen J. Collins
A NOTARY PUBLIC IN AND FOR SAID STATE, PERSONALLY APPEARED DANIEL R. FERONS PERSONALLY KNOWN TO ME OR PROVED TO ME ON THE BASIS OF SATISFACTORY EVIDENCE TO BE THE PERSON WHOSE NAME IS SUBSCRIBED TO THE WITHIN INSTRUMENT AND ACKNOWLEDGED TO ME THAT HE EXECUTED THE SAME IN HIS AUTHORIZED CAPACITY, AND THAT BY HIS SIGNATURE ON THE INSTRUMENT THE PERSON OR THE ENTITY UPON BEHALF OF WHICH THE PERSON ACTED, EXECUTED THE INSTRUMENT.

WITNESS MY HAND:

MY COMMISSION EXPIRES 1/20/2008

Kristen J. Collins MY PRINCIPAL PLACE OF BUSINESS
NOTARY PUBLIC IN AND FOR SAID STATE IS IN Orange COUNTY

Kristen J. Collins
PRINT NAME

AUTOMATIC FIRE SPRINKLER NOTE:
ALL MULTIFAMILY RESIDENTIAL STRUCTURES; ALL SINGLE FAMILY STRUCTURES EXCEEDING 5,500 SQUARE FEET; AND ALL STRUCTURES EXCEEDING FIRE DEPARTMENT ACCESS REQUIREMENTS SHALL BE PROTECTED BY AN AUTOMATIC SPRINKLER SYSTEM, IN A MANNER MEETING THE APPROVAL OF THE FIRE CHIEF.

SPECIAL FIRE PROTECTION NOTE:
PROPERTY IS IN A SPECIAL FIRE PROTECTION AREA.

HIGH FIRE HAZARD AREA NOTE:
THE LOTS SHOWN ON THIS MAP ARE IN A HIGH/VERY HIGH FIRE HAZARD AREA DUE TO WILD LAND EXPOSURE.

SIGNATURE OMISSIONS

PURSUANT TO THE PROVISIONS OF SECTION 66436 (a)(3)(A)(C) OF THE SUBDIVISION MAP ACT, THE FOLLOWING SIGNATURES HAVE BEEN OMITTED:

LADERA DEVELOPMENT COMPANY, L.L.C., HOLDER OF OIL, GAS, AND MINERAL RIGHTS PER DEED RECORDED DECEMBER 10, 1998 AS INSTRUMENT NO. 19960624029 OF OFFICIAL RECORDS.

SOUTHERN CALIFORNIA EDISON COMPANY HOLDER OF AN EASEMENT FOR PUBLIC UTILITIES AND INCIDENTAL PURPOSES PER DOCUMENT RECORDED APRIL 16, 1985, IN BOOK 7485, PAGE 714, OF OFFICIAL RECORDS.

NOTES:

"THE PRIVATE STREETS CONSTRUCTED WITHIN THIS MAP SHALL BE OWNED, OPERATED AND MAINTAINED BY THE DEVELOPER, SUCCESSORS OR ASSIGNS. THE COUNTY OF ORANGE SHALL HAVE NO RESPONSIBILITY THEREFORE UNLESS PURSUANT TO APPROPRIATE SECTIONS OF THE STREETS AND HIGHWAYS CODE OF THE STATE OF CALIFORNIA, THE SAID PRIVATE STREETS HAVE BEEN ACCEPTED INTO THE COUNTY ROAD ROAD SYSTEM BY APPROPRIATE RESOLUTION OF THE ORANGE COUNTY BOARD OF SUPERVISORS."

EASEMENT NOTES

- ☒ INDICATES SOUTHERN CALIFORNIA EDISON COMPANY EASEMENT FOR PUBLIC UTILITIES AND INCIDENTAL PURPOSES PER DOCUMENT RECORDED APRIL 16, 1985, IN BOOK 7485, PAGE 714, OF OFFICIAL RECORDS.
- ☒ INDICATES WATER, RECYCLED WATER, SEWER AND ACCESS EASEMENT DEDICATED TO SANTA MARGARITA WATER DISTRICT.
- ☒ INDICATES STORM DRAIN EASEMENT AS DEDICATED TO THE COUNTY OF ORANGE.
- ☒ INDICATES FIRE PROTECTION ACCESS EASEMENT AS DEDICATED TO THE COUNTY OF ORANGE.
- ☒ INDICATES SCENIC PRESERVATION EASEMENT AS DEDICATED TO THE COUNTY OF ORANGE.
- ☒ INDICATES PUBLIC PEDESTRIAN EASEMENT AS DEDICATED TO THE COUNTY OF ORANGE.
- ☒ INDICATES DRAINAGE AND ACCESS EASEMENT DEDICATED TO SANTA MARGARITA WATER DISTRICT.

BASIS OF BEARINGS

THE BEARINGS SHOWN HEREON ARE BASED ON THE BEARING BETWEEN O.C.S. HORIZONTAL CONTROL STATION GPS NO. 1417 AND STATION GPS NO. 1448, BEING NORTH 10°48'13" EAST PER RECORDS ON FILE IN THE OFFICE OF THE ORANGE COUNTY SURVEYOR.

DATUM STATEMENT

COORDINATES SHOWN ARE BASED ON THE CALIFORNIA COORDINATE SYSTEM (CCS 83), ZONE VI, 1983 NAD (1991.35 EPOCH OCS GPS ADJUSTMENT). ALL DISTANCES ARE GROUND DISTANCES UNLESS OTHERWISE NOTED. TO OBTAIN GRID DISTANCE MULTIPLY GROUND DISTANCE BY 0.999948295. THIS FACTOR IS PROJECT-SPECIFIC.

MONUMENT NOTES

- INDICATES FOUND MONUMENT AS NOTED.
- ☒ INDICATES FOUND 2 1/2" IRON PIPE W/2" OCS BRASS CAP STAMPED "GPS 1448 9-95" PER TRACT NO. 16203, M.M. 826/8-20 AND RECORDS ON FILE IN THE ORANGE COUNTY SURVEYORS OFFICE. N2146790.819, E8142602.585
- ☒ INDICATES FOUND 2 1/2" IRON PIPE W/2" OCS BRASS CAP STAMPED "GPS 1417 9-95" PER TRACT NO. 16203, M.M. 826/8-20 AND RECORDS ON FILE IN THE ORANGE COUNTY SURVEYORS OFFICE. N2141450.558, E8141583.535
- ☐ INDICATES 2" I.P. TAGGED P.L.S. 5557 OR SPIKE & WASHER STAMPED P.L.S. 5557 OR LEAD, TACK & TAG P.L.S. 5557 TO BE SET PER TRACT NO. 16271 M.M. 839/34-45, UNLESS OTHERWISE NOTED.
- ☐ INDICATES 2" I.P. TAGGED P.L.S. 5557 OR SPIKE & WASHER STAMPED P.L.S. 5557 OR LEAD, TACK & TAG P.L.S. 5557 TO BE SET PER TRACT NO. 15986 M.M. 849/1-15, UNLESS OTHERWISE NOTED.
- 2" I.P. TAGGED L.S. 6217 OR SPIKE & WASHER STAMPED L.S. 6217 OR LEAD, TACK & TAG L.S. 6217 TO BE SET AT ALL TRACT BOUNDARY CORNERS WITHIN 90 DAYS AFTER ACCEPTANCE OF IMPROVEMENTS.
- 1" I.P. TAGGED L.S. 6217 OR SPIKE & WASHER STAMPED L.S. 6217 OR LEAD, TACK & TAG L.S. 6217 TO BE SET AT LOT CORNERS WITHIN 90 DAYS AFTER ACCEPTANCE OF IMPROVEMENTS.
- 1" I.P. TAGGED L.S. 6217 OR SPIKE & WASHER STAMPED L.S. 6217 OR LEAD, TACK & TAG L.S. 6217 TO BE SET AT ALL CENTERLINE INTERSECTIONS, E.C.'S AND B.C.'S WITHIN 90 DAYS AFTER ACCEPTANCE OF IMPROVEMENTS.

NOTES

LOT BA IS FOR PRIVATE STREET PURPOSES AND IS NOT A SEPARATE BUILDING SITE.

LOTS A THROUGH (AND H THROUGH R) ARE FOR LANDSCAPE/OPEN SPACE PURPOSES AND ARE NOT SEPARATE RESIDENTIAL BUILDING SITES.

LOTS 1 AND 2 ARE NOT RESIDENTIAL BUILDING SITES, BUT ARE PRIVATE RECREATION SITES.

() INDICATES MEASURED AND RECORD PER TRACT NO. 15986 M.M. 849/1-15

[] INDICATES MEASURED AND RECORD PER TRACT NO. 16271 M.M. 839/34-45.

LOT G IS NOT A SEPARATE RESIDENTIAL BUILDING SITE.

861- 94

TRACT MAP NO. 16471

IN THE UNINCORPORATED TERRITORY OF THE COUNTY OF ORANGE,
STATE OF CALIFORNIA



HALL & FOREMAN, INC. STEVEN C. SHAMBECK, P.L.S. 6217

APRIL, 2004

BOUNDARY AND INDEX SHEET

SEE SHEET 2 FOR BASIS OF
BEARINGS, DATUM STATEMENT,
MONUMENT NOTES, EASEMENT
NOTES AND NOTES
SEE SHEET 8 FOR CURVE DATA
AND LINE DATA

SHEET 3 OF 8 SHEETS
2 NUMBERED LOTS
19 LETTERED LOTS
23.023 ACRES
PORTION OF VESTING
T.T.M. 15990
DATE OF SURVEY:
JANUARY, 1999

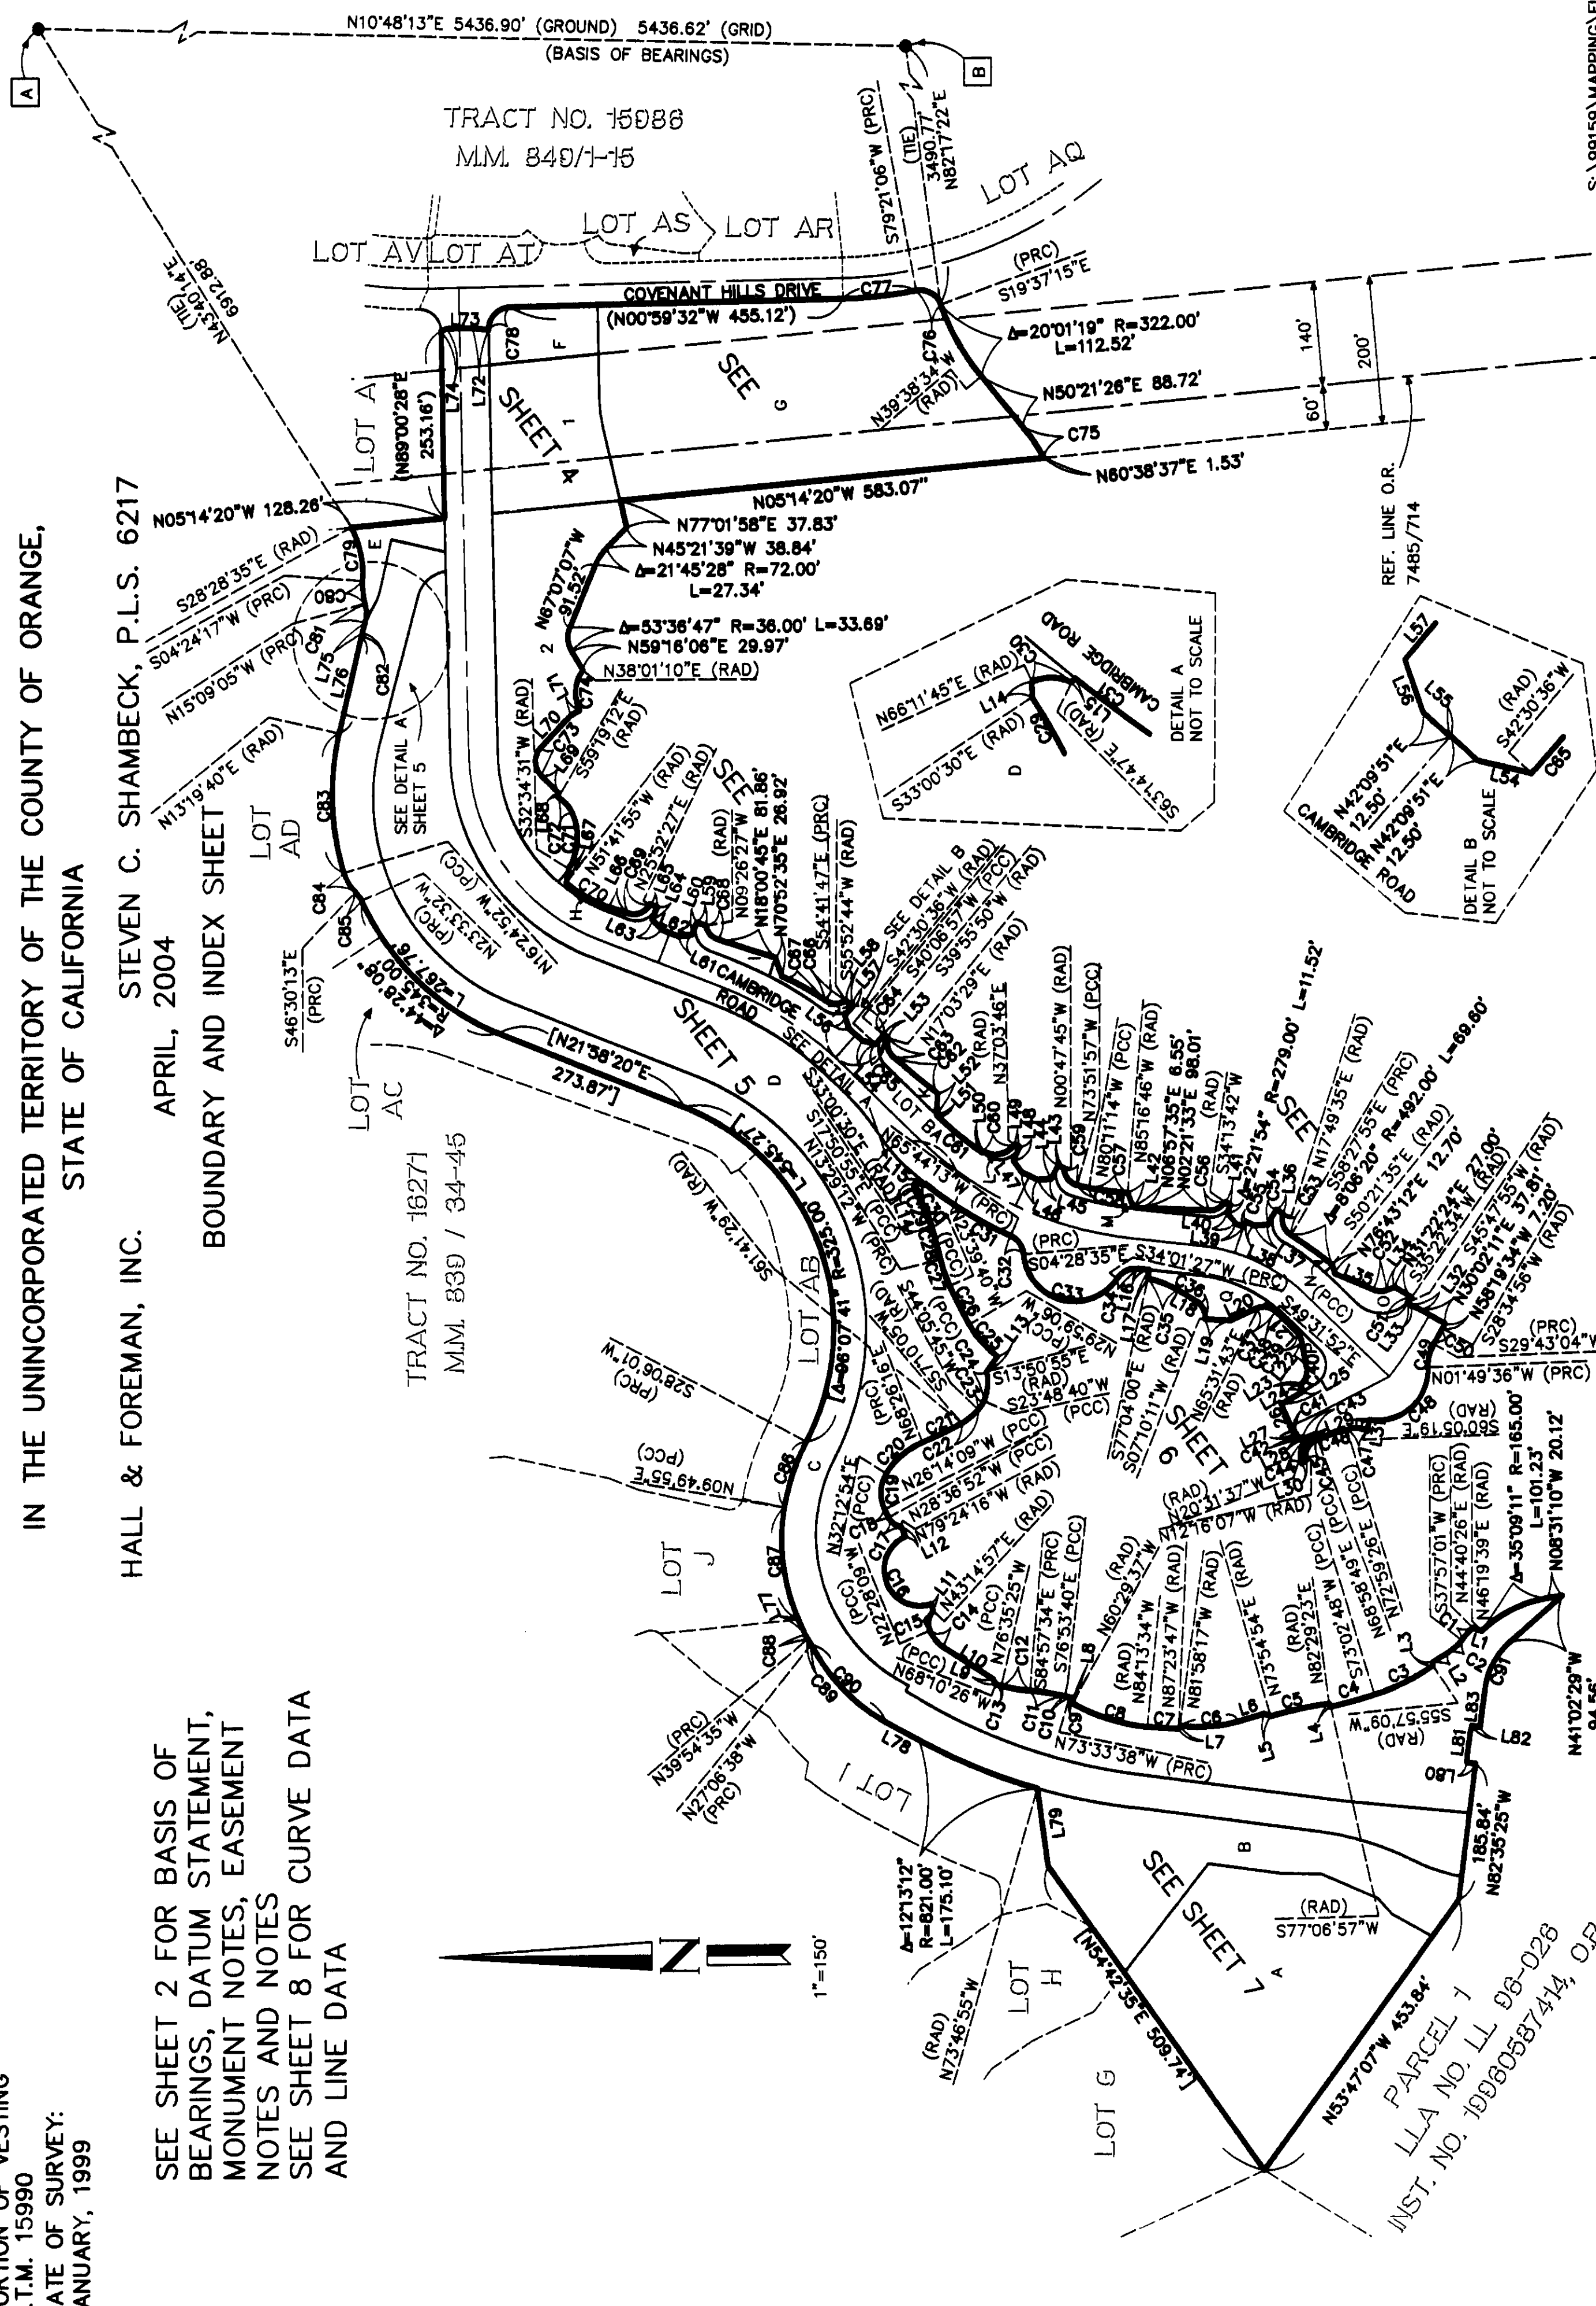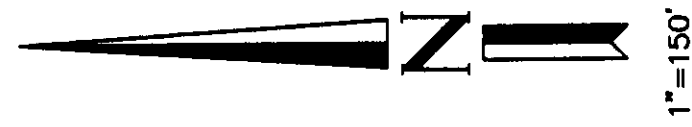

TRACT MAP NO. 16471

HALL & FOREMAN, INC.

SEE SHEET 2 FOR BASIS OF
BEARINGS, DATUM STATEMENT,
MONUMENT NOTES, EASEMENT
NOTES AND NOTES

SEE SHEET 5

LOT D

6.393 ACRES


LOT C
3.193 AC

LOT E
10.143 AC

LOT A

TRACT NO. 15986
M.M. 849/1-15

SEE SHEET 5

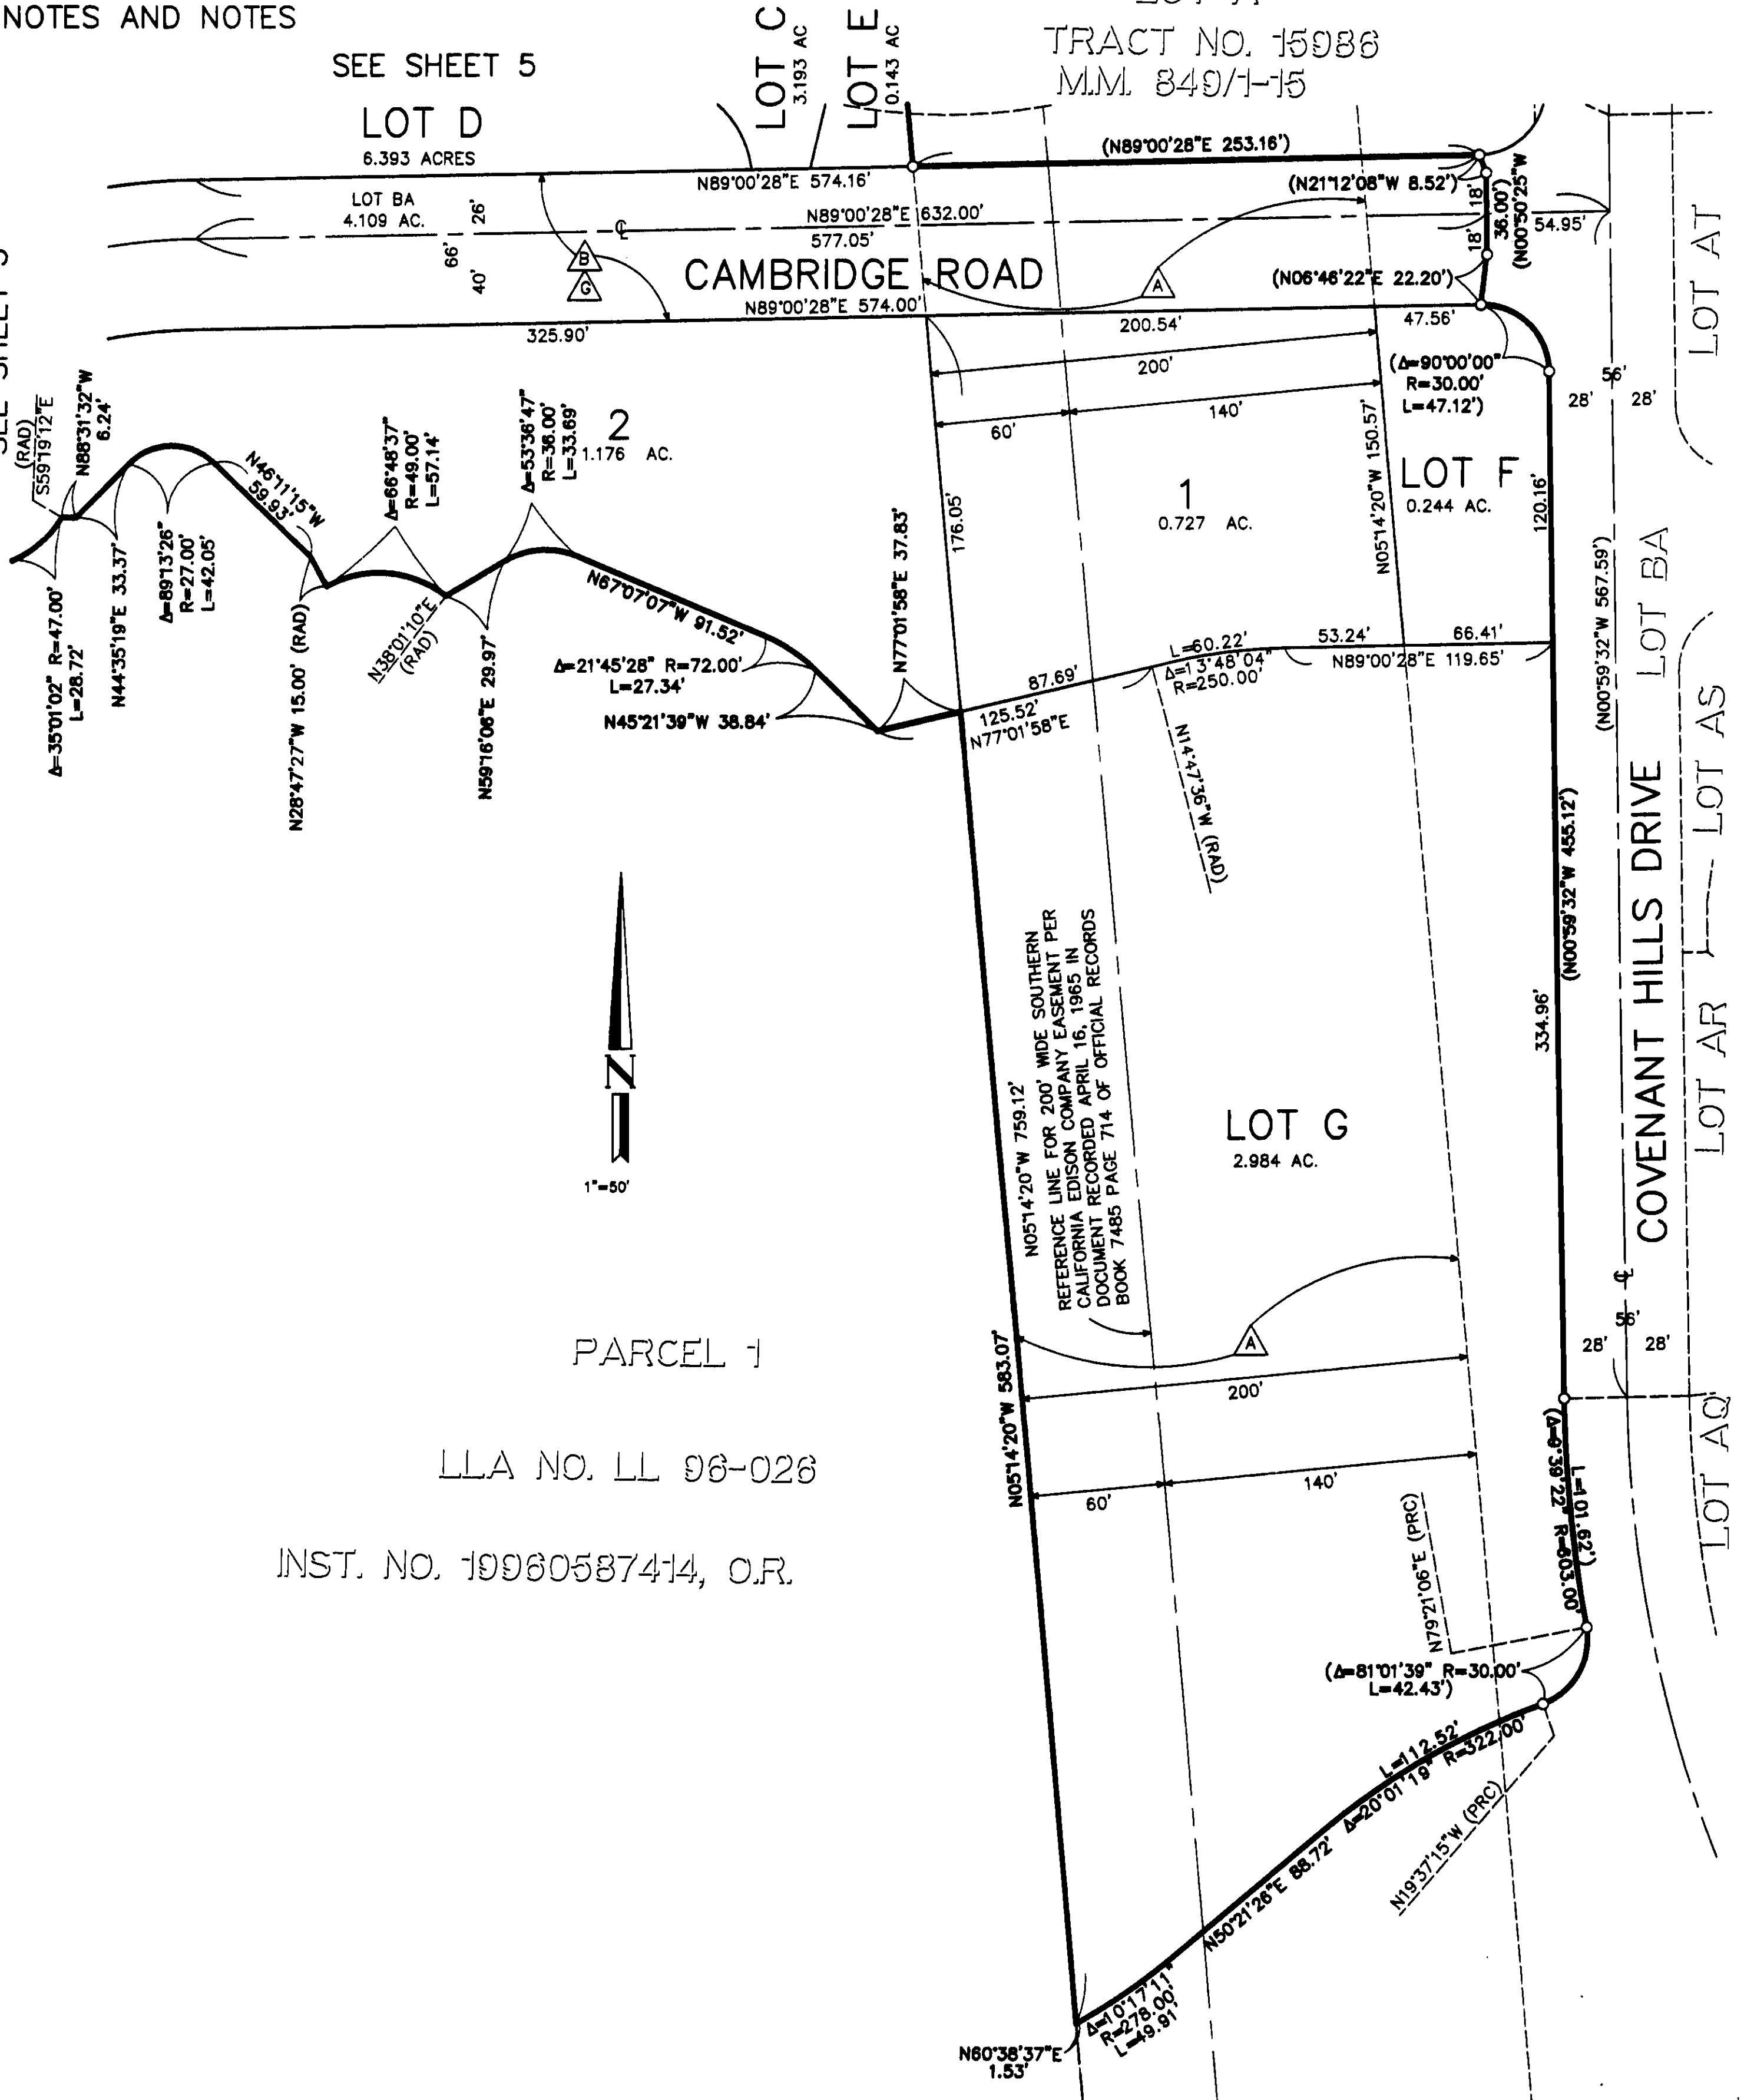

PARCEL 1

LLA NO. LL 96-026

INST. NO. 19960587414, O.R.

JOB NO. 99159-009
S: \\99159\\MAPPING\\FINAL MAPS\\TR16471\\1647104.DWG

861 55

867. 48

SHEET 5 OF 8 SHEETS
2 NUMBERED LOTS
19 LETTERED LOTS
23.023 ACRES
PORTION OF VESTING
T.T.M. 15990
DATE OF SURVEY:
JANUARY, 1999

TRACT MAP NO. 16471


IN THE UNINCORPORATED TERRITORY OF THE COUNTY OF ORANGE,
STATE OF CALIFORNIA

HALL & FOREMAN, INC.

STEVEN C. SHAMBECK, P.L.S. 6217

APRIL, 2004

SEE SHEET 2 FOR BASIS OF
BEARINGS, DATUM STATEMENT,
MONUMENT NOTES, EASEMENT
NOTES AND NOTES

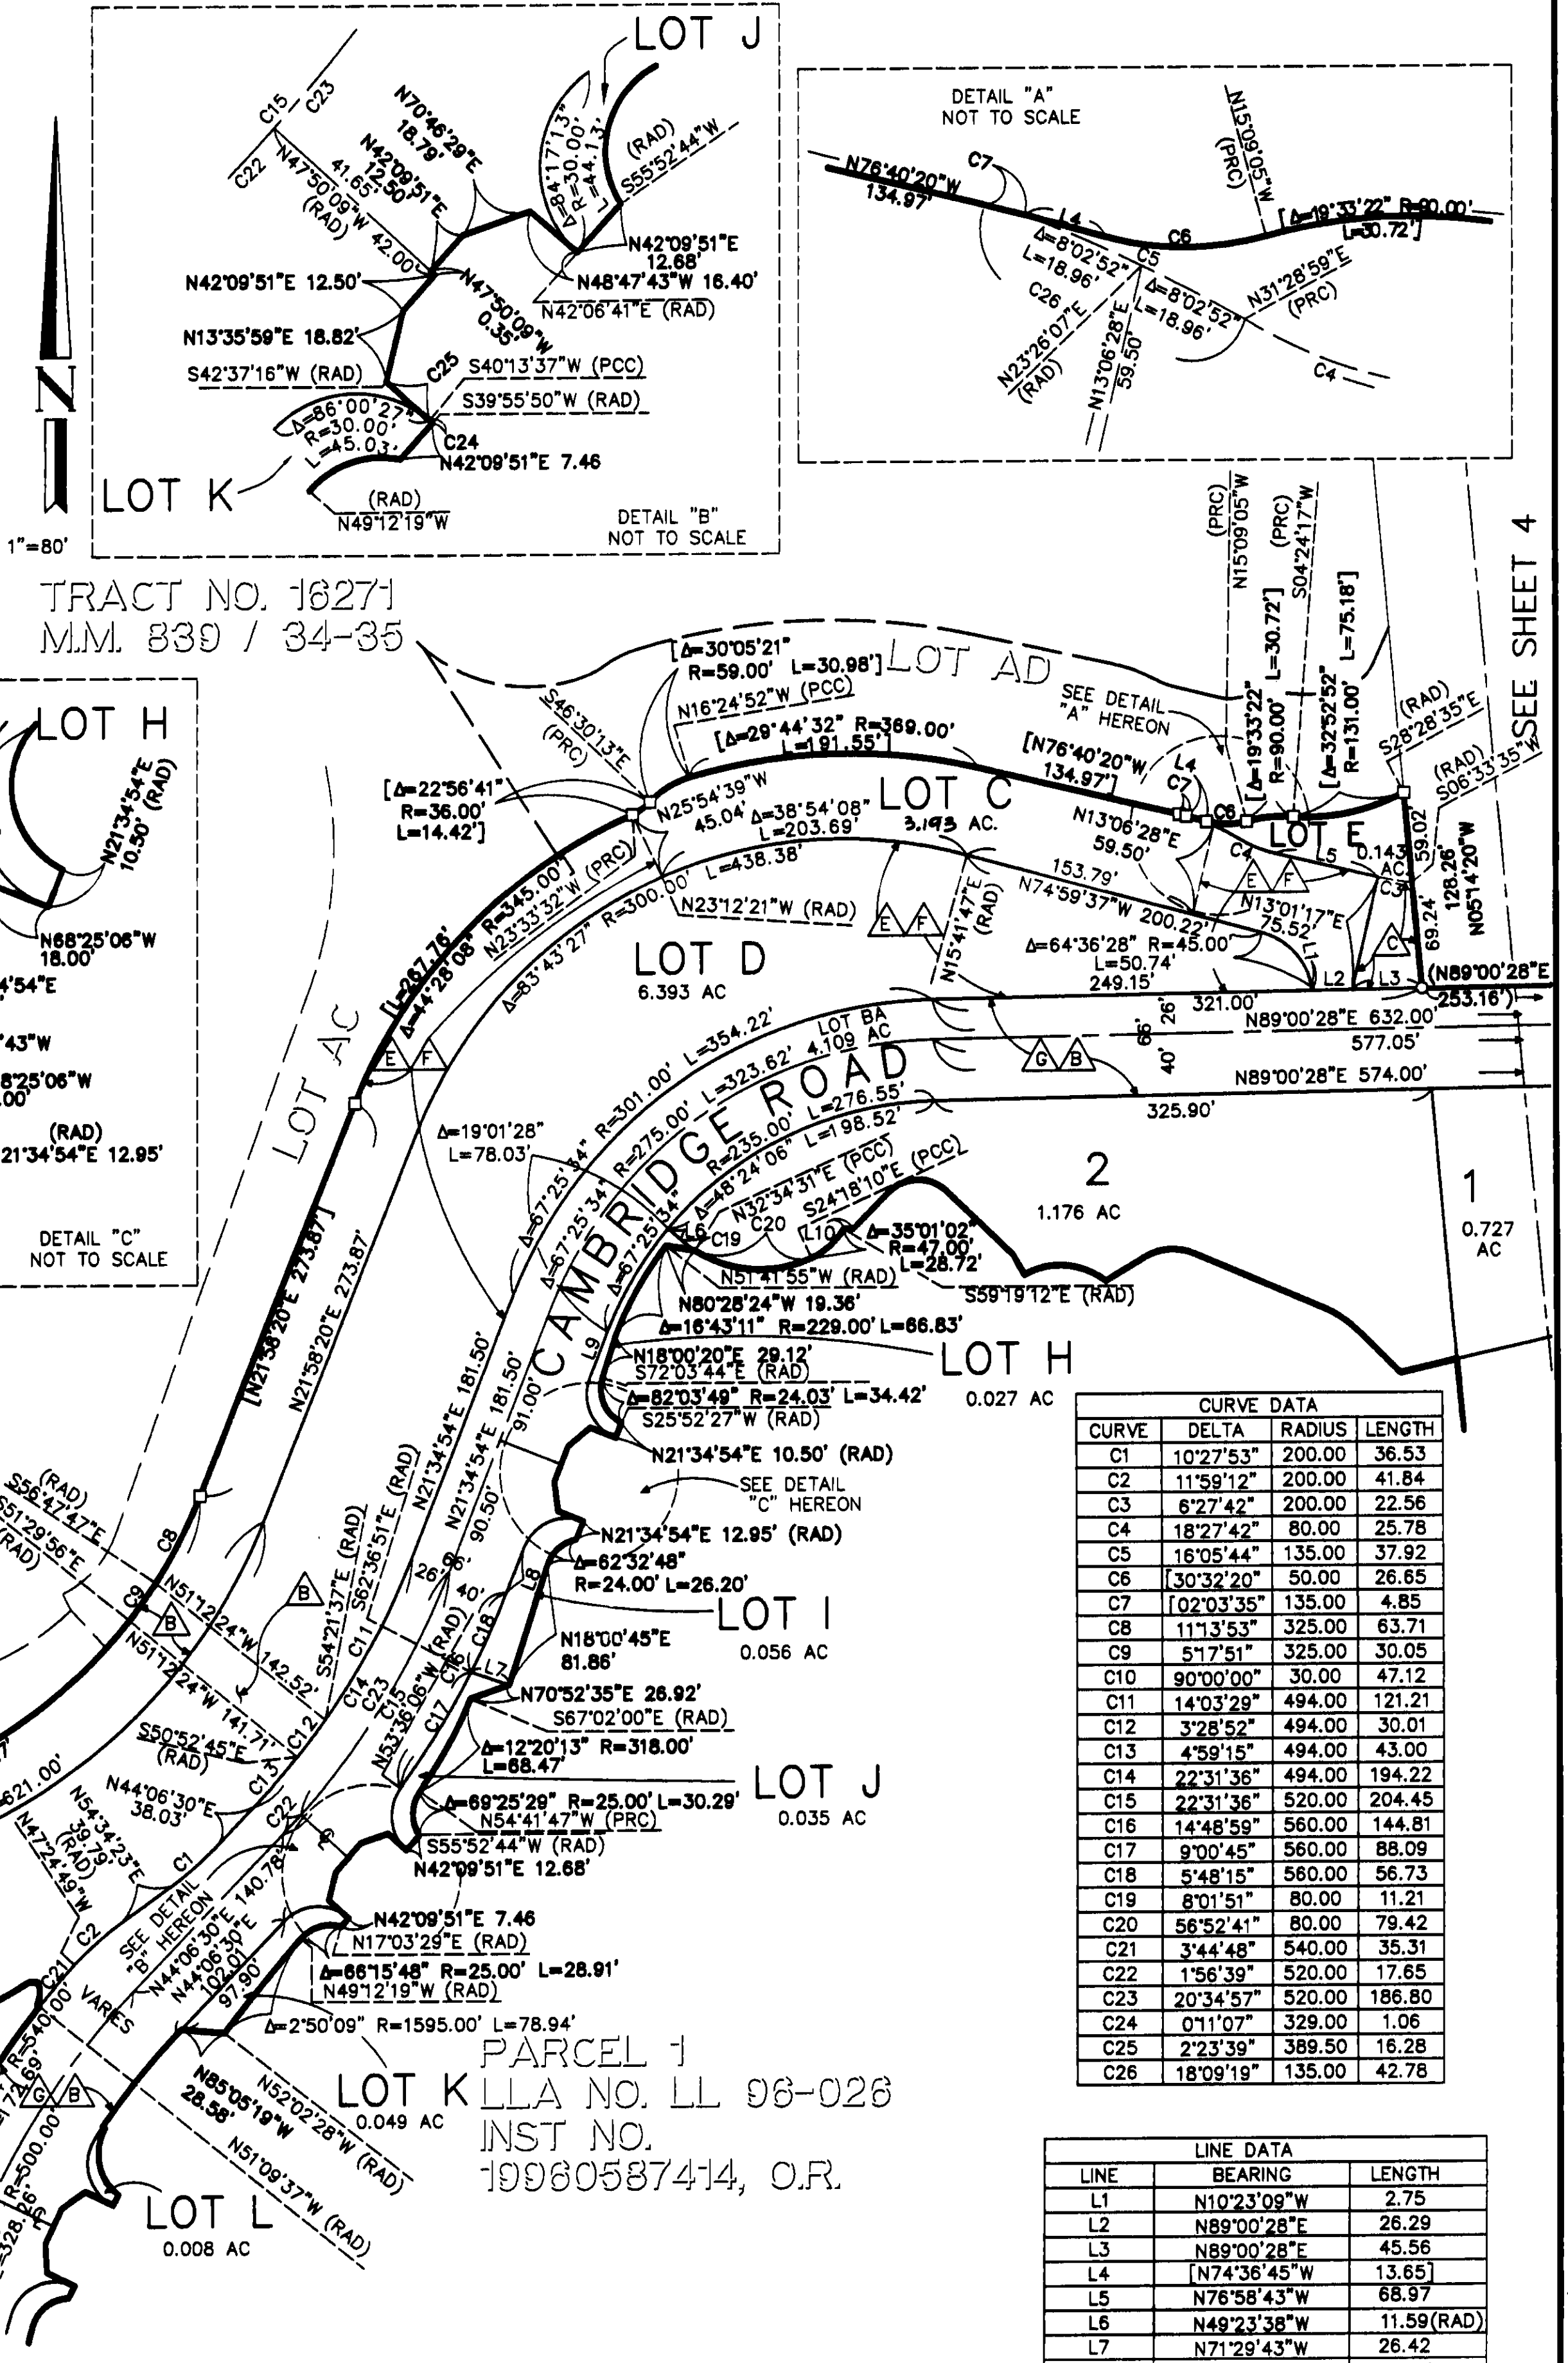

SEE SHEET 6

867. 48

861 47

SHEET 6 OF 8 SHEETS
2 NUMBERED LOTS
19 LETTERED LOTS
23.023 ACRES
PORTION OF VESTING
T.T.M. 15990
DATE OF SURVEY:
JANUARY, 1999

TRACT MAP NO. 16471

IN THE UNINCORPORATED TERRITORY OF THE COUNTY OF ORANGE,
STATE OF CALIFORNIA

HALL & FOREMAN, INC.

STEVEN C. SHAMBECK, P.L.S. 6217
APRIL, 2004


SEE SHEET 2 FOR BASIS OF
BEARINGS, DATUM STATEMENT,
MONUMENT NOTES, EASEMENT
NOTES AND NOTES

SEE SHEET 5

SEE SHEET 7

PARCEL 1
LLA NO. LL 96-026
INST. NO.
19960587414, O.R.

PARCEL 1
LLA NO. LL 96-026
INST. NO.
19960587414, O.R.

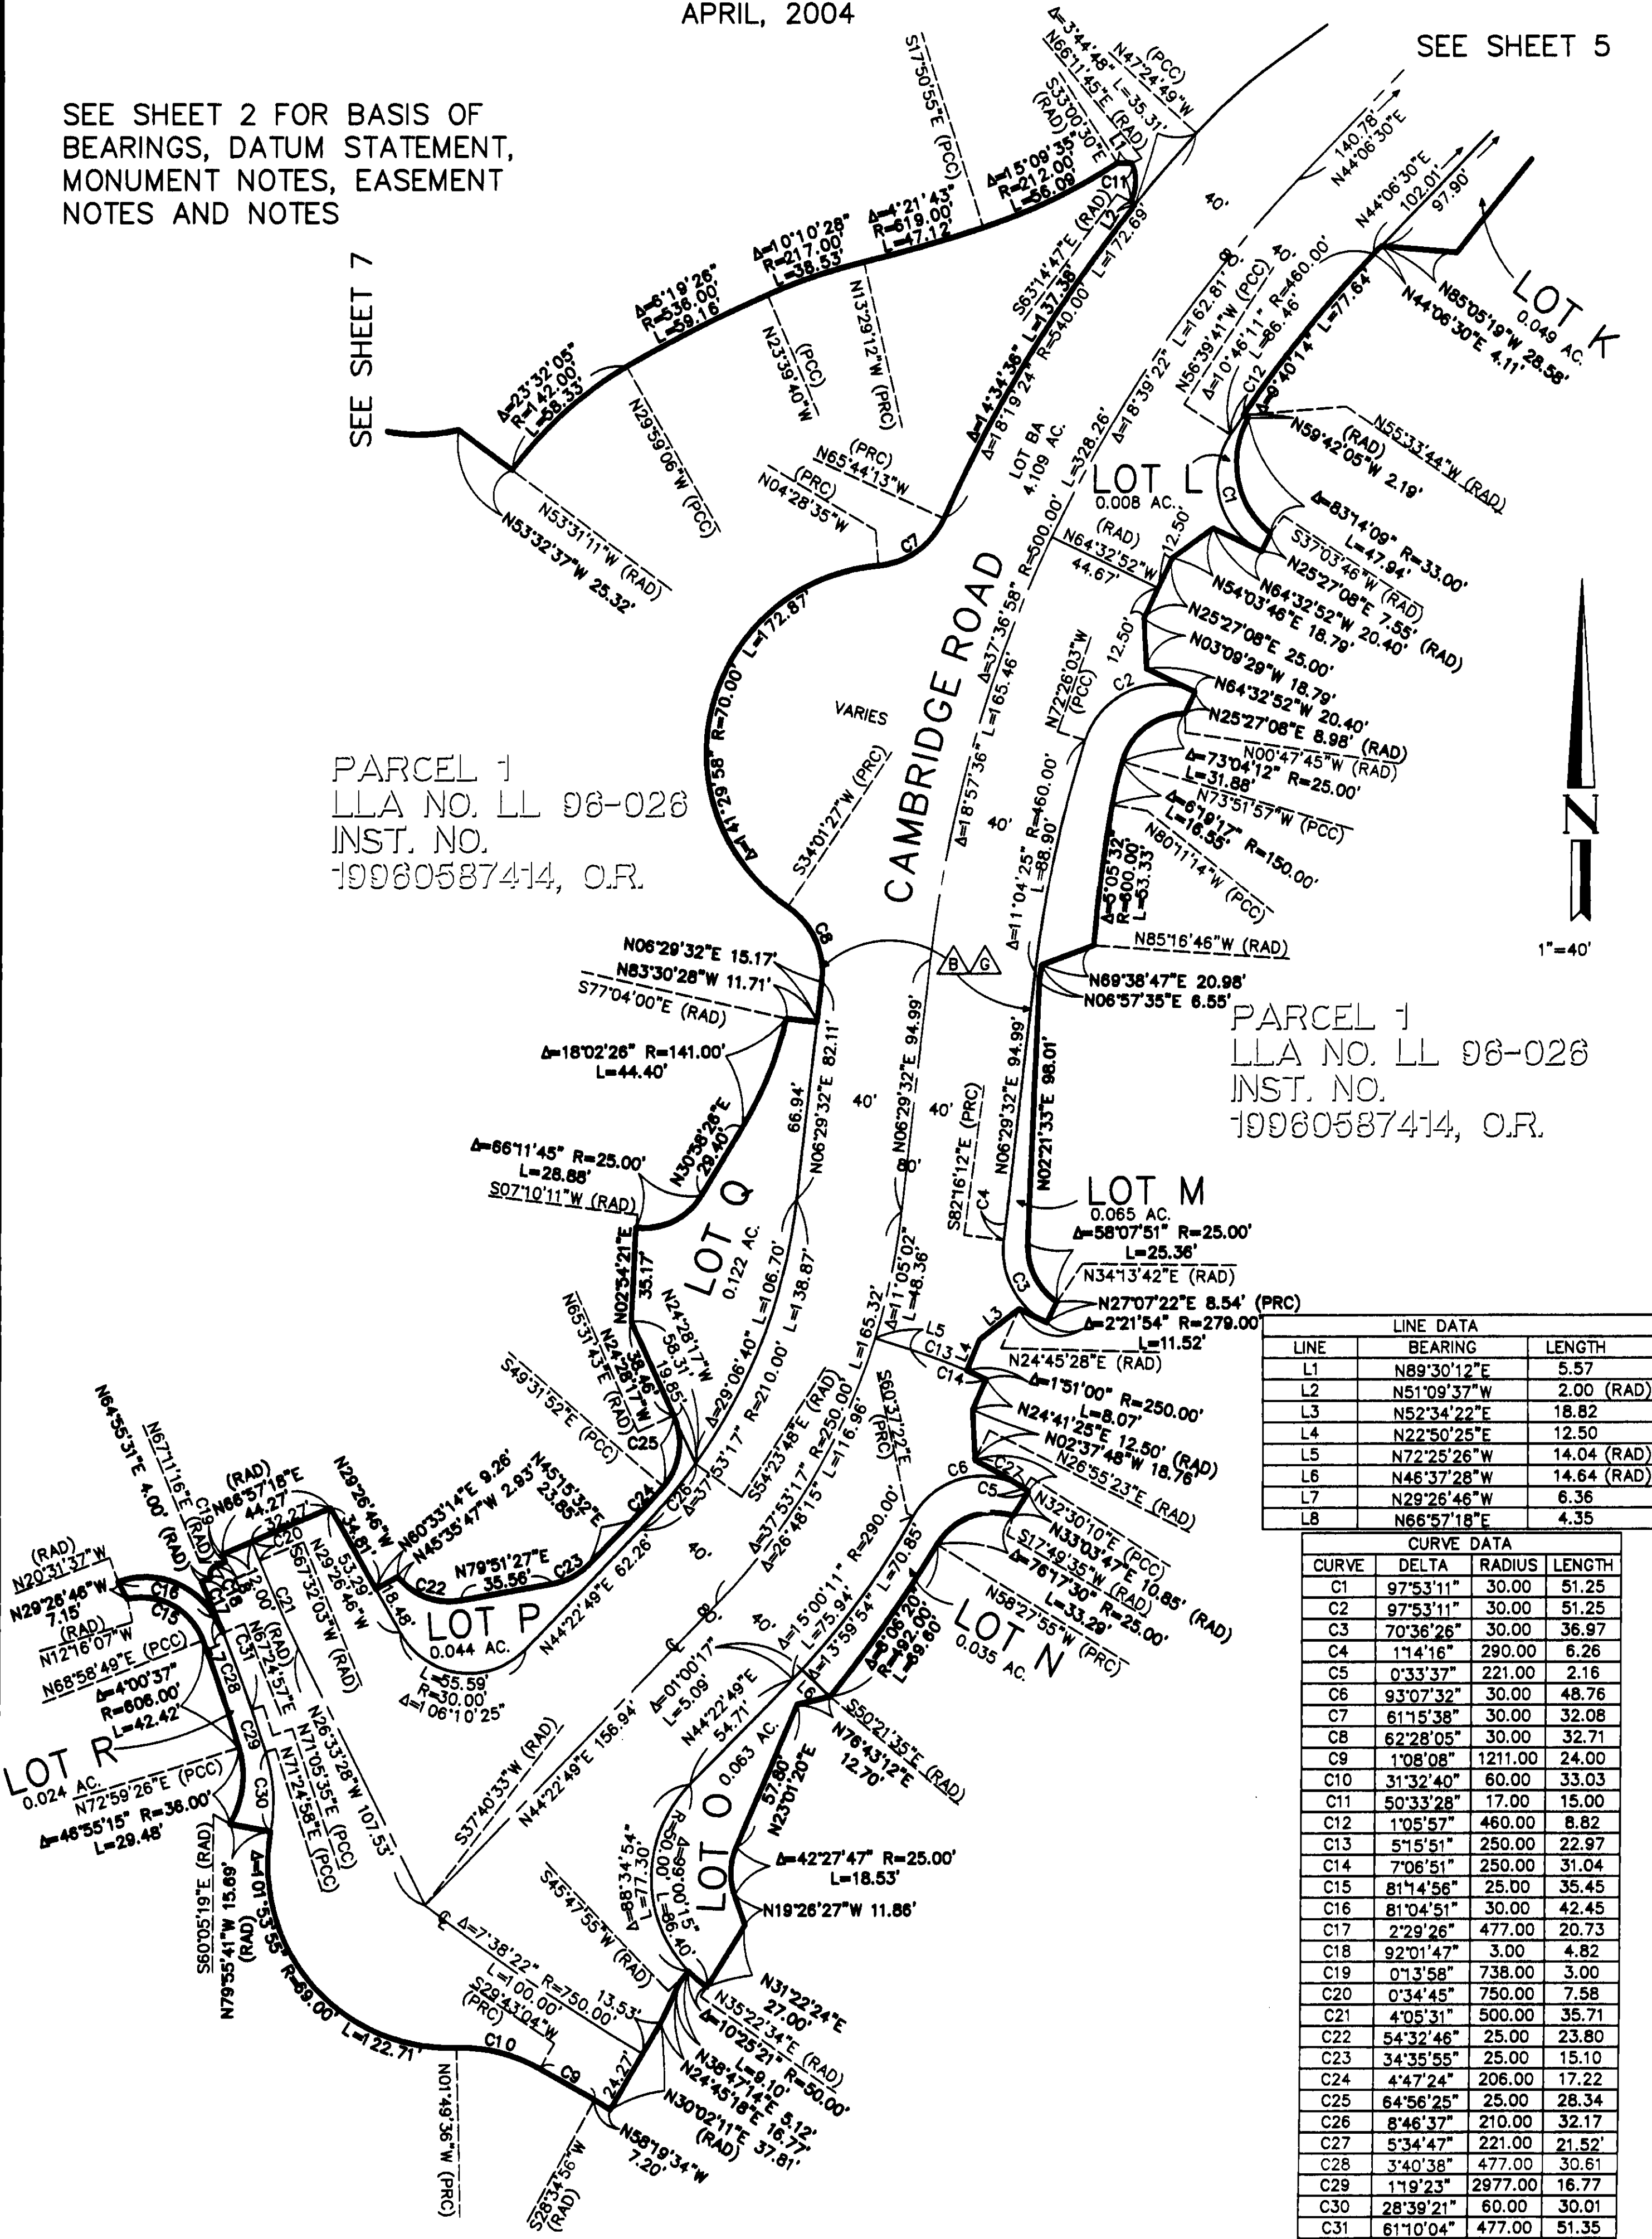

LINE DATA		
LINE	BEARING	LENGTH
L1	N89°30'12"E	5.57
L2	N51°09'37"W	2.00 (RAD)
L3	N52°34'22"E	18.82
L4	N22°50'25"E	12.50
L5	N72°25'26"W	14.04 (RAD)
L6	N46°37'28"W	14.64 (RAD)
L7	N29°26'46"W	6.36
L8	N66°57'18"E	4.35

CURVE DATA			
CURVE	DELTA	RADIUS	LENGTH
C1	97°53'11"	30.00	51.25
C2	97°53'11"	30.00	51.25
C3	70°36'26"	30.00	36.97
C4	1°14'16"	290.00	6.26
C5	0°33'37"	221.00	2.16
C6	93°07'32"	30.00	48.76
C7	61°15'38"	30.00	32.08
C8	62°28'05"	30.00	32.71
C9	1°08'08"	1211.00	24.00
C10	31°32'40"	60.00	33.03
C11	50°33'28"	17.00	15.00
C12	1°05'57"	450.00	8.82
C13	5°15'51"	250.00	22.97
C14	7°06'51"	250.00	31.04
C15	81°14'56"	25.00	35.45
C16	81°04'51"	30.00	42.45
C17	2°29'26"	477.00	20.73
C18	92°01'47"	3.00	4.82
C19	0°13'58"	738.00	3.00
C20	0°34'45"	750.00	7.58
C21	4°05'31"	500.00	35.71
C22	54°32'46"	25.00	23.80
C23	34°35'55"	25.00	15.10
C24	4°47'24"	206.00	17.22
C25	64°56'25"	25.00	28.34
C26	8°46'37"	210.00	32.17
C27	5°34'47"	221.00	21.52
C28	3°40'38"	477.00	30.61
C29	1°19'23"	2977.00	16.77
C30	28°39'21"	60.00	30.01
C31	61°10'04"	477.00	51.35

861 47

861 48

SHEET 7 OF 8 SHEETS
2 NUMBERED LOTS
19 LETTERED LOTS
23.023 ACRES
PORTION OF VESTING
T.T.M. 15990
DATE OF SURVEY:
JANUARY, 1999

TRACT MAP NO. 16471

IN THE UNINCORPORATED TERRITORY OF THE COUNTY OF ORANGE,
STATE OF CALIFORNIA


HALL & FOREMAN, INC.

STEVEN C. SHAMBECK, P.L.S. 6217


APRIL, 2004

SEE SHEET 2 FOR BASIS OF
BEARINGS, DATUM STATEMENT,
MONUMENT NOTES, EASEMENT
NOTES AND NOTES

CURVE DATA			
CURVE	DELTA	RADIUS	LENGTH
C1	12°47'57"	40.00	8.94
C2	15°57'02"	25.00	6.96
C3	20°17'05"	40.00	14.16
C4	13°04'20"	127.00	28.98
C5	36°13'22"	105.00	66.38
C6	58°27'03"	50.00	51.01
C7	50°47'24"	25.00	22.16
C9	34°53'28"	49.00	29.84
C10	83°29'14"	49.00	71.40
C11	35°39'36"	49.00	30.50
C12	55°37'11"	49.00	47.57
C13	8°22'09"	271.00	39.58
C14	8°03'54"	344.00	48.42
C15	9°47'40"	30.00	5.13
C16	23°43'57"	260.00	107.69
C17	3°10'13"	779.00	43.10
C18	23°42'08"	196.00	81.08
C19	8°34'29"	551.00	82.46
C20	17°05'39"	300.00	89.50
C21	20°56'21"	62.00	22.66
C22	6°43'25"	195.00	22.88
C23	11°08'18"	300.00	58.32
C24	2°56'17"	300.00	15.38
C25	4°04'09"	871.00	61.86
C26	43°38'24"	37.50	28.56
C27	43°38'24"	52.50	39.99
C28	15°09'16"	270.00	71.41
C29	174°46'01"	49.00	149.46
C30	0°45'10"	40.00	0.53
C31	12°02'47"	40.00	8.41
C32	36°58'51"	250.00	161.36
C33	8°24'59"	53.00	7.79
C34	65°43'06"	25.00	28.68
C35	2°22'43"	300.00	12.45
C36	37°39'35"	62.00	40.75
C37	3°20'02"	108.00	6.28
C38	89°51'33"	17.00	26.66

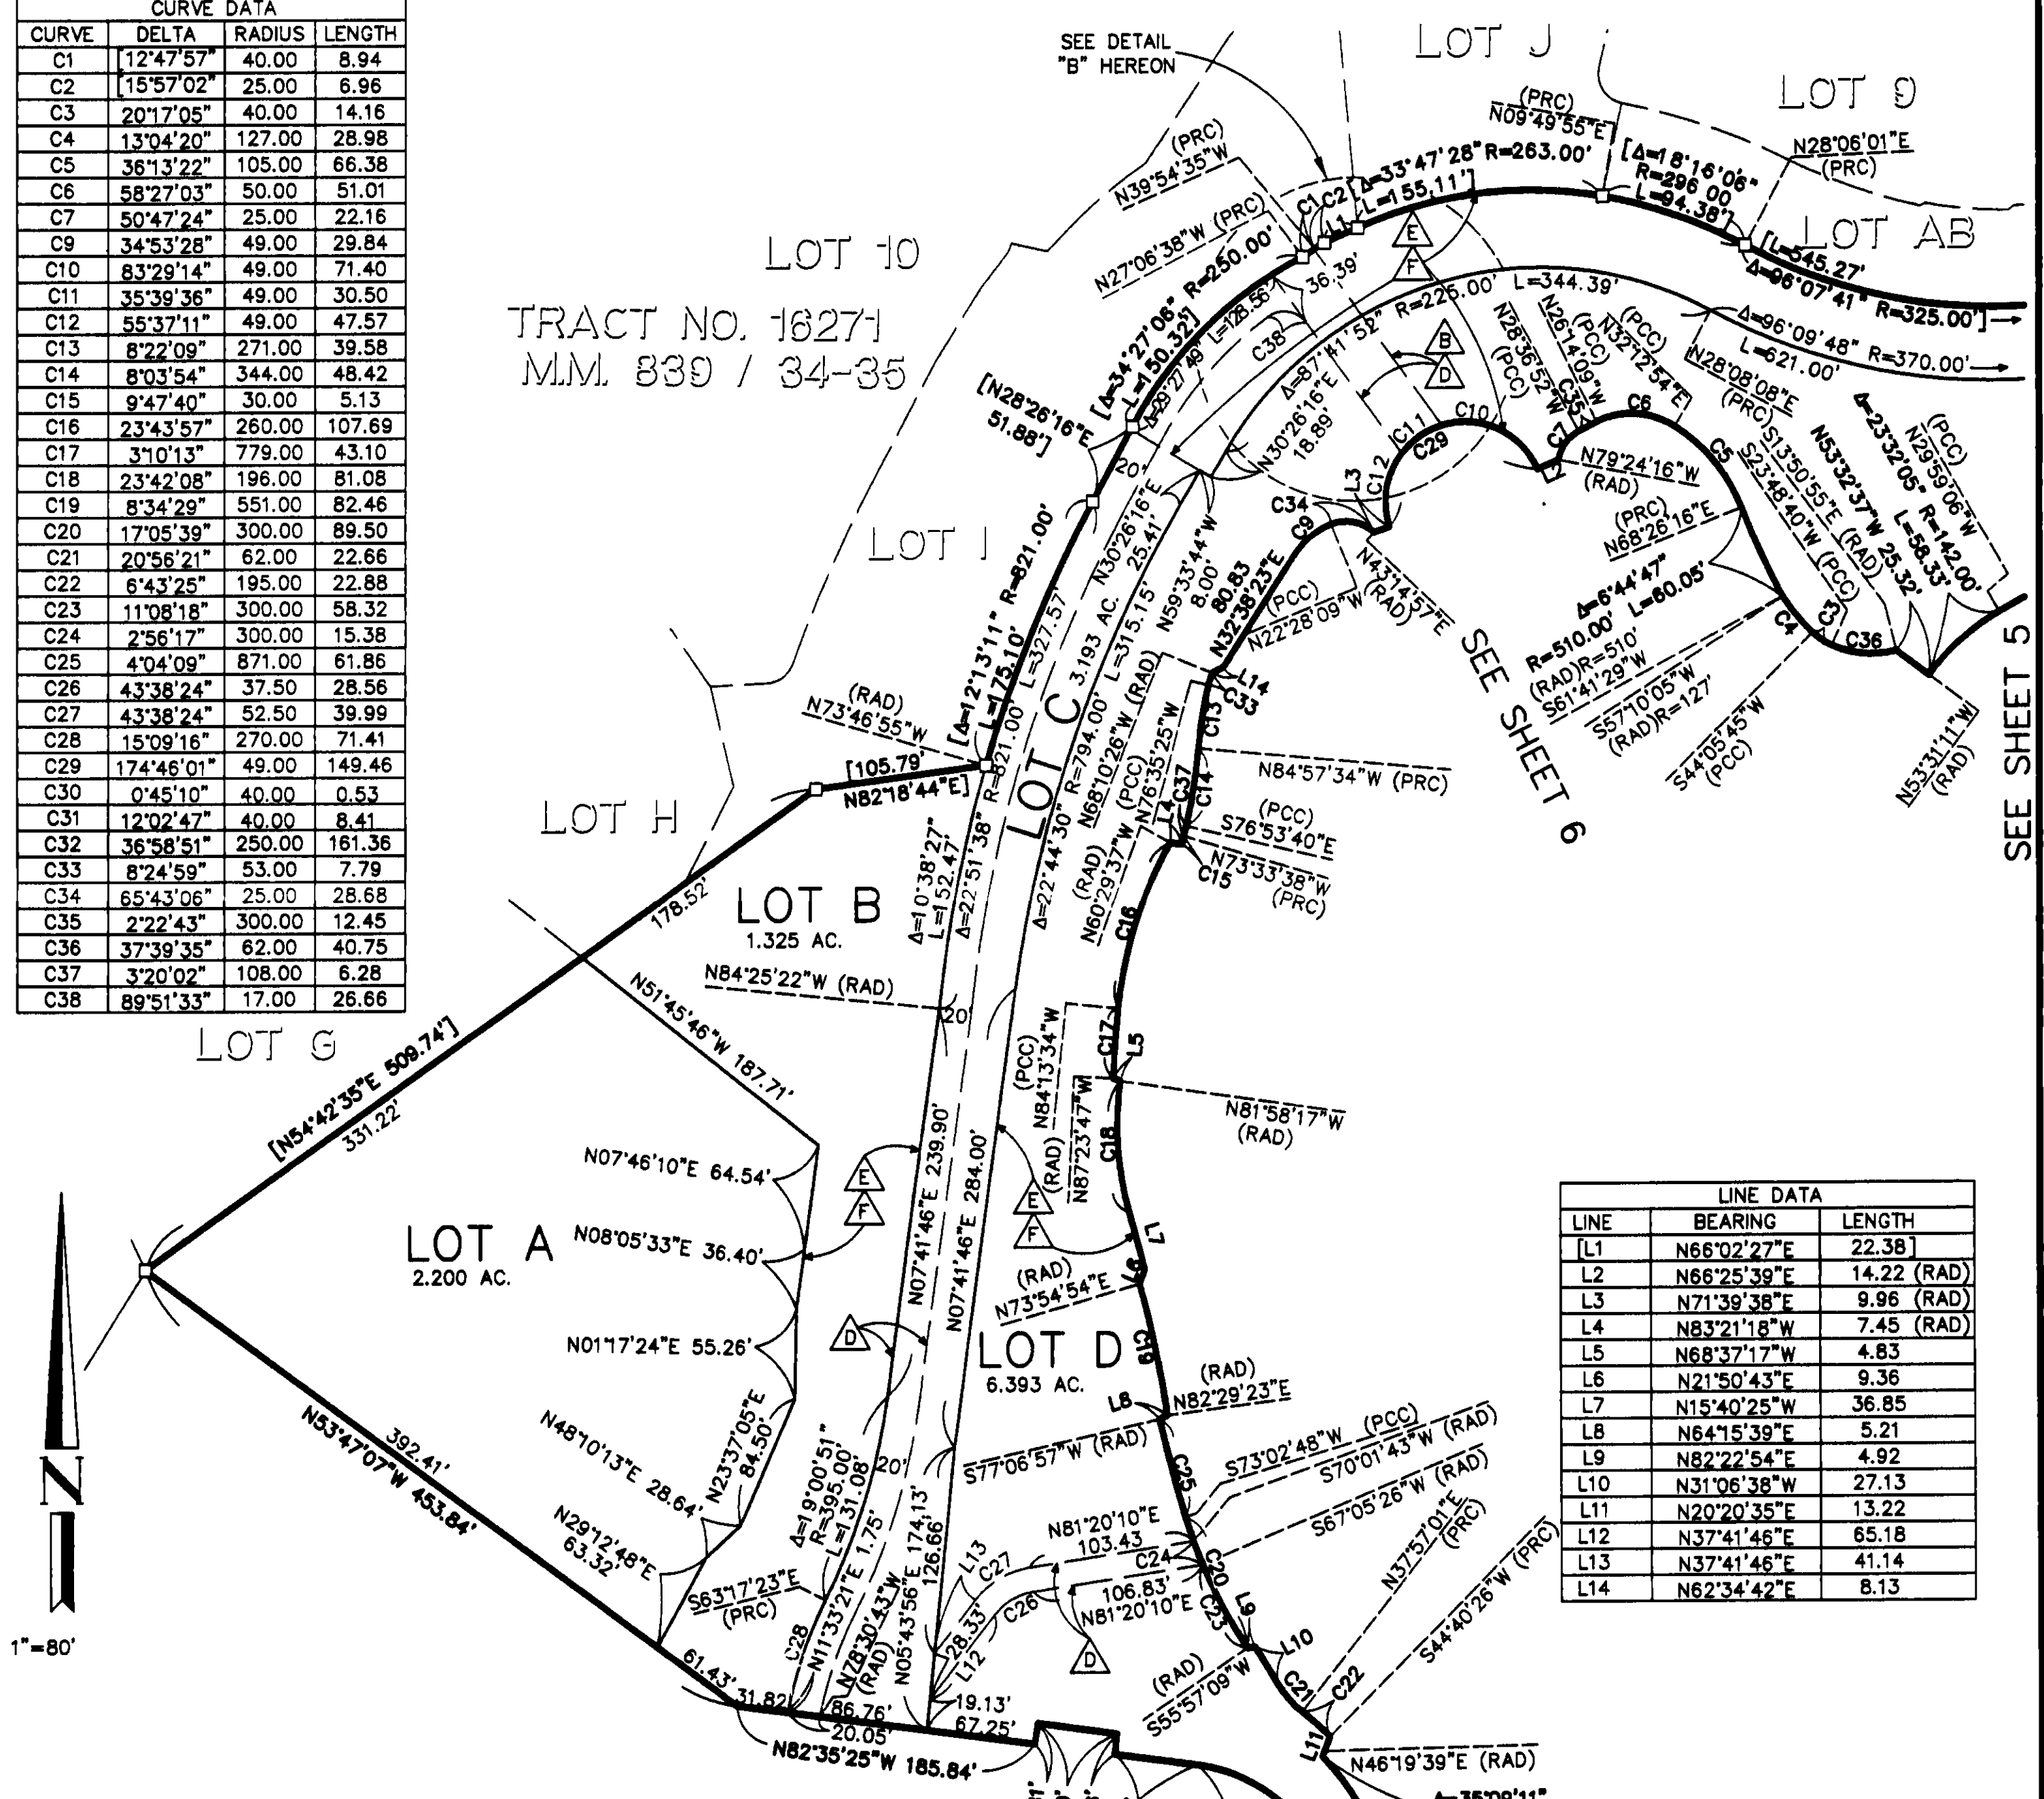

LINE DATA		
LINE	BEARING	LENGTH
L1	N66°02'27"E	22.38
L2	N66°25'39"E	14.22 (RAD)
L3	N71°39'38"E	9.96 (RAD)
L4	N83°21'18"W	7.45 (RAD)
L5	N68°37'17"W	4.83
L6	N21°50'43"E	9.36
L7	N15°40'25"W	36.85
L8	N64°15'39"E	5.21
L9	N82°22'54"E	4.92
L10	N31°06'38"W	27.13
L11	N20°20'35"E	13.22
L12	N37°41'46"E	65.18
L13	N37°41'46"E	41.14
L14	N62°34'42"E	8.13

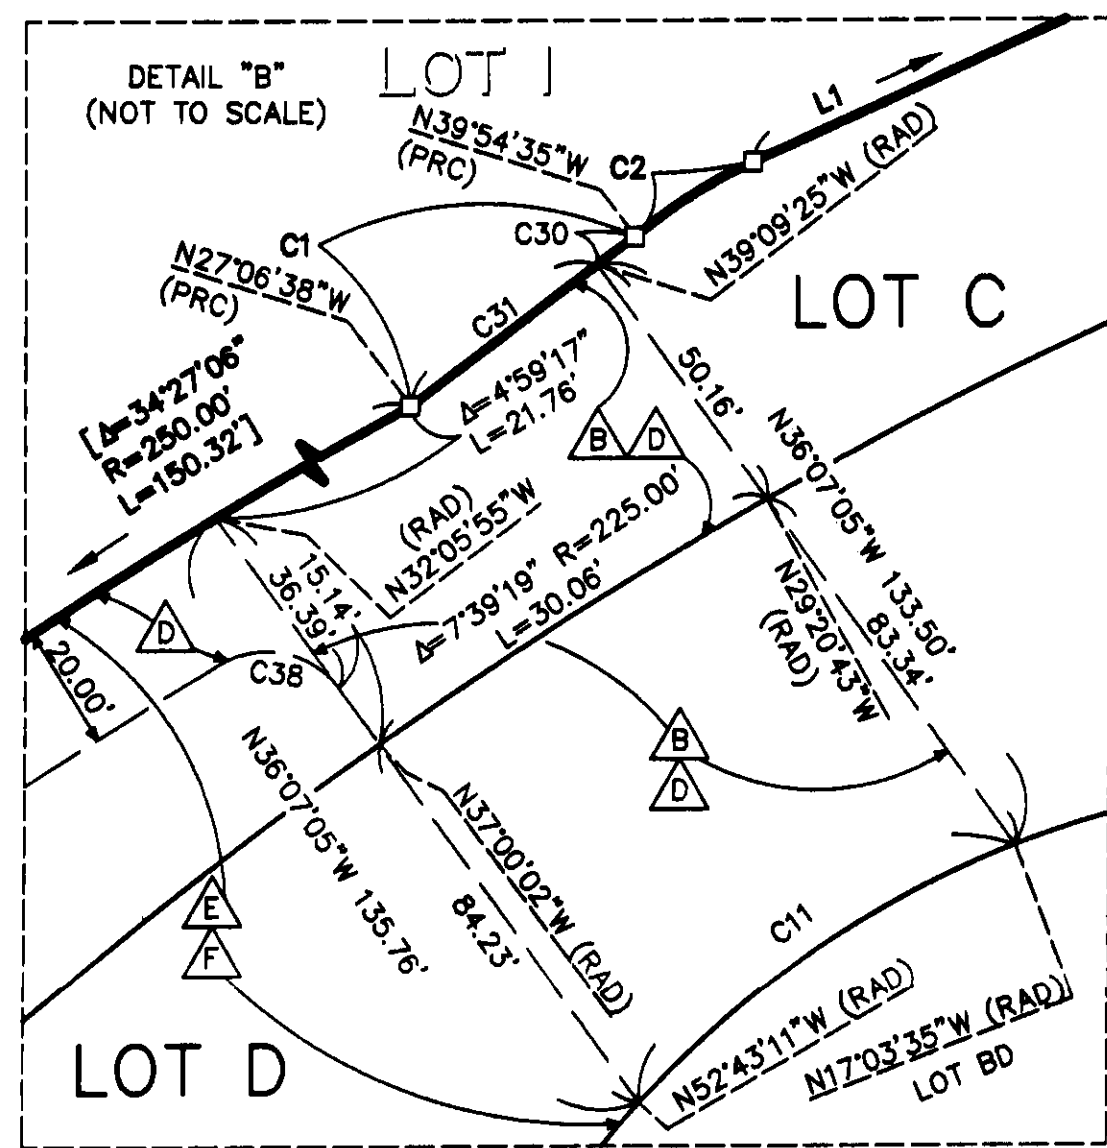

PARCEL 1

LLA NO. LL 06-026

INST. NO. 10080587414, O.R.

861-48

SHEET 8 OF 8 SHEETS
2 NUMBERED LOTS
19 LETTERED LOTS
23.023 ACRES
PORTION OF VESTING
T.T.M. 15990
DATE OF SURVEY:
JANUARY, 1999

TRACT MAP NO. 16471

IN THE UNINCORPORATED TERRITORY OF THE COUNTY OF ORANGE,
STATE OF CALIFORNIA

HALL & FOREMAN, INC.

STEVEN C. SHAMBECK, P.L.S. 6217
APRIL, 2004

SEE SHEET 2 FOR BASIS OF
BEARINGS, DATUM STATEMENT,
MONUMENT NOTES, EASEMENT
NOTES AND NOTES

DATA FROM SHEET NO. 3

CURVE DATA			
CURVE	DELTA	RADIUS	LENGTH
C1	6°43'25"	195.00	22.88
C2	20°56'21"	62.00	22.66
C3	17°05'39"	300.00	89.50
C4	4°04'09"	871.00	61.86
C5	8°34'29"	551.00	82.46
C6	23°42'08"	196.00	81.08
C7	3°10'13"	779.00	43.10
C8	23°43'57"	260.00	107.69
C9	9°47'40"	30.00	5.13
C10	3°20'02"	108.00	6.28
C11	8°03'54"	344.00	48.42
C12	8°22'09"	271.00	39.58
C13	8°24'59"	53.00	7.79
C14	34°53'28"	49.00	29.84
C15	65°43'06"	25.00	28.68
C16	174°46'01"	49.00	149.46
C17	50°47'24"	25.00	22.16
C18	2°22'43"	300.00	12.45
C19	58°27'03"	50.00	51.01
C20	36°13'22"	105.00	66.38
C21	6°44'47"	510.00	60.05
C22	13°04'20"	127.00	28.98
C23	20°17'05"	40.00	14.16
C24	37°39'35"	62.00	40.75
C25	23°32'05"	142.00	58.33
C26	6°19'26"	536.00	59.16
C27	10°10'28"	217.00	38.53
C28	4°21'43"	619.00	47.12
C29	15°09'35"	212.00	56.09
C30	50°33'28"	17.00	15.00
C31	14°34'36"	540.00	137.38
C32	61°15'38"	30.00	32.08
C33	141°29'58"	70.00	172.87
C34	62°28'05"	30.00	32.71
C35	18°02'26"	141.00	44.40
C36	66°11'45"	25.00	28.88
C37	64°56'25"	25.00	28.34
C38	4°47'24"	206.00	17.22
C39	34°35'55"	25.00	15.10
C40	54°32'46"	25.00	23.80
C41	0°13'58"	738.00	3.00
C42	92°01'47"	3.00	4.82
C43	2°29'26"	477.00	20.73
C44	81°04'51"	30.00	42.45
C45	81°14'56"	25.00	35.45
C46	4°00'37"	606.00	42.42
C47	46°55'15"	36.00	29.48
C48	101°53'55"	69.00	122.71
C49	31°32'40"	60.00	33.03
C50	1°08'08"	1211.00	24.00
C51	10°25'21"	50.00	9.10
C52	42°27'47"	25.00	18.53
C53	76°17'30"	25.00	33.29
C54	6°08'24"	221.00	23.68
C55	1°51'00"	250.00	8.07
C56	58°07'51"	25.00	25.36
C57	5°05'32"	600.00	53.33
C58	6°19'17"	150.00	16.55
C59	73°04'12"	25.00	31.88
C60	83°14'09"	33.00	47.94
C61	9°40'14"	460.00	77.64
C62	2°50'09"	1595.00	78.94
C63	66°15'48"	25.00	28.91
C64	0°11'07"	329.00	1.06
C65	2°23'39"	389.50	16.28
C66	69°25'29"	25.00	30.29
C67	12°20'13"	318.00	68.47
C68	62°32'48"	24.00	26.20
C69	82°03'49"	24.03	34.42
C70	16°43'11"	229.00	66.82
C71	56°52'41"	80.00	79.42
C72	35°01'02"	47.00	28.72
C73	89°13'26"	27.00	42.05
C74	66°48'37"	49.00	57.14
C75	10°17'11"	278.00	49.91
C76	81°01'39"	30.00	42.43
C77	9°39'22"	603.00	101.62
C78	90°00'00"	30.00	47.12
C79	32°52'52"	131.00	75.18
C80	19°33'22"	90.00	30.72
C81	30°32'20"	50.00	26.65
C82	2°03'35"	135.00	4.85
C83	29°44'32"	369.00	191.55
C84	30°05'21"	59.00	30.98
C85	22°56'41"	36.00	14.42
C86	18°16'06"	296.00	94.38
C87	33°47'28"	263.00	155.11
C88	15°57'02"	25.00	6.96
C89	12°47'57"	40.00	8.94
C90	34°27'06"	250.00	150.32
C91	41°32'56"	100.00	72.52

LINE DATA		
LINE	BEARING	LENGTH
L1	N20°20'35"E	13.22
L2	N31°06'38"W	27.13
L3	N82°22'54"E	4.92
L4	N64°15'39"E	5.21
L5	N21°50'43"E	9.36
L6	N15°40'25"W	36.85
L7	N68°37'17"W	4.83
L8	N83°21'18"W	7.45 (RAD)
L9	N62°34'42"E	8.13
L10	N32°38'23"E	80.83
L11	N71°39'38"E	9.96 (RAD)
L12	N66°25'39"E	14.22 (RAD)
L13	N53°32'37"W	25.32
L14	N89°30'12"E	5.57
L15	N51°09'37"W	2.00 (RAD)
L16	N06°29'32"E	15.17
L17	N83°30'28"W	11.71
L18	N30°58'26"E	29.40
L19	N02°54'21"E	35.17
L20	N24°28'17"W	38.46
L21	N45°15'32"E	23.85
L22	N79°51'27"E	35.56
L23	N45°35'47"W	2.93
L24	N60°33'14"E	9.26
L25	N29°26'46"W	34.81
L26	N66°57'18"E	44.27
L27	N66°57'18"E	4.35
L28	N64°55'31"E	4.00 (RAD)
L29	N29°26'46"W	6.36
L30	N29°26'46"W	7.15
L31	N79°55'41"W	15.69
L32	N24°45'18"E	16.77
L33	N38°47'14"E	5.12
L34	N19°26'27"W	11.86
L35	N23°01'20"E	57.80
L36	N33°03'47"E	10.85
L37	N02°37'48"W	18.76
L38	N24°41'25"E	12.50 (RAD)
L39	N22°50'25"E	12.50 (RAD)
L40	N52°34'22"E	18.82
L41	N27°07'22"E	8.54
L42	N69°38'47"E	20.98
L43	N25°27'08"E	8.98
L44	N64°32'52"W	20.40
L45	N03°09'29"W	18.79
L46	N25°27'08"E	25.00
L47	N54°03'46"E	18.79
L48	N64°32'52"W	20.40
L49	N25°27'08"E	7.55
L50	N59°42'05"W	2.19
L51	N44°06'30"E	4.11
L52	N85°05'19"W	28.58
L53	N42°09'51"E	7.46
L54	N13°35'59"E	18.82
L55	N47°50'09"W	0.35
L56	N70°46'29"E	18.79
L57	N48°47'43"W	16.40
L58	N42°09'51"E	12.68
L59	N21°34'54"E	12.95
L60	N68°25'06"W	18.00
L61	N07°01'43"W	18.79
L62	N21°34'54"E	25.00
L63	N50°11'32"E	18.79
L64	N68°25'06"W	18.00
L65	N21°34'54"E	10.50
L66	N18°00'20"E	29.12
L67	N80°28'24"W	19.36
L68	N88°31'32"W	6.24
L69	N44°35'19"E	33.37
L70	N46°11'15"W	59.93
L71	N28°47'27"W	15.00 (RAD)
L72	(N06°46'22"E	22.20)
L73	(N00°50'25"W	36.00)
L74	(N21°12'08"W	8.52)
L75	N74°36'45"W	13.65
L76	N76°40'20"W	134.97
L77	N66°02'27"E	22.38
L78	N28°26'16"E	51.88
L79	N82°18'44"E	105.79
L80	N07°41'46"E	12.81
L81	N82°18'14"W	50.00
L82	N07°41'46"E	12.56
L83	N82°35'25"W	51.95