

SHEET 2 OF 10 SHEETS
68 NUMBERED LOTS
6 LETTERED LOTS
19.486 ACRES
PORTION OF VESTING
T.T.M. 15990
DATE OF SURVEY:
JANUARY, 1999

TRACT MAP NO. 16472

IN THE UNINCORPORATED TERRITORY OF THE COUNTY OF ORANGE,
STATE OF CALIFORNIA

HALL & FOREMAN, INC.

STEVEN C. SHAMBECK, P.L.S. 6217
MAY, 2004

SANTA MARGARITA WATER DISTRICT

STATE OF CALIFORNIA)
COUNTY OF ORANGE)

ON THIS 20th DAY OF SEPT. 2004, BEFORE ME, CINDY R. LANE
A NOTARY PUBLIC IN AND FOR SAID STATE, PERSONALLY APPEARED DANIEL R.
FERONS PERSONALLY KNOWN TO ME OR PROVED TO ME ON THE BASIS OF SATISFACTORY
EVIDENCE TO BE THE PERSON WHOSE NAME IS SUBSCRIBED TO THE WITHIN INSTRUMENT
AND ACKNOWLEDGED TO ME THAT HE EXECUTED THE SAME IN HIS AUTHORIZED CAPACITY,
AND THAT BY HIS SIGNATURE ON THE INSTRUMENT THE PERSON OR THE ENTITY UPON
BEHALF OF WHICH THE PERSON ACTED, EXECUTED THE INSTRUMENT.

WITNESS MY HAND:

MY COMMISSION EXPIRES 2-20-05

Cindy R. Lane
NOTARY PUBLIC IN AND FOR SAID STATE

MY PRINCIPAL PLACE OF BUSINESS
IS IN ORANGE COUNTY

CINDY R. LANE
PRINT NAME

AUTOMATIC FIRE SPRINKLER NOTE:
ALL MULTIFAMILY RESIDENTIAL STRUCTURES; ALL SINGLE FAMILY STRUCTURES EXCEEDING
5,500 SQUARE FEET; AND ALL STRUCTURES EXCEEDING FIRE DEPARTMENT ACCESS
REQUIREMENTS SHALL BE PROTECTED BY AN AUTOMATIC SPRINKLER SYSTEM, IN A
MANNER MEETING THE APPROVAL OF THE FIRE CHIEF.

SPECIAL FIRE PROTECTION NOTE:
PROPERTY IS IN A SPECIAL FIRE PROTECTION AREA.

HIGH FIRE HAZARD AREA NOTE:
THE LOTS SHOWN ON THIS MAP ARE IN A HIGH/VERY HIGH FIRE HAZARD AREA DUE TO
WILD LAND EXPOSURE.

SIGNATURE OMISSIONS

PURSUANT TO THE PROVISIONS OF SECTION 66436 (a)(3)(A)(C) OF
THE SUBDIVISION MAP ACT, THE FOLLOWING SIGNATURE HAS BEEN
OMITTED:

LADERA DEVELOPMENT COMPANY, L.L.C., HOLDER OF OIL, GAS, AND MINERAL
RIGHTS PER DEED RECORDED DECEMBER 10, 1996 AS INSTRUMENT NO.
19960624029 OF OFFICIAL RECORDS.

NOTES:

"THE PRIVATE STREETS CONSTRUCTED WITHIN THIS MAP
SHALL BE OWNED, OPERATED AND MAINTAINED BY THE
DEVELOPER, SUCCESSORS OR ASSIGNS. THE COUNTY
OF ORANGE SHALL HAVE NO RESPONSIBILITY
THEREFORE UNLESS PURSUANT TO APPROPRIATE
SECTIONS OF THE STREETS AND HIGHWAYS CODE OF
THE STATE OF CALIFORNIA, THE SAID PRIVATE STREETS
HAVE BEEN ACCEPTED INTO THE COUNTY ROAD SYSTEM
BY APPROPRIATE RESOLUTION OF THE ORANGE COUNTY
BOARD OF SUPERVISORS."

EASEMENT NOTES

- ☐ A INDICATES DRAINAGE AND ACCESS EASEMENT DEDICATED TO
SANTA MARGARITA WATER DISTRICT.
- ☐ B INDICATES WATER, RECYCLED WATER, SEWER AND ACCESS
EASEMENT DEDICATED TO SANTA MARGARITA WATER DISTRICT.

BASIS OF BEARINGS

THE BEARINGS SHOWN HEREON ARE BASED ON THE BEARING BETWEEN
O.C.S. HORIZONTAL CONTROL STATION GPS NO. 1417 AND STATION
GPS NO. 1448, BEING NORTH 10°48'13" EAST PER RECORDS ON FILE
IN THE OFFICE OF THE ORANGE COUNTY SURVEYOR.

DATUM STATEMENT

COORDINATES SHOWN ARE BASED ON THE CALIFORNIA COORDINATE
SYSTEM (CCS 83), ZONE VI, 1983 NAD (1991.35 EPOCH OCS GPS
ADJUSTMENT). ALL DISTANCES ARE GROUND DISTANCES UNLESS
OTHERWISE NOTED. TO OBTAIN GRID DISTANCE MULTIPLY GROUND
DISTANCE BY 0.999948295. THIS FACTOR IS PROJECT-SPECIFIC

MONUMENT NOTES

- INDICATES FOUND MONUMENT AS NOTED.
- ☐ A INDICATES FOUND 2 1/2" IRON PIPE W/2" OCS BRASS CAP STAMPED "GPS
1448 9-95" PER TRACT NO. 16203, M.M. 826/8-20 AND RECORD ON FILE
IN THE ORANGE COUNTY SURVEYORS OFFICE.
N2146790.819, E6142602.585
- ☐ B INDICATES FOUND 2 1/2" IRON PIPE W/2" OCS BRASS CAP STAMPED "GPS
1417 9-95" PER TRACT NO. 16203, M.M. 826/8-20 AND RECORD ON FILE
IN THE ORANGE COUNTY SURVEYORS OFFICE.
N2141450.558, E6141563.535
- ☐ O INDICATES 2" I.P. TAGGED L.S. 6217 OR SPIKE & WASHER STAMPED L.S.
6217 OR LEAD, TACK & TAG L.S. 6217 TO BE SET PER TRACT NO. 16471
M.M. 861/ 42-49, UNLESS OTHERWISE NOTED.
- ☐ INDICATES 1" I.P. TAGGED L.S. 6217 OR SPIKE & WASHER STAMPED L.S.
6217 OR LEAD, TACK & TAG L.S. 6217 TO BE SET PER TRACT NO. 16471
M.M. 861/ 42-49, UNLESS OTHERWISE NOTED.
- 2" I.P. TAGGED L.S. 6217 OR SPIKE & WASHER STAMPED L.S. 6217
OR LEAD, TACK & TAG L.S. 6217 TO BE SET AT ALL TRACT BOUNDARY
CORNERS WITHIN 90 DAYS AFTER ACCEPTANCE OF IMPROVEMENTS.
- 1" I.P. TAGGED L.S. 6217 OR SPIKE & WASHER STAMPED L.S. 6217 OR
LEAD, TACK & TAG L.S. 6217 TO BE SET AT LOT CORNERS WITHIN 90 DAYS
AFTER ACCEPTANCE OF IMPROVEMENTS.
- 1" I.P. TAGGED L.S. 6217 OR SPIKE & WASHER STAMPED L.S. 6217 OR
LEAD, TACK & TAG L.S. 6217 TO BE SET AT ALL CENTERLINE INTERSECTIONS,
E.C.'S AND B.C.'S WITHIN 90 DAYS AFTER ACCEPTANCE OF IMPROVEMENTS.

NOTES

LOTS BA THROUGH BD ARE FOR PRIVATE STREET PURPOSES AND ARE NOT
SEPARATE BUILDING SITES.

LOTS A AND B ARE FOR LANDSCAPE/OPEN SPACE PURPOSES AND
ARE NOT SEPARATE BUILDING SITES.

LOTS 66 THROUGH 68 ARE NOT RESIDENTIAL BUILDING SITES, BUT ARE PRIVATE
RECREATION SITES.

() INDICATES MEASURED AND RECORD PER TRACT NO. 16471 M.M. 861/ 42-49

☐ INDICATES 2" I.P. TAGGED L.S. 6217 OR SPIKE & WASHER
STAMPED L.S. 6217 OR LEAD, TACK & TAG L.S. 6217 TO BE
SET PRIOR TO MAP RECORDATION.

862 4

TRACT MAP NO. 16472

IN THE UNINCORPORATED TERRITORY OF THE COUNTY OF ORANGE,

STATE OF CALIFORNIA

HALL & FOREMAN, INC.

STEVEN C. SHAMBECK, P.L.S. 6217

MAY, 2004


SHEET 4 OF 10 SHEETS
68 NUMBERED LOTS
6 LETTERED LOTS
19.486 ACRES
PORTION OF VESTING
T.T.M. 15990
DATE OF SURVEY:
JANUARY, 1999

SEE SHEET 2 FOR BASIS OF
BEARINGS, DATUM STATEMENT,
MONUMENT NOTES, EASEMENT
NOTES AND NOTES

LINE DATA		
LINE	BEARING	LENGTH
L1	(N88°25'06"W	18.00'
L2	(N50°11'32"E	18.79'
L3	(N21°34'54"E	25.00'
L4	(N21°34'54"E	12.50'
L5	(N21°34'54"E	12.50'
L6	(N07°01'43"W	18.79'
L7	(N68°25'06"W	18.00'
L8	(N70°52'35"E	26.92'
L9	(N68°25'06"W	43.00' (RAD)

CURVE DATA		
CURVE	DELTA	LENGTH
C1	82°11'42"	34.43'

TRACT NO. 16471
M.M. 801/42-49

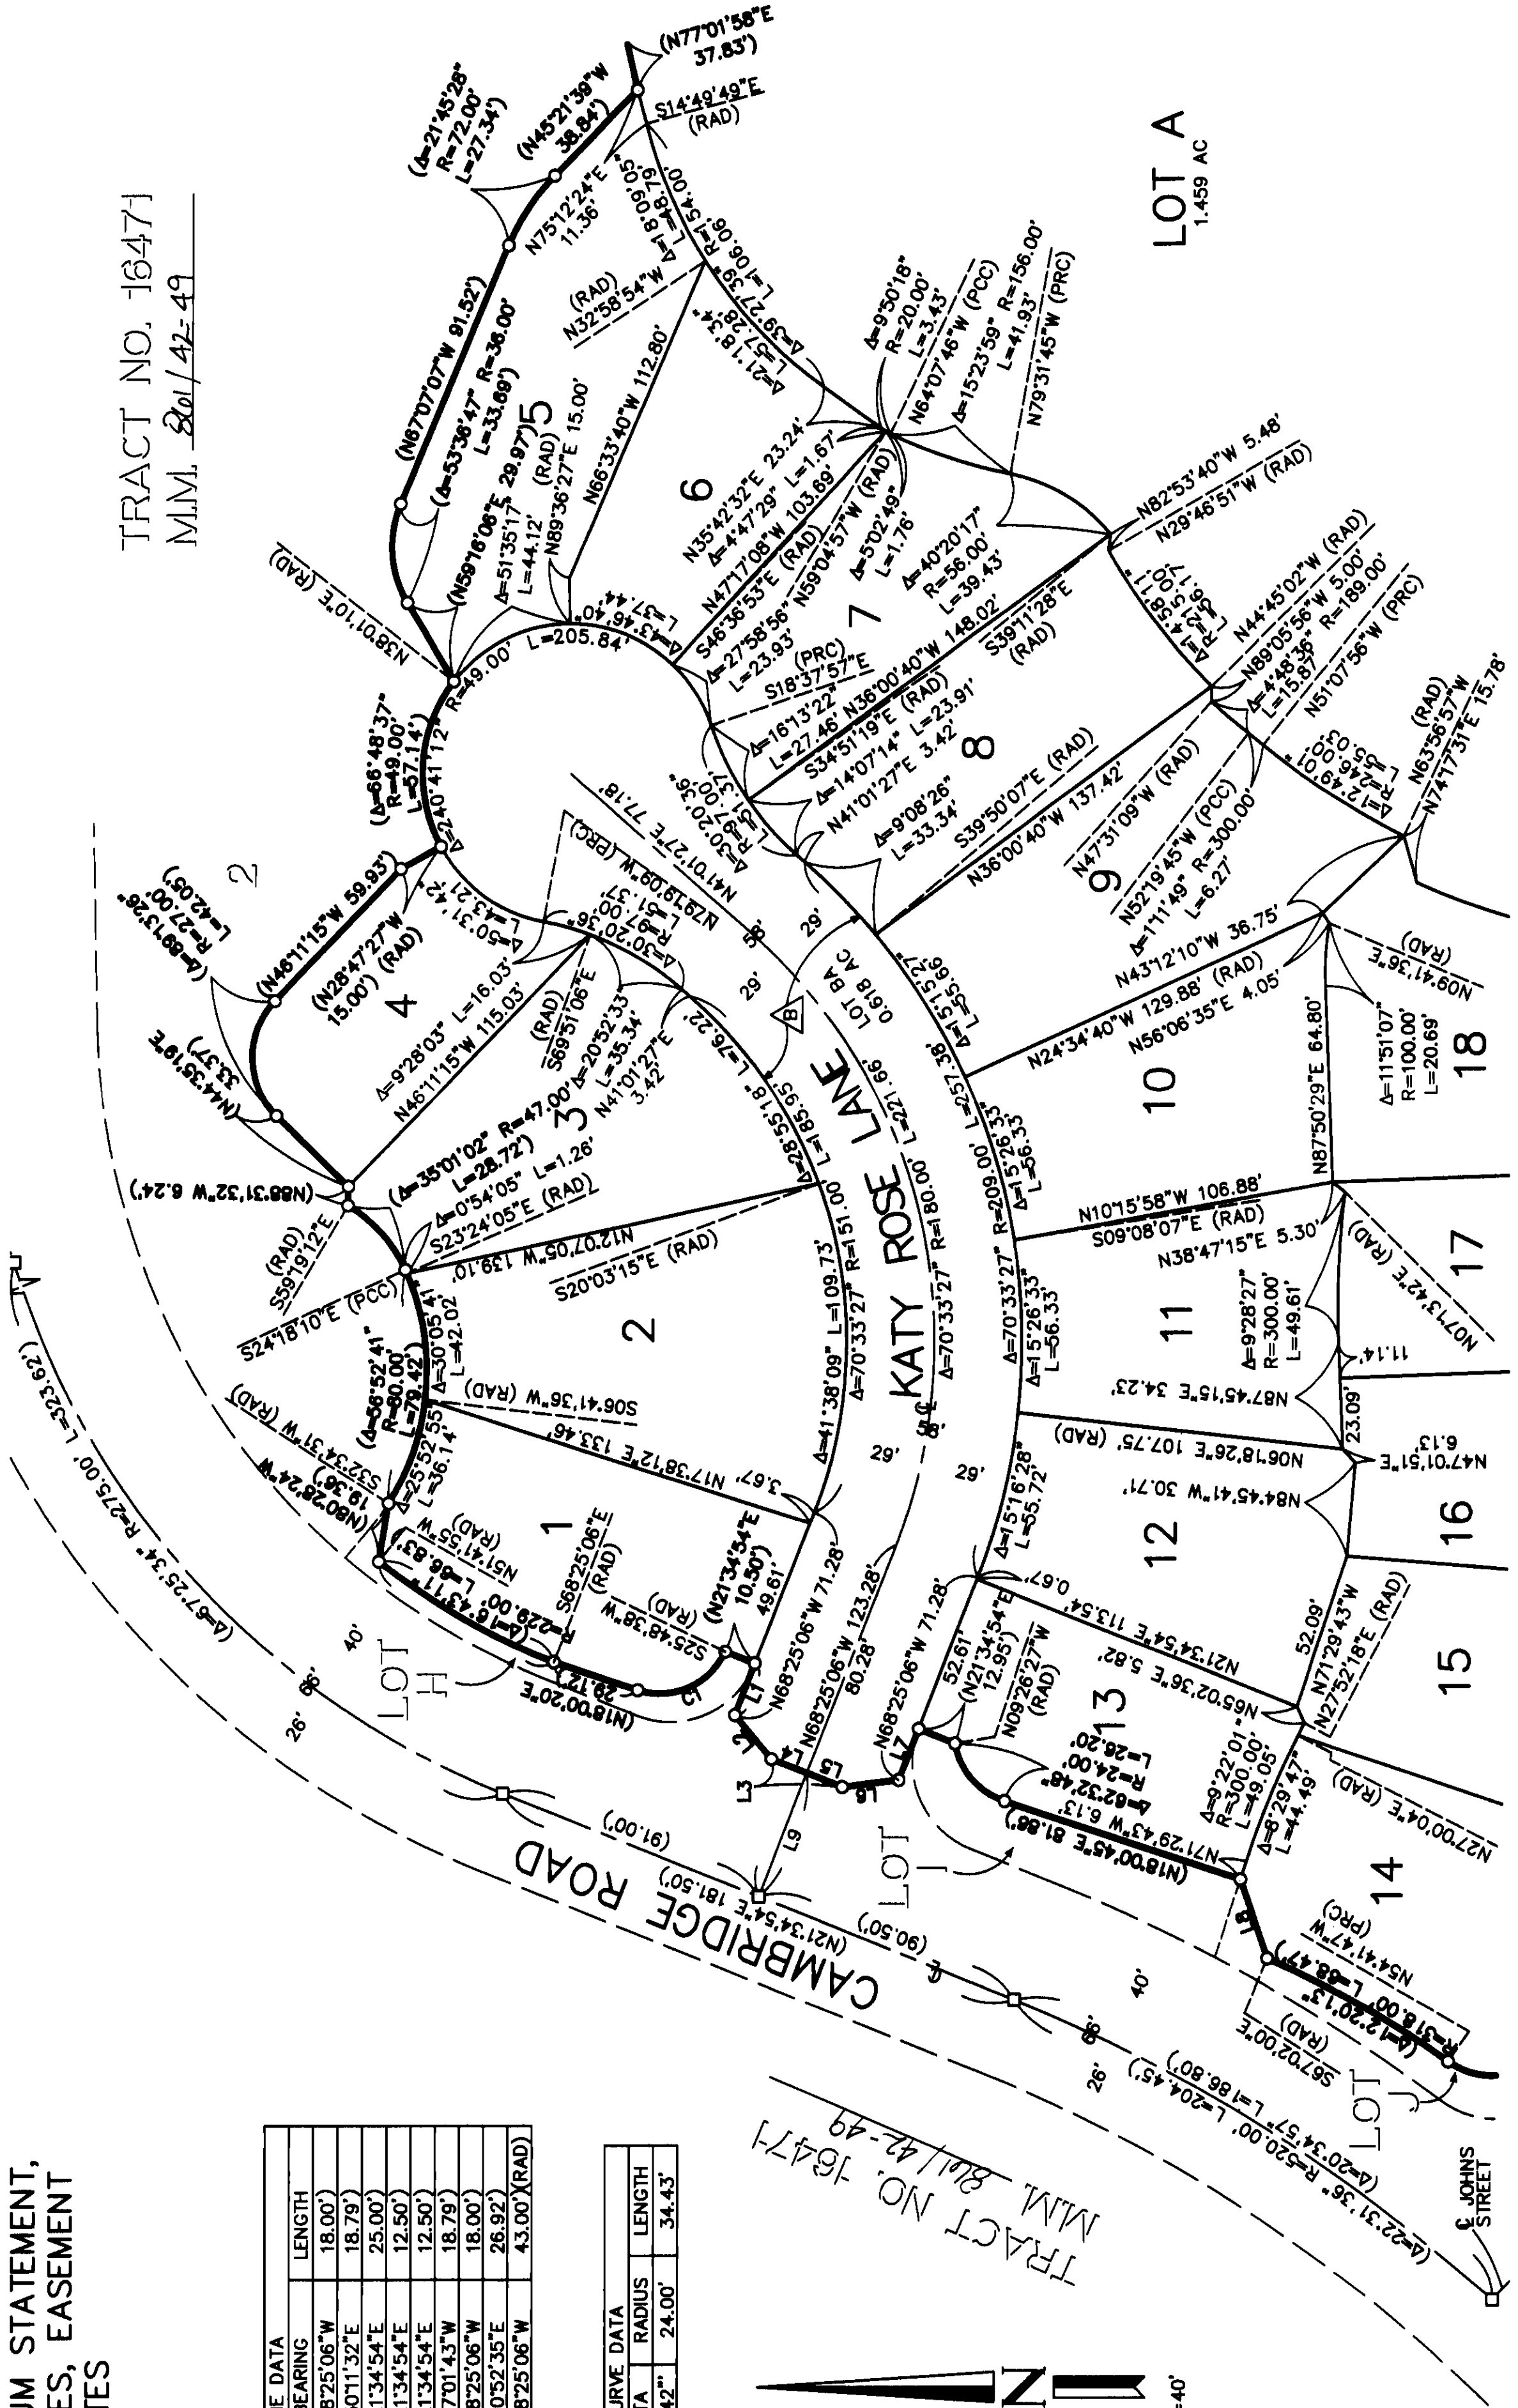

SEE SHEET 8

LOT A
1.459 AC

SEE SHEET 5

TRACT NO. 16471
M.M. 801/42-49

862 5

SHEET 5 OF 10 SHEETS
68 NUMBERED LOTS
6 LETTERED LOTS
19.486 ACRES
PORTION OF VESTING
T.T.M. 15990
DATE OF SURVEY:
JANUARY, 1999

TRACT MAP NO. 16472


IN THE UNINCORPORATED TERRITORY OF THE COUNTY OF ORANGE,
STATE OF CALIFORNIA

HALL & FOREMAN, INC. STEVEN C. SHAMBECK, P.L.S. 6217
MAY, 2004

SEE SHEET 2 FOR BASIS OF
BEARINGS, DATUM STATEMENT,
MONUMENT NOTES, EASEMENT
NOTES AND NOTES

CURVE DATA		
CURVE	DELTA	LENGTH
C1	69°25'29"	25.00'
C2	071°07'	329.00'
C3	66°15'48"	25.00'
C5	1°56'39"	520.00'
C6	2°23'39"	389.50'

LINE DATA		
LINE	BEARING	LENGTH
L1	(N70°52'35"E	26.92')
L2	(N42°09'51"E	12.68')
L3	(N48°47'43"W	16.40')
L4	(N70°46'29"E	18.79')
L5	(N42°09'51"E	12.50')
L6	(N47°50'09"W	0.35')
L7	(N42°09'51"E	12.50')
L8	(N13°35'59"W	18.82')
L9	(N47°50'09"W	55.51')
L10	(N42°09'51"E	7.46')
L11	(N47°50'09"W	41.65' (RAD)

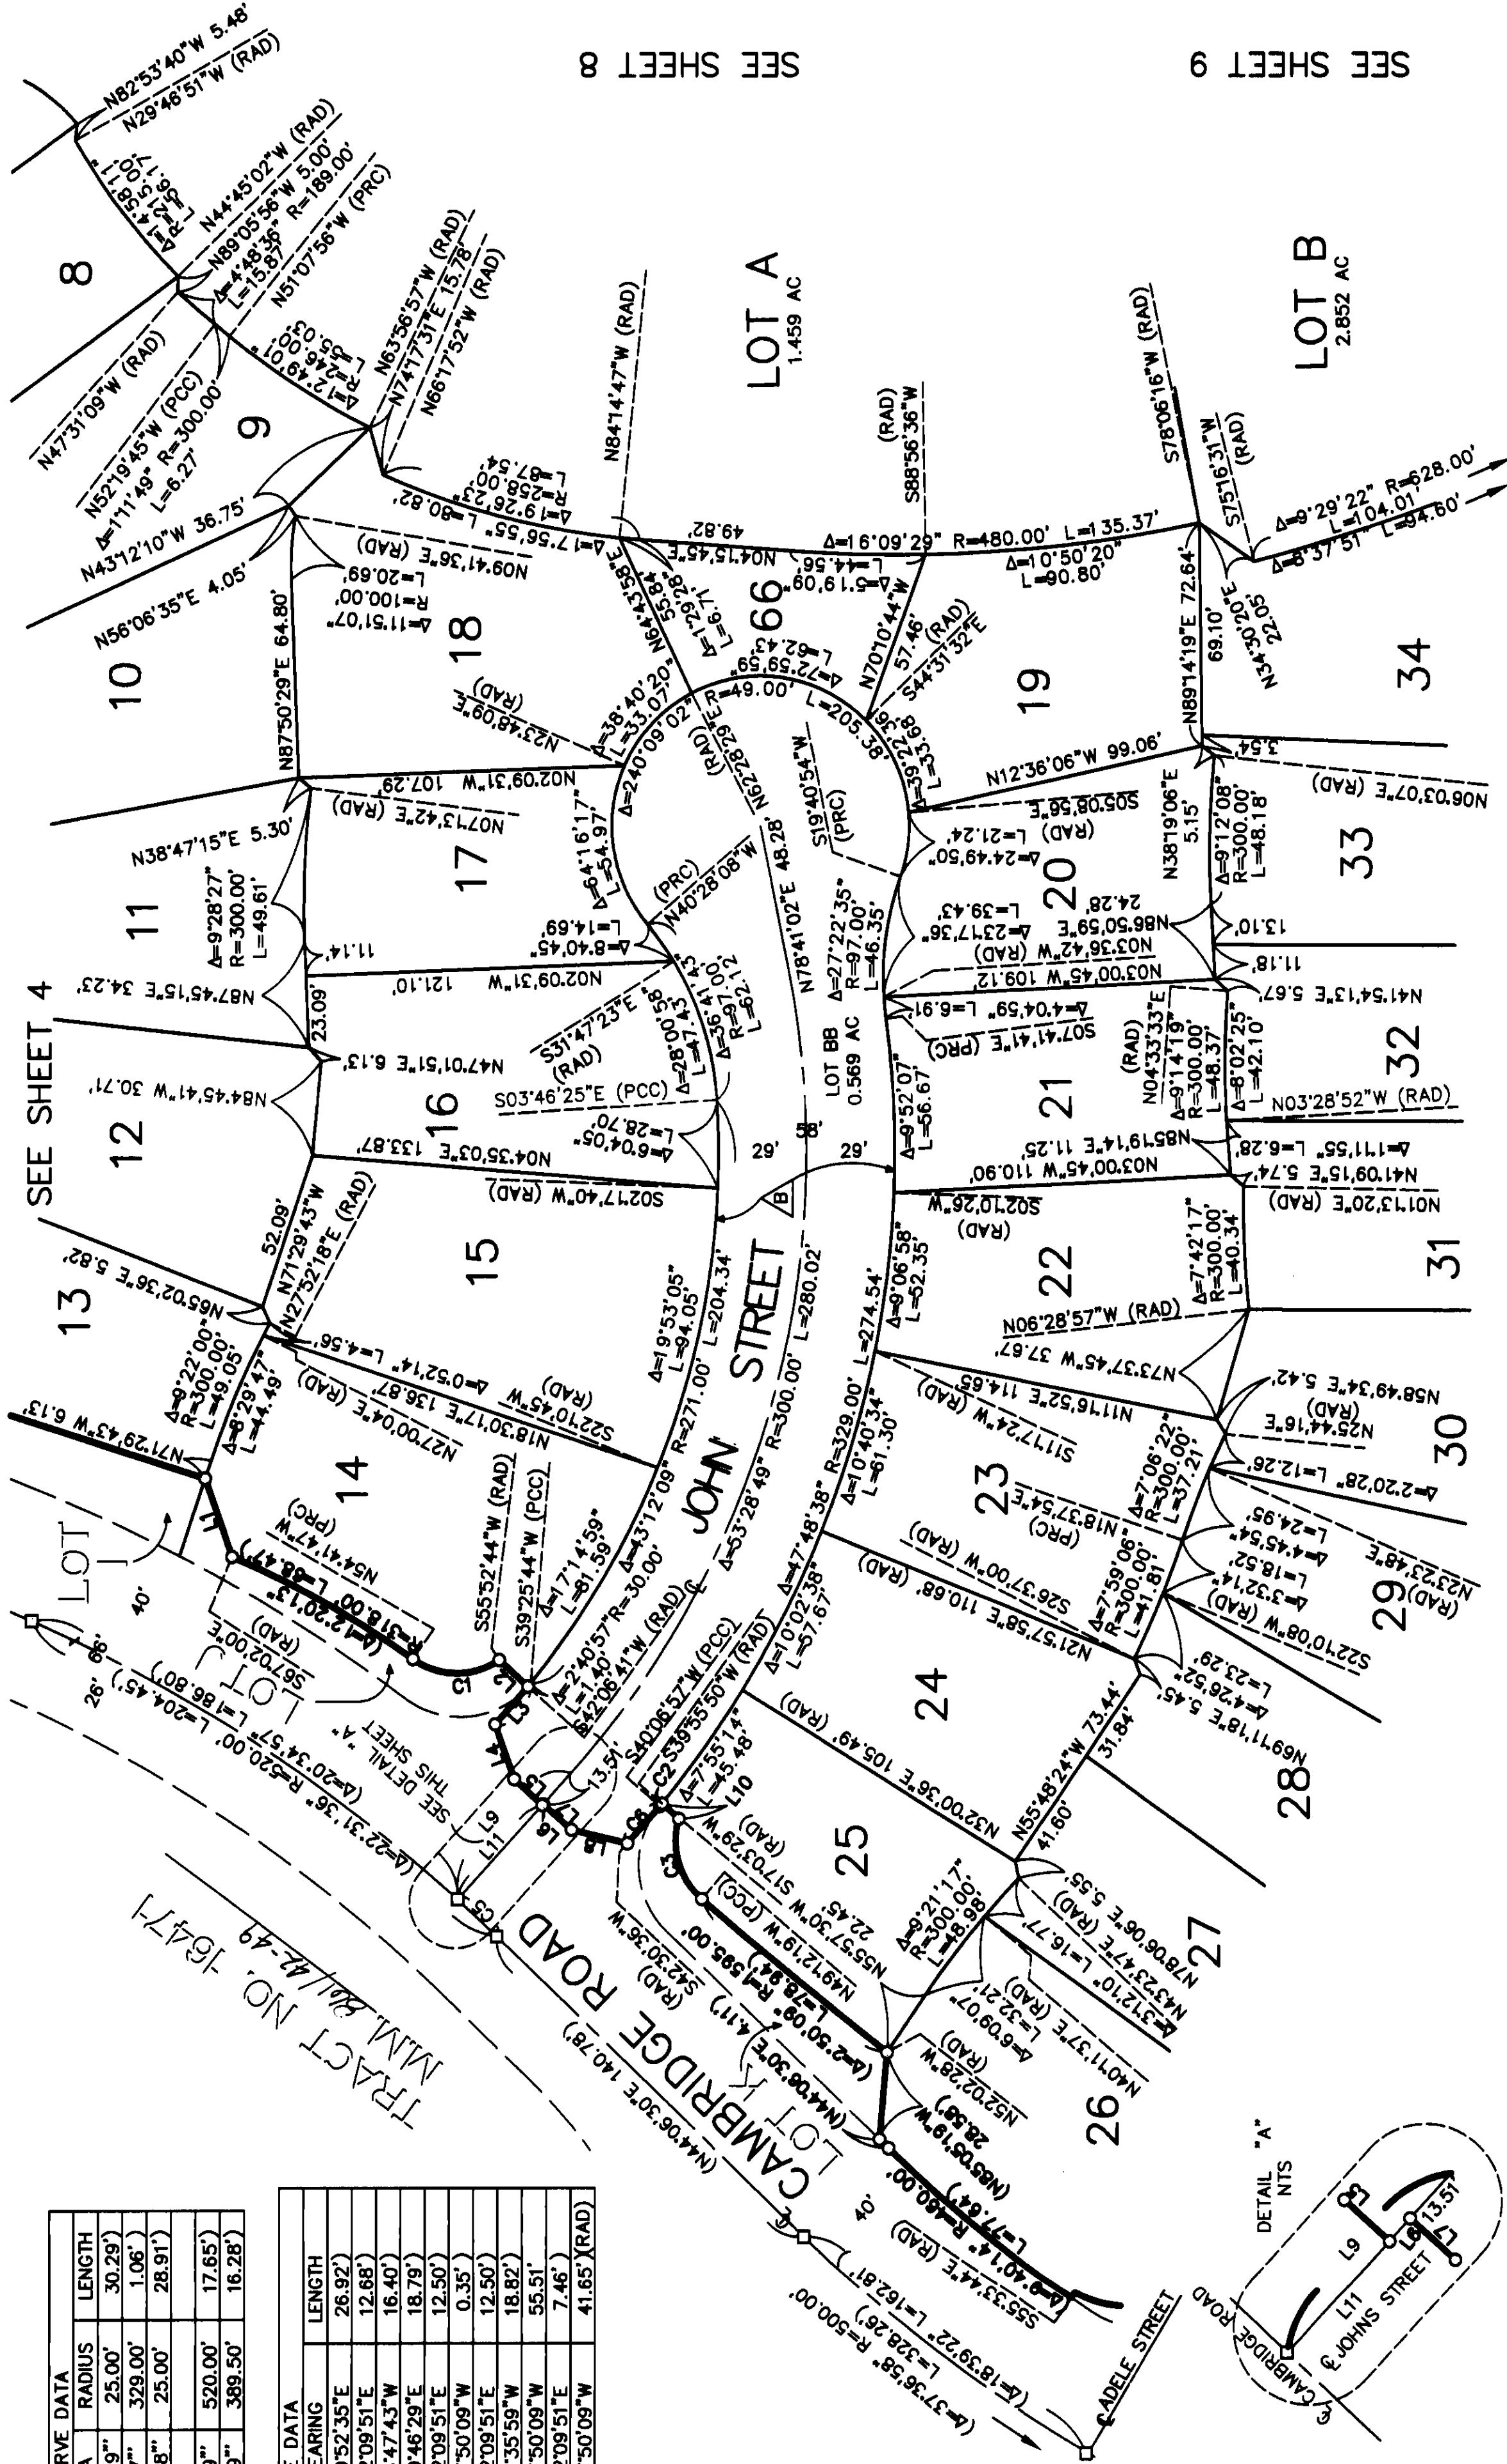

SEE SHEET 8

SEE SHEET 9

SEE SHEET 6

862 6


SHEET 6 OF 10 SHEETS
68 NUMBERED LOTS
6 LETTERED LOTS
19.486 ACRES
PORTION OF VESTING
T.T.M. 15990
DATE OF SURVEY:
JANUARY, 1999

TRACT MAP NO. 16472

IN THE UNINCORPORATED TERRITORY OF THE COUNTY OF ORANGE,
STATE OF CALIFORNIA

HALL & FOREMAN, INC. STEVEN C. SHAMBECK, P.L.S. 6217
MAY, 2004

SEE SHEET 2 FOR BASIS OF
BEARINGS, DATUM STATEMENT,
MONUMENT NOTES, EASEMENT
NOTES AND NOTES

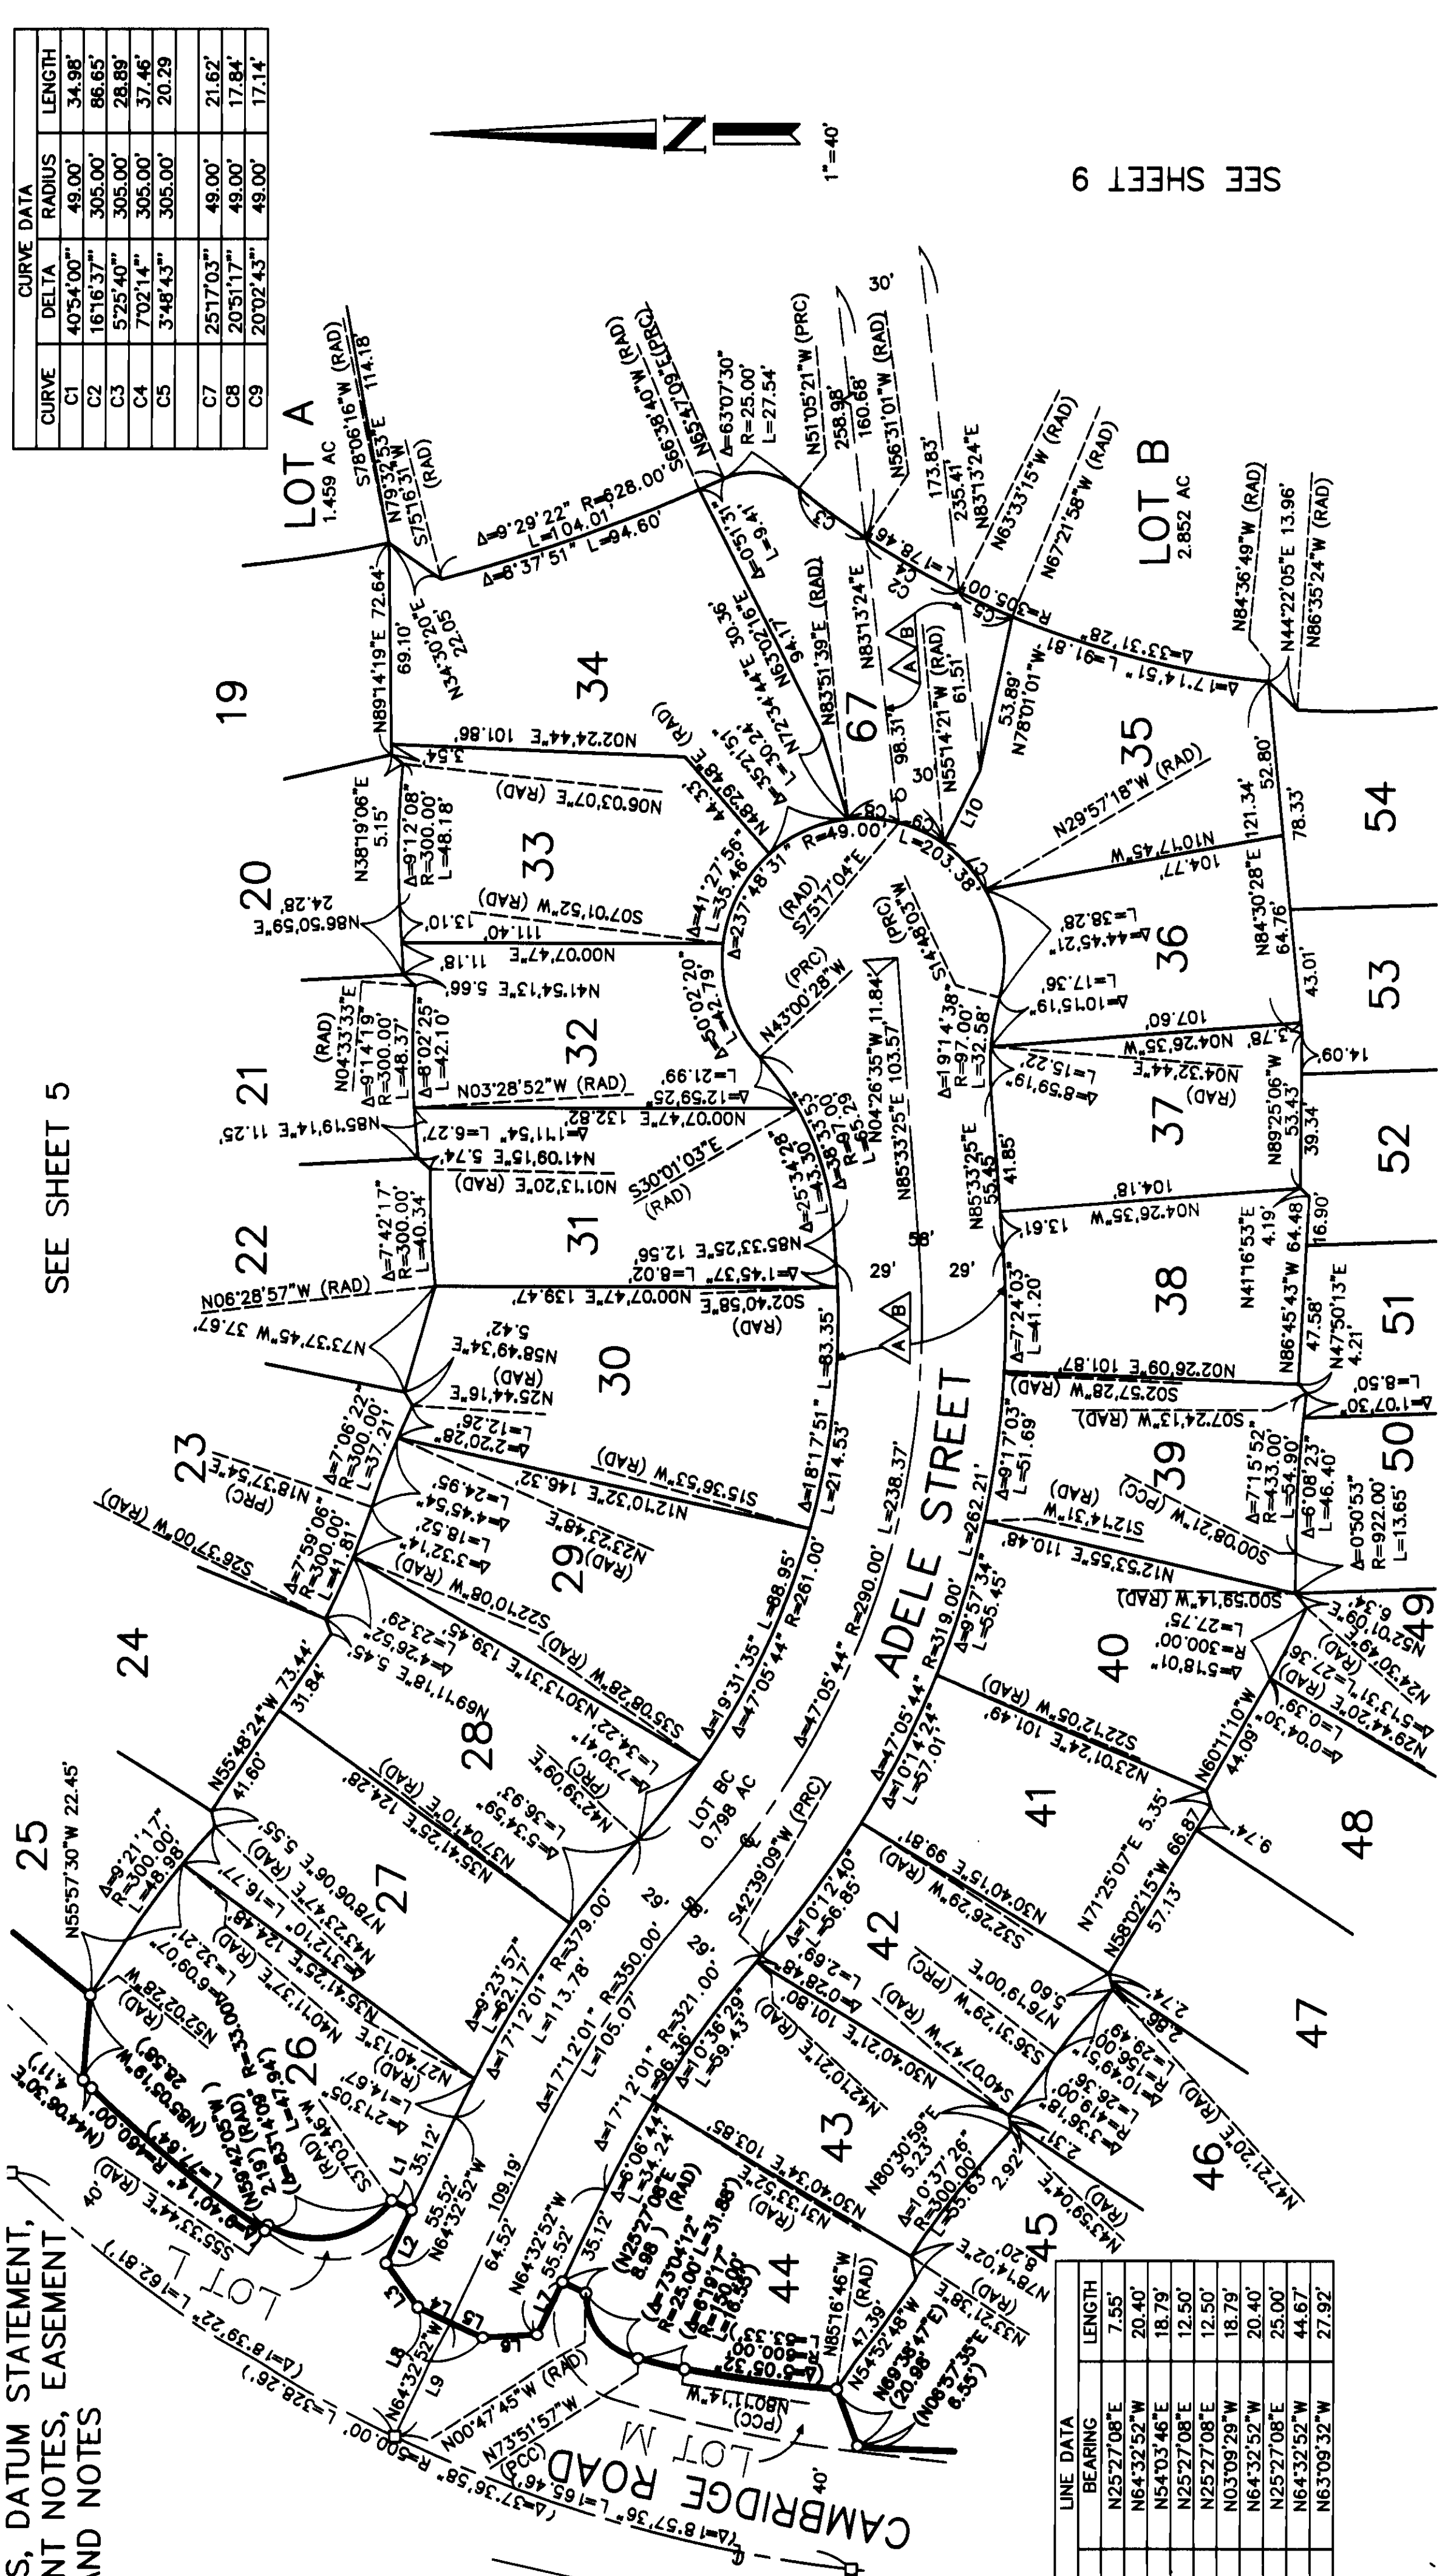

CURVE DATA			
CURVE	DELTA	RADIUS	LENGTH
C1	40°54'00"	49.00'	34.98'
C2	16°16'37"	305.00'	86.65'
C3	5°25'40"	305.00'	28.89'
C4	7°02'14"	305.00'	37.46'
C5	3°48'43"	305.00'	20.29'
C7	25°17'03"	49.00'	21.62'
C8	20°51'17"	49.00'	17.84'
C9	20°02'43"	49.00'	17.14'

LINE DATA		
LINE	BEARING	LENGTH
L1	N25°27'08"E	7.55'
L2	N64°32'52"W	20.40'
L3	N54°03'46"E	18.79'
L4	N25°27'08"E	12.50'
L5	N25°27'08"E	12.50'
L6	N03°09'29"W	18.79'
L7	N64°32'52"W	20.40'
L8	N25°27'08"E	25.00'
L9	N64°32'52"W	44.67'
L10	N63°09'32"W	27.92'

SEE SHEET 9

SEE SHEET 7

TRACT NO. 16471
M.M. 8/11/42-49

862 7

SHEET 7 OF 10 SHEETS
68 NUMBERED LOTS
6 LETTERED LOTS
19.486 ACRES
PORTION OF VESTING
T.T.M. 15990
DATE OF SURVEY:
JANUARY, 1999

TRACT MAP NO. 16472


IN THE UNINCORPORATED TERRITORY OF THE COUNTY OF ORANGE,
STATE OF CALIFORNIA
STEVEN C. SHAMBECK, P.L.S. 6217

HALL & FOREMAN, INC.

MAY, 2004

CURVE	DELTA	RADIUS	LENGTH
C2	2°21'54"	279.00	11.52
C3	5°15'51"	250.00	22.97
C4	1°51'00"	250.00	8.07
C5	5°34'47"	221.00	21.52
C6	15°29'13"	250.00	67.57
C7	0°33'37"	221.00	2.16

LINE	BEARING	LENGTH
L1	N52°34'22"E	18.82
L2	N22°50'25"E	12.50 (RAD)
L3	N24°41'25"E	12.50 (RAD)
L4	N02°37'48"W	18.76

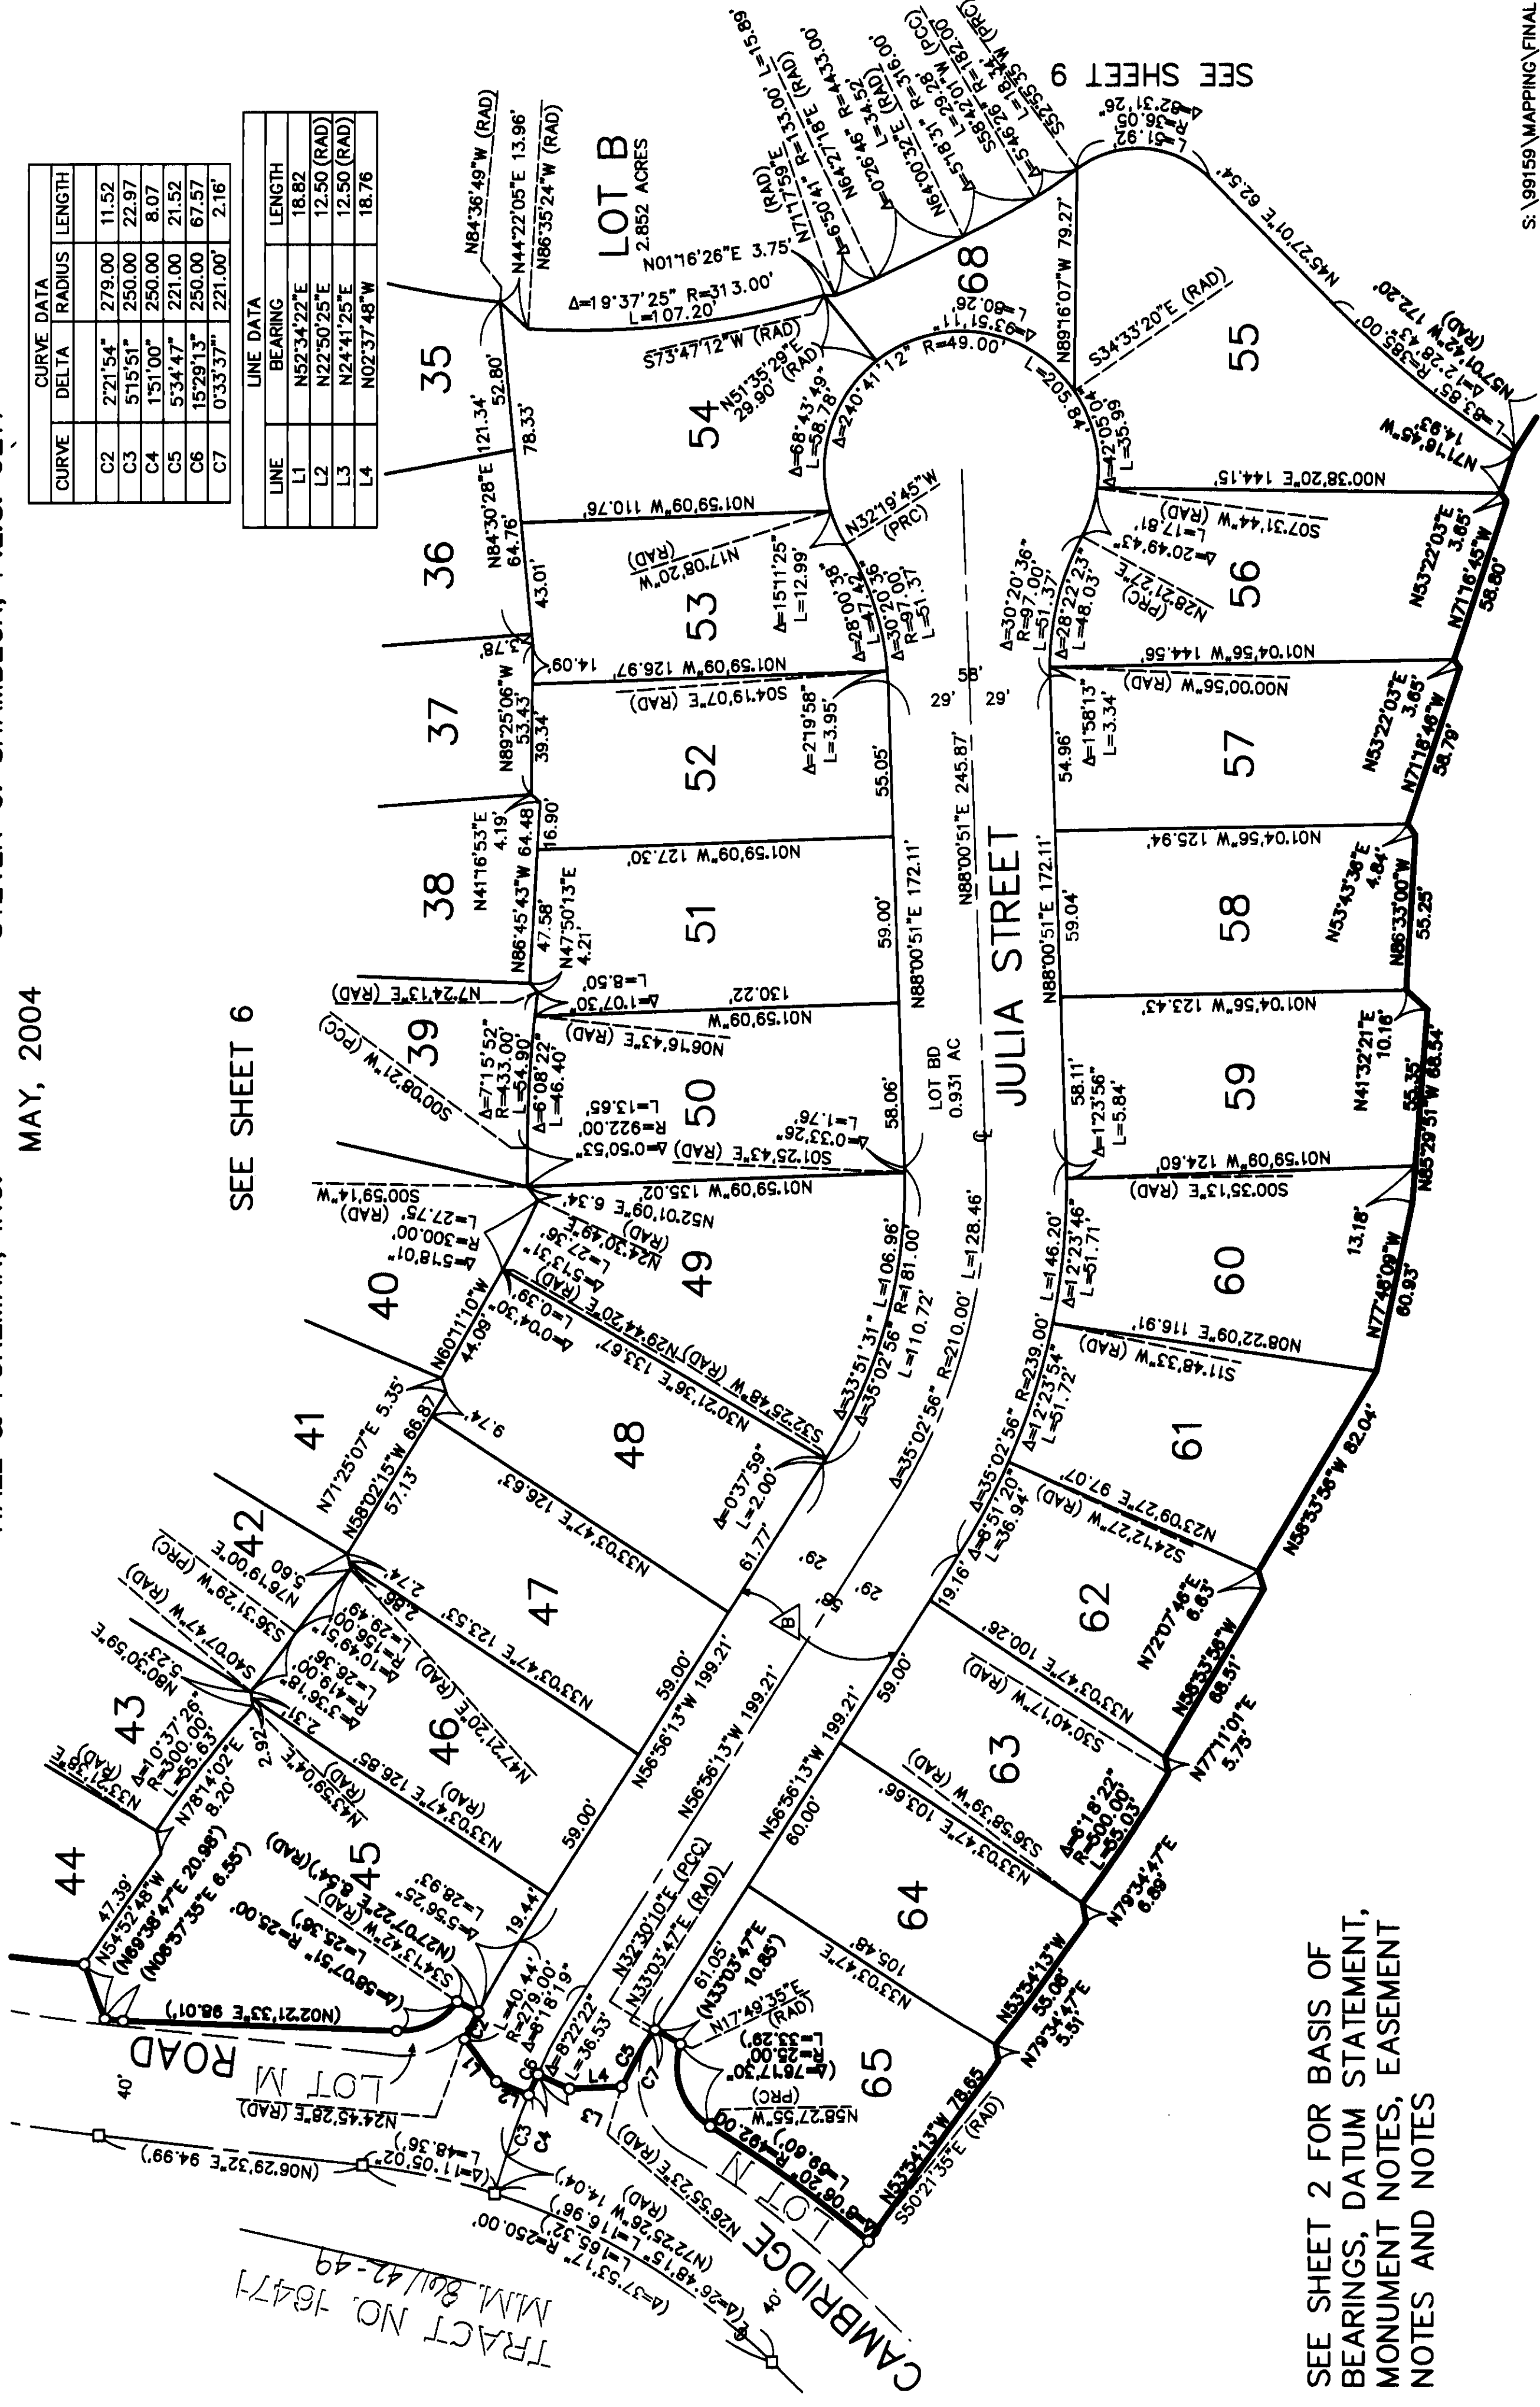

TRACT NO. 16471
M.M. 80142-49

SEE SHEET 2 FOR BASIS OF
BEARINGS, DATUM STATEMENT,
MONUMENT NOTES, EASEMENT
NOTES AND NOTES

SHEET 8 OF 10 SHEETS
68 NUMBERED LOTS
6 LETTERED LOTS
19.486 ACRES
PORTION OF VESTING
T.T.M. 15990
DATE OF SURVEY:
JANUARY, 1999


TRACT MAP NO. 16472

IN THE UNINCORPORATED TERRITORY OF THE COUNTY OF ORANGE,
STATE OF CALIFORNIA

HALL & FOREMAN, INC.

STEVEN C. SHAMBECK, P.L.S. 6217
MAY, 2004

SEE SHEET 2 FOR BASIS OF
BEARINGS, DATUM STATEMENT,
MONUMENT NOTES, EASEMENT
NOTES AND NOTES

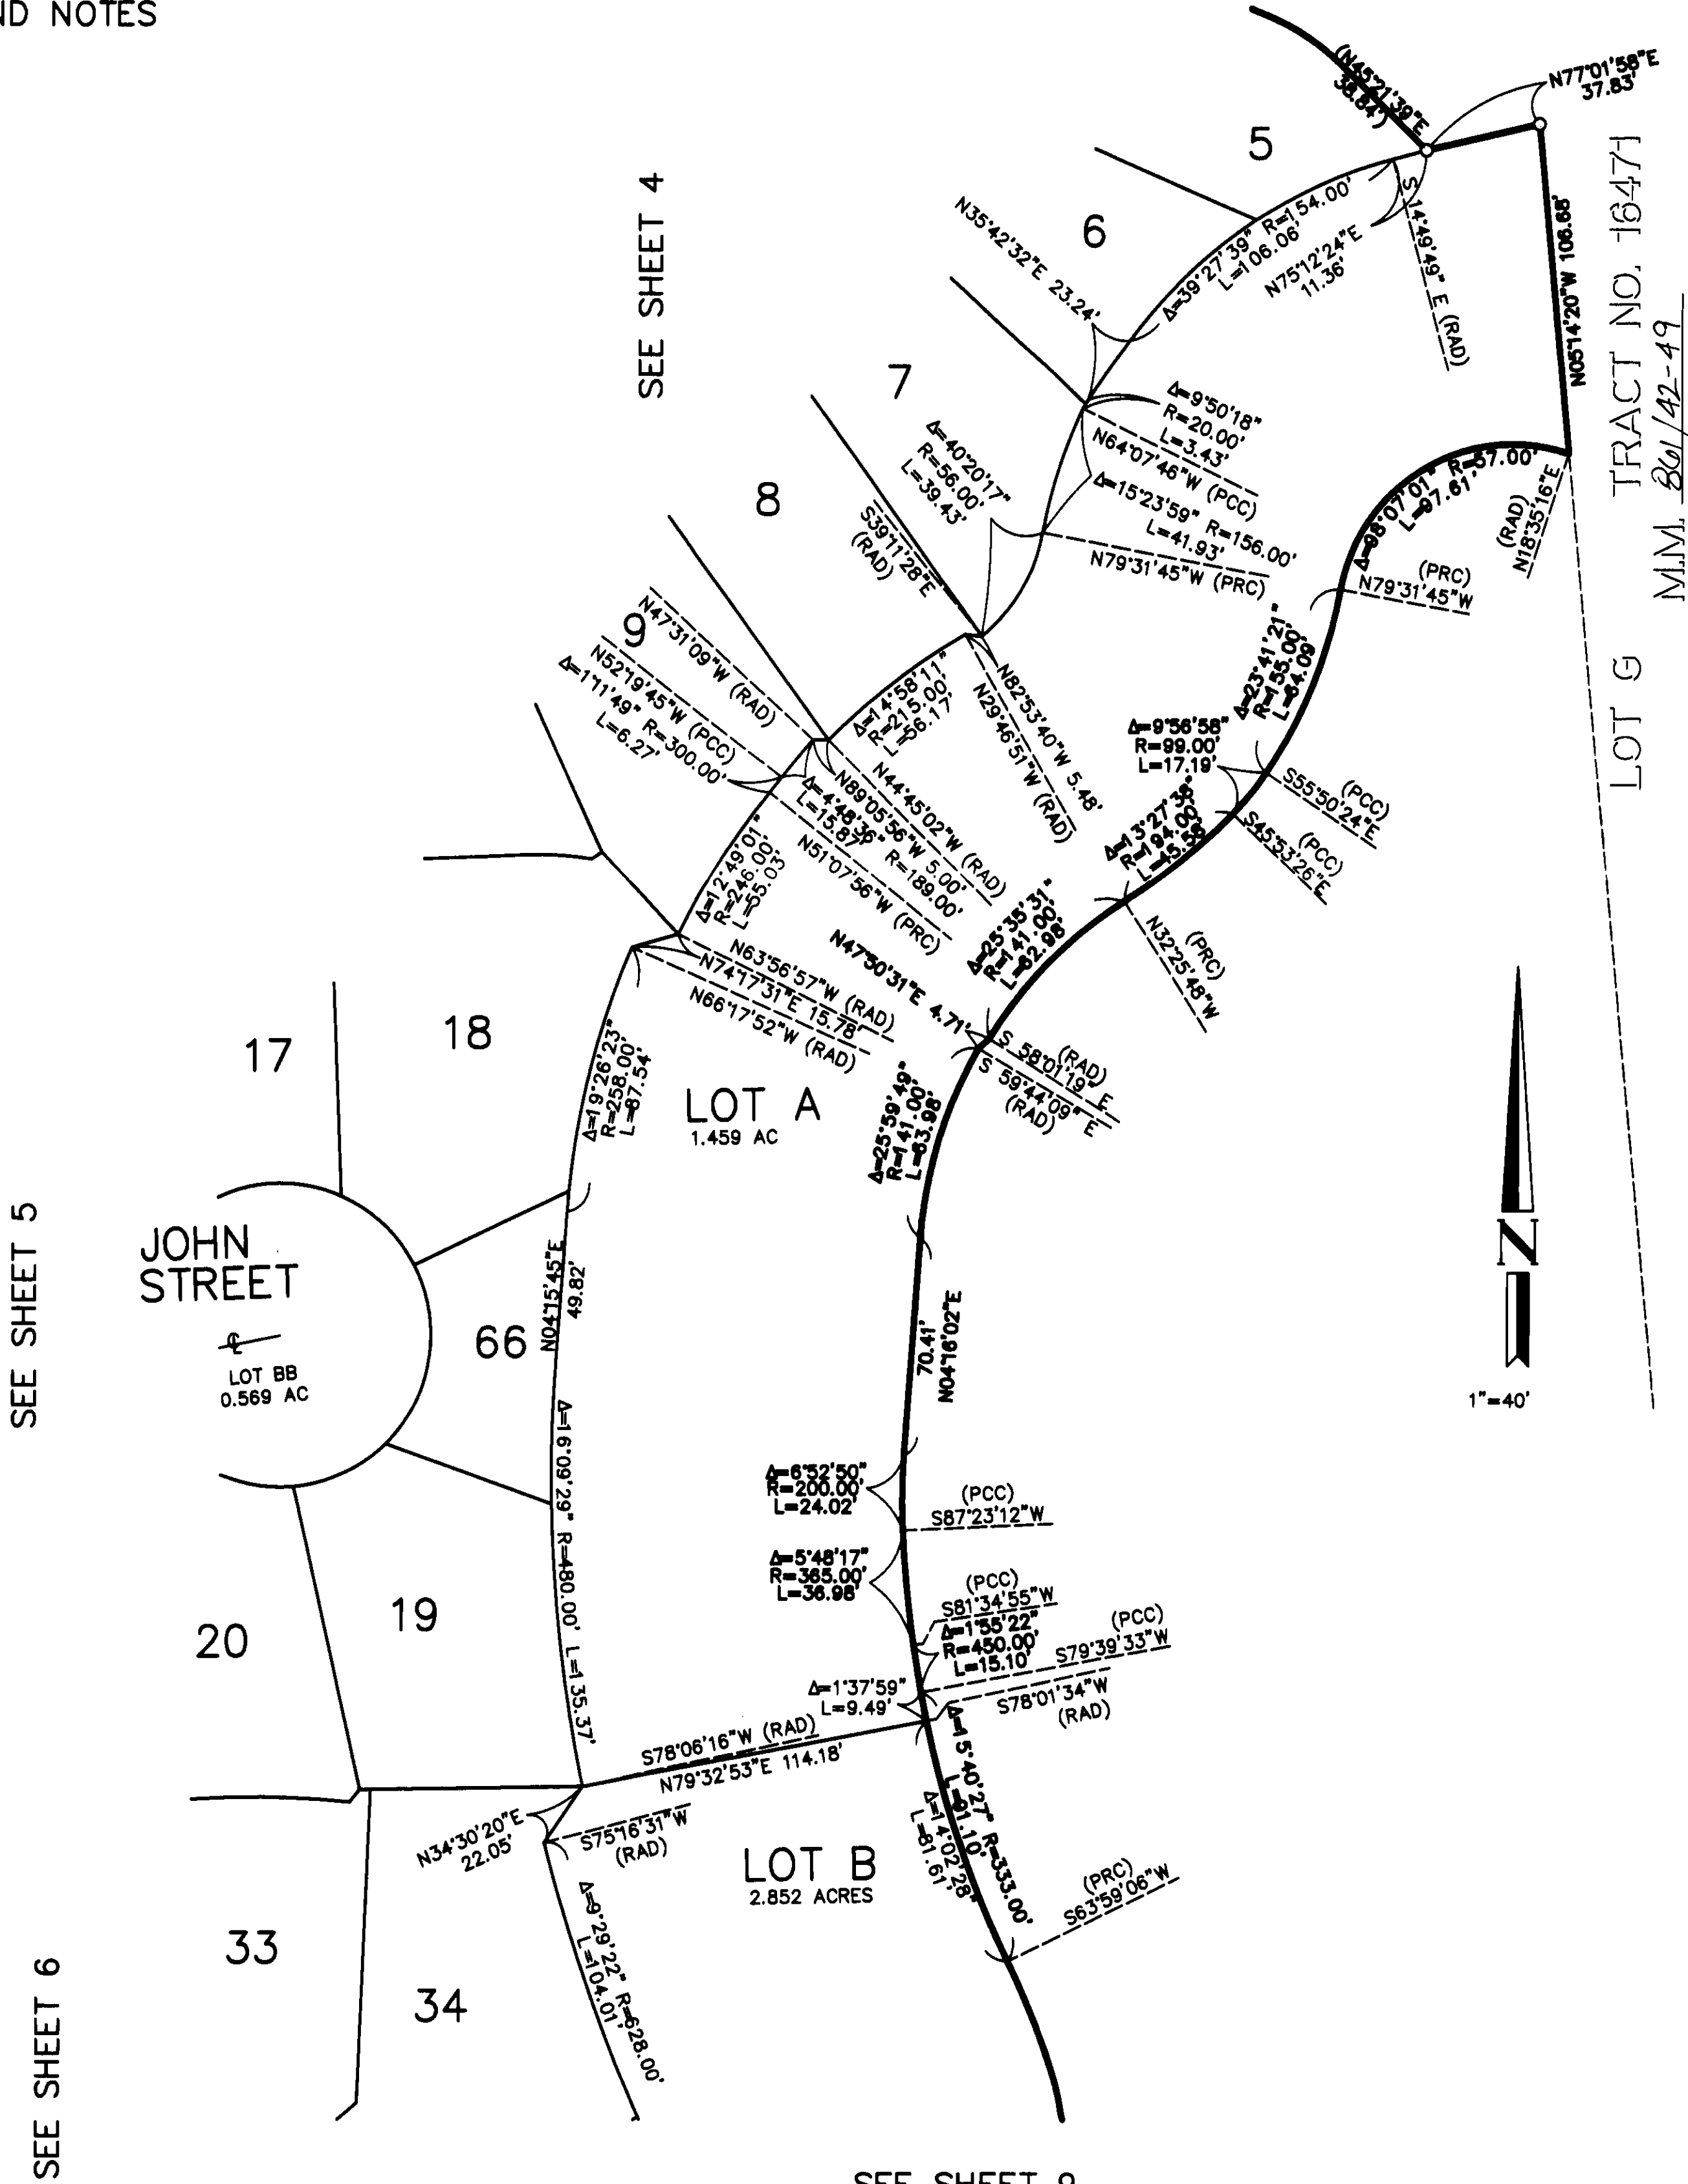

SHEET 9 OF 10 SHEETS
68 NUMBERED LOTS
6 LETTERED LOTS
19.486 ACRES
PORTION OF VESTING
T.T.M. 15990
DATE OF SURVEY:
JANUARY, 1999

TRACT MAP NO. 16472

IN THE UNINCORPORATED TERRITORY OF THE COUNTY OF ORANGE,
STATE OF CALIFORNIA

HALL & FOREMAN, INC.

STEVEN C. SHAMBECK, P.L.S. 6217

MAY, 2004

SEE SHEET 2 FOR BASIS OF
BEARINGS, DATUM STATEMENT,
MONUMENT NOTES, EASEMENT
NOTES AND NOTES

SEE SHEET 8

SEE SHEET 5


SEE SHEET 6

SEE SHEET 7



PARCEL 1
LLA NO. 96-026
INST. NO. 19960587414, O.R.

PARCEL 1
LLA NO. 96-026
INST. NO. 19960587414

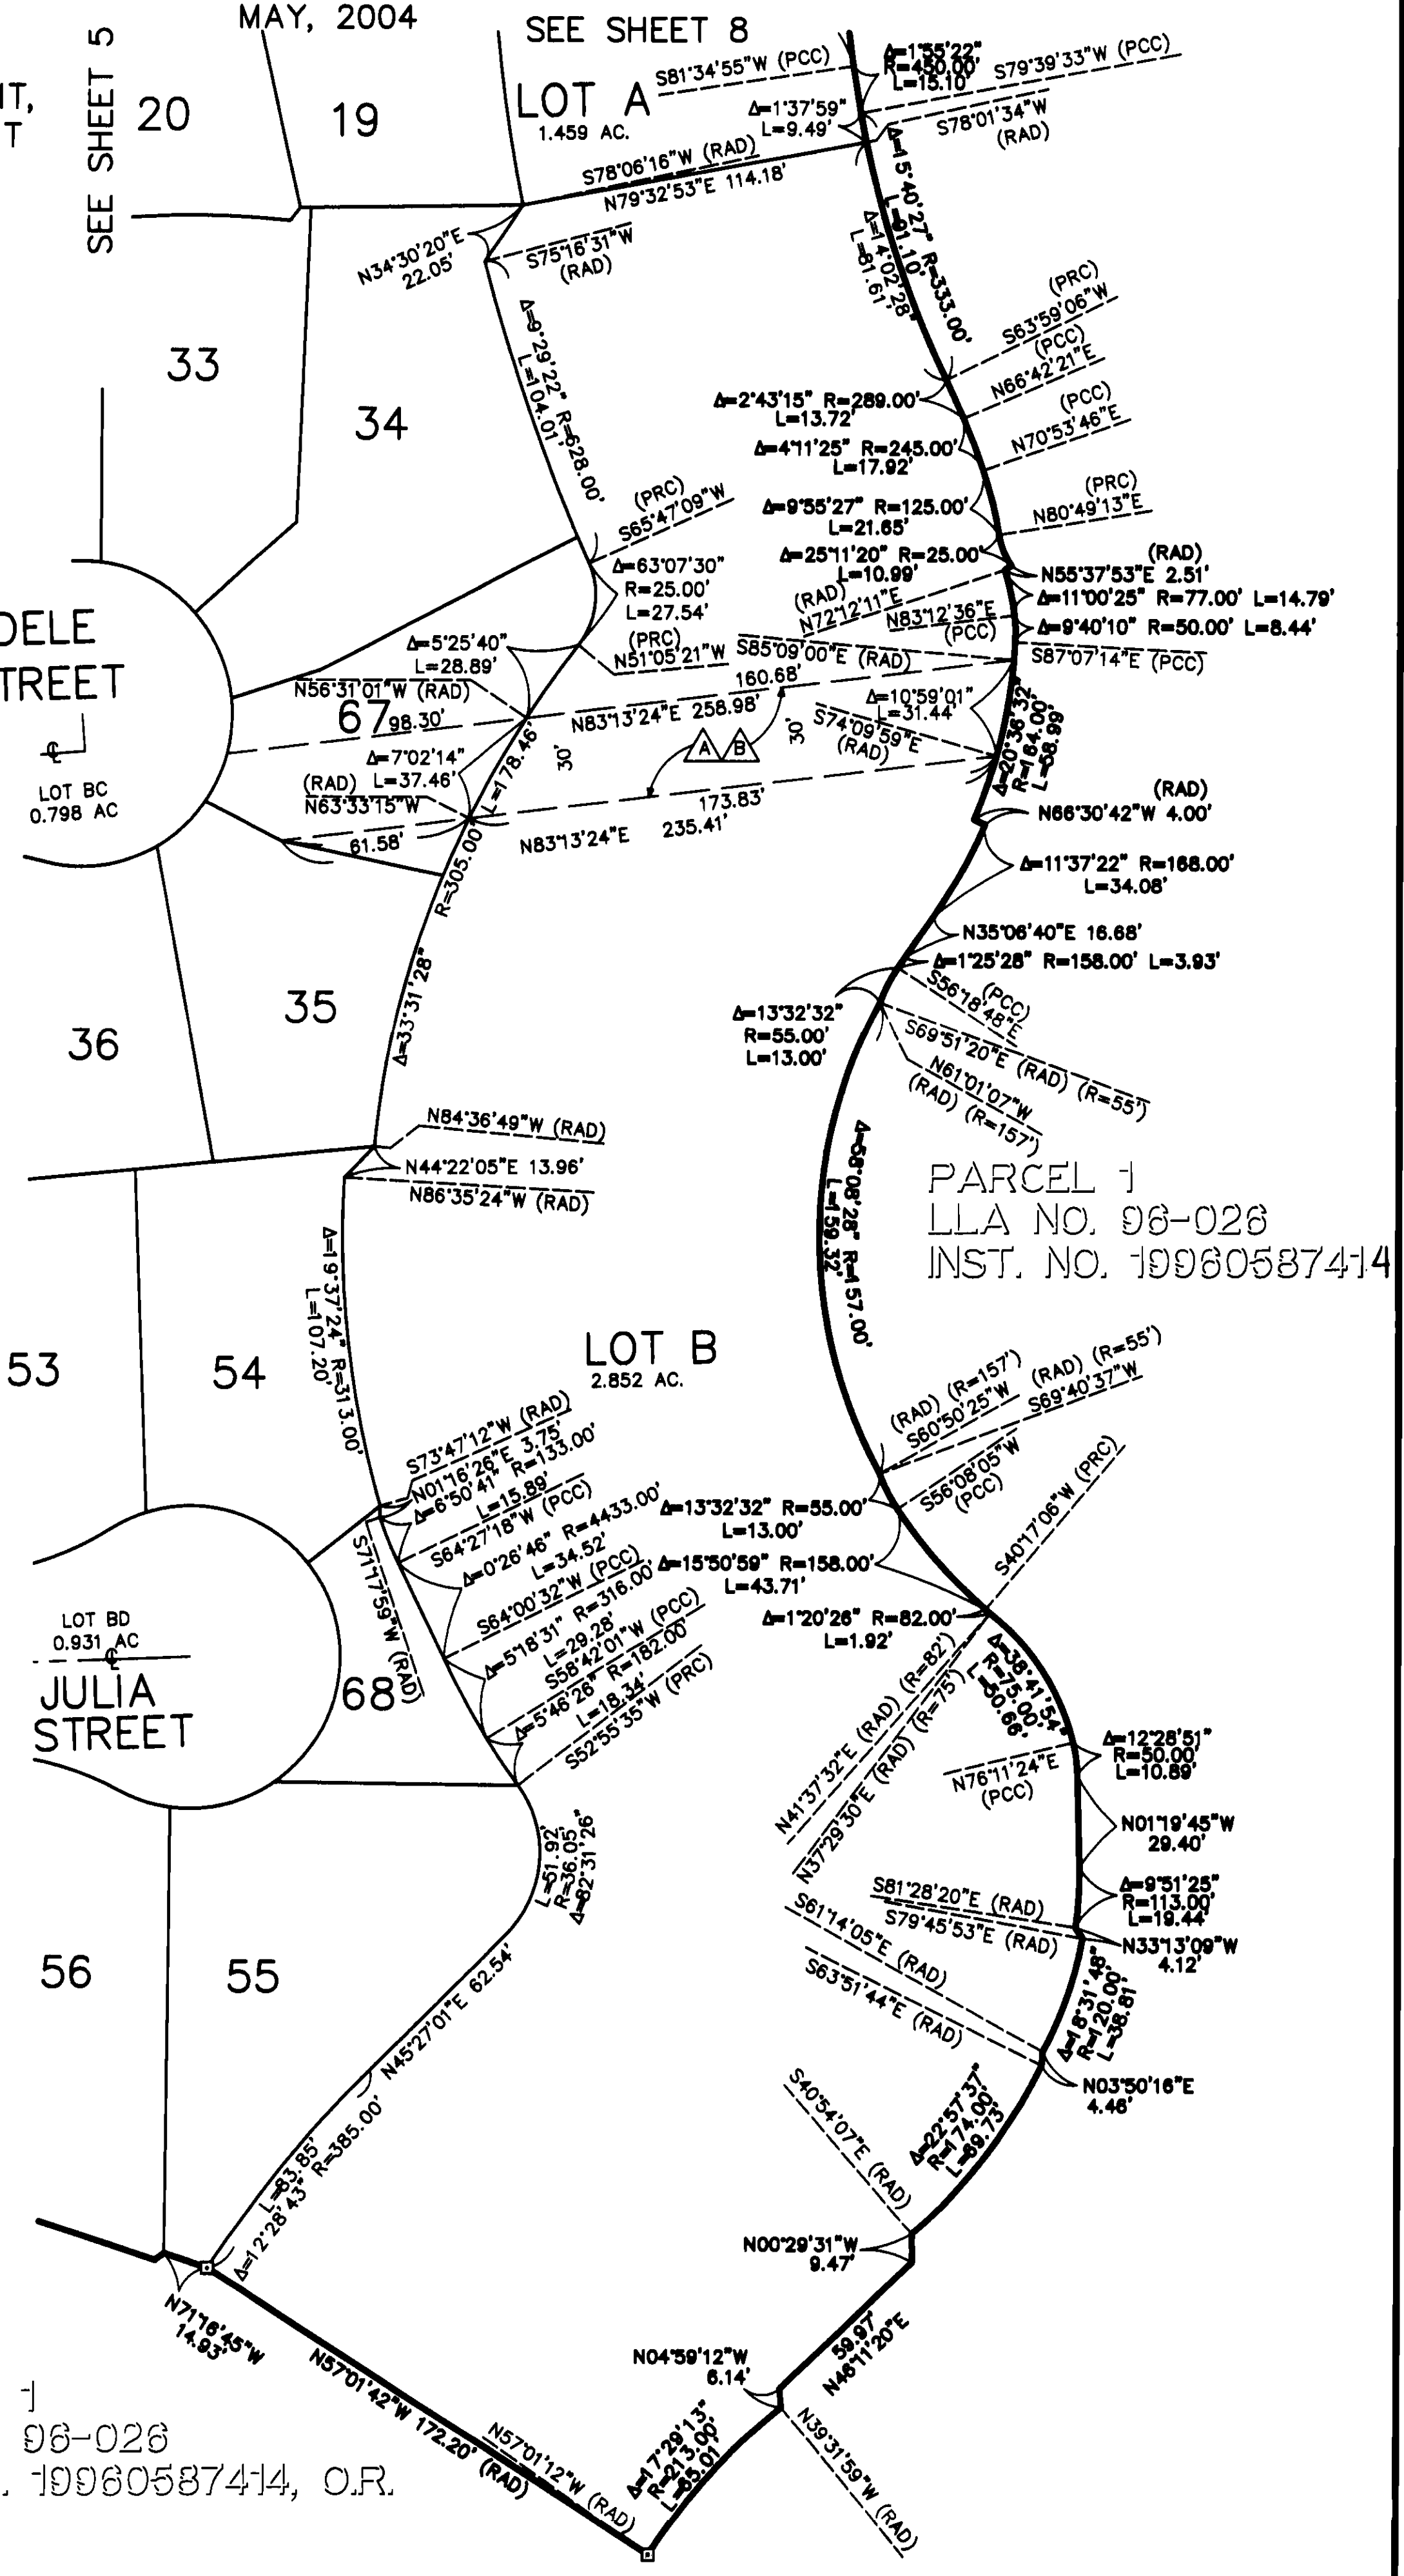

SHEET 10 OF 10 SHEETS
68 NUMBERED LOTS
2 LETTERED LOTS
19.486 ACRES
PORTION OF VESTING
T.T.M. 15990
DATE OF SURVEY:
JANUARY, 1999

TRACT MAP NO. 16472

IN THE UNINCORPORATED TERRITORY OF THE COUNTY OF ORANGE,
STATE OF CALIFORNIA

HALL & FOREMAN, INC.

STEVEN C. SHAMBECK, P.L.S. 6217
MAY, 2004

SEE SHEET 2 FOR BASIS OF
BEARINGS, DATUM STATEMENT,
MONUMENT NOTES, EASEMENT
NOTES AND NOTES

DATA FROM SHEET NO. 3

CURVE DATA			
CURVE	DELTA	RADIUS	LENGTH
C1	17°29'13"	213.00'	85.01'
C2	22°57'37"	174.00'	69.73'
C3	18°31'48"	120.00'	38.81'
C4	9°51'25"	113.00'	19.44'
C5	12°28'51"	50.00'	10.89'
C6	38°41'54"	75.00'	50.66'
C7	1°20'26"	82.00'	1.92'
C8	15°50'59"	158.00'	43.71'
C9	13°32'32"	55.00'	13.00'
C10	58°08'28"	157.00'	159.32'
C11	13°32'32"	55.00'	13.00'
C12	1°25'28"	158.00'	3.93'
C13	11°37'21"	168.00'	34.08'
C14	20°36'32"	164.00'	58.99'
C15	9°40'10"	50.00'	8.44'
C16	11°00'25"	77.00'	14.79'
C17	25°11'20"	25.00'	10.99'
C18	9°55'27"	125.00'	21.65'
C19	4°11'25"	245.00'	17.92'
C20	2°43'15"	289.00'	13.72'
C21	15°40'27"	333.00'	91.10'
C22	1°55'22"	450.00'	15.10'
C23	5°48'17"	365.00'	36.98'
C24	6°52'50"	200.00'	24.02'
C25	25°59'49"	141.00'	63.98'
C26	25°35'31"	141.00'	62.98'
C27	13°27'38"	194.00'	45.58'
C28	23°41'21"	155.00'	64.09'
C29	98°07'01"	57.00'	97.61'
C30	21°45'28"	72.00'	27.34'
C31	53°36'47"	36.00'	33.69'
C32	66°48'37"	49.00'	57.14'
C33	89°13'26"	27.00'	42.05'
C34	35°01'02"	47.00'	28.72'
C35	56°52'41"	80.00'	79.42'
C36	16°43'11"	229.00'	66.83'
C37	82°11'42"	24.00'	34.43'
C38	62°32'48"	24.00'	26.20'
C39	12°20'13"	318.00'	68.47'
C40	69°25'29"	25.00'	30.29'
C41	0°11'07"	329.00'	1.06'
C42	66°15'48"	25.00'	28.91'
C43	2°50'09"	1595.00'	78.94'
C44	9°40'14"	460.00'	77.64'
C45	83°14'09"	33.00'	47.94'
C46	73°04'12"	25.00'	31.88'
C47	6°19'17"	150.00'	16.55'
C48	5°05'32"	600.00'	53.33'
C49	58°07'51"	25.00'	25.36'
C50	2°21'54"	279.00'	11.52'
C51	1°51'00"	250.00'	8.07'
C52	5°34'57"	221.00'	21.52'
C53	76°17'30"	25.00'	33.29'
C54	8°06'20"	492.00'	69.60'
C55	22°31'36"	520.00'	204.45'
C56	1°56'39"	520.00'	17.65'
C57	20°34'57"	520.00'	186.80'
C58	18°57'36"	500.00'	165.46'
C59	18°39'22"	500.00'	162.81'
C60	5°15'51"	250.00'	22.97'
C61	37°53'17"	250.00'	165.32'
C62	26°48'15"	250.00'	116.96'
C63	11°05'02"	250.00'	48.36'
C64	0°33'37"	221.00'	2.16'
C65	9°56'58"	99.00'	17.19'
C66	6°18'22"	500.00'	55.03'
C67	2°23'39"	389.50'	16.28'

LINE DATA		
LINE	BEARING	LENGTH
L1	N44°06'30"E	4.11'
L2	N53°54'13"W	78.65'
L3	N79°34'47"E	5.51'
L4	N53°54'13"W	55.08'
L5	N79°34'47"E	6.89'
L7	N77°11'01"E	5.75'
L8	N58°53'56"W	68.51'
L9	N72°07'46"E	6.63'
L10	N58°53'56"W	82.04'
L11	N77°48'09"W	60.93'
L12	N85°29'51"W	68.54'
L13	N41°32'21"E	10.16'
L14	N86°33'00"W	55.25'
L15	N53°43'36"E	4.84'
L16	N71°18'46"W	58.79'
L17	N53°22'03"E	3.65'
L18	N71°16'45"W	58.80'
L19	N53°22'03"E	3.65'
L20	N71°16'45"W	14.93'
L21	N04°59'12"W	6.14'
L22	N46°11'20"E	59.97'
L23	N00°29'31"W	9.47'
L24	N03°50'16"E	4.46'
L25	N33°13'09"W	4.12'
L26	N66°30'42"W	4.00' (RAD)
L27	N55°37'53"E	2.51' (RAD)
L28	N47°50'31"E	4.71'
L29	N77°01'58"E	37.83'
L30	N45°21'39"W	38.84'
L31	N59°18'06"E	29.97'
L32	N28°47'27"W	15.00' (RAD)
L33	N46°11'15"W	59.93'
L34	N44°35'19"E	33.37'
L35	N88°31'32"W	6.24'
L36	N80°28'24"W	19.36'
L37	N18°00'20"E	29.12'
L38	N21°34'54"E	10.50'
L39	N68°25'06"W	18.00'
L40	N50°11'32"E	18.79'
L41	N21°34'54"E	12.50'
L42	N21°34'54"E	12.50'
L43	N21°34'54"E	25.00'
L44	N07°01'43"W	18.79'
L45	N68°25'06"W	18.00'
L46	N21°34'54"E	12.95'
L47	N18°00'45"E	81.86'
L48	N70°52'35"E	26.92'
L49	N42°09'51"E	12.68'
L50	N48°47'43"W	16.40'
L51	N70°46'29"E	18.79'
L52	N42°09'51"E	12.50'
L53	N47°50'09"W	0.35'
L54	N42°09'51"E	12.50'
L55	N13°35'59"E	18.82'
L57	N42°09'51"E	7.46'
L58	N85°05'19"W	28.58'
L59	N59°42'05"W	2.19' (RAD)
L60	N25°27'08"E	7.55'
L61	N64°32'52"W	20.40'
L62	N54°03'46"E	18.79'
L63	N25°27'08"E	12.50'
L64	N25°27'08"E	12.50'
L65	N25°27'08"E	25.00'
L66	N03°09'29"W	18.79'
L67	N64°32'52"W	20.40'
L68	N25°27'08"E	8.98'
L69	N69°38'47"E	20.98'
L70	N06°57'35"E	6.55'
L71	N02°21'33"E	98.01'
L72	N27°07'22"E	8.54' (RAD)
L73	N52°34'22"E	18.82'
L74	N22°50'25"E	12.50' (RAD)
L75	N24°41'25"E	12.50' (RAD)
L76	N02°37'48"W	18.76'
L77	N33°03'47"E	10.85' (RAD)
L78	N68°25'06"W	43.00'
L79	N47°50'09"W	41.65'
L80	N64°32'52"W	44.67'
L81	N72°25'26"W	14.04'