

SHEET 1 OF 10 SHEETS
62 NUMBERED LOTS
18 LETTERED LOTS
23.224 ACRES
PORTION OF VESTING
T.T.M. 15990
DATE OF SURVEY:
JANUARY, 1999

TRACT MAP NO. 16473

IN THE UNINCORPORATED TERRITORY OF THE COUNTY OF ORANGE,
STATE OF CALIFORNIA

BEING A SUBDIVISION OF A PORTION OF PARCEL 1 OF LOT LINE ADJUSTMENT NO. LL 96-026, IN THE UNINCORPORATED TERRITORY OF THE COUNTY OF ORANGE, STATE OF CALIFORNIA, AS SHOWN ON EXHIBIT "B" ATTACHED TO THAT CERTAIN DOCUMENT RECORDED NOVEMBER 21, 1996 AS INSTRUMENT NO. 19960587414 OF OFFICIAL RECORDS, IN THE OFFICE OF THE COUNTY RECORDER OF SAID COUNTY.

HALL & FOREMAN, INC.

STEVEN C. SHAMBECK, P.L.S. 6217
MAY, 2004

ACCEPTED AND FILED AT THE
REQUEST OF

FIRST AMERICAN TITLE INSURANCE COMPANY

DATE October 26, 2004

TIME 11:18 AM FEE\$ 34.00

INSTRUMENT # 2004 000963390

BOOK 862 PAGE 11-20 m/m

TOM DALY
COUNTY CLERK-RECORDER

BY [Signature]
DEPUTY

OWNERSHIP CERTIFICATE

WE, THE UNDERSIGNED, BEING ALL PARTIES HAVING ANY RECORD TITLE INTEREST IN THE LAND COVERED BY THIS MAP, DO HEREBY CONSENT TO THE PREPARATION AND RECORDATION OF SAID MAP, AS SHOWN WITHIN THE DISTINCTIVE BORDER LINE.

WE HEREBY DEDICATE TO THE COUNTY OF ORANGE:

1. THE EASEMENT FOR EMERGENCY ACCESS PURPOSES OVER ALL OF LOTS BA, THROUGH BF AS SHOWN ON SAID MAP.
2. THE EASEMENT FOR PUBLIC PEDESTRIAN PURPOSES AS SHOWN ON SAID MAP.

WE ALSO HEREBY DEDICATE TO THE SANTA MARGARITA WATER DISTRICT THE EASEMENTS FOR WATER, RECYCLED WATER, SEWER, DRAINAGE, AND ACCESS PURPOSES OVER THOSE EASEMENT AREAS AS SHOWN ON SAID MAP WHICH EASEMENTS SHALL BE SUBJECT TO THE SAME CONDITIONS AS ARE SHOWN IN THAT CERTAIN GRANT OF EASEMENT TO SANTA MARGARITA WATER DISTRICT RECORDED SEPTEMBER 18, 2002 AS INSTRUMENT NO. 20020799401, OF OFFICIAL RECORDS, COUNTY OF ORANGE.

DMB LADERA, L.L.C., A DELAWARE LIMITED LIABILITY COMPANY

BY: RANCHO MISSION VIEJO, L.L.C. A DELAWARE LIMITED LIABILITY COMPANY,
IT'S AUTHORIZED AGENT AND MANAGER.

BY: [Signature] BY: [Signature]
PRINT NAME: PAUL JOHNSON PRINT NAME: Greg Edwards
PRINT TITLE: SVP - COMM. DEVL. PRINT TITLE: Sr. V.P. - CFO

NOTARY ACKNOWLEDGEMENT

STATE OF California
COUNTY OF Orange, SS

ON July 29, 2004 BEFORE ME, Diana L. Binks

PERSONALLY APPEARED Paul Johnson and Greg Edwards
PERSONALLY KNOWN TO ME (OR PROVED TO ME ON THE BASIS OF SATISFACTORY EVIDENCE) TO BE THE PERSON(S) WHOSE NAME(S) IS/ARE SUBSCRIBED TO THE WITHIN INSTRUMENT AND ACKNOWLEDGED TO ME THAT HE/SHE/ THEY EXECUTED THE SAME IN HIS/HER/ THEIR AUTHORIZED CAPACITY(IES), AND THAT BY HIS/ HER/ THEIR SIGNATURE(S) ON THE INSTRUMENT THE PERSON(S) OR THE ENTITY UPON BEHALF OF WHICH THE PERSON(S) ACTED, EXECUTED THE INSTRUMENT.

WITNESS MY HAND:

Diana L. Binks
NOTARY PUBLIC IN AND FOR SAID STATE

Diana L. Binks
PRINT NAME

MY PRINCIPAL PLACE OF BUSINESS IS IN Orange COUNTY
MY COMMISSION EXPIRES Dec. 12, 2006

CERTIFICATE OF ACCEPTANCE

THE UNDERSIGNED, BEING THE DULY APPOINTED AGENT OF THE SANTA MARGARITA WATER DISTRICT, A PUBLIC CORPORATION OF ORANGE COUNTY, CALIFORNIA, PURSUANT TO ITS RESOLUTION NO. 88-10-02, DOES HEREBY ACCEPT ON BEHALF OF SAID DISTRICT THE EASEMENTS FOR, WATER, RECYCLED WATER, SEWER, DRAINAGE, AND ACCESS PURPOSES, AS DEDICATED AND AS SHOWN ON THIS TRACT MAP, BY AND BETWEEN THE SANTA MARGARITA WATER DISTRICT AND DMB LADERA, L.L.C., AND DOES HEREBY CERTIFY THAT THE GRANTEE CONSENTS TO THE RECORDATION OF SAID TRACT.

[Signature]
DANIEL R. FERONS, CHIEF ENGINEER
SANTA MARGARITA WATER DISTRICT

SURVEYOR'S STATEMENT

THIS MAP WAS PREPARED BY ME OR UNDER MY DIRECTION AND IS BASED UPON A FIELD SURVEY IN CONFORMANCE WITH THE REQUIREMENTS OF THE SUBDIVISION MAP ACT AND LOCAL ORDINANCE AT THE REQUEST OF DMB LADERA, LLC IN JANUARY, 1999. I HEREBY STATE THAT ALL MONUMENTS ARE OF THE CHARACTER AND OCCUPY THE POSITIONS INDICATED, OR THAT THEY WILL BE SET IN SUCH POSITIONS; AND THAT SAID MONUMENTS ARE SUFFICIENT TO ENABLE THE SURVEY TO BE RETRACED. I HEREBY STATE THAT THIS FINAL MAP SUBSTANTIALLY CONFORMS TO THE CONDITIONALLY APPROVED TENTATIVE MAP.

[Signature]
STEVEN C. SHAMBECK, P.L.S. 6217
LICENSE EXPIRES: 3/31/06

7-21-2004
DATE



COUNTY SURVEYOR'S STATEMENT

I HEREBY STATE THAT I HAVE EXAMINED THIS MAP AND HAVE FOUND IT TO BE SUBSTANTIALLY IN CONFORMANCE WITH THE TENTATIVE MAP AS FILED WITH, AMENDED AND APPROVED BY THE ORANGE COUNTY SUBDIVISION COMMITTEE; THAT ALL PROVISIONS OF THE SUBDIVISION MAP ACT AND COUNTY SUBDIVISION REGULATIONS HAVE BEEN COMPLIED WITH AND I AM SATISFIED SAID MAP IS TECHNICALLY CORRECT.

DATED THIS 27th DAY OF September, 2004.

[Signature]
RAYMOND L. MATHE, COUNTY SURVEYOR
L.S. 6185 EXPIRATION DATE: 3-31-06



CLERK OF THE BOARD OF SUPERVISOR'S CERTIFICATE

STATE OF CALIFORNIA } SS
COUNTY OF ORANGE }

I HEREBY CERTIFY THAT THIS MAP WAS PRESENTED FOR APPROVAL TO THE BOARD OF SUPERVISORS OF ORANGE COUNTY AT A REGULAR MEETING THEREOF HELD ON THE 19th DAY OF October, 2004 AND THAT THEREUPON SAID BOARD DID, BY AN ORDER DULY PASSED AND ENTERED, APPROVE SAID MAP.

AND DID ACCEPT ON BEHALF OF THE COUNTY OF ORANGE:

1. THE EASEMENT FOR EMERGENCY ACCESS PURPOSES OVER ALL OF LOTS BA THROUGH BF AS DEDICATED.
2. THE EASEMENT FOR PUBLIC PEDESTRIAN PURPOSES AS DEDICATED.

AND DID ALSO APPROVE SUBJECT MAP PURSUANT TO THE PROVISIONS OF SECTION 66436(a)(3)(A) AND (C) OF THE SUBDIVISION MAP ACT.

DATED THIS 19th DAY OF October, 2004.

[Signature]
DARLENE J. BLOOM
CLERK OF THE BOARD OF SUPERVISORS



COUNTY TREASURER-TAX COLLECTOR'S CERTIFICATE

STATE OF CALIFORNIA)
COUNTY OF ORANGE) SS

I HEREBY CERTIFY THAT ACCORDING TO THE RECORDS OF MY OFFICE THERE ARE NO LIENS AGAINST THE LAND COVERED BY THIS MAP OR ANY PART THEREOF FOR UNPAID STATE, COUNTY, MUNICIPAL OR LOCAL TAXES OR SPECIAL ASSESSMENTS COLLECTED AS TAXES, EXCEPT TAXES OR SPECIAL ASSESSMENTS COLLECTED AS TAXES.

AND DO CERTIFY TO THE RECORDER OF THE COUNTY OF ORANGE THAT THE PROVISIONS OF THE SUBDIVISION MAP ACT HAVE BEEN COMPLIED WITH REGARDING DEPOSITS TO SECURE PAYMENT OF TAXES OR SPECIAL ASSESSMENTS COLLECTED AS TAXES ON THE LAND COVERED BY THIS MAP.

DATED THIS 26th DAY OF August, 2004.

JOHN M.W. MOORLACH
COUNTY TREASURER-TAX COLLECTOR

BY: [Signature]
DEPUTY TREASURER -
TAX COLLECTOR

SEE SHEET 2 FOR ADDITIONAL NOTARY ACKNOWLEDGMENT AND SIGNATURE OMISSIONS

SHEET 2 OF 10 SHEETS
62 NUMBERED LOTS
18 LETTERED LOTS
23.224 ACRES
PORTION OF VESTING
T.T.M. 15990
DATE OF SURVEY:
JANUARY, 1999

TRACT MAP NO. 16473

IN THE UNINCORPORATED TERRITORY OF THE COUNTY OF ORANGE,
STATE OF CALIFORNIA

HALL & FOREMAN, INC.

STEVEN C. SHAMBECK, P.L.S. 6217
MAY, 2004

SANTA MARGARITA WATER DISTRICT

STATE OF CALIFORNIA)
COUNTY OF ORANGE)

ON THIS 20th DAY OF August 2004, BEFORE ME, Kristen S. Collins
A NOTARY PUBLIC IN AND FOR SAID STATE, PERSONALLY APPEARED DANIEL R.
FERONS PERSONALLY KNOWN TO ME OR PROVED TO ME ON THE BASIS OF SATISFACTORY
EVIDENCE TO BE THE PERSON WHOSE NAME IS SUBSCRIBED TO THE WITHIN INSTRUMENT
AND ACKNOWLEDGED TO ME THAT HE EXECUTED THE SAME IN HIS AUTHORIZED CAPACITY,
AND THAT BY HIS SIGNATURE ON THE INSTRUMENT THE PERSON OR THE ENTITY UPON
BEHALF OF WHICH THE PERSON ACTED, EXECUTED THE INSTRUMENT.

WITNESS MY HAND:

MY COMMISSION EXPIRES January 20, 2008

Kristen S. Collins MY PRINCIPAL PLACE OF BUSINESS
NOTARY PUBLIC IN AND FOR SAID STATE IS IN Orange COUNTY

Kristen S. Collins
PRINT NAME

AUTOMATIC FIRE SPRINKLER NOTE:
ALL MULTIFAMILY RESIDENTIAL STRUCTURES; ALL SINGLE FAMILY STRUCTURES EXCEEDING
5,500 SQUARE FEET AND ALL STRUCTURES EXCEEDING FIRE DEPARTMENT ACCESS
REQUIREMENTS SHALL BE PROTECTED BY AN AUTOMATIC SPRINKLER SYSTEM, IN A
MANNER MEETING THE APPROVAL OF THE FIRE CHIEF.

SPECIAL FIRE PROTECTION NOTE:
PROPERTY IS IN A SPECIAL FIRE PROTECTION AREA.

HIGH FIRE HAZARD AREA NOTE:
THE LOTS SHOWN ON THIS MAP ARE IN A HIGH/VERY HIGH FIRE HAZARD AREA DUE TO
WILD LAND EXPOSURE.

SIGNATURE OMISSIONS

PURSUANT TO THE PROVISIONS OF SECTION 66436 (a)(3)(A) AND (C) OF
THE SUBDIVISION MAP ACT, THE FOLLOWING SIGNATURES HAVE BEEN
OMITTED:

LADERA DEVELOPMENT COMPANY, L.L.C., HOLDER OF OIL, GAS, AND MINERAL
RIGHTS PER DEED RECORDED DECEMBER 10, 1996 AS INSTRUMENT NO.
19960624029 OF OFFICIAL RECORDS.

SAN DIEGO GAS & ELECTRIC COMPANY HOLDER OF AN EASEMENT FOR PUBLIC
UTILITIES AND INCIDENTAL PURPOSES PER DOCUMENT RECORDED FEBRUARY 27,
2004 AS INSTRUMENT NO. 2004000153368 OF OFFICIAL RECORDS.

NOTES:

"THE PRIVATE STREETS CONSTRUCTED WITHIN THIS
MAP SHALL BE OWNED, OPERATED AND MAINTAINED BY
THE DEVELOPER, SUCCESSORS OR ASSIGNS. THE
COUNTY OF ORANGE SHALL HAVE NO RESPONSIBILITY
THEREFORE UNLESS PURSUANT TO APPROPRIATE
SECTIONS OF THE STREETS AND HIGHWAYS CODE OF
THE STATE OF CALIFORNIA, THE SAID PRIVATE
STREETS HAVE BEEN ACCEPTED INTO THE COUNTY ROAD
SYSTEM BY APPROPRIATE RESOLUTION OF THE ORANGE
COUNTY BOARD OF SUPERVISORS."

EASEMENT NOTES

- ☒ INDICATES WATER, RECYCLED WATER, SEWER AND ACCESS
EASEMENT DEDICATED TO SANTA MARGARITA WATER DISTRICT.
- ☒ INDICATES DRAINAGE AND ACCESS EASEMENT DEDICATED TO
SANTA MARGARITA WATER DISTRICT.
- ☒ INDICATES SAN DIEGO GAS & ELECTRIC COMPANY EASEMENT FOR
PUBLIC UTILITIES AND INCIDENTAL PURPOSES PER DOCUMENT
RECORDED FEBRUARY 27, 2004 AS INSTRUMENT NO.
2004000153368 OF OFFICIAL RECORDS.
- ☒ INDICATES PUBLIC PEDESTRIAN EASEMENT AS
DEDICATED TO THE COUNTY OF ORANGE.

BASIS OF BEARINGS

THE BEARINGS SHOWN HEREON ARE BASED ON THE BEARING BETWEEN
O.C.S. HORIZONTAL CONTROL STATION GPS NO. 1417 AND STATION
GPS NO. 1448, BEING NORTH 10°48'13" EAST PER RECORDS ON FILE
IN THE OFFICE OF THE ORANGE COUNTY SURVEYOR.

DATUM STATEMENT

COORDINATES SHOWN ARE BASED ON THE CALIFORNIA COORDINATE
SYSTEM (CCS 83), ZONE VI, 1983 NAD (1991.35 EPOCH OCS GPS
ADJUSTMENT). ALL DISTANCES ARE GROUND DISTANCES UNLESS
OTHERWISE NOTED. TO OBTAIN GRID DISTANCE MULTIPLY GROUND
DISTANCE BY 0.999948295. THIS FACTOR IS PROJECT-SPECIFIC.

MONUMENT NOTES

- INDICATES FOUND MONUMENT AS NOTED.
- ☒ INDICATES FOUND 2 1/2" IRON PIPE W/2" OCS BRASS CAP STAMPED "GPS
1448 9-95" PER TRACT NO. 16203, M.M. 826/8-20 AND RECORDS ON FILE
IN THE ORANGE COUNTY SURVEYORS OFFICE.
N2146790.819, E6142602.585
- ☒ INDICATES FOUND 2 1/2" IRON PIPE W/2" OCS BRASS CAP STAMPED "GPS
1417 9-95" PER TRACT NO. 16203, M.M. 826/8-20 AND RECORDS ON FILE
IN THE ORANGE COUNTY SURVEYORS OFFICE.
N2141450.558, E6141583.535
- ☐ INDICATES 2" I.P. TAGGED L.S. 6217 OR SPIKE & WASHER STAMPED L.S.
6217 OR LEAD, TACK & TAG L.S. 6217 TO BE SET PER TRACT NO. 16471
M.M. 861/ 42-49 UNLESS OTHERWISE NOTED.
- ☒ INDICATES 1" I.P. TAGGED L.S. 6217 OR SPIKE & WASHER STAMPED L.S.
6217 OR LEAD, TACK & TAG L.S. 6217 TO BE SET PER TRACT NO. 16471
M.M. 861/ 42-49 UNLESS OTHERWISE NOTED.
- ☐ INDICATES 2" I.P. TAGGED L.S. 6217 OR SPIKE & WASHER STAMPED L.S.
6217 OR LEAD, TACK & TAG L.S. 6217 TO BE SET PER TRACT NO. 16472
M.M. 862/ 1-10 UNLESS OTHERWISE NOTED.
- 2" I.P. TAGGED L.S. 6217 OR SPIKE & WASHER STAMPED L.S. 6217
OR LEAD, TACK & TAG L.S. 6217 TO BE SET AT ALL TRACT BOUNDARY
CORNERS WITHIN 90 DAYS AFTER ACCEPTANCE OF IMPROVEMENTS.
- 1" I.P. TAGGED L.S. 6217 OR SPIKE & WASHER STAMPED L.S. 6217 OR
LEAD, TACK & TAG L.S. 6217 TO BE SET AT LOT CORNERS WITHIN 90 DAYS
AFTER ACCEPTANCE OF IMPROVEMENTS.
- 1" I.P. TAGGED L.S. 6217 OR SPIKE & WASHER STAMPED L.S. 6217 OR
LEAD, TACK & TAG L.S. 6217 TO BE SET AT ALL CENTERLINE INTERSECTIONS,
E.C.'S AND B.C.'S WITHIN 90 DAYS AFTER ACCEPTANCE OF IMPROVEMENTS.
- ☐ INDICATES 2" I.P. TAGGED L.S. 6217 OR SPIKE & WASHER
STAMPED L.S. 6217 OR LEAD, TACK & TAG L.S. 6217 TO BE
SET PRIOR TO MAP RECORDATION.

NOTES

LOTS BA THROUGH BF ARE FOR PRIVATE STREET PURPOSES AND ARE NOT
SEPARATE BUILDING SITES.

LOTS A THROUGH L ARE FOR LANDSCAPE/OPEN SPACE PURPOSES AND
ARE NOT SEPARATE BUILDING SITES.

LOTS 60 THROUGH 62 ARE NOT RESIDENTIAL BUILDING SITES, BUT ARE PRIVATE
RECREATION SITES.

() INDICATES MEASURED AND RECORD PER TRACT NO. 16471 M.M. 861/ 42-49

[] INDICATES MEASURED AND RECORD PER TRACT NO. 16472 M.M. 862/ 1-10

862 13

SHEET 3 OF 10 SHEETS
62 NUMBERED LOTS
18 LETTERED LOTS
23.224 ACRES
PORTION OF VESTING
T.T.M. 15990
DATE OF SURVEY:
JANUARY, 1999

SEE SHEET 2 FOR BASIS OF
BEARINGS, DATUM STATEMENT,
MONUMENT NOTES, EASEMENT
NOTES AND NOTES
SEE SHEET 10 FOR CURVE DATA
AND LINE DATA


TRACT MAP NO. 16473

IN THE UNINCORPORATED TERRITORY OF THE COUNTY OF ORANGE,
STATE OF CALIFORNIA

HALL & FOREMAN, INC.

STEVEN C. SHAMBECK, P.L.S. 6217
MAY, 2004

BOUNDARY AND INDEX SHEET

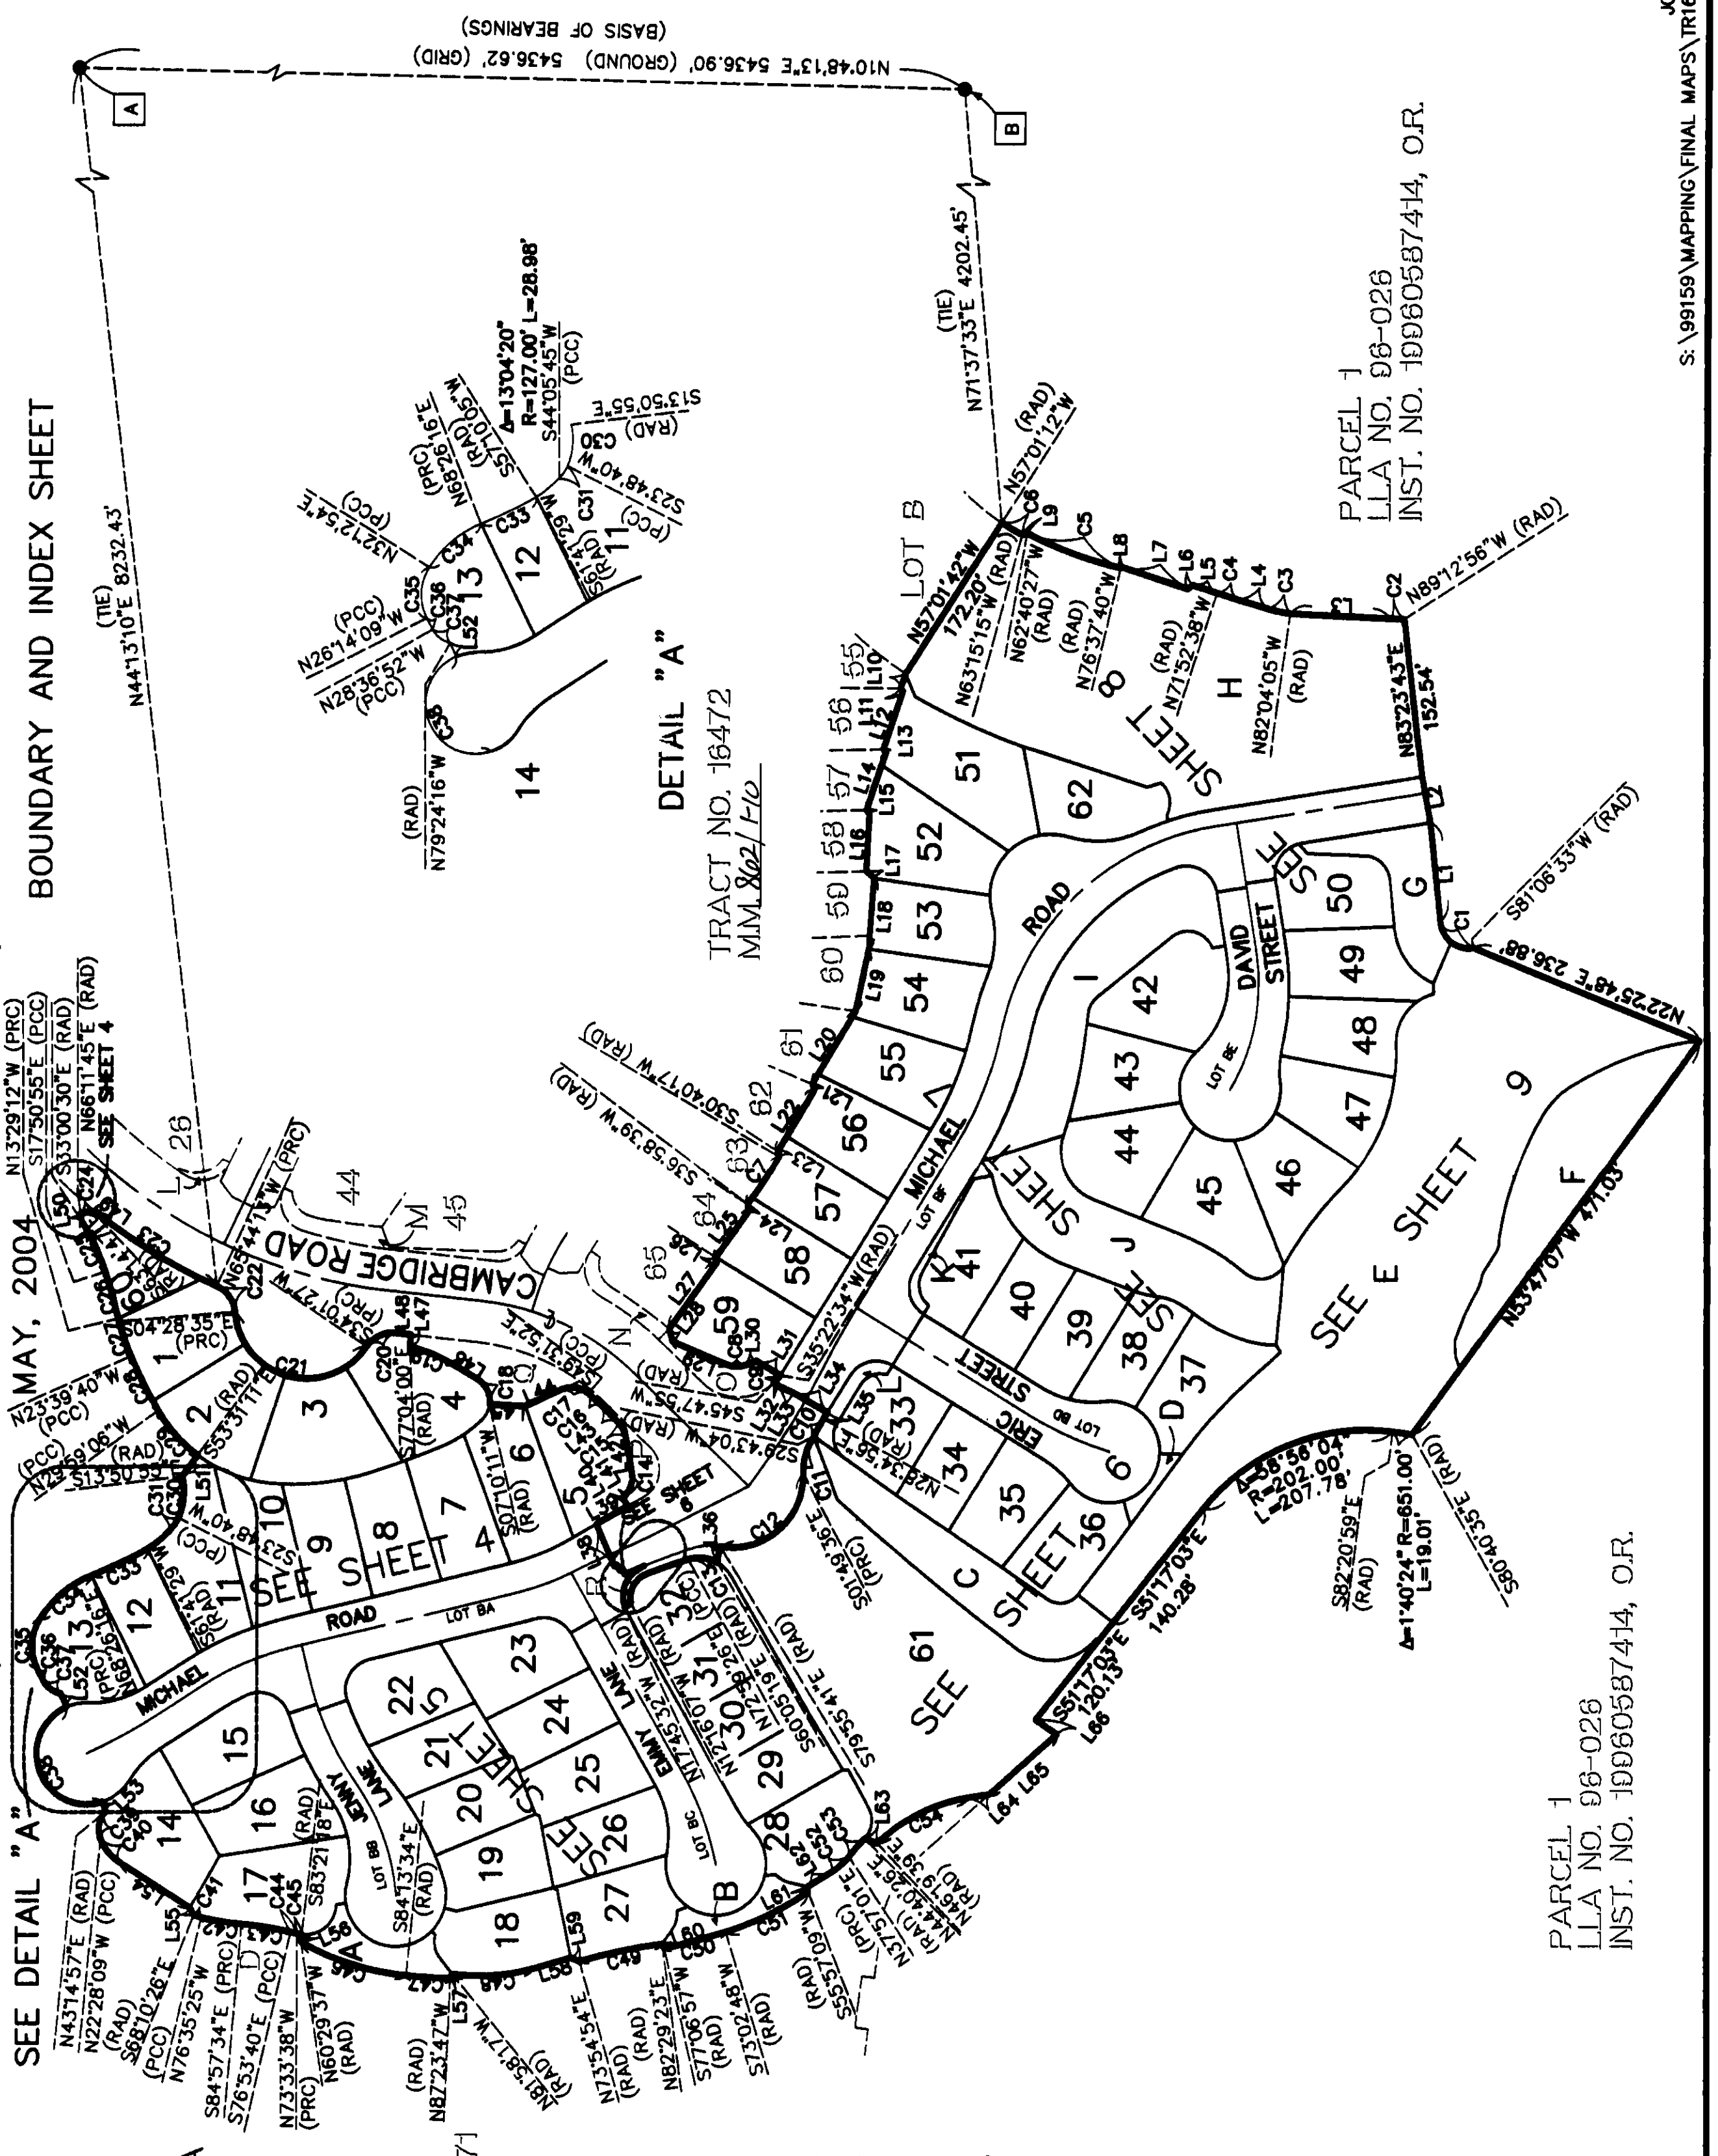

TRACT NO. 16473
M.M. 80/42-49

PARCEL 1
LLA NO. 98-026
INST. NO. 10060587414, O.R.

PARCEL 1
LLA NO. 98-026
INST. NO. 10060587414, O.R.

SHEET 4 OF 10 SHEETS
62 NUMBERED LOTS
18 LETTERED LOTS
23.224 ACRES
PORTION OF VESTING
T.T.M. 15990
DATE OF SURVEY:
JANUARY, 1999

TRACT MAP NO. 16473


IN THE UNINCORPORATED TERRITORY OF THE COUNTY OF ORANGE,
STATE OF CALIFORNIA

HALL & FOREMAN, INC.

STEVEN C. SHAMBECK, P.L.S. 6217
MAY, 2004

SEE SHEET 2 FOR BASIS OF
BEARINGS, DATUM STATEMENT,
MONUMENT NOTES, EASEMENT
NOTES AND NOTES

TRACT NO. 16471
M.M. 801 / 42-49

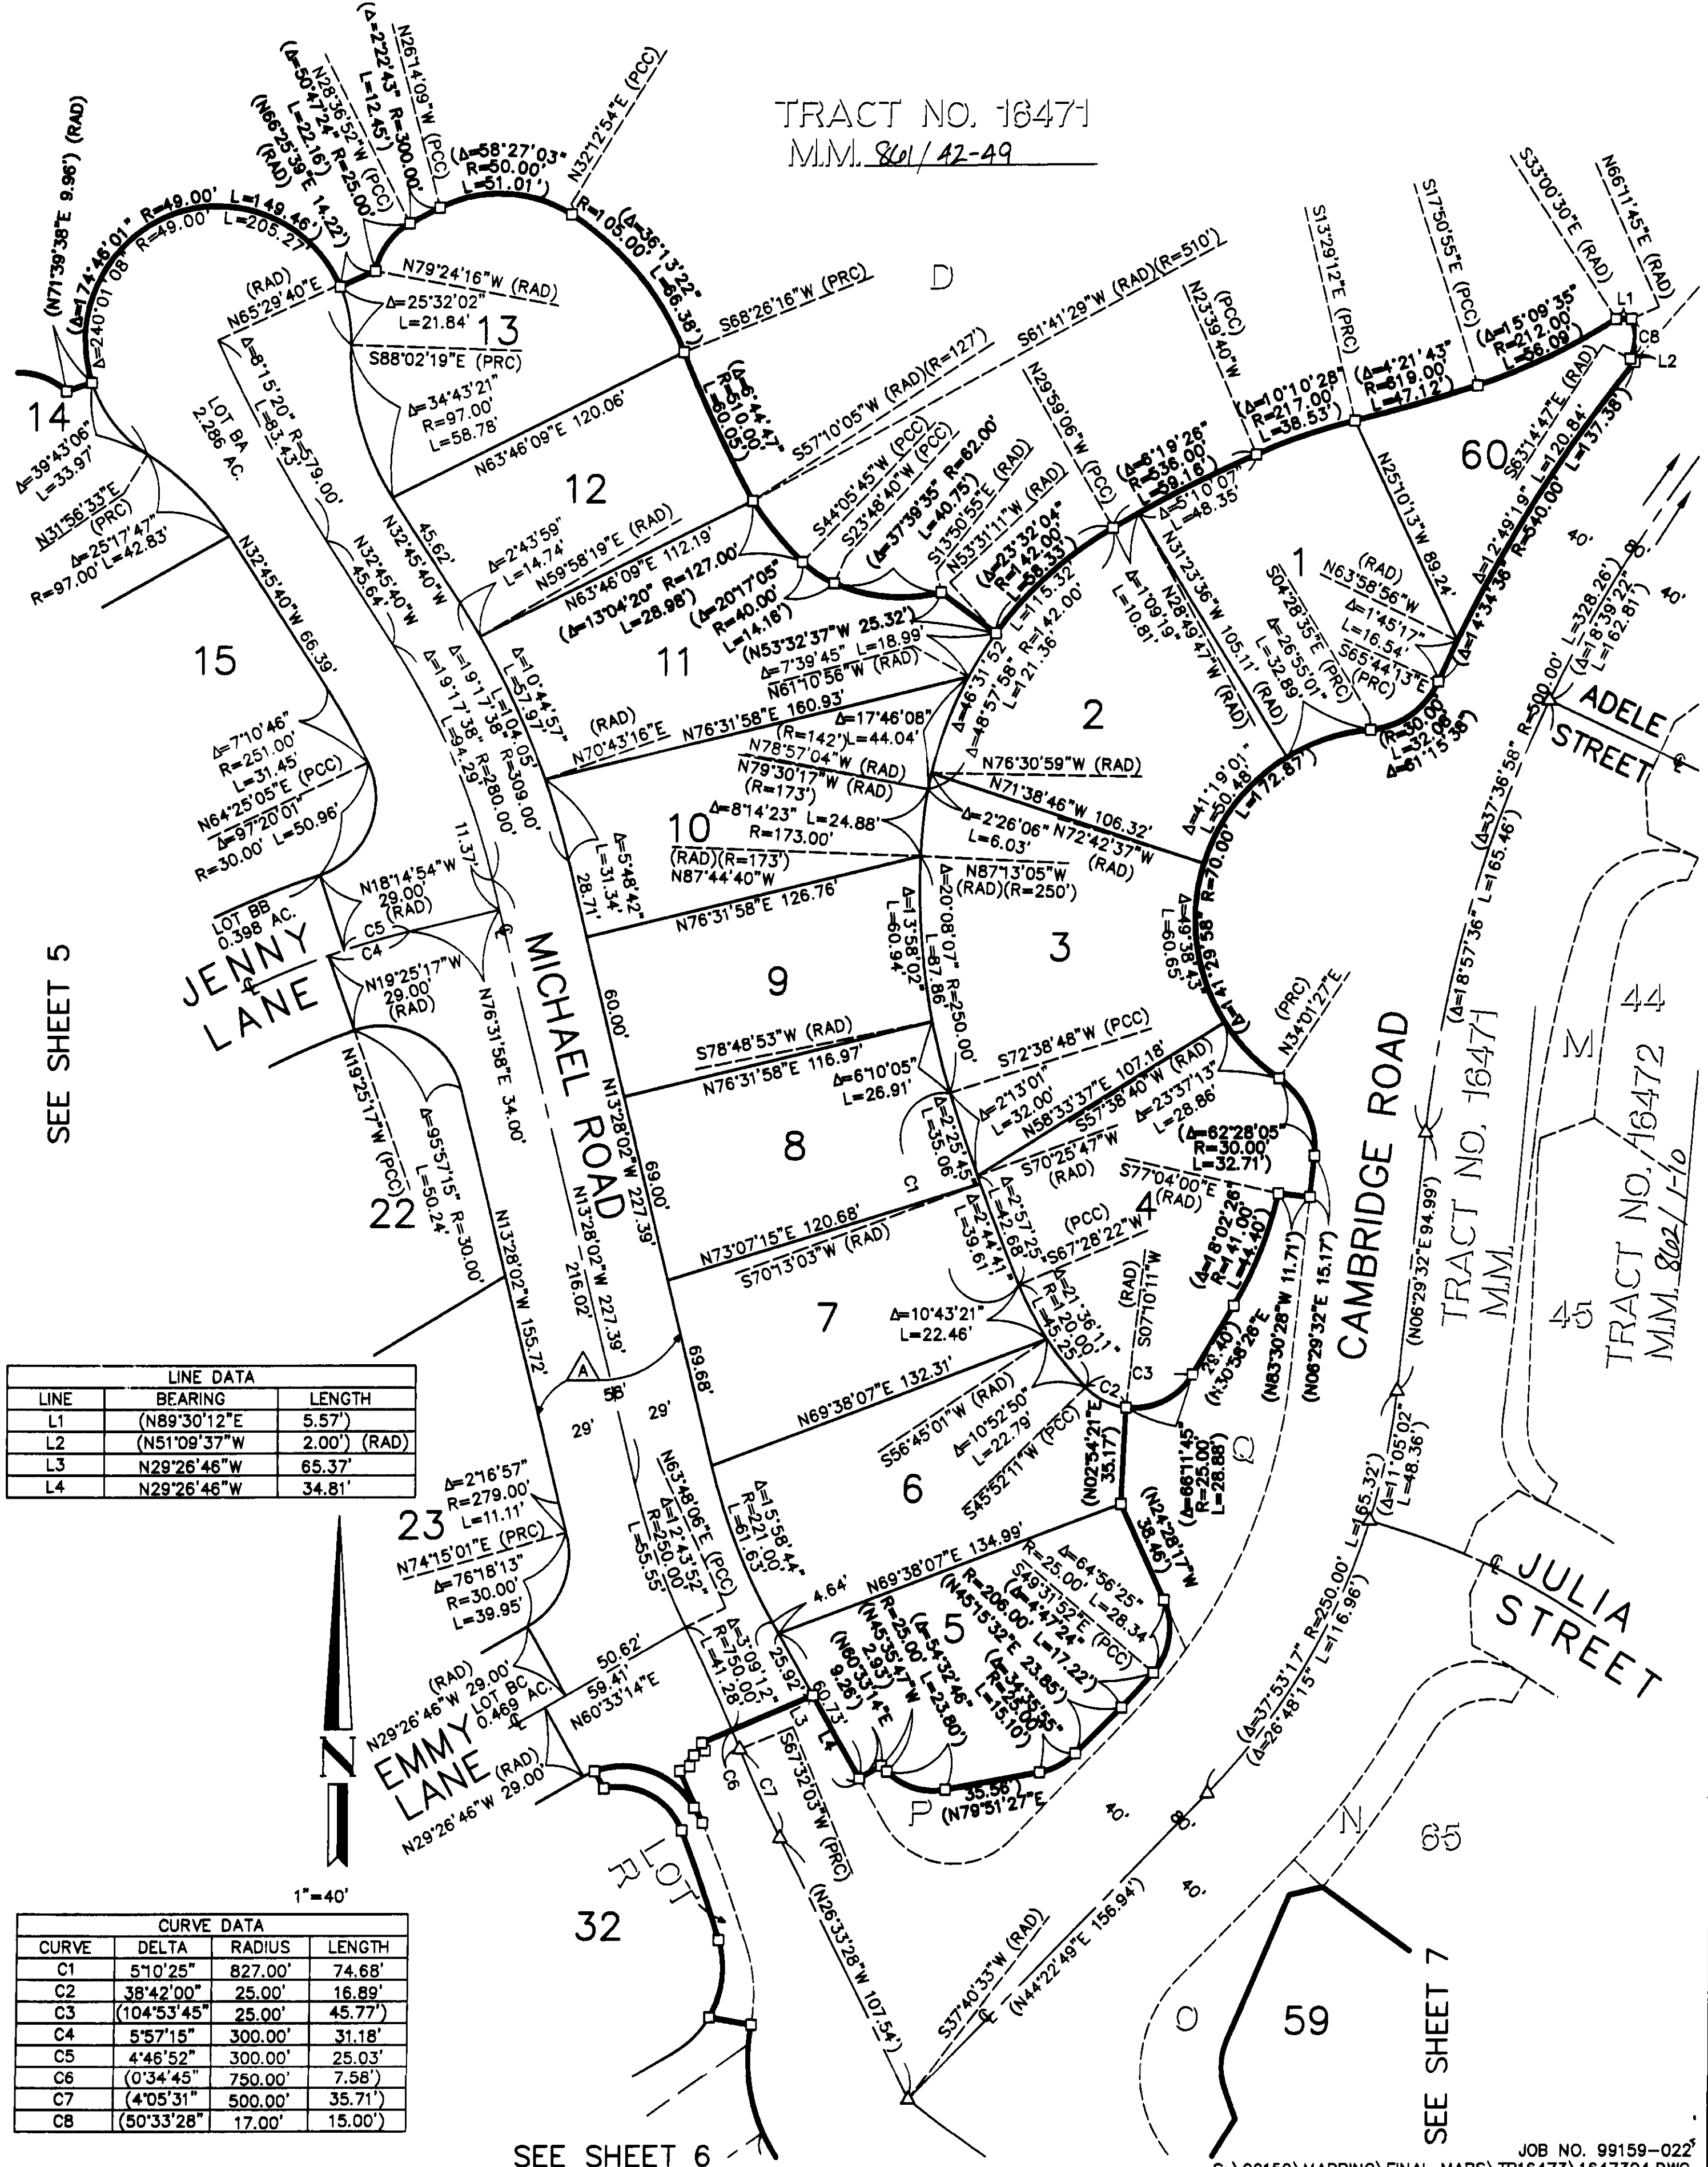

LINE DATA		
LINE	BEARING	LENGTH
L1	(N89°30'12"E	5.57')
L2	(N51°09'37"W	2.00') (RAD)
L3	(N29°26'46"W	65.37'
L4	(N29°26'46"W	34.81'

CURVE DATA			
CURVE	DELTA	RADIUS	LENGTH
C1	5°10'25"	827.00'	74.68'
C2	38°42'00"	25.00'	16.89'
C3	(104°53'45"	25.00'	45.77')
C4	5°57'15"	300.00'	31.18'
C5	4°46'52"	300.00'	25.03'
C6	(0°34'45"	750.00'	7.58')
C7	(4°05'31"	500.00'	35.71')
C8	(50°33'28"	17.00'	15.00')

SEE SHEET 6

SEE SHEET 7

SHEET 5 OF 10 SHEETS
62 NUMBERED LOTS
18 LETTERED LOTS
23.224 ACRES
PORTION OF VESTING
T.T.M. 15990
DATE OF SURVEY:
JANUARY, 1999


TRACT MAP NO. 16473

IN THE UNINCORPORATED TERRITORY OF THE COUNTY OF ORANGE,
STATE OF CALIFORNIA

HALL & FOREMAN, INC.

STEVEN C. SHAMBECK, P.L.S. 6217
MAY, 2004

SEE SHEET 2 FOR BASIS OF
BEARINGS, DATUM STATEMENT,
MONUMENT NOTES, EASEMENT
NOTES AND NOTES

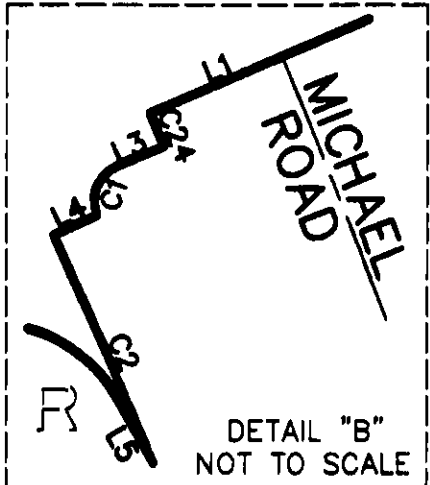

TRACT NO. 16471
M.M. 801/42-49

CURVE DATA			
CURVE	DELTA	RADIUS	LENGTH
C1	(92°01'47"")	3.00'	4.82'
C2	(2°29'26"")	477.00'	20.73'
C3	(81°04'51"")	30.00'	42.45'
C4	(8°55'09"")	30.00'	4.67'
C5	(81°14'56"")	25.00'	35.45'
C6	(22°14'05"")	49.00'	19.02'
C7	(94°37'58"")	30.00'	49.55'
C8	(9°47'40"")	30.00'	5.13'
C9	(3°20'02"")	108.00'	6.28'
C10	(53°53'29"")	25.00'	23.51'
C11	(36°33'41"")	25.00'	15.95'
C12	(30°16'48"")	49.00'	25.90'
C13	(19°59'29"")	49.00'	17.10'
C14	(60°46'36"")	49.00'	51.98'
C15	(4°04'09"")	871.00'	61.86'
C16	(3°01'06"")	300.00'	15.80'
C17	(2°56'17"")	300.00'	15.38'
C18	(11°08'18"")	300.00'	58.32'
C19	(5°57'15"")	300.00'	31.18'
C20	(4°46'52"")	300.00'	25.03'
C21	(21°20'42"")	300.00'	111.76'
C22	(127°16'46"")	49.00'	108.85'
C23	(111°02'53"")	49.00'	94.97'
C23	(0°13'58"")	738.00'	3.00'

LINE DATA		
LINE	BEARING	LENGTH
L1	(N66°57'18"E	44.27')
L3	(N66°57'18"E	4.35')
L4	(N64°55'31"E	4.00') (RAD)
L5	(N29°26'46"W	6.36')
L6	(N29°26'46"W	7.15')
L7	(N83°21'18"W	7.45') (RAD)
L8	(N07°34'26"W	10.55')
L9	(N64°15'39"E	5.21')
L10	(N82°22'54"E	4.92')
L11	(N81°20'10"E	16.36')
L12	(N81°20'10"E	20.98')
L13	(N29°26'46"W	30.56')
L14	(N18°14'54"W	29.00') (RAD)
L15	(N19°25'17"W	29.00') (RAD)
L16	(N66°57'18"E	12.00')
L17	(N66°57'18"E	32.27')

TRACT NO. 16471
M.M. 801/42-49

LOT B
0.074 AC.

1"=40'

SEE SHEET 6

JOB NO. 99159-022
S:\99159\MAPPING\FINAL MAPS\TR16473\1647305.DWG

SEE SHEET 9

SEE SHEET 4

SEE SHEET 4

SHEET 6 OF 10 SHEETS
62 NUMBERED LOTS
18 LETTERED LOTS
23.224 ACRES
PORTION OF VESTING
T.T.M. 15990
DATE OF SURVEY:
JANUARY, 1999

TRACT MAP NO. 16473

IN THE UNINCORPORATED TERRITORY OF THE COUNTY OF ORANGE,
STATE OF CALIFORNIA




HALL & FOREMAN, INC.

STEVEN C. SHAMBECK, P.L.S. 6217

MAY, 2004

SEE SHEET 2 FOR BASIS OF
BEARINGS, DATUM STATEMENT,
MONUMENT NOTES, EASEMENT
NOTES AND NOTES

LINE	BEARING	LENGTH
L1	(N29°26'46"W	7.15'
L2	(N79°55'41"W	15.69' (PRC)
L3	(N64°55'31"E	4.00' (RAD)
L4	(N66°57'18"E	4.35'
L5	(N66°57'18"E	44.27' (RAD)
L6	(N58°19'34"W	7.20'
L7	(N30°02'11"E	37.81' (RAD)
L8	(N24°45'18"E	16.77'
L9	(N38°47'14"E	5.12'
L10	(N58°19'34"W	48.97'
L11	(N07°34'26"W	10.55'
L12	(N38°42'57"E	13.00'
L13	(N38°42'57"E	13.00'
L14	(N51°17'03"W	36.59'
L15	(N29°26'46"W	6.36'
L16	(N48°08'04"W	14.26'

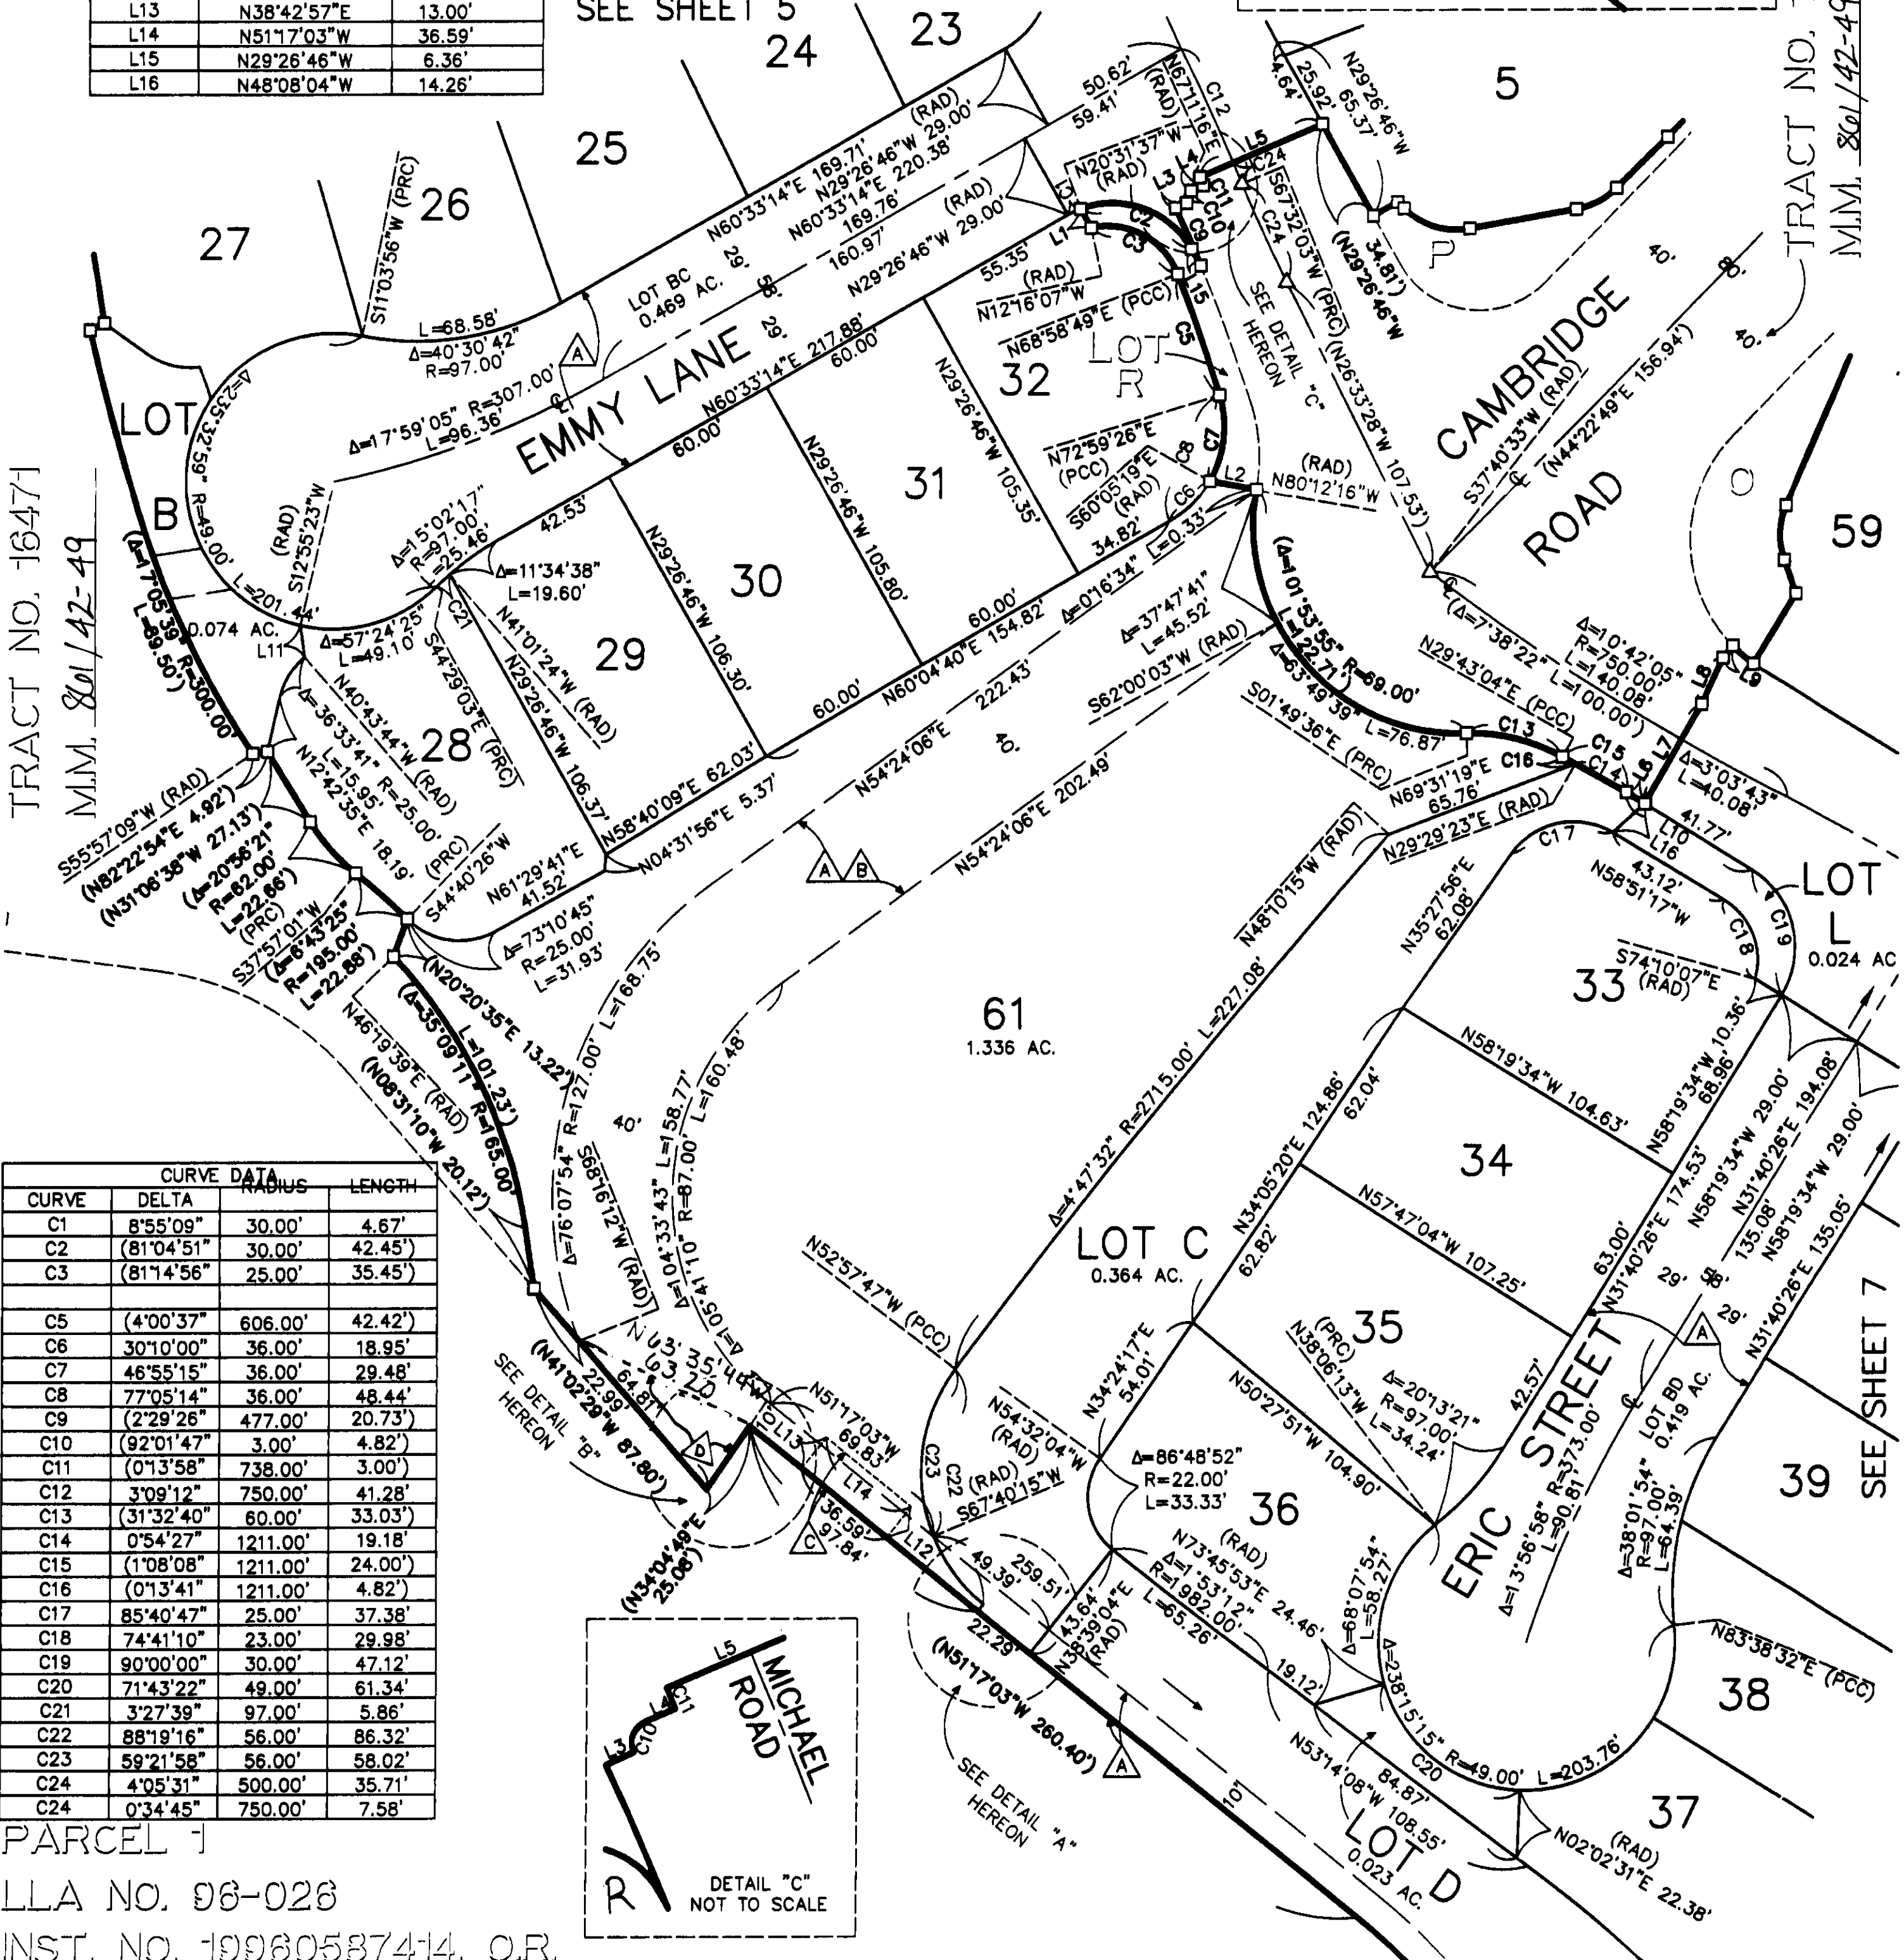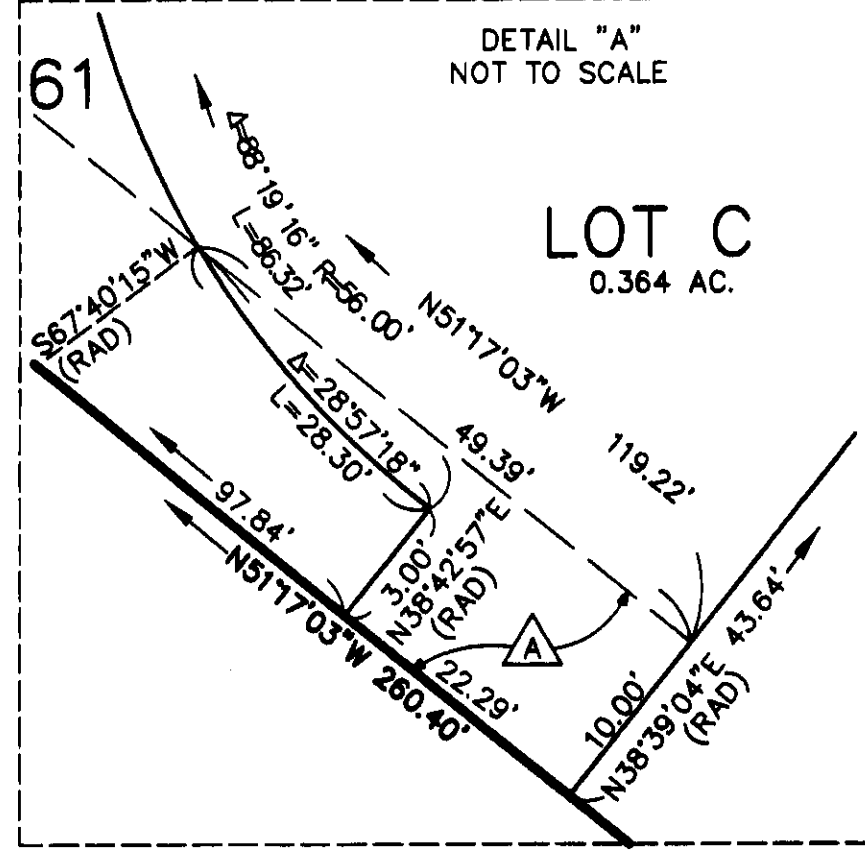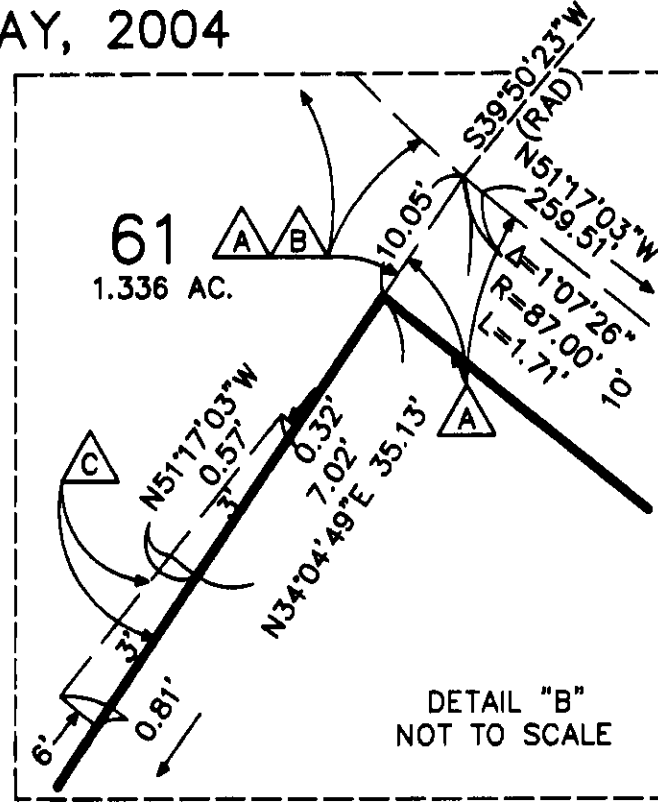

CURVE	DELTA	RADIUS	LENGTH
C1	8°55'09"	30.00'	4.67'
C2	(81°04'51"	30.00'	42.45')
C3	(81°14'56"	25.00'	35.45')
C5	(4°00'37"	606.00'	42.42')
C6	30°10'00"	36.00'	18.95'
C7	46°55'15"	36.00'	29.48'
C8	77°05'14"	36.00'	48.44'
C9	(2°29'26"	477.00'	20.73')
C10	(92°01'47"	3.00'	4.82')
C11	(0°13'58"	738.00'	3.00')
C12	3°09'12"	750.00'	41.28'
C13	(31°32'40"	60.00'	33.03')
C14	0°54'27"	1211.00'	19.18'
C15	(1°08'08"	1211.00'	24.00')
C16	(0°13'41"	1211.00'	4.82')
C17	85°40'47"	25.00'	37.38'
C18	74°41'10"	23.00'	29.98'
C19	90°00'00"	30.00'	47.12'
C20	71°43'22"	49.00'	61.34'
C21	3°27'39"	97.00'	5.86'
C22	88°19'16"	56.00'	86.32'
C23	59°21'58"	56.00'	58.02'
C24	4°05'31"	500.00'	35.71'
C24	0°34'45"	750.00'	7.58'

PARCEL 1

LLA NO. 96-026

INST. NO. 19960587414, O.R.

SEE SHEET 9

862 17

SHEET 7 OF 10 SHEETS
62 NUMBERED LOTS
18 LETTERED LOTS
23.224 ACRES
PORTION OF VESTING
T.T.M. 15990
DATE OF SURVEY:
JANUARY, 1999

TRACT MAP NO. 16473

IN THE UNINCORPORATED TERRITORY OF THE COUNTY OF ORANGE,
STATE OF CALIFORNIA


HALL & FOREMAN, INC.

STEVEN C. SHAMBECK, P.L.S. 6217
MAY, 2004

SEE SHEET 2 FOR BASIS OF
BEARINGS, DATUM STATEMENT,
MONUMENT NOTES, EASEMENT
NOTES AND NOTES

TRACT NO. 16471
M.M. 801/42-49

TRACT NO. 16472
M.M. 802/1-10

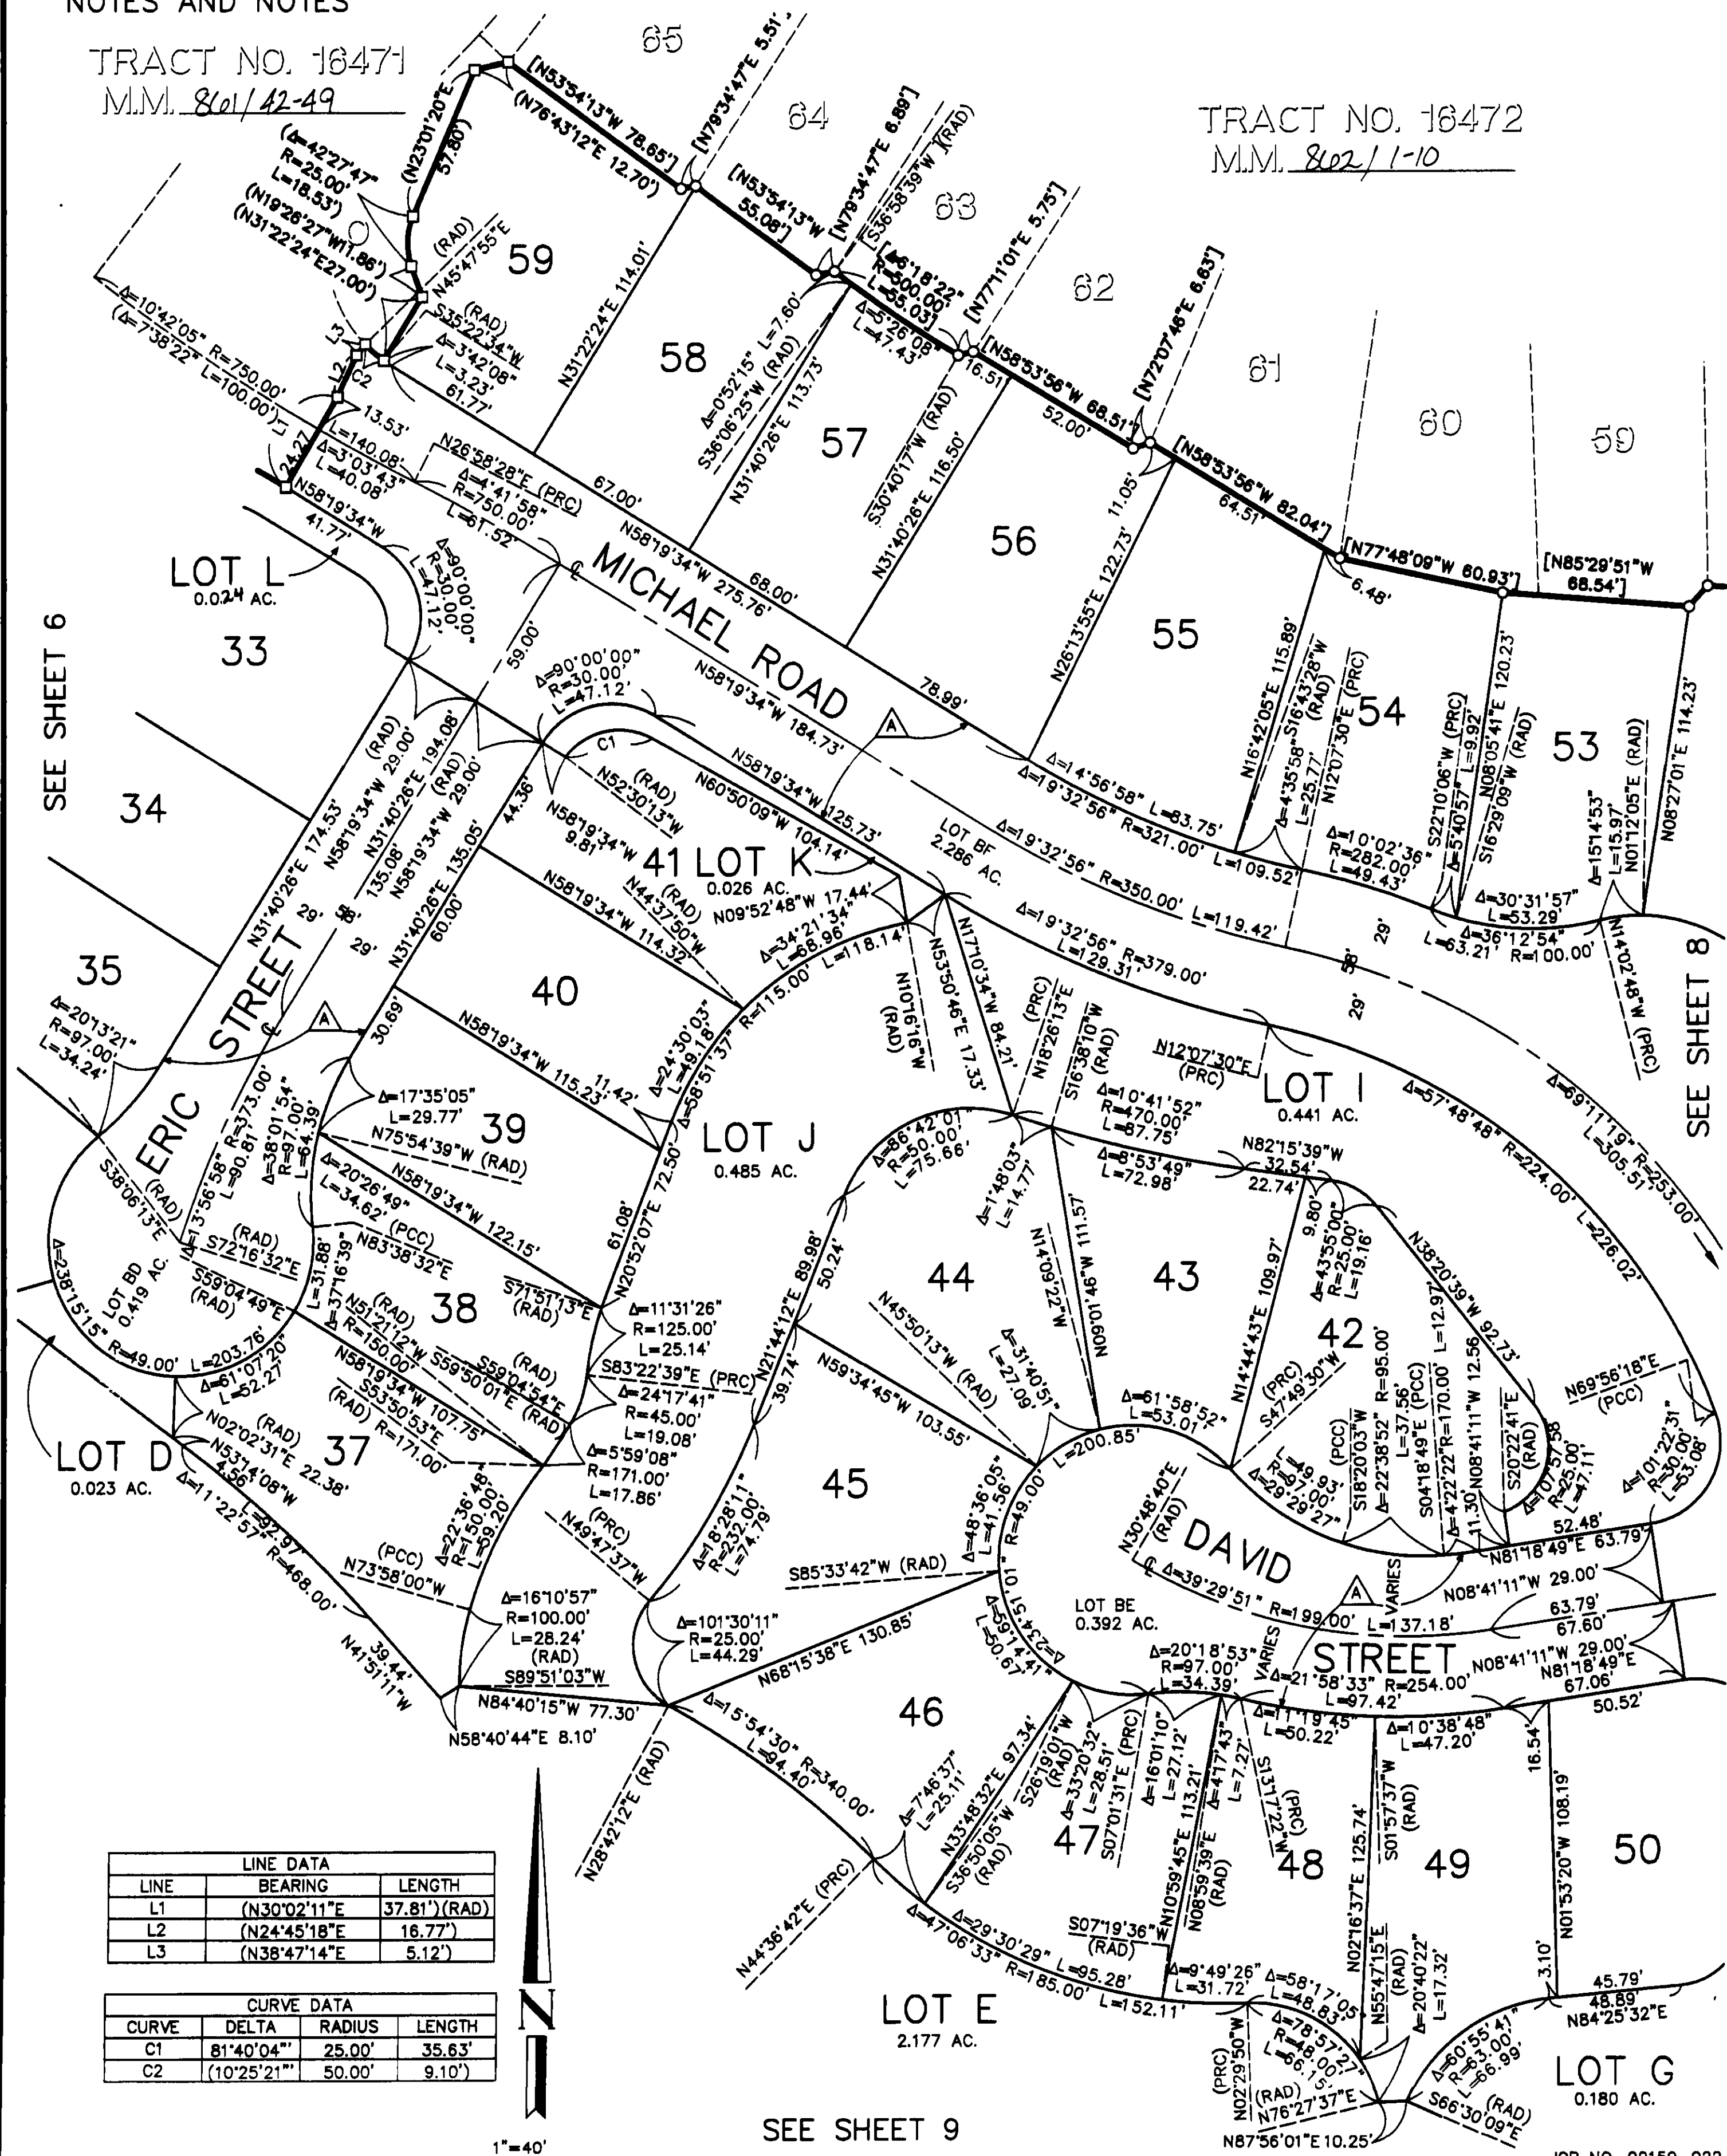

LINE DATA		
LINE	BEARING	LENGTH
L1	(N30°02'11"E	37.81'(RAD)
L2	(N24°45'18"E	16.77')
L3	(N38°47'14"E	5.12')

CURVE DATA			
CURVE	DELTA	RADIUS	LENGTH
C1	81°40'04"	25.00'	35.63'
C2	10°25'21"	50.00'	9.10'

862 17

862 18

SHEET 8 OF 10 SHEETS
62 NUMBERED LOTS
18 LETTERED LOTS
23.224 ACRES
PORTION OF VESTING
T.T.M. 15990
DATE OF SURVEY:
JANUARY, 1999

TRACT MAP NO. 16473


IN THE UNINCORPORATED TERRITORY OF THE COUNTY OF ORANGE,
STATE OF CALIFORNIA

HALL & FOREMAN, INC.

STEVEN C. SHAMBECK, P.L.S. 6217
MAY, 2004

SEE SHEET 2 FOR BASIS OF
BEARINGS, DATUM STATEMENT,
MONUMENT NOTES, EASEMENT
NOTES AND NOTES

TRACT NO. 16472 M.M. 862/1-10

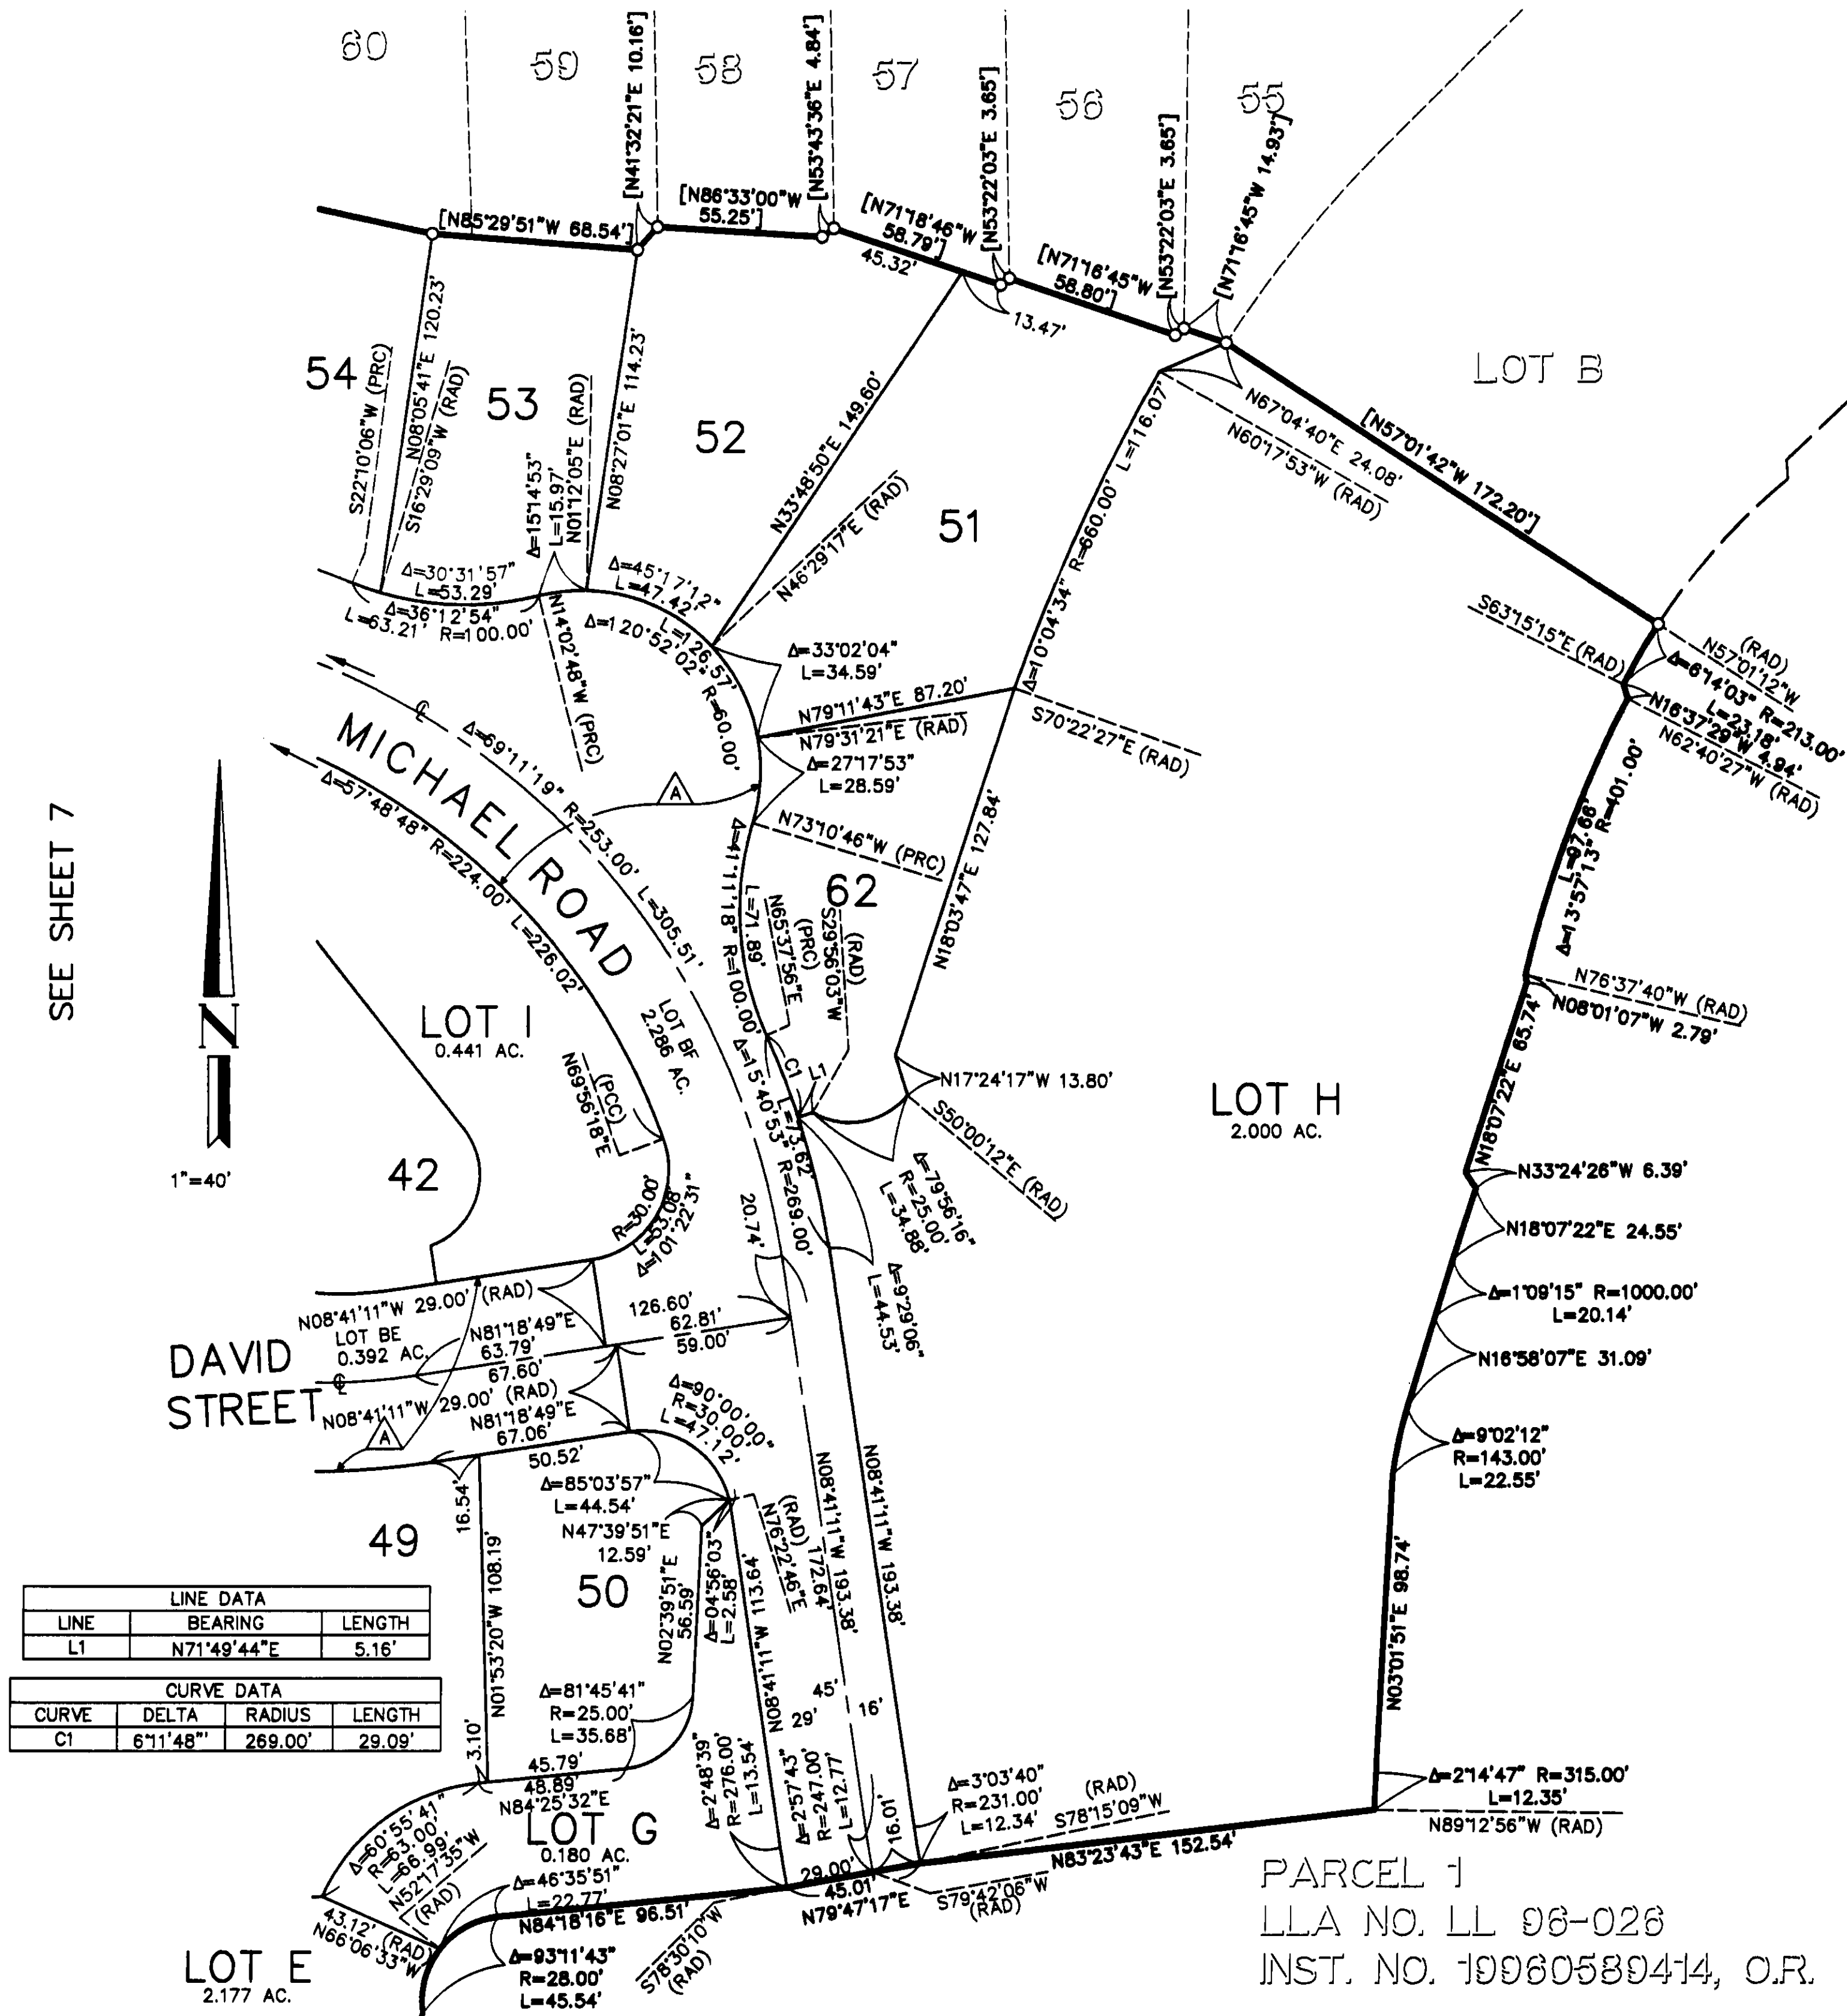

SEE SHEET 9

862 18

862 20

SHEET 10 OF 10 SHEETS
62 NUMBERED LOTS
18 LETTERED LOTS
23.224 ACRES
PORTION OF VESTING
T.T.M. 15990
DATE OF SURVEY:
JANUARY, 1999

TRACT MAP NO. 16473

IN THE UNINCORPORATED TERRITORY OF THE COUNTY OF ORANGE,
STATE OF CALIFORNIA

HALL & FOREMAN, INC. STEVEN C. SHAMBECK, P.L.S. 6217
MAY, 2004

SEE SHEET 2 FOR BASIS OF
BEARINGS, DATUM STATEMENT,
MONUMENT NOTES, EASEMENT
NOTES AND NOTES

DATA FROM SHEET NO. 3

CURVE DATA			
CURVE	DELTA	RADIUS	LENGTH
C1	93°11'43"	28.00'	45.54'
C2	2°14'47"	315.00'	12.35'
C3	9°02'12"	143.00'	22.55'
C4	1°09'15"	1000.00'	20.14'
C5	13°57'13"	401.00'	97.66'
C6	6°14'03"	213.00'	23.18'
C7	6°18'22"	500.00'	55.03'
C8	42°27'47"	25.00'	18.53'
C9	10°25'21"	50.00'	9.10'
C10	1°08'08"	1211.00'	24.00'
C11	31°32'40"	60.00'	33.03'
C12	101°53'54"	69.00'	122.71'
C13	46°55'15"	36.00'	29.48'
C14	54°32'46"	25.00'	23.80'
C15	34°35'55"	25.00'	15.10'
C16	4°47'24"	206.00'	17.22'
C17	64°56'25"	25.00'	28.34'
C18	66°11'45"	25.00'	28.88'
C19	18°02'26"	141.00'	44.40'
C20	62°28'05"	30.00'	32.71'
C21	141°29'58"	70.00'	172.87'
C22	61°15'38"	30.00'	32.08'
C23	14°34'36"	540.00'	137.38'
C24	50°33'28"	17.00'	15.00'
C25	15°09'35"	212.00'	56.09'
C26	4°21'43"	619.00'	47.11'
C27	10°10'28"	217.00'	38.54'
C28	6°19'26"	536.00'	59.16'
C29	23°32'05"	142.00'	58.33'
C30	37°39'35"	62.00'	40.75'
C31	20°17'05"	40.00'	14.16'
C33	6°44'47"	510.00'	60.05'
C34	36°13'22"	105.00'	66.38'
C35	58°27'03"	50.00'	51.01'
C36	2°22'43"	300.00'	12.45'
C37	50°47'24"	25.00'	22.16'
C38	174°46'01"	49.00'	149.46'
C39	65°43'06"	25.00'	28.68'
C40	34°53'28"	49.00'	29.84'
C41	8°24'59"	53.00'	7.79'
C42	8°22'09"	271.00'	39.58'
C43	8°03'54"	344.00'	48.42'
C44	3°20'02"	108.00'	6.28'
C45	9°47'40"	30.00'	5.13'
C46	23°43'58"	260.00'	107.69'
C47	3°10'13"	779.00'	43.10'
C48	23°42'08"	196.00'	81.08'
C49	8°34'29"	551.00'	82.46'
C50	4°04'09"	871.00'	61.86'
C51	17°05'39"	300.00'	89.50'
C52	20°56'21"	62.00'	22.66'
C53	6°43'25"	195.00'	22.88'
C54	35°09'11"	165.00'	101.23'

LINE DATA		
LINE	BEARING	LENGTH
L1	N84°18'16"E	96.51'
L2	N79°47'17"E	45.01'
L3	N03°01'51"E	98.74'
L4	N16°58'07"E	31.09'
L5	N18°07'22"E	24.55'
L6	N33°24'26"W	6.39'
L7	N18°07'22"E	65.74'
L8	N08°01'07"W	2.79'
L9	N16°37'29"W	4.94'
L10	N71°16'45"W	14.93'
L11	N53°22'03"E	3.65'
L12	N71°16'45"W	58.80'
L13	N53°22'03"E	3.65'
L14	N71°18'46"W	58.79'
L15	N53°43'36"E	4.84'
L16	N86°33'00"W	55.25'
L17	N41°32'21"E	10.16'
L18	N85°29'51"W	68.54'
L19	N77°48'09"W	60.93'
L20	N58°53'56"W	82.04'
L21	N72°07'46"E	6.63'
L22	N58°53'56"W	68.51'
L23	N77°11'01"E	5.75'
L24	N79°34'47"E	6.89'
L25	N53°54'13"W	55.08'
L26	N79°34'47"E	5.51'
L27	N53°54'13"W	78.65'
L28	N76°43'12"E	12.70'
L29	N23°01'20"E	57.80'
L30	N19°26'27"W	11.86'
L31	N31°22'24"E	27.00'
L32	N38°47'14"E	5.12'
L33	N24°45'18"E	16.77'
L34	N30°02'11"E	37.81'
L35	N58°19'34"W	7.20'
L36	N79°55'41"W	15.69'
L38	N66°57'18"E	44.27'
L39	N29°26'46"W	34.81'
L40	N60°33'14"E	9.26'
L41	N45°35'47"W	2.93'
L42	N79°51'27"E	35.56'
L43	N45°15'32"E	23.85'
L44	N24°28'17"W	38.46'
L45	N02°54'21"E	35.17'
L46	N30°58'26"E	29.40'
L47	N83°30'28"W	11.71'
L48	N06°28'32"E	15.17'
L49	N51°09'37"W	2.00' (RAD)
L50	N89°30'12"E	5.57'
L51	N53°32'37"W	25.32'
L52	N66°25'39"E	14.22' (RAD)
L53	N71°39'38"E	9.96' (RAD)
L54	N32°38'23"E	80.83'
L55	N62°34'42"E	8.13'
L56	N83°21'18"W	7.45'
L57	N68°37'17"W	4.83'
L58	N15°40'25"W	36.85'
L59	N21°50'43"E	9.36'
L60	N64°15'39"E	5.21'
L61	N82°22'54"E	4.92'
L62	N31°06'38"W	27.13'
L63	N20°20'35"E	13.22'
L64	N08°31'10"W	20.12'
L65	N41°02'29"W	87.80'
L66	N34°04'49"E	25.08'

862 20