

(ALL OF VESTING TENTATIVE
TRACT NO. 16505)TOTAL ACRES: 9.293 AC.
NUMBERED LOTS: 34
LETTERED LOTS: 4
DATE OF SURVEY: MAY 2003.

TRACT NO. 16505

IN THE UNINCORPORATED TERRITORY OF ORANGE COUNTY, STATE OF CALIFORNIA

BEING LOT 3 OF TRACT NO. 15987 IN THE UNINCORPORATED TERRITORY OF THE
COUNTY OF ORANGE, STATE OF CALIFORNIA, AS SHOWN ON A MAP FILED IN BOOK
839, PAGES 1-18 INCLUSIVE OF MISCELLANEOUS MAPS, RECORDS IN THE OFFICE
OF THE COUNTY RECORDER OF ORANGE COUNTY, CALIFORNIA.DOUGLAS BENDER AND ASSOCIATES DOUGLAS W. BENDER R.C.E. 28946
MAY 2003ACCEPTED AND FILED AT THE
REQUEST OF

FIRST AMERICAN TITLE INSURANCE COMPANY

DATE April 30, 2004

TIME 09:57am FEE \$ 19.00

INSTRUMENT #2004000374 102

BOOK 8510 PAGE 42-46

TOM DALY m/m
COUNTY CLERK-RECORDERBY Julia Granules
DEPUTYOWNERSHIP CERTIFICATE:WE, THE UNDERSIGNED, BEING ALL PARTIES HAVING ANY RECORD TITLE
INTEREST IN THE LAND COVERED BY THIS MAP, DO HEREBY CONSENT TO
THE PREPARATION AND RECORDATION OF SAID MAP, AS SHOWN WITHIN
THE DISTINCTIVE BORDER LINE.

WE ALSO HEREBY DEDICATE TO THE COUNTY OF ORANGE:

1. AN EASEMENT FOR PEDESTRIAN AND EMERGENCY AND PUBLIC SERVICE VEHICULAR
INGRESS AND EGRESS PURPOSES AS SHOWN ON MAP.WE ALSO HEREBY DEDICATE TO SANTA MARGARITA WATER DISTRICT, THE EASEMENTS FOR WATER AND
SEWER PIPELINES, AND ACCESS PURPOSES OVER THOSE EASEMENT AREAS AS SHOWN ON THIS MAP
SAID EASEMENTS SHALL BE SUBJECT TO THE SAME TERMS AND CONDITIONS AS ARE SHOWN IN THAT
CERTAIN GRANT OF EASEMENT TO SANTA MARGARITA WATER DISTRICT RECORDED SEPTEMBER 18, 2002,
AS INSTRUMENT NO. 20020799401 OF OFFICIAL RECORDS, COUNTY OF ORANGE.WARMINGTON MERIDEN ASSOCIATES, L.P.

A CALIFORNIA LIMITED PARTNERSHIP

BY: Brian L. Sinderhoff BY: Michael Riddlesperger
PRINT NAME: Brian L. Sinderhoff PRINT NAME: Michael Riddlesperger
PRINT TITLE: Pres. So. Calif. Division PRINT TITLE: VP CFODMB LADERA, L.L.C.

A DELAWARE LIMITED LIABILITY COMPANY

BENEFICIARY UNDER DEED OF TRUST RECORDED AS INSTRUMENT NO. 2003001130546
OF OFFICIAL RECORDS.BY: Rancho Mission Viejo, L.L.C., A DELAWARE LIMITED LIABILITY COMPANY,
ITS AUTHORIZED AGENT AND MANAGERBY: Gregory S. Edwards BY: Gregory S. Edwards
PRINT NAME: Gregory S. Edwards PRINT NAME: Gregory S. Edwards
PRINT TITLE: V.P. PRINT TITLE: Sr. V.P./CFOCALIFORNIA BANK & TRUST

A CALIFORNIA BANKING CORPORATION

BENEFICIARY UNDER DEED OF TRUST RECORDED AS INSTRUMENT NO. 2003001130545
OF OFFICIAL RECORDS.BY: Enn Johnson BY: Angela Herring
PRINT NAME: Enn Johnson PRINT NAME: Angela Herring
PRINT TITLE: Vice President PRINT TITLE: Vice PresidentCERTIFICATE OF ACCEPTANCE - SANTA MARGARITA WATER DISTRICTTHE UNDERSIGNED, BEING THE DULY APPOINTED AGENT OF THE SANTA MARGARITA WATER DISTRICT, A
PUBLIC CORPORATION OF ORANGE COUNTY, CALIFORNIA, PURSUANT TO ITS RESOLUTION NO. 88-10-2 DOES
HEREBY ACCEPT ON BEHALF OF SAID DISTRICT, THE PIPELINE EASEMENTS FOR WATER, SEWER & ACCESS
PURPOSES, AS DEDICATED AND SHOWN ON THIS TRACT MAP, AS DEDICATED, BY AND BETWEEN
THE SANTA MARGARITA WATER DISTRICT AND WARMINGTON HOMES, AND DOES HEREBY CERTIFY THAT
THE QUALITY CONSENTS TO THE RECORDATION OF SAID TRACT.BY: Daniel R. Ferons
DANIEL R. FERONS, CHIEF ENGINEER
SANTA MARGARITA WATER DISTRICTWARMINGTON MERIDEN ASSOCIATES, L.P.STATE OF CALIFORNIA) SS
COUNTY OF ORANGE)ON THIS November 5, 2003, BEFORE ME, Denise Miller,


A NOTARY PUBLIC IN AND FOR SAID STATE, PERSONALLY APPEARED

PERSONALLY KNOWN TO ME (OR PROVED TO ME ON THE BASIS OF SATISFACTORY EVIDENCE)
TO BE THE PERSON (S) WHOSE NAME (S) IS/ARE SUBSCRIBED TO THE WITHIN INSTRUMENT
AND ACKNOWLEDGED TO ME THAT HE/SHE/they EXECUTED THE SAME IN HIS/HER/their
AUTHORIZED CAPACITY (IES), AND THAT BY HIS/HER/their SIGNATURE (S) ON THE
INSTRUMENT THE PERSON (S), OR THE ENTITY UPON BEHALF OF WHICH THE PERSON (S)
ACTED, EXECUTED THE INSTRUMENT.

WITNESS MY HAND:

SIGNATURE Denise Miller
NOTARY PUBLIC IN AND FOR SAID STATEMY PRINCIPAL PLACE OF BUSINESS IS
IN Orange COUNTY.Denise Miller
(NAME PRINTED)MY COMMISSION EXPIRES 6/20/07SIGNATURE OMISSIONPURSUANT TO SECTION 66436 (a) (3) (A) (C) OF THE SUBDIVISION MAP ACT, THE
FOLLOWING SIGNATURES HAVE BEEN OMITTED:

1. LADERA DEVELOPMENT COMPANY, L.L.C., HOLDER OF OIL, GAS AND MINERAL RIGHTS
RECORDED AS INSTRUMENT NO. 19980624029 OF OFFICIAL RECORDS.
2. DMB LADERA, LLC, HOLDER OF AN EASEMENT RESERVED IN THE DEED RECORDED
AS INSTRUMENT NO. 2003001130544 OF OFFICIAL RECORDS.

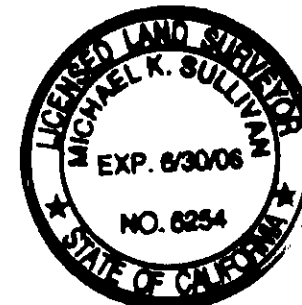ENGINEER'S STATEMENT:THIS MAP WAS PREPARED BY ME OR UNDER MY DIRECTION AND IS BASED UPON A FIELD
SURVEY IN CONFORMANCE WITH THE REQUIREMENTS OF THE SUBDIVISION MAP ACT AND LOCAL
ORDINANCE AT THE REQUEST OF WARMINGTON HOMES ON MAY 2003. I HEREBY STATE THAT ALL
MONUMENTS ARE OF THE CHARACTER AND OCCUPY THE POSITIONS INDICATED OR THAT THEY
WILL BE SET IN SUCH POSITIONS; AND THAT SAID MONUMENTS ARE SUFFICIENT TO ENABLE THE
SURVEY TO BE RETRACED. I HEREBY STATE THAT THIS FINAL MAP SUBSTANTIALLY CONFORMS TO
THE CONDITIONALLY APPROVED TENTATIVE MAP.DOUGLAS W. BENDER, R.C.E. 28946
MY REGISTRATION EXPIRES MARCH 31, 2007.COUNTY SURVEYOR'S STATEMENT:I HEREBY STATE THAT I HAVE EXAMINED THIS MAP AND HAVE FOUND IT TO BE
SUBSTANTIALLY IN CONFORMANCE WITH THE TENTATIVE MAP AS FILED WITH, AMENDED
AND APPROVED BY THE ORANGE COUNTY SUBDIVISION COMMITTEE; THAT ALL
PROVISIONS OF THE SUBDIVISION MAP ACT AND COUNTY SUBDIVISION REGULATIONS
HAVE BEEN COMPLIED WITH AND I AM SATISFIED SAID MAP IS TECHNICALLY CORRECT.DATED THIS 5TH DAY OF APRIL, 2004Michael K. Sullivan
COUNTY SURVEYORBY: MICHAEL K. SULLIVAN, DEPUTY
LS 2254 EXPIRES 8/30/08CLERK OF THE BOARD OF SUPERVISOR'S CERTIFICATE:STATE OF CALIFORNIA)
COUNTY OF ORANGE)I HEREBY CERTIFY THAT THIS MAP WAS PRESENTED FOR APPROVAL TO THE BOARD OF
SUPERVISORS OF ORANGE COUNTY AT A REGULAR MEETING THEREOF HELD ON THE 27th
DAY OF April, 2004, AND THAT THEREUPON SAID BOARD DID, BY AN ORDER
DULY PASSED AND ENTERED, AND DID ALSO APPROVE SAID MAP PURSUANT TO THE
PROVISIONS OF SECTION 66436 (a) (3) (A) OF THE SUBDIVISION ACT.

WE DID ALSO ACCEPT ON BEHALF OF THE COUNTY OF ORANGE:

1. AN EASEMENT FOR PEDESTRIAN AND EMERGENCY AND PUBLIC SERVICE VEHICULAR
INGRESS AND EGRESS PURPOSES AS SHOWN ON MAP.DATED THIS 27th DAY OF April, 2004Darlene J. Bloom
DARLENE J. BLOOM
CLERK OF THE BOARD OF SUPERVISORSCOUNTY TREASURER-TAX COLLECTOR'S CERTIFICATE:STATE OF CALIFORNIA)
COUNTY OF ORANGE)I HEREBY CERTIFY THAT ACCORDING TO THE RECORDS OF MY OFFICE THERE ARE NO
LIENS AGAINST THE LAND COVERED BY THIS MAP OR ANY PART THEREOF FOR UNPAID
STATE, COUNTY, MUNICIPAL OR LOCAL TAXES OR SPECIAL ASSESSMENTS COLLECTED
AS TAXES, EXCEPT TAXES OR SPECIAL ASSESSMENTS COLLECTED AS TAXES NOT YET
PAYABLE.AND DO ALSO CERTIFY TO THE RECORDER OF ORANGE COUNTY THAT THE PROVISIONS OF
THE SUBDIVISION MAP ACT HAVE BEEN COMPLIED WITH REGARDING DEPOSITS TO
SECURE THE PAYMENT OF TAXES OR SPECIAL ASSESSMENTS COLLECTED AS TAXES ON
THE LAND COVERED BY THIS MAP.DATED THIS 9th DAY OF March, 2004JOHN M.W. MOORLACH
COUNTY TREASURER-TAX COLLECTORBY: John Moorlach
DEPUTY TREASURER-TAX COLLECTOR"THE PRIVATE STREETS CONSTRUCTED WITHIN THIS MAP SHALL BE OWNED, OPERATED
AND MAINTAINED BY THE DEVELOPER, SUCCESSORS OR ASSIGNS. THE COUNTY OF
ORANGE SHALL HAVE NO RESPONSIBILITY THEREFOR UNLESS PURSUANT TO APPROPRIATE
SECTIONS OF THE STREETS AND HIGHWAYS CODE OF THE STATE OF CALIFORNIA, THE SAID
PRIVATE STREETS HAVE BEEN ACCEPTED INTO THE COUNTY ROAD SYSTEM BY APPROPRIATE
RESOLUTION OF THE ORANGE COUNTY BOARD OF SUPERVISORS."AUTOMATIC FIRE SPRINKLER NOTE:ALL COMMERCIAL STRUCTURES OVER 6,000 SQUARE FEET; ALL MULTIFAMILY
RESIDENTIAL STRUCTURES; ALL DETACHED, SINGLE-FAMILY STRUCTURES EXCEEDING
5,500 SQUARE FEET, AND ALL STRUCTURES EXCEEDING FIRE AUTHORITY ACCESS
REQUIREMENTS SHALL BE PROTECTED BY AN AUTOMATIC SPRINKLER SYSTEM, IN A
MANNER MEETING THE APPROVAL OF THE FIRE CHIEF.SPECIAL FIRE PROTECTION NOTE:PROPERTY IS GIVEN TOTAL EXCLUSION FROM A SPECIAL FIRE PROTECTION AREA AND MUST MEET
ALL REQUIREMENTS OF THE EXCLUSION FOR DEVELOPMENT WITHIN THE AREA.HIGH FIRE HAZARD AREA NOTE:THE LOTS SHOWN ON THIS MAP ARE IN A HIGH FIRE HAZARD AREA DUE TO
WILDLAND EXPOSURE.NOTES:PROPERTY MAY BE SUBJECT TO IMPACTS FROM THE FOOTHILL/EASTERN
TRANSPORTATION CORRIDOR.

8510 42

SHEET 2 OF 5 SHEETS

(ALL OF VESTING TENTATIVE
TRACT NO. 16505)

TOTAL ACRES: 9.293 AC.
NUMBERED LOTS: 34
LETTERED LOTS: 4
DATE OF SURVEY: MAY 2003.

TRACT NO. 16505

IN THE UNINCORPORATED TERRITORY OF ORANGE COUNTY, STATE OF CALIFORNIA
DOUGLAS BENDER AND ASSOCIATES DOUGLAS W. BENDER R.C.E. 28946
MAY 2003

CALIFORNIA BANK & TRUST

STATE OF CALIFORNIA)
COUNTY OF ORANGE) SS

ON THIS November 5th 2003, BEFORE ME, Elaine Marie Pelletier
A NOTARY PUBLIC IN AND FOR SAID STATE, PERSONALLY APPEARED

~~PERSONALLY KNOWN TO ME (OR PROVED TO ME ON THE BASIS OF SATISFACTORY EVIDENCE)~~
TO BE THE PERSON ~~(S)~~ WHOSE NAME ~~(S)~~ ARE SUBSCRIBED TO THE WITHIN INSTRUMENT
AND ACKNOWLEDGED TO ME THAT HE ~~(S)~~ SHE ~~(S)~~ THEY EXECUTED THE SAME IN HIS ~~(S)~~ HER ~~(S)~~ THEIR
AUTHORIZED CAPACITY ~~(S)~~, AND THAT BY HIS ~~(S)~~ HER ~~(S)~~ THEIR SIGNATURE ~~(S)~~ ON THE
INSTRUMENT THE PERSON ~~(S)~~, OR THE ENTITY UPON BEHALF OF WHICH THE PERSON ~~(S)~~
ACTED, EXECUTED THE INSTRUMENT.

WITNESS MY HAND:

SIGNATURE Elaine Marie Pelletier MY PRINCIPAL PLACE OF BUSINESS IS
NOTARY PUBLIC IN AND FOR SAID STATE IN Orange COUNTY.

Elaine Marie Pelletier MY COMMISSION EXPIRES 7/20/04
(NAME PRINTED)

SANTA MARGARITA WATER DISTRICT

STATE OF CALIFORNIA)
COUNTY OF ORANGE) SS

ON THIS JAN 8, 2004, BEFORE ME, CINDY R. LANE,
A NOTARY PUBLIC IN AND FOR SAID STATE, PERSONALLY APPEARED DANIEL R. FERONS

~~PERSONALLY KNOWN TO ME (OR PROVED TO ME ON THE BASIS OF SATISFACTORY EVIDENCE)~~
TO BE THE PERSON ~~(S)~~ WHOSE NAME ~~(S)~~ ARE SUBSCRIBED TO THE WITHIN INSTRUMENT
AND ACKNOWLEDGED TO ME THAT HE ~~(S)~~ SHE ~~(S)~~ THEY EXECUTED THE SAME IN HIS ~~(S)~~ HER ~~(S)~~ THEIR
AUTHORIZED CAPACITY ~~(S)~~, AND THAT BY HIS ~~(S)~~ HER ~~(S)~~ THEIR SIGNATURE ~~(S)~~ ON THE
INSTRUMENT THE PERSON ~~(S)~~, OR THE ENTITY UPON BEHALF OF WHICH THE PERSON ~~(S)~~
ACTED, EXECUTED THE INSTRUMENT.

WITNESS MY HAND:

SIGNATURE Cindy R. Lane MY PRINCIPAL PLACE OF BUSINESS IS
NOTARY PUBLIC IN AND FOR SAID STATE IN ORANGE COUNTY.

Cindy R. LANE MY COMMISSION EXPIRES 2-20-2005
(NAME PRINTED)

DMB LADERA, LLC

STATE OF CALIFORNIA)
COUNTY OF ORANGE) SS

ON THIS December 18, 2003, BEFORE ME, Diana L. BINKS,
A NOTARY PUBLIC IN AND FOR SAID STATE, PERSONALLY APPEARED Donald F. Stanton and Gregory S. Edwards

~~PERSONALLY KNOWN TO ME (OR PROVED TO ME ON THE BASIS OF SATISFACTORY EVIDENCE)~~
TO BE THE PERSON ~~(S)~~ WHOSE NAME ~~(S)~~ ARE SUBSCRIBED TO THE WITHIN INSTRUMENT
AND ACKNOWLEDGED TO ME THAT HE ~~(S)~~ SHE ~~(S)~~ THEY EXECUTED THE SAME IN HIS ~~(S)~~ HER ~~(S)~~ THEIR
AUTHORIZED CAPACITY ~~(S)~~, AND THAT BY HIS ~~(S)~~ HER ~~(S)~~ THEIR SIGNATURE ~~(S)~~ ON THE
INSTRUMENT THE PERSON ~~(S)~~, OR THE ENTITY UPON BEHALF OF WHICH THE PERSON ~~(S)~~
ACTED, EXECUTED THE INSTRUMENT.

WITNESS MY HAND:

SIGNATURE Diana L. BINKS MY PRINCIPAL PLACE OF BUSINESS IS
NOTARY PUBLIC IN AND FOR SAID STATE IN Orange COUNTY.

Diana L. BINKS MY COMMISSION EXPIRES 12/12/06
(NAME PRINTED)

SHEET 3 OF 5 SHEETS

(PORTION OF VESTING TENTATIVE TRACT NO. 16505)

TOTAL ACREAGE: 9.293 AC.
NUMBERED LOTS: 34
LETTERED LOTS: 4
DATE OF SURVEY: MAY 2003

TRACT NO. 16505

IN THE UNINCORPORATED TERRITORY OF ORANGE COUNTY, STATE OF CALIFORNIA
DOUGLAS BENDER AND ASSOCIATES DOUGLAS W. BENDER R.C.E. 28946
MAY 2003

GPS NO. 1448

MONUMENT NOTES

2" IRON PIPE TAGGED "R.C.E. 28946" OR SPIKE AND WASHER STAMPED "R.C.E. 28946" OR LEAD AND TACK TAGGED "R.C.E. 28946" TO BE SET AT ALL TRACT CORNERS UNLESS OTHERWISE NOTED, WITHIN 90 DAYS AFTER ACCEPTANCE OF IMPROVEMENTS.

8" SPIKE & WASHER STAMPED "R.C.E. 28946" IN ASPHALT PAVING OR LEAD & TAG "R.C.E. 28946" IN CONCRETE TO BE SET AT ALL CENTERLINE INTERSECTIONS, B.C.'S, E.C.'S AND ALL OTHER CENTERLINE POINTS OF CONTROL, UNLESS OTHERWISE NOTED, WITHIN 90 DAYS AFTER ACCEPTANCE OF IMPROVEMENTS.

1" IRON PIPE TAGGED "R.C.E. 28946" OR SPIKE AND WASHER STAMPED "R.C.E. 28946" OR LEAD AND TACK TAGGED "R.C.E. 28946" TO BE SET AT ALL LOT CORNERS, EXCEPT B.C.'S, E.C.'S, P.R.C.'S AND P.C.C.'S THAT ABUT A STREET AND ARE NOT LOT CORNERS MARKING SIDE LOT LINES, UNLESS OTHERWISE NOTED, WITHIN 90 DAYS AFTER ACCEPTANCE OF IMPROVEMENTS.

MONUMENT NOTES (CONT.)

⊙ INDICATES FOUND O.C.S. G.P.S. MONUMENTS AS NOTED.


□ INDICATES LOCATION OF 2" I.P. TAGGED "P.L.S. 5557" OR SPIKE & WASHER STAMPED "P.L.S. 5557" OR LEAD, TACK & TAG "P.L.S. 5557" TO BE SET PER TRACT 15987, M.M. 839/1-18.

△ INDICATES LOCATION OF 1" I.P. TAGGED "P.L.S. 5557" OR SPIKE & WASHER STAMPED "P.L.S. 5557" OR LEAD, TACK & TAG "P.L.S. 5557" TO BE SET PER TRACT NO. 16025 M.M. 812/40-48, UNLESS OTHERWISE NOTED.


○ INDICATES LOCATION OF 1" I.P. TAGGED "P.L.S. 5557" OR SPIKE & WASHER STAMPED "P.L.S. 5557" OR LEAD, TACK & TAG "P.L.S. 5557" TO BE SET PER TRACT 15987, M.M. 839/1-18.

● INDICATES 2" I.P. R.C.E. 28946 TO BE SET PRIOR TO RECORDATION.

FD. 2" IRON PIPE W/1-3/4" OCS BRASS CAP STAMPED "GPS 1448 9-95" PER TRACT NO. 16203, M.M. 826/8-20 AND RECORDS ON FILE IN THE ORANGE COUNTY SURVEYORS OFFICE

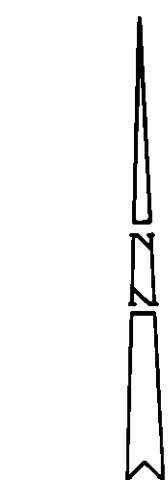

SCALE: 1" = 100'

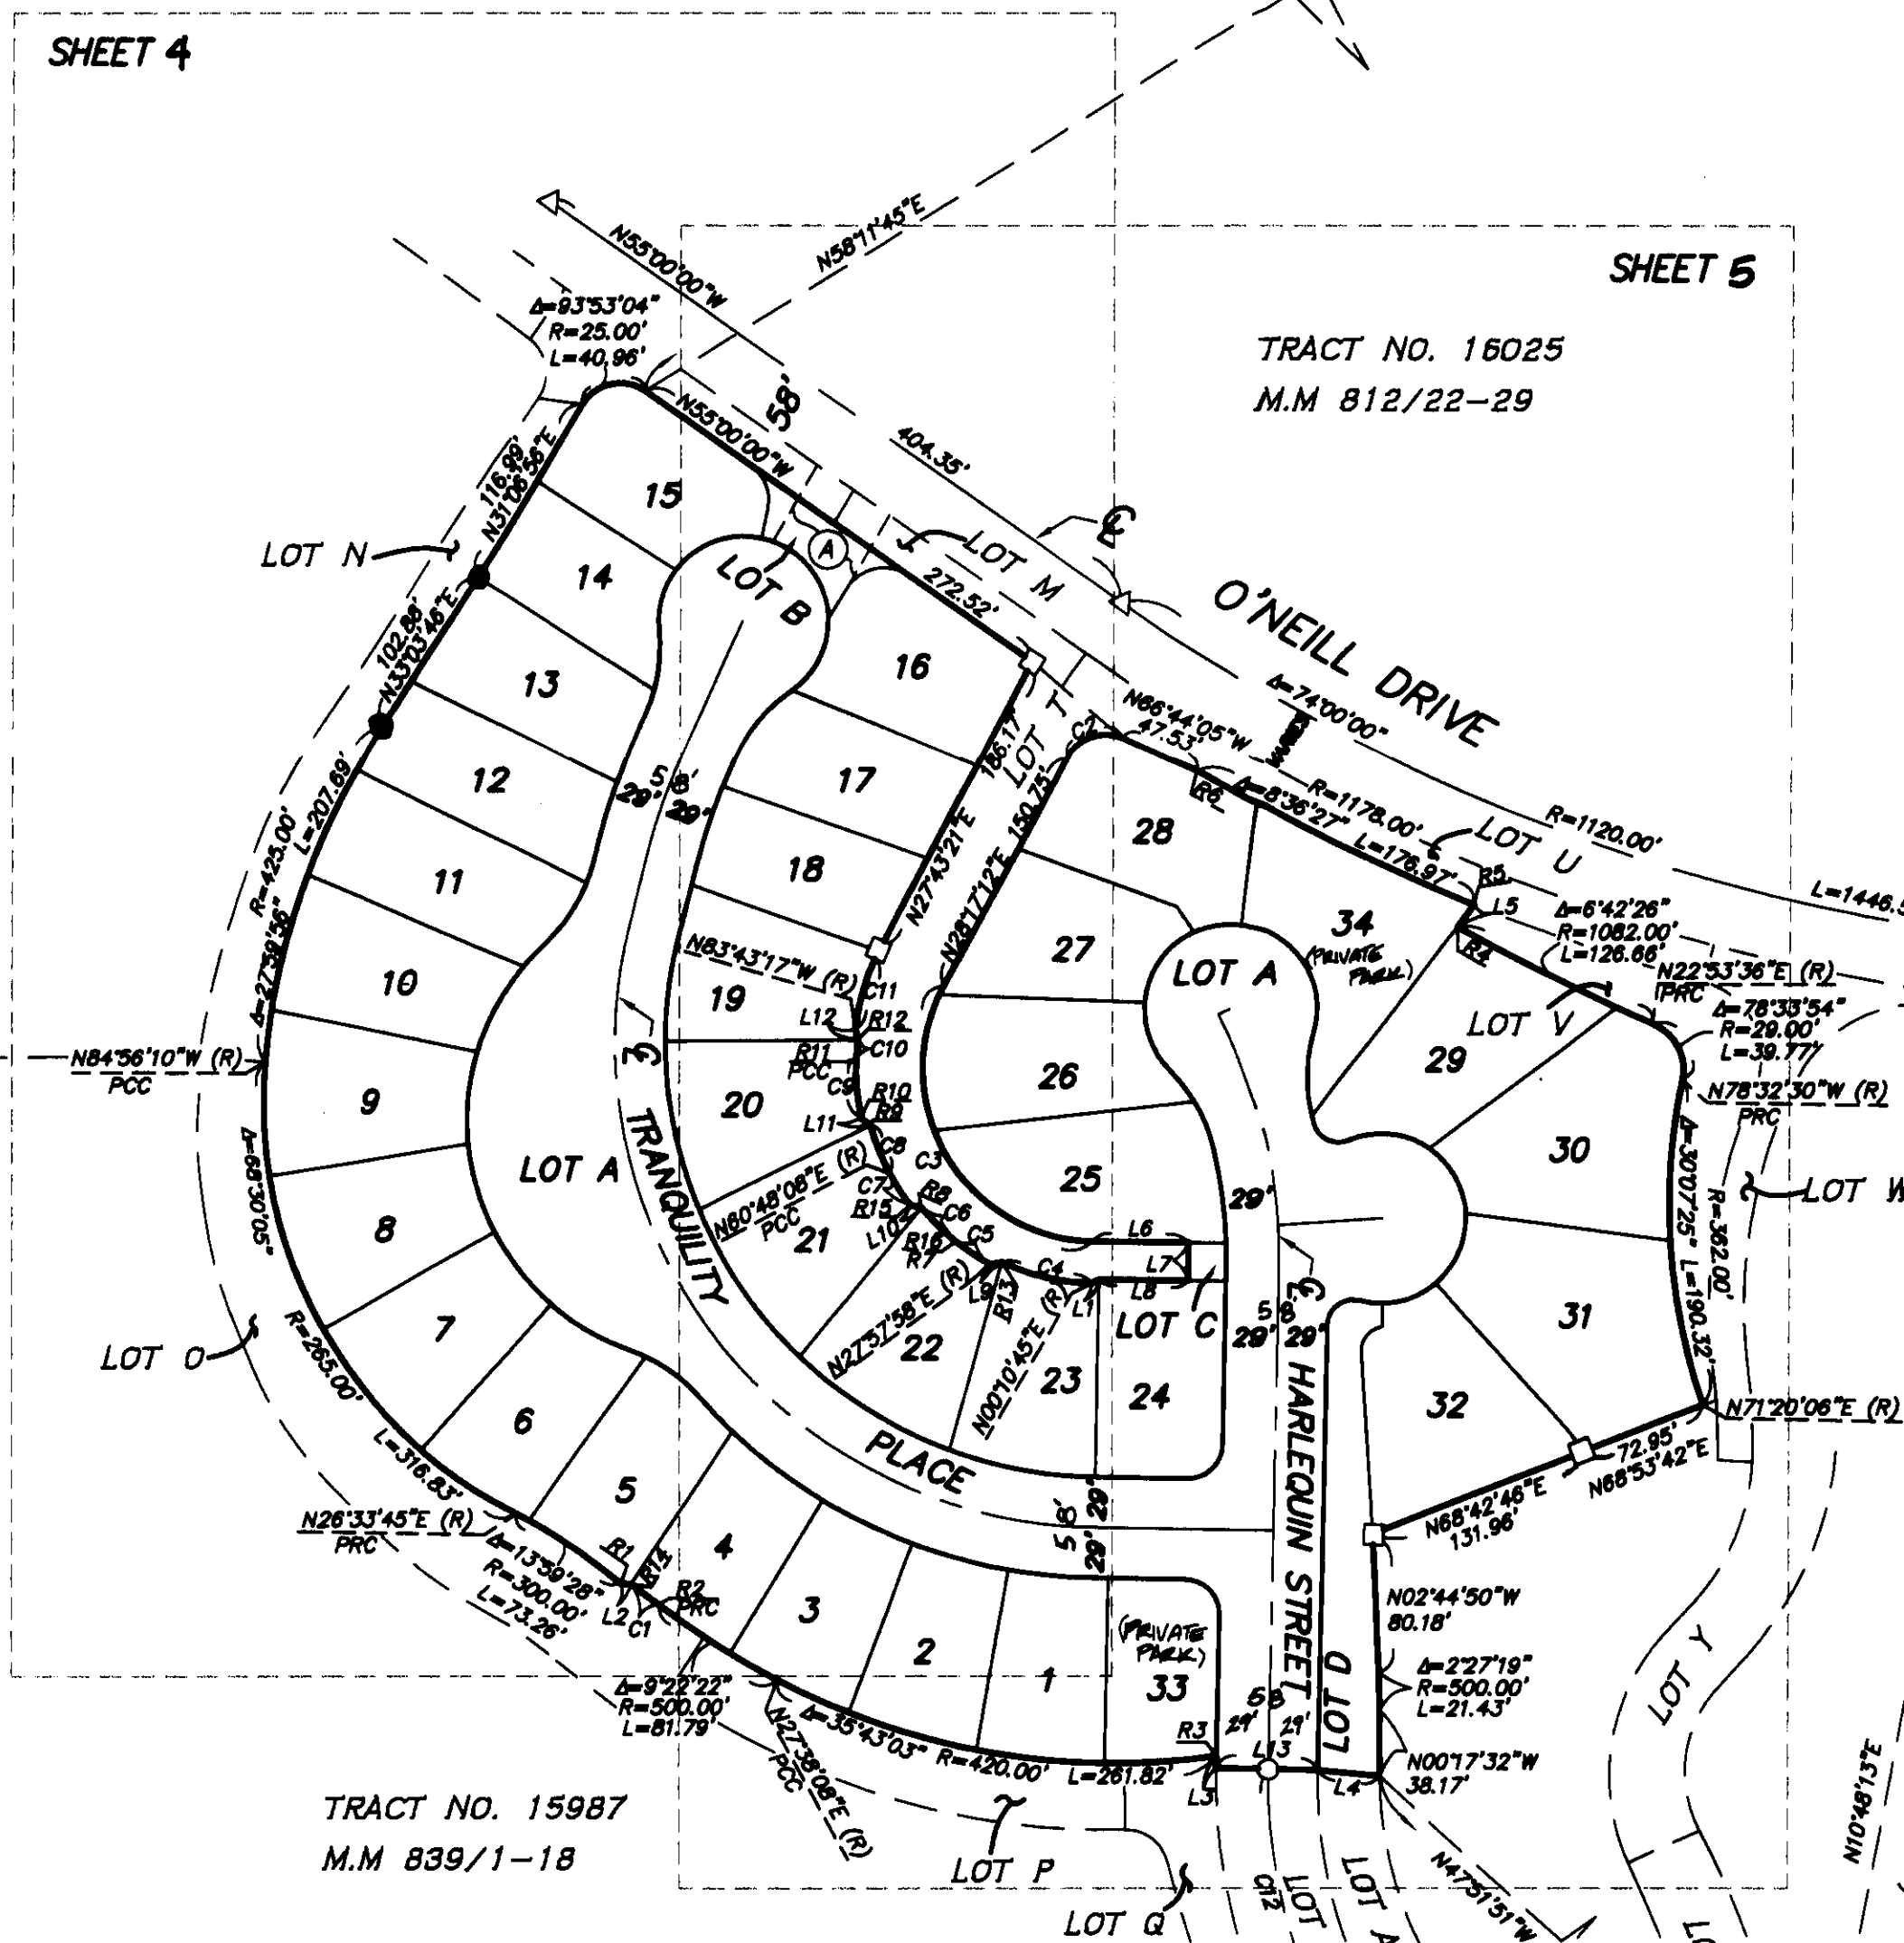

NOTES:

LOTS A THROUGH D ARE NOT SEPARATE BUILDING SITES.
LOT A IS FOR PRIVATE STREET PURPOSES.
LOTS 33 & 34 ARE FOR PRIVATE PARK PURPOSES AND ARE NOT SEPARATE BUILDING SITES.

BASIS OF BEARINGS

BEARINGS SHOWN HEREON ARE BASED ON THE BEARING BETWEEN O.C.S. HORIZONTAL CONTROL STATION GPS NO. 1417 AND STATION GPS NO. 1448, BEING N10°48'13"W PER RECORDS ON FILE IN THE OFFICE OF THE ORANGE COUNTY SURVEYOR.

DATUM STATEMENT

COORDINATES SHOWN HEREON ARE BASED ON THE CALIFORNIA COORDINATE SYSTEM (CCS83) ZONE VI 1983 NAD (1991.35 EPOCH O.C.S. GPS ADJUSTMENT). ALL DISTANCES SHOWN ARE GROUND DISTANCES UNLESS OTHERWISE NOTED. TO OBTAIN GRID DISTANCES, MULTIPLY GROUND DISTANCES BY 0.99993286.

EASEMENT NOTES

(A) INDICATES AN EASEMENT FOR SEWER, WATER & ACCESS PURPOSES PURPOSES DEDICATED TO THE SANTA MARGARITA WATER DISTRICT AS DEDICATED HEREON.

(B) INDICATES EASEMENT FOR PEDESTRIAN, EMERGENCY ACCESS AND PUBLIC SERVICE VEHICLE INGRESS AND EGRESS AS DEDICATED HEREON.

RADIAL TABLE

RADIAL	BEARING
R1	N40°33'13"E (R)
R2	N37°00'30"E (R)
R3	N08°04'55"W (R)
R4	N29°36'02"E (R)
R5	N21°53'39"E (R)
R6	N30°30'06"E (R)
R7	N38°51'31"E (R)
R8	N50°08'12"E (R)
R9	N75°03'05"E (R)
R10	N77°28'46"E (R)
R11	N86°50'19"W (R)
R12	N83°51'02"W (R)
R13	N26°34'39"E (R)
R14	N35°06'41"E (R)
R15	N52°13'58"E (R)
R16	N38°50'46"E (R)

LINE TABLE

LINE	BEARING	LENGTH
L1	N84°18'16"E	4.48'
L2	N86°49'21"W	5.81'
L3	N01°05'21"E	7.10'
L4	N84°29'08"W	35.50'
L5	N37°24'03"E	15.84'
L6	N89°15'39"W	56.14'
L7	N00°44'21"E	22.00'
L8	N89°15'39"W	52.26'
L9	N79°49'01"E	6.85'
L10	N75°59'11"W	6.62'
L11	N91°00'32"W	6.60'
L12	N14°33'48"W	6.21'
L13	N88°54'39"W	58.00'

CURVE TABLE

CURVE	DELTA	RADIUS	LENGTH
C1	1°53'30"	800.00'	19.87'
C2	84°58'43"	25.00'	37.08'
C3	117°32'51"	100.00'	205.16'
C4	25°23'54"	123.00'	54.52'
C5	10°53'34"	127.00'	24.14'
C6	11°15'28"	140.00'	27.51'
C7	6°34'09"	144.00'	21.54'
C8	14°14'58"	122.00'	30.34'
C9	15°40'55"	126.00'	34.49'
C10	2°38'16"	208.00'	10.85'
C11	21°26'38"	136.50'	51.09'
C12	29°12'18"	300.00'	152.92'

GPS NO. 1417

N. 2141450.558
E. 6141583.535
FD. 2 1/2" IRON PIPE W/2" OCS BRASS CAP STAMPED "GPS 1417 9-95" PER TRACT NO. 15987, M.M. 826/8-20 AND RECORDS ON FILE IN THE ORANGE COUNTY SURVEYORS OFFICE.

856 44


8560 45

SHEET 4 OF 5 SHEETS
(PORTION OF VESTING TENTATIVE
TRACT NO. 16505)

TOTAL ACREAGE: 9.293 AC.
NUMBERED LOTS: 34
LETTERED LOTS: 4
DATE OF SURVEY: MAY 2003

TRACT NO. 16505


IN THE UNINCORPORATED TERRITORY OF ORANGE COUNTY, STATE OF CALIFORNIA
DOUGLAS BENDER AND ASSOCIATES DOUGLAS W. BENDER R.C.E. 28946
MARCH, 2003

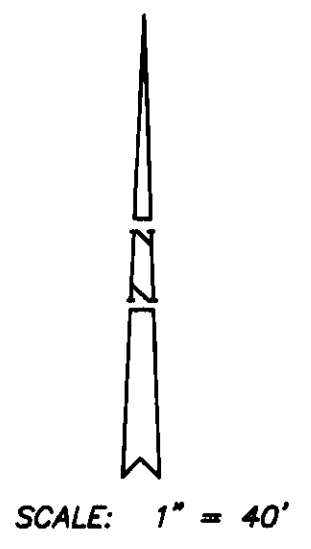

NOTES:
SEE SHEET 3 FOR BASIS OF BEARINGS, DATUM STATEMENT,
EASEMENT NOTES AND MONUMENTS.
LOTS A THROUGH D ARE NOT SEPARATE BUILDING SITES.
LOT A IS FOR PRIVATE STREET PURPOSES.
LOTS 33 & 34 ARE FOR PRIVATE PARK PURPOSES
AND ARE NOT SEPARATE BUILDING SITES.

LINE TABLE		
LINE	BEARING	LENGTH
L1	N12°14'57"E	18.71'
L2	N29°39'12"E	20.13'
L3	N14°33'48"W	8.21'
L4	N51°00'32"W	8.80'
L5	N75°39'11"W	6.82'
L6	N78°49'01"E	6.65'
L7	N84°18'18"E	4.48'
L8	N29°39'12"E	28.84'
L9	N29°39'12"E	47.42'

CURVE TABLE			
CURVE	DELTA	RADIUS	LENGTH
C1	1°35'27"	300.00'	8.33'
C2	6°74'57"	25.00'	28.34'
C3	85°00'48"	25.00'	41.46'
C4	1°25'24"	136.50'	3.39'
C5	2°39'18"	208.00'	10.85'
C6	8°34'08"	144.00'	21.54'
C7	8°08'57"	48.00'	6.98'
C8	9°06'14"	48.00'	7.79'

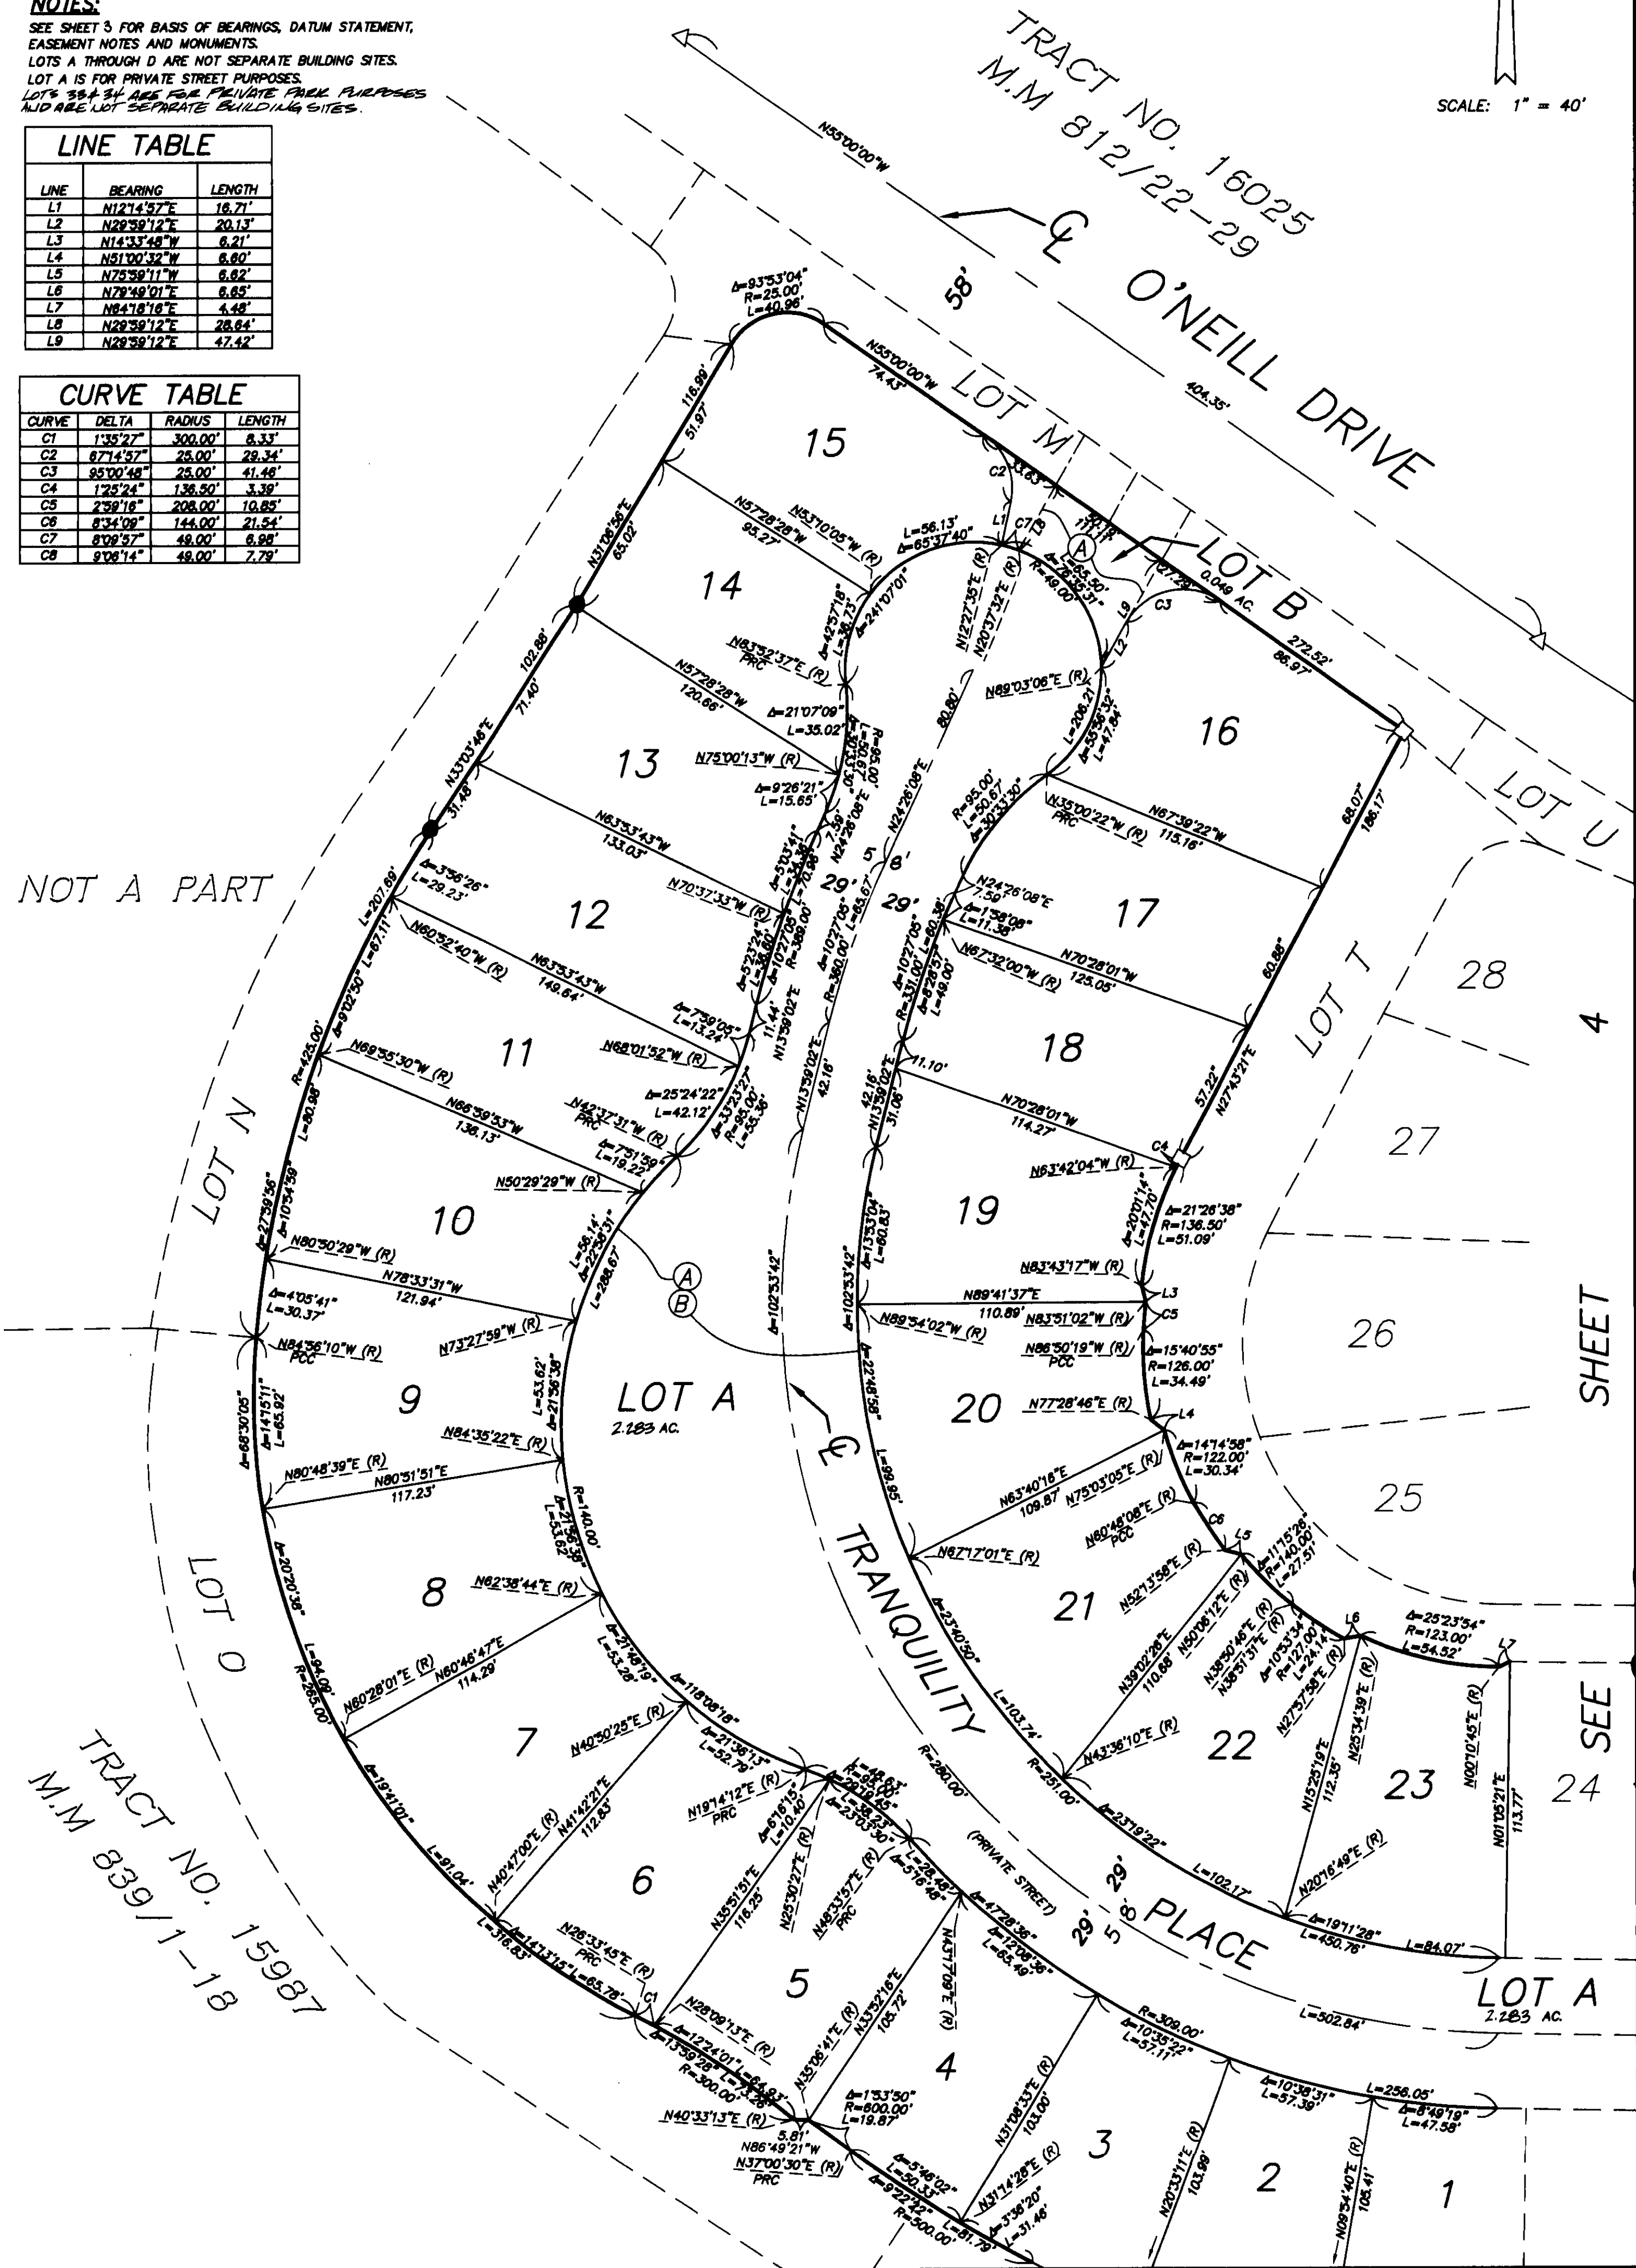

8560 45
SEE SHEET 45

TOTAL ACREAGE: 9.293 AC.
NUMBERED LOTS: 34
LETTERED LOTS: 4
DATE OF SURVEY: MAY 2003

IN THE UNINCORPORATED TERRITORY OF ORANGE COUNTY, STATE OF CALIFORNIA
DOUGLAS BENDER AND ASSOCIATES DOUGLAS W. BENDER R.C.E. 28946
MAY, 2003

NOTES:

SEE SHEET 3 FOR BASIS OF BEARINGS, DATUM STATEMENT,
EASEMENT NOTES AND MONUMENTS.

LOTS A THROUGH D ARE NOT SEPARATE BUILDING SITES.

LOT A IS FOR PRIVATE STREET PURPOSES.

LOTS 30 & 34 ARE FOR PRIVATE PARK PURPOSES
AND ARE NOT SEPARATE BUILDING SITES.

CURVE	DELTA	RADIUS	LENGTH
C1	371°44"	291.00'	16.23'
C2	86°43'42"	15.00'	25.32'
C3	103°37'17"	15.00'	27.02'
C4	84°36'29"	14.00'	20.67'
C5	45°11'	320.00'	27.10'

SCALE: 1" = 40'

