

SHEET 1 OF 5 SHEETS
10 NUMBERED LOTS AND
LOTS A THROUGH H, INCLUSIVE
ACREAGE: 13.199 ACRES
(ALL OF TENTATIVE
TRACT NO. 16515)

TRACT NO. 16515

IN UNINCORPORATED TERRITORY OF THE COUNTY OF ORANGE,
STATE OF CALIFORNIA

BEING A SUBDIVISION OF PARCEL 1 OF LOT LINE ADJUSTMENT NO. LL 2003-019,
RECORDED AS INSTRUMENT NO. 2003-001005449 OF OFFICIAL RECORDS,
TOGETHER WITH LOTS Y, Z AND AA OF TRACT NO. 15987, AS PER MAP FILED IN
BOOK 839, PAGES 1 THROUGH 18, INCLUSIVE, OF MISCELLANEOUS MAPS, BOTH IN
THE OFFICE OF THE COUNTY RECORDER OF SAID COUNTY.

HUNSAKER AND ASSOCIATES IRVINE, INC.
RORY S. WILLIAMS, L.S. 6654 DATE OF SURVEY: JULY, 2003

ACCEPTED AND FILED AT THE
REQUEST OF

COMMERCE TITLE

DATE: OCTOBER 27, 2003

TIME: 01:38 PM FEE: \$ 15.00

INSTRUMENT NO. 2003001317908

BOOK 850 PAGE 21-25A/m

TOM DALY
COUNTY CLERK - RECORDER

BY  DEPUTY

OWNERSHIP CERTIFICATE:

WE, THE UNDERSIGNED, BEING ALL PARTIES HAVING ANY RECORD TITLE INTEREST IN THE LAND COVERED BY THIS MAP, DO HEREBY CONSENT TO THE PREPARATION AND RECORDATION OF SAID MAP, AS SHOWN WITHIN THE DISTINCTIVE BORDER LINE.

WE HEREBY DEDICATE TO THE COUNTY OF ORANGE THE EASEMENTS FOR INGRESS AND EGRESS OF EMERGENCY AND PUBLIC SERVICE VEHICLES, AS SHOWN ON SAID MAP.

WE ALSO HEREBY DEDICATE TO THE SANTA MARGARITA WATER DISTRICT THE EASEMENTS FOR WATER, RECYCLED WATER, SEWER, ACCESS AND DRAINAGE PURPOSES, AS SHOWN ON THIS TRACT MAP, WHICH EASEMENTS SHALL BE SUBJECT TO THE SAME TERMS AND CONDITIONS AS SHOWN IN THAT CERTAIN EASEMENT RECORDED SEPTEMBER 18, 2002, AS INSTRUMENT NO. 20020799401 OF OFFICIAL RECORDS OF ORANGE COUNTY, CALIFORNIA.

SURVEYOR'S STATEMENT:

THIS MAP WAS PREPARED BY ME OR UNDER MY DIRECTION AND IS BASED UPON A FIELD SURVEY IN CONFORMANCE WITH THE REQUIREMENTS OF THE SUBDIVISION MAP ACT AND LOCAL ORDINANCE AT THE REQUEST OF DMB LADERA, L.L.C., IN JULY, 2003. I HEREBY STATE THAT ALL MONUMENTS ARE OF THE CHARACTER AND OCCUPY THE POSITIONS INDICATED, OR THAT THEY WILL BE SET IN SUCH POSITIONS; AND THAT SAID MONUMENTS ARE SUFFICIENT TO ENABLE THE SURVEY TO BE RETRACED. I HEREBY STATE THAT THIS FINAL MAP SUBSTANTIALLY CONFORMS TO THE CONDITIONALLY APPROVED TENTATIVE MAP.

 9/10/03
RORY S. WILLIAMS, L.S. 6654 DATE
LICENSE EXPIRES: 12/31/03



COUNTY SURVEYOR'S STATEMENT

I HEREBY STATE THAT I HAVE EXAMINED THIS MAP AND HAVE FOUND IT TO BE SUBSTANTIALLY IN CONFORMANCE WITH THE TENTATIVE MAP AS FILED WITH, AMENDED AND APPROVED BY THE ORANGE COUNTY SUBDIVISION COMMITTEE; THAT ALL PROVISIONS OF THE SUBDIVISION MAP ACT AND COUNTY SUBDIVISION REGULATIONS HAVE BEEN COMPLIED WITH AND I AM SATISFIED SAID MAP IS TECHNICALLY CORRECT.

DATED THIS 30TH DAY OF SEPTEMBER, 2003.


COUNTY SURVEYOR

LS EXPIRATION DATE: 6/30/06
BY MICHAEL K. SULLIVAN
LS 6234 EXPIRES 6/30/06



COUNTY TREASURER-TAX COLLECTOR'S CERTIFICATE:

STATE OF CALIFORNIA }
COUNTY OF ORANGE } SS

I HEREBY CERTIFY THAT ACCORDING TO THE RECORDS OF MY OFFICE THERE ARE NO LIENS AGAINST THE LAND COVERED BY THIS MAP OR ANY PART THEREOF FOR UNPAID STATE, COUNTY, MUNICIPAL OR LOCAL TAXES OR SPECIAL ASSESSMENTS COLLECTED AS TAXES, EXCEPT TAXES OR SPECIAL ASSESSMENTS COLLECTED AS TAXES NOT YET PAYABLE.

AND DO CERTIFY TO THE RECORDER OF ORANGE COUNTY THAT THE PROVISIONS OF THE SUBDIVISION MAP ACT HAVE BEEN COMPLIED WITH REGARDING DEPOSITS TO SECURE PAYMENT OF TAXES OR SPECIAL ASSESSMENTS COLLECTED AS TAXES ON THE LAND COVERED BY THIS MAP.

DATED THIS 22TH DAY OF September, 2003.

JOHN M.W. MOORLACH
COUNTY TREASURER-TAX COLLECTOR

BY:  DEPUTY TREASURER-TAX COLLECTOR

CLERK OF THE BOARD OF SUPERVISORS' CERTIFICATE:


STATE OF CALIFORNIA }
COUNTY OF ORANGE } SS

I HEREBY CERTIFY THAT THIS MAP WAS PRESENTED FOR APPROVAL TO THE BOARD OF SUPERVISORS OF THE COUNTY OF ORANGE AT REGULAR MEETING THEREOF HELD ON THE 21ST DAY OF October, 2003, AND THAT THEREUPON SAID BOARD DID, BY AN ORDER DULY PASSED AND ENTERED, APPROVE SAID MAP.

AND DID ACCEPT ON BEHALF OF THE COUNTY OF ORANGE THE EASEMENTS FOR INGRESS AND EGRESS OF EMERGENCY AND PUBLIC SERVICE VEHICLES, AS DEDICATED.

AND DID ALSO APPROVE SUBJECT MAP PURSUANT TO THE PROVISIONS OF SECTION 66436 (a)(3)(A) OF THE SUBDIVISION MAP ACT.

DATED THIS 21ST DAY OF October, 2003.

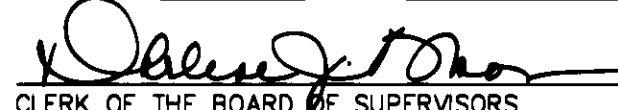
CLERK OF THE BOARD OF SUPERVISORS
DARLENE J. BLOOM



CERTIFICATE OF ACCEPTANCE - SANTA MARGARITA WATER DISTRICT

THE UNDERSIGNED, BEING THE DULY APPOINTED AGENT OF THE SANTA MARGARITA WATER DISTRICT, A PUBLIC CORPORATION IN ORANGE COUNTY, CALIFORNIA, PURSUANT TO ITS RESOLUTION NO. 88-10-2, DOES HEREBY ACCEPT ON BEHALF OF SAID DISTRICT, THE EASEMENTS FOR WATER, RECYCLED WATER, SEWER, ACCESS AND DRAINAGE PURPOSES, AS DEDICATED AND SHOWN ON THIS TRACT MAP, BY AND BETWEEN THE SANTA MARGARITA WATER DISTRICT AND DMB LADERA, L.L.C., A DELAWARE LIMITED LIABILITY COMPANY, AND DOES HEREBY CERTIFY THAT THE GRANTEE CONSENTS TO THE RECORDATION OF SAID TRACT MAP.



DANIEL R. FERONS, CHIEF ENGINEER
SANTA MARGARITA WATER DISTRICT

NOTARY ACKNOWLEDGMENT - SANTA MARGARITA WATER DISTRICT

STATE OF CALIFORNIA }
COUNTY OF ORANGE } SS

ON Sept. 11, 2003, BEFORE ME, Cindy R. Lane, Notary Public, PERSONALLY APPEARED DANIEL R. FERONS, PERSONALLY KNOWN TO ME (OR PROVED TO ME ON THE BASIS OF SATISFACTORY EVIDENCE) TO BE THE PERSON WHOSE NAME IS SUBSCRIBED TO THE WITHIN INSTRUMENT AND ACKNOWLEDGED TO ME THAT HE EXECUTED THE SAME IN HIS AUTHORIZED CAPACITY, AND THAT BY HIS SIGNATURE ON THE INSTRUMENT THE PERSON, OR ENTITY UPON BEHALF OF WHICH THE PERSON ACTED, EXECUTED THE INSTRUMENT.

WITNESS MY HAND:

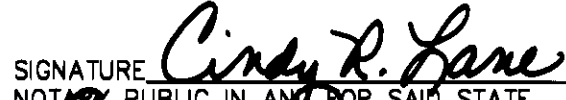SIGNATURE 
NOTARY PUBLIC IN AND FOR SAID STATE
CINDY R. LANE
(NAME PRINTED)

MY PRINCIPAL PLACE OF BUSINESS IS
IN ORANGE COUNTY.

MY COMMISSION EXPIRES: Feb 20, 2005

AUTOMATIC FIRE SPRINKLER NOTE:

ALL COMMERCIAL STRUCTURES GREATER THAN 6,000 SQUARE FEET, ALL MULTIFAMILY RESIDENTIAL STRUCTURES, ALL SINGLE-FAMILY STRUCTURES EXCEEDING 5,500 SQUARE FEET, AND ALL STRUCTURES EXCEEDING FIRE DEPARTMENT ACCESS REQUIREMENTS SHALL BE PROTECTED BY AN AUTOMATIC FIRE SPRINKLER SYSTEM.

SPECIAL FIRE PROTECTION NOTE:

SUBJECT PROPERTY IS IN A "SPECIAL FIRE PROTECTION AREA" AND MUST MEET ALL REQUIREMENTS FOR DEVELOPMENT WITHIN THE AREA OR FILE FOR AN EXCLUSION WITH THE FIRE CHIEF.

HIGH FIRE HAZARD AREA NOTE:

THE LOTS SHOWN ON THIS MAP ARE IN A HIGH FIRE HAZARD AREA DUE TO WILDLAND EXPOSURE.

NOTE:

THE PRIVATE STREETS CONSTRUCTED WITHIN THIS MAP SHALL BE OWNED, OPERATED AND MAINTAINED BY THE DEVELOPER, SUCCESSORS OR ASSIGNS. THE COUNTY OF ORANGE SHALL HAVE NO RESPONSIBILITY THEREFOR, UNLESS PURSUANT TO APPROPRIATE SECTIONS OF THE STREETS AND HIGHWAYS CODE OF THE STATE OF CALIFORNIA, THE SAID PRIVATE STREETS HAVE BEEN ACCEPTED INTO THE COUNTY ROAD SYSTEM BY APPROPRIATE RESOLUTION OF THE ORANGE COUNTY BOARD OF SUPERVISORS.

SIGNATURE OMISSIONS:

PURSUANT TO THE PROVISIONS OF SECTION 66436 (a)(3)(A)&(C) OF THE SUBDIVISION MAP ACT, THE FOLLOWING SIGNATURES HAVE BEEN OMITTED:

LADERA DEVELOPMENT COMPANY, L.L.C., HOLDER OF OIL, GAS AND MINERAL RIGHTS RECORDED DECEMBER 10, 1996, AS INSTRUMENT NO. 19960624029 OF OFFICIAL RECORDS.

SANTA MARGARITA WATER DISTRICT, HOLDER OF EASEMENTS FOR SEWER, WATER, RECYCLED WATER AND ACCESS PURPOSES, AND THE EASEMENT FOR DRAINAGE PURPOSES AS DEDICATED ON THE MAP OF TRACT NO. 15987, M.M. 839/1-18.

850 21

SHEET 2 OF 5 SHEETS
SCALE: 1" = 200'
10 NUMBERED LOTS AND
LOTS A THROUGH H, INCLUSIVE
ACREAGE: 13.199 ACRES
(ALL OF TENTATIVE
TRACT NO. 16515)

TRACT NO. 16515

IN UNINCORPORATED TERRITORY OF THE COUNTY OF ORANGE,
STATE OF CALIFORNIA

HUNSAKER AND ASSOCIATES IRVINE, INC.
RORY S. WILLIAMS, L.S. 6654 DATE OF SURVEY: JULY, 2003

BASIS OF BEARINGS:
THE BEARINGS SHOWN HEREON ARE BASED ON THE BEARING BETWEEN O.C.S. HORIZONTAL CONTROL STATION GPS NO. 1417 AND STATION GPS NO. 1448 BEING N10°48'15"E PER RECORDS ON FILE IN THE OFFICE OF THE ORANGE COUNTY SURVEYOR.

DATUM STATEMENT:
COORDINATES SHOWN ARE BASED ON THE CALIFORNIA COORDINATE SYSTEM (CCS83). ZONE 14N, 1983 NAD, (1991.35 EPOCH OCS GPS ADJUSTMENT). ALL DISTANCES SHOWN ARE GROUND, UNLESS OTHERWISE NOTED. TO OBTAIN GRID DISTANCE, MULTIPLY GROUND DISTANCE BY 0.999948295. COMBINATION FACTOR IS PROJECT SPECIFIC.

MONUMENT NOTES:
2" I.P. TAGGED L.S. 6654 OR LEAD, TACK & TAG L.S. 6654 OR NAIL & TAG L.S. 6654 OR 8" SAW STAMPED L.S. 6654 TO BE SET AT ALL TRACT BOUNDARY CORNERS WITHIN 90 DAYS AFTER ACCEPTANCE OF IMPROVEMENTS, UNLESS OTHERWISE NOTED.

© INDICATES LOCATION OF 1" I.P. TAGGED L.S. 6654 OR LEAD, TACK & TAG L.S. 6654 OR NAIL & TAG L.S. 6654 OR 8" SAW STAMPED L.S. 6654 TO BE SET, WITHIN 90 DAYS AFTER ACCEPTANCE OF IMPROVEMENTS, UNLESS OTHERWISE NOTED.

8" SAW STAMPED L.S. 6654 OR LEAD, TACK & TAG L.S. 6654 OR 1" I.P. TAGGED L.S. 6654 TO BE SET AT ALL STREET CENTERLINE POINTS OF CONTROL, WITHIN 90 DAYS AFTER ACCEPTANCE OF IMPROVEMENTS, UNLESS OTHERWISE NOTED.

● INDICATES FOUND MONUMENT OR LOCATION OF MONUMENT SET, AS NOTED.

▲ INDICATES FOUND ORANGE COUNTY SURVEYOR GPS CONTROL MONUMENT AS NOTED.

1 INDICATES LOCATION OF 2" I.P. TAGGED "P.L.S. 5557" OR SPIKE & WASHER STAMPED "P.L.S. 5557" OR LEAD, TACK & TAG "P.L.S. 5557" TO BE SET PER TRACT NO. 15987, M.M. 839/1-18.

2 INDICATES LOCATION OF 1" I.P. TAGGED "P.L.S. 5557" OR SPIKE & WASHER STAMPED "P.L.S. 5557" OR LEAD, TACK & TAG "P.L.S. 5557" TO BE SET PER TRACT NO. 15987, M.M. 839/1-18.


3 INDICATES SET 2" I.P. TAGGED L.S. 6654 PRIOR TO MAP RECORDATION.

EASEMENT NOTES:

- (A) INDICATES AN EASEMENT FOR INGRESS AND EGRESS OF EMERGENCY AND PUBLIC SERVICE VEHICLES DEDICATED HEREON TO THE COUNTY OF ORANGE.
- (B) INDICATES AN EASEMENT FOR WATER, RECYCLED WATER, SEWER, ACCESS AND DRAINAGE PURPOSES DEDICATED HEREON TO THE SANTA MARGARITA WATER DISTRICT.
- (C) INDICATES A SEWER, WATER, RECYCLED WATER AND ACCESS EASEMENT DEDICATED TO THE SANTA MARGARITA WATER DISTRICT PER TRACT NO. 15987, M.M. 839/1-18.
- (D) INDICATES A DRAINAGE EASEMENT DEDICATED TO THE SANTA MARGARITA WATER DISTRICT PER TRACT NO. 15987, M.M. 839/1-18.
- (E) INDICATES AN EASEMENT FOR PRIVATE DRAINAGE PURPOSES RESERVED HEREON FOR THE HOMEOWNER'S ASSOCIATION.
- (F) INDICATES AN EASEMENT FOR COMMUNITY TRAIL PURPOSES RESERVED HEREON FOR FUTURE GRANT.


NOTES:

LOTS A, B, C AND D ARE FOR PRIVATE STREET PURPOSES.
LOTS E, F, AND G ARE FOR OPEN SPACE/LANDSCAPING PURPOSES, AND ARE NOT SEPARATE BUILDING SITES.
LOT H IS FOR COMMUNITY TRAIL PURPOSES.

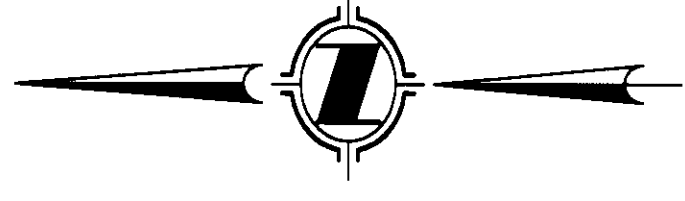

GPS NO. 1448
FD. 2" IRON PIPE WITH 1 3/4" OCS BRASS
CAP STAMPED "1448 9-95" PER R.S.B.
154/8-18 AND RECORDS ON FILE IN THE
ORANGE COUNTY SURVEYOR'S OFFICE
N 214°07'00.819 E 61°42'02.585

GPS NO. 1417
FD. 2 1/2" IRON PIPE WITH 2" OCS BRASS
CAP STAMPED "GPS 1417 9-95" PER R.S.B.
154/8-18 AND RECORDS ON FILE IN THE
ORANGE COUNTY SURVEYOR'S OFFICE
N 214°50.558 E 61°15'53.535

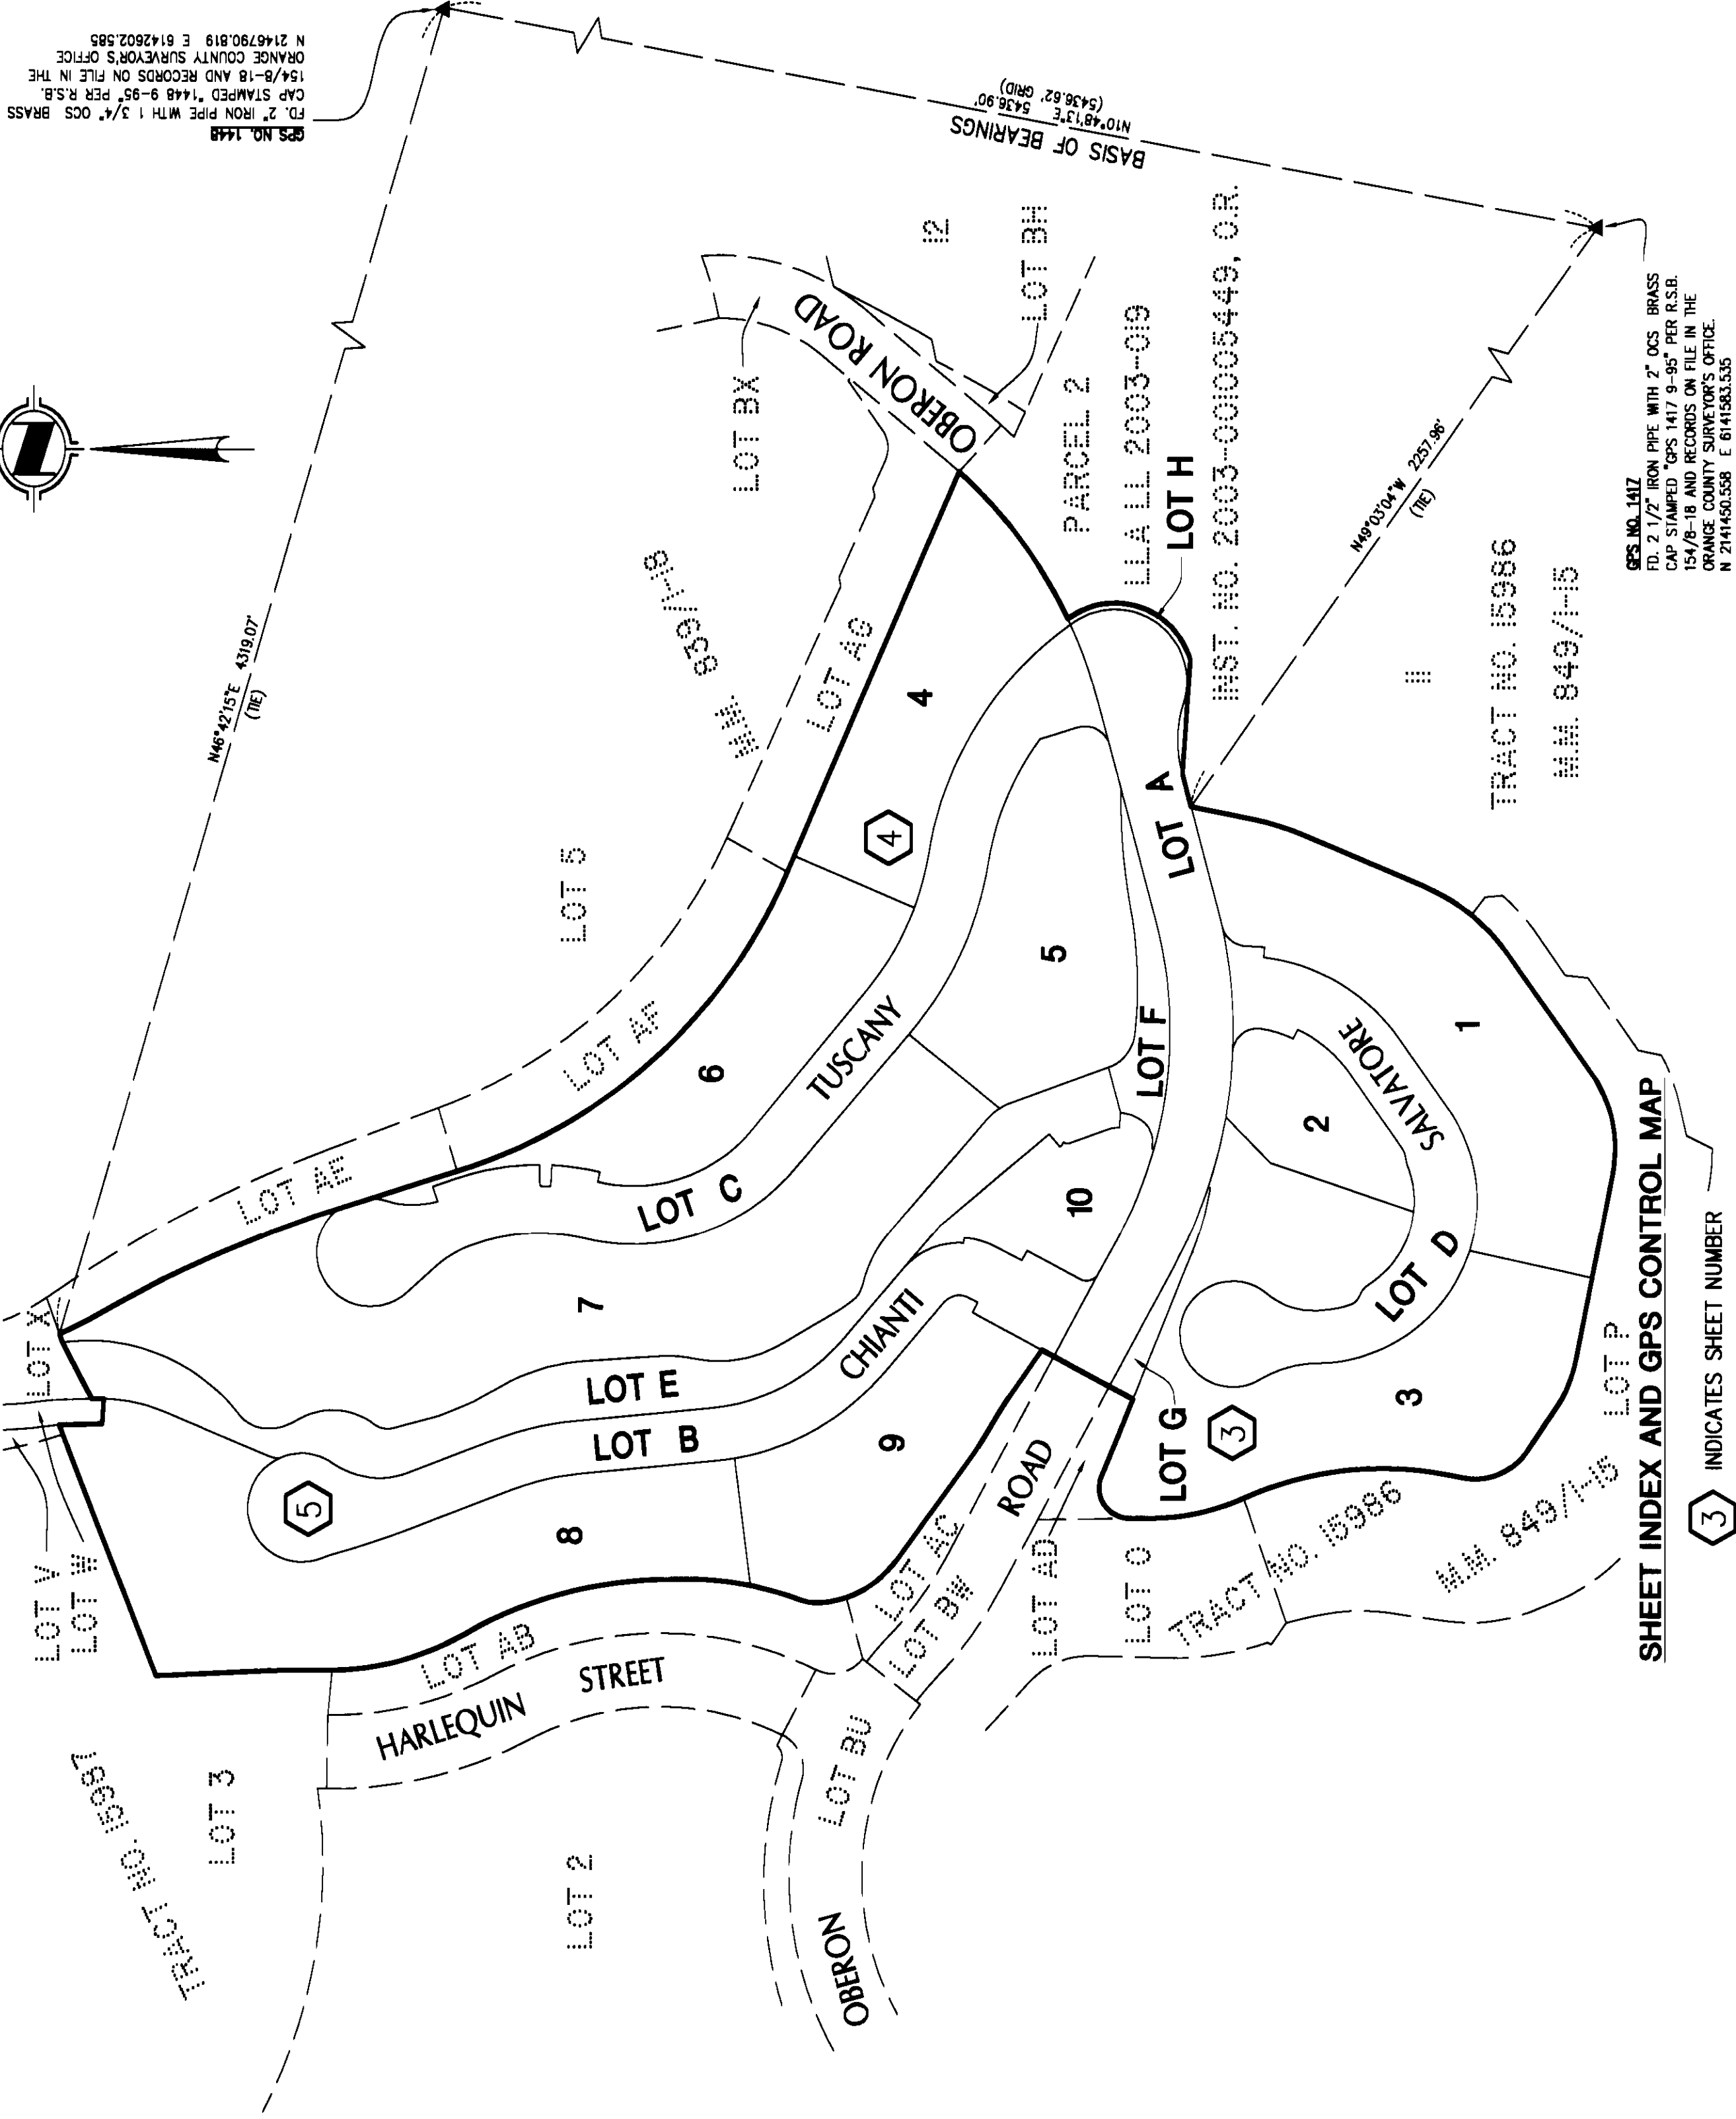

TRACT NO. 15986
M.M. 849/1-15

TRACT NO. 15986
M.M. 849/1-15

SHEET INDEX AND GPS CONTROL MAP

3 INDICATES SHEET NUMBER

SHEET 3 OF 5 SHEETS
SCALE: 1" = 40'
10 NUMBERED LOTS AND LOTS
A THROUGH H, INCLUSIVE
ACREAGE: 13.199 ACRES
(ALL OF TENTATIVE
TRACT NO. 16515)

TRACT NO. 16515

IN UNINCORPORATED TERRITORY OF THE COUNTY OF ORANGE,
STATE OF CALIFORNIA

HUNSAKER AND ASSOCIATES IRVINE, INC.
RORY S. WILLIAMS, L.S. 8654 DATE OF SURVEY: JULY, 2003


SEE SHEET 4

SHEET

SEE


...

TRACT NO. 16515
M.M. 849 / 1 - 15

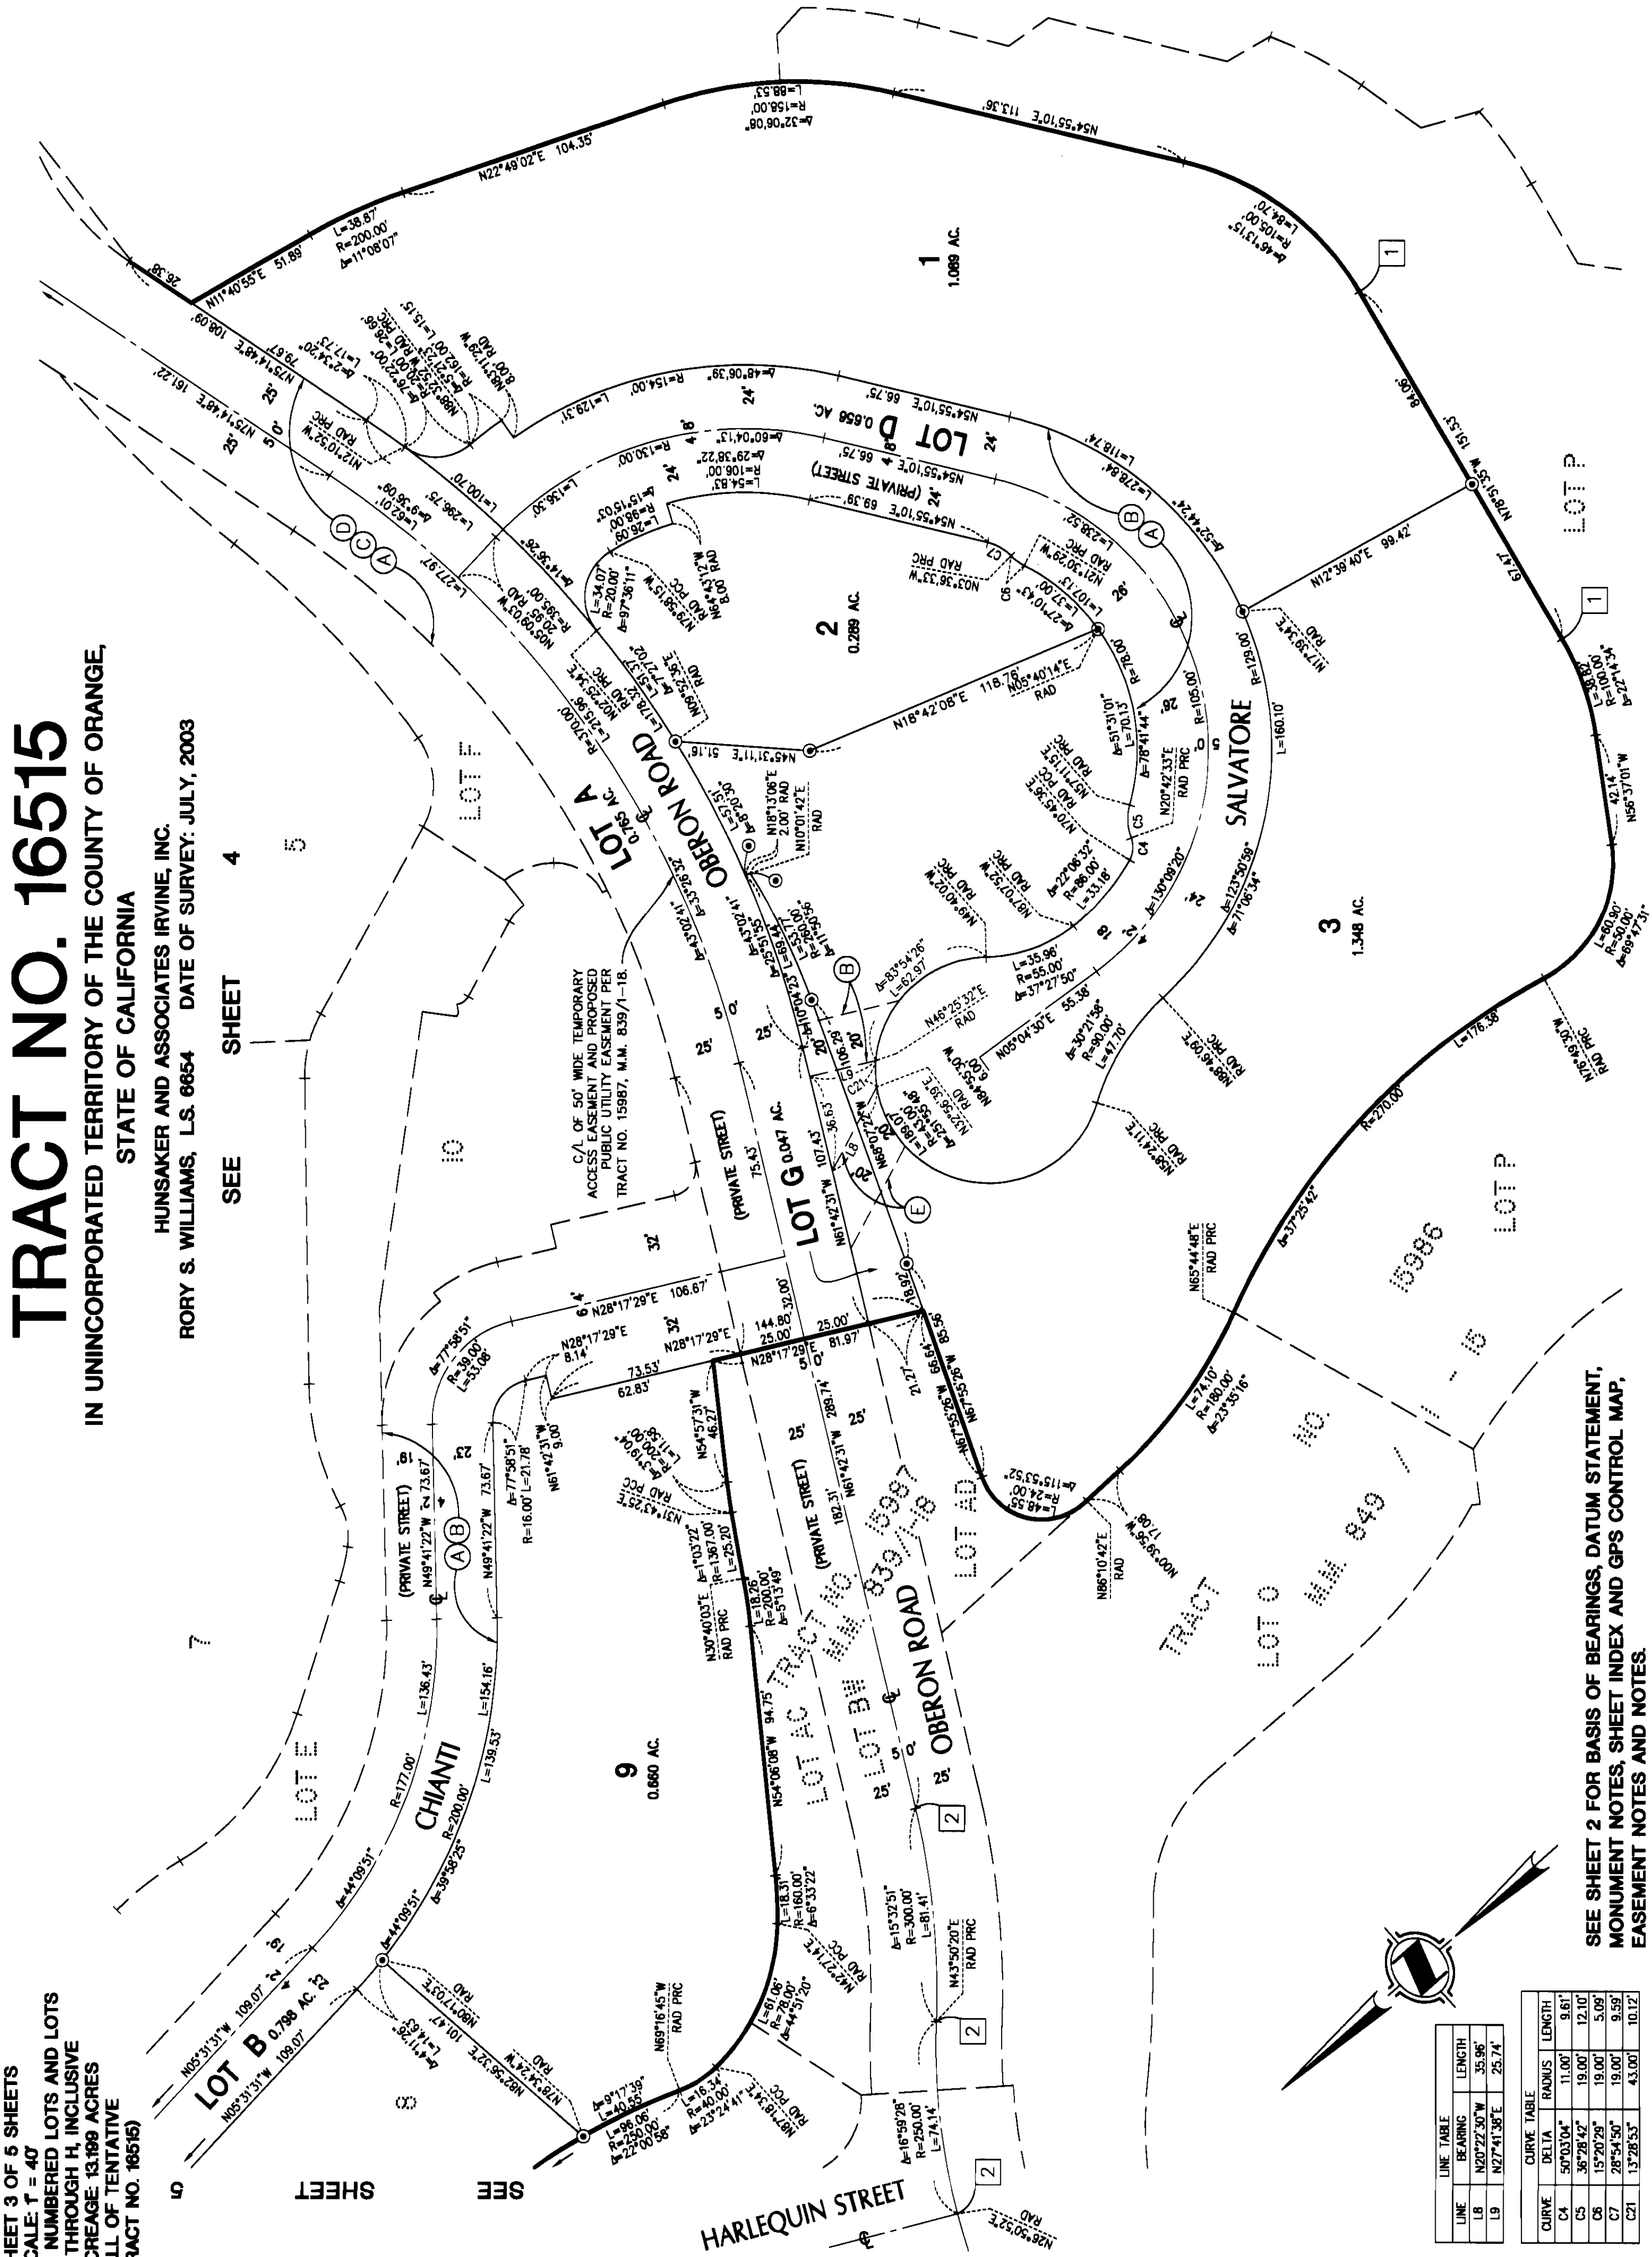

LINE TABLE		CURVE TABLE	
LINE	BEARING	DELTA	RADIUS
1B	N20°22'30"W	35.96'	
1C	N27°41'38"E	25.74'	

CURVE	DELTA	RADIUS	LENGTH
C4	50°03'04"	11.00'	9.61'
C5	36°28'42"	19.00'	12.10'
C6	15°20'29"	19.00'	5.09'
C7	28°54'50"	19.00'	9.59'
C21	13°28'53"	43.00'	10.12'

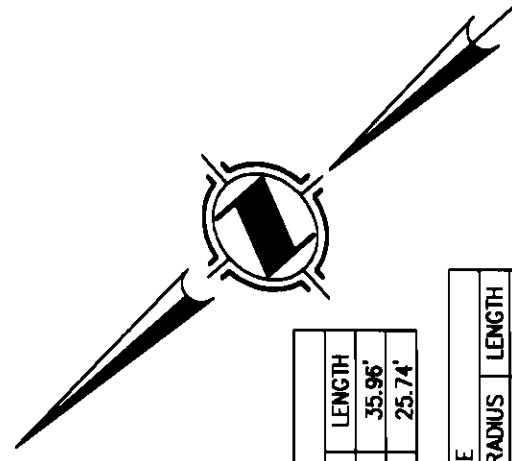


SEE SHEET 2 FOR BASIS OF BEARINGS, DATUM STATEMENT,
MONUMENT NOTES, SHEET INDEX AND GPS CONTROL MAP.
EASEMENT NOTES AND NOTES.

TRACT NO. 16515

IN UNINCORPORATED TERRITORY OF THE COUNTY OF ORANGE,
STATE OF CALIFORNIA

HUNSAKER AND ASSOCIATES IRVINE, INC.
RORY S. WILLIAMS, L.S. 8654 DATE OF SURVEY: JULY, 2003

SHEET 4 OF 5 SHEETS
SCALE: 1" = 40'
10 NUMBERED LOTS AND LOTS
A THROUGH H, INCLUSIVE
ACREAGE: 13.199 ACRES
(ALL OF TENTATIVE
TRACT NO. 16515)

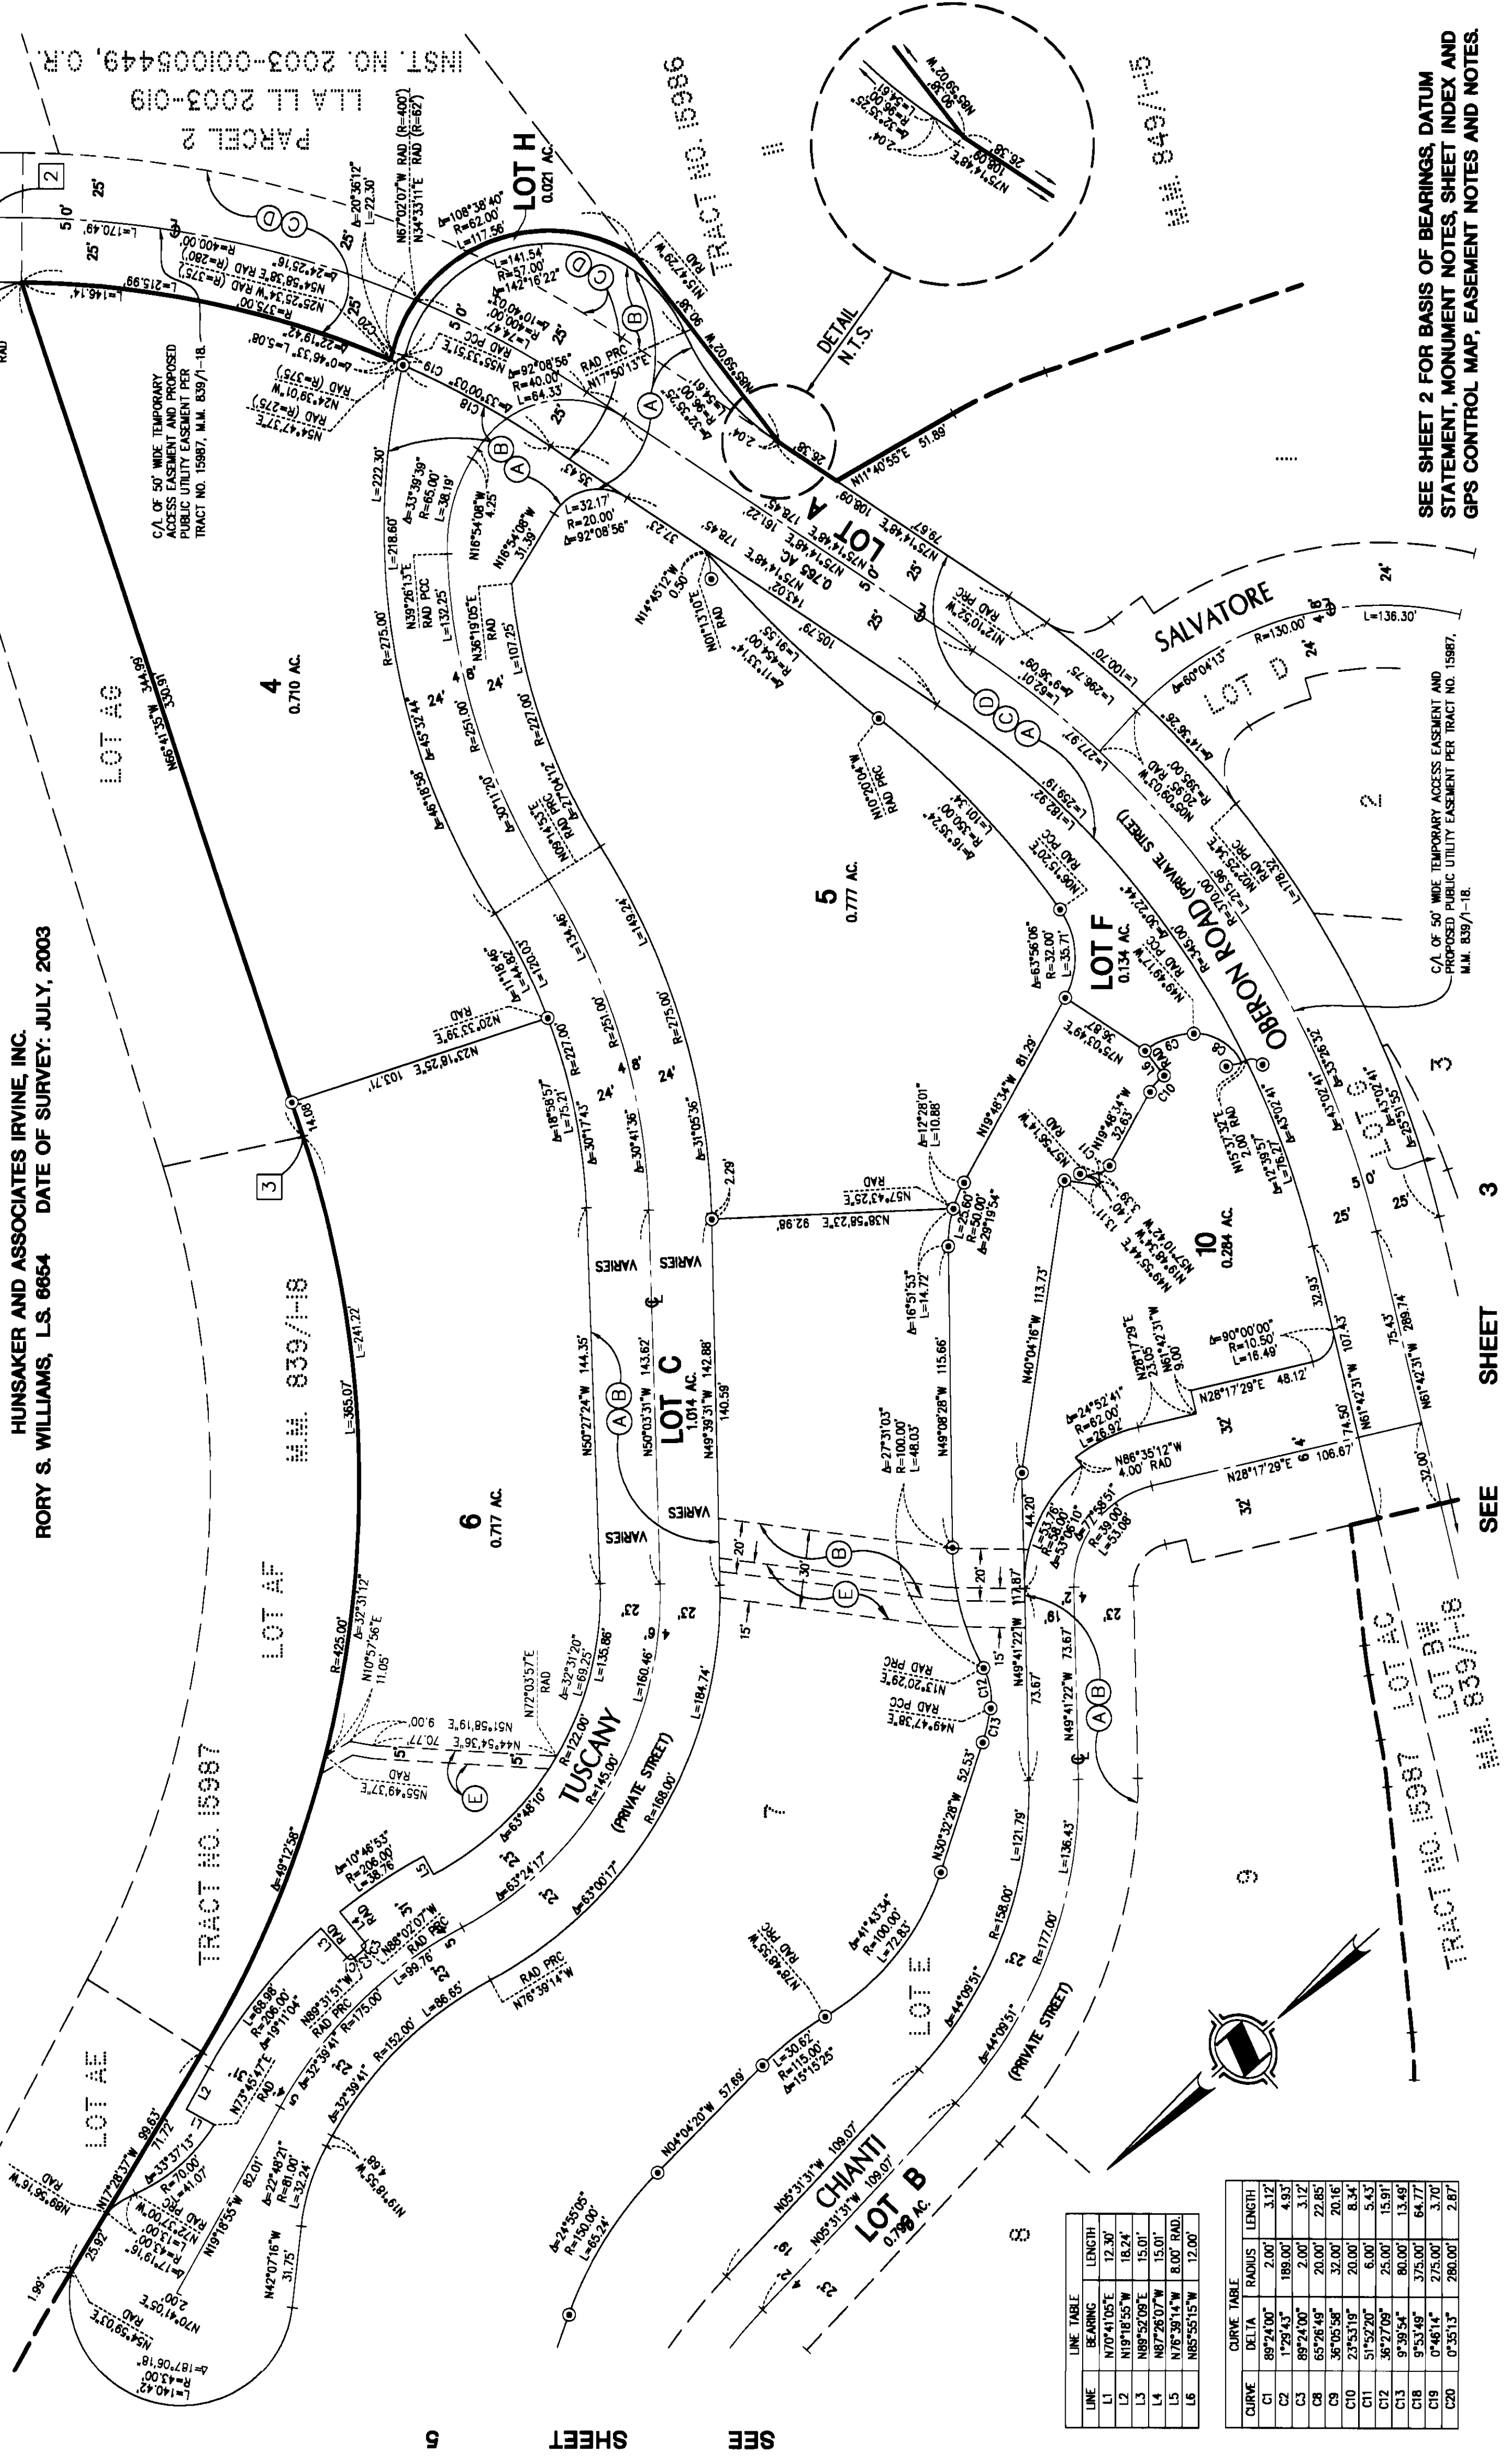

LINE TABLE		
LINE	BEARING	LENGTH
L1	N70°41'05"E	12.30'
L2	N19°18'55"W	18.24'
L3	N89°52'08"E	15.01'
L4	N67°26'07"W	15.01'
L5	N76°59'14"W	8.00' RAD.
L6	N85°55'15"W	12.00'

CURVE TABLE		
CURVE	DELTA	RADIUS
C1	89°24'00"	2.00'
C2	1°29'43"	189.00'
C3	89°24'00"	2.00'
C4	65°26'49"	20.00'
C5	96°05'58"	32.00'
C10	23°53'19"	20.00'
C11	51°52'20"	6.00'
C12	36°22'09"	25.00'
C13	9°39'54"	80.00'
C18	9°53'48"	375.00'
C19	0°46'14"	275.00'
C20	0°55'13"	280.00'

SEE SHEET 2 FOR BASIS OF BEARINGS, DATUM
STATEMENT, MONUMENT NOTES, SHEET INDEX AND
GPS CONTROL MAP, EASEMENT NOTES AND NOTES.

C/A OF 50' WIDE TEMPORARY ACCESS EASEMENT AND
PROPOSED PUBLIC UTILITY EASEMENT PER TRACT NO. 15987,
M.M. 839/1-18.


SEE SHEET 3

SHEET 5 OF 5 SHEETS
SCALE: 1" = 40'
10 NUMBERED LOTS AND LOTS
A THROUGH H, INCLUSIVE
ACREAGE: 13.189 ACRES
(ALL OF TENTATIVE
TRACT NO. 16515)

TRACT NO. 16515

IN UNINCORPORATED TERRITORY OF THE COUNTY OF ORANGE,
STATE OF CALIFORNIA

HUNSAKER AND ASSOCIATES IRVINE, INC.
RORY S. WILLIAMS, L.S. 8854 DATE OF SURVEY: JULY, 2003

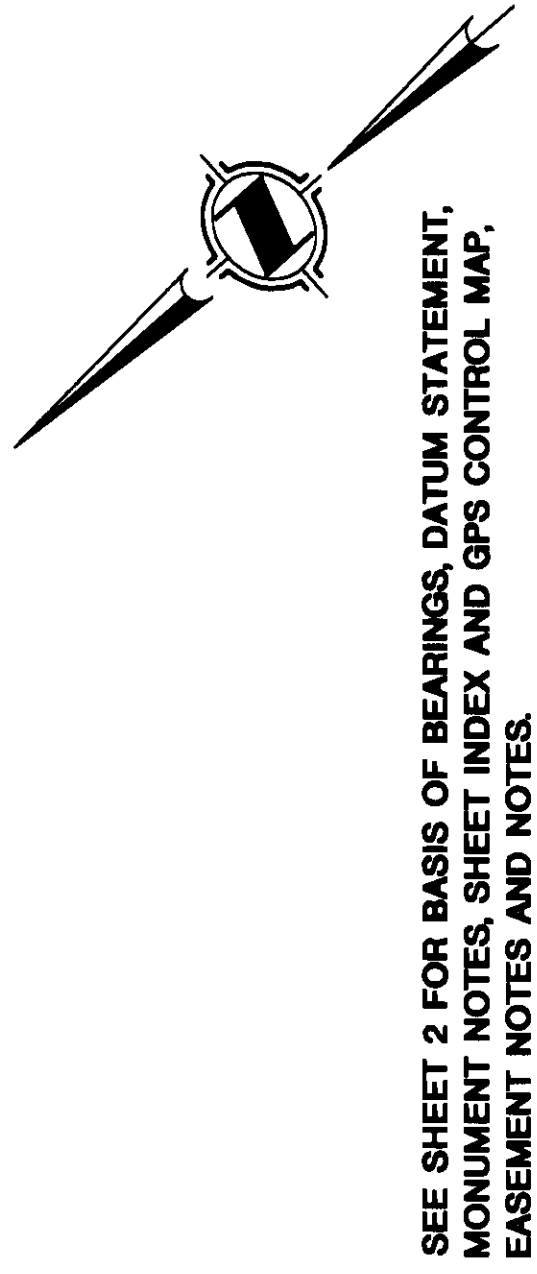

SEE SHEET 2 FOR BASIS OF BEARINGS, DATUM STATEMENT,
MONUMENT NOTES, SHEET INDEX AND GPS CONTROL MAP,
EASEMENT NOTES AND NOTES.

LINE TABLE		
LINE	BEARING	LENGTH
L1	N70°41'05"E	12.30'
L2	N19°18'55"W	18.24'
L3	N88°52'09"E	15.01'
L4	N87°26'07"W	15.01'
L5	N76°39'14"W	8.00'
L6	N85°55'15"W	12.00'
L7	N07°37'15"W	16.96'

CURVE TABLE		
CURVE	DELTA	RADIUS
C1	88°24'00"	2.00'
C2	1°28'43"	189.00'
C3	89°24'00"	2.00'
C10	2°53'19"	20.00'
C11	51°52'20"	6.00'
C12	36°27'09"	25.00'
C13	9°39'54"	80.00'
C14	25°16'29"	20.00'
C15	19°03'50"	42.00'
C16	7°53'33"	205.00'
C17	27°34'02"	125.00'

SEE SHEET 3

SHEET 4

SEE

SHEET 3

SEE