

SHEET 1 OF 4 SHEETS
16 NUMBERED LOTS AND
LOTS A THROUGH C, INCLUSIVE
ACREAGE: 7.047 ACRES
(PORTION OF VESTING
TENTATIVE TRACT NO. 16395)

TRACT NO. 16667

IN UNINCORPORATED TERRITORY OF THE COUNTY OF ORANGE,
STATE OF CALIFORNIA

BEING A SUBDIVISION OF LOT 6 OF TRACT NO. 15986, AS PER MAP FILED
IN BOOK 849, PAGES 1 THROUGH 15, INCLUSIVE, OF MISCELLANEOUS MAPS,
IN THE OFFICE OF THE COUNTY RECORDER OF SAID COUNTY.

HUNSAKER AND ASSOCIATES IRVINE, INC.
RORY S. WILLIAMS, L.S. 6654 DATE OF SURVEY: JULY, 2002

861 25
ACCEPTED AND FILED AT THE
REQUEST OF
First American Title
DATE: October 29, 2004
TIME: 1:24 PM FEE: \$116.00
INSTRUMENT NO. 2004000978757
BOOK 861 PAGE 25-29mm
TOM DALY
COUNTY CLERK - RECORDER
BY Sammy J. Dineen
DEPUTY

OWNERSHIP CERTIFICATE:

WE, THE UNDERSIGNED, BEING ALL PARTIES HAVING ANY RECORD TITLE INTEREST IN THE LAND COVERED BY THIS MAP, DO HEREBY CONSENT TO THE PREPARATION AND RECORDATION OF SAID MAP, AS SHOWN WITHIN THE DISTINCTIVE BORDER LINE.

WE HEREBY DEDICATE TO COUNTY OF ORANGE THE EASEMENTS FOR INGRESS AND EGRESS OF EMERGENCY AND PUBLIC SERVICE VEHICLES AS SHOWN ON SAID MAP.

WE ALSO HEREBY DEDICATE TO THE SANTA MARGARITA WATER DISTRICT THE EASEMENTS FOR WATER, RECYCLED WATER, SEWER AND ACCESS PURPOSES OVER THOSE EASEMENT AREAS AS SHOWN ON SAID MAP, WHICH EASEMENTS SHALL BE SUBJECT TO THE SAME CONDITIONS AS SHOWN IN THAT CERTAIN GRANT OF EASEMENT TO SANTA MARGARITA WATER DISTRICT RECORDED SEPTEMBER 18, 2002, AS INSTRUMENT NO. 20020799401 OF OFFICIAL RECORDS, COUNTY OF ORANGE.

WARMINGTON ARBOLEDO ASSOCIATES, L.P. A CALIFORNIA LIMITED PARTNERSHIP, OWNER.

BY: WARMINGTON HOMES CALIFORNIA, A CALIFORNIA CORPORATION, GENERAL PARTNER

BY: [Signature] BY: Robert G. McClaire
NAME: JAMES W. SKINNER NAME: ROBERT G. MCCLAIRE
TITLE: V.P. DIRECTOR OF ENGINEERING TITLE: VP PROJECT DEVELOPMENT

COMERICA BANK, BENEFICIARY UNDER DEED OF TRUST RECORDED SEPTEMBER 9, 2004,
AS INSTRUMENT NO. 2004000816842 OF OFFICIAL RECORDS.

BY: [Signature] BY: _____
NAME: Sonathan Ward NAME: _____
TITLE: Vice President TITLE: _____

DMB LADERA, LLC, A DELAWARE LIMITED LIABILITY COMPANY BENEFICIARY UNDER DEED OF TRUST RECORDED SEPTEMBER 9, 2004, AS INSTRUMENT NO. 2004000816841 OF OFFICIAL RECORDS, AND HOLDER OF EASEMENTS FOR CONSTRUCTION, MAINTENANCE, STORAGE, INGRESS AND EGRESS PURPOSES RESERVED IN THE DEED RECORDED SEPTEMBER 9, 2004 AS INSTRUMENT NO. 2004000816839 OF OFFICIAL RECORDS.

BY: RANCHO MISSION VIEJO, L.L.C., A DELAWARE LIMITED LIABILITY COMPANY, ITS
AUTHORIZED AGENT AND MANAGER.

BY: [Signature] BY: [Signature]
NAME: Paul Johnson NAME: Gregory S. Edwards
TITLE: Senior V.P. TITLE: C.F.O.

NOTARY ACKNOWLEDGMENT:

STATE OF CALIFORNIA } SS
COUNTY OF ORANGE }

ON Oct. 21, 2004 BEFORE ME, Diana L. Binks, PERSONALLY
APPEARED Paul Johnson AND Gregory S. Edwards PERSONALLY
KNOWN TO ME (OR PROVED TO ME ON THE BASIS OF SATISFACTORY EVIDENCE) TO BE THE PERSON(S)
WHOSE NAME(S) IS/ARE SUBSCRIBED TO THE WITHIN INSTRUMENT AND ACKNOWLEDGED TO ME THAT
HE/SHE/HEY EXECUTED THE SAME IN HIS/HER/THEIR AUTHORIZED CAPACITY(IES) AND THAT BY
HIS/HER/THEIR SIGNATURE(S) ON THE INSTRUMENT THE PERSON(S) OR ENTITY UPON BEHALF OF
WHICH THE PERSON(S) ACTED, EXECUTED THE INSTRUMENT.

WITNESS MY HAND:

SIGNATURE Diana L. Binks
NOTARY PUBLIC IN AND FOR SAID STATE
Diana L. Binks
(NAME PRINTED)

MY PRINCIPAL PLACE OF BUSINESS IS
IN Orange COUNTY.
MY COMMISSION EXPIRES: Dec. 12, 2006

SEE SHEET 2 FOR ADDITIONAL NOTARY ACKNOWLEDGMENTS.

AUTOMATIC FIRE SPRINKLER NOTE:

ALL COMMERCIAL STRUCTURES GREATER THAN 6,000 SQUARE FEET, ALL MULTIFAMILY RESIDENTIAL STRUCTURES, ALL SINGLE-FAMILY STRUCTURES EXCEEDING 5,500 SQUARE FEET, AND ALL STRUCTURES EXCEEDING FIRE DEPARTMENT ACCESS REQUIREMENTS SHALL BE PROTECTED BY AN AUTOMATIC FIRE SPRINKLER SYSTEM.

SPECIAL FIRE PROTECTION NOTE:

SUBJECT PROPERTY IS IN A SPECIAL FIRE PROTECTION AREA AND MUST MEET ALL REQUIREMENTS FOR DEVELOPMENT WITHIN THE AREA.

HIGH FIRE HAZARD AREA NOTE:

THE LOTS SHOWN ON THIS MAP ARE IN A HIGH FIRE HAZARD AREA DUE TO WILDLAND EXPOSURE.


NOTE:

THE PRIVATE STREETS CONSTRUCTED WITHIN THIS MAP SHALL BE OWNED, OPERATED AND MAINTAINED BY THE DEVELOPER, SUCCESSORS OR ASSIGNS. THE COUNTY OF ORANGE SHALL HAVE NO RESPONSIBILITY THEREFOR, UNLESS PURSUANT TO APPROPRIATE SECTIONS OF THE STREETS AND HIGHWAYS CODE OF THE STATE OF CALIFORNIA, THE SAID PRIVATE STREETS HAVE BEEN ACCEPTED INTO THE COUNTY ROAD SYSTEM BY APPROPRIATE RESOLUTION OF THE ORANGE COUNTY BOARD OF SUPERVISORS.

SURVEYOR'S STATEMENT:

THIS MAP WAS PREPARED BY ME OR UNDER MY DIRECTION AND IS BASED UPON A FIELD SURVEY IN CONFORMANCE WITH THE REQUIREMENTS OF THE SUBDIVISION MAP ACT AND LOCAL ORDINANCE AT THE REQUEST OF DMB LADERA, L.L.C., IN JULY, 2002. I HEREBY STATE THAT ALL MONUMENTS ARE OF THE CHARACTER AND OCCUPY THE POSITIONS INDICATED, OR THAT THEY WILL BE SET IN SUCH POSITIONS; AND THAT SAID MONUMENTS ARE SUFFICIENT TO ENABLE THE SURVEY TO BE RETRACED. I HEREBY STATE THAT THIS FINAL MAP SUBSTANTIALLY CONFORMS TO THE CONDITIONALLY APPROVED TENTATIVE MAP.

Rory S. Williams 5/21/04
RORY S. WILLIAMS, L.S. 6654 DATE
LICENSE EXPIRES: 12/31/05

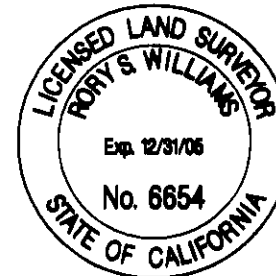


COUNTY SURVEYOR'S STATEMENT

I HEREBY STATE THAT I HAVE EXAMINED THIS MAP AND HAVE FOUND IT TO BE SUBSTANTIALLY IN CONFORMANCE WITH THE TENTATIVE MAP AS FILED WITH, AMENDED AND APPROVED BY THE ORANGE COUNTY SUBDIVISION COMMITTEE; THAT ALL PROVISIONS OF THE SUBDIVISION MAP ACT AND COUNTY SUBDIVISION REGULATIONS HAVE BEEN COMPLIED WITH AND I AM SATISFIED SAID MAP IS TECHNICALLY CORRECT.

DATED THIS 31st DAY OF September, 2004.

RAYMOND L. MATHE, COUNTY SURVEYOR

[Signature]
RAYMOND L. MATHE COUNTY SURVEYOR
LS 6185, EXPIRATION DATE: 3/31/06

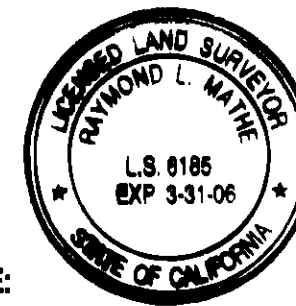

COUNTY TREASURER-TAX COLLECTOR'S CERTIFICATE:

STATE OF CALIFORNIA } SS
COUNTY OF ORANGE }

I HEREBY CERTIFY THAT ACCORDING TO THE RECORDS OF MY OFFICE THERE ARE NO LIENS AGAINST THE LAND COVERED BY THIS MAP OR ANY PART THEREOF FOR UNPAID STATE, COUNTY, MUNICIPAL OR LOCAL TAXES OR SPECIAL ASSESSMENTS COLLECTED AS TAXES, EXCEPT TAXES OR SPECIAL ASSESSMENTS COLLECTED AS TAXES NOT YET PAYABLE.

AND DO CERTIFY TO THE RECORDER OF ORANGE COUNTY THAT THE PROVISIONS OF THE SUBDIVISION MAP ACT HAVE BEEN COMPLIED WITH REGARDING DEPOSITS TO SECURE PAYMENT OF TAXES OR SPECIAL ASSESSMENTS COLLECTED AS TAXES ON THE LAND COVERED BY THIS MAP.

DATED THIS 20th DAY OF July, 2004.

JOHN M.W. MOORLACH COUNTY TREASURER-TAX COLLECTOR
BY: [Signature] DEPUTY TREASURER-TAX COLLECTOR

CLERK OF THE BOARD OF SUPERVISORS' CERTIFICATE:

STATE OF CALIFORNIA } SS
COUNTY OF ORANGE }

I HEREBY CERTIFY THAT THIS MAP WAS PRESENTED FOR APPROVAL TO THE BOARD OF SUPERVISORS OF THE COUNTY OF ORANGE AT REGULAR MEETING THEREOF HELD ON THE 19th DAY OF October, 2004, AND THAT THEREUPON SAID BOARD DID, BY AN ORDER DULY PASSED AND ENTERED, APPROVE SAID MAP.

AND DID ACCEPT ON BEHALF OF THE COUNTY OF ORANGE THE EASEMENTS FOR INGRESS AND EGRESS OF EMERGENCY AND PUBLIC SERVICE VEHICLES AS DEDICATED.

DATED THIS 19th DAY OF October, 2004.

[Signature]
CLERK OF THE BOARD OF SUPERVISORS
DARLENE J. BLOOM



CERTIFICATE OF ACCEPTANCE - SANTA MARGARITA WATER DISTRICT

THE UNDERSIGNED, BEING THE DULY APPOINTED AGENT OF THE SANTA MARGARITA WATER DISTRICT, A PUBLIC CORPORATION IN ORANGE COUNTY, CALIFORNIA, PURSUANT TO ITS RESOLUTION NO. 88-10-2, DOES HEREBY ACCEPT ON BEHALF OF SAID DISTRICT, THE EASEMENTS FOR WATER, RECYCLED WATER, SEWER AND ACCESS PURPOSES AS DEDICATED AND SHOWN ON THIS TRACT MAP, BY AND BETWEEN THE SANTA MARGARITA WATER DISTRICT AND WARMINGTON ARBOLEDO ASSOCIATES, L.P. A CALIFORNIA LIMITED PARTNERSHIP AND DOES HEREBY CERTIFY THAT THE GRANTEE CONSENTS TO THE RECORDATION OF SAID TRACT MAP.

[Signature]
DANIEL R. FERONS, CHIEF ENGINEER
SANTA MARGARITA WATER DISTRICT

NOTARY ACKNOWLEDGMENT - SANTA MARGARITA WATER DISTRICT

STATE OF CALIFORNIA } SS
COUNTY OF ORANGE }

ON 7-8-04 BEFORE ME, Cindy R. Lane, Notary Public, PERSONALLY
APPEARED DANIEL R. FERONS, PERSONALLY KNOWN TO ME (OR PROVED TO ME ON THE BASIS
OF SATISFACTORY EVIDENCE) TO BE THE PERSON WHOSE NAME IS SUBSCRIBED TO THE WITHIN
INSTRUMENT AND ACKNOWLEDGED TO ME THAT HE EXECUTED THE SAME IN HIS AUTHORIZED
CAPACITY, AND THAT BY HIS SIGNATURE ON THE INSTRUMENT THE PERSON, OR ENTITY UPON
BEHALF OF WHICH THE PERSON ACTED, EXECUTED THE INSTRUMENT.

WITNESS MY HAND:

SIGNATURE Cindy R. Lane
NOTARY PUBLIC IN AND FOR SAID STATE
CINDY R. LANE
(NAME PRINTED)

MY PRINCIPAL PLACE OF BUSINESS IS
IN Orange COUNTY.
MY COMMISSION EXPIRES: 2-20-2005

SIGNATURE OMISSIONS:

PURSUANT TO THE PROVISIONS OF SECTION 66436(a)(3)(C) OF THE SUBDIVISION MAP ACT, THE FOLLOWING SIGNATURES HAVE BEEN OMITTED:

LADERA DEVELOPMENT COMPANY, L.L.C., HOLDER OF OIL, GAS AND MINERAL RIGHTS RECORDED DECEMBER 10, 1996, AS INSTRUMENT NO. 19960624029 OF OFFICIAL RECORDS.

861 25

861 26

TRACT NO. 16667

IN UNINCORPORATED TERRITORY OF THE COUNTY OF ORANGE,
STATE OF CALIFORNIA

RORY S. WILLIAMS, L.S. 6654 DATE OF SURVEY: JULY, 2002
HUNSAKER AND ASSOCIATES IRVINE, INC.

SHEET 2 OF 4 SHEETS
SCALE: 1" = 150'
LOTS A THROUGH C, INCLUSIVE
ACREAGE: 7.047 ACRES
(A PORTION OF VESTING
TENTATIVE TRACT NO. 16395)

BASIS OF BEARINGS:

THE BEARINGS SHOWN HEREON ARE BASED ON THE BEARING BETWEEN O.C.S. HORIZONTAL CONTROL STATION GPS NO. 1417 AND STATION GPS NO. 1448 BEING N10°48'13"E PER RECORDS ON FILE IN THE OFFICE OF THE ORANGE COUNTY SURVEYOR.

DATUM STATEMENT:

COORDINATES SHOWN ARE BASED ON THE CALIFORNIA COORDINATE SYSTEM (CCS83), ZONE VI, 1983 NAD, (1981.35 EPOCH OCS GPS ADJUSTMENT). ALL DISTANCES SHOWN ARE GROUND, UNLESS OTHERWISE NOTED. TO OBTAIN GRID DISTANCE MULTIPLY GROUND DISTANCE BY 0.999948295. THIS COMBINATION FACTOR IS PROJECT SPECIFIC.

MONUMENT NOTES:

2" I.P. TAGGED L.S. 6654 OR LEAD, TACK & TAG L.S. 6654 OR NAIL & TAG L.S. 6654 OR 8" SAW STAMPED L.S. 6654 TO BE SET AT ALL TRACT BOUNDARY CORNERS WITHIN 90 DAYS AFTER ACCEPTANCE OF IMPROVEMENTS, UNLESS OTHERWISE NOTED.

1" I.P. TAGGED L.S. 6654 OR LEAD, TACK & TAG L.S. 6654 OR NAIL & TAG L.S. 6654 OR 8" SAW STAMPED L.S. 6654 TO BE SET AT ALL LOT CORNERS, EXCEPT LOT CORNERS THAT ARE THE INTERSECTION OF SIDELINES WITH STREET RIGHT OF WAY, WITHIN 90 DAYS AFTER ACCEPTANCE OF IMPROVEMENTS, UNLESS OTHERWISE NOTED.

8" SAW STAMPED L.S. 6654 OR LEAD, TACK & TAG L.S. 6654 OR 1" I.P. TAGGED L.S. 6654 TO BE SET AT ALL STREET CENTERLINE POINTS OF CONTROL, WITHIN 90 DAYS AFTER ACCEPTANCE OF IMPROVEMENTS, UNLESS OTHERWISE NOTED.

LEAD, TACK & TAG L.S. 6654 TO BE SET IN TOP OF CURB AT AN OFFSET ALONG FRONT SIDE LOT LINES PRODUCED, IN LIEU OF AT FRONT LOT CORNERS, WITHIN 90 DAYS AFTER ACCEPTANCE OF IMPROVEMENTS, UNLESS OTHERWISE NOTED. BEARING AND DISTANCE OF PRODUCTION IS AS NOTED IN MONUMENT OFFSET TABLES HEREON.

● INDICATES FOUND MONUMENT OR LOCATION OF MONUMENT SET, AS NOTED.

■ INDICATES NOTHING TO BE SET.

▲ INDICATES FOUND ORANGE COUNTY SURVEYOR GPS CONTROL MONUMENT AS NOTED.

P# INDICATES BEARING AND DISTANCE OF LOT LINE PRODUCTION FROM LOT CORNER TO MONUMENT.

1 INDICATES SET 2" I.P. TAGGED L.S. 6654 PRIOR TO MAP RECORDATION.

2 INDICATES LOCATION OF 1" I.P. TAGGED "P.L.S. 5557" OR SPIKE & WASHER STAMPED "P.L.S. 5557" OR LEAD, TACK & TAG "P.L.S. 5557" TO BE SET PER TRACT NO. 15986, M.M. 849/1-15.

EASEMENT NOTES:

(A) INDICATES AN EASEMENT FOR WATER, RECYCLED WATER, SEWER AND ACCESS PURPOSES DEDICATED HEREON TO THE SANTA MARGARITA WATER DISTRICT, AND AN EASEMENT FOR INGRESS AND EGRESS OF EMERGENCY AND PUBLIC SERVICE VEHICLES DEDICATED HEREON TO THE COUNTY OF ORANGE.

(B) INDICATES CENTERLINE OF A PROPOSED 36' WIDE ACCESS EASEMENT AS SHOWN ON TRACT NO. 15986, M.M. 849/1-15.

(C) INDICATES CENTERLINE OF A PROPOSED 58' WIDE ACCESS EASEMENT AS SHOWN ON TRACT NO. 15986, M.M. 849/1-15.

NOTES:

LOT A IS FOR PRIVATE STREET PURPOSES.

LOT B IS FOR POCKET PARK PURPOSES.

LOT C IS FOR OPEN SPACE/LANDSCAPE PURPOSES AND IS NOT A SEPARATE BUILDING SITE.

NOTARY ACKNOWLEDGMENT:


STATE OF CALIFORNIA } SS
COUNTY OF ORANGE }

ON October 21, 2004 BEFORE ME, Kendra Clement AND Jonathan David PERSONALLY
APPEARED Jonathan David AND Kendra Clement PERSONALLY
KNOWN TO ME (OR PROVED TO ME ON THE BASIS OF SATISFACTORY EVIDENCE) TO BE THE PERSON(S)
WHOSE NAME(S) IS/ARE SUBSCRIBED TO THE WITHIN INSTRUMENT AND ACKNOWLEDGED TO ME THAT
HE/SHE/they executed the SAME IN HIS/HER/their AUTHORIZED CAPACITY(IES) AND THAT BY
HIS/HER/their SIGNATURE(S) ON THE INSTRUMENT THE PERSON(S), OR ENTITY UPON BEHALF OF
WHICH THE PERSON(S) ACTED, EXECUTED THE INSTRUMENT.
WITNESS MY HAND:

SIGNATURE Kendra Clement MY PRINCIPAL PLACE OF BUSINESS IS
NOTARY PUBLIC IN AND FOR SAID STATE IN Orange COUNTY.
Kendra Clement MY COMMISSION EXPIRES: May 25, 2006
(NAME PRINTED)

SHEET INDEX AND GPS CONTROL MAP

3 INDICATES SHEET NUMBER

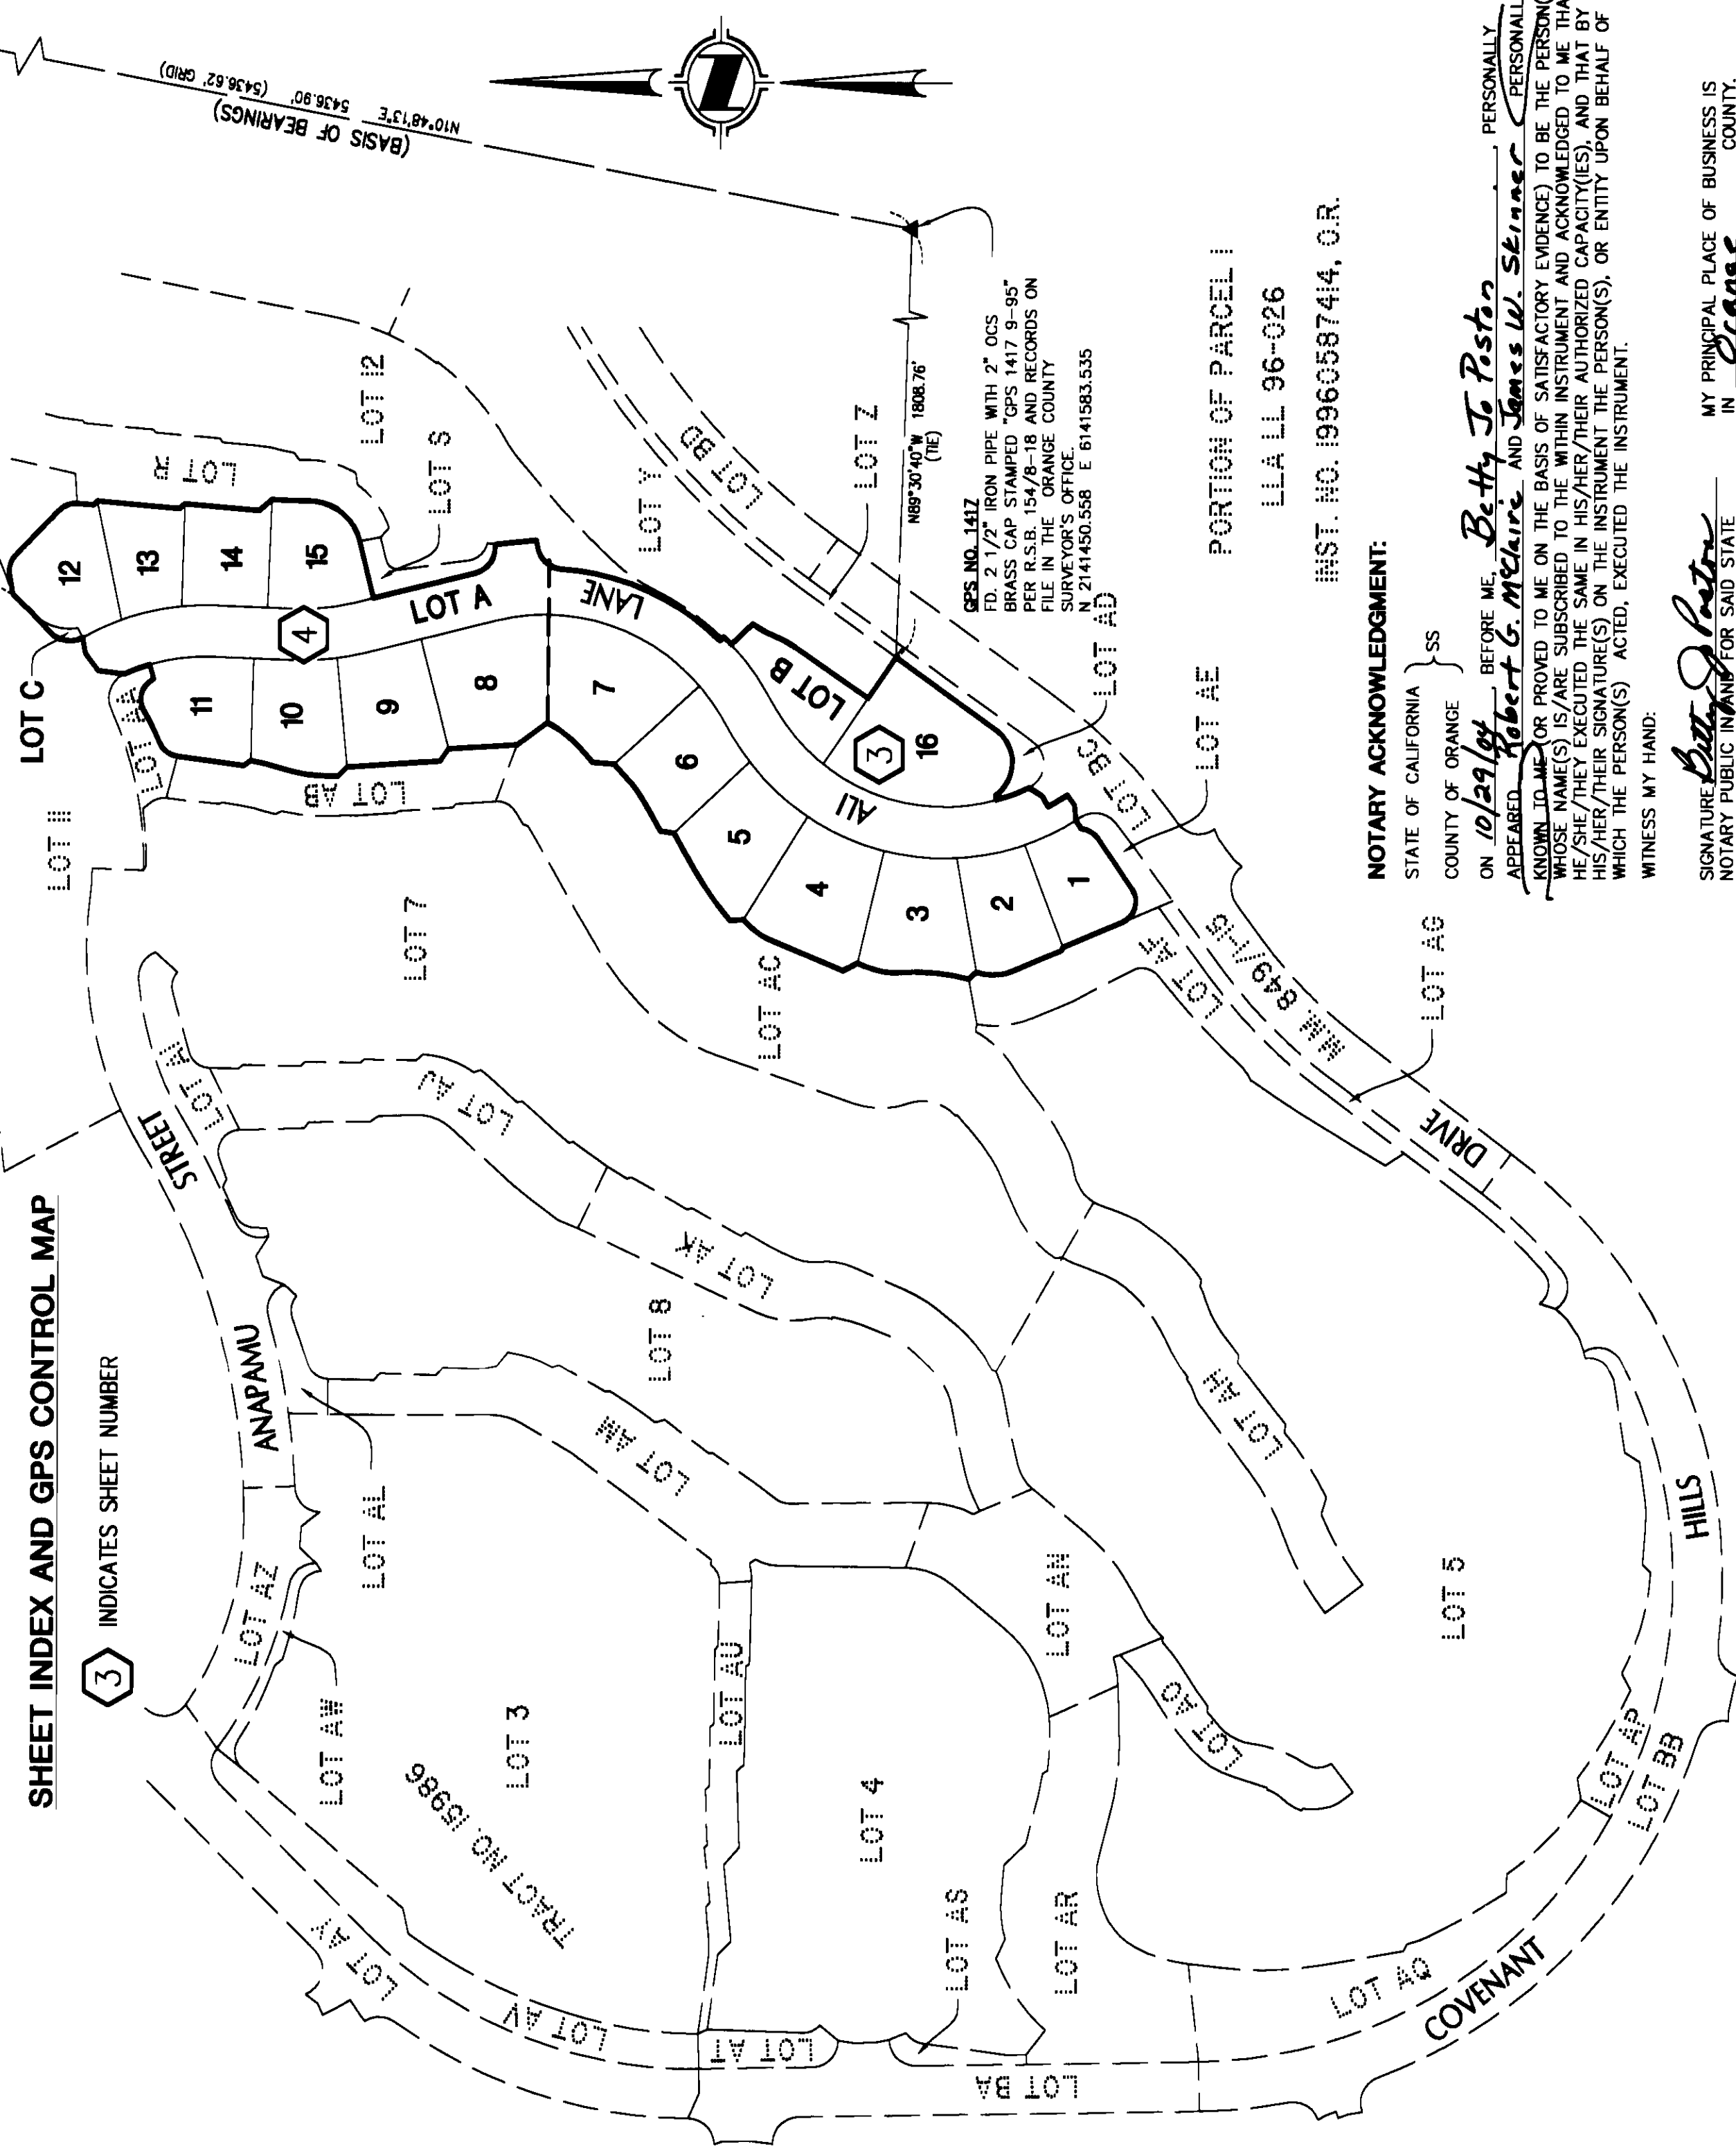

GPS NO. 1448
FD. 2" IRON PIPE WITH 1 3/4" OCS
BRASS CAP STAMPED "1448 9-95" PER
R.S.B. 154/B-18 AND RECORDS ON FILE
IN THE ORANGE COUNTY SURVEYOR'S
OFFICE
N 2146790.819 E 6142602.585
N 10°48'13"E 5436.90' (S436.92' GRID)

GPS NO. 1417
FD. 2 1/2" IRON PIPE WITH 2" OCS
BRASS CAP STAMPED "GPS 1417 9-95"
PER R.S.B. 154/B-18 AND RECORDS ON
FILE IN THE ORANGE COUNTY
SURVEYOR'S OFFICE.
N 2141450.558 E 6141583.535
N 89°30'40"W 1808.76' (NE)

PORTION OF PARCEL I

LLA LL 96-026

INST. NO. 19960587414, O.R.

NOTARY ACKNOWLEDGMENT:

STATE OF CALIFORNIA } SS
COUNTY OF ORANGE }

ON 10/29/04 BEFORE ME, Betty Jo Poston AND Robert G. McNamee PERSONALLY
APPEARED Betty Jo Poston AND Robert G. McNamee PERSONALLY
KNOWN TO ME (OR PROVED TO ME ON THE BASIS OF SATISFACTORY EVIDENCE) TO BE THE PERSON(S)
WHOSE NAME(S) IS/ARE SUBSCRIBED TO THE WITHIN INSTRUMENT AND ACKNOWLEDGED TO ME THAT
HE/SHE/they executed the SAME IN HIS/HER/their AUTHORIZED CAPACITY(IES), AND THAT BY
HIS/HER/their SIGNATURE(S) ON THE INSTRUMENT THE PERSON(S), OR ENTITY UPON BEHALF OF
WHICH THE PERSON(S) ACTED, EXECUTED THE INSTRUMENT.
WITNESS MY HAND:

SIGNATURE Betty Jo Poston MY PRINCIPAL PLACE OF BUSINESS IS
NOTARY PUBLIC IN AND FOR SAID STATE IN Orange COUNTY.
Betty Jo Poston MY COMMISSION EXPIRES: 3/17/05
(NAME PRINTED)


SHEET 3 OF 4 SHEETS
SCALE: 1" = 40'
16 NUMBERED LOTS AND
LOTS A THROUGH C, INCLUSIVE
ACREAGE: 7.047 ACRES
(A PORTION OF VESTING
TENTATIVE TRACT NO. 16396)

TRACT NO. 16667

IN UNINCORPORATED TERRITORY OF THE COUNTY OF ORANGE,
STATE OF CALIFORNIA

HUNSAKER AND ASSOCIATES IRVINE, INC.
RORY S. WILLIAMS, L.S. 6664 DATE OF SURVEY: JULY, 2002

SEE SHEET 4

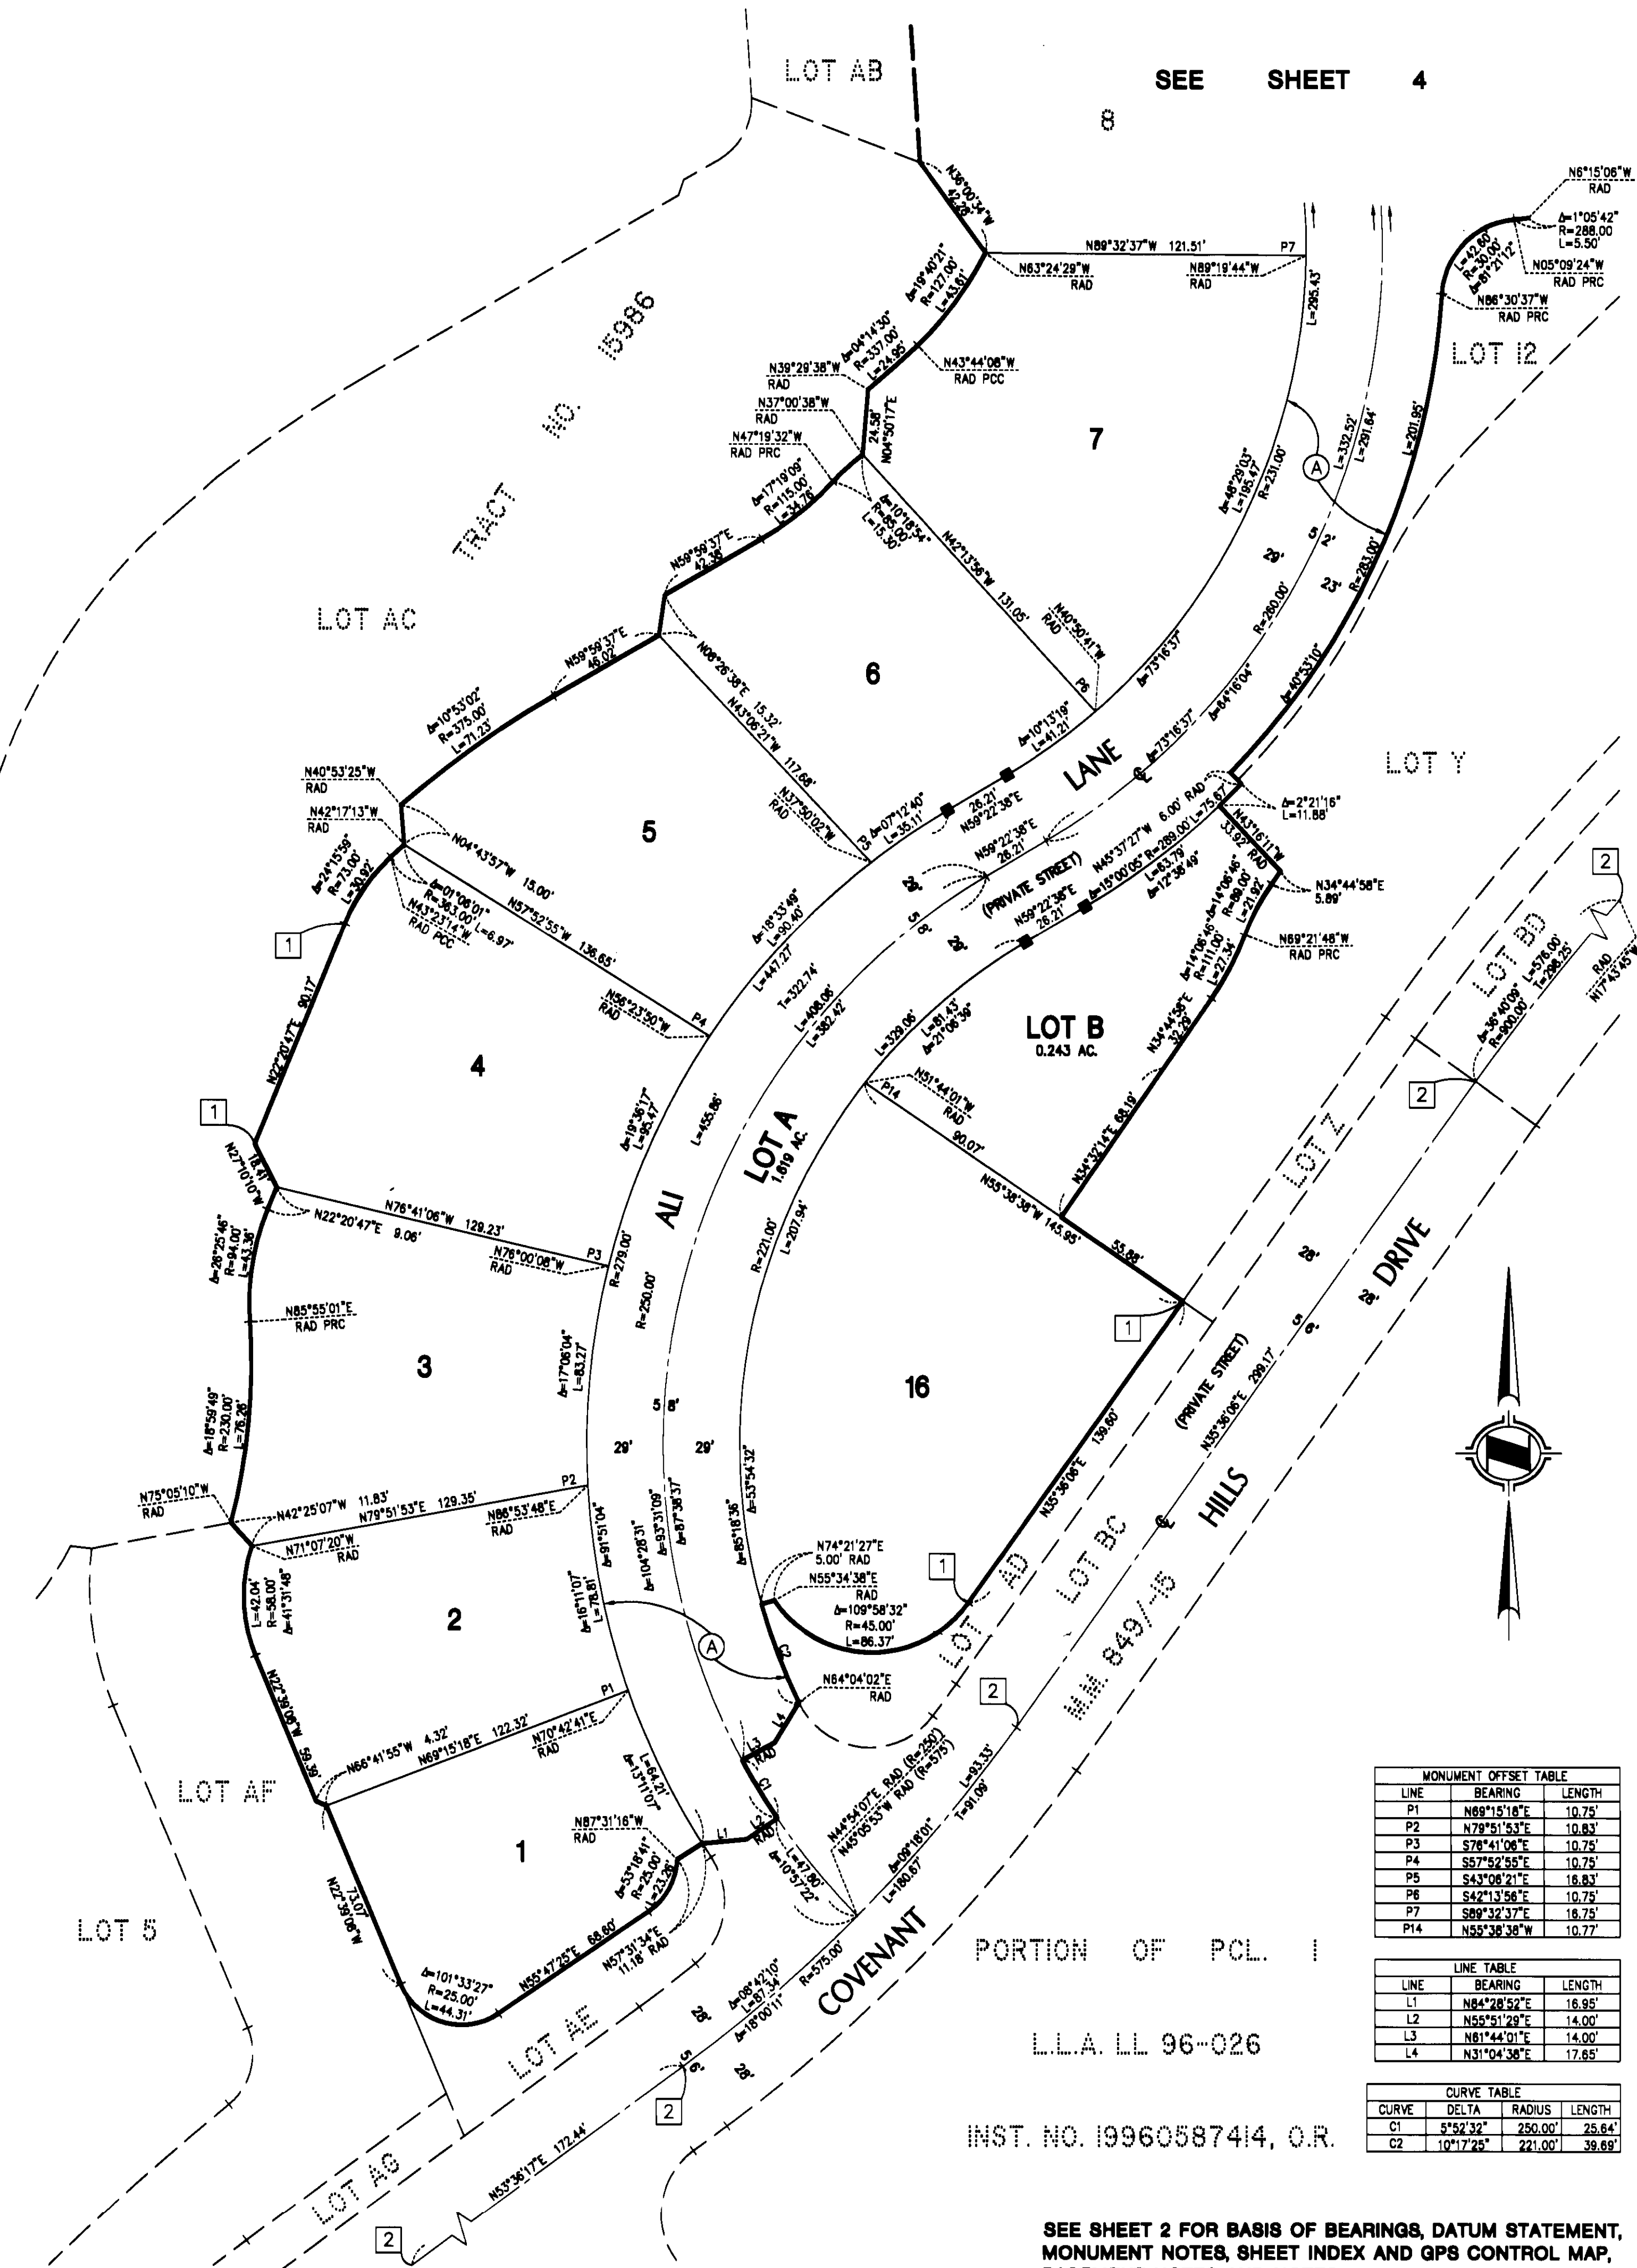

MONUMENT OFFSET TABLE		
LINE	BEARING	LENGTH
P1	N89°15'18"E	10.75'
P2	N79°51'53"E	10.83'
P3	S78°41'08"E	10.75'
P4	S57°52'55"E	10.75'
P5	S43°08'21"E	16.83'
P6	S42°13'56"E	10.75'
P7	S89°32'37"E	16.75'
P14	N55°38'38"W	10.77'

LINE TABLE		
LINE	BEARING	LENGTH
L1	N84°28'52"E	16.95'
L2	N55°51'29"E	14.00'
L3	N81°44'01"E	14.00'
L4	N31°04'38"E	17.65'

CURVE TABLE			
CURVE	DELTA	RADIUS	LENGTH
C1	5°52'32"	250.00'	25.64'
C2	10°17'25"	221.00'	39.69'

LLA LL 96-026

INST. NO. 19960587414, O.R.

SEE SHEET 2 FOR BASIS OF BEARINGS, DATUM STATEMENT,
MONUMENT NOTES, SHEET INDEX AND GPS CONTROL MAP,
EASEMENT NOTES AND NOTES.


SHEET 4 OF 4 SHEETS
SCALE: 1" = 40'
16 NUMBERED LOTS AND
LOTS A THROUGH C, INCLUSIVE
ACREAGE: 7.047 ACRES
(A PORTION OF VESTING
TENTATIVE TRACT NO. 16396)

TRACT NO. 16667

IN UNINCORPORATED TERRITORY OF THE COUNTY OF ORANGE,
STATE OF CALIFORNIA

HUNSAKER AND ASSOCIATES IRVINE, INC.
RORY S. WILLIAMS, L.S. 0664 DATE OF SURVEY: JULY, 2002

DETAIL 'A'
N.T.S.

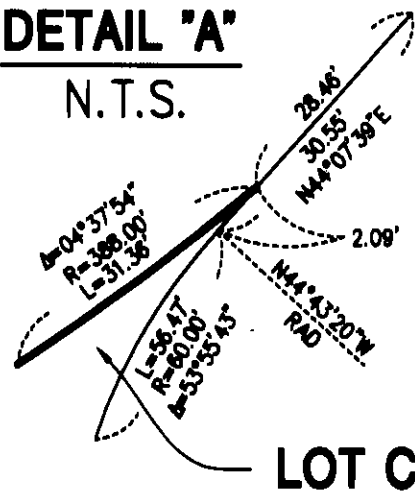

LOT C

TRACT NO. 15986

LOT II

SEE DETAIL ABOVE LEFT

LOT C
0.011 AC.

12

13

14

15

11

10

9

8

7

LOT 7

LOT AB


LOT AC

ALU LANE

LOT A

LOT S

LOT I2

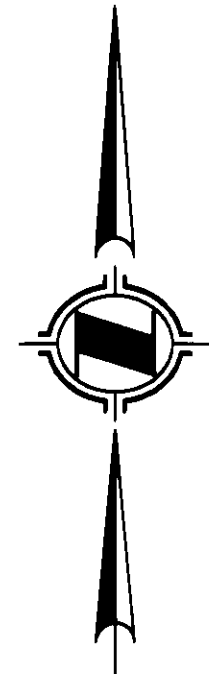

MONUMENT OFFSET TABLE		
LINE	BEARING	LENGTH
P7	S89°32'37"E	16.75'
P8	N75°25'55"E	10.75'
P9	N84°29'44"E	10.76'
P10	S88°35'04"E	16.75'
P11	S78°20'31"W	10.87'
P12	N88°29'25"W	10.83'
P13	N87°37'04"W	16.75'

LINE TABLE		
LINE	BEARING	LENGTH
L5	N07°04'41"E	29.76'
L6	N52°24'38"E	24.16'
L7	N81°24'41"E	18.34'
L8	N60°10'22"E	11.89'

CURVE TABLE			
CURVE	DELTA	RADIUS	LENGTH
C3	00°55'30"	270.00'	4.36'
C4	00°55'28"	272.00'	4.39'

SEE SHEET 2 FOR BASIS OF BEARINGS, DATUM STATEMENT,
MONUMENT NOTES, SHEET INDEX AND GPS CONTROL MAP,
EASEMENT NOTES AND NOTES.

SEE SHEET 3